Nurse call points | GREEN = bed / chair: 0 | BLUE = toilet: 0

Floor plan B02 - שקעים

1 : 100

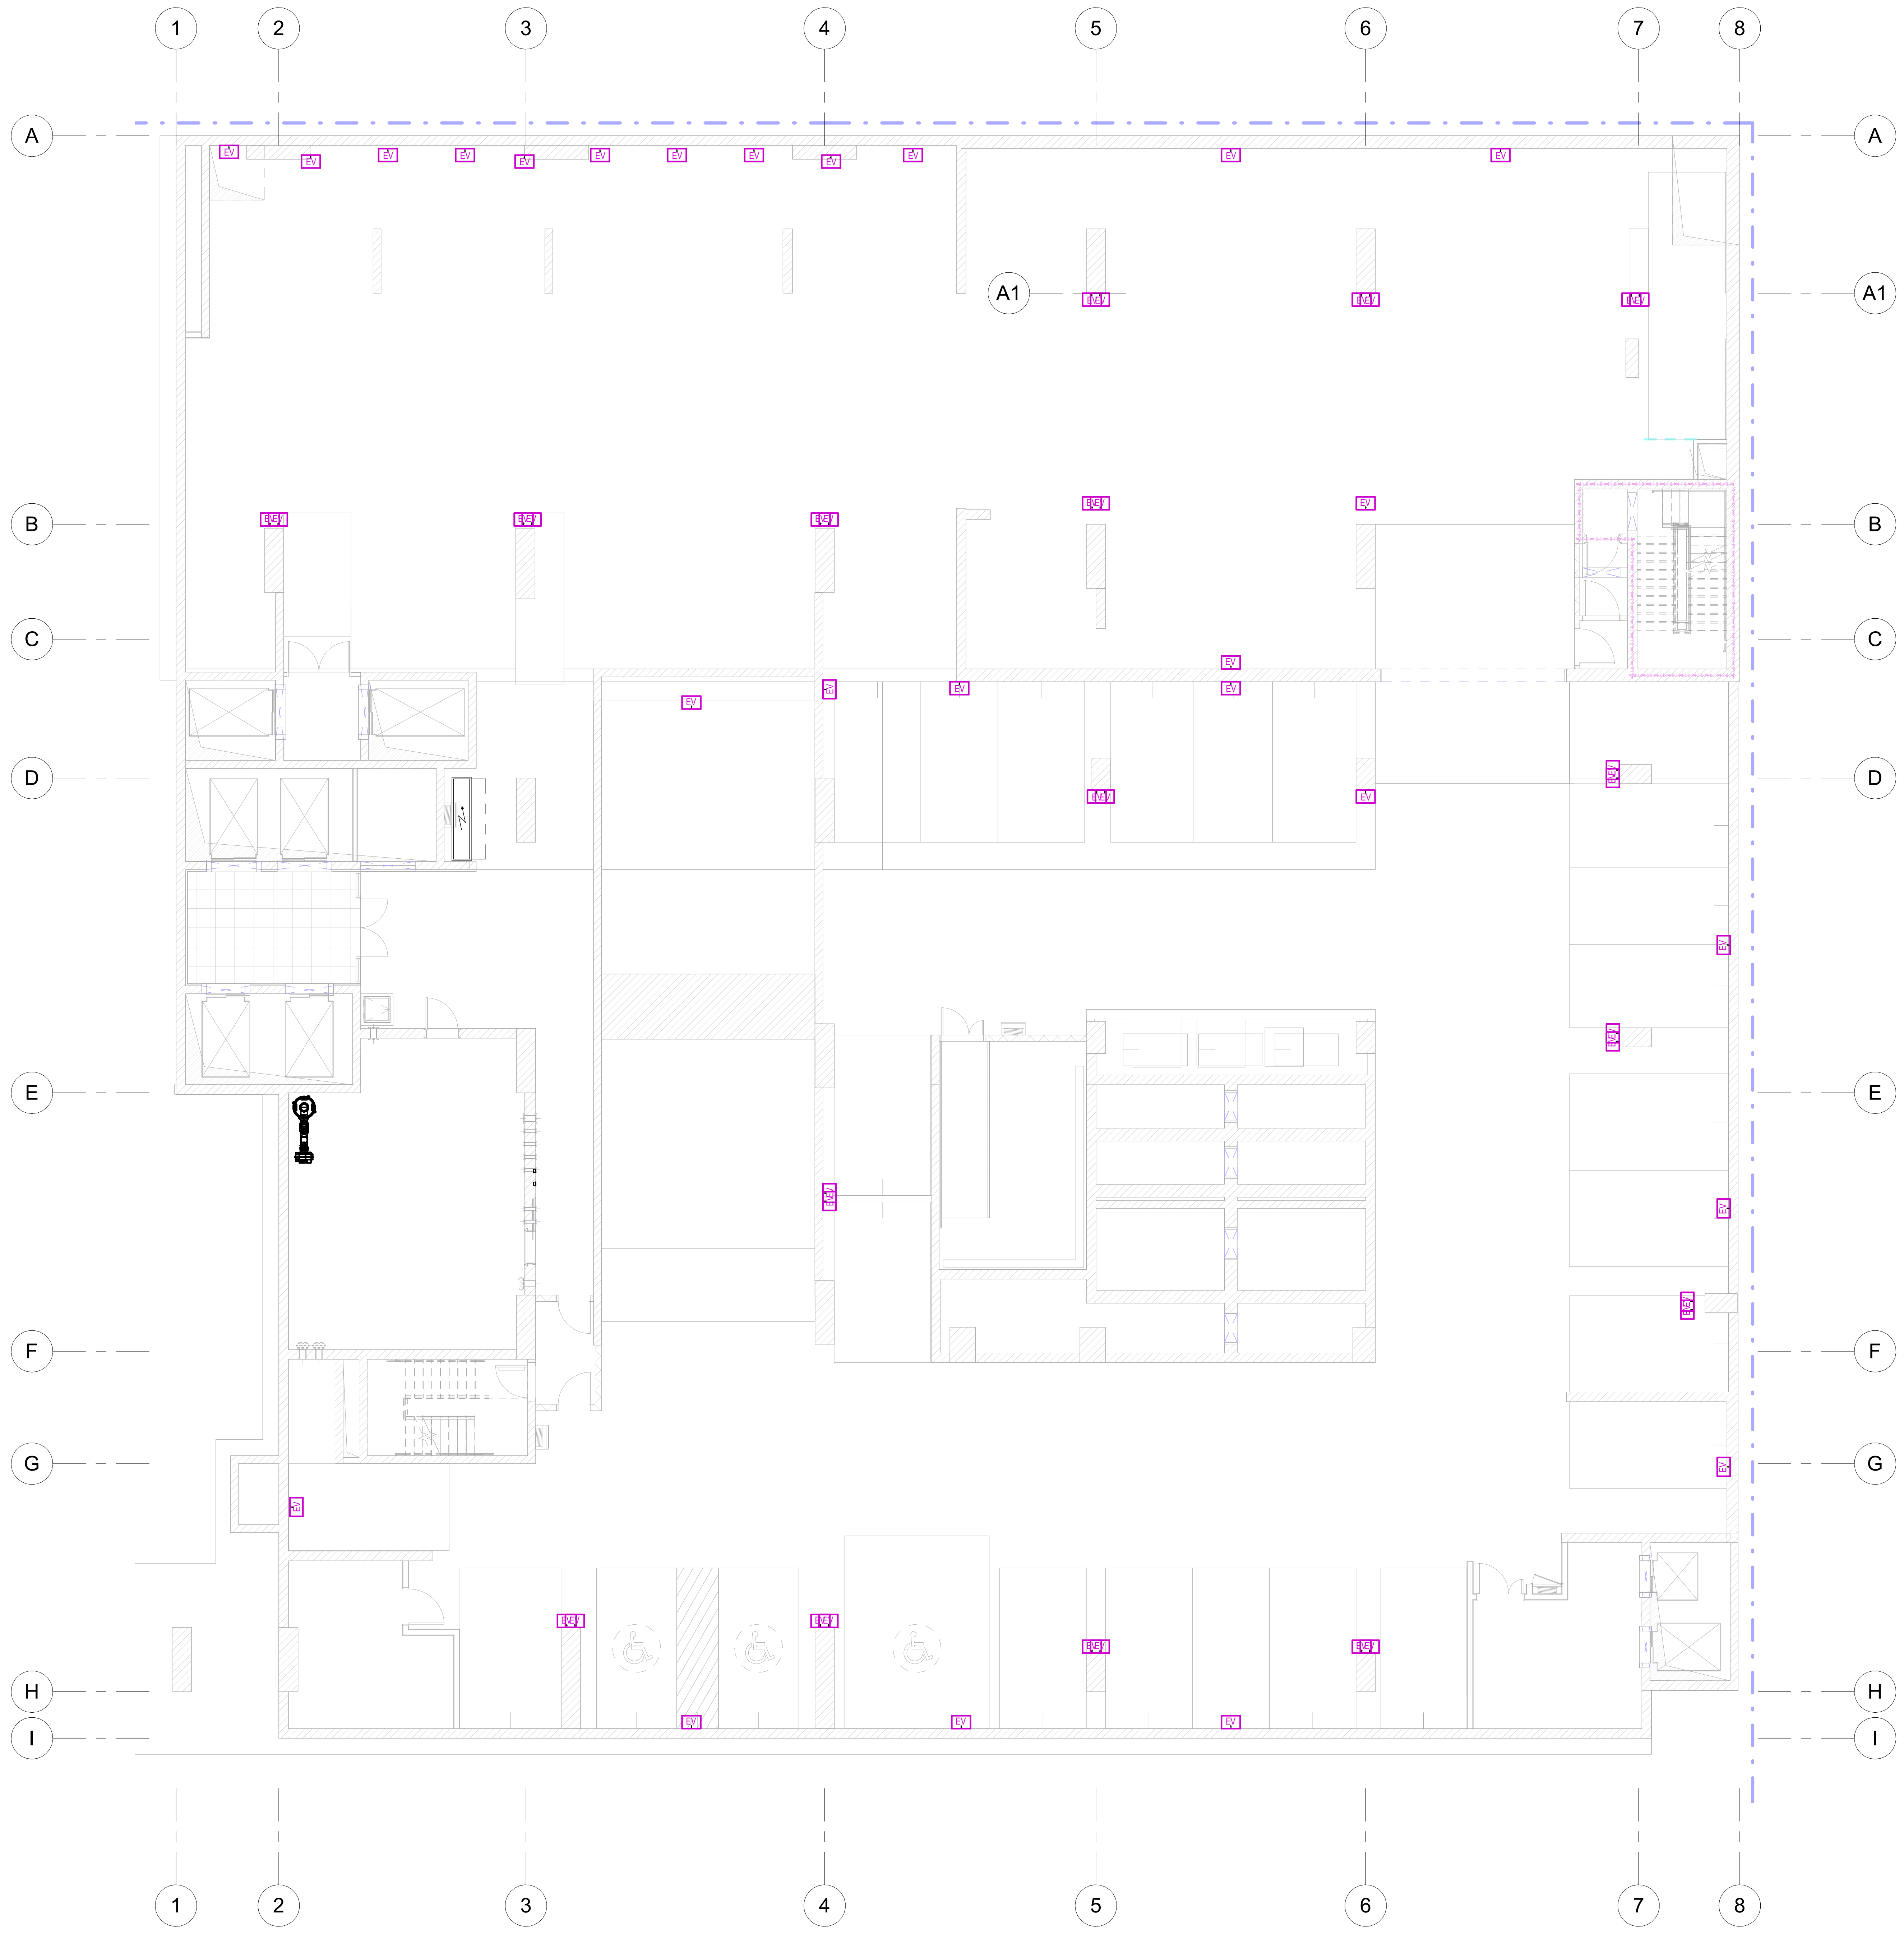

מהדורה	תאריך	תאור	שרטט	תפוצה
0	29.07.24	למכרז	אלכס.ר	

מטרת התכנית: (מחק את המיותר)
☑לעיון ☐למכרז ☐לאישור ☐לביצוע

הקבלן אחראי להתאמת כל המידות והכמויות בתכניות ובבנין לפני תחילת העבודה .כל אי תאום יש לברר עם המזמין אין למדוד על התכנית . התכנית היא רכושו הרעיוני של המתכנן.ואין לעשות בה כל שימוש ללא הסכמתו

מהדורה:
0

מספר תכנית	מתכנן	נושא	מבנה/מתחם	מתקן

מחלקת בינוי
ומערכות

שם העבודה:

שם התכנית:
קומה - B02 תוכנית שקעים

מתכנן יועץ

קלינפלץ הנדסה בע"מ
יעוץ תכנון פיקוח ובדיקות מתקני חשמל

מספר התוכנית:
GCN-ELC-B02-03

	תאריך	שם	חתימה
שרטט	08/10/20	אלכס.ר	
תיכנן	08/10/20	Designer	
בדק	08/10/20	Checker	
אישר	08/10/20	Approver	

קנה מידה
1 : 100

מספרי מתכנן/יועץ
עבודה:
גליון:

תכנית זו היא רכוש המזמין ואסורה בשימוש כולה או בחלקה לכל גורם אחד ,ללא אישור.

Autodesk Docs://Nesher-M17 (R23)/E-GCN-MAIN.rvt