Nurse call points | GREEN = bed / chair: 15 (#1-15) | BLUE = toilet: 0

Floor plan L01 - שקעים
1 : 100

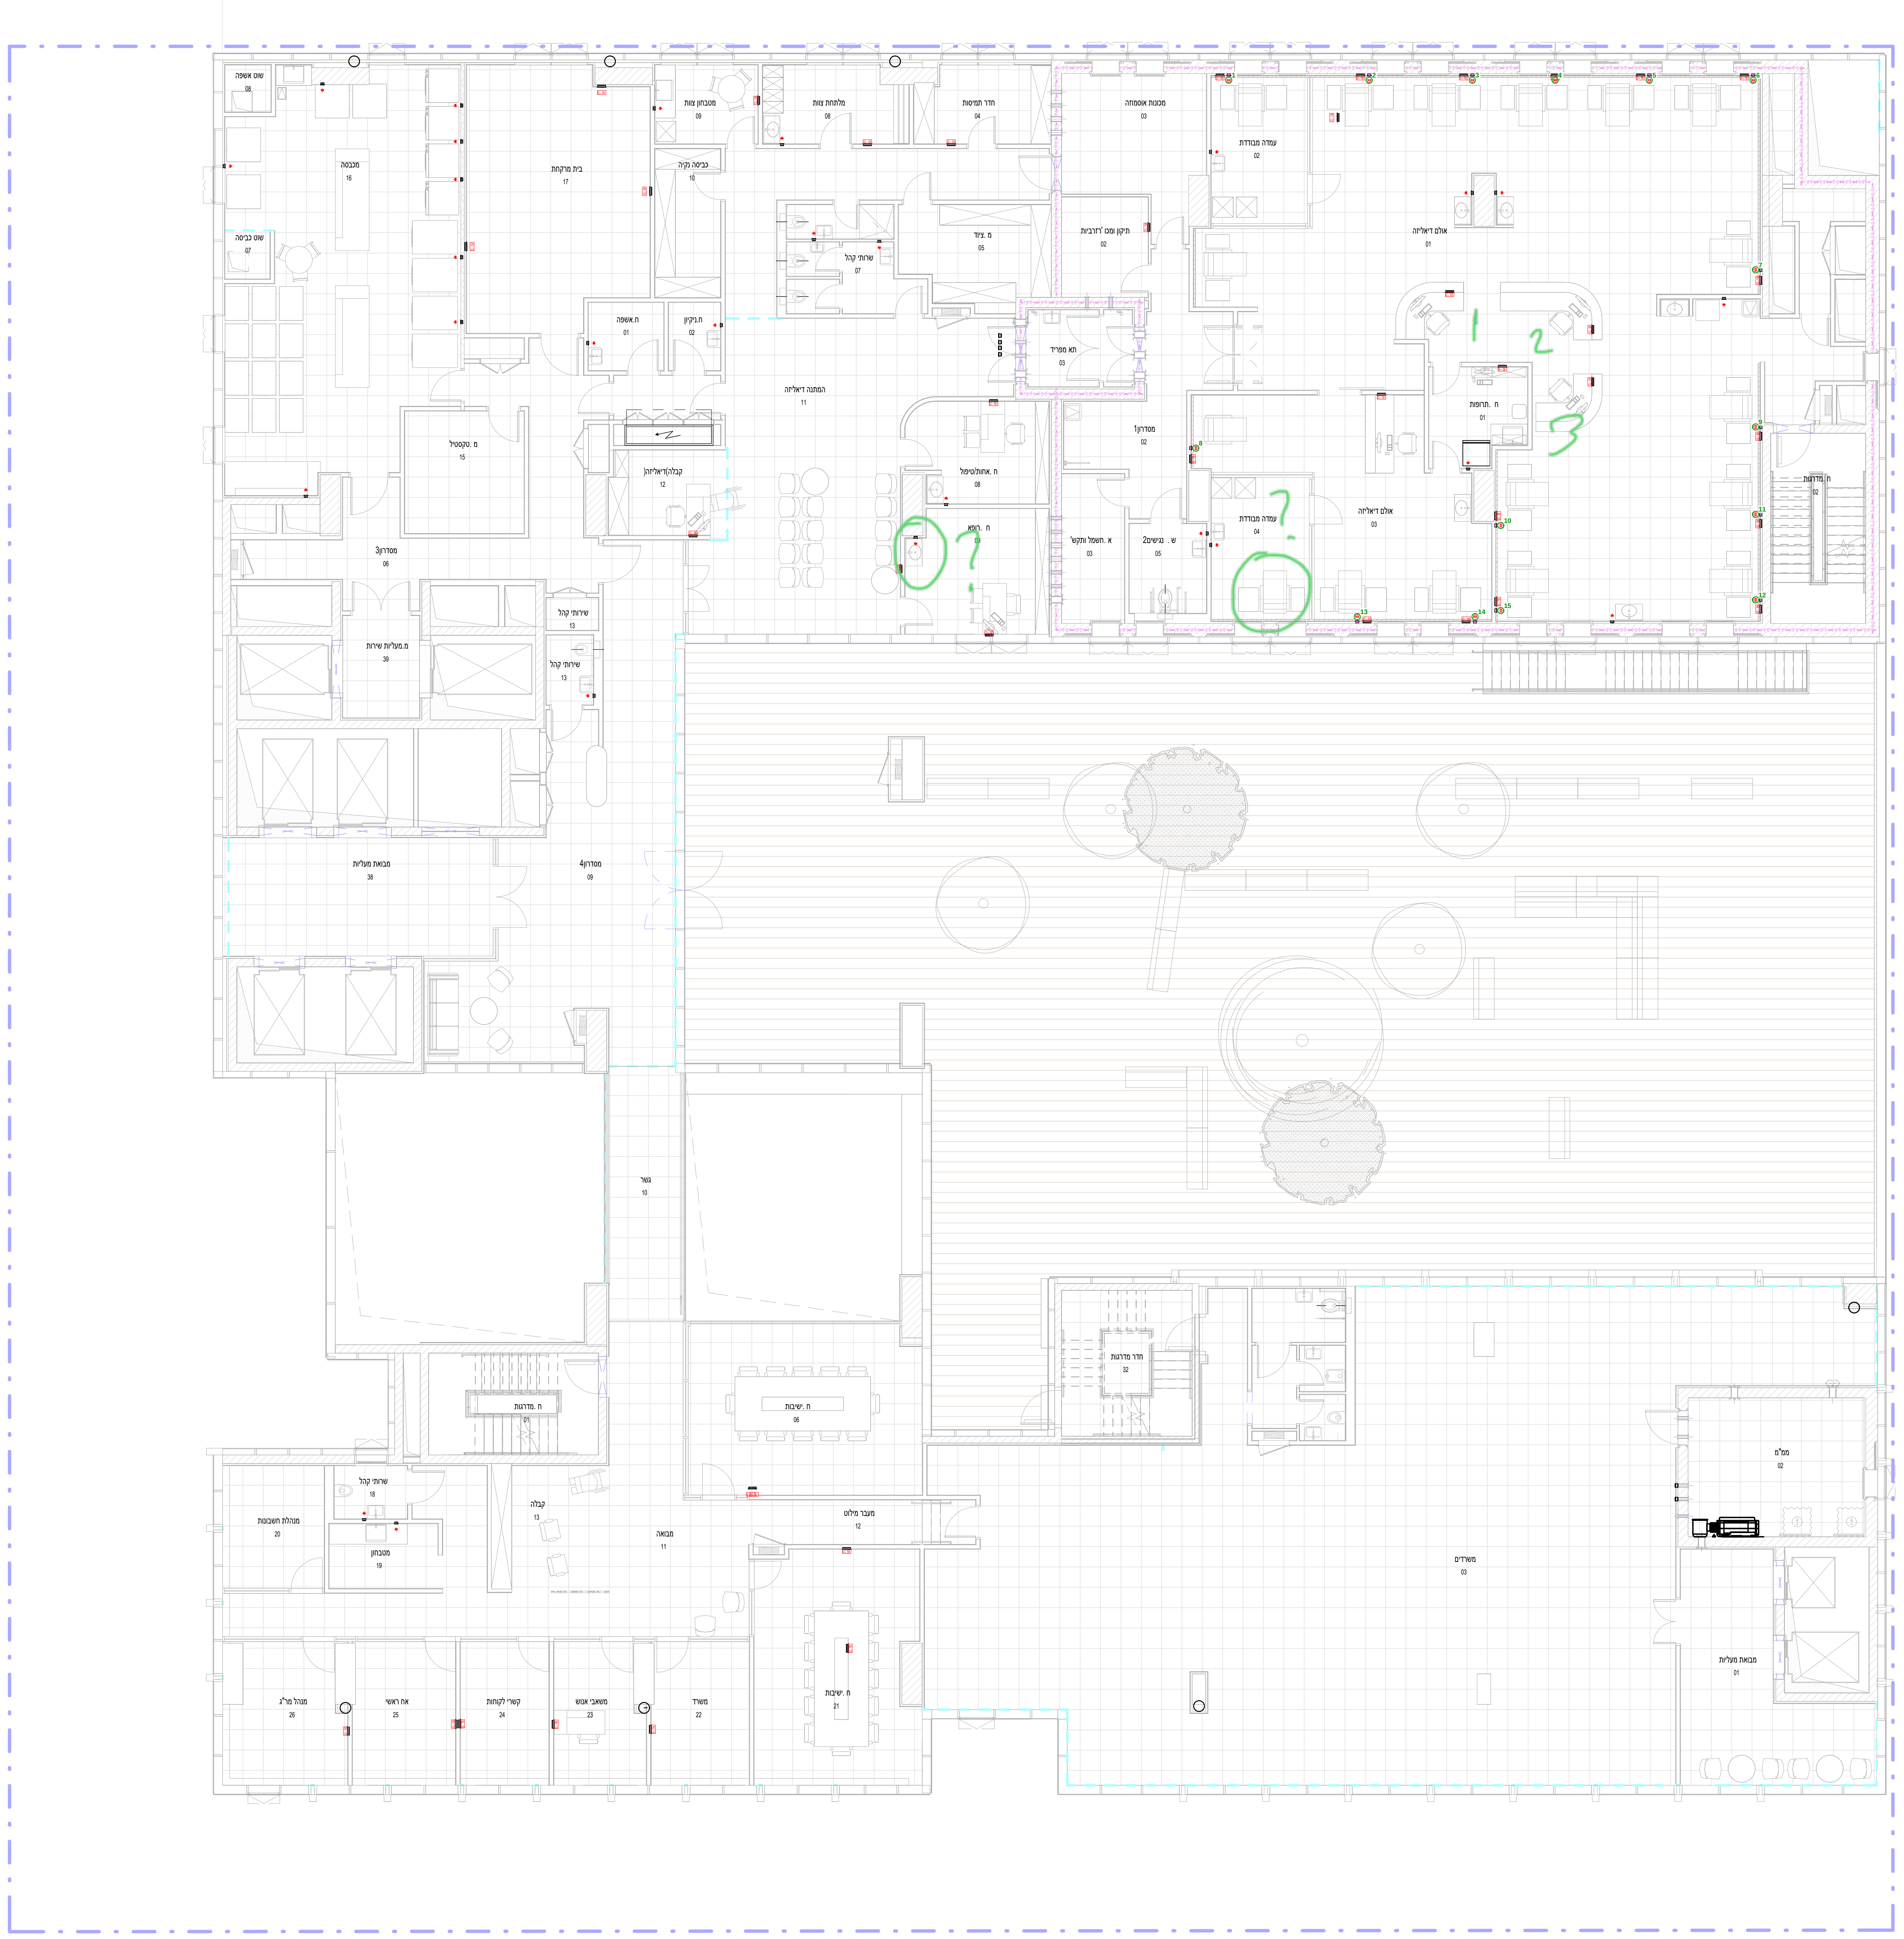

מהדורה	תאריך	תאור	שרטט	תפוצה
0	29.07.24	למכרז	אלכס.ר	

מטרת התכנית: (מחק את המיותר)
☑ לעיון ☐ למכרז ☐ לאישור ☐ לביצוע

הקבלן אחראי להתאמת כל המידות והכמויות בתכניות ובבנין לפני תחילת העבודה. כל אי תאום יש לברר עם המזמין. אין למדוד על התכנית. התכנית היא רכושו הרעיוני של המתכנן. ואין לעשות בה כל שימוש ללא הסכמתו

מהדורה: 0

מספר תכנית	מתכנן	נושא	מבנה/מתחם	מתקן

מחלקת בינוי ומערכות

שם העבודה:

שם התכנית:
קומה - L01 תוכנית שקעים

מתכנן יועץ
קלינפלץ הנדסה בע"מ
יעוץ תכנון פיקוח ובדיקות מתקני חשמל

מספר התוכנית:
GCN-ELC-L01-03

	תאריך	שם	חתימה
שרטט	08/10/20	אלכס.ר	
תיכנן	08/10/20	Designer	
בדק	08/10/20	Checker	
אישר	08/10/20	Approver	

קנה מידה: 1 : 100

מספרי מתכנן/יועץ
עבודה:
גליון:

תכנית זו היא רכוש המזמין ואסורה בשימוש כולה או בחלקה לכל גורם אחד, ללא אישור.

Autodesk Docs://Nesher-M17 (R23)/E-GCN-MAIN.rvt