Nurse call points | GREEN = bed / chair: 30 (#16-45) | BLUE = toilet: 11 (#3-13)

Floor plan L02 - שקעים
1 : 100

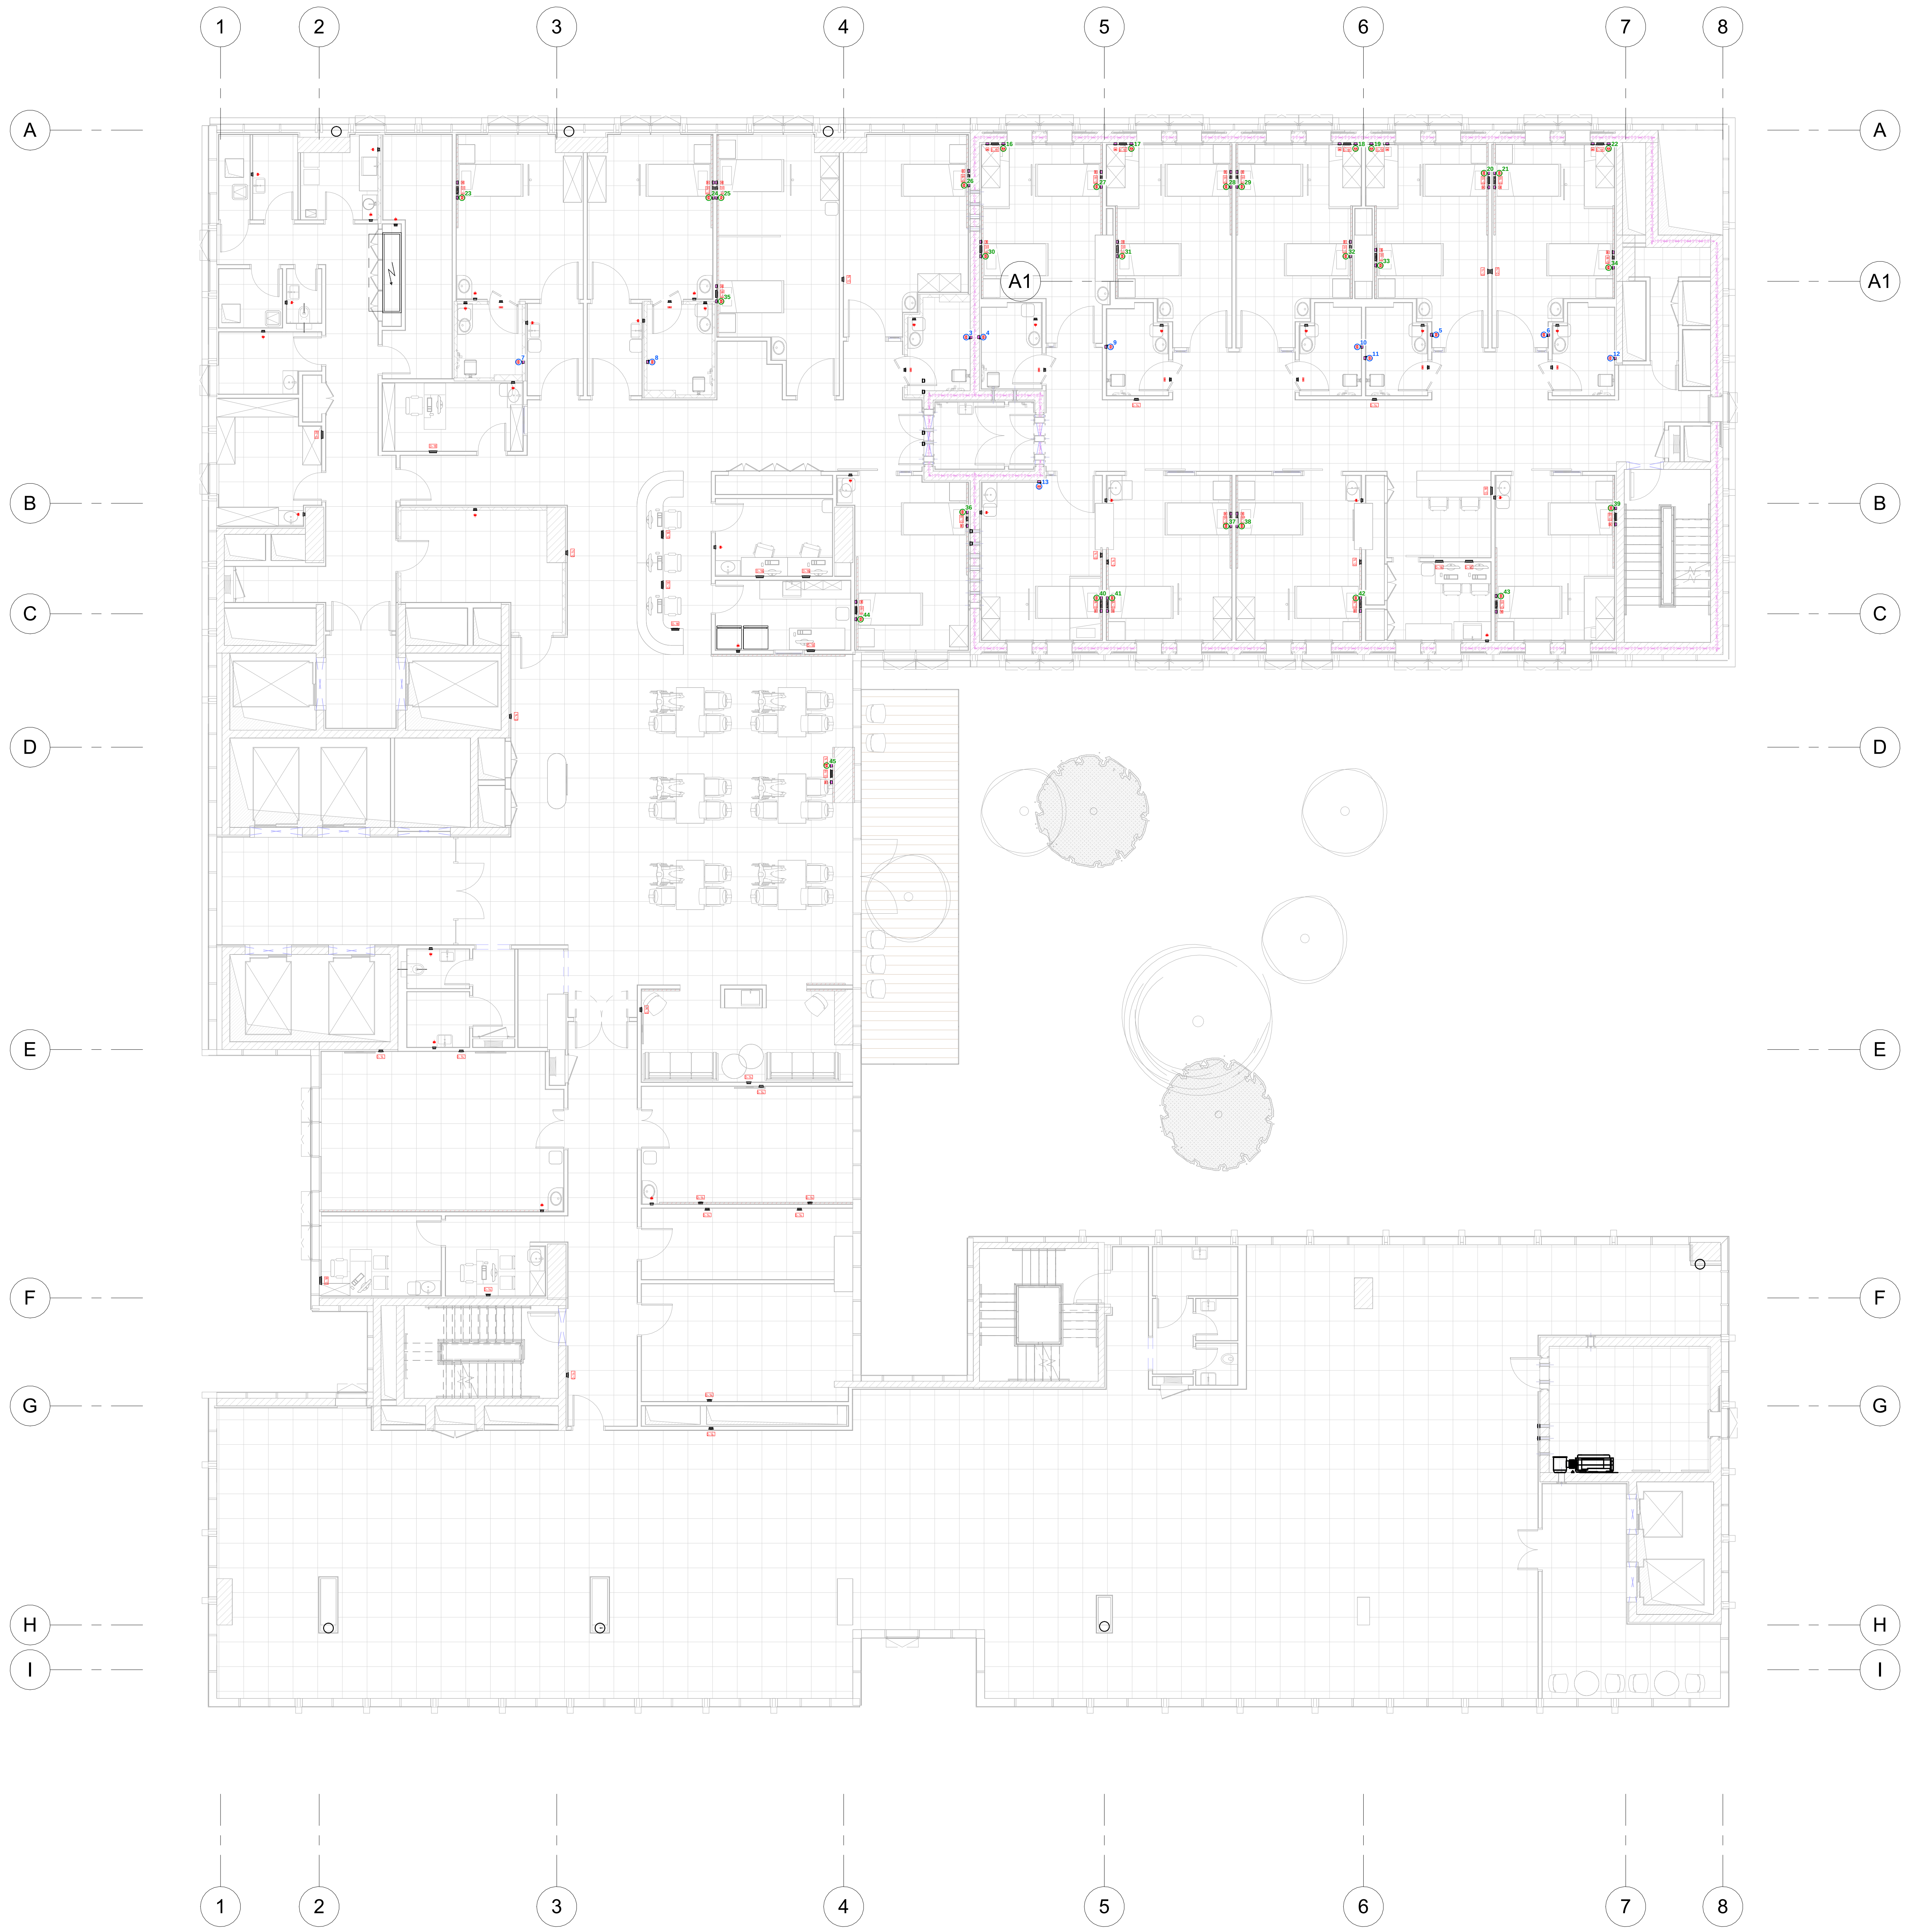

מהדורה	תאריך	תאור	שרטט	תפוצה
0	29.07.24	למכרז	אלכס.ר	

מטרת התכנית: (מחק את המיותר)
☑ לעיון ☐ למכרז ☐ לאישור ☐ לביצוע

הקבלן אחראי להתאמת כל המידות והכמויות בתכניות ובבנין לפני.תחילת העבודה .כל אי תאום יש לברר עם המזמין אין למדוד על התכנית . התכנית היא רכושו הרעיוני של המתכנן.ואין לעשות בה כל שימוש ללא הסכמתו

מהדורה: 0

מספר תכנית	מתכנן	נושא	מבנה/מתחם	מתקן

מחלקת בינוי
ומערכות

שם העבודה:

שם התכנית:
קומה - L02 תוכנית שקעים

מתכנן יועץ
קלינפלץ הנדסה בע"מ
יעוץ תכנון פיקוח ובדיקות מתקני חשמל

מספר התוכנית:
GCN-ELC-L02-03

	תאריך	שם	חתימה	קנה מידה	מספרי מתכנן/יועץ
שרטט	08/10/20	אלכס.ר		1 : 100	עבודה:
תיכנן	08/10/20	Designer			
בדק	08/10/20	Checker			גליון:
אישר	08/10/20	Approver			

תכנית זו היא רכוש המזמין ואסורה בשימוש כולה או בחלקה לכל גורם אחד ,ללא אישור.

Autodesk Docs://Nesher-M17 (R23)/E-GCN-MAIN.rvt