Nurse call points | GREEN = bed / chair: 32 (#78-109) | BLUE = toilet: 11 (#25-35)

Floor plan L04 - שקעים

1 : 100

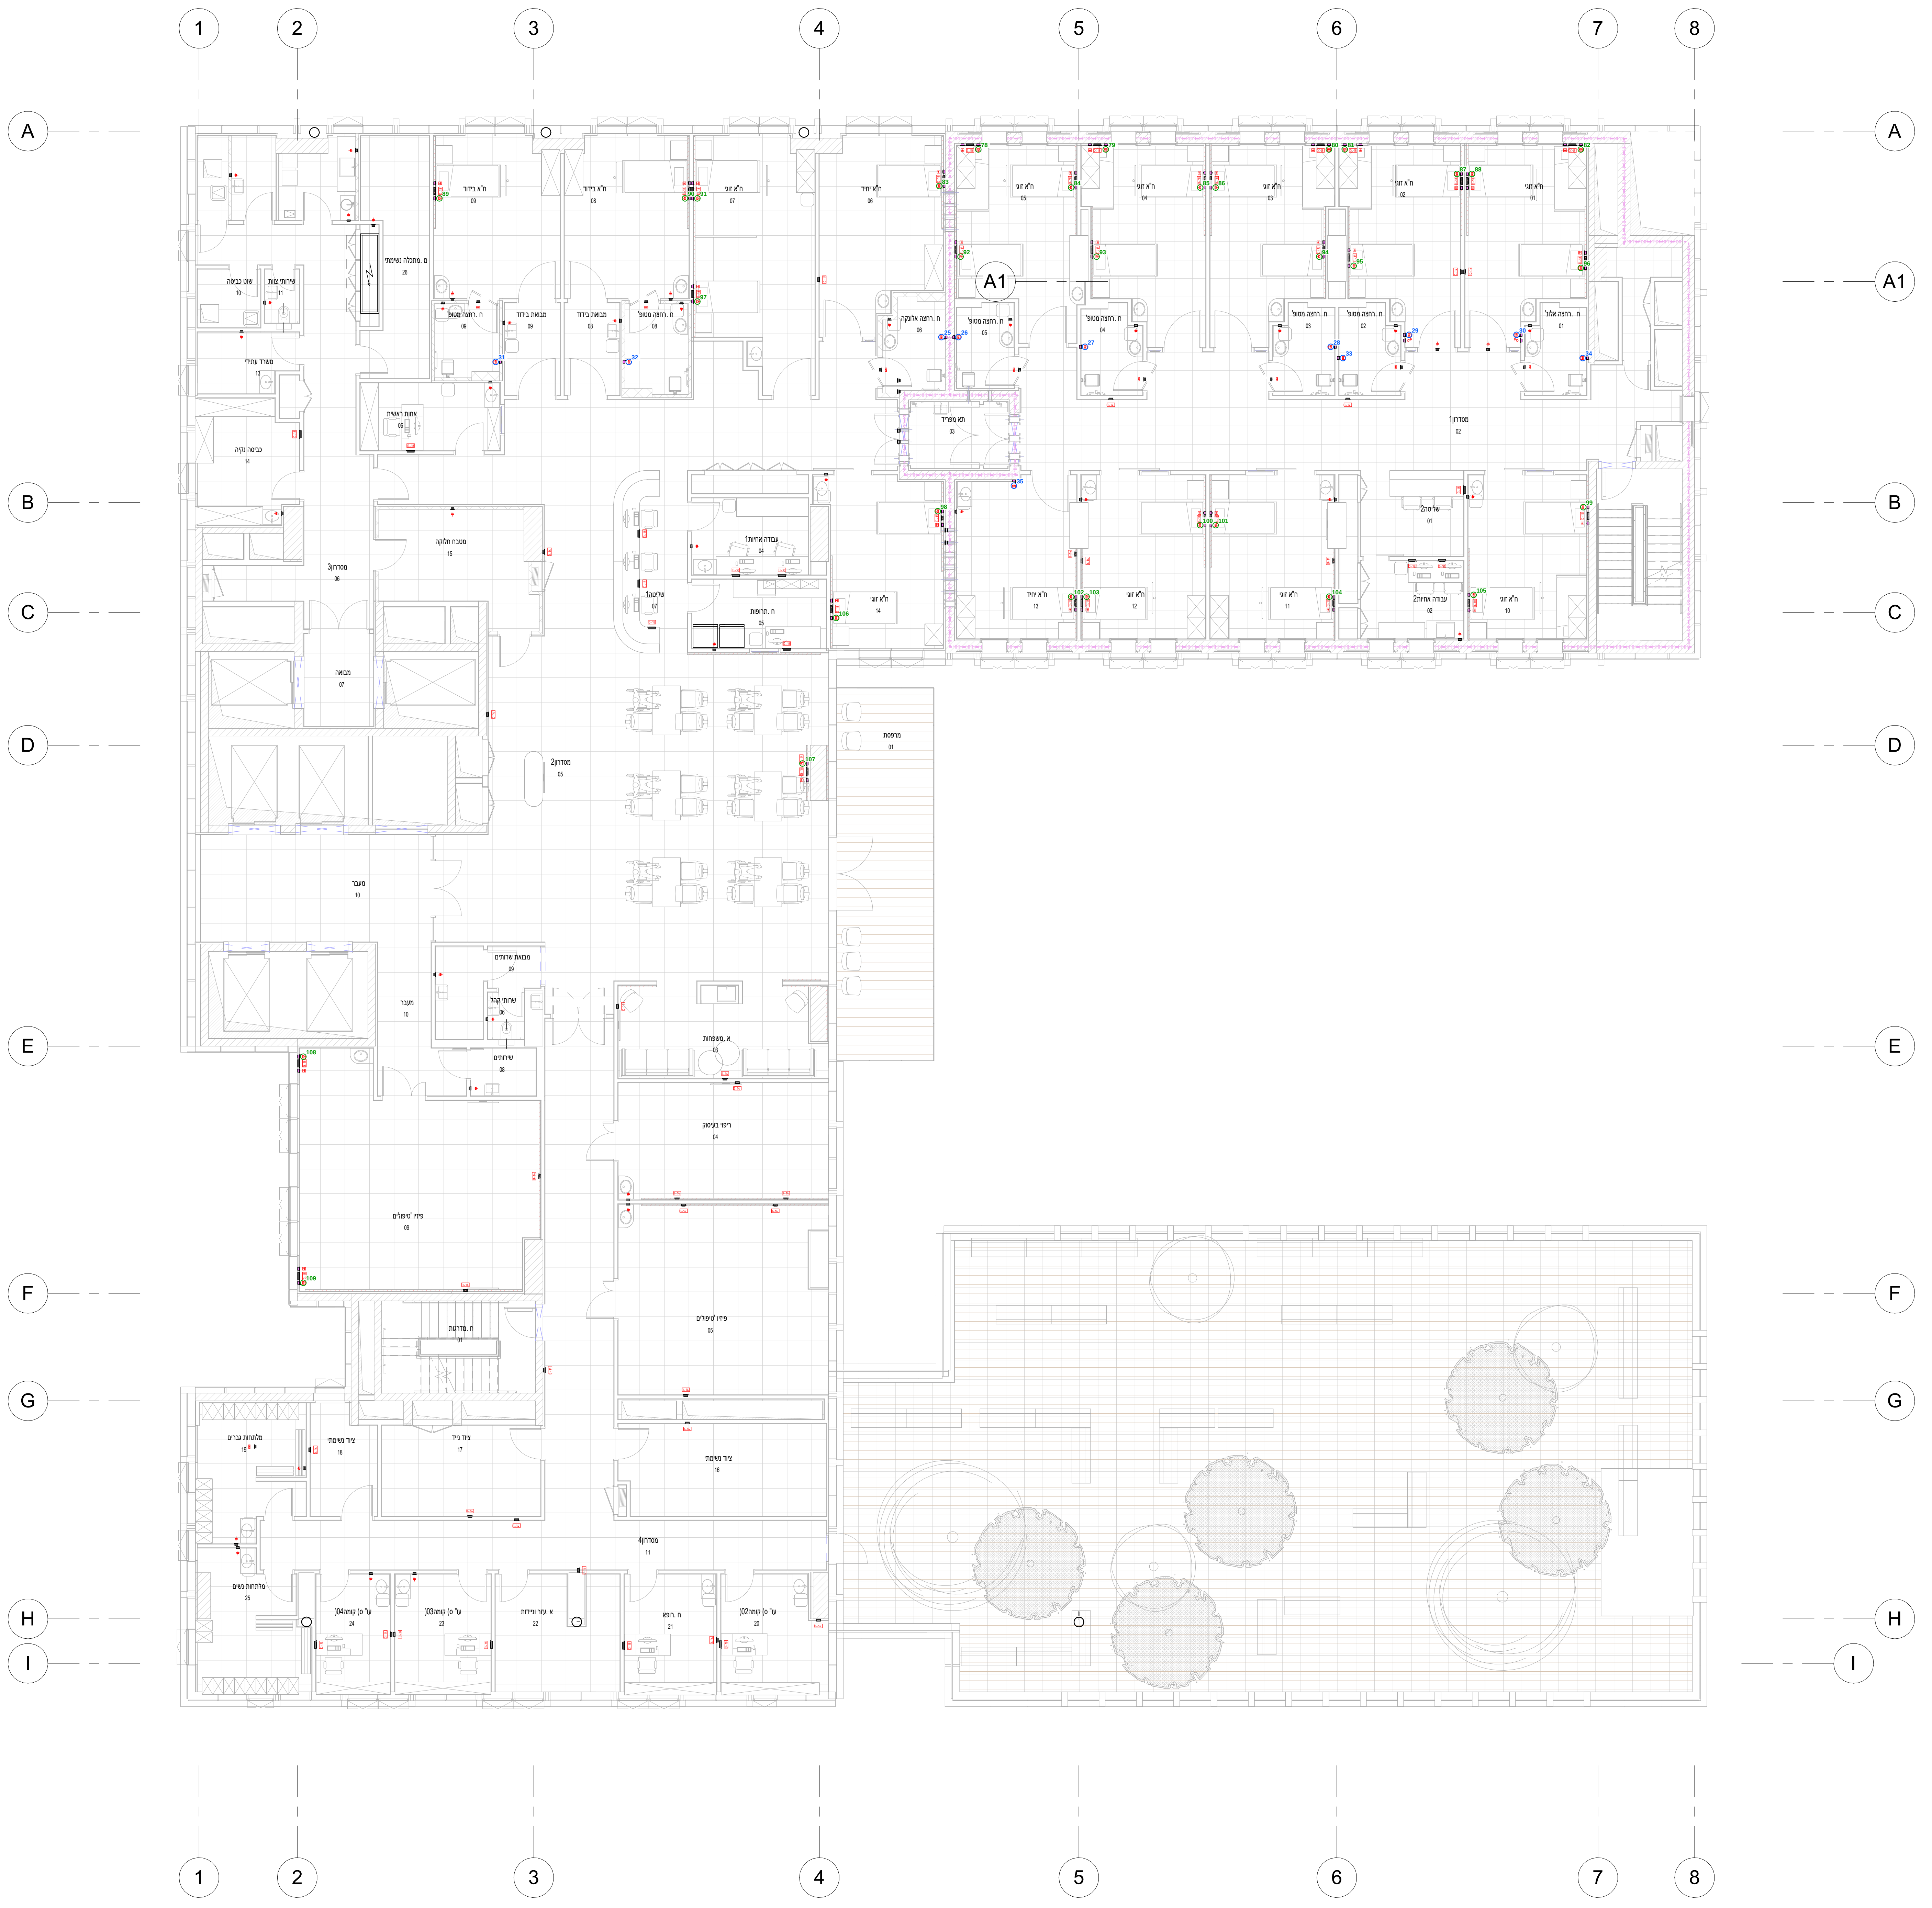

תפוצה	שרטט	תאור	תאריך	מהדורה
	אלכס.ד	למכרז	29.07.24	0

מטרת התכנית: (מחק את המיותר)
☑ לעיון ☐ למכרז ☐ לאישור ☐ לביצוע

הקבלן אחראי להתאמת כל המידות והכמויות בתכניות ובבנין לפני תחילת העבודה .כל אי תאום יש לברר עם המזמין אין למדוד על התכנית . התכנית היא רכושו הרעיוני של המתכנן.ואין לעשות בה כל שימוש ללא הסכמתו

מהדורה:
0

מתקן	מבנה/מתחם	נושא	מתכנן	מספר תכנית

מחלקת בינוי
ומערכות

שם העבודה:

שם התכנית:
קומה - L04 תוכנית שקעים

מתכנן יועץ

קלינפלץ הנדסה בע"מ
יעוץ תכנון פיקוח ובדיקות מתקני חשמל

מספר התוכנית:
GCN-ELC-L04-03

	תאריך	שם	חתימה
שרטט	08/10/20	אלכס.ד	
תיכנן	08/10/20	Designer	
בדק	08/10/20	Checker	
אישר	08/10/20	Approver	

קנה מידה
1 : 100

מספרי מתכנן/יועץ
עבודה:
גליון:

תכנית זו היא רכוש המזמין ואסורה בשימוש כולה או בחלקה לכל גורם אחד ,ללא אישור.

Autodesk Docs://Nesher-M17 (R23)/E-GCN-MAIN.rvt