Nurse call points | GREEN = bed / chair: 50 (#110-159) | BLUE = toilet: 10 (#36-45)

Floor plan L05 - שקעים
1 : 100

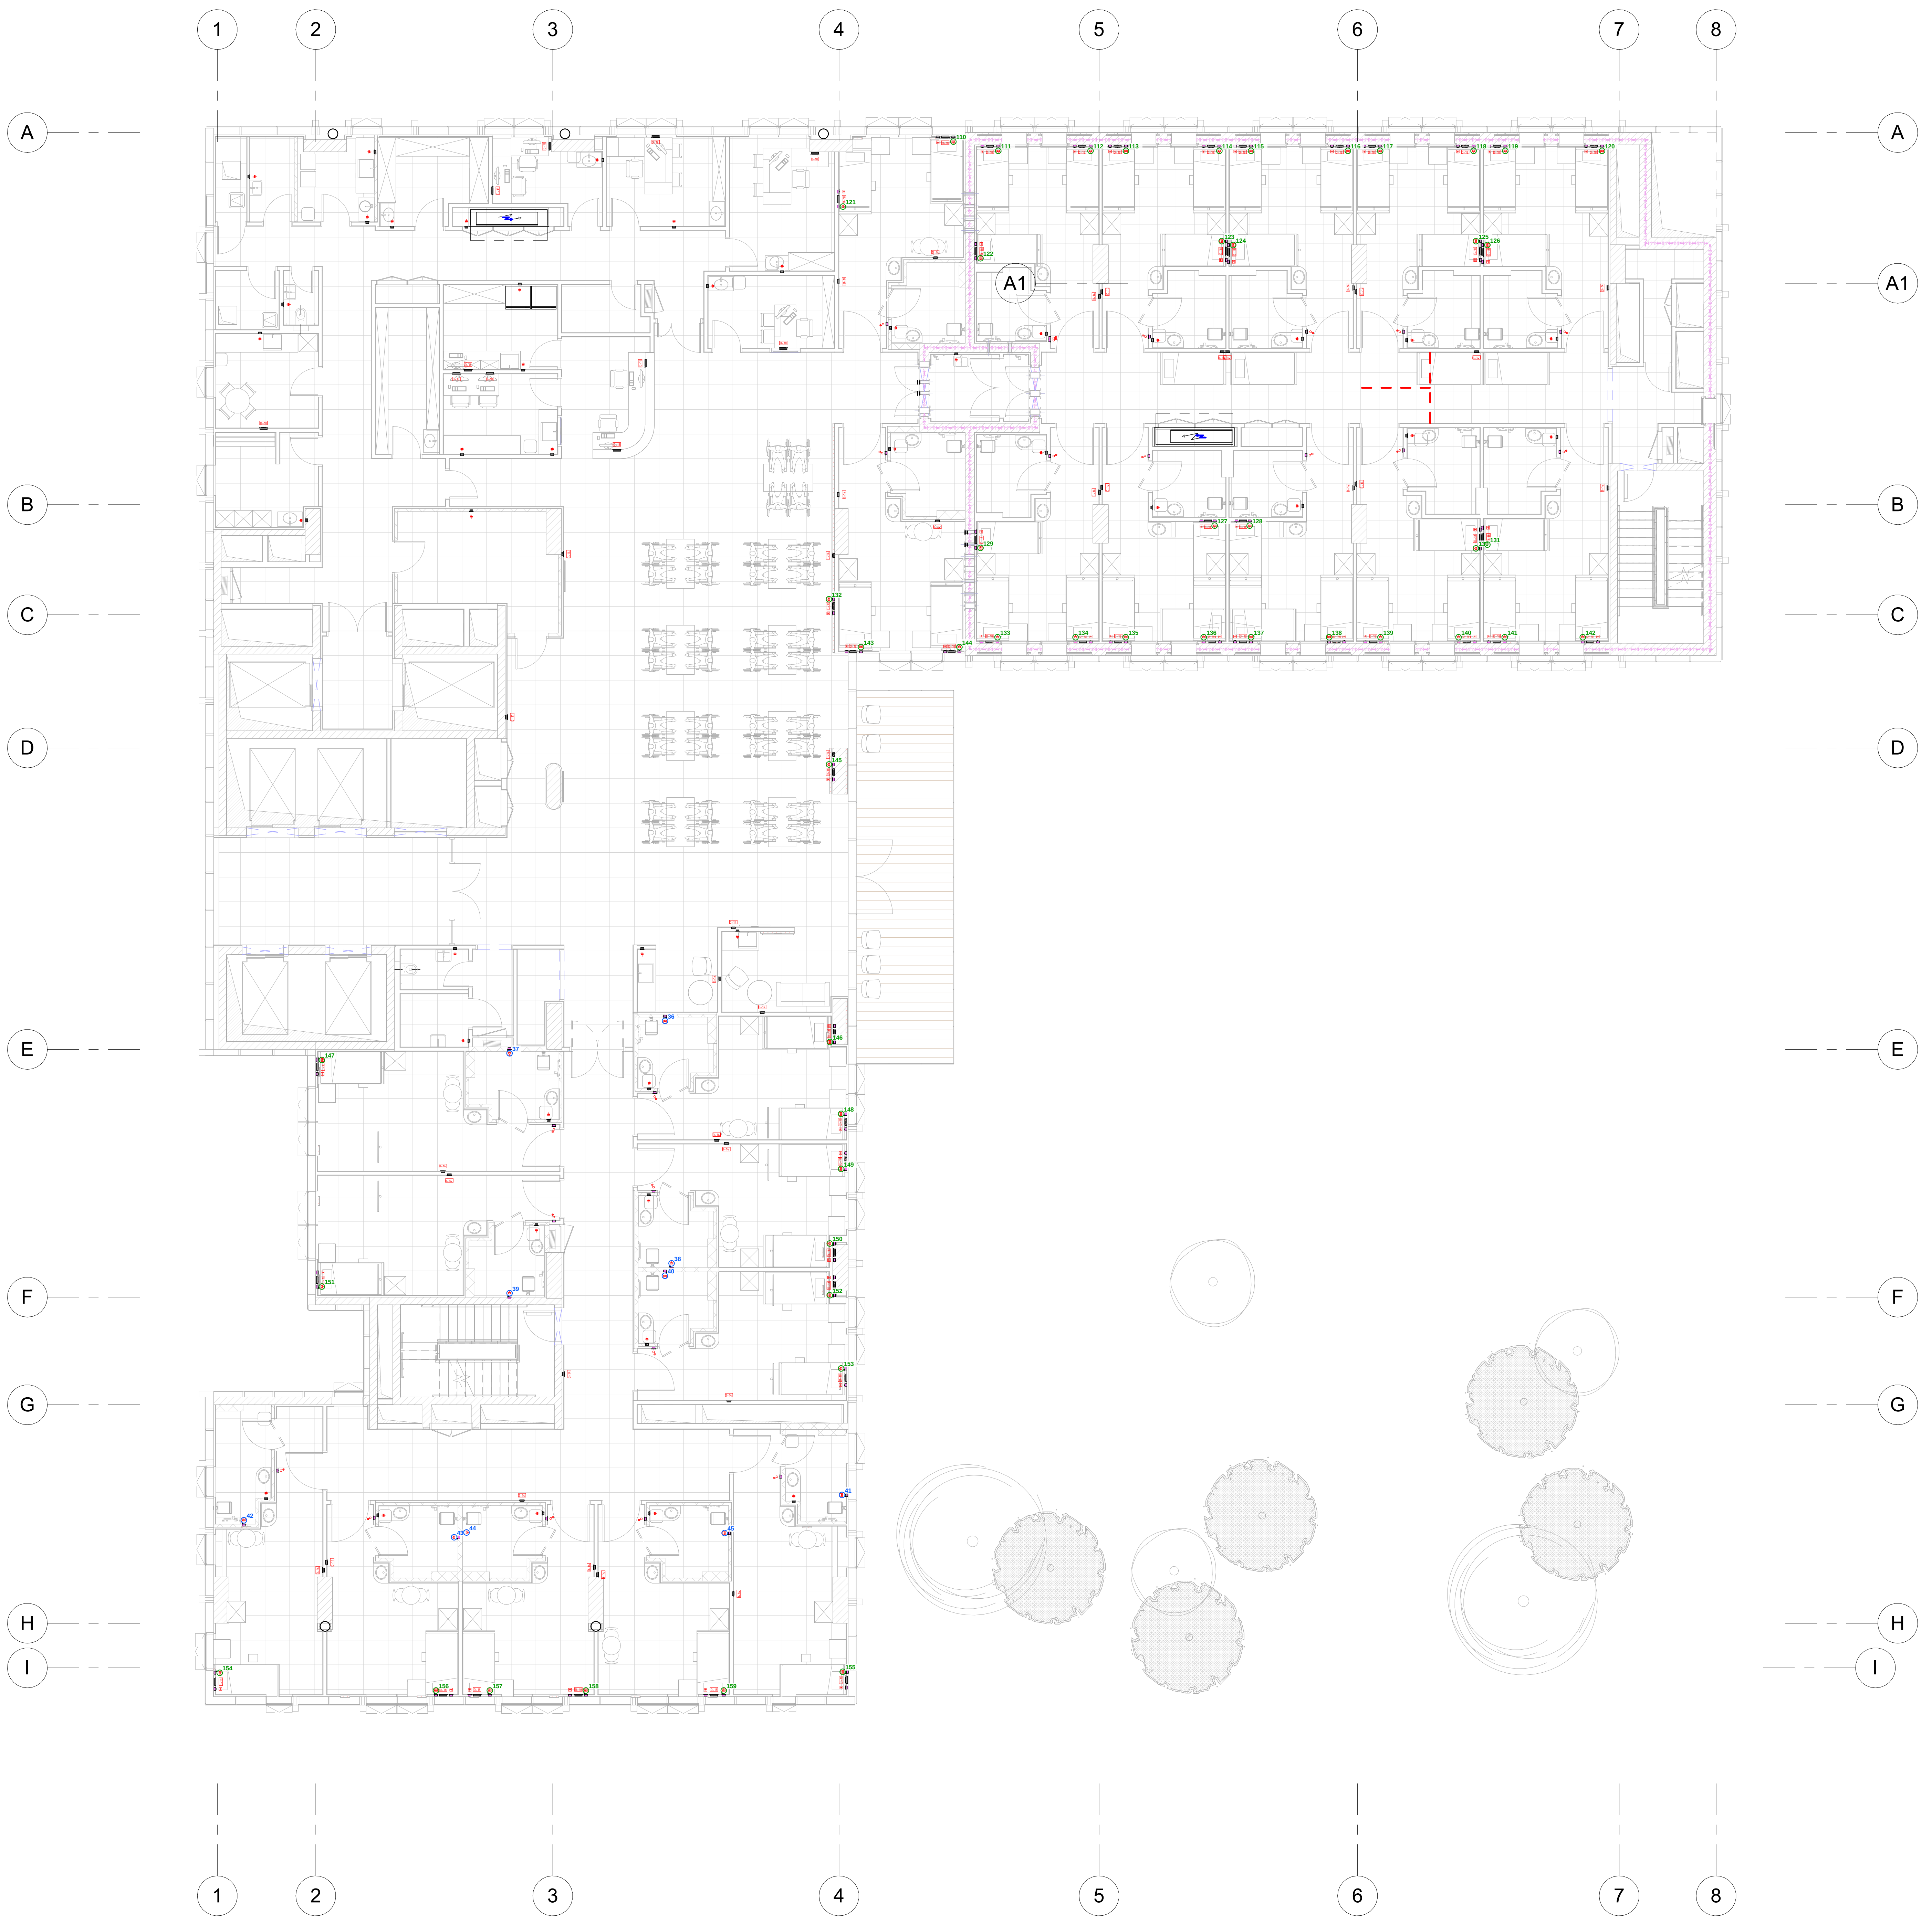

מהדורה	תאריך	תאור	שרטט	תפוצה
0	29.07.24	למכרז	אלכס.ד	

הקבלן אחראי להתאמת כל המידות והכמויות בתכניות ובבנין לפני.תחילת העבודה .כל אי תאום יש לברר עם המזמין אין למדוד על התכנית . התכנית היא רכושו הרעיוני של המתכנן.ואין לעשות בה כל שימוש ללא הסכמתו

מטרת התכנית) :מחק את המיותר(
☑לעיון ☐למכרז ☐לאישור ☐לביצוע

מהדורה:
0

מספר תכנית	מתכנן	נושא	מבנה/מתחם	מתקן

שם העבודה:

שם התכנית:
קומה - L05 תוכנית שקעים

מחלקת בינוי
ומערכות

מתכנן יועץ

מספר התוכנית:
GCN-ELC-L05-03

	תאריך	שם	חתימה	קנה מידה	מספרי מתכנן/יועץ
שרטט	08/10/20	אלכס.ד		1 : 100	
תיכנן	08/10/20	Designer			עבודה:
בדק	08/10/20	Checker			
אישר	08/10/20	Approver			גליון:

תכנית זו היא רכוש המזמין ואסורה בשימוש כולה או בחלקה לכל גורם אחד ,ללא אישור.

Autodesk Docs://Nesher-M17 (R23)/E-GCN-MAIN.rvt