Nurse call points | GREEN = bed / chair: 50 (#160-209) | BLUE = toilet: 10 (#46-55)

Floor plan L06 - שקעים

1 : 100

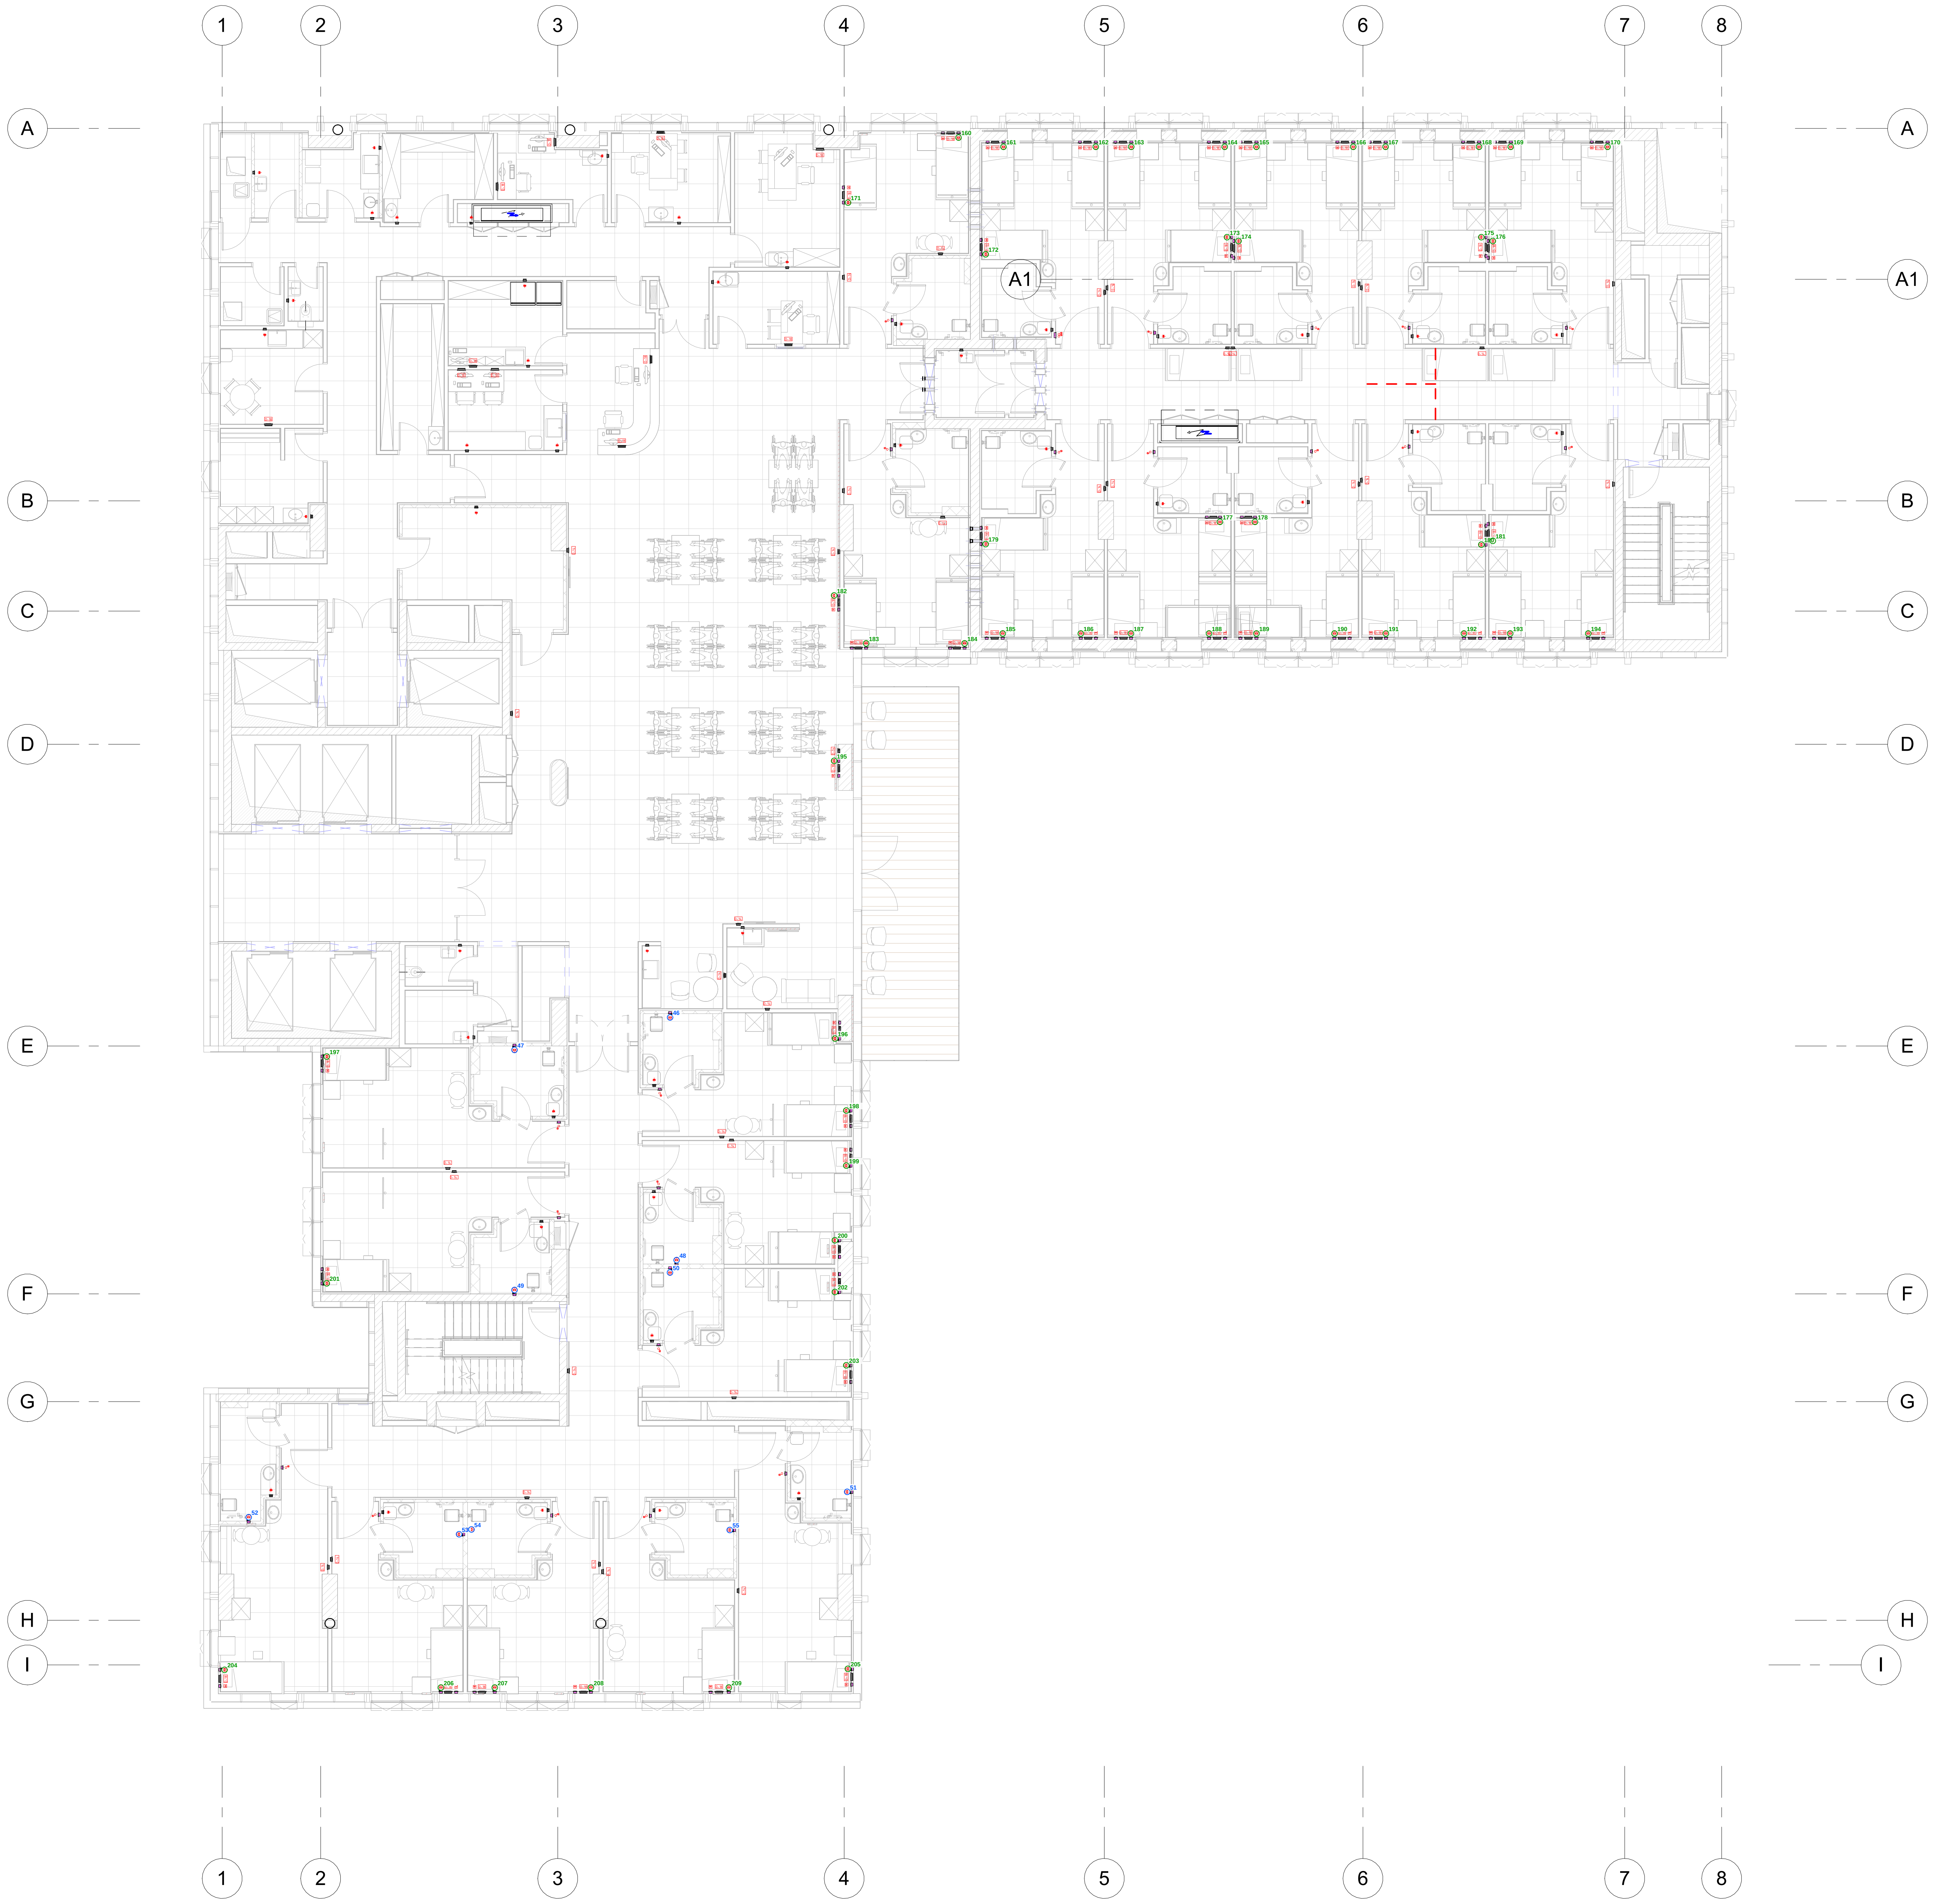

מהדורה	תאריך	תאור	שרטט	תפוצה
0	29.07.24	למכרז	אלכס.ר	

מטרת התכנית: (מחק את המיותר)
☑לעיון ☐למכרז ☐לאישור ☐לביצוע

הקבלן אחראי להתאמת כל המידות והכמויות בתכניות ובבנין לפני תחילת העבודה. כל אי תאום יש לברר עם המזמין. אין למדוד על התכנית. התכנית היא רכושו הרעיוני של המתכנן ואין לעשות בה כל שימוש ללא הסכמתו

מהדורה: 0

מספר תכנית	מתכנן	נושא	מבנה/מתחם	מתקן

מחלקת בינוי ומערכות

שם העבודה:

שם התכנית:
קומה - L06 תוכנית שקעים

מתכנן יועץ
קלינפלץ הנדסה בע"מ
יעוץ תכנון פיקוח ובדיקות מתקני חשמל

מספר התוכנית:
GCN-ELC-L06-03

	תאריך	שם	חתימה	קנה מידה	מספרי מתכנן/יועץ
שרטט	08/10/20	אלכס.ר		1 : 100	עבודה:
תיכנן	08/10/20	Designer			גליון:
בדק	08/10/20	Checker			
אישר	08/10/20	Approver			

תכנית זו היא רכוש המזמין ואסורה בשימוש כולה או בחלקה לכל גורם אחד ,ללא אישור.

Autodesk Docs://Nesher-M17 (R23)/E-GCN-MAIN.rvt