Nurse call points | GREEN = bed / chair: 50 (#210-259) | BLUE = toilet: 30 (#56-85)

Floor plan L07 - שקעים

1 : 100

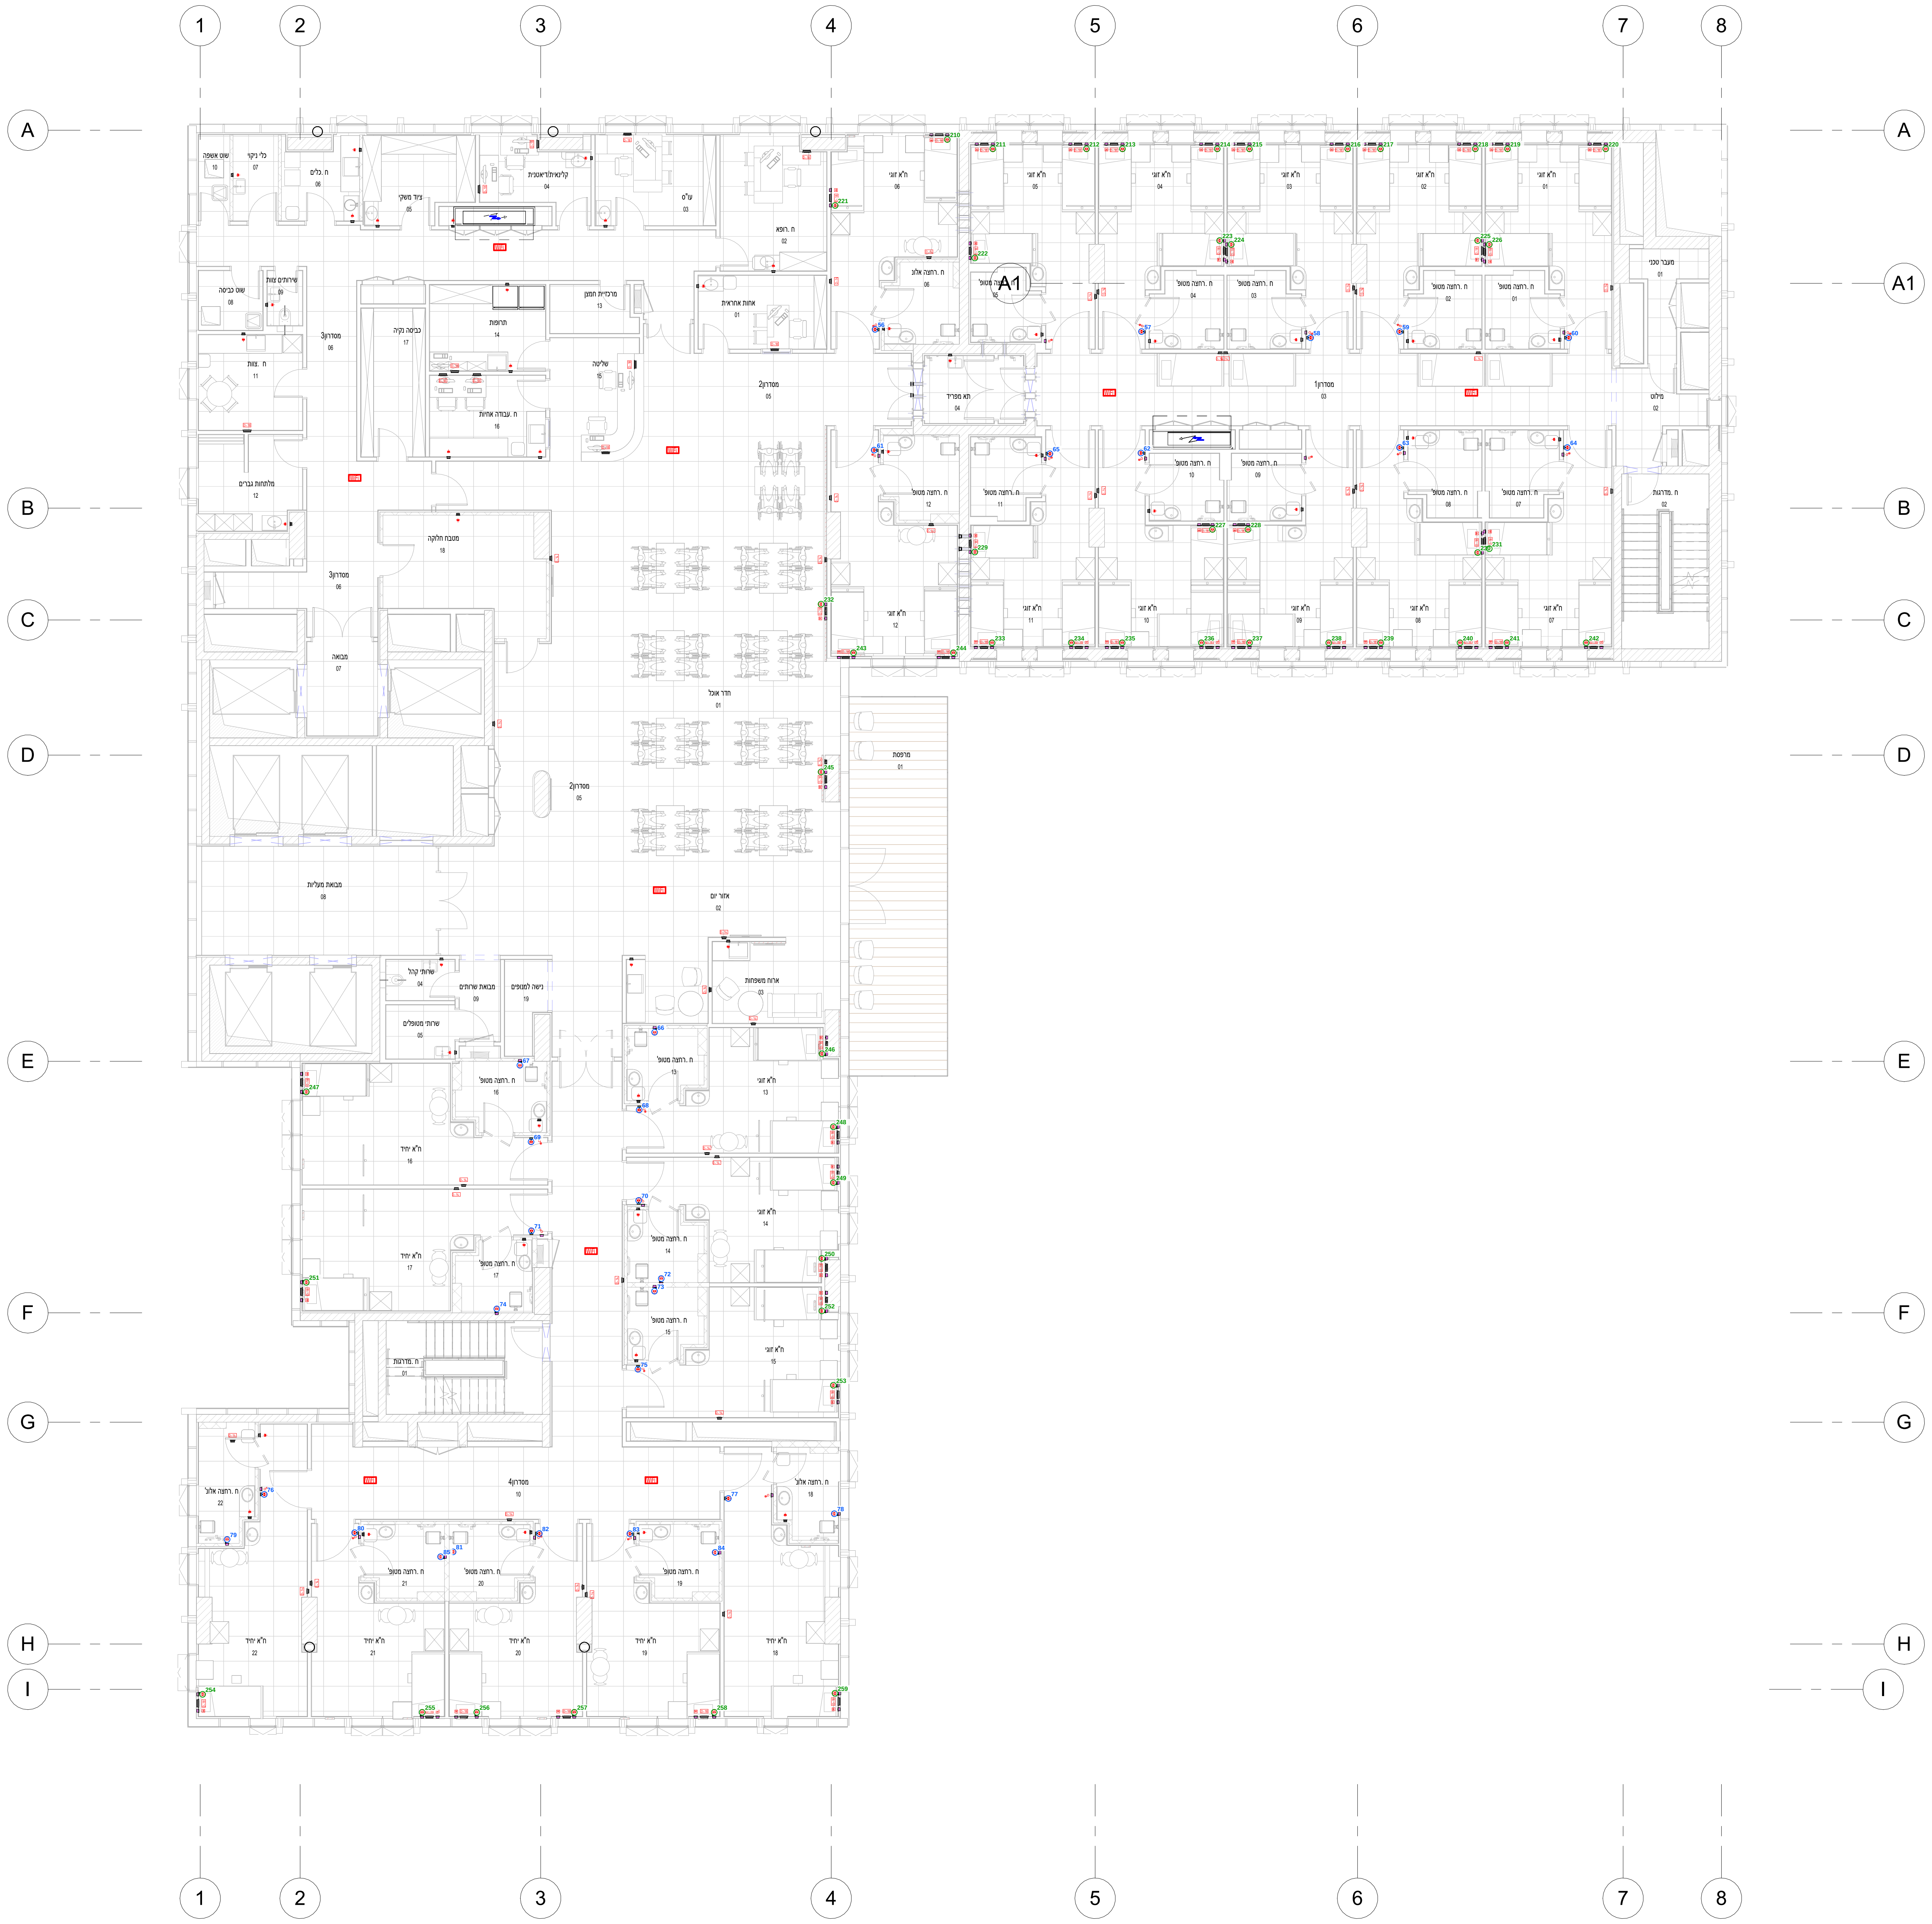

מהדורה	תאריך	תאור	שרטט	תפוצה
0	29.07.24	למכרז	אלכס.ר	

מטרת התכנית: (מחק את המיותר)
☑ לעיון ☐ למכרז ☐ לאישור ☐ לביצוע

הקבלן אחראי להתאמת כל המידות והכמויות בתכניות ובבנין לפני תחילת העבודה. כל אי תאום יש לברר עם המזמין. אין למדוד על התכנית. התכנית היא רכושו הרעיוני של המתכנן ואין לעשות בה כל שימוש ללא הסכמתו

מהדורה: 0

מספר תכנית	מתכנן	נושא	מבנה/מתחם	מתקן

מחלקת בינוי ומערכות

שם העבודה:

שם התכנית:
קומה - L07 תוכנית שקעים

מתכנן יועץ

קליינפלץ הנדסה בע"מ
יעוץ תכנון פיקוח ובדיקות מתקני חשמל

מספר התוכנית:
GCN-ELC-L07-03

	תאריך	שם	חתימה	קנה מידה	מספרי מתכנן/יועץ
שרטט	08/10/20	אלכס.ר		1 : 100	עבודה:
תיכנן	08/10/20	Designer			
בדק	08/10/20	Checker			גליון:
אישר	08/10/20	Approver			

תכנית זו היא רכוש המזמין ואסורה בשימוש כולה או בחלקה לכל גורם אחד, ללא אישור.

Autodesk Docs://Nesher-M17 (R23)/E-GCN-MAIN.rvt