Nurse call points | GREEN = bed / chair: 48 (#260-307) | BLUE = toilet: 37 (#86-122)

① Floor plan L08 - שקעים

1 : 100

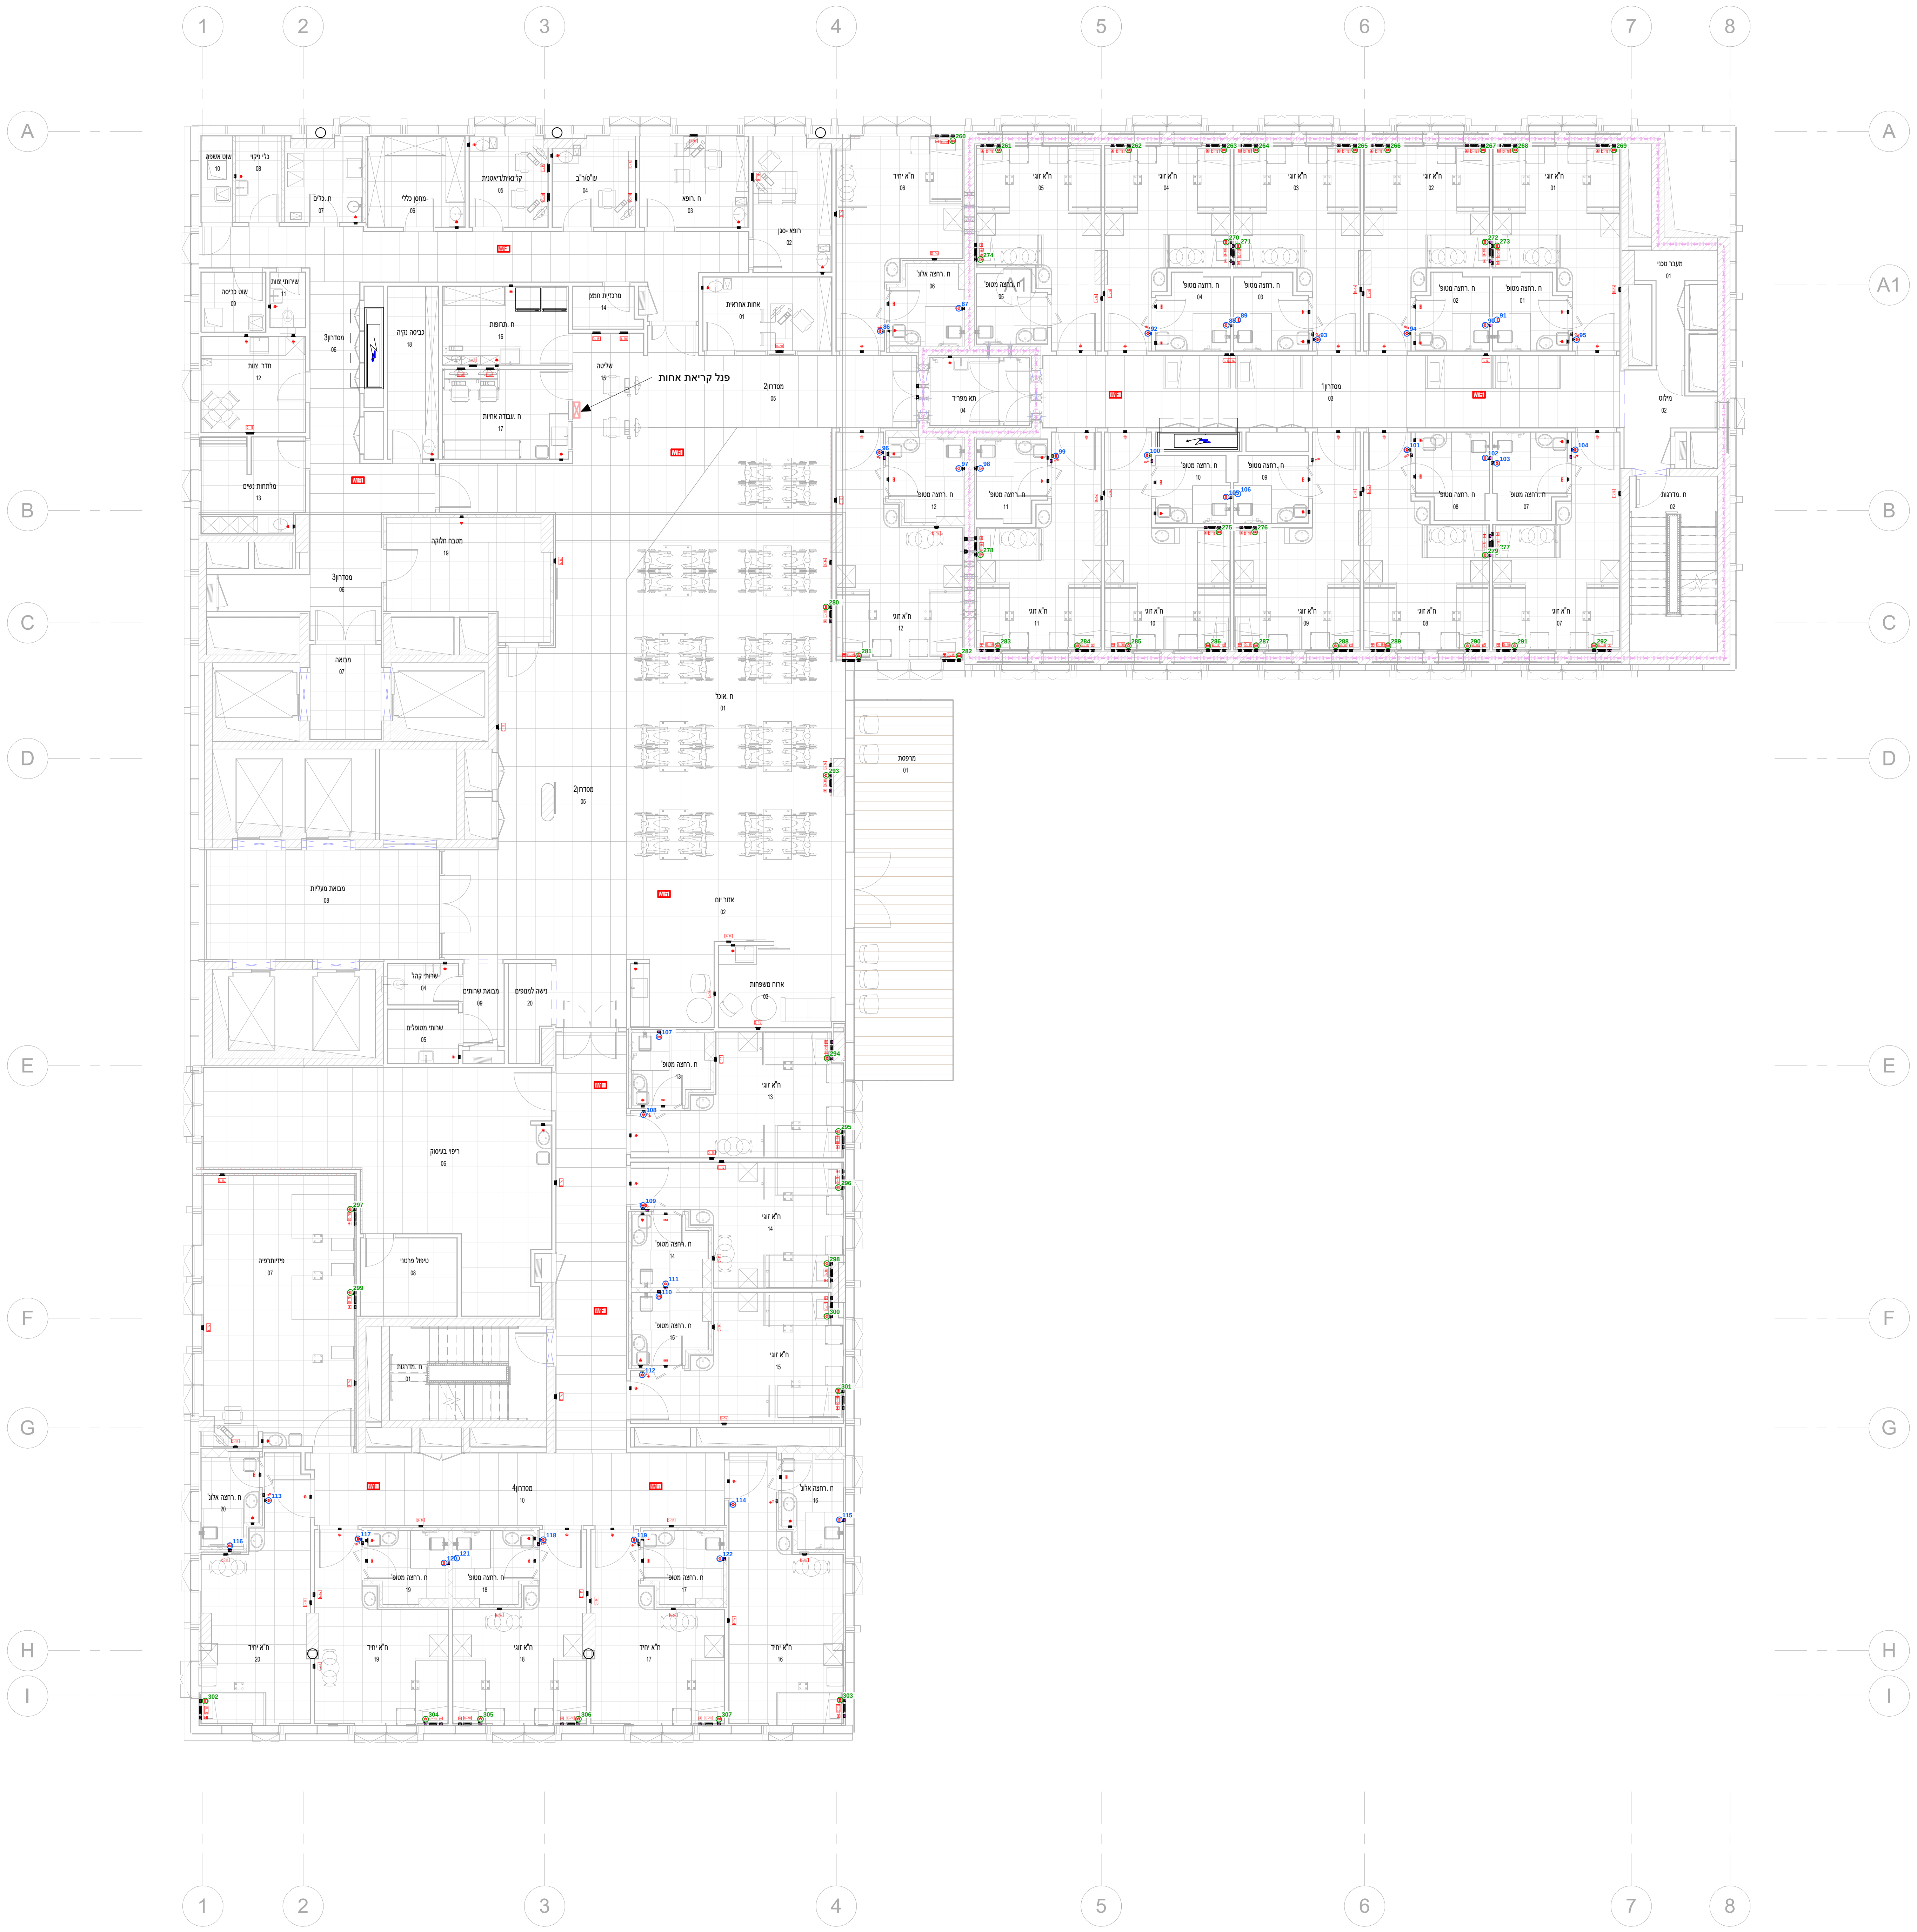

מהדורה	תאריך	תאור	שרטט	תפוצה
0	29.07.24	למכרז	אלכס.ר	

מטרת התכנית) :מחק את המיותר)

☑ לעיון ☐ למכרז ☐ לאישור ☐ לביצוע

הקבלן אחראי להתאמת כל המידות והכמויות בתכניות ובבנין לפני.תחילת העבודה .כל אי תאום יש לברר עם המזמין אין למדוד על התכנית . התכנית היא רכושו הרעיוני של המתכנן.ואין לעשות בה כל שימוש ללא הסכמתו

מהדורה: 0

מספר תכנית	מתכנן	נושא	מבנה/מתחם	מתקן

שם העבודה:

שם התכנית:

קומה - L08 תוכנית שקעים

מתכנן יועץ

קליינפלץ הנדסה בע"מ

יעוץ תכנון פיקוח ובדיקות מתקני חשמל

מספר התוכנית:

GCN-ELC-L08-03

	תאריך	שם	חתימה
שרטט	08/10/20	אלכס.ר	
תיכנן	08/10/20	Designer	
בדק	08/10/20	Checker	
אישר	08/10/20	Approver	

קנה מידה: 1 : 100

מספרי מתכנן/יועץ

עבודה:

גליון:

Autodesk Docs://Nesher-M17 (R23)/E-GCN-MAIN.rvt

תכנית זו היא רכוש המזמין ואסורה בשימוש כולה או בחלקה לכל גורם אחד ,ללא אישור.