Nurse call points | GREEN = bed / chair: 46 (#308-353) | BLUE = toilet: 19 (#123-141)

Floor plan L09 - שקעים
1 : 100

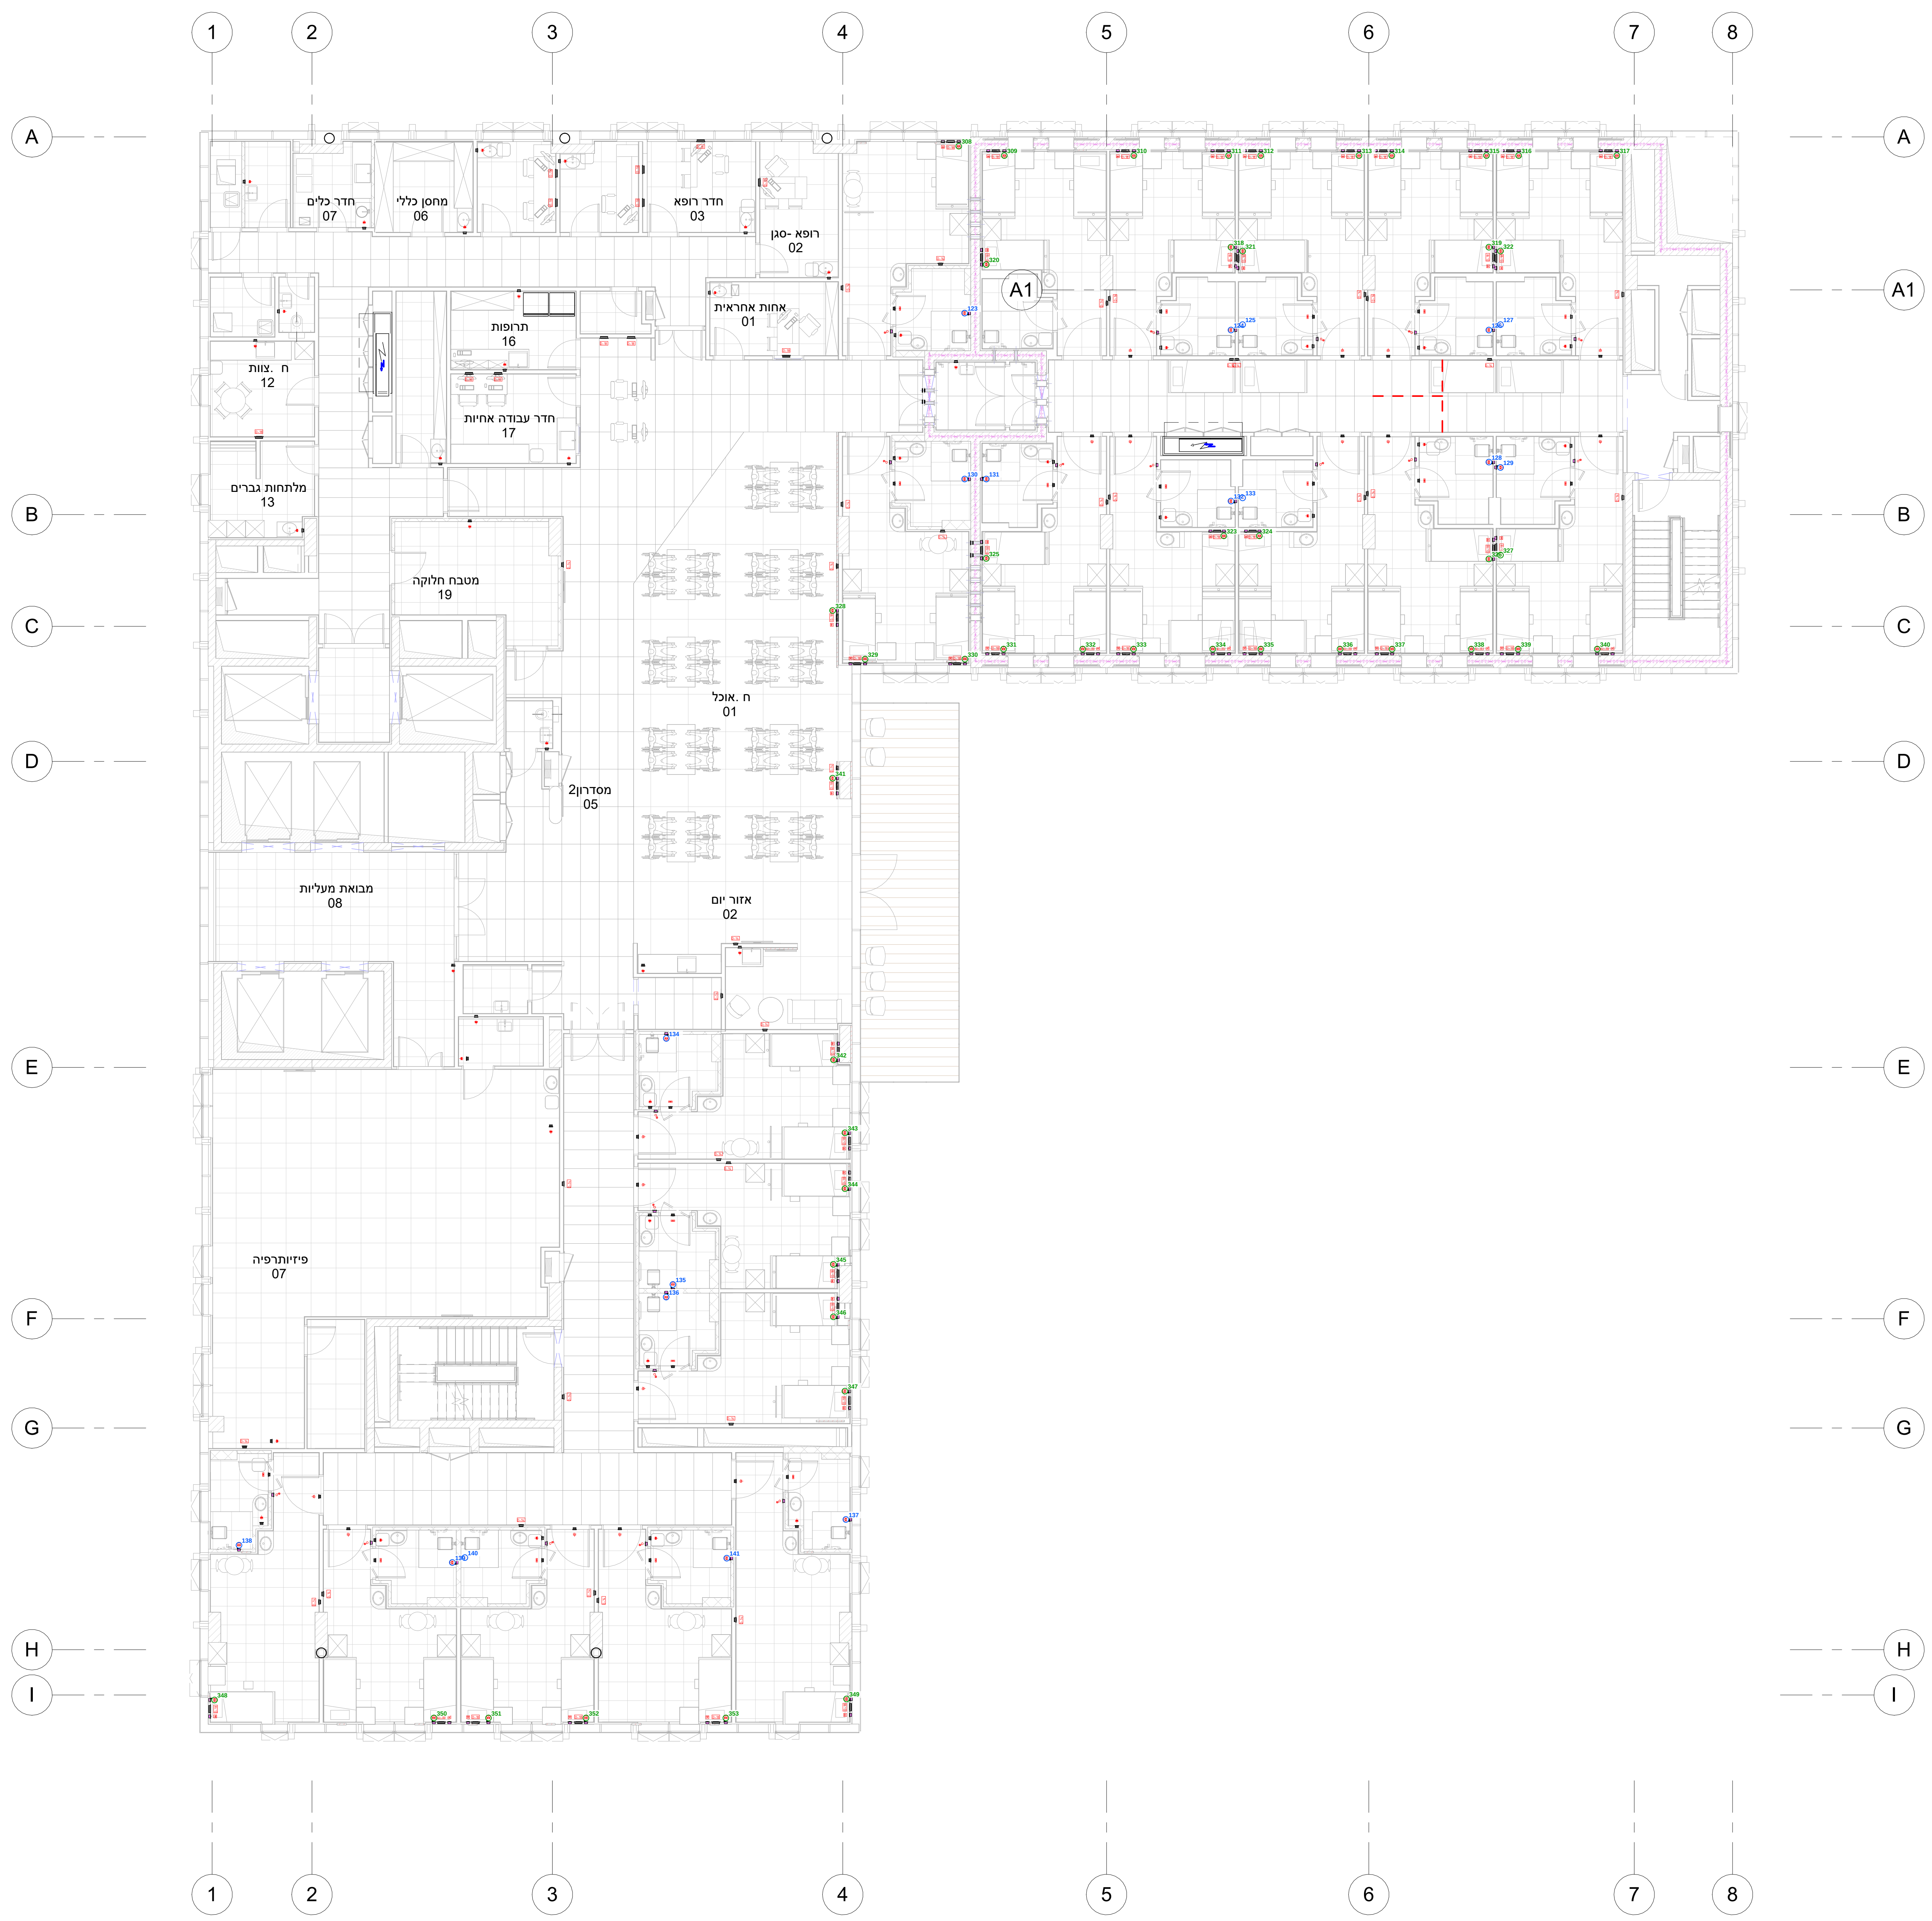
1
2
3
4
5
6
7
8
A
A1
B
C
D
E
F
G
H
I
חדר כלים
07
מחסן כללי
06
חדר רופא
03
רופא -סגן
02
אחות אחראית
01
תרופות
16
ח .צוות
12
חדר עבודה אחיות
17
מלתחות גברים
13
מטבח חלוקה
19
ח .אוכל
01
מסדרון2
05
מבואת מעליות
08
אזור יום
02
פיזיותרפיה
07

מהדורה	תאריך	תאור	שרטט	תפוצה
0	29.07.24	למכרז	אלכס.ר	

מטרת התכנית) :מחק את המיותר(
☑ לעיון ☐ למכרז ☐ לאישור ☐ לביצוע

הקבלן אחראי להתאמת כל המידות והכמויות בתכניות ובבנין לפני.תחילת העבודה .כל אי תאום יש לברר עם המזמין אין למדוד על התכנית . התכנית היא רכושו הרעיוני של המתכנן.ואין לעשות בה כל שימוש ללא הסכמתו

מהדורה:
0

מספר תכנית	מתכנן	נושא	מבנה/מתחם	מתקן

שם העבודה:

שם התכנית:
קומה - L09 תוכנית שקעים

מתכנן יועץ

מספר התוכנית:
GCN-ELC-L09-03

	תאריך	שם	חתימה
שרטט	08/10/20	אלכס.ר	
תיכנן	08/10/20	Designer	
בדק	08/10/20	Checker	
אישר	08/10/20	Approver	

קנה מידה
1 : 100

מספרי מתכנן/יועץ
עבודה:
גליון:

תכנית זו היא רכוש המזמין ואסורה בשימוש כולה או בחלקה לכל גורם אחד ,ללא אישור.

Autodesk Docs://Nesher-M17 (R23)/E-GCN-MAIN.rvt