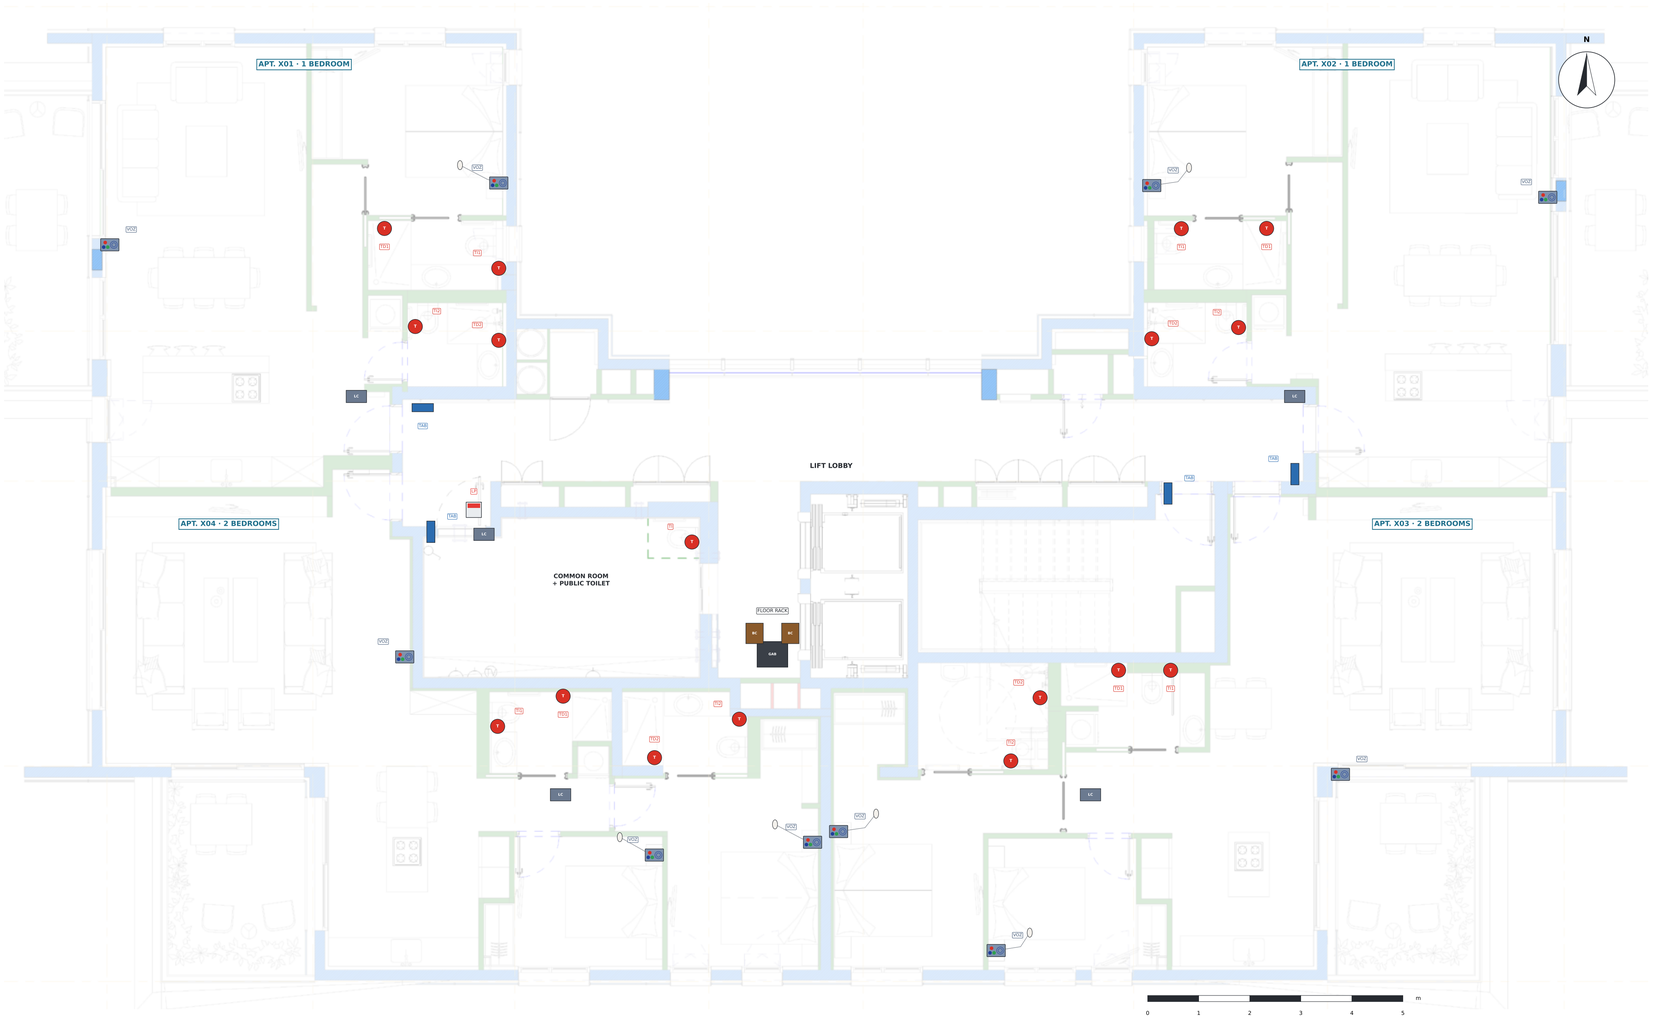


DEVICES · EQUIPOS · דוגמ

- **TAB** · Door tablet (iPad / Android) – call and voice, h 1.40 m
  Door tablet – call and voice · טאבלט כניסה – שיחה וקול · מכשיר טלפאנו – כניסה
- **VOZ** · Voice panel with buttons ACE82182451 – living room and bedrooms, h 1.20–1.30 m
  Voice panel with buttons – living room and bedrooms · פנל קריאה עם כפתורים – סלון וחדרי שינה · פנל כפתורים – סלון וחדרים
- Call pear next to the bed (bedrooms)
  Call pear next to the bed (bedrooms) · אגסון ליד המיטה בחדרי שינה · אגסון ליד המיטה
- **TI / TD** · Pull-cord ACE40320303W – toilet and shower, h 1.85 m
  Pull-cord – toilet and shower, h 1.85 m · חבל משיכה לשירותים ולמקלחת – גובה 1.85 מ · חבל משיכה לשירותים ולמקלחת – גובה 1.85 מ
- **LP** · Corridor light ACE41020309 – above each public toilet door
  Corridor light – above each public toilet door · מנורת מסדרון מעל דלת כל שירותים ציבוריים · מנורת מסדרון מעל דלת כל שירותים ציבוריים
- **LC** · LCom ACE71610003 – apartment hub (ceiling)
  LCom – apartment hub (ceiling) · LCom – נקודת ריכוז בתוך הדירה (בתקרה) · LCom – נקודת ריכוז בתוך הדירה (בתקרה)
- **BC** · BoxCom ACE70810000 – bus hub for several apartments (ceiling)
  BoxCom – bus hub for several apartments (ceiling) · BoxCom – נקודת חיבור לכמה דירות · BoxCom – נקודת חיבור לכמה דירות
- **GAB** · 12U floor rack: D-Link DES-1210-28P PoE switch (24 PoE ports)
  Floor rack: D-Link DES-1210-28P PoE switch · מתלה עמוד: D-Link DES-1210-28P מתג PoE · מתלה עמוד: D-Link DES-1210-28P מתג PoE


QUANTITIES PER FLOOR × 8 FLOORS

Code	Device	Per floor	8 floors
TAB	Door tablet	4	32
VOZ	Voice panel with buttons	10	80
TI/TD	Pull-cord (toilet + shower)	17	136
LP	Corridor light (public toilet)	1	8
LC	LCom	5	40
BC	BoxCom	2	16
SW	PoE switch	1	8

NOTES · NOTAS

1. Base: architectural plan L5 (typical floor) – all 8 floors are identical: 4 apartments per floor, 32 in total.
2. Apartments x01 and x02: 1 bedroom, living room with kitchen and 2 bathrooms. Apartments x03 and x04: 2 bedrooms and 2 bathrooms.
3. Tablet at the door of each apartment (iPad / Android) to call and talk to the nurse.
4. Voice panel with buttons (ACE82182451) in the living room and in each bedroom; in bedrooms, with a pear next to the bed.
5. Pull-cords (ACE40320303W) at the toilet and shower of every bathroom, at 1.85 m.
6. One public toilet per floor in the common room: pull-cord + corridor light above the door. With the 2 on GF, 10 public toilets in total.
7. Floor rack next to the lifts with the D-Link DES-1210-28P PoE switch; the 2 BoxComs go on the ceiling next to it.
8. Locations per the client's marks on plan L2 (nt = voice panel, tab = tablet): see sheet 03.

MOUNTING HEIGHTS

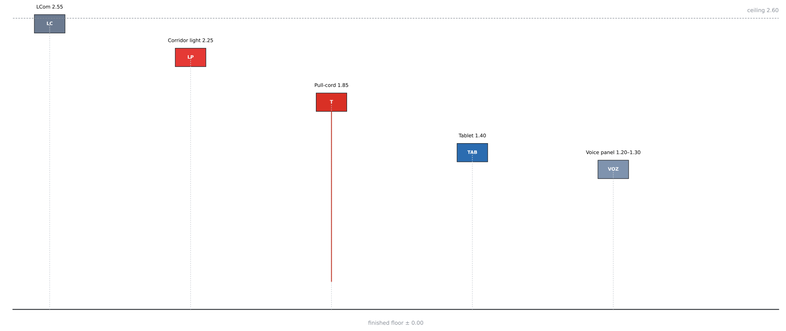

שירותים קריאת אחות



Pull-cord

טבלט אנדרואיד קריאת אחות



Door tablet (iPad / Android)

מנורה קריאת אחות



Corridor light

פנל קריאת אחות



Voice panel with buttons

MIGDALEI YAM A TIJON · ASSISTED LIVING

Nurse call – GF + 8 floors · 32 apartments

System: ACE BG · Advantecnia Prepared by: Telab International

TYPICAL FLOOR F1–F8 · NURSE CALL

SCALE · ESCALA	DATE · FECHA	REV	SHEET
1:60	15/10/2026	B	01

Base: architect's plan L5 (Massad Oz / Triplet) · dimensions in m

A1 format · Rev. B – on the real plan

שירותים קריאת אחות



Pull-cord

Code	**ACE40320303W**
Location	Toilet and shower of every bathroom and the 10 public toilets
Height	**1.85 m**
Quantity	**138**

1

טבלט אנדרואיד קריאת אחות



Door tablet (iPad / Android)

Code	**Advantecnia TV**
Location	In the lobby, next to each apartment door
Height	**1.40 m**
Quantity	**32**

2

מנורה קריאת אחות



Corridor light

Code	**ACE41020309**
Location	Above each public toilet door
Height	**2.25 m**
Quantity	**10**

3

NOTES · NOTAS

1. Reference photos from ACE BG / Advantecnia, with their title.

2. Pull-cord: red cord with handle, reachable from the floor.

3. The door tablet calls and talks to the nurse.

4. The corridor light turns on when someone calls from the public toilet.

5. The panel has a red call button, a blue (left) and a green (right) button and a speaker to talk.

6. Chain: devices → LCom (radial) → BoxCom (bus) → PoE switch → server.

7. The desk phone goes straight to the PoE switch.

פנל קריאת אחות



Voice panel with buttons

Code	**ACE82182451**
Location	Living room and each bedroom (with pear in bedrooms)
Height	**1.20–1.30 m**
Quantity	**80**


4



Desk phone (Android)

Code	**Grandstream**
Location	Nurse desk on GF · PoE straight to the switch
Height	**on the desk**
Quantity	**1**


5

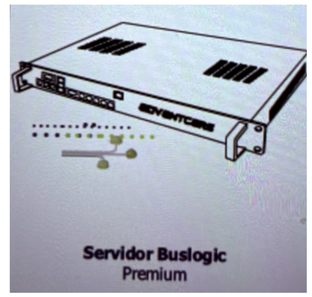

Buslogic Premium server

Code	**Advantcare**
Location	Main GF rack
Height	**in rack**
Quantity	**1**


6

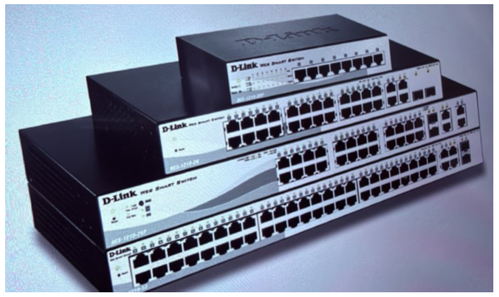

24-port PoE switch

Code	**D-Link DES-1210-28P**
Location	Rack on each floor and GF
Height	**in rack**
Quantity	**9**

7

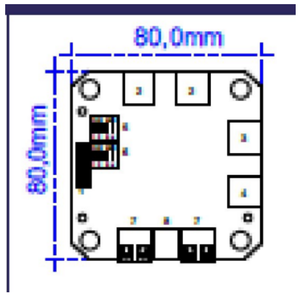

LCom – radial hub

Code	**ACE71610003**
Location	Ceiling of each apartment and public toilets
Height	**2,55 m**
Quantity	**41**

8



BoxCom – bus hub

Code	**ACE70810000**
Location	Ceiling next to the rack: joins several apartments
Height	**2,55 m**
Quantity	**17**

9

DESK PHONE – WHICH COLOUR SHOWS

Alarm (pull-cord / SOS)	**Red**
Green button once: presence	**Green**
Green button again: cancels call or alarm	Cleared
Blue button: doctor call (blue call)	**Blue**
Voice call	**Yellow / orange**

MIGDALEI YAM A TIJON · ASSISTED LIVING

Nurse call – GF + 8 floors · 32 apartments


System: ACE BG · Advantecnia Prepared by: Telab International

SYSTEM DEVICES

SCALE · ESCALA	DATE · FECHA	REV	SHEET
S/E	**15/10/2026**	**B**	**02**

Base: architect's plan L5 (Massad Oz / Triplet) · dimensions in m

A1 format · Rev. B – on the real plan

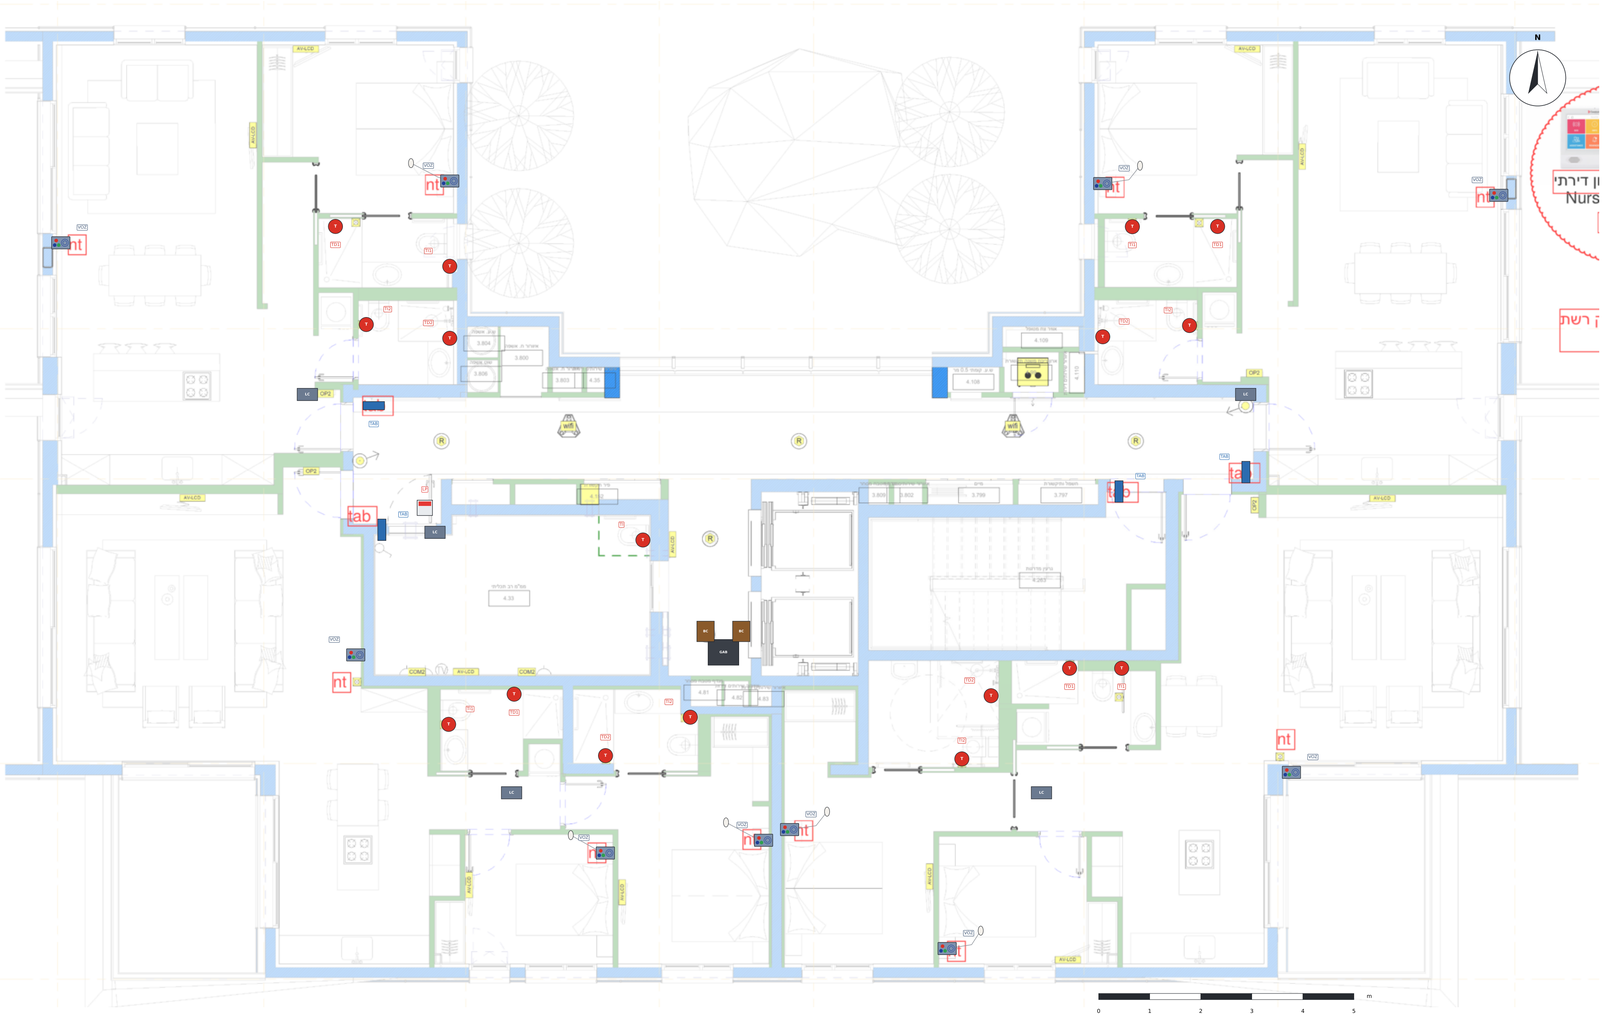

NOTES · NOTAS

1. Background: the client's IT plan L2 with their red marks:
«nt» = voice panel and «tab» = door tablet.

2. On top, in colour: the devices of this proposal.
Each panel and tablet is where the client marked it.

3. The yellow ⊠ squares in the L2 bathrooms
are the pull-cords (toilet and shower).

4. The 4 tablets are in the lobby, next to each
apartment door, as in the «tab» marks.

5. Plans L2 and L5 (base of this proposal) share
the same structure; L5 is the typical floor for floors 1 to 8.

DEVICES · EQUIPOS · דגמ

TAB · Door tablet (iPad / Android) – call and voice, h 1.40 m
Door tablet – call and voice · טבלט אנדרואיד קריאת אחות – כפתור קריאה

VOZ · Voice panel with buttons ACE82182451 – living room and bedrooms, h 1.20–1.30 m
Voice panel with buttons – living room and bedrooms · פנל קריאת אחות – כפתורי לחץ ליחה

Call pear next to the bed (bedrooms)
Call pear next to the bed (bedrooms) · מנורה ליד מיטת אם

T / TD · Pull-cord ACE40320303W – toilet and shower, h 1.85 m
Pull-cord – toilet and shower, h 1.85 m · חבל משיכה לחדר שירותים – לחדר מקלחת

LP · Corridor light ACE41020309 – above each public toilet door
Corridor light – above each public toilet door · מנורה מיוחדת לחדר שירותים – מעל כל דלת

שירותים קריאת אחות



Pull-cord

טבלט אנדרואיד קריאת אחות



Door tablet (iPad / Android)

מנורה קריאת אחות



Corridor light

פנל קריאת אחות



Voice panel with buttons

MIGDALEI YAM A TIJON · ASSISTED LIVING

Nurse call – GF + 8 floors · 32 apartments


System: ACE BG · Advantecnia Prepared by: Telab International

CLIENT MARKS (PLAN L2) AND PROPOSAL

SCALE · ESCALA	DATE · FECHA	REV	SHEET
1:60	**15/10/2026**	**B**	**03**

Base: architect's plan L5 (Massad Oz / Triplet) · dimensions in m

A1 format · Rev. B – on the real plan

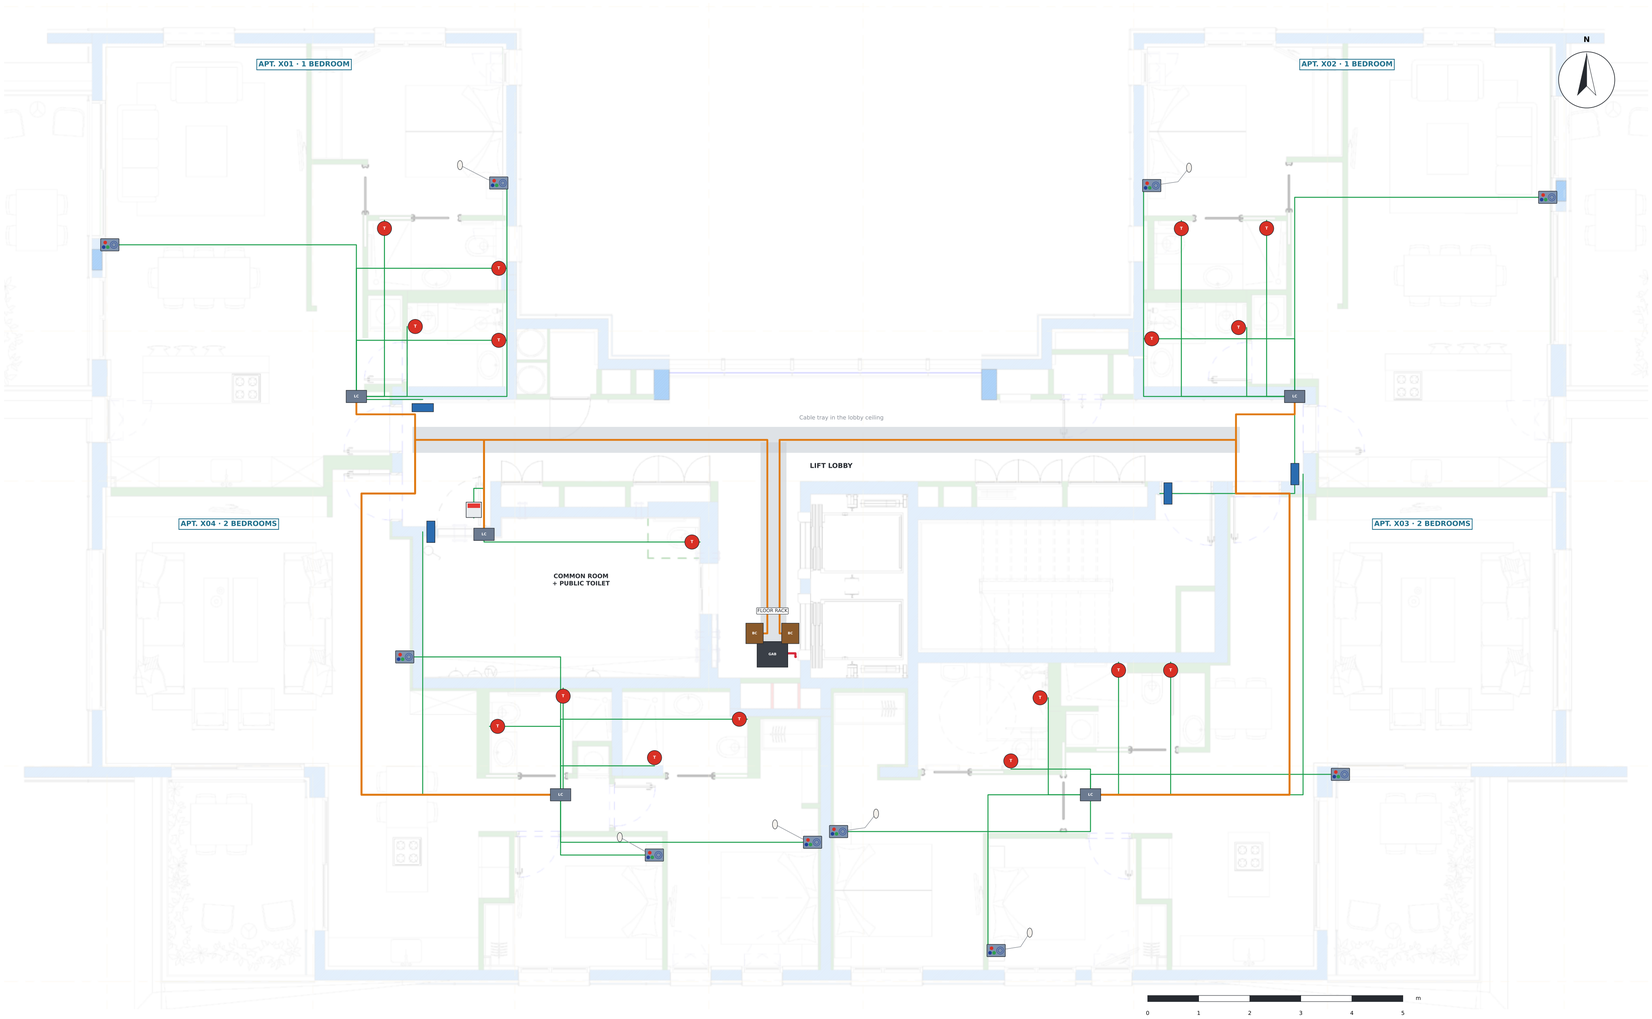

WIRING · CABLEADO · סוגיות

- Cat6 radial: each device → its apartment LCom
  Cat6 radial: each device → apartment LCom · Cat6 רדיאלי: כל התקן → LCom הדירה שלו
- Cat6 / Cat7 chain: LCom → LCom → ceiling BoxCom
  Cat6 / Cat7 chain: LCom → LCom → BoxCom · Cat6 / Cat7 שרשרת: LCom ← LCom ← BoxCom
- Cat6A / Cat7 network: BoxCom → PoE switch → riser → GF server
  Cat6A / Cat7 network: BoxCom → switch → riser → GF server · Cat6A / Cat7 רשת: BoxCom ← נתב ← רייזר ← שרת

TYPICAL FLOOR LENGTHS (no spare)

Cat6 radial inside the apartments	**183 m**
Cat6 / Cat7 chain LCom → BoxCom	**80 m**
Cat6A / Cat7 rack and riser	**7 m**

NOTES · NOTAS

1. Each device runs radially (Cat6) to its apartment LCom, in the hall ceiling.
2. The LComs are chained along the lobby tray to the ceiling BoxComs next to the rack: x01 → x04 → common room → BoxCom 1 · x02 → x03 → BoxCom 2.
3. The BoxComs drop to the PoE switch in the rack; the switch runs up the Cat6A / Cat7 riser to the GF server.
4. Everything is PoE: no 230 V needed for the apartment devices.

NOTES · NOTAS

1. Base: architectural plan L5 (typical floor) – all 8 floors are identical: 4 apartments per floor, 32 in total.
2. Apartments x01 and x02: 1 bedroom, living room with kitchen and 2 bathrooms. Apartments x03 and x04: 2 bedrooms and 2 bathrooms.
3. Tablet at the door of each apartment (iPad / Android) to call and talk to the nurse.
4. Voice panel with buttons (ACE82182451) in the living room and in each bedroom; in bedrooms, with a pear next to the bed.
5. Pull-cords (ACE40320303W) at the toilet and shower of every bathroom, at 1.85 m.
6. One public toilet per floor in the common room: pull-cord + corridor light above the door. With the 2 on GF, 10 public toilets in total.
7. Floor rack next to the lifts with the D-Link DES-1210-28P PoE switch; the 2 BoxComs go on the ceiling next to it.
8. Locations per the client's marks on plan L2 (nt = voice panel, tab = tablet): see sheet 03.

MIGDALEI YAM A TIJON · ASSISTED LIVING

Nurse call – GF + 8 floors · 32 apartments


System: ACE BG · Advantecnia Prepared by: Telab International

TYPICAL FLOOR F1–F8 · WIRING

SCALE · ESCALA	DATE · FECHA	REV	SHEET
1:60	15/10/2026	B	04

Base: architect's plan L5 (Massad Oz / Triplet) · dimensions in m

A1 format · Rev. B – on the real plan

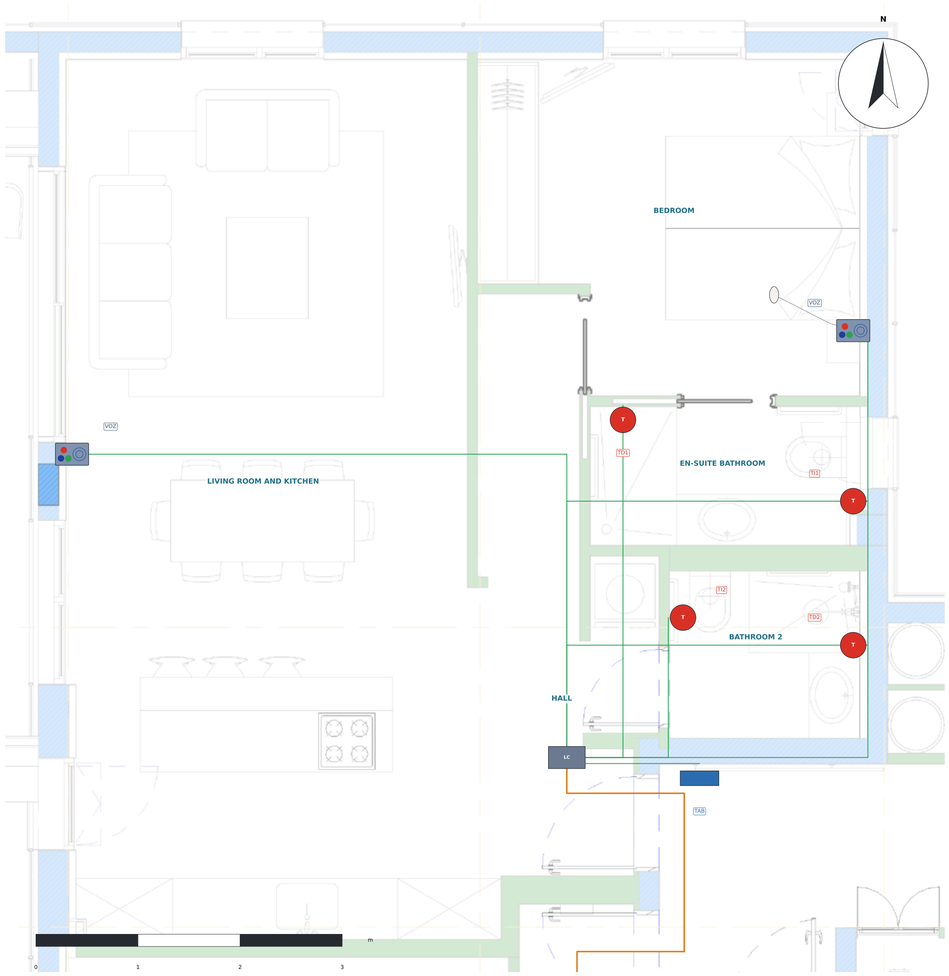

APARTMENT DEVICES

ID	Device	Room	Height
TAB	Door tablet	Hall	1.40 m
VOZ-S	Voice panel with buttons	Living room and kitchen	1,30 m
VOZ-D	Voice panel with buttons + pear	Bedroom	1,20 m
TI1	Pull-cord	En-suite bathroom	1.85 m
TD1	Pull-cord	En-suite bathroom	1.85 m
TI2	Pull-cord	Bathroom 2	1.85 m
TD2	Pull-cord	Bathroom 2	1.85 m
LCOM	LCom ACE71610003	Hall	2,55 m

SYMBOLS · SÍMBOLOS · סימנים

TAB · Door tablet (iPad / Android) – call and voice, h 1.40 m
Door tablet – call and voice · · הגדרה: דיור – מסמכים וחלאנס

VOZ · Voice panel with buttons ACE82182451 – living room and bedrooms, h 1.20–1.30 m
Voice panel with buttons – living room and bedrooms · · הגדרה: לוח קולי עם כפתורים – סלון וחדרי שינה

Call pear next to the bed (bedrooms)
Call pear next to the bed (bedrooms) · · הגדרה: דיור כאריס ליד המיטה

TI / TD · Pull-cord ACE40320303W – toilet and shower, h 1.85 m
Pull-cord – toilet and shower, h 1.85 m · · הגדרה: חבל, מתלה לשירותים ולמקלחת – לגובה 1.85 מ'

LP · Corridor light ACE41020309 – above each public toilet door
Corridor light – above each public toilet door · · הגדרה: מחוברת מחוץ לדלת – בדלת הציבורית

LC · LCom ACE71610003 – apartment hub (ceiling)
LCom – apartment hub (ceiling) · · הגדרה: LCom – (בתקרה)

BC · BoxCom ACE70810000 – bus hub for several apartments (ceiling)
BoxCom – bus hub for several apartments (ceiling) · · הגדרה: BoxCom – (בתקרה) תיבה המחבר מספר יחידות

NOTES · NOTAS

1. Apartment x02 mirrors x01 (same devices).
2. Tablet in the lobby, next to the front door (client's «tab» mark).
3. Voice panel in the living room and in the bedroom (with pear next to the bed).
4. 2 bathrooms: pull-cord at the toilet and at the shower of each (4 pull-cords).
5. Everything runs radially in Cat6 to the hall LCom.

שירותים קריאת אחות



Pull-cord

טבלט אנדרואיד קריאת אחות



Door tablet (iPad / Android)

מנורה קריאת אחות



Corridor light

פנל קריאת אחות



Voice panel with buttons

MIGDALEI YAM A TIJON · ASSISTED LIVING

Nurse call – GF + 8 floors · 32 apartments

System: ACE BG · Advantecnia Prepared by: Telab International

1-BEDROOM APT. (x01 / x02)

SCALE · ESCALA	DATE · FECHA	REV	SHEET
1:30	15/10/2026	B	05

Base: architect's plan LS (Massad Oz / Triplet) · dimensions in m

A1 format · Rev. B – on the real plan

MIGDALEI YAM A TIJON · ASSISTED LIVING

Nurse call – GF + 8 floors · 32 apartments


System: ACE BG · Avvantecnia Prepared by: Talab International

2-BEDROOM APT. (x04 / x03)

SCALE · ESCALA	DATE · FECHA	REV	SHEET
1:35	15/10/2026	B	06

A1 format - Rev. B – on the real plan

Base: architect's plan LS (Masséd OZ / Tigavi) - dimensions in m

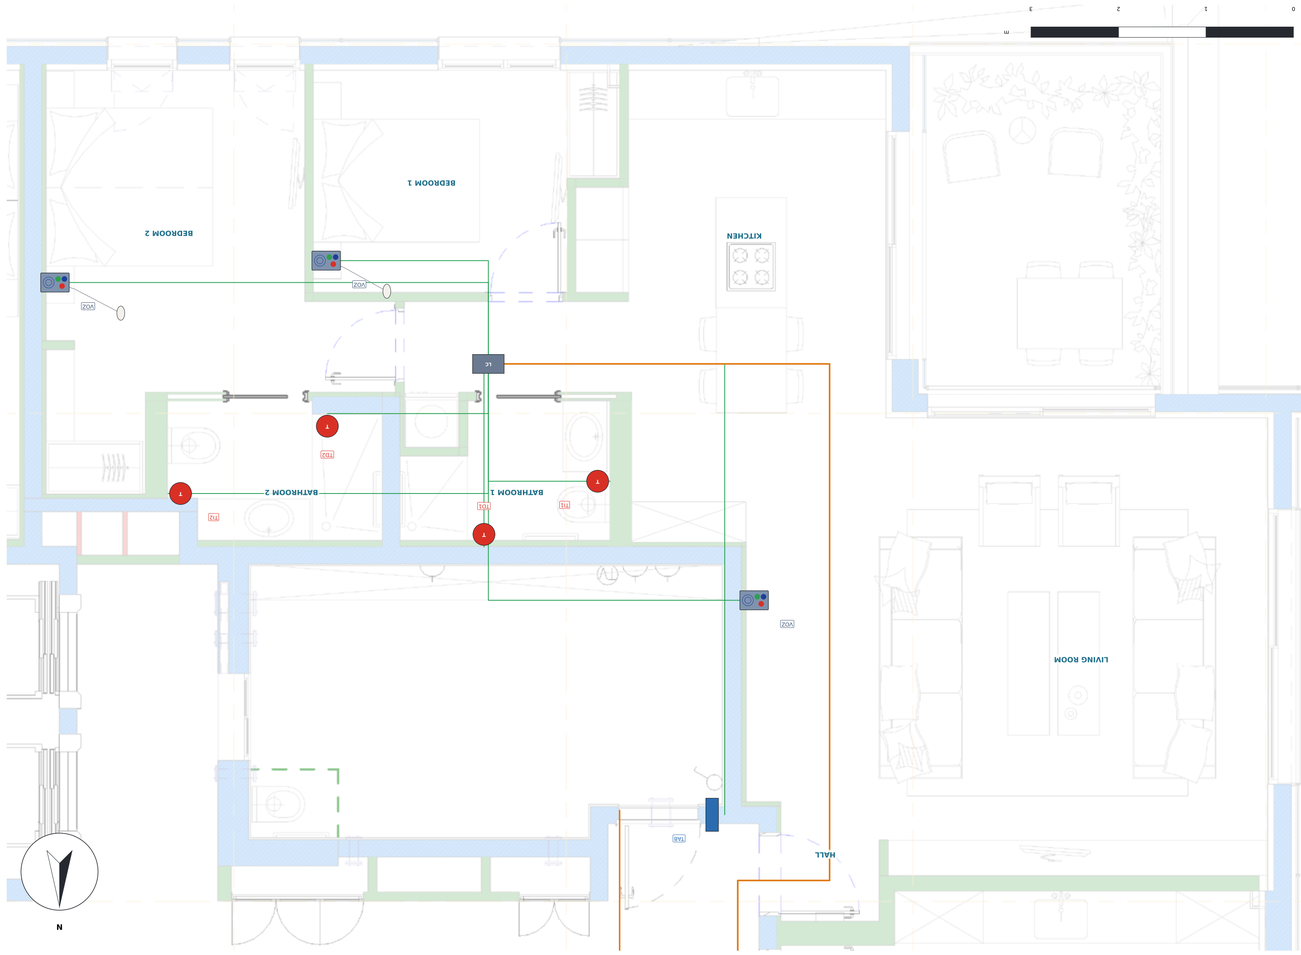

APARTMENT DEVICES

ID	Device	Room	Height
TAB	Door tablet	Hall	1.40 m
VOZ·S	Voice panel with buttons	Living room	1.30 m
VOZ·D1	Voice panel with buttons + pear	Bedroom 1	1.20 m
VOZ·D2	Voice panel with buttons + pear	Bedroom 2	1.20 m
TI1	Pull-cord	Bathroom 1	1.85 m
TD1	Pull-cord	Bathroom 1	1.85 m
TI2	Pull-cord	Bathroom 2	1.85 m
TD2	Pull-cord	Bathroom 2	1.85 m
LCOM	LCom ACE716100D3	Hall	2.55 m

SYMBOLS · SIMBOLOS · σήματα

- TAB - door tablet (iPad / Android) – call and voice, h 1.40 m
  Door tablet - call and voice · οθόνη τύπου – γρηγ πόρτα
- VOZ · Voice panel with buttons ACE821824S1 - living room and bedrooms, h 1.20-1.30 m
  Voice panel with buttons - living room and bedrooms · φωνητικός – σήμα κλήσης
- Call pear next to the bed (bedrooms)
  Call pear next to the bed (bedrooms) · κουμπί κλήσης δίπλα στο κρεβάτι
- T / TD - Pull-cord ACE032039W - toilet and shower, h 1.85 m
  Pull-cord - toilet and shower, h 1.85 m · σχοινί κλήσης, ύψος 1.85 m
- LT - Corridor light ACE410203D9 - above each public toilet door
  Corridor light - above each public toilet door · φώτα διαδρόμου – ένα πάνω από κάθε δημόσια τουαλέτα
- LC - LCom ACE716100D3 - apartment hub (ceiling)
  LCom - apartment hub (ceiling) · LCom – κύριο ελεγκτήριο διαμερίσματος
- BC - BoxCom ACE708100D0 - bus hub for several apartments (ceiling)
  BoxCom - bus hub for several apartments (ceiling) · BoxCom – κύριο λεωφορείο για πολλά διαμερίσματα


Voice panel with buttons

Corridor light


Door tablet (iPad / Android)



Pull-cord

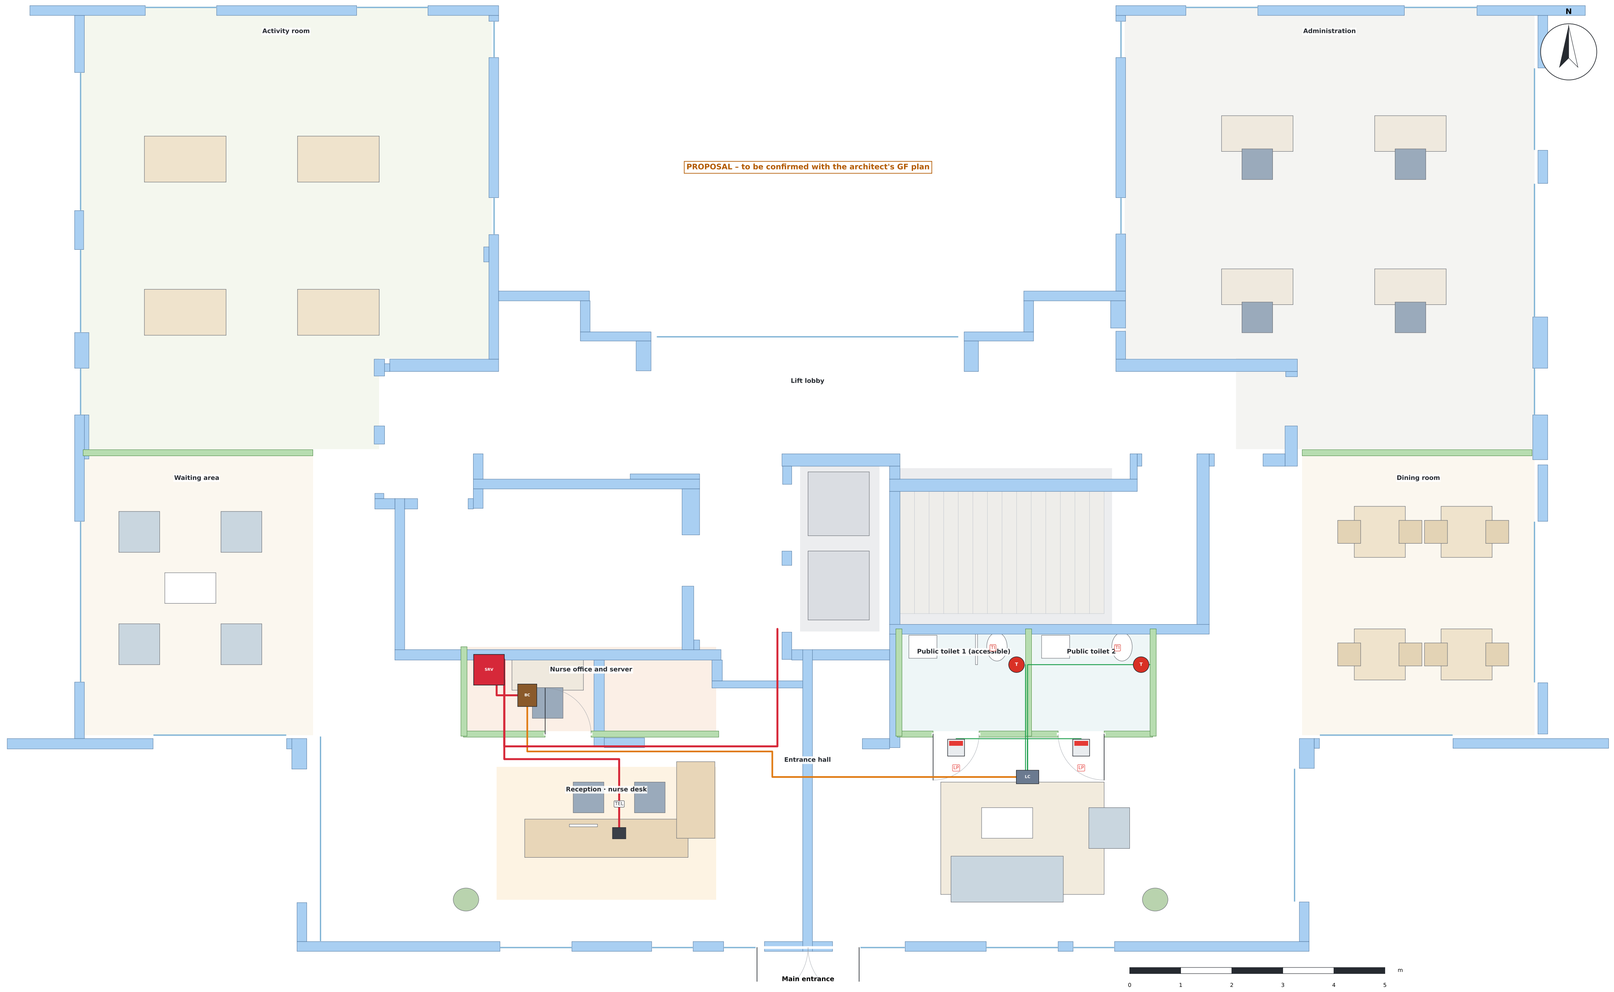

DETAIL · RECEPTION AND NURSE DESK (1:40)

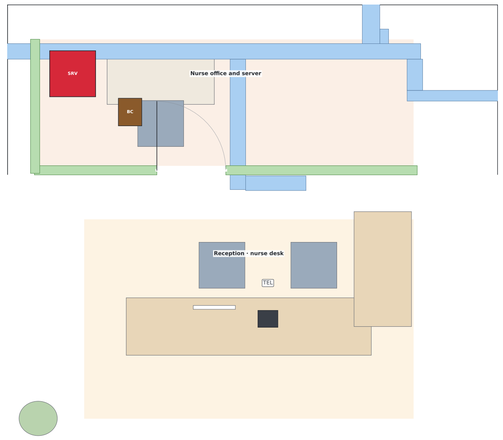

NOTES · NOTAS

1. Nurse desk at reception, facing the entrance and the lifts.
2. On the desk: Grandstream Android phone, connected straight to the PoE switch. Each call shows in its colour.
3. Behind the desk: office with the main rack: Buslogic Premium server and D-Link PoE switch. GF BoxCom on the ceiling.
4. 2 public toilets on GF: pull-cord next to the toilet and corridor light above each door.
5. The riser from the 8 floors runs down the core to the main rack.
6. Proposed GF layout: to be adjusted when the architect's plan arrives.

SYMBOLS · SÍMBOLOS · סימלים

- **T** — TI / TD · Pull-cord ACE40320303W – toilet and shower, h 1.85 m
  Pull-cord – toilet and shower, h 1.85 m · מתקן חירום – שירותים ומקלחת, גובה 1.85 מ'
- **LP** — LP · Corridor light ACE41020309 – above each public toilet door
  Corridor light – above each public toilet door · מיקרוע מסדרון מעל כל דלת שירותים ציבוריים
- **LC** — LC · LCom ACE71610003 – apartment hub (ceiling)
  LCom – apartment hub (ceiling) · LCom – נקודת התקנה בתוך הדירה
- **TEL** — TEL · Grandstream Android phone – PoE straight to the switch
  Grandstream Android phone – PoE straight to the switch · טלפון Grandstream אנדרואיד – ישירות אל המתג PoE
- **SRV** — SRV · GF rack: Buslogic Premium server + D-Link PoE switch
  GF rack: Buslogic Premium server + D-Link PoE switch · מדף GF: שרת Buslogic Premium + מתג PoE D-Link
- **BC** — BC · BoxCom ACE70810000 – bus hub for several apartments (ceiling)
  BoxCom – bus hub for several apartments (ceiling) · BoxCom – מרכז אוטובוס עבור מספר דירות (בתקרה)

DESK PHONE – WHICH COLOUR SHOWS

Alarm (pull-cord / SOS)	**Red**
Green button once: presence	**Green**
Green button again: cancels call or alarm	**Cleared**
Blue button: doctor call (blue call)	**Blue**
Voice call	**Yellow / orange**

MIGDALEI YAM A TIJON · ASSISTED LIVING

Nurse call – GF + 8 floors · 32 apartments

System: ACE BG · Advantecnia Prepared by: Telab International

GROUND FLOOR · LOBBY AND NURSE DESK

SCALE · ESCALA	DATE · FECHA	REV	SHEET
1:60	15/10/2026	B	07


Base: architect's plan LS (Massad Oz / Triplet) · dimensions in m

A1 format · Rev. B – on the real plan

A · BUILDING GF + 8 FLOORS



B · TOPOLOGY OF ONE APARTMENT

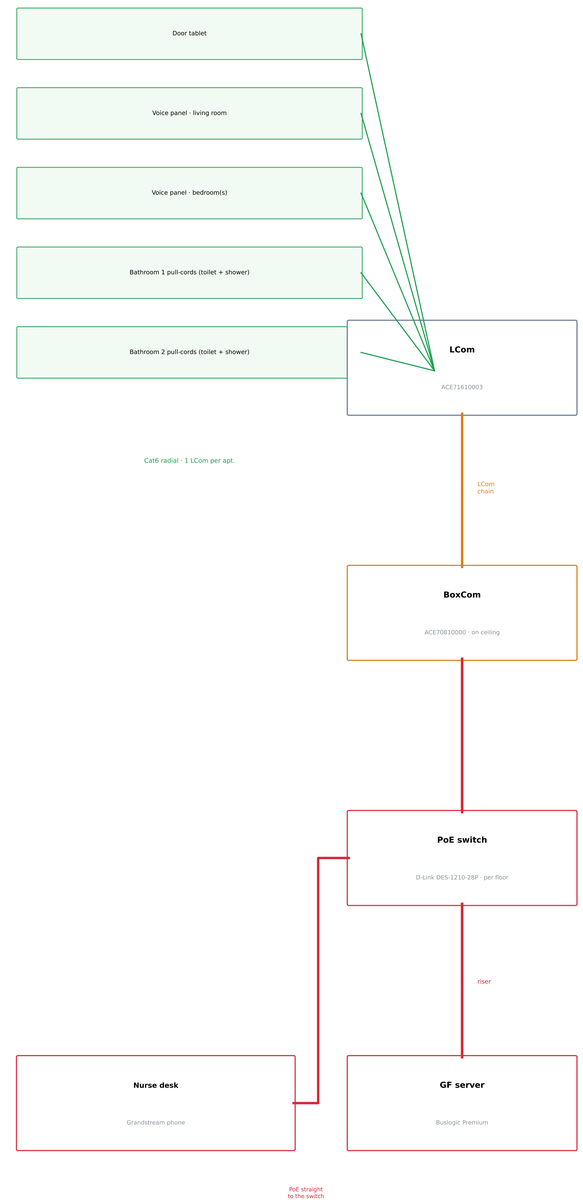

NOTES · NOTAS

1. 8 identical floors with 4 apartments (2 one-bedroom and 2 two-bedroom).
2. On each floor: 2 BoxComs on the ceiling and a rack with the PoE switch.
3. Chain 1: x01 → x04 → public toilet. Chain 2: x02 → x03.
4. The switches run up the riser to the main GF rack.
5. The Grandstream desk phone goes straight to the PoE switch and shows each call in its colour.
6. The whole system is PoE.
7. Preliminary quantities: validate with Advantecnia and on site.

MIGDALEI YAM A TIJON · ASSISTED LIVING

Nurse call – GF + 8 floors · 32 apartments

System: ACE BG · Advantecnia Prepared by: Telab International

RISER DIAGRAM AND TOPOLOGY

SCALE · ESCALA	DATE · FECHA	REV	SHEET
S/E	15/10/2026	B	08

Base: architect's plan LS (Massad Oz / Triplet) · dimensions in m

A1 format · Rev. B – on the real plan

BILL OF MATERIALS – WHOLE BUILDING (GF + 8 floors · 32 apartments · 10 public toilets)

Code	Description	Qty.	Remark
IN THE APARTMENTS (32)			
TAB	Door tablet (iPad / Android) – call and voice	**32**	1 per apartment
VOZ	Voice call panel with buttons – ACE82182451	**80**	living room + each bedroom
TI/TD	Pull-cord – ACE40320303W (toilet and shower)	**128**	4 per apartment
LC	LCom – ACE71610003	**32**	1 per apartment
PUBLIC TOILETS (10)			
T	Pull-cord – ACE40320303W	**10**	8 floors + 2 on GF
LP	Corridor light – ACE41020309	**10**	above each door
LC	LCom – ACE71610003	**9**	1 per floor + 1 on GF
RACKS AND HEAD-END			
BC	BoxCom – ACE70810000 (on the ceiling)	**17**	2 per floor + 1 on GF
SW	24-port PoE switch – D-Link DES-1210-28P	**9**	1 per floor + GF
GAB	12U wall rack with patch panel (for the switch)	**8**	1 per floor
GAB-PB	Main floor-standing rack with UPS	**1**	GF
SRV	Buslogic Premium server (Advantcare) with software	**1**	GF
TEL	Grandstream Android phone (PoE, colours by call type)	**1**	nurse desk
CABLES (+ 15 % spare)			
—	Cat6 radial inside the apartments (green)	**1700 m**	183 m per floor
—	Cat6 / Cat7 chain LCom → BoxCom (orange)	**750 m**	80 m por piso
—	Cat6A / Cat7 racks and riser (red)	**130 m**	includes riser

NOTES · NOTAS

1. Quantities calculated from the model (typical floor × 8 + GF).

2. Cable lengths measured on the drawn route, + 15 %.

3. Prices: per current Advantecnia price list.

4. Validate on site before purchasing.

MIGDALEI YAM A TIJON · ASSISTED LIVING

Nurse call – GF + 8 floors · 32 apartments


System: ACE BG · Advantecnia Prepared by: Telab International

BILL OF MATERIALS

SCALE · ESCALA	DATE · FECHA	REV	SHEET
S/E	15/10/2026	B	09

Base: architect's plan LS (Massad Oz / Triplet) · dimensions in m

A1 format · Rev. B – on the real plan

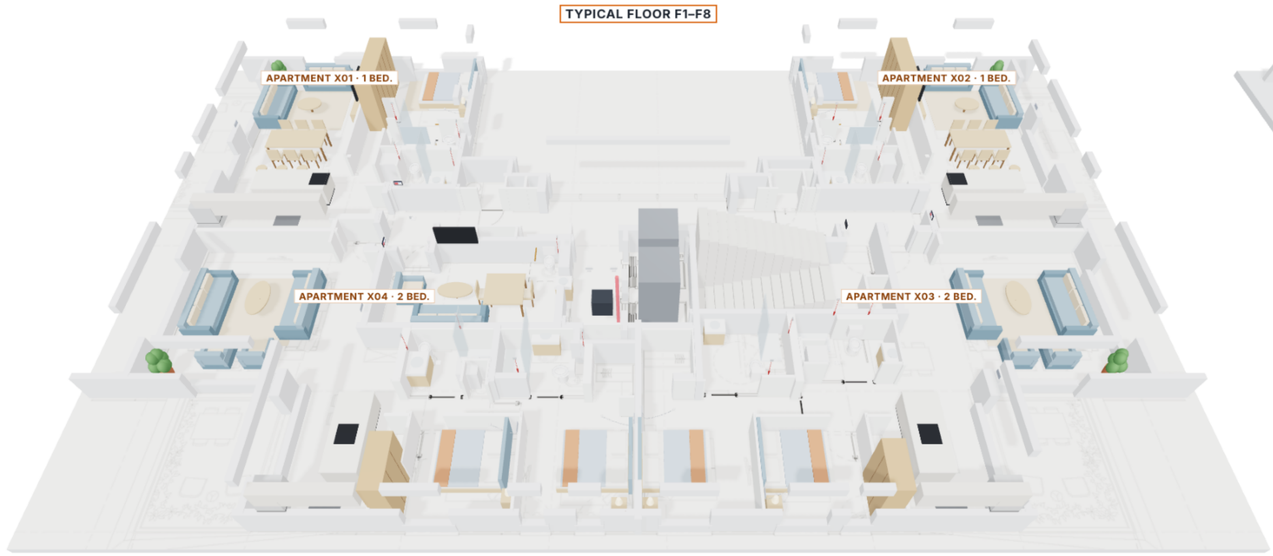


A · Typical floor – 4 apartments




B · Door tablet




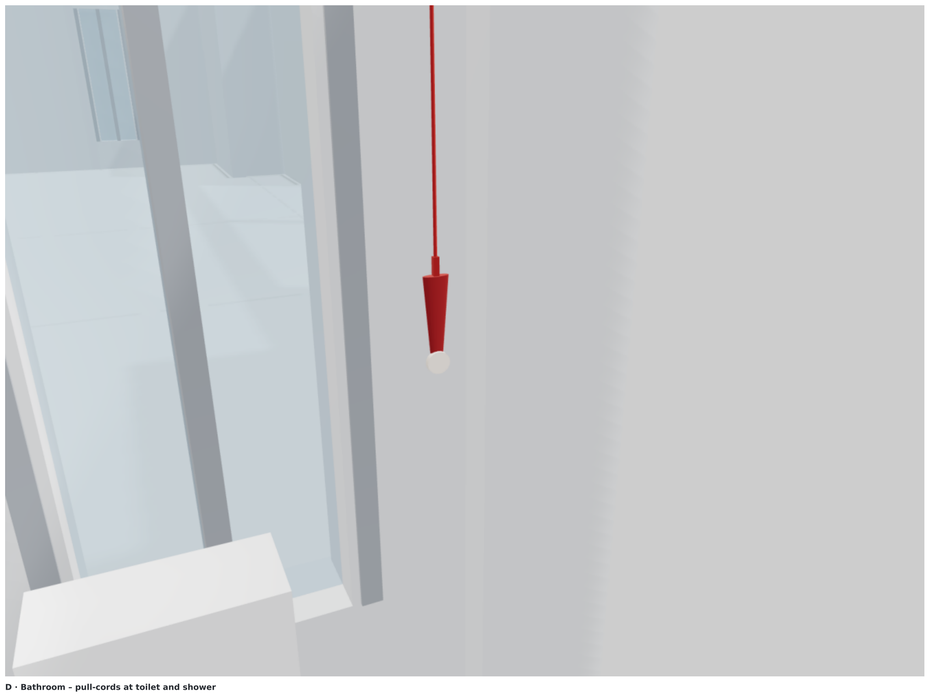

D · Bathroom – pull-cords at toilet and shower

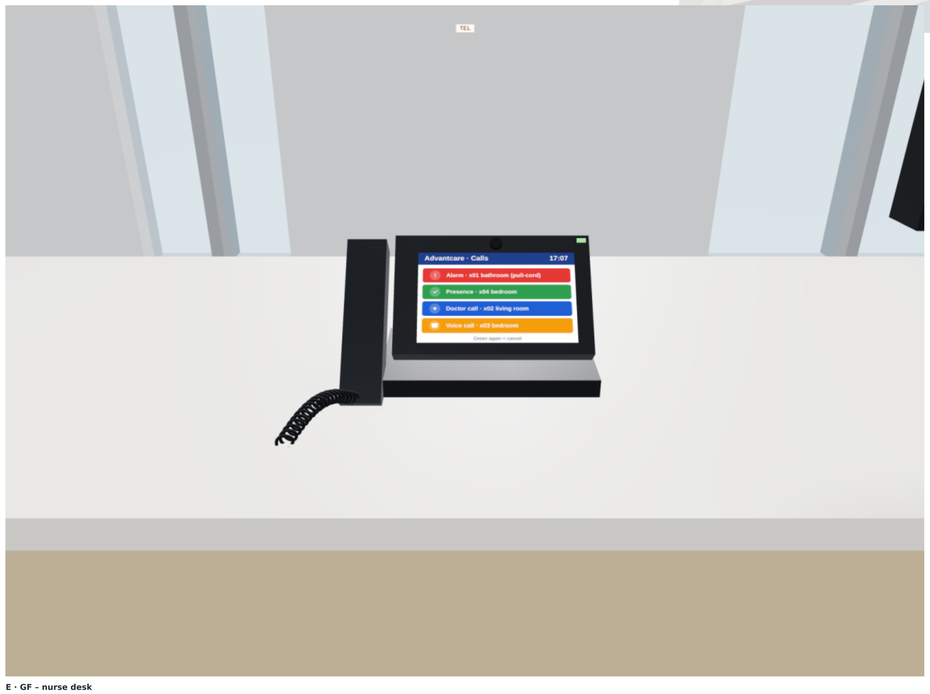

E · GF – nurse desk

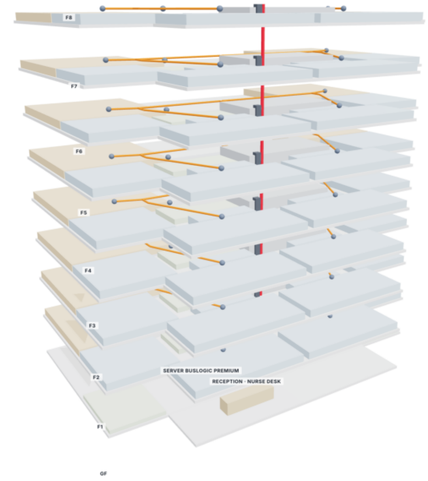

F · Building GF + 8 floors

MIGDALEI YAM A TIJON · ASSISTED LIVING

Nurse call – GF + 8 floors · 32 apartments


System: ACE BG · Advantecnia Prepared by: Telab International

3D VIEWS

SCALE · ESCALA	DATE · FECHA	REV	SHEET
S/E	15/10/2026	B	10

Base: architect's plan LS (Massad Oz / Triplet) · dimensions in m

A1 format · Rev. B – on the real plan

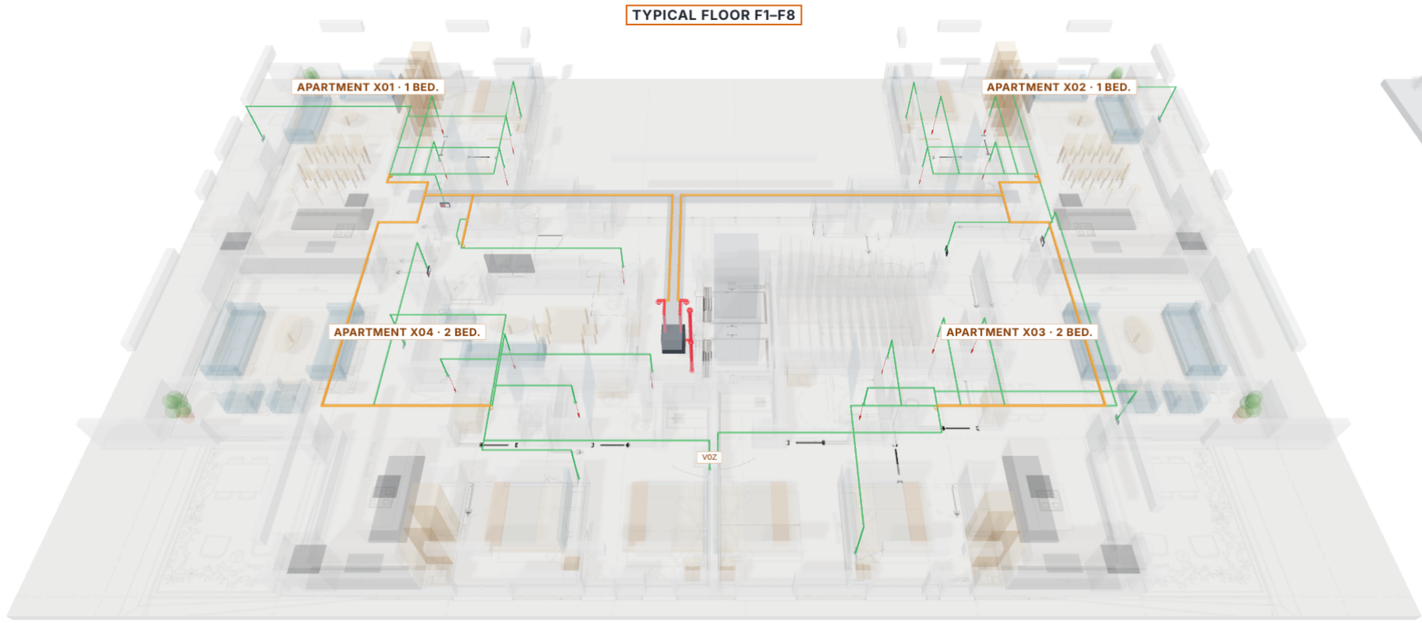

A · Typical floor – wiring (green radial · orange LCom chain · red network)



B · Ground floor – lobby and reception



C · Living room – voice panel with buttons

COLOURS · COLORES · סיעבג

Cat6 radial: each device → its apartment LCom
Cat6 radial: each device → apartment LCom · Cat6 רדיאל: כל מכשיר → LCom של הדירה

Cat6 / Cat7 chain: LCom → LCom → ceiling BoxCom
Cat6 / Cat7 chain: LCom → LCom → BoxCom · Cat6 / Cat7 שרשרת: LCom → LCom → BoxCom

Cat6A / Cat7 network: BoxCom → PoE switch → riser → GF server
Cat6A / Cat7 network: BoxCom → switch → riser → GF server · Cat6A / Cat7 רשת: BoxCom → מתג → עמוד → שרת

MIGDALEI YAM A TIJON · ASSISTED LIVING

Nurse call – GF + 8 floors · 32 apartments

System: ACE BG · Advantecnia Prepared by: Telab International

3D VIEWS – WIRING

SCALE · ESCALA	DATE · FECHA	REV	SHEET
S/E	15/10/2026	B	11

Base: architect's plan LS (Massad Oz / Triplet) · dimensions in m

A1 format · Rev. B – on the real plan