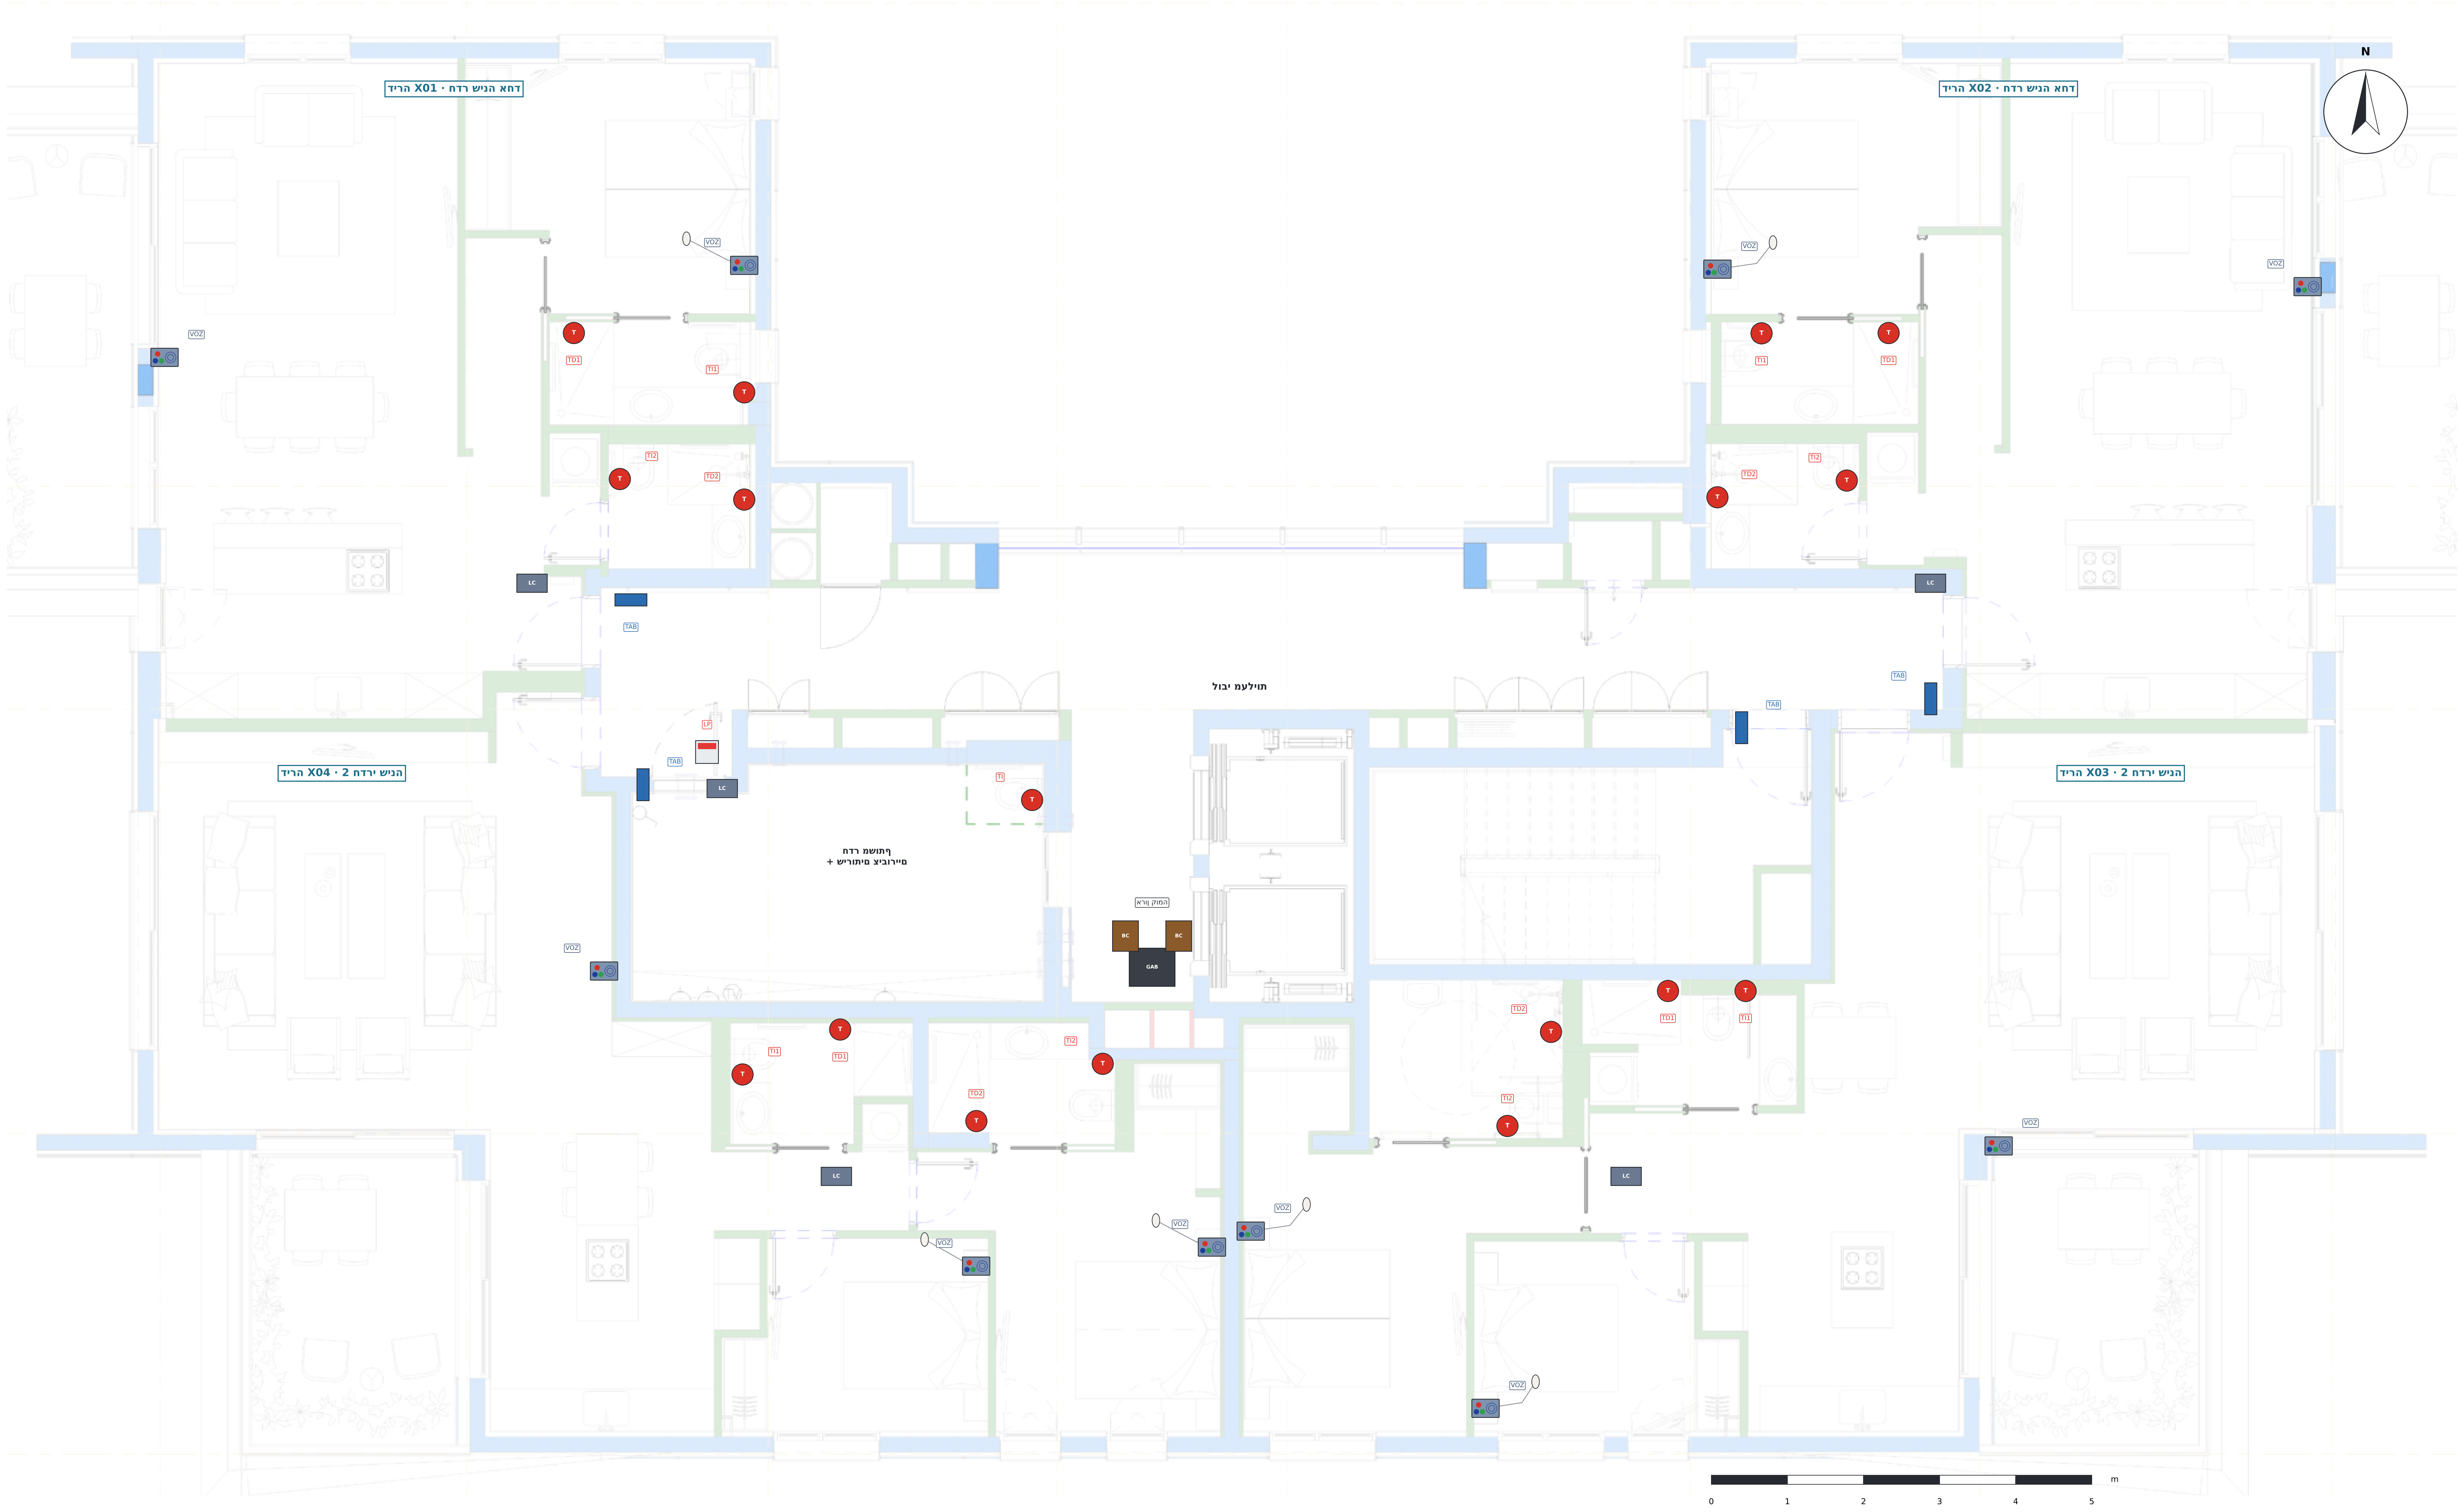
דירה X01 - דירת חדר אחד
דירה X02 - דירת חדר אחד
N
לובי מעליות
דירה X04 - 2 חדרי שינה
חדר משותף + שירותים ציבוריים
דירה X03 - 2 חדרי שינה
TAB
VOZ
T
TI
TD
LC
LP
BC
GAB
0
1
2
3
4
5
m

DEVICES · EQUIPOS · ציוד

▬	TAB · טאבלט בכניסה (iPad / אנדרואיד) – קריאה ודיבור, גובה 1.40 מ' Door tablet – call and voice · טאבלט בכניסה – קריאה ודיבור
●	VOZ · פנל קולי עם לחצנים ACE82182451 – סלון וחדרי שינה, גובה 1.20–1.30 מ' Voice panel with buttons – living room and bedrooms · פנל קולי עם לחצנים – סלון וחדרי שינה
○	אגס קריאה ליד המיטה (בחדרי השינה) Call pear next to the bed (bedrooms) · אגס קריאה ליד המיטה
T	TI / TD · משיכת חבל ACE40320303W – אסלה ומקלחת, גובה 1.85 מ' Pull-cord – toilet and shower, h 1.85 m · משיכת חבל – אסלה ומקלחת, גובה 1.85 מ'
🟥	LP · מנורת מסדרון ACE41020309 – מעל דלת כל שירותים ציבוריים Corridor light – above each public toilet door · מנורת מסדרון – מעל דלת כל שירותים ציבוריים
LC	LC · LCom ACE71610003 – מרכז הדירה (תקרה) LCom – apartment hub (ceiling) · LCom – מרכז הדירה (תקרה)
BC	BC · BoxCom ACE70810000 – מרכז באס לכמה דירות (תקרה) BoxCom – bus hub for several apartments (ceiling) · BoxCom – מרכז באס לכמה דירות (תקרה)
GAB	ארון קומה 12U: מתג D-Link DES-1210-28P (24 יציאות PoE) Floor rack: D-Link DES-1210-28P PoE switch · ארון קומה: מתג PoE D-Link DES-1210-28P

כמויות לקומה × 8 קומות

קוד	התקן	לקומה	8 קומות
TAB	טאבלט בכניסה	4	32
VOZ	פנל קולי עם לחצנים	10	80
TI/TD	משיכת חבל (אסלה + מקלחת)	17	136
LP	מנורת מסדרון (שירותים ציבוריים)	1	8
LC	LCom	5	40
BC	BoxCom	2	16
SW	מתג PoE	1	8

NOTES · הערות

1. בסיס: תוכנית אדריכלית L5 (קומה טיפוסית) – 8 קומות זהות: 4 דירות בקומה, 32 בסך הכל.
2. דירות x01 ו-x02: חדר שינה אחד, סלון עם מטבח ו-2 חדרי רחצה. דירות x03 ו-x04: 2 חדרי שינה ו-2 חדרי רחצה.
3. טאבלט בכניסה לכל דירה (iPad / אנדרואיד) לקריאה ודיבור עם האחות.
4. פנל קולי עם לחצנים (ACE82182451) בסלון ובכל חדר שינה; בחדר השינה עם אגס ליד המיטה.
5. משיכות חבל (ACE40320303W) באסלה ובמקלחת בכל חדר רחצה, בגובה 1.85 מ'.
6. שירותים ציבוריים בכל קומה בחדר המשותף: משיכת חבל + מנורת מסדרון מעל הדלת. עם 2 בקרקע – 10 שירותים ציבוריים.
7. ארון קומה ליד המעליות עם מתג PoE D-Link DES-1210-28P; 2 ה-BoxCom בתקרה לידו.
8. מיקומים לפי סימוני הלקוח בתוכניות L2 (nt = פנל קולי, tab = טאבלט): ראו גיליון 03.

גובהי התקנה

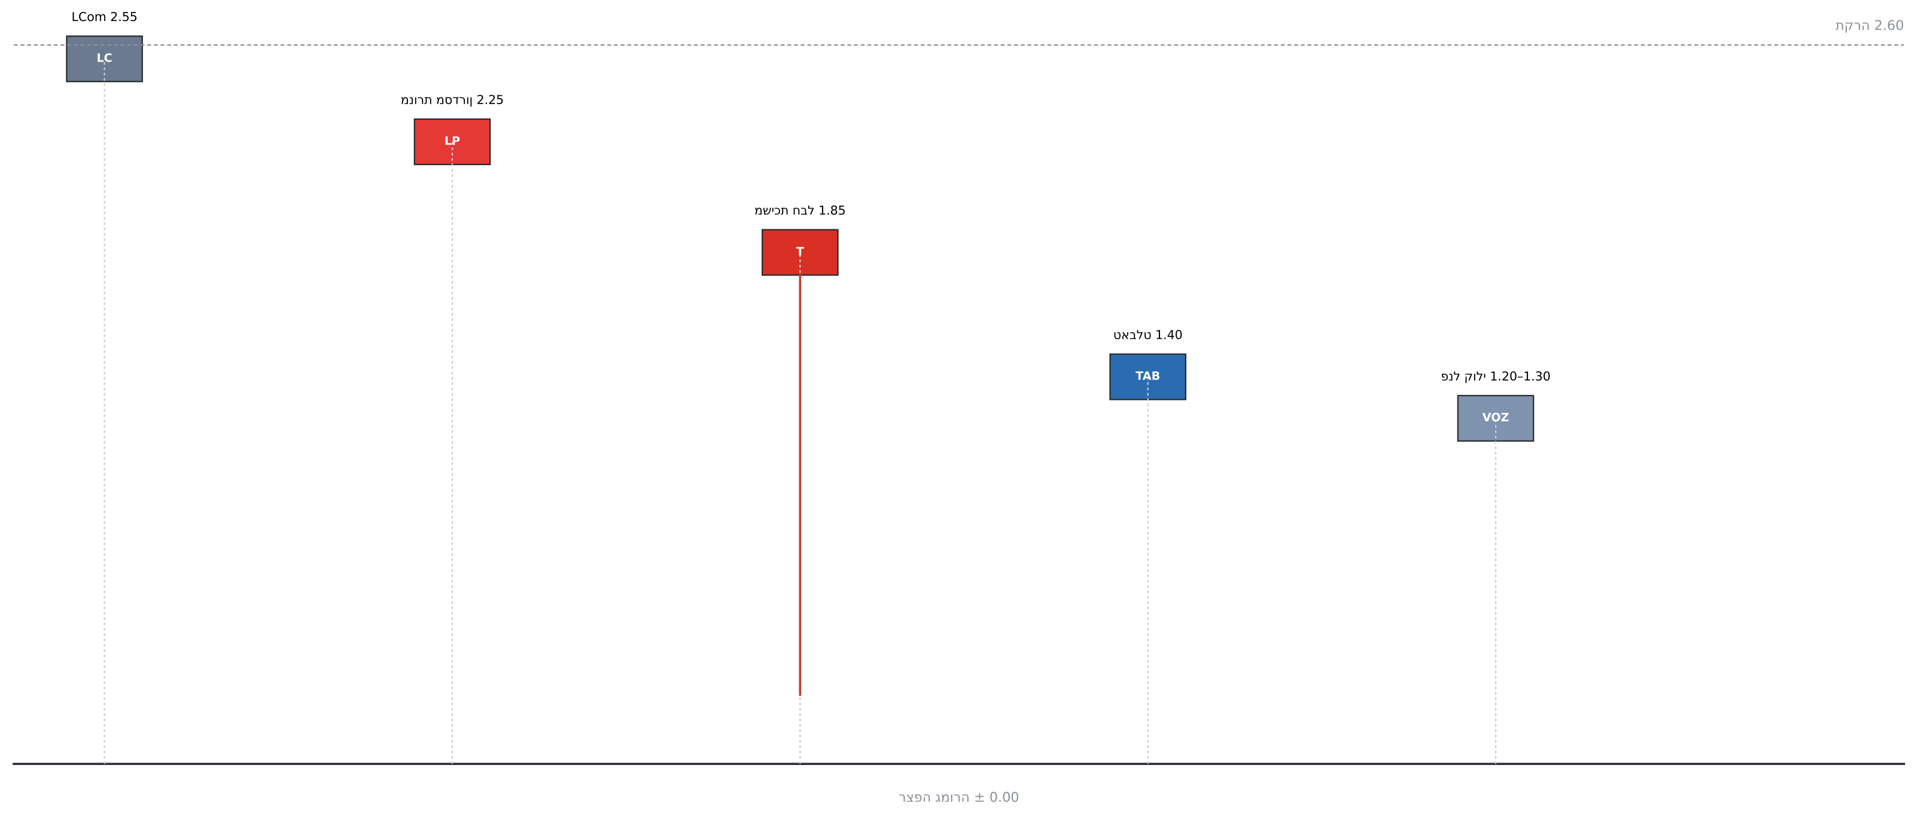

שירותים קריאת אחות

משיכת חבל

טבלט אנדרואיד קריאת אחות
Advantecnia
Llamada de enfermera

טאבלט בכניסה (iPad / אנדרואיד)

מנורה קריאת אחות

מנורת מסדרון

פנל קריאת אחות

פנל קולי עם לחצנים

דיור מוגן · מגדלי ים התיכון
32 דירות · 8 קומות + קרקע – קריאת אחות
הוכן ע"י: Telab International   מערכת: ACE BG · Advantecnia

קריאת אחות · 1–8 קומה טיפוסית

Typical floor F1–F8 · nurse call

SCALE · קנה מידה	DATE · תאריך	REV	גיליון
1:60	15/10/2026	B	01

בסיס: תוכנית האדריכל L5 (מסד זוג / Triplet) · מידות במטרים
פורמט A1 · מהדורה B – על התוכנית האמיתית

שירותים קריאת אחות

לבח תכישמ

דוק	**ACE40320303W**
סוקימ	סיירוביצה סיתורישה 10-בו הצחר רדח לכב תחלקמו הלסא
הבוג	**1.85 מ'**
תומכ	**138**

1

טבלט אנדרואיד קריאת אחות
Advantecnia
TV
Llamada de enfermera
Hospital
Salud y bienestar

הסינכב טלבאט (iPad / דיאורדנא)

דוק	**Advantecnia TV**
סוקימ	הריד לכ תלד דיל ,יבולב
הבוג	**1.40 מ'**
תומכ	**32**

2

מנורה קריאת אחות

וורדסמ תרונמ

דוק	**ACE41020309**
סוקימ	סיירוביצ סיתוריש לכ תלד לעמ
הבוג	**2.25 מ'**
תומכ	**10**

3

NOTES · תורעה

/ ACE BG 1. לש סוחיי תונומת
Advantecnia, םע תרתוכה ןהלש.

2. משיכת חבל: לבח אודמ םע ידית,
הפצרהמ םג שיגנ.

3. הסינכב טלבאטה ארוק ומדבר
םע תוחאה.

4. תרונמ וורדסמה תקלדנ םיארוקשכ
םיירוביצה םיתורישהמ.

5. לנפב ןצחל האירק ,אודמ
ןצחל לוחכ (לאמש) קוריו (ןימי)
רובידל לוקמרו.

6. תרשרש: םינקתה ← LCom (ילאידר) ←
BoxCom (סאב) ← גתמ PoE ← תרש.

7. תורישי רבוחמ הדמעה ןופלט
.PoE-ה גתמל

פנל קריאת אחות

םינצחל םע ילוק לנפ

דוק	**ACE82182451**
סוקימ	(סגא םע הנישה רדחב) הניש רדח לכו ןולס
הבוג	**1.20–1.30 מ'**
תומכ	**80**

4

GRANDSTREAM
HD

ןופלט הדמעה (דיאורדנא)

דוק	**Grandstream**
סוקימ	גתמל תורישי PoE · עקרקב תוחא תדמע
הבוג	**הדמעה לע**
תומכ	**1**

5

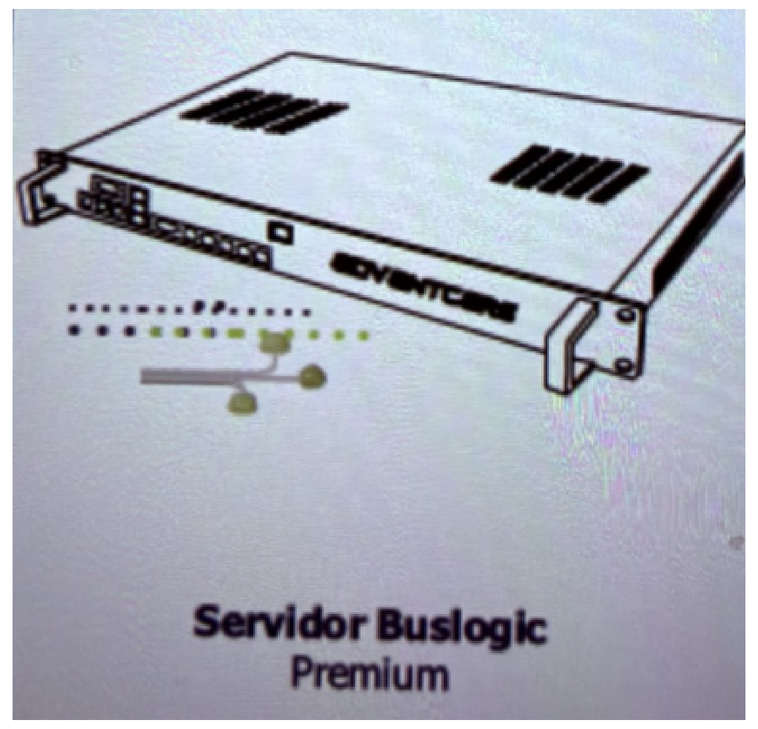
Servidor Buslogic
Premium

Buslogic Premium תרש

דוק	**Advantcare**
סוקימ	עקרקב ישאר ןורא
הבוג	**ןוראב**
תומכ	**1**

6

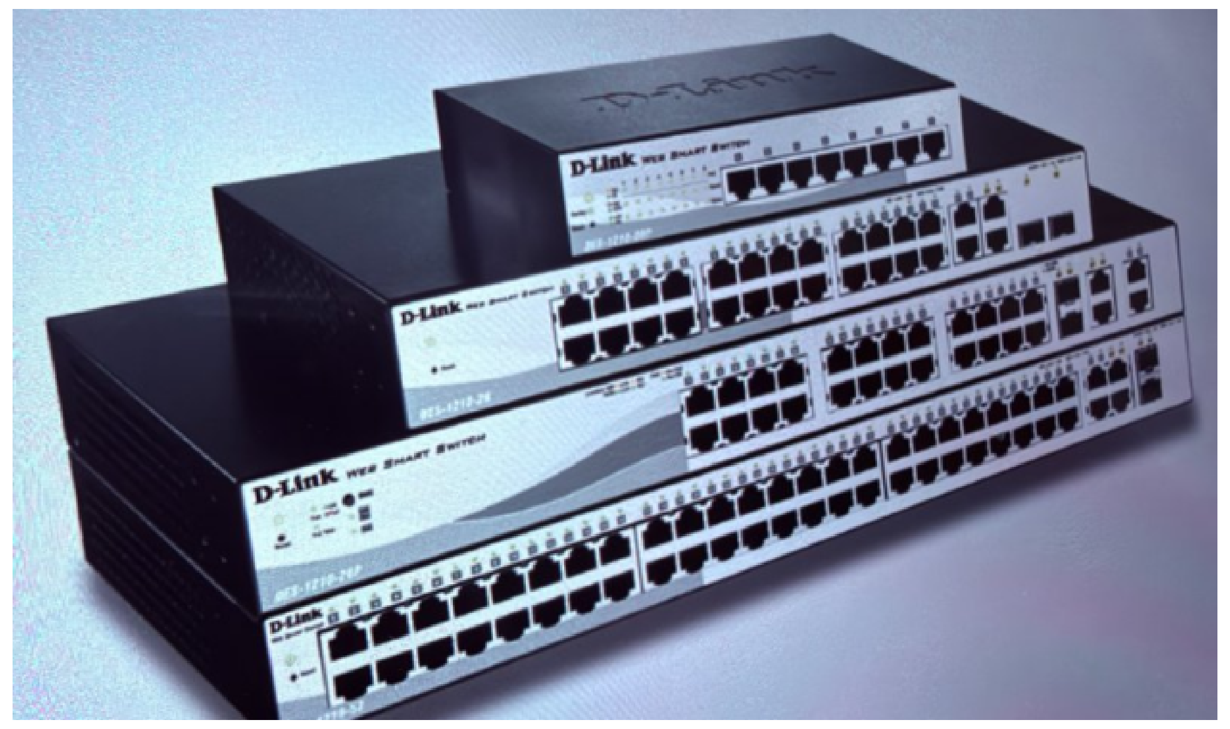

גתמ PoE םע 24 תואיצי

דוק	**D-Link DES-1210-28P**
סוקימ	עקרקבו המוק לכב ןורא
הבוג	**ןוראב**
תומכ	**9**

7

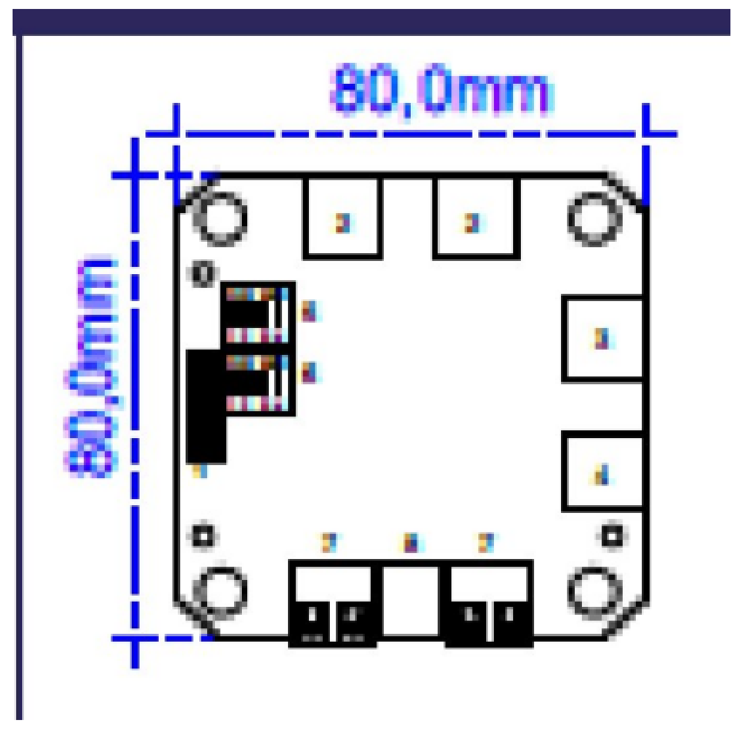
80,0mm
80,0mm

LCom – זכרמ ילאידר

דוק	**ACE71610003**
סוקימ	סיירוביצה סיתורישהו הריד לכ תרקת
הבוג	**2,55 m**
תומכ	**41**

8

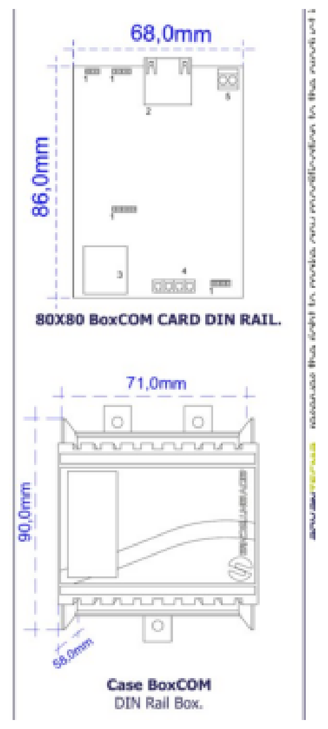
68,0mm
86,0mm
80X80 BoxCOM CARD DIN RAIL.
71,0mm
90,0mm
58,0mm
Case BoxCOM
DIN Rail Box.

BoxCom – זכרמ סאב

דוק	**ACE70810000**
סוקימ	תוריד המכ רבחמ :ןוראה דיל הרקת
הבוג	**2,55 m**
תומכ	**17**

9

גצומ עבצ הזיא – הדמעה ןופלט

מודא	(SOS / הכישמ) הקעזה	🟥
קורי	תוחכונ :תחא םעפ קורי ןצחל	🟩
קחמנ	הקעזה וא האירק לטבמ :בוש קורי ןצחל	⬜
לוחכ	(blue call) ןצחל לוחכ: האירק רופא	🟦
בוהצ / םותכ	תילוק החיש	🟧

ןגומ רויד · ןוכיתה םי ילדגמ

תוריד 32 · תומוק 8 + עקרק – תוחא תאירק

Telab International :ןכוה י"ע ACE BG · Advantecnia :תכרעמ

תכרעמה דויצ

System devices

SCALE · הדימ הנק	DATE · ךיראת	REV	ןוילג
S/E	**15/10/2026**	**B**	**02**

סיסב: תינכות לכירדאה L5 (זוע דסמ / Triplet) · םירטמב תודימ

טמרופ A1 · הרודהמ B – לע תינכותה תיתימאה

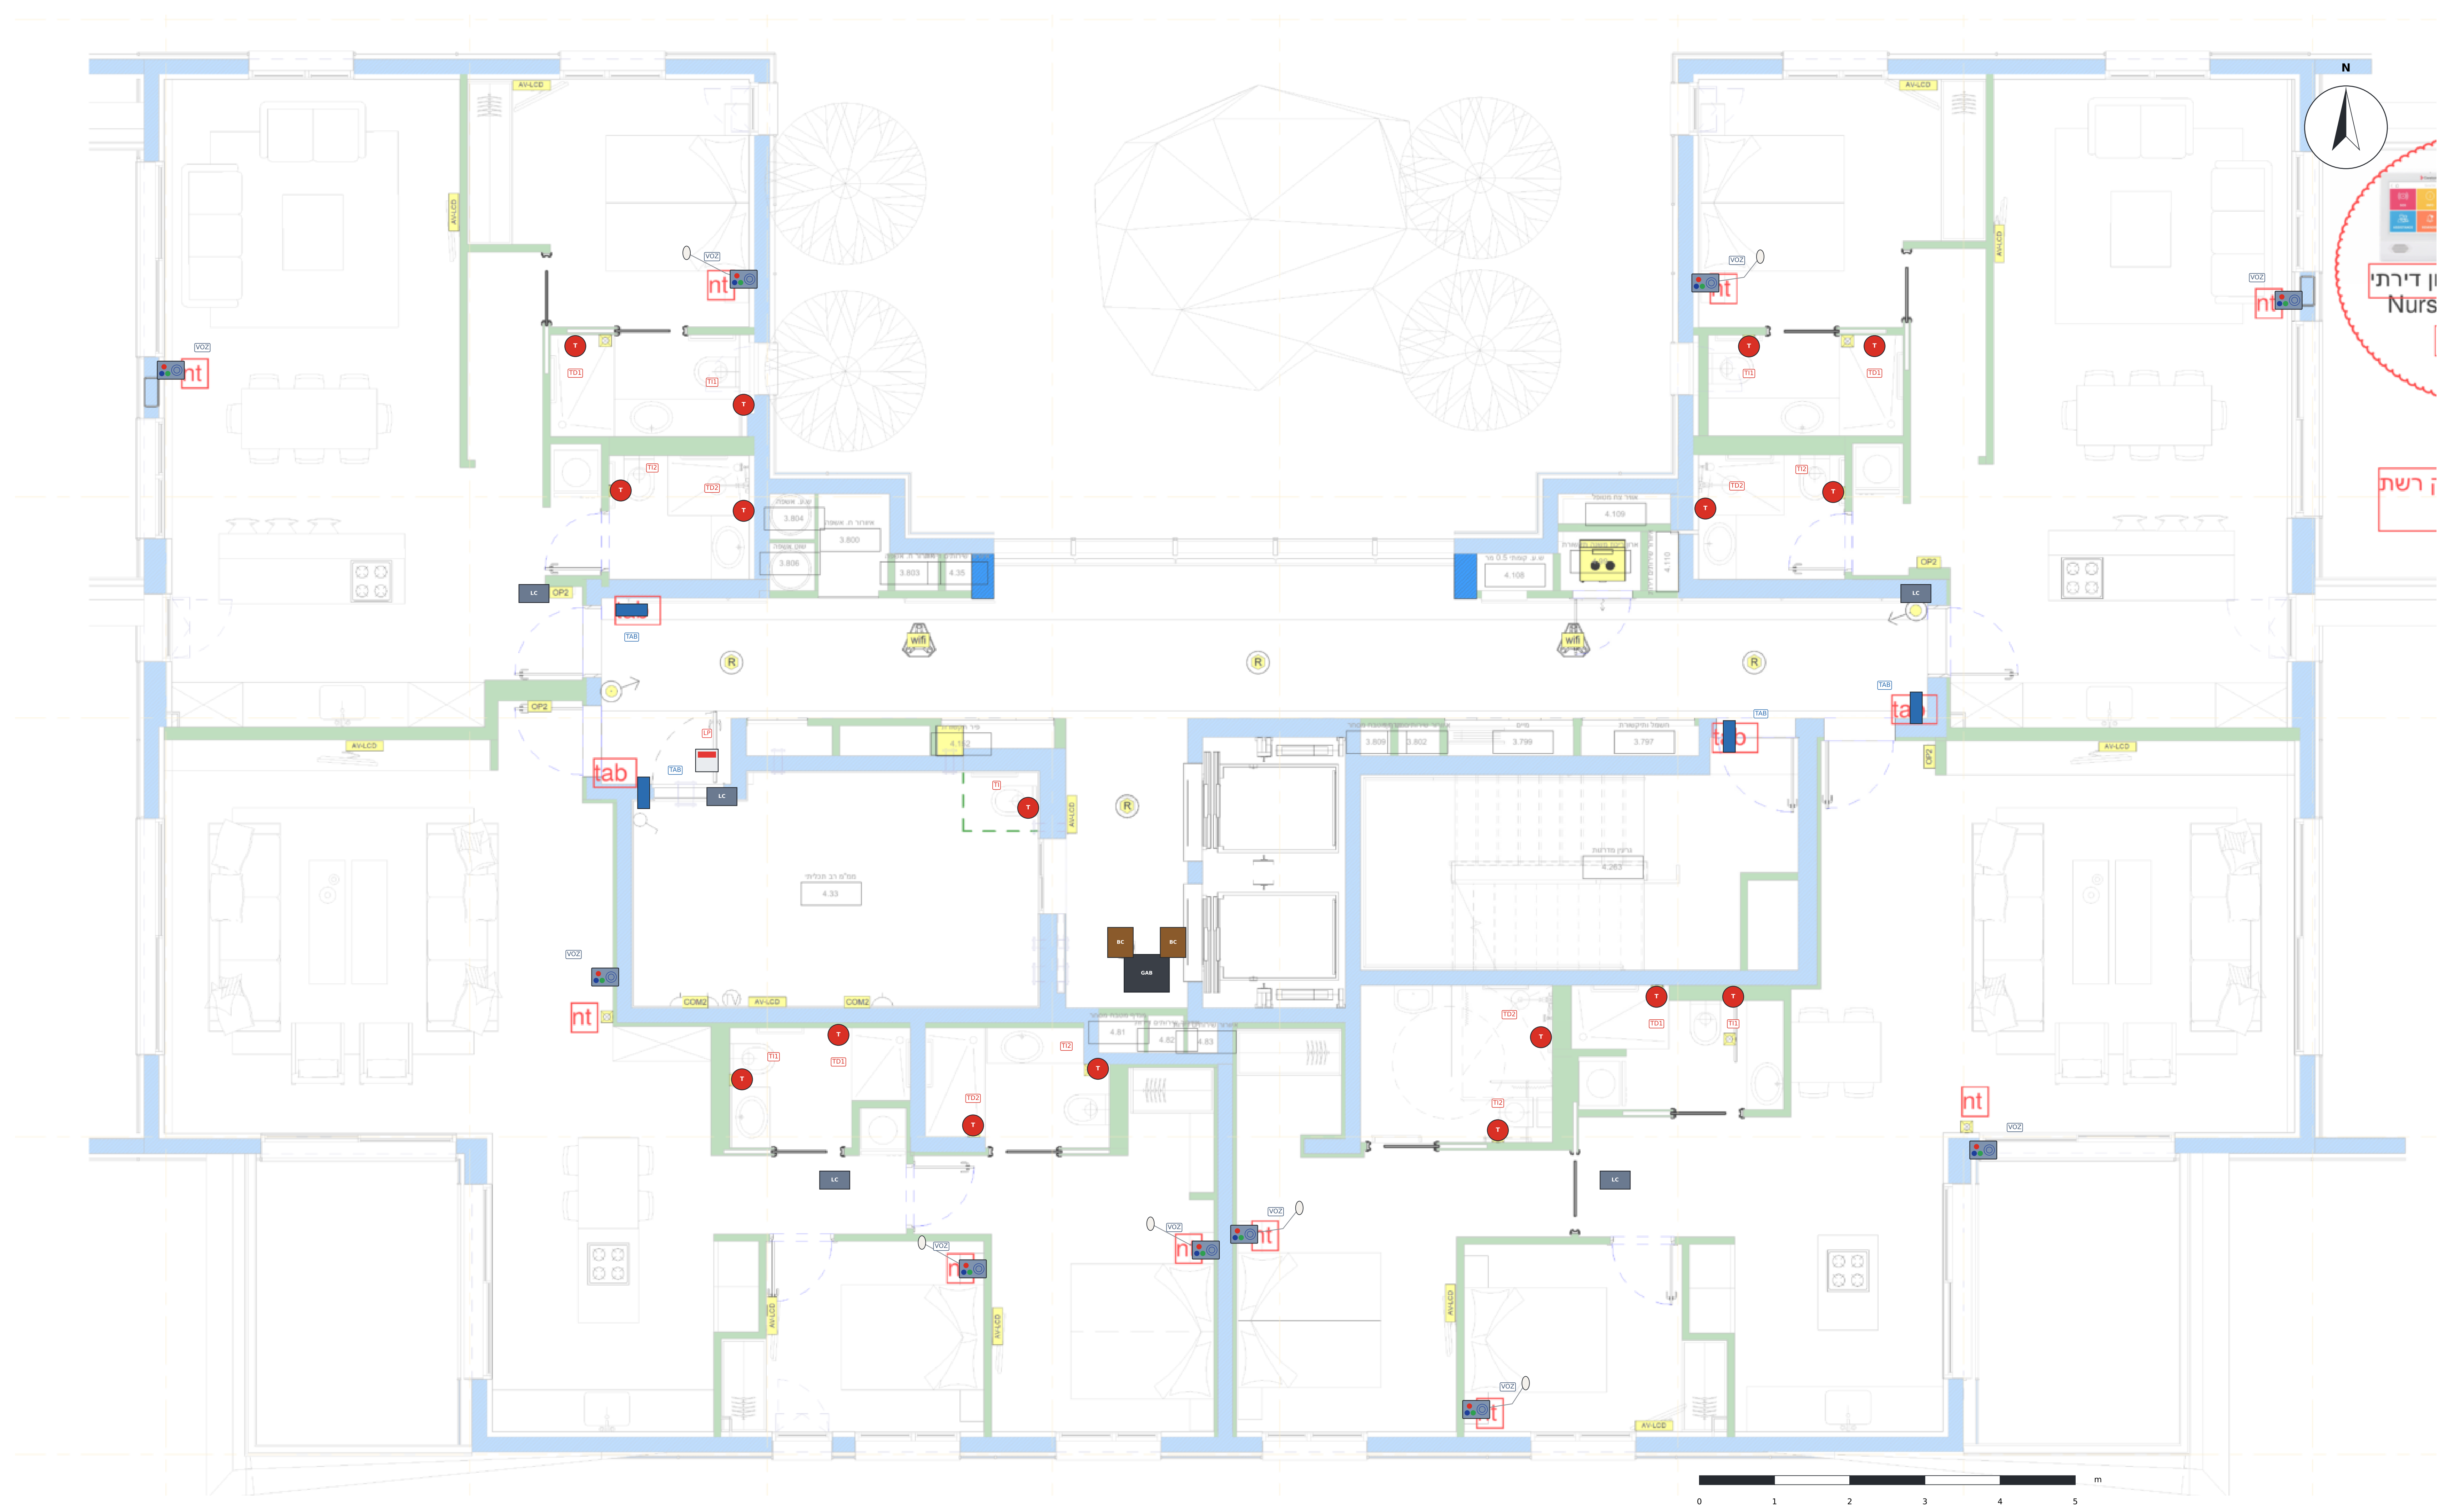

NOTES · תורעה

1. רקע: תינכות IT L2 לש חוקלה םע םינומיסה ולש םודאב:
«nt» = לנפ ילוק ו-«tab» = טלבאט הסינכב.

2. לעמ, עבצב: הציוד העצהב וז.
לכ לנפ ולכו טלבאט םיאצמנ םוקמב שהלקוח םיסמן.

L2 3. תינכותה הצחרה ירדחב ☒ םיבוהצה םיעובירה
הם תוכישמ לבחה (תחלקמו הלסא).

4. 4 הטלבאטים בולבי, הריד לכ תלד דיל,
.«tab» ומכ םנומיסבי

5. תוינכותל L2 ו-L5 (העצהה סיסב) הנבמ ותוא;
L5 8 איה הקומה תיסופיטה תומוקל 1 דע.

DEVICES · EQUIPOS · דויצ

🟦 TAB · טלבאט הסינכב (iPad / דיאורדנא) – רובידו האירק, הבוג 1.40 מ'
Door tablet – call and voice · טלבאט הסינכב – רובידו האירק

VOZ · לנפ ילוק םע םינצחל ACE82182451 – ןולס ירדחו הניש, הבוג 1.20–1.30 מ'
Voice panel with buttons – living room and bedrooms · ןולס ירדחו הניש – לנפ ילוק םע םינצחל

אגס האירק דיל הטימה (ירדחב הנישה)
Call pear next to the bed (bedrooms) · אגס האירק דיל הטימה

T TI / TD · תכישמ לבח ACE40320303W – הלסא ומקלחת, הבוג 1.85 מ'
Pull-cord – toilet and shower, h 1.85 m · תכישמ לבח – הלסא ומקלחת, הבוג 1.85 מ'

LP · תרונמ ןורדסמ ACE41020309 – לעמ תלד לכ םיתוריש םיירוביצ
Corridor light – above each public toilet door · תרונמ ןורדסמ – לעמ תלד לכ םיתוריש םיירוביצ

שירותים קריאת אחות

לבח תכישמ

טבלט אנדרואיד קריאת אחות

Advantecnia
Llamada de enfermera

הסינכב טלבאט (iPad / דיאורדנא)

מנורה קריאת אחות

ןורדסמ תרונמ

פנל קריאת אחות

םינצחל םע ילוק לנפ

ןגומ רויד · ןוכיתה םי ילדגמ
קריאת אחות – עקרק + 8 תומוק · 32 תוריד
Telab International :ןכוה ע"י   ACE BG · Advantecnia :תכרעמ

העצההו (תינכות L2) חוקלה ינומיס

Client marks (plan L2) and proposal

SCALE · הדימ הנק	DATE · ךיראת	REV	ןוילג
1:60	**15/10/2026**	**B**	**03**

סיסב: תינכות האדריכל L5 (םסד זוג / Triplet) · םירטמב תודימ
טמרופ A1 · הרודהמ B – לע תינכותה תיתימאה

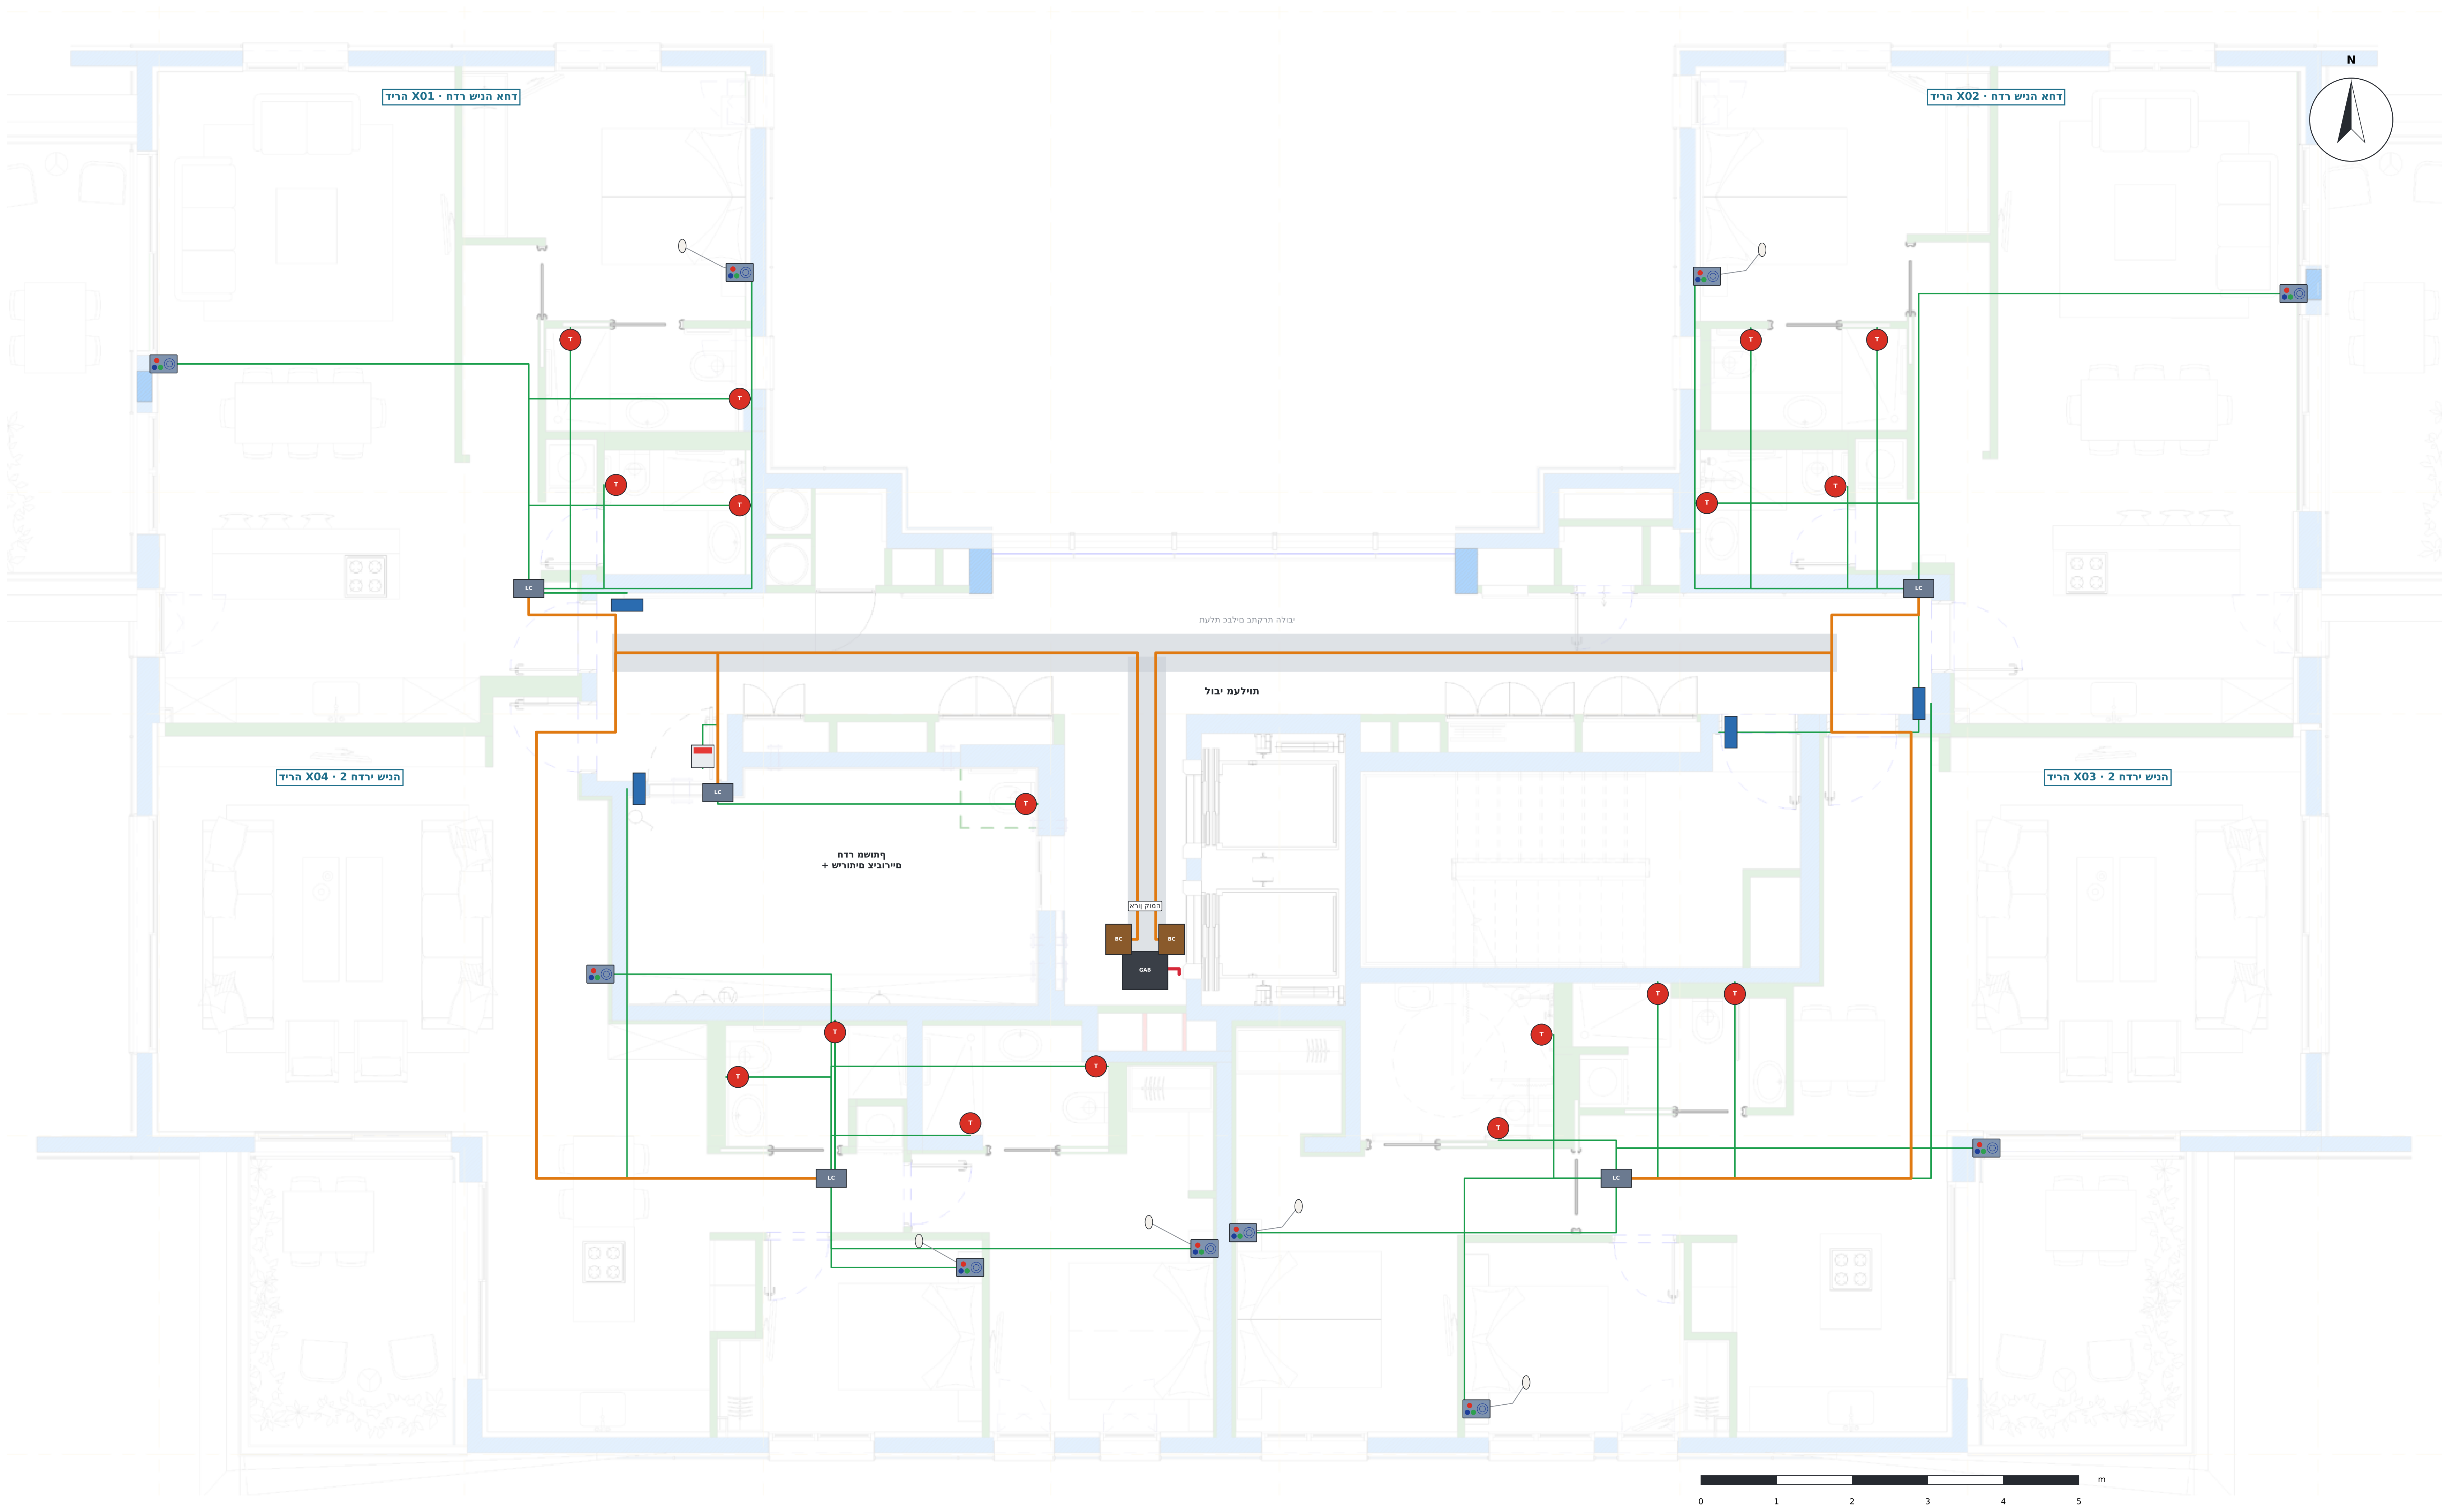

WIRING · CABLEADO · טוויח

Cat6 ילאידר: לכ ןקתה ← LCom הרידה לש
Cat6 radial: each device → apartment LCom · Cat6 ילאידר: לכ ןקתה ← LCom הרידה לש

Cat6 / Cat7 תרשרש: LCom ← LCom ← BoxCom הרקתב
Cat6 / Cat7 chain: LCom → LCom → BoxCom · Cat6 / Cat7 תרשרש: LCom ← LCom ← BoxCom

Cat6A / Cat7 תשר: BoxCom ← גתמ PoE ← דומע ← תרש עקרק
Cat6A / Cat7 network: BoxCom → switch → riser → GF server · Cat6A / Cat7 תשר: BoxCom ← גתמ ← דומע ← תרש

םיכרוא תיסופיט המוקב (הברזר אלל)

🟩	Cat6 ילאידר ךותב תורידה	183 m
🟧	Cat6 / Cat7 תרשרש LCom ← BoxCom	80 m
🟥	Cat6A / Cat7 דומעו ןורא	7 m

NOTES · תורעה

1. לכ ןקתה רבוחמ תילאידר (Cat6) ל-LCom הרידה לש, האובמה תרקתב.
2. ה-LCom םירשרושמ תלעתב יבולה דע ה-BoxCom הרקתב,
.BoxCom 1 · x02 ← x03 ← BoxCom 2 ← ףתושמ רדח ← x01 ← x04 :דיל הארו
3. ה-BoxCom םידרוי גתמל ה-PoE ןוראב; הלוע גתמה
דומעב Cat6A / Cat7 דע תרשה עקרקב.
4. לוכה PoE: ןיא ךרוצ ב-230V ינקתהל תורידה.

NOTES · תורעה

1. סיסב: תינכות תילכירדא L5 (תיסופיט המוק) – 8 תומוקה תוהז: 4 תוריד המוקב, 32 ךסב לוכה.
2. תוריד x01 ו-x02: רדח הניש דחא, ןולס םע חבטמ ו-2 ירדח הצחר. תוריד x03 ו-x04: 2 ירדח הניש ו-2 ירדח הצחר.
3. טלבאט הסינכב לכל הריד (iPad / דיאורדנא) האירקל ורובידלו םע תוחאה.
4. לנפ ילוק םע םינצחל (ACE82182451) ןולסב לכבו רדח הניש; רדחב הנישה םע גאס דיל הטימה.
5. תוכישמ לבח (ACE40320303W) הלסאב תחלקמבו לכב ירדח הצחרה, הבוגב 1.85 מ'.
6. םיתוריש םיירוביצ לכב המוק רדחב ףתושמה: תכישמ לבח + תרונמ ןורדסמ לעמ תלדה. םע 2 עקרקב – 10 םיתוריש םיירוביצ.
7. ןורא המוק דיל תוילעמה םע גתמ PoE D-Link DES-1210-28P; 2 ה-BoxCom הרקתב ודיל.
8. םימוקימ יפל םינומיס הלקוח תינכותב L2 (nt = לנפ ילוק, tab = טלבאט): ואר ןוילג 03.

ןגומ רויד · ןוכיתה םי ילדגמ

קרקע תואחא תיריק – 8 תומוק + עקרק · 32 תוריד

Telab International :ןכוה ע"י ACE BG · Advantecnia :תכרעמ

טוויח · 1–8 תיסופיט המוק

Typical floor F1–F8 · wiring

SCALE · הדימ תנק	DATE · ךיראת	REV	ןוילג
1:60	15/10/2026	B	04

סיסב: תינכות הלכירדא L5 (זוע דסמ / Triplet) · םירטמב תודימ

טמרופ A1 · הרודהמ B – לע תינכותה תיתימאה

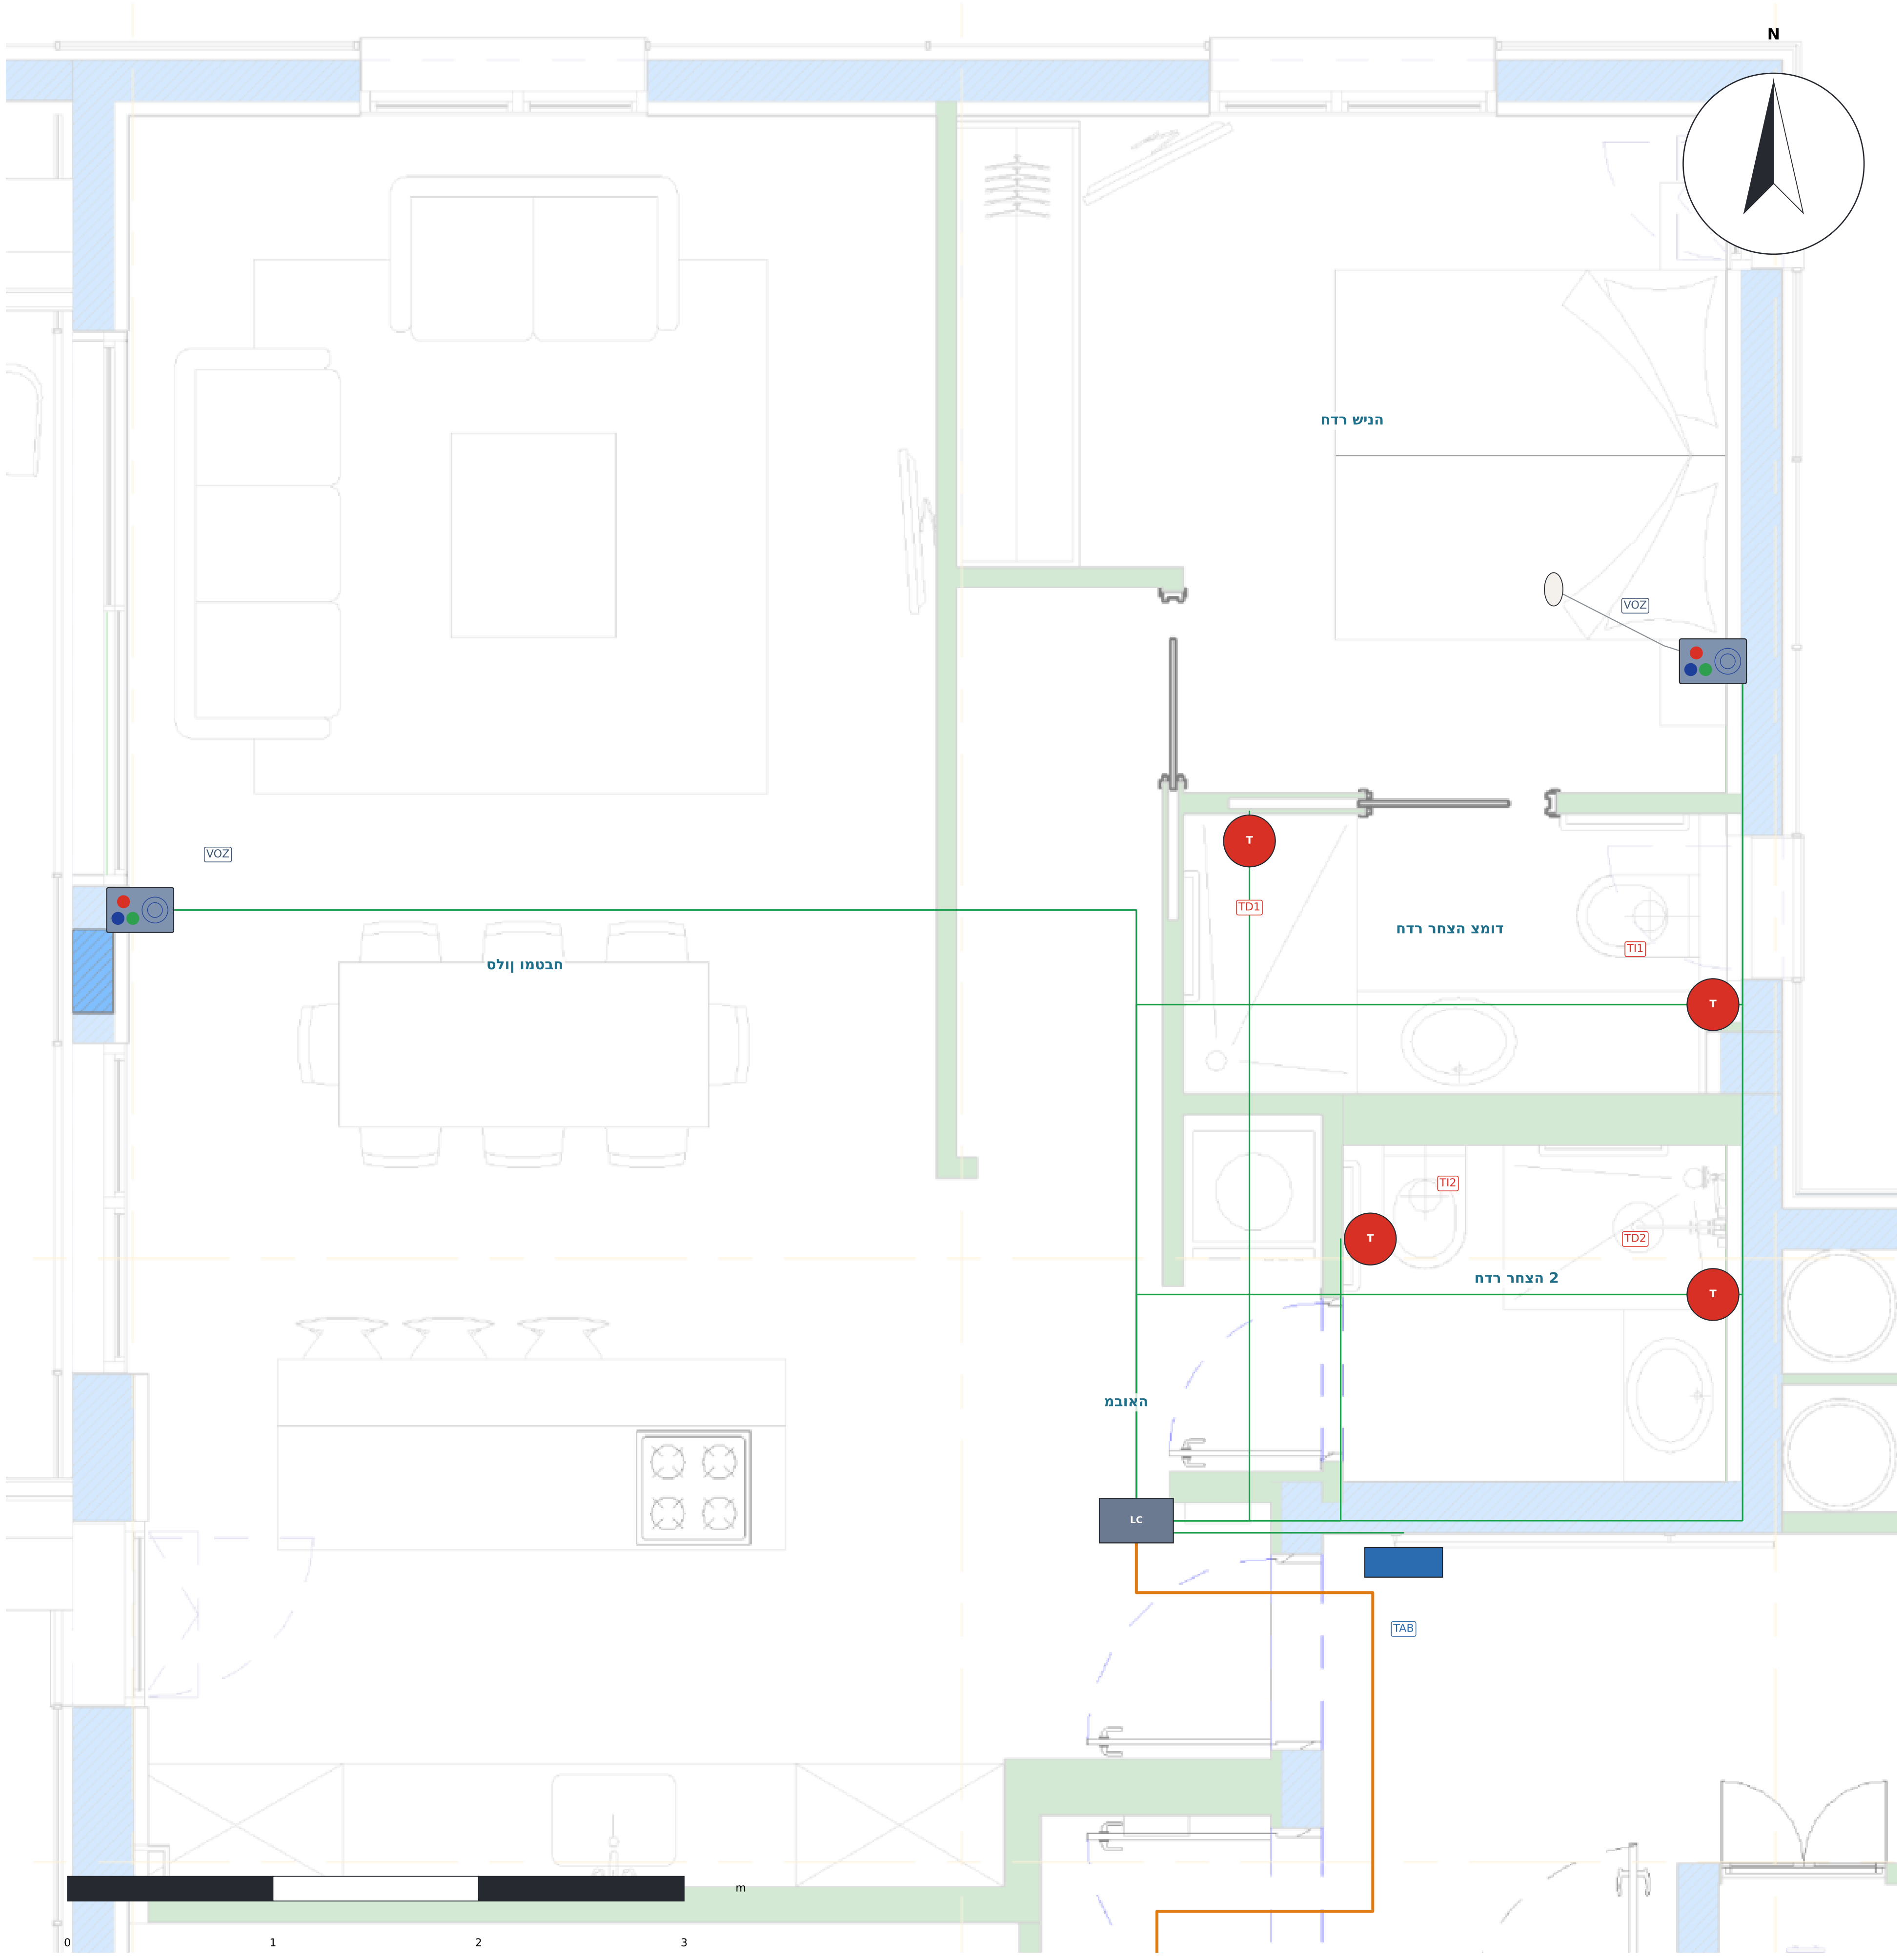
N
חדר שינה
VOZ
VOZ
סלון ומטבח
T
TD1
TI1
חדר רחצה צמוד
T
TI2
TD2
T
T
חדר רחצה 2
מבואה
LC
TAB
0
1
2
3
m

ציוד הדירה

ID	התקן	חדר	גובה
TAB	טאבלט בכניסה	מבואה	1.40 מ'
VOZ-S	פנל קולי עם לחצנים	סלון ומטבח	1,30 m
VOZ-D	פנל קולי עם לחצנים + אגס	חדר שינה	1,20 m
TI1	משיכת חבל	חדר רחצה צמוד	1.85 מ'
TD1	משיכת חבל	חדר רחצה צמוד	1.85 מ'
TI2	משיכת חבל	חדר רחצה 2	1.85 מ'
TD2	משיכת חבל	חדר רחצה 2	1.85 מ'
LCOM	LCom ACE71610003	מבואה	2,55 m

SYMBOLS · SÍMBOLOS · סמלים

- TAB · טאבלט בכניסה (iPad / אנדרואיד) – קריאה ודיבור, גובה 1.40 מ'
  Door tablet – call and voice · טאבלט בכניסה – קריאה ודיבור
- VOZ · פנל קולי עם לחצנים ACE82182451 – סלון וחדרי שינה, גובה 1.20–1.30 מ'
  Voice panel with buttons – living room and bedrooms · פנל קולי עם לחצנים – סלון וחדרי שינה
- אגס קריאה ליד המיטה (בחדרי השינה)
  Call pear next to the bed (bedrooms) · אגס קריאה ליד המיטה
- T TI / TD · משיכת חבל ACE40320303W – אסלה ומקלחת, גובה 1.85 מ'
  Pull-cord – toilet and shower, h 1.85 m · משיכת חבל – אסלה ומקלחת, גובה 1.85 מ'
- LP · מנורת מסדרון ACE41020309 – מעל דלת כל שירותים ציבוריים
  Corridor light – above each public toilet door · מנורת מסדרון – מעל דלת כל שירותים ציבוריים
- LC LC · LCom ACE71610003 – רכזת הדירה (תקרה)
  LCom – apartment hub (ceiling) · LCom – רכזת הדירה (תקרה)
- BC BC · BoxCom ACE70810000 – רכזת באס לכמה דירות (תקרה)
  BoxCom – bus hub for several apartments (ceiling) · BoxCom – רכזת באס לכמה דירות (תקרה)

NOTES · הערות

1. דירה x02 היא תמונת ראי של x01 (אותו ציוד).
2. טאבלט בלובי, ליד דלת הכניסה (סימון «tab» של הלקוח).
3. פנל קולי בסלון ובחדר השינה (עם אגס ליד המיטה).
4. 2 חדרי רחצה: משיכת חבל באסלה ובמקלחת בכל אחד (4 משיכות חבל).
5. הכול מחובר רדיאלית ב-Cat6 ל-LCom במבואה.

שירותים קריאת אחות

משיכת חבל

טבלט אנדרואיד קריאת אחות
Advantecnia
TV
Llamada de enfermera
Hospital
Salud y bienestar

טאבלט בכניסה (iPad / אנדרואיד)

מנורה קריאת אחות

מנורת מסדרון

פנל קריאת אחות

פנל קולי עם לחצנים

מגדלי ים התיכון · דיור מוגן
קריאת אחות – קרקע + 8 קומות · 32 דירות
מערכת: ACE BG · Advantecnia   הוכן ע"י: Telab International

דירת חדר שינה אחד (x01 / x02)

1-bedroom apartment (x01 / x02)

SCALE · קנה מידה	DATE · תאריך	REV	גליון
1:30	15/10/2026	B	05

בסיס: תכניות האדריכל L5 (מסד עוז / Triplet) · מידות במטרים
פורמט A1 · מהדורה B – על התוכנית האמיתית

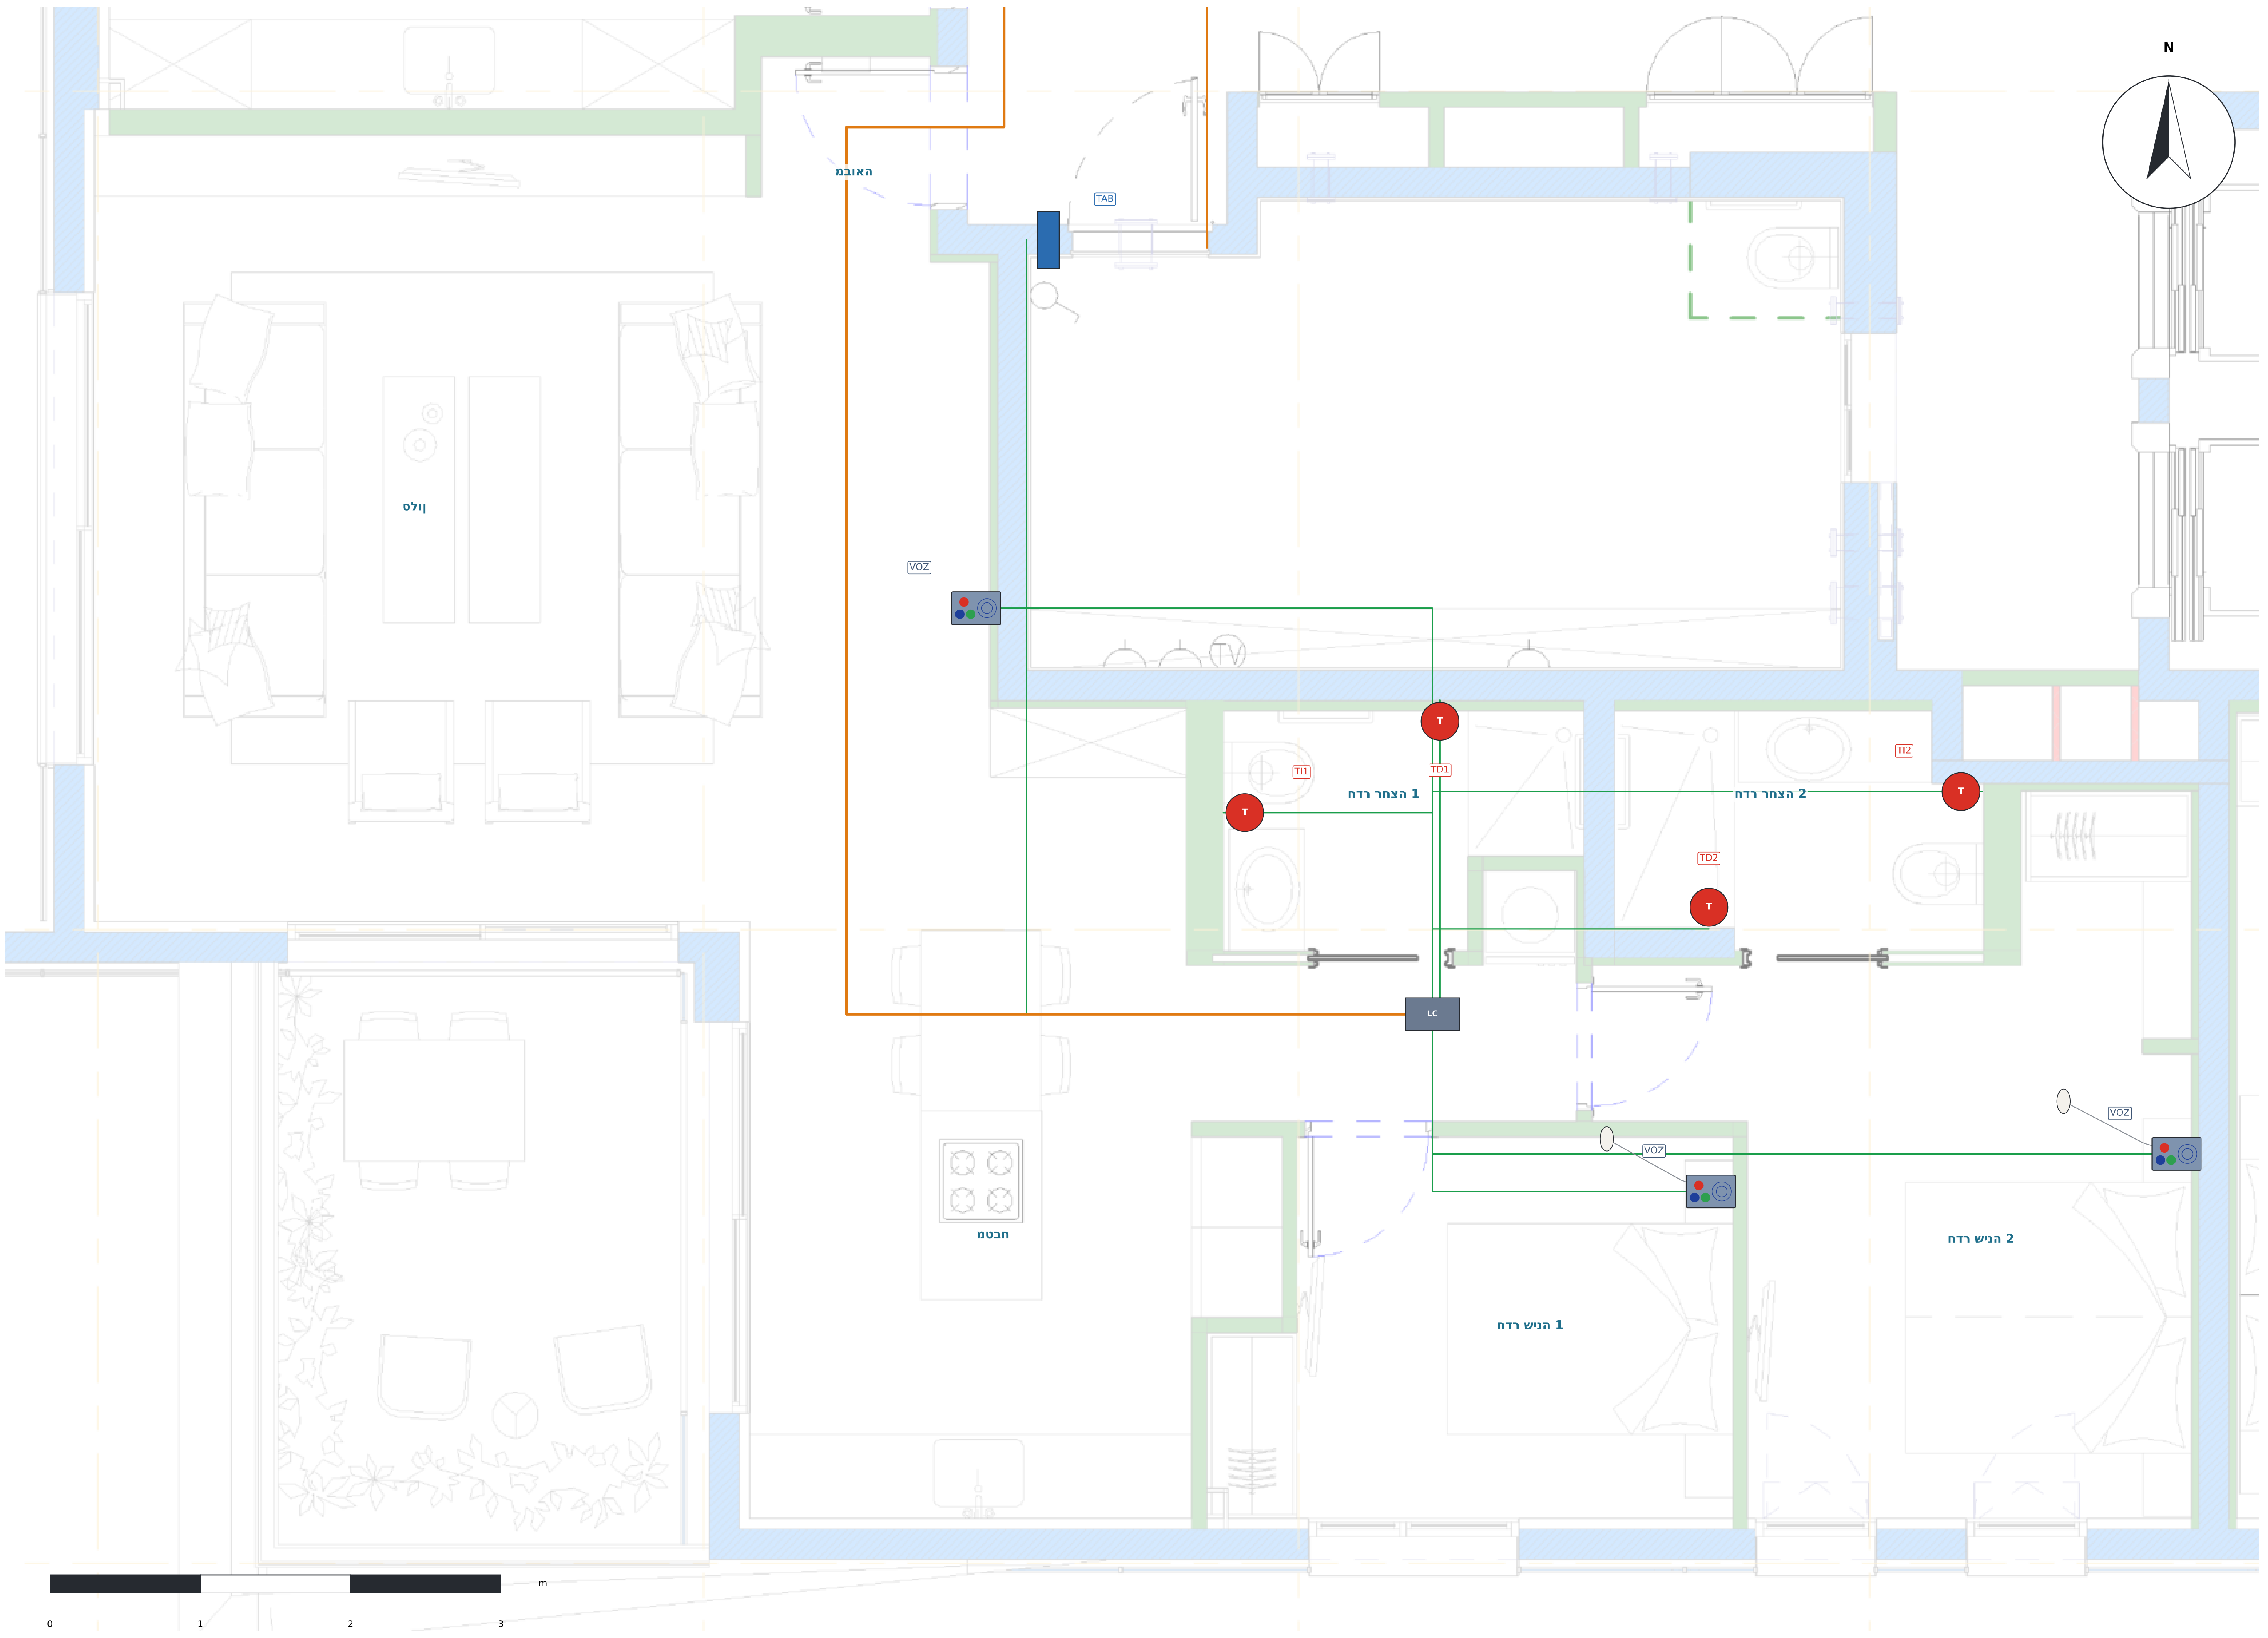
N
האובמ
TAB
VOZ
ןולס
T
TI1
TD1
TI2
TD2
הצחר רדח 1
הצחר רדח 2
LC
VOZ
VOZ
חבטמ
הניש רדח 1
הניש רדח 2
0
1
2
3
m

הרידה דויצ

ID	ןקתה	רדח	הבוג
TAB	הסינכב טלבאט	האובמ	1.40 מ'
VOZ-S	םינצחל םע ילוק לנפ	ןולס	1,30 m
VOZ-D1	סגא + םינצחל םע ילוק לנפ	הניש רדח 1	1,20 m
VOZ-D2	סגא + םינצחל םע ילוק לנפ	הניש רדח 2	1,20 m
TI1	לבח תכישמ	הצחר רדח 1	1.85 מ'
TD1	לבח תכישמ	הצחר רדח 1	1.85 מ'
TI2	לבח תכישמ	הצחר רדח 2	1.85 מ'
TD2	לבח תכישמ	הצחר רדח 2	1.85 מ'
LCOM	LCom ACE71610003	האובמ	2,55 m

SYMBOLS · SÍMBOLOS · םילמס

🟦	TAB · הסינכב טלבאט (iPad / דיאורדנא) – רובידו האירק, הבוג 1.40 מ' Door tablet – call and voice · הסינכב טלבאט – רובידו האירק
● ● ○	VOZ · םינצחל םע ילוק לנפ ACE82182451 – ןולס ירדחו הניש, הבוג 1.20–1.30 מ' Voice panel with buttons – living room and bedrooms · םינצחל םע ילוק לנפ – ןולס ירדחו הניש
○	סגא האירק דיל הטימה (הנישה ירדחב) Call pear next to the bed (bedrooms) · סגא האירק דיל הטימה
T	TI / TD · לבח תכישמ ACE40320303W – אסלה ותחלקמו, הבוג 1.85 מ' Pull-cord – toilet and shower, h 1.85 m · לבח תכישמ – אסלה ותחלקמו, הבוג 1.85 מ'
🟥	LP · תרונמ ןורדסמ ACE41020309 – לעמ תלד לכ שירותים ציבוריים Corridor light – above each public toilet door · תרונמ ןורדסמ – לעמ תלד לכ שירותים ציבוריים
LC	LC · LCom ACE71610003 – זכרמ הרידה (הרקת) LCom – apartment hub (ceiling) · LCom – זכרמ הרידה (הרקת)
BC	BC · BoxCom ACE70810000 – זכרמ סאב לכמה תוריד (הרקת) BoxCom – bus hub for several apartments (ceiling) · BoxCom – זכרמ סאב לכמה תוריד (הרקת)

NOTES · תורעה

1. הרידב x03 ואות דויצ (ירדח הצחרה הסירפב הנוש).
2. טלבאט יבולב, דיל תלד הסינכה (ומיס «tab» לש חוקלה).
3. לנפ ילוק ןולסב ינשבו ירדח הנישה (םע סגא דיל הטימה).
4. 2 ירדח הצחר: תכישמ לבח הלסאב ובמקלחת לכב דחא (4 תוכישמ לבח).
5. לוכה רבוחמ תילאידר ב-Cat6 ל-LCom ןורדסמב ירדח הנישה.

שירותים קריאת אחות

לבח תכישמ

טבלט אנדרואיד קריאת אחות
Advantecnia
Llamada de enfermera
Hospital
Salud y bienestar

הסינכב טלבאט (iPad / דיאורדנא)

מנורה קריאת אחות

ןורדסמ תרונמ

פנל קריאת אחות

םינצחל םע ילוק לנפ

ןגומ רויד · ןוכיתה םי ילדגמ
תוריד 32 · תומוק 8 + עקרק – תוחא תאירק
Telab International :ןכוה ע"י ACE BG · Advantecnia :תכרעמ

הניש ירדח ינש תריד (x04 / x03)
2-bedroom apartment (x04 / x03)

SCALE · הדימ הנק	DATE · ךיראת	REV	ןוילג
1:35	15/10/2026	B	06

סיסב: תינכות לכירדאה L5 (זוע דסמ / Triplet) · םירטמב תודימ
טמרופ A1 · הרודהמ B – לע תינכותה תיתימאה

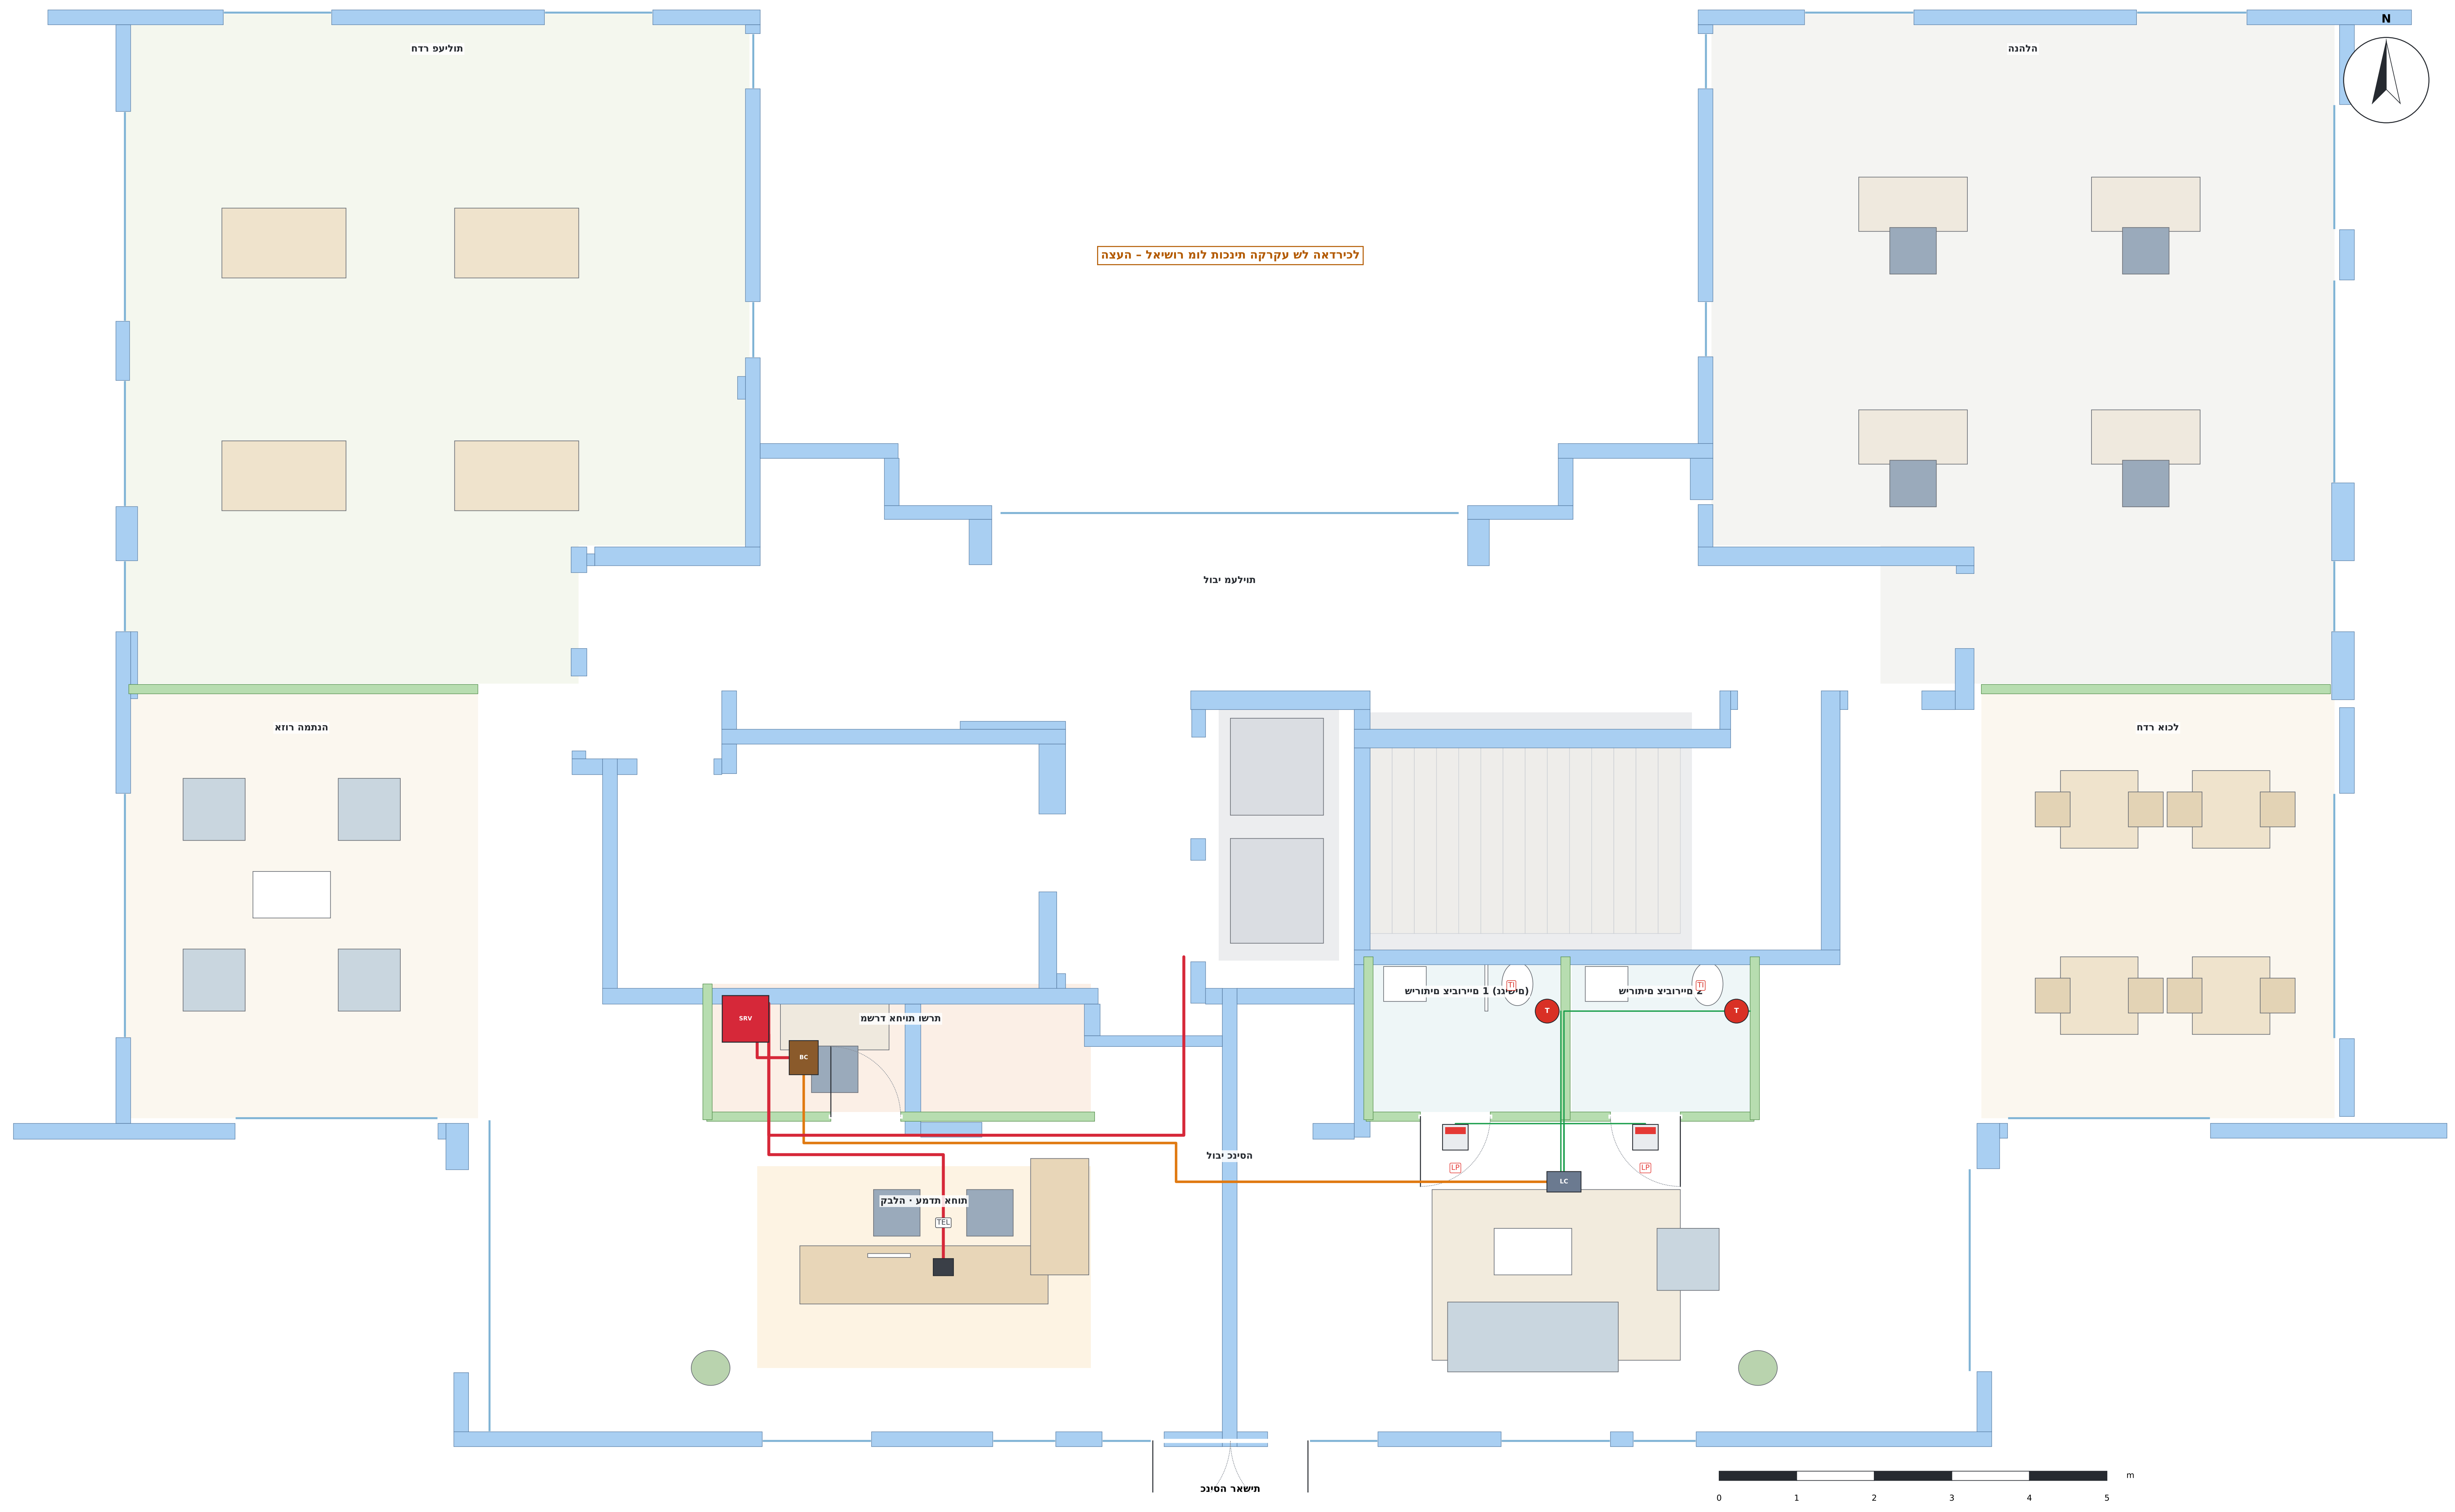
חדר פעילות
הערה – לאישור מול תוכנית הקרקע של האדריכל
הנהלה
N
לובי מעליות
אזור המתנה
חדר אוכל
SRV
BC
משרד אחיות ושרת
שירותים ציבוריים 1 (נשים)
שירותים ציבוריים 2
TI
T
LP
LC
לובי כניסה
קבלה · עמדת אחות
TEL
כניסה ראשית
0
1
2
3
4
5
m

פרט · קבלה ועמדת אחות (1:40)

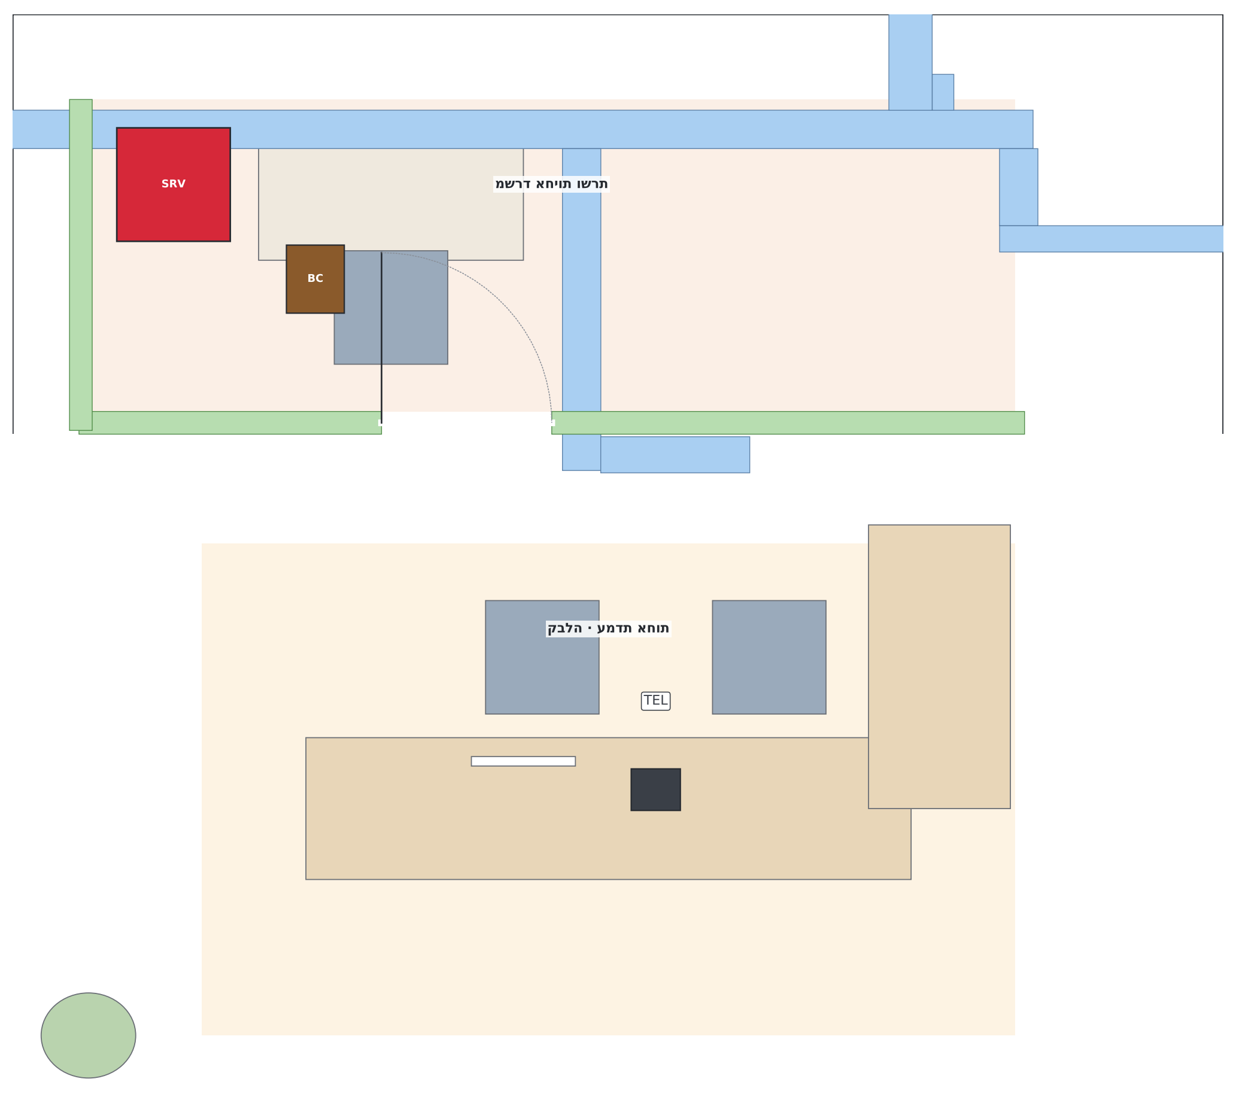
SRV
BC
משרד אחיות ושרת
קבלה · עמדת אחות
TEL

NOTES · הערות

1. עמדת האחות בקבלה, מול הכניסה והמעליות.
2. על העמדה: טלפון Grandstream אנדרואיד, מחובר ישירות למתג ה-PoE. כל קריאה מוצגת בצבע שלה.
3. מאחורי העמדה: משרד עם הארון הראשי: שרת Buslogic Premium ומתג PoE D-Link. BoxCom של הקרקע בתקרה.
4. 2 שירותים ציבוריים בקרקע: משיכת חבל ליד האסלה ומנורת מסדרון מעל כל דלת.
5. העמוד מ-8 הקומות יורד בגרעין עד הארון הראשי.
6. פריסת קרקע מוצעת: תעודכן כשתגיע תוכנית של האדריכל.

SYMBOLS · SÍMBOLOS · סמלים

T — TI / TD · משיכת חבל ACE40320303W – אסלה ומקלחת, גובה 1.85 מ'
Pull-cord – toilet and shower, h 1.85 m · משיכת חבל – אסלה ומקלחת, גובה 1.85 מ'

LC — LC · LCom ACE71610003 – מרכז דירה (תקרה)
LCom – apartment hub (ceiling) · LCom – מרכז דירה (תקרה)

SRV — SRV · ארון קרקע: שרת Buslogic Premium + מתג PoE D-Link
GF rack: Buslogic Premium server + D-Link PoE switch · ארון קרקע: שרת Buslogic Premium + מתג PoE D-Link

LP · מנורת מסדרון ACE41020309 – מעל דלת כל שירותים ציבוריים
Corridor light – above each public toilet door · מנורת מסדרון – מעל דלת כל שירותים ציבוריים

TEL — TEL · טלפון Grandstream אנדרואיד – PoE ישירות למתג
Grandstream Android phone – PoE straight to the switch · טלפון Grandstream אנדרואיד – PoE ישירות למתג

BC — BC · BoxCom ACE70810000 – מרכז באס לכמה דירות (תקרה)
BoxCom – bus hub for several apartments (ceiling) · BoxCom – מרכז באס לכמה דירות (תקרה)

טלפון העמדה – איזה צבע מוצג

🟥	אזעקה (SOS / משיכה)	אדום
🟩	נוכחות: לחצן ירוק פעם אחת	ירוק
⬜	מבטל קריאה או אזעקה: לחצן ירוק שוב	נמחק
🟦	קריאת רופא: לחצן כחול (blue call)	כחול
🟧	שיחה קולית	כתום / צהוב

מגדלי ים התיכון · דיור מוגן
32 דירות · 8 קומות + קרקע – קריאת אחות
הוכן ע"י: Telab International   מערכת: ACE BG · Advantecnia

קומת קרקע · לובי ועמדת אחות

Ground floor · lobby and nurse desk

SCALE · קנה מידה
1:60
DATE · תאריך
15/10/2026
REV
B
גיליון
07

בסיס: תוכנית האדריכל L5 (מסד זוג / Triplet) · מידות במטרים
פורמט A1 · מהדורה B – על התוכנית האמיתית

א · בניין קרקע + 8 קומות

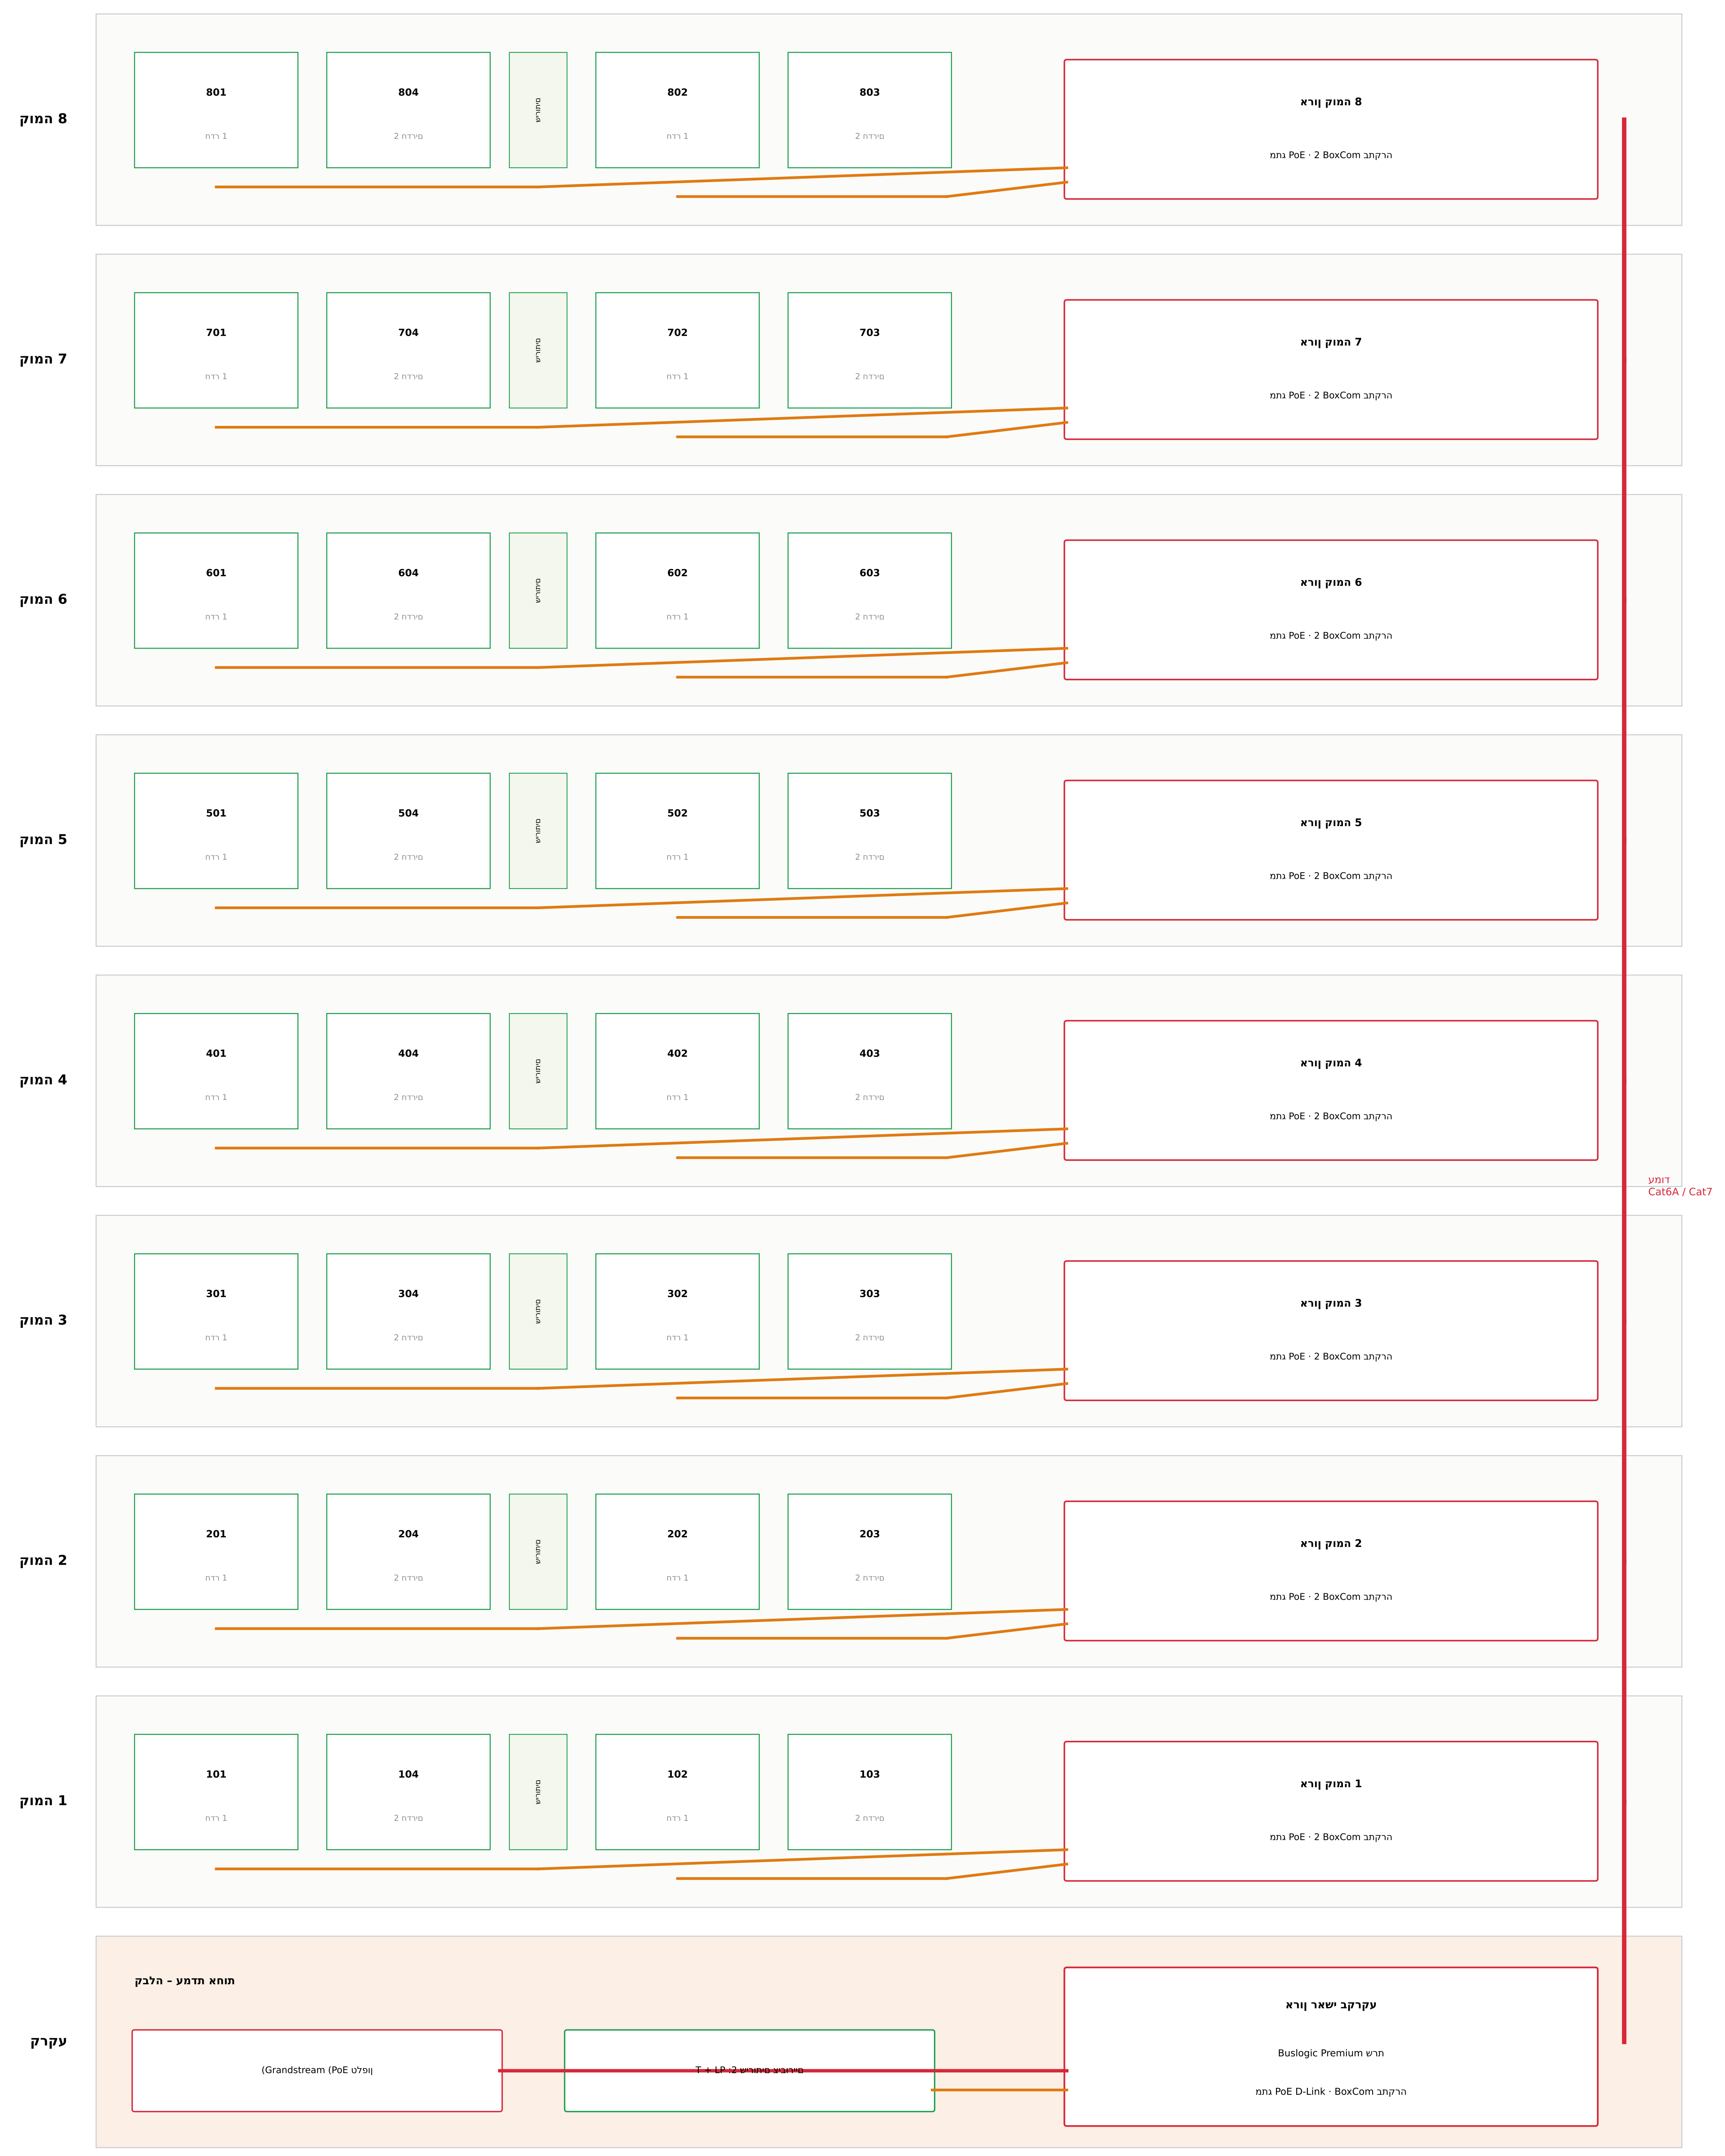
קומה 8
801
1 חדר
804
2 חדרים
שירותים
802
1 חדר
803
2 חדרים
ארון קומה 8
בתקרה 2 BoxCom · מתג PoE
קומה 7
701
704
702
703
ארון קומה 7
קומה 6
601
604
602
603
ארון קומה 6
קומה 5
501
504
502
503
ארון קומה 5
קומה 4
401
404
402
403
ארון קומה 4
קומה 3
301
304
302
303
ארון קומה 3
קומה 2
201
204
202
203
ארון קומה 2
קומה 1
101
104
102
103
ארון קומה 1
עמוד
Cat6A / Cat7
קרקע
קבלה – עמדת אחות
טלפון Grandstream (PoE)
שירותים ציבוריים 2: T + LP
ארון ראשי בקרקע
שרת Buslogic Premium
בתקרה BoxCom · מתג PoE D-Link

ב · טופולוגיה של דירה

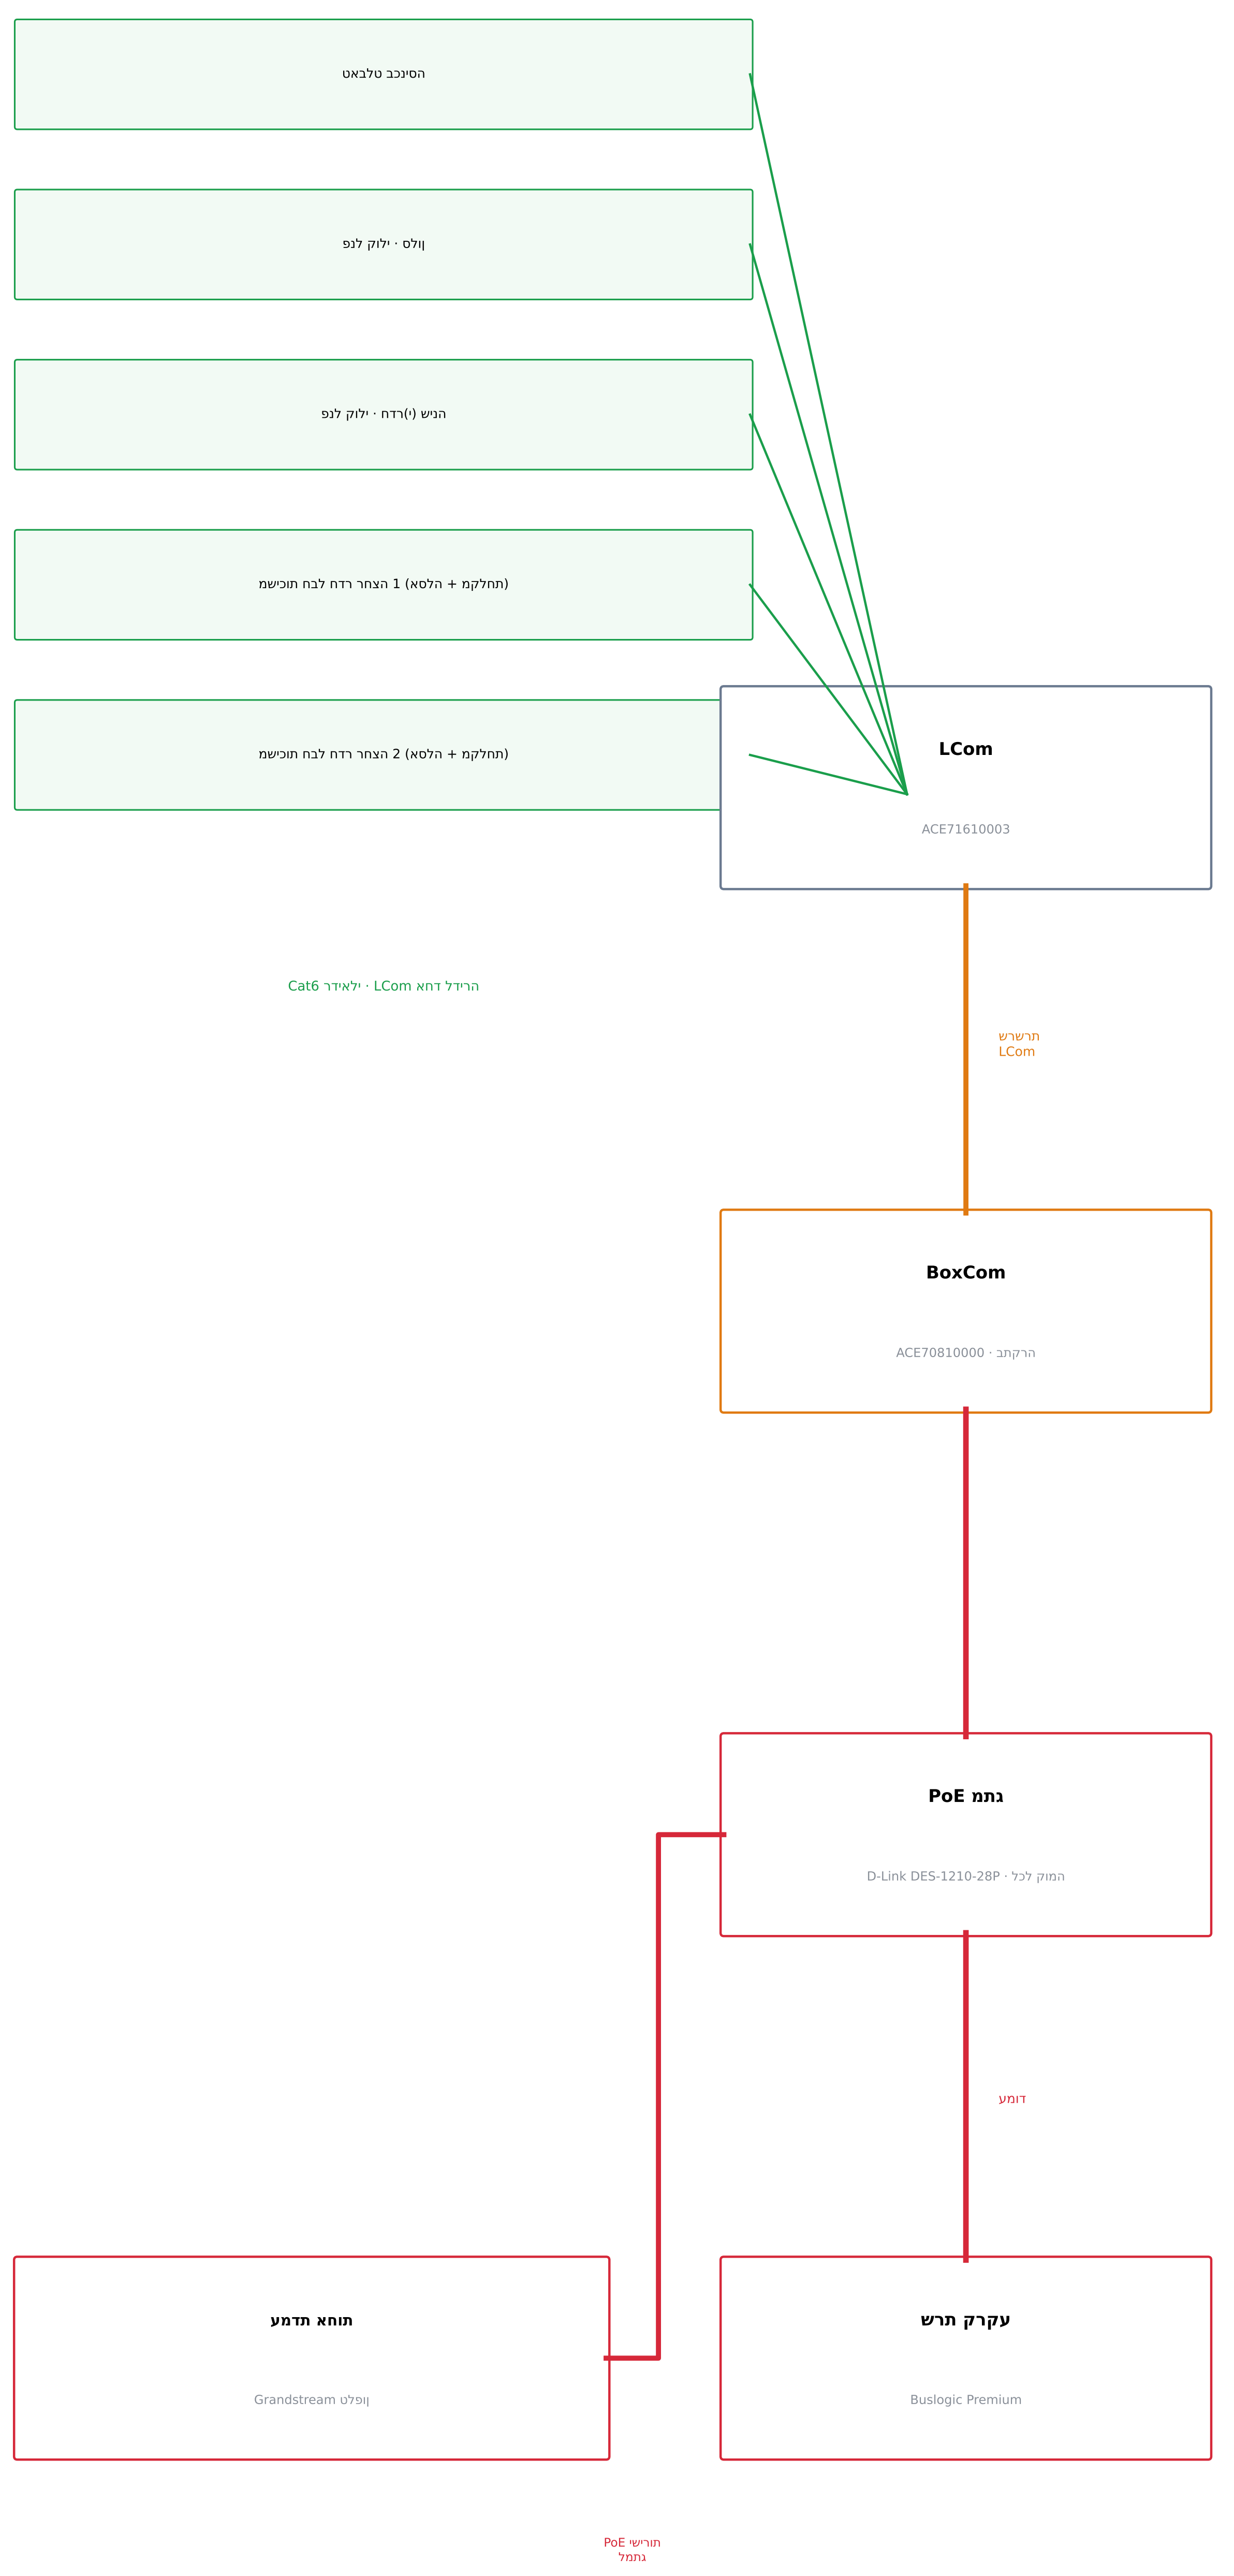
טאבלט בכניסה
פנל קולי · סלון
פנל קולי · חדר(י) שינה
משיכות חבל בכל חדר רחצה 1 (אסלה + מקלחת)
משיכות חבל בכל חדר רחצה 2 (אסלה + מקלחת)
LCom
ACE71610003
LCom אחד לדירה · Cat6 אידיאלי
שרשרת
LCom
BoxCom
ACE70810000 · בתקרה
מתג PoE
D-Link DES-1210-28P · לכל קומה
עמוד
עמדת אחות
טלפון Grandstream
שרת קרקע
Buslogic Premium
PoE ישירות
למתג

NOTES · הערות

1. 8 קומות זהות עם 4 דירות
(2 דירות חדר שינה אחד ו-2 דירות שני חדרי שינה).

2. בכל קומה: 2 BoxCom בתקרה
וארון עם מתג ה-PoE.

3. שרשרת 1: x01 ← x04 ← שירותים ציבוריים.
שרשרת 2: x03 ← x02.

4. המתגים מחוברים דרך העמוד
עד הארון הראשי בקרקע.

5. טלפון ה-Grandstream בעמדה מחובר
ישירות למתג ה-PoE ומציג
כל קריאה בצבע שלה.

6. כל המערכת PoE.

7. כמויות ראשוניות: לאמת
מול Advantecnia ובאתר.

מגדלי ים התיכון · דיור מוגן
קריאת אחות – קרקע + 8 קומות · 32 דירות
מערכת: ACE BG · Advantecnia   הוכן ע"י: Telab International

תרשים אנכי וטופולוגיה
Riser diagram and topology

SCALE · קנה מידה	DATE · תאריך	REV	גיליון
S/E	15/10/2026	B	08

בסיס: תוכנית האדריכל L5 (מסד זוג / Triplet) · מידות במטרים
פורמט A1 · מהדורה B – על התוכנית האמיתית

רשימת חומרים – כל הבניין (קרקע + 8 קומות · 32 דירות · 10 שירותים ציבוריים)

קוד	**תיאור**	**כמות**	**הערה**
בדירות (32)			
TAB	טאבלט בכניסה (iPad / אנדרואיד) – קריאה ודיבור	**32**	1 לכל דירה
VOZ	ACE82182451 – פנל קריאה קולי עם לחצנים	**80**	סלון + כל חדר שינה
TI/TD	משיכת חבל – ACE40320303W (אסלה ומקלחת)	**128**	4 לכל דירה
LC	LCom – ACE71610003	**32**	1 לכל דירה
שירותים ציבוריים (10)			
T	ACE40320303W – משיכת חבל	**10**	8 קומות + 2 בקרקע
LP	ACE41020309 – מנורת מסדרון	**10**	מעל כל דלת
LC	LCom – ACE71610003	**9**	1 לכל קומה + 1 בקרקע
ארונות ומרכזייה			
BC	BoxCom – ACE70810000 (בתקרה)	**17**	2 לקומה + 1 בקרקע
SW	D-Link DES-1210-28P – מתג 24 יציאות PoE	**9**	1 לכל קומה + קרקע
GAB	ארון ריק 12U עם פאץ' פאנל (למתג)	**8**	1 לכל קומה
GAB-PB	ארון ראשי עומד עם UPS	**1**	קרקע
SRV	שרת Buslogic Premium (Advantcare) עם תוכנה	**1**	קרקע
TEL	טלפון אנדרואיד Grandstream (PoE, צבע לפי סוג קריאה)	**1**	עמדת אחות
כבלים (+ 15% רזרבה)			
—	Cat6 רדיאלי בתוך הדירה (ירוק)	**1700 m**	183 מ' לקומה
—	Cat6 / Cat7 שרשרת LCom ← BoxCom (כתום)	**750 m**	80 m por piso
—	Cat6A / Cat7 ארונות ועמוד (אדום)	**130 m**	כולל עמוד

NOTES · הערות

1. כמויות מחושבות מהמודל (קומה טיפוסית × 8 + קרקע).
2. אורכי כבל נמדדו על התוואי המשורטט, + 15%.
3. מחירים: לפי מחירון Advantecnia העדכני.
4. לאמת באתר לפני רכישה.

מגדלי ים התיכון · דיור מוגן

קריאת אחות – קרקע + 8 קומות · 32 דירות

מערכת: ACE BG · Advantecnia הוכן ע"י: Telab International

רשימת חומרים

Bill of materials

SCALE · קנה מידה
S/E

DATE · תאריך
15/10/2026

REV
B

גיליון
09

בסיס: תוכנית האדריכל L5 (מסד עוז / Triplet) · מידות במטרים

פורמט A1 · מהדורה B – על התוכנית האמיתית

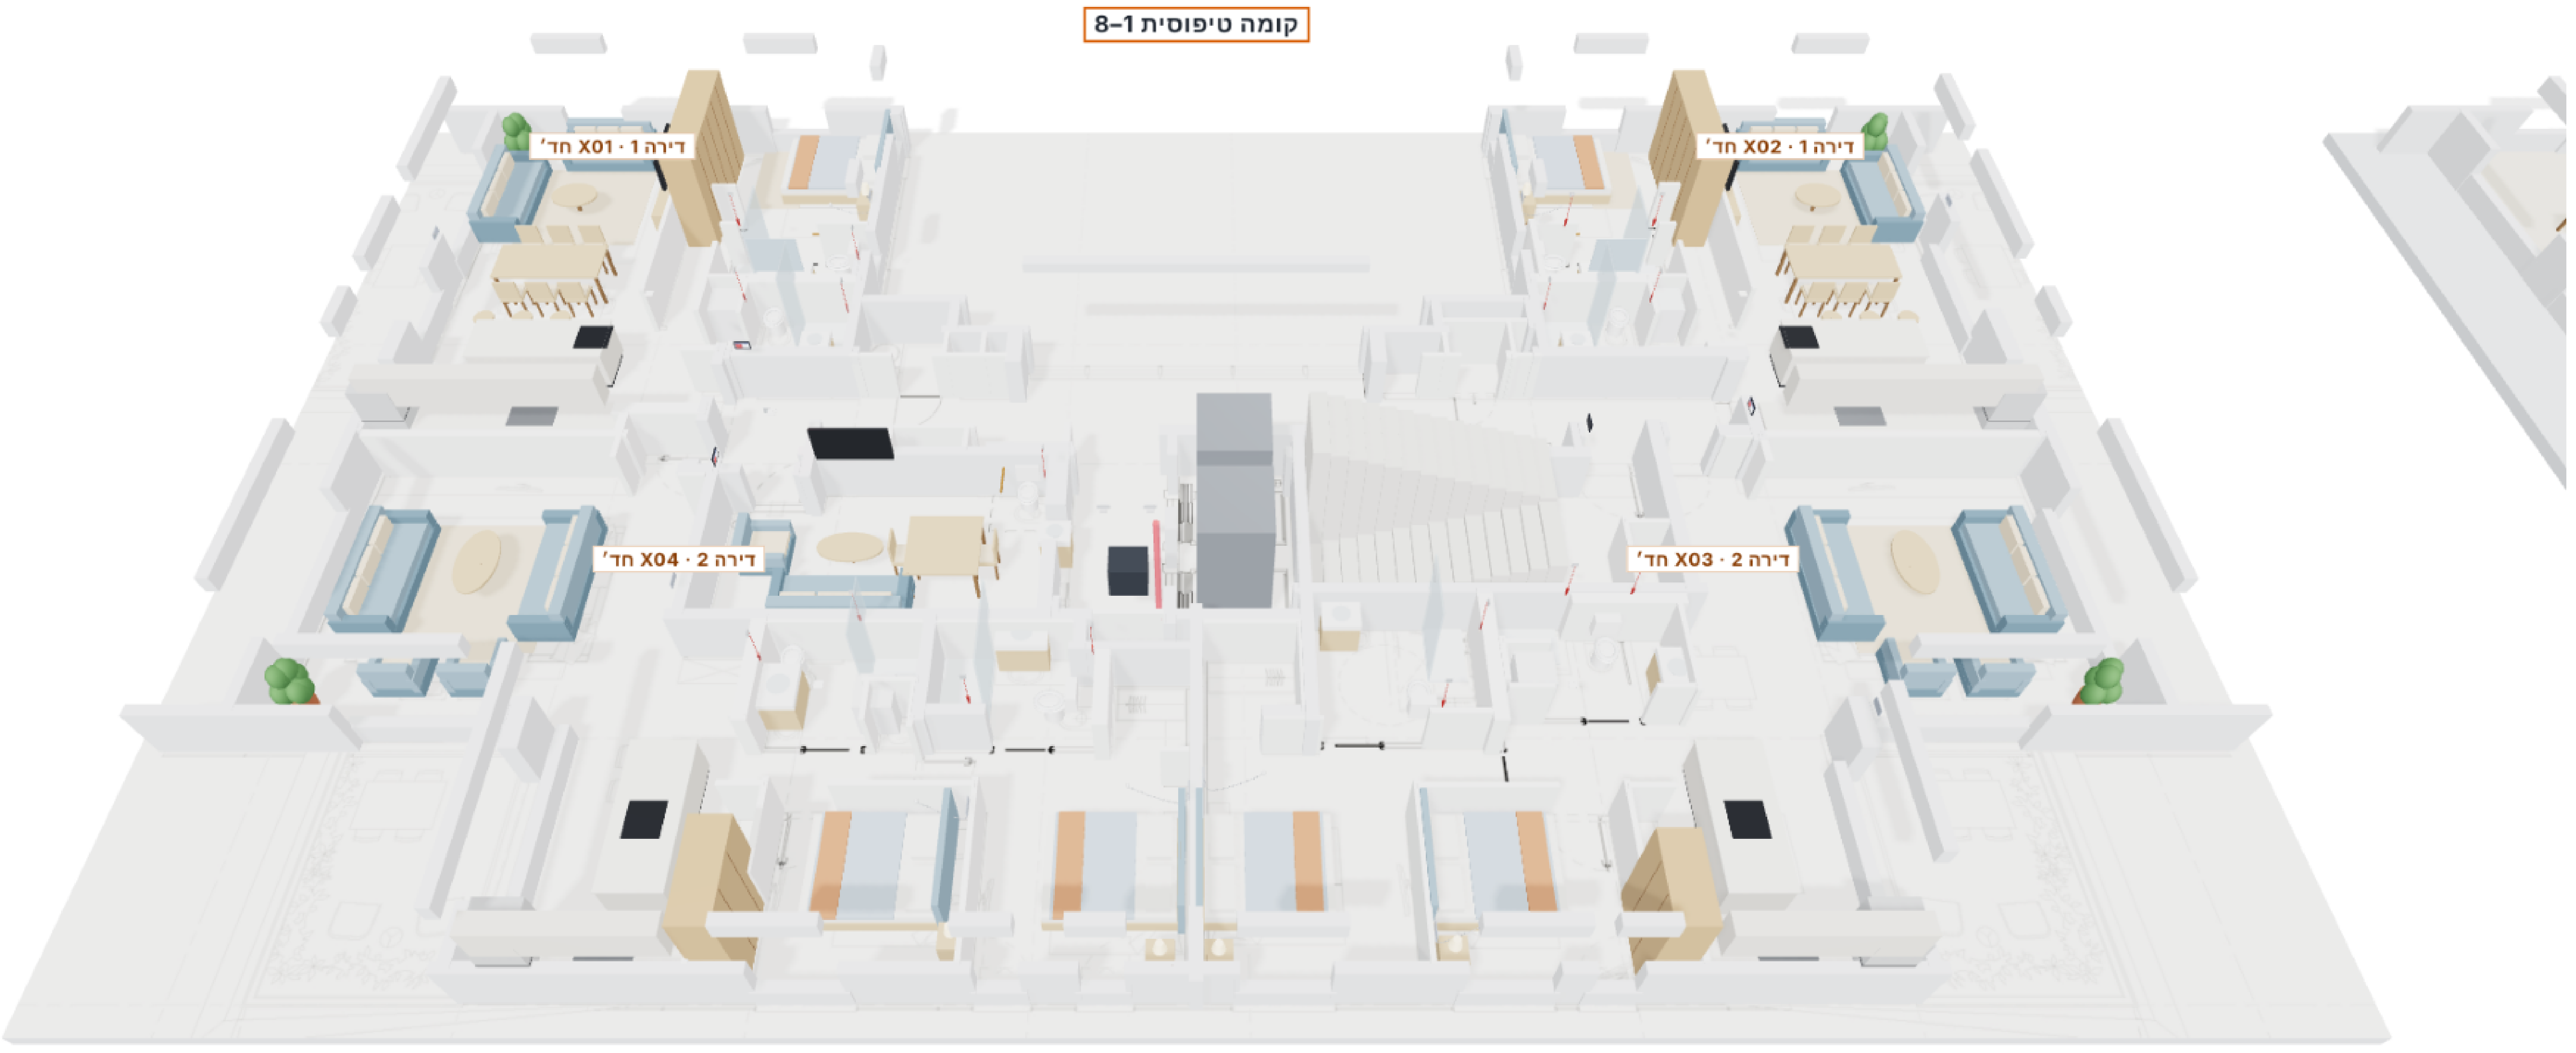
קומה טיפוסית 1–8
דירה 1 · X01 חד׳
דירה 1 · X02 חד׳
דירה 2 · X04 חד׳
דירה 2 · X03 חד׳

תוריד 4 – תיסופיט המוק · א

הסינכב טלבאט · ב

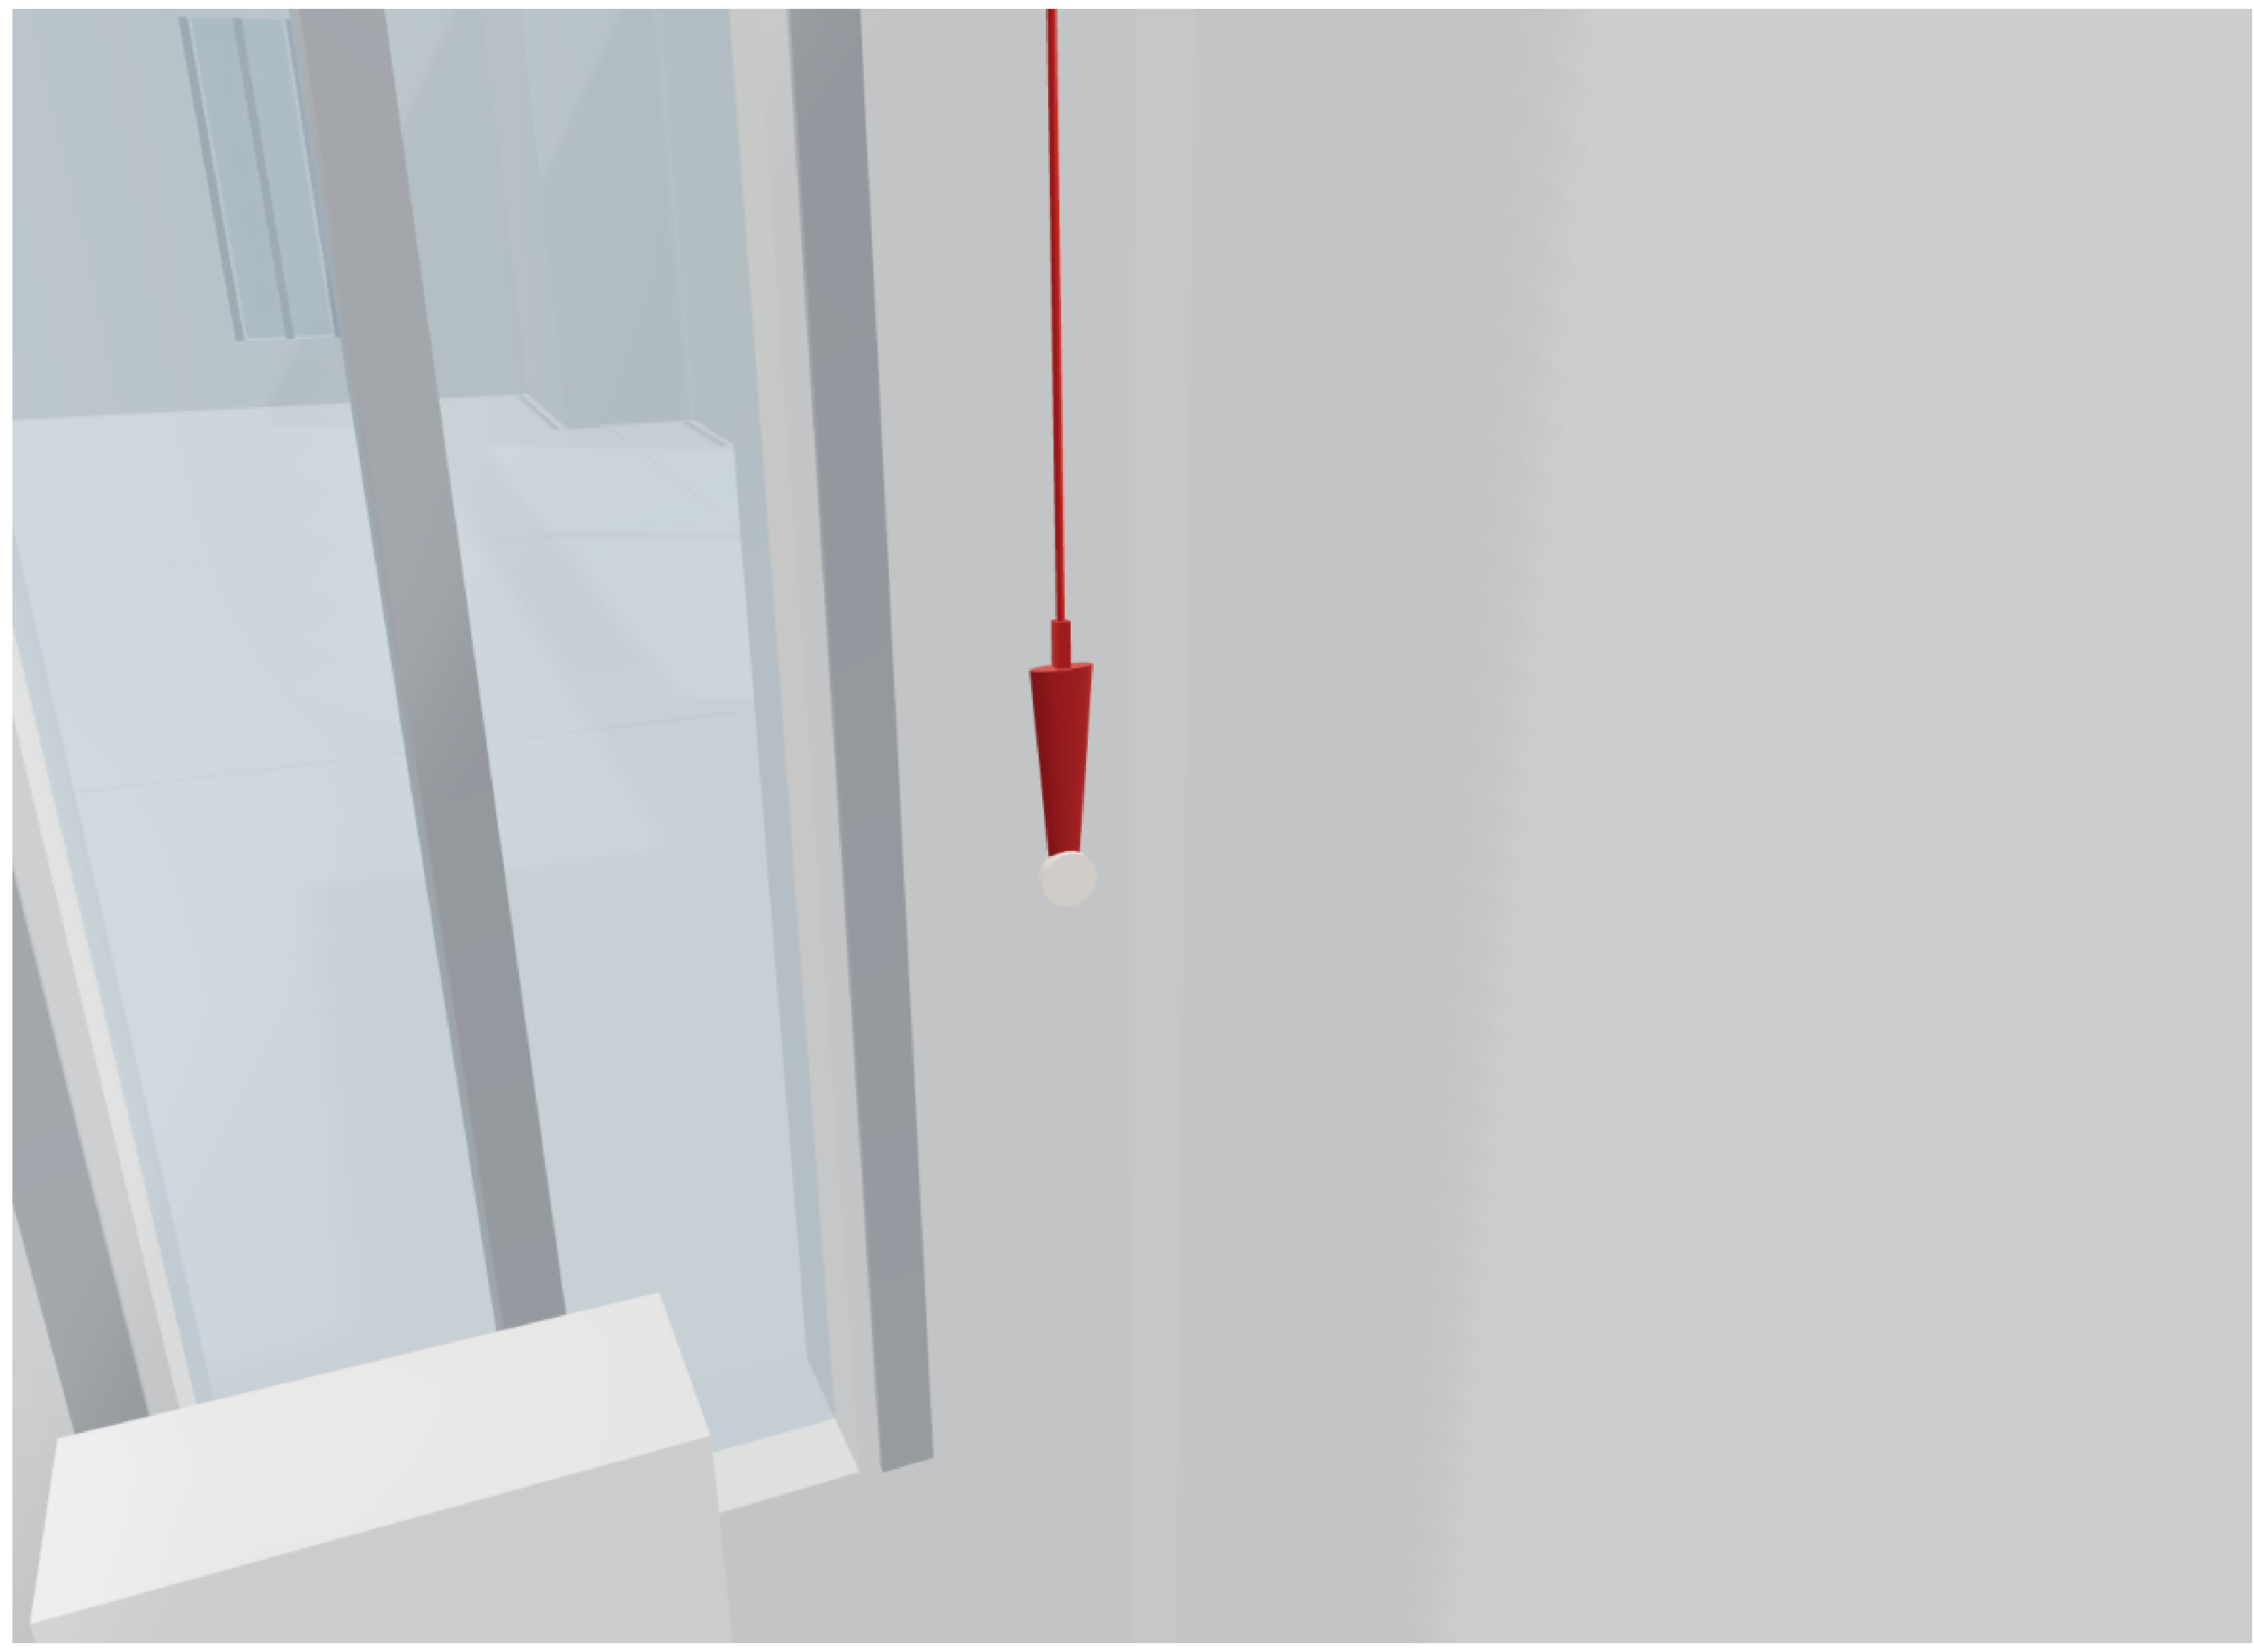

תחלקמבו הלסאב לבח תוכישמ – הצחר רדח · ד

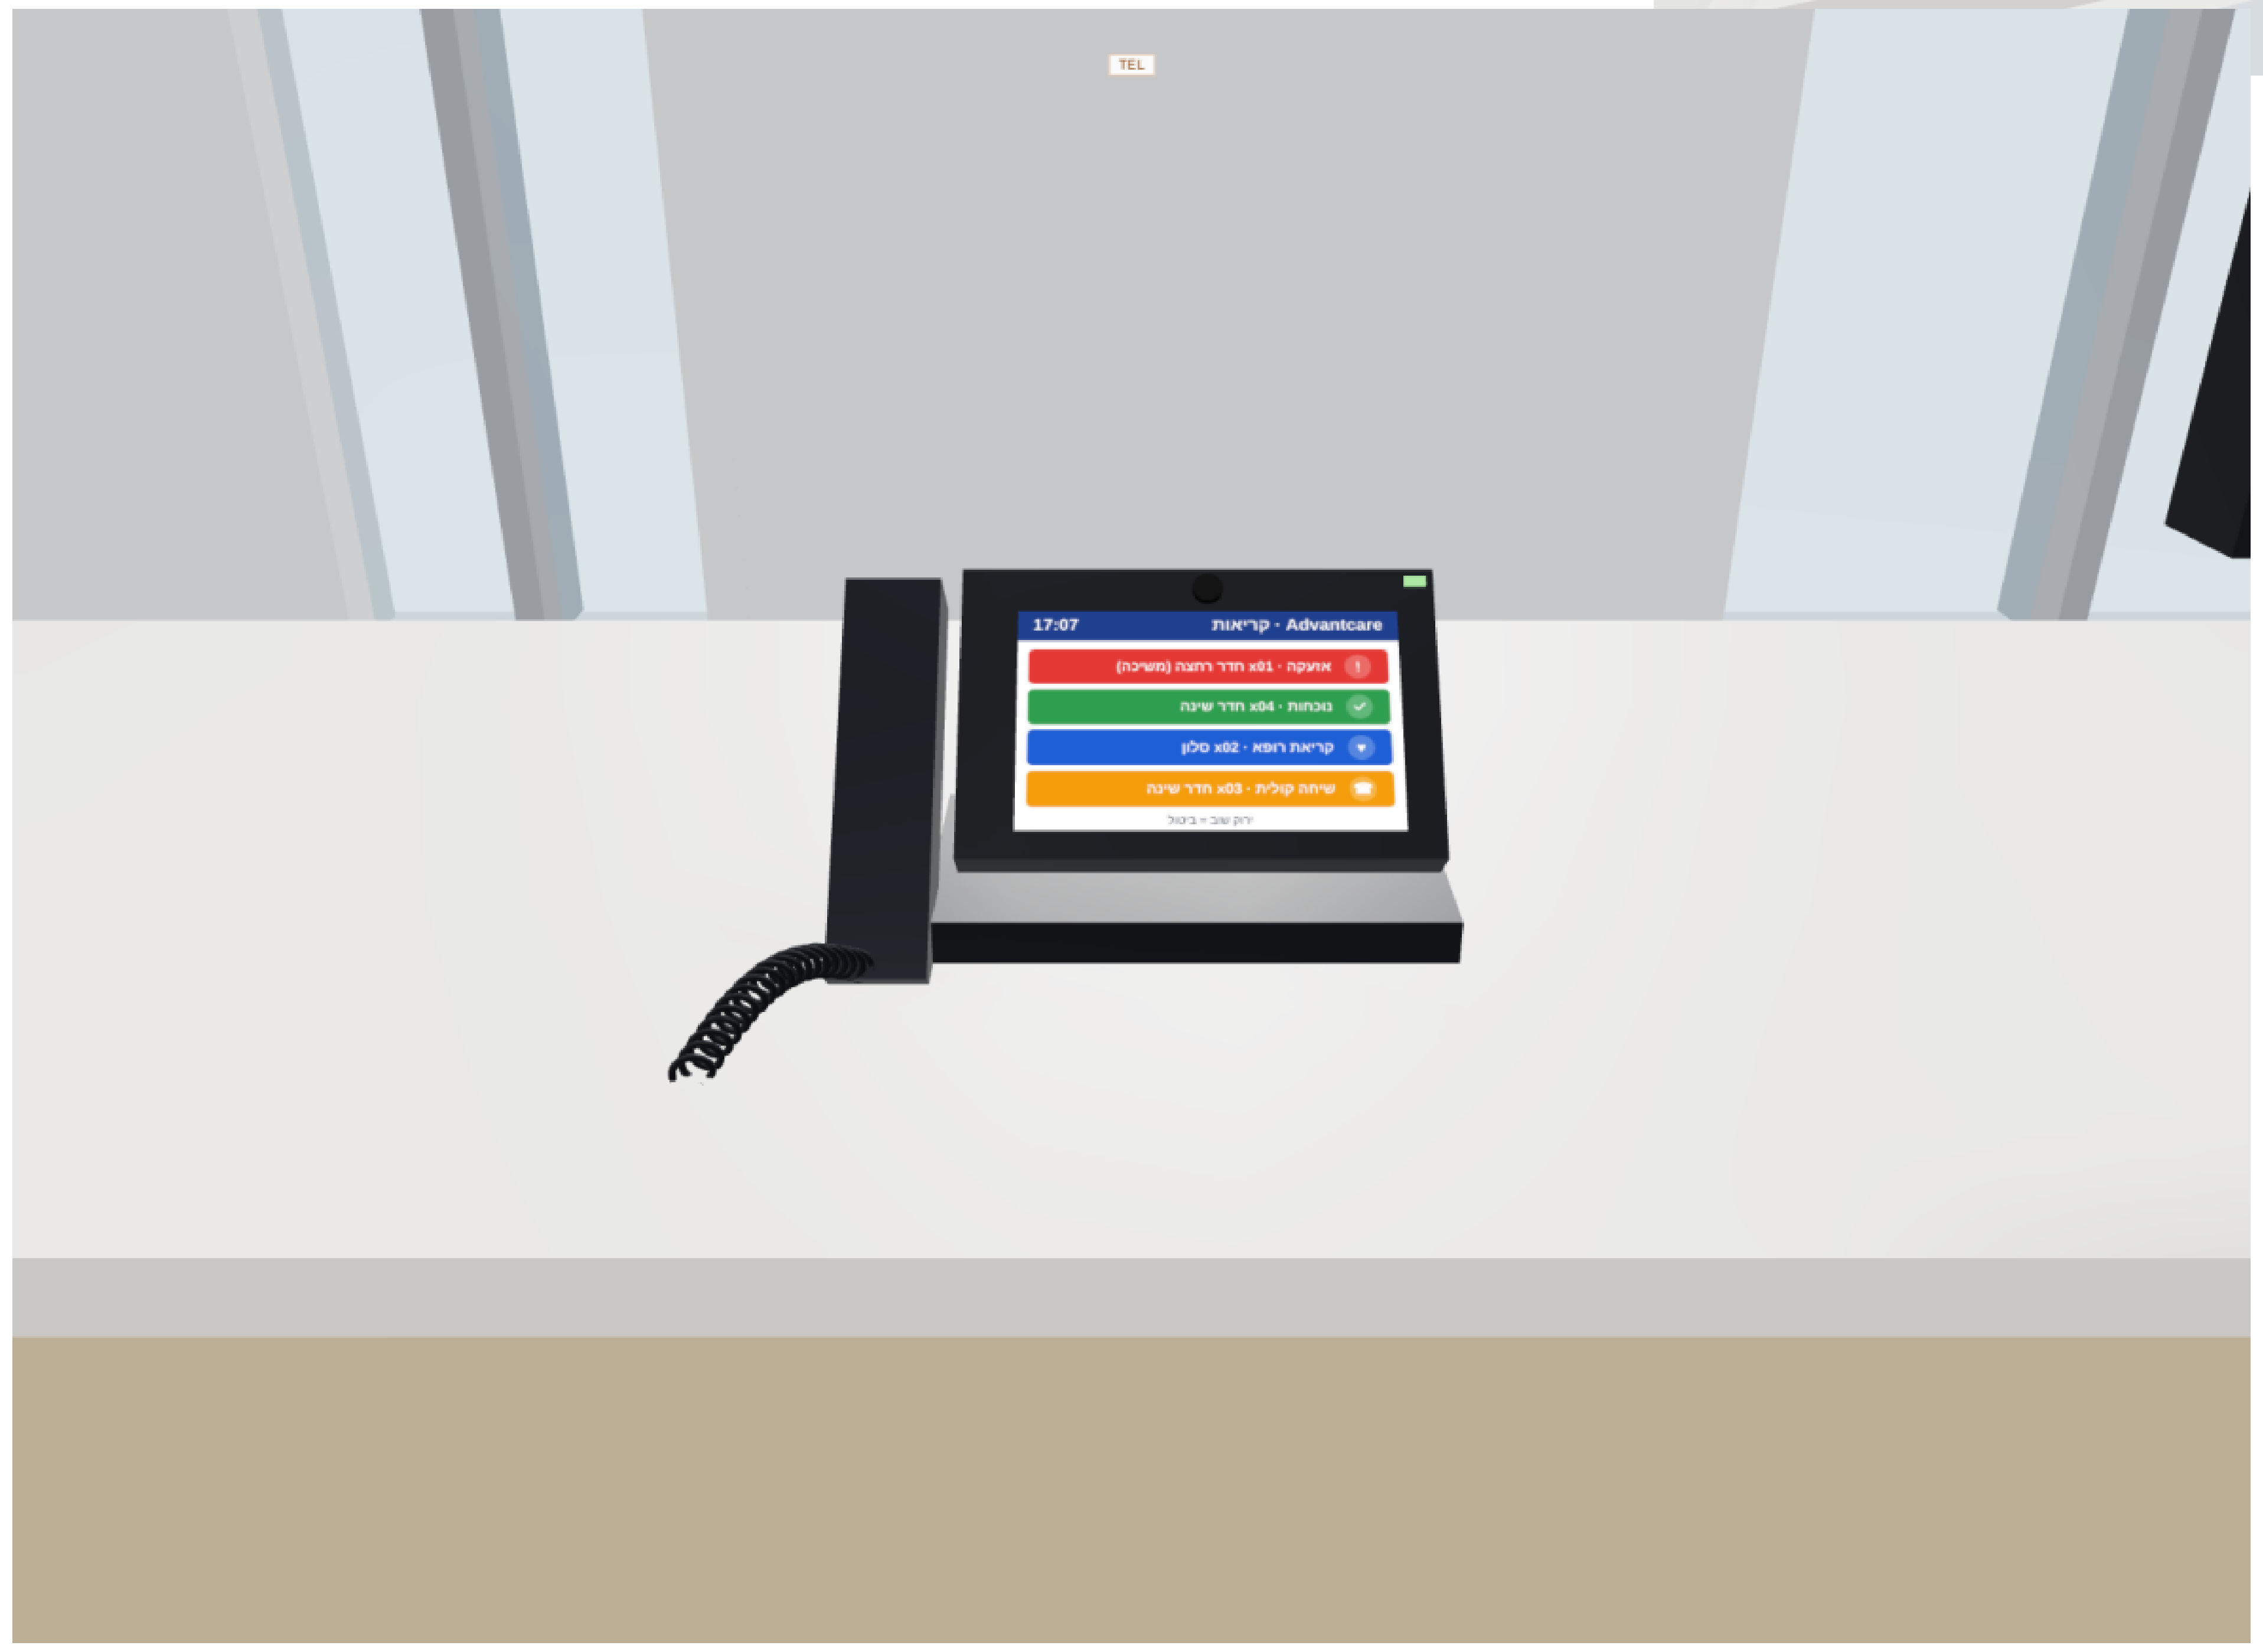

17:07 קריאות · Advantcare

אזעקה · x01 חדר רחצה (משיכה)

נוכחות · x04 חדר שינה

קריאת רופא · x02 סלון

שיחה קולית · x03 חדר שינה

ירוק שב = ביטול

תוחא תדמע – עקרק · ה

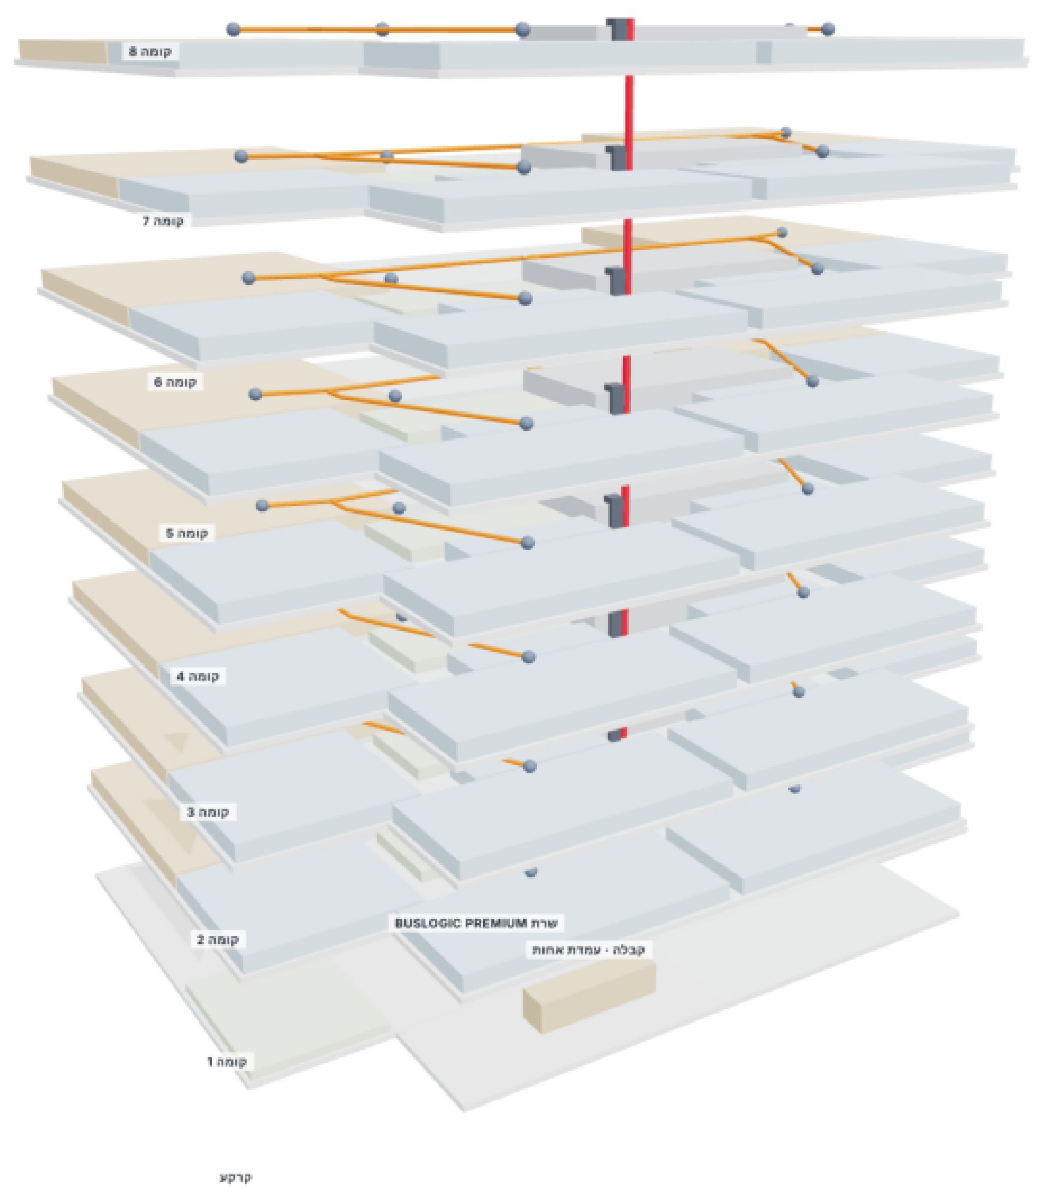
קומה 8
קומה 7
קומה 6
קומה 5
קומה 4
קומה 3
קומה 2
קומה 1
שרת BUSLOGIC PREMIUM
קבלה · עמדת אחות
קרקע

תומוק 8 + עקרק ןיינב · ו

ןגומ רויד · ןוכיתה םי ילדגמ

קרקא תוחא – עקרק + 8 תומוק · 32 תוריד

Telab International :ןכוה ע"י ACE BG · Advantecnia :תכרעמ

םיידממ-תלת םיטבמ

3D views

SCALE · הדימ הנק	DATE · ךיראת	REV	ןוילג
S/E	15/10/2026	B	10

סיסב: לכירדאה תינכות L5 (זוע דסמ / Triplet) · םירטמב תודימ

טמרופ A1 · הרודהמ B – לע תינכותה תיתימאה

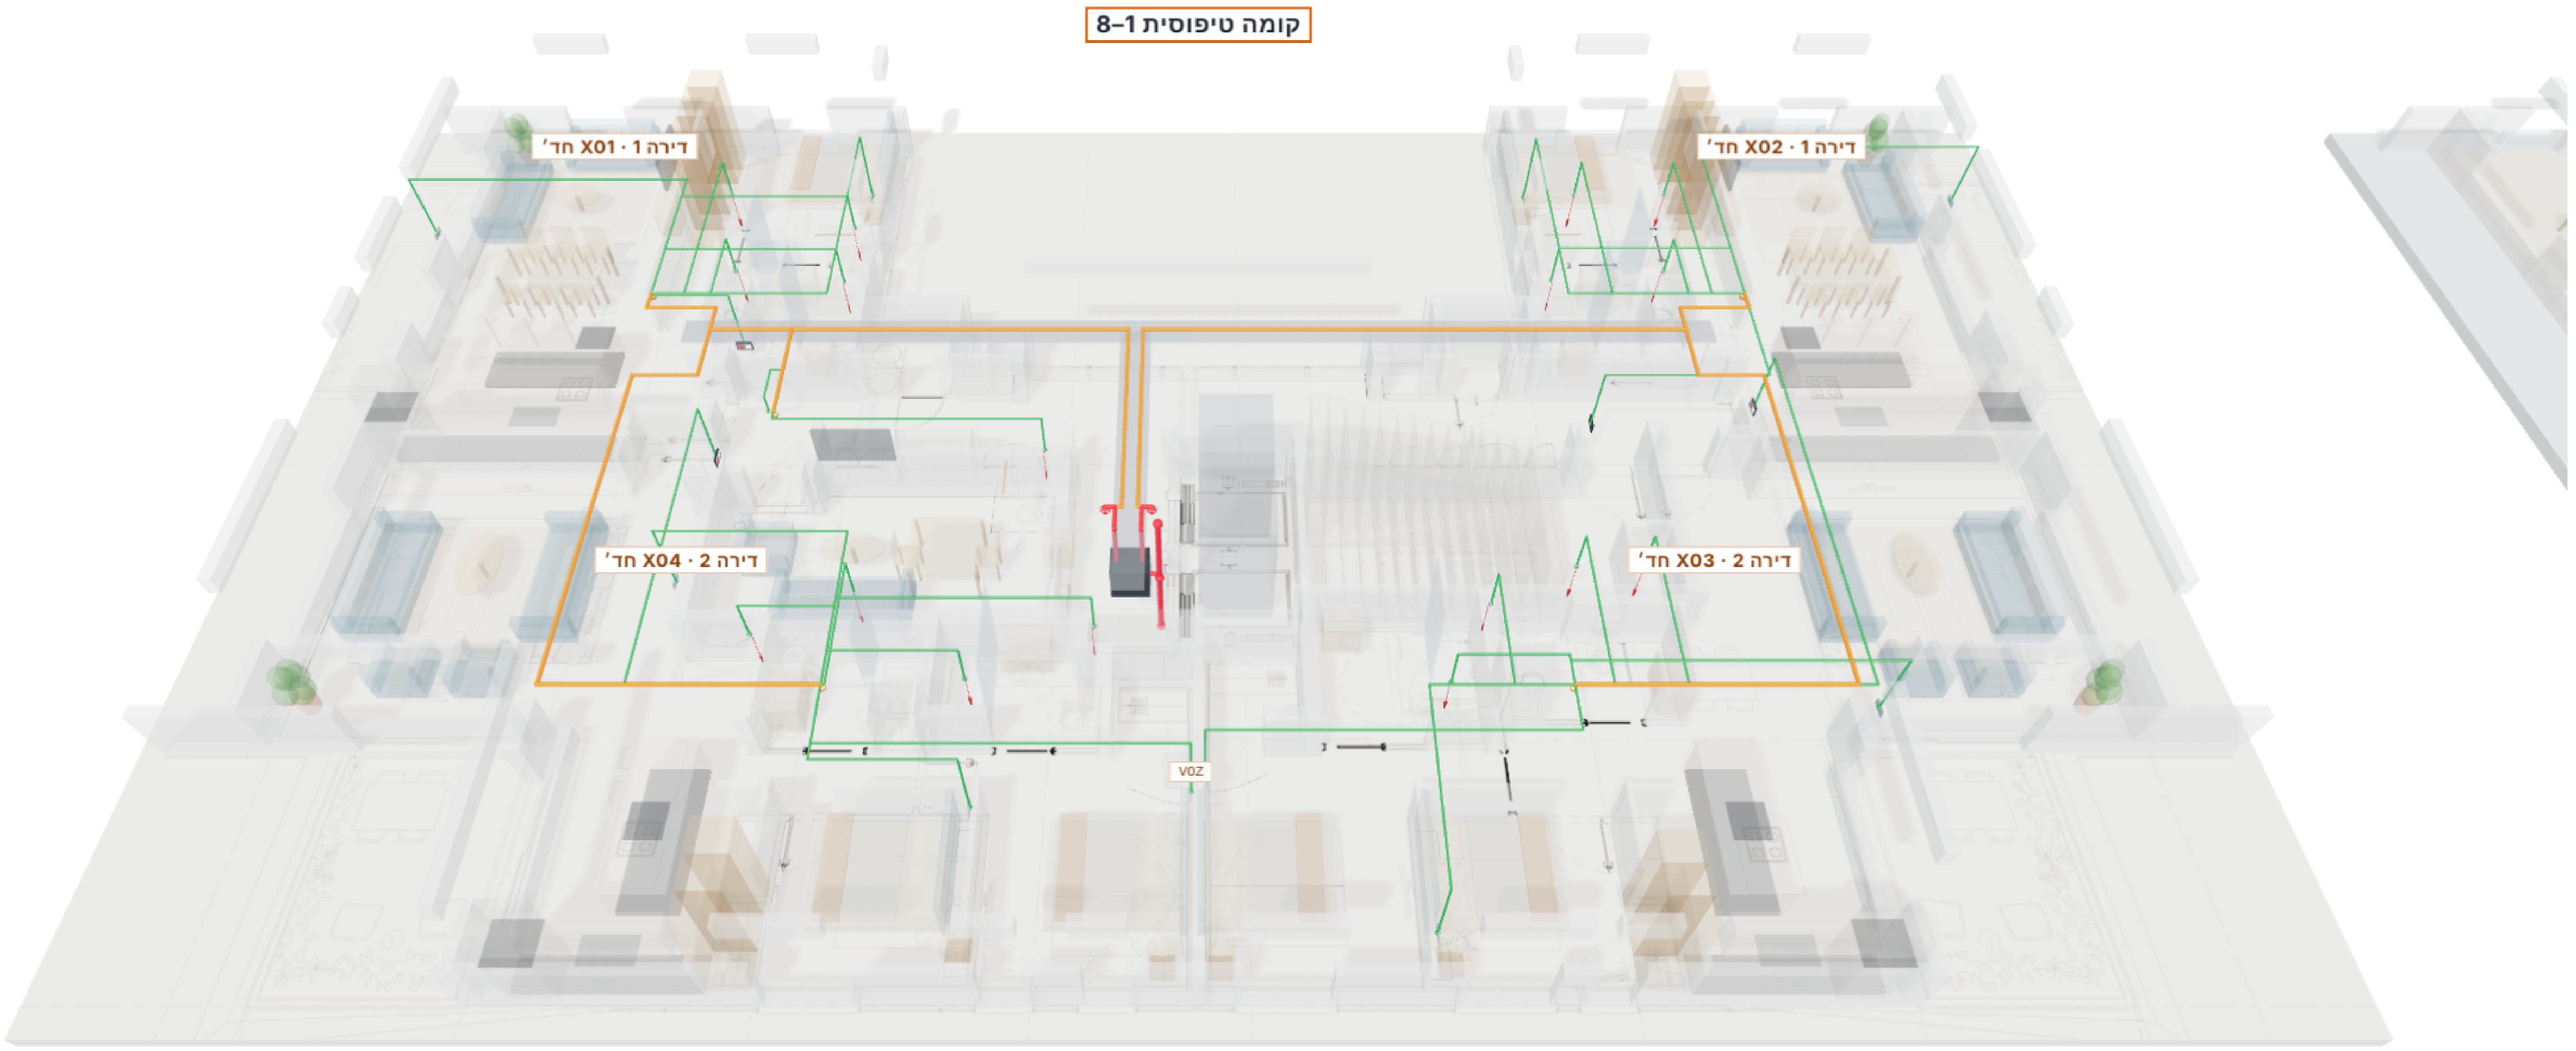

(תשר םודא · LCom תרשרש םותכ · ילאידר קורי) טוויח – תיסופיט המוק · א

הלבקו יבול – עקרק תמוק · ב

םינצחל םע ילוק לנפ – ןולס · ג

COLOURS · COLORES · םיעבצ

🟩 Cat6 ילאידר: לכ ןקתה ← LCom לש הרידה
Cat6 radial: each device → apartment LCom · Cat6 ילאידר: לכ ןקתה ← LCom לש הרידה

🟧 Cat6 / Cat7 תרשרש: LCom ← LCom ← BoxCom הרקתב
Cat6 / Cat7 chain: LCom → LCom → BoxCom · Cat6 / Cat7 תרשרש: LCom ← LCom ← BoxCom

🟥 Cat6A / Cat7 תשר: BoxCom ← גתמ PoE ← דומע ← תרש עקרק
Cat6A / Cat7 network: BoxCom → switch → riser → GF server · Cat6A / Cat7 תשר: BoxCom ← גתמ ← דומע ← תרש

ןגומ רויד · ןוכיתה םי ילדגמ
קרקע + 8 תומוק · 32 תוריד – תוחא תאירק
Telab International :ץעוי ןכוה   ACE BG · Advantecnia :תכרעמ

טוויח – םיידממ-תלת םיטבמ
3D views – wiring

SCALE · הדימ הנק	DATE · ךיראת	REV	ןוילג
S/E	15/10/2026	B	11

סיסב: תונכות האדריכל L5 (זוג דסמ / Triplet) · םירטמב תודימ
טמרופ A1 · הרודהמ B – לע תונכותה תיתימאה