
3D installation and wiring

Yoseftal Medical Center, Eilat · Nurse call system — Floor overview

ADVANTECNIA ACE BG · Orad	
Made by	ACE BG · Advantecnia
Revised by	Technical dept. ACE BG · October 2026
Reference	9722600017_esq3D_REV03

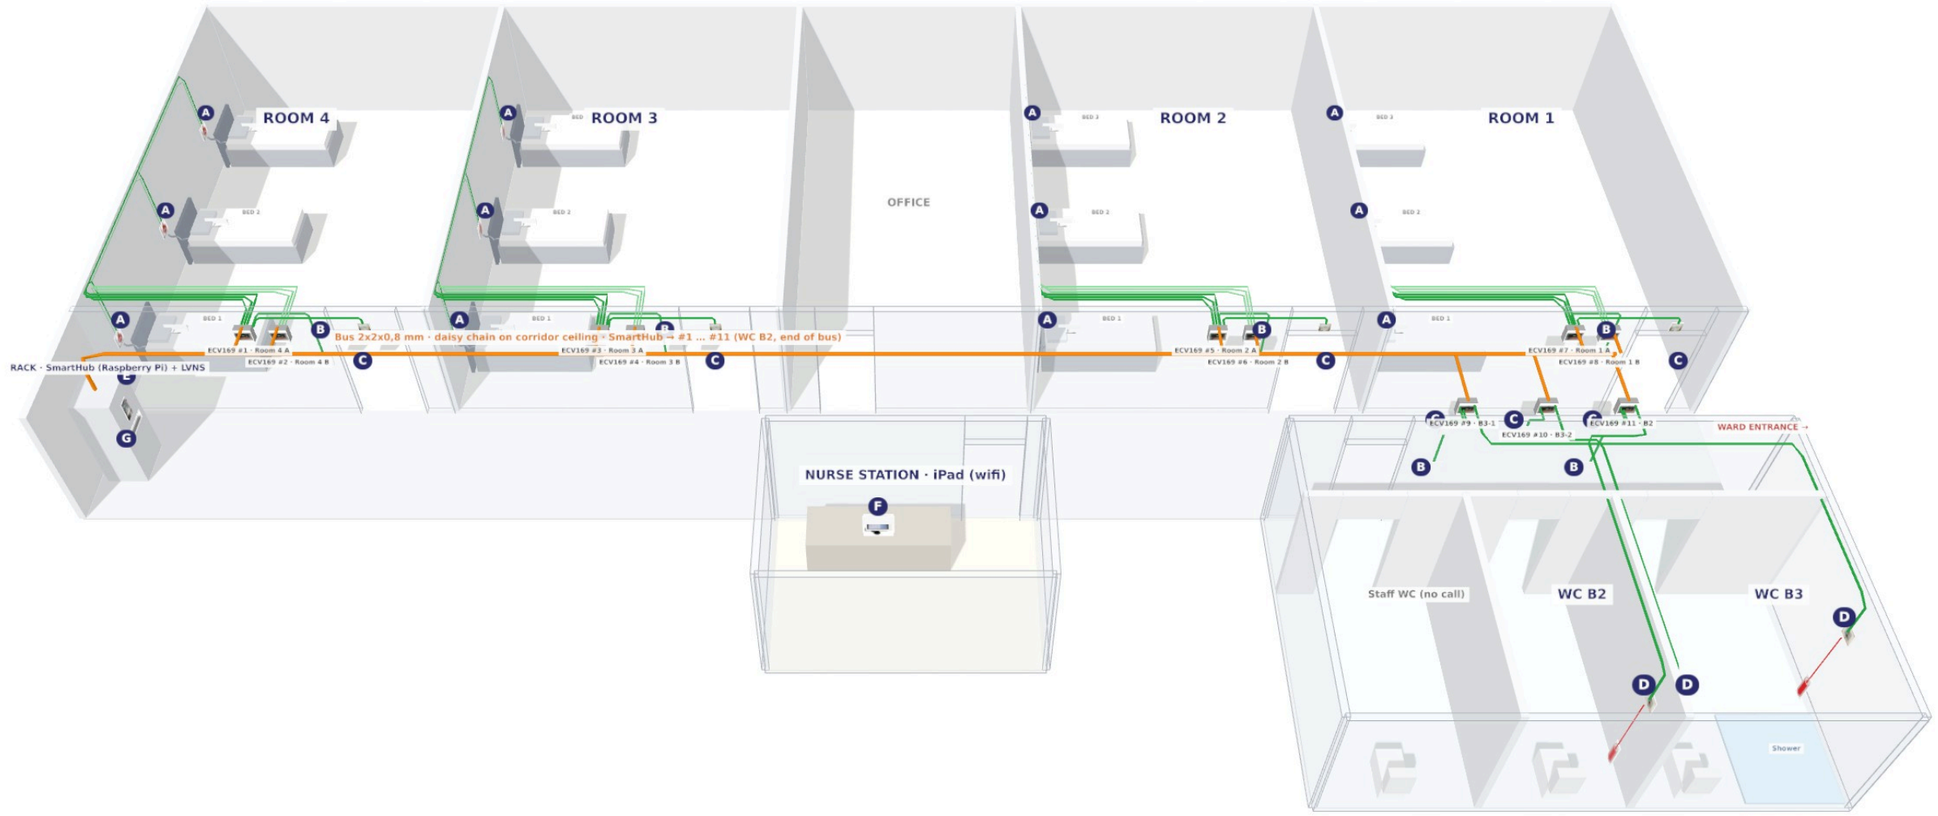

Components

			Qty
A		**ACE82012153** · Bed call panel + bayonet and 1-button handset · side wall, h 1.15 m	12
B		**ACE82082137** · Presence / cancel (IONVV011) · next to the exit door, h 1.35 m	6
C		**EOP004** · Corridor light · above the door, h 2.42 m	7
D		**ACE40320303** · SOS pull-cord · WC B2 ×1, WC B3 ×2 · h 1.85 m	3
E		**EVV049** · SmartHub connectia (server + bus head)	1
F		**EOP002** · Nurse iPad 10.9" (Wi-Fi)	1
G		**EOP006** · Video local server & notifications (LVNS)	1
■		**ECV169** · Junction box with 24-pin PCB ECV169	11

Cabling


- Bus 2x2x0.8 mm · RS485 + 12-48 VDC · daisy chain along corridor ceiling
- UTP Cat6 · device signal → PCB (terminals / RJ45 / RJ12)
- UTP Cat6 · handset disconnection → PCB B

Layout per floor plan plans_2D_EN; wall devices enlarged. Bed call on the side wall at each bed head (h 1.15 m), presence/cancel inside next to the exit door (h 1.35 m), corridor light above the door (h 2.42 m), PCBs in the corridor ceiling, pull-cords h 1.85 m. Nurse desk on iPad. PoE switch, UPS, rack, Wi-Fi, cabling and boxes not included.

3D installation and wiring

Yoseftal Medical Center, Eilat · Nurse call system — Rooms 1-2 · 3 beds each (typical ×4)

ADVANTECNIA ACE BG · Orad	Made by	ACE BG · Advantecnia
	Revised by	Technical dept. ACE BG · October 2026
	Reference	9722600017_esq3D_REV03

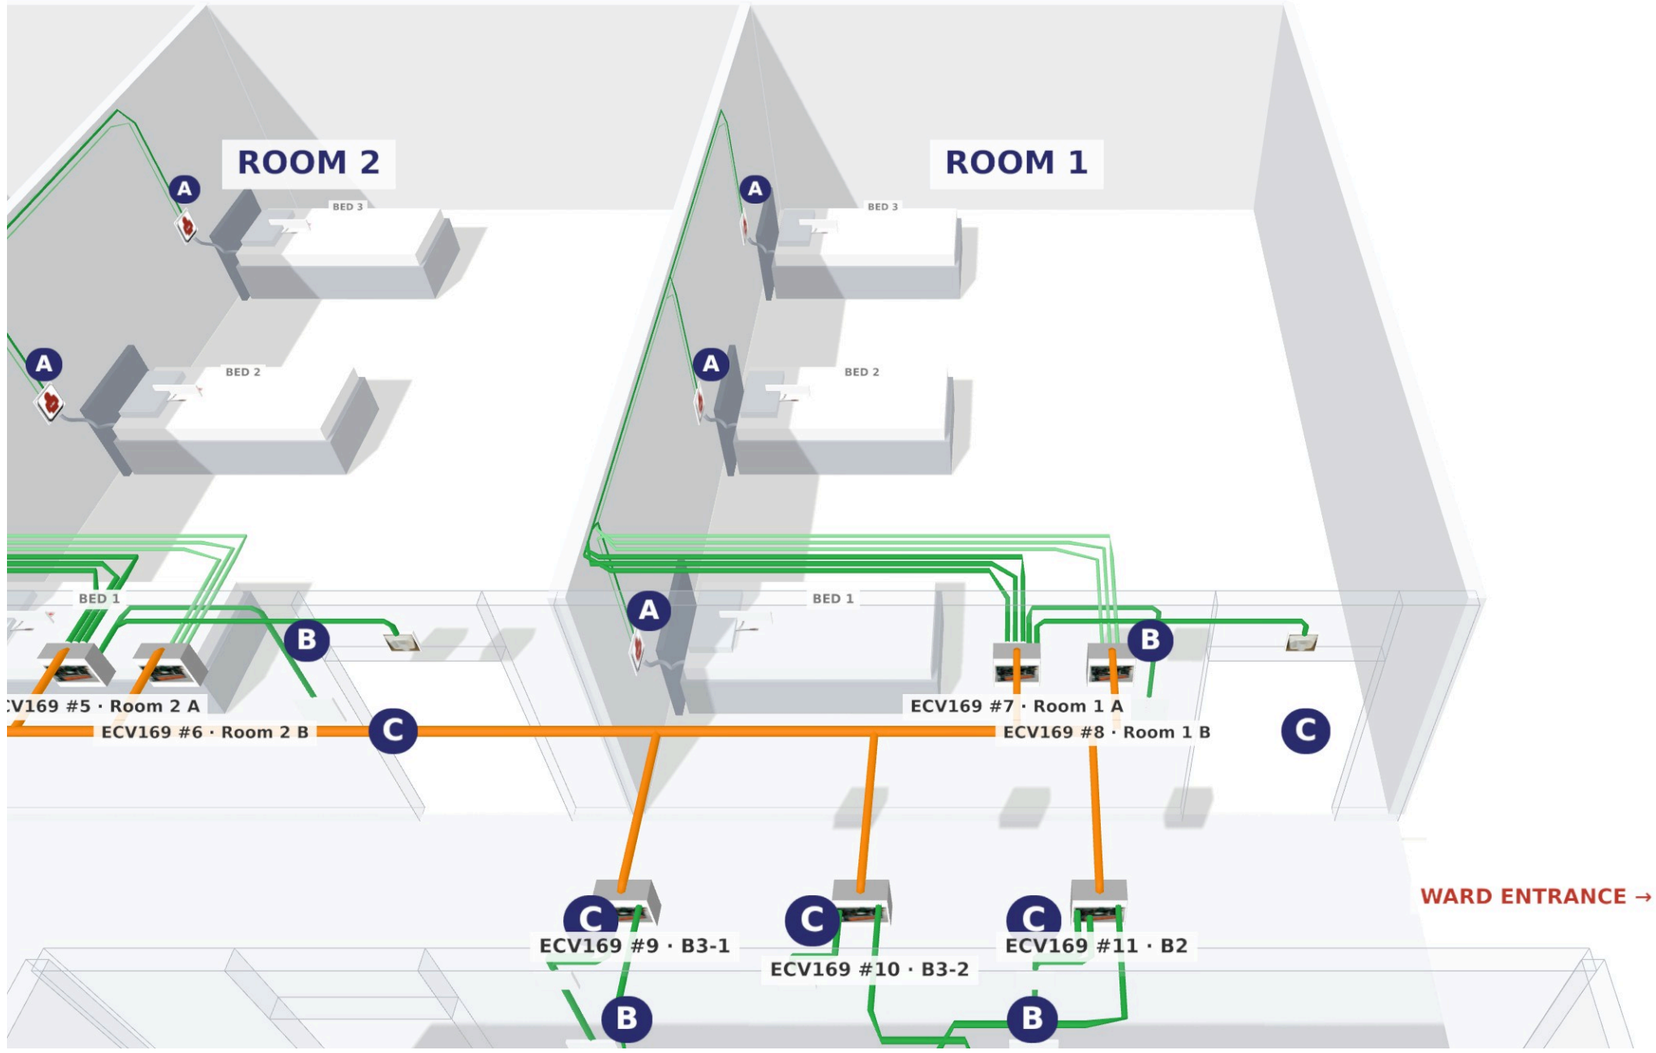

Components

			Qty
A		**ACE82012153** · Bed call panel + bayonet and 1-button handset · side wall, h 1.15 m	12
B		**ACE82082137** · Presence / cancel (IONVV011) · next to the exit door, h 1.35 m	6
C		**EOP004** · Corridor light · above the door, h 2.42 m	7
D		**ACE40320303** · SOS pull-cord · WC B2 ×1, WC B3 ×2 · h 1.85 m	3
E		**EVV049** · SmartHub connectia (server + bus head)	1
F		**EOP002** · Nurse iPad 10.9" (Wi-Fi)	1
G		**EOP006** · Video local server & notifications (LVNS)	1
■		**ECV169** · Junction box with 24-pin PCB ECV169	11

Cabling


- Bus 2x2x0.8 mm · RS485 + 12-48 VDC · daisy chain along corridor ceiling
- UTP Cat6 · device signal → PCB (terminals / RJ45 / RJ12)
- UTP Cat6 · handset disconnection → PCB B

Layout per floor plan plans_2D_EN; wall devices enlarged. Bed call on the side wall at each bed head (h 1.15 m), presence/cancel inside next to the exit door (h 1.35 m), corridor light above the door (h 2.42 m), PCBs in the corridor ceiling, pull-cords h 1.85 m. Nurse desk on iPad. PoE switch, UPS, rack, Wi-Fi, cabling and boxes not included.

3D installation and wiring

Yoseftal Medical Center, Eilat · Nurse call system — Toilets · WC B3 + WC B2

ADVANTECNIA ACE BG · Orad		
	Made by	ACE BG · Advantecnia
	Revised by	Technical dept. ACE BG · October 2026
	Reference	9722600017_esq3D_REV03

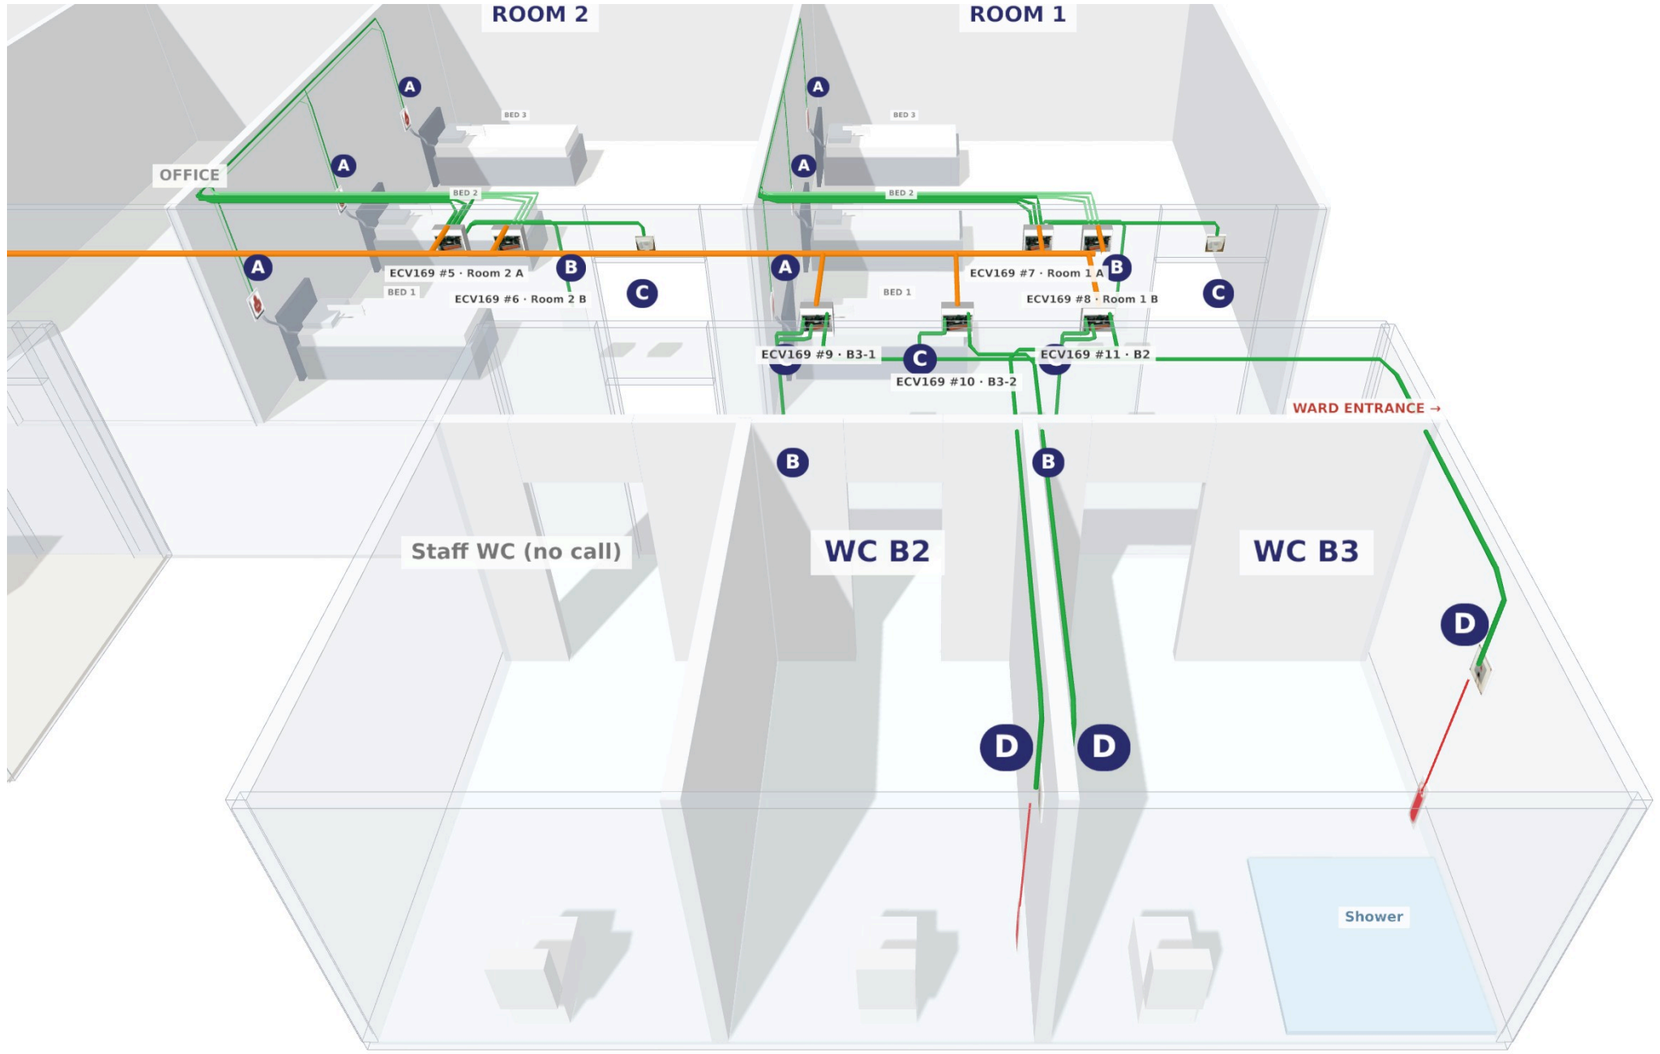

Components

			Qty
A		**ACE82012153** · Bed call panel + bayonet and 1-button handset · side wall, h 1.15 m	12
B		**ACE82082137** · Presence / cancel (IONVV011) · next to the exit door, h 1.35 m	6
C		**EOP004** · Corridor light · above the door, h 2.42 m	7
D		**ACE40320303** · SOS pull-cord · WC B2 ×1, WC B3 ×2 · h 1.85 m	3
E		**EVV049** · SmartHub connectia (server + bus head)	1
F		**EOP002** · Nurse iPad 10.9" (Wi-Fi)	1
G		**EOP006** · Video local server & notifications (LVNS)	1
■		**ECV169** · Junction box with 24-pin PCB ECV169	11

Cabling


- Bus 2x2x0.8 mm · RS485 + 12-48 VDC · daisy chain along corridor ceiling
- UTP Cat6 · device signal → PCB (terminals / RJ45 / RJ12)
- UTP Cat6 · handset disconnection → PCB B

Layout per floor plan plans_2D_EN; wall devices enlarged. Bed call on the side wall at each bed head (h 1.15 m), presence/cancel inside next to the exit door (h 1.35 m), corridor light above the door (h 2.42 m), PCBs in the corridor ceiling, pull-cords h 1.85 m. Nurse desk on iPad. PoE switch, UPS, rack, Wi-Fi, cabling and boxes not included.

3D installation and wiring

Yoseftal Medical Center, Eilat · Nurse call system — Nurse station · iPad

ADVANTECNIA ACE BG · Orad		
	Made by	ACE BG · Advantecnia
	Revised by	Technical dept. ACE BG · October 2026
	Reference	9722600017_esq3D_REV03

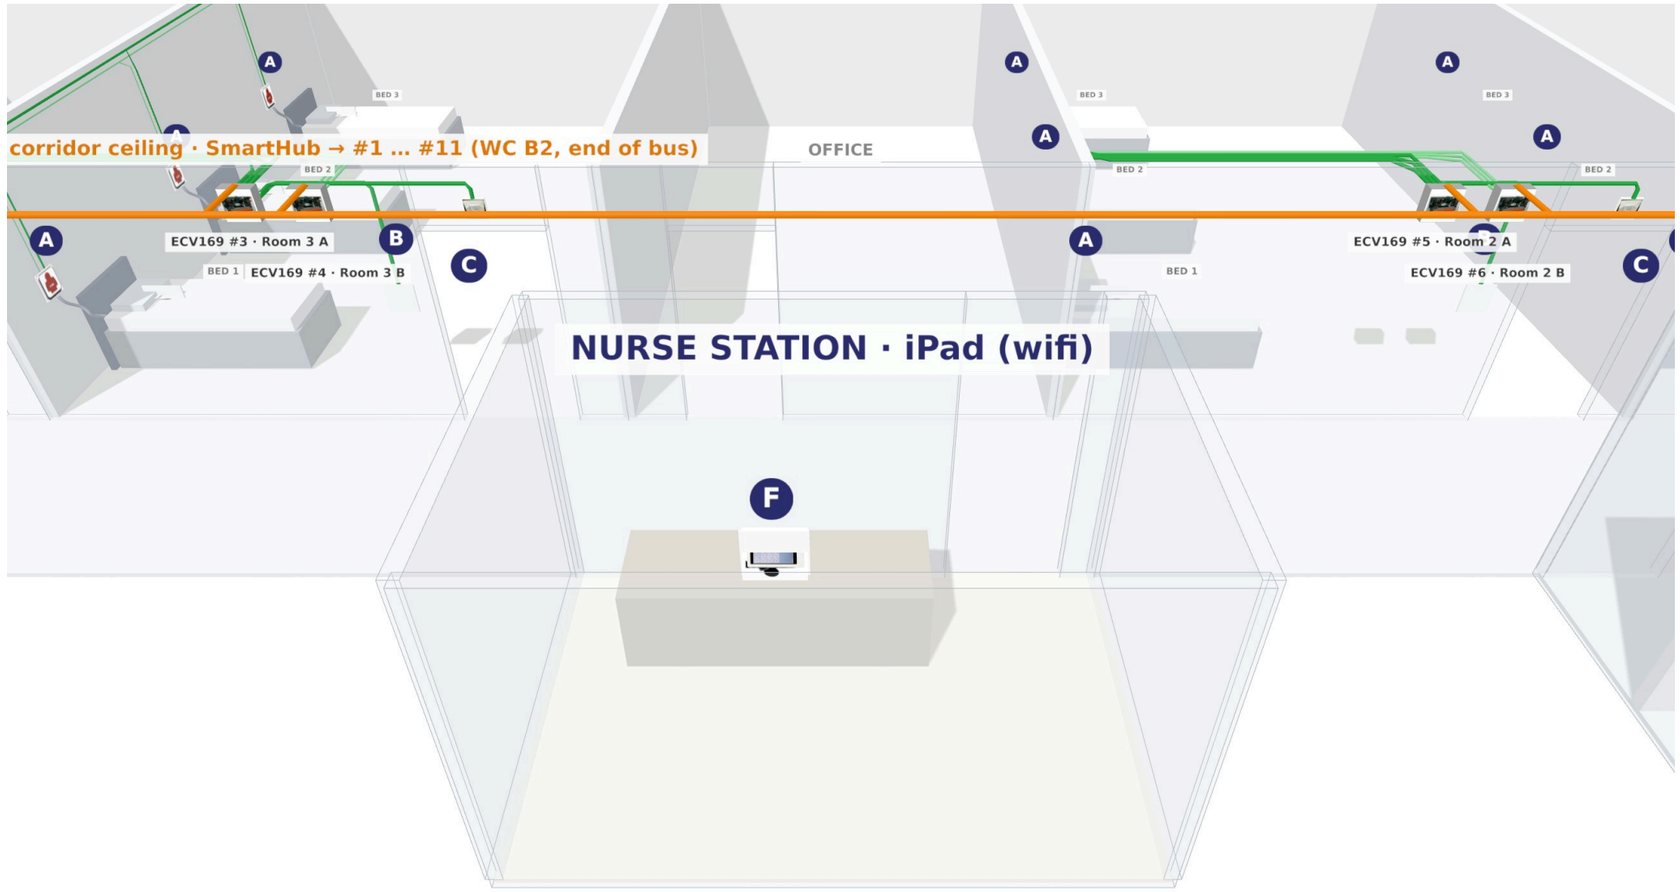

Components

			Qty
A		**ACE82012153** · Bed call panel + bayonet and 1-button handset · side wall, h 1.15 m	12
B		**ACE82082137** · Presence / cancel (IONVV011) · next to the exit door, h 1.35 m	6
C		**EOP004** · Corridor light · above the door, h 2.42 m	7
D		**ACE40320303** · SOS pull-cord · WC B2 ×1, WC B3 ×2 · h 1.85 m	3
E		**EVV049** · SmartHub connectia (server + bus head)	1
F		**EOP002** · Nurse iPad 10.9" (Wi-Fi)	1
G		**EOP006** · Video local server & notifications (LVNS)	1
■		**ECV169** · Junction box with 24-pin PCB ECV169	11

Cabling


- Bus 2x2x0.8 mm · RS485 + 12-48 VDC · daisy chain along corridor ceiling
- UTP Cat6 · device signal → PCB (terminals / RJ45 / RJ12)
- UTP Cat6 · handset disconnection → PCB B

Layout per floor plan plans_2D_EN; wall devices enlarged. Bed call on the side wall at each bed head (h 1.15 m), presence/cancel inside next to the exit door (h 1.35 m), corridor light above the door (h 2.42 m), PCBs in the corridor ceiling, pull-cords h 1.85 m. Nurse desk on iPad. PoE switch, UPS, rack, Wi-Fi, cabling and boxes not included.

3D installation and wiring

Yoseftal Medical Center, Eilat · Nurse call system — Main rack · SmartHub + LVNS

ADVANTECNIA ACE BG · Orad		
	Made by	ACE BG · Advantecnia
	Revised by	Technical dept. ACE BG · October 2026
	Reference	9722600017_esq3D_REV03

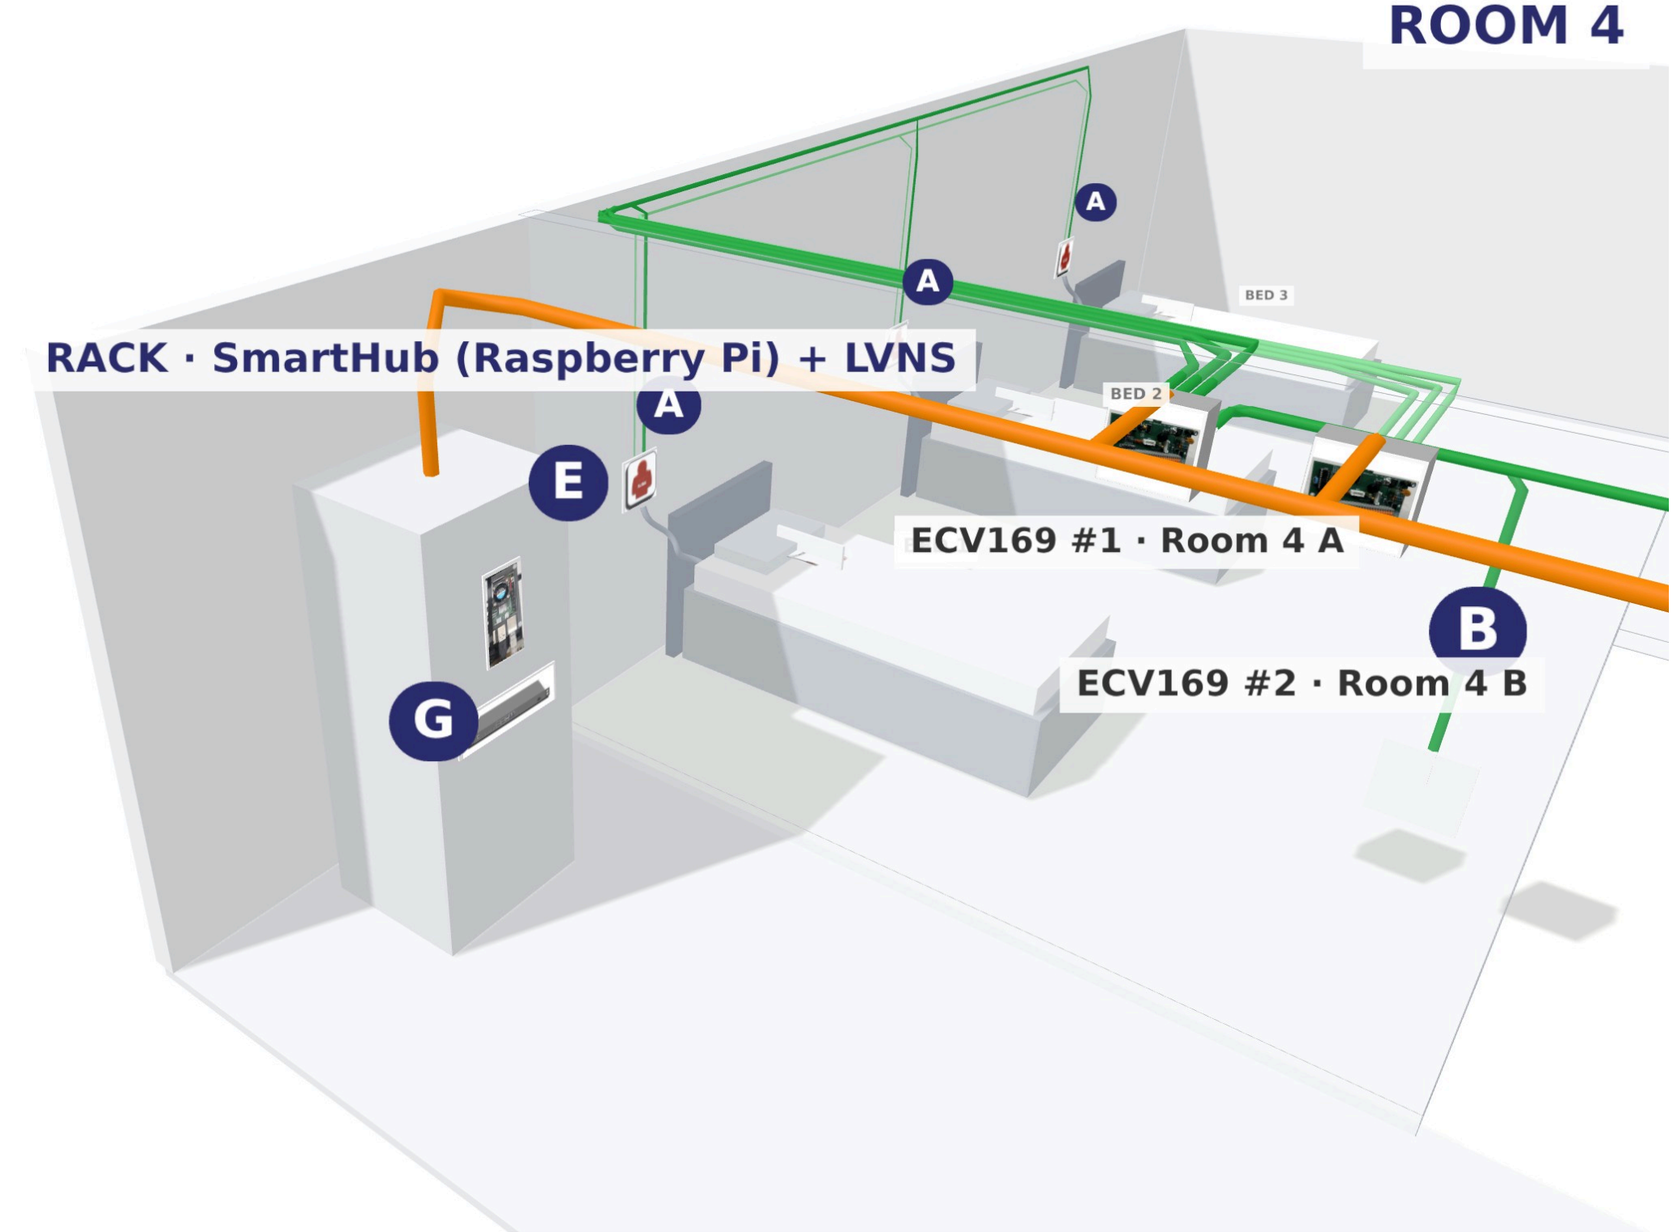

Components

			Qty
A		**ACE82012153** · Bed call panel + bayonet and 1-button handset · side wall, h 1.15 m	**12**
B		**ACE82082137** · Presence / cancel (IONVV011) · next to the exit door, h 1.35 m	**6**
C		**EOP004** · Corridor light · above the door, h 2.42 m	**7**
D		**ACE40320303** · SOS pull-cord · WC B2 ×1, WC B3 ×2 · h 1.85 m	**3**
E		**EVV049** · SmartHub connectia (server + bus head)	**1**
F		**EOP002** · Nurse iPad 10.9" (Wi-Fi)	**1**
G		**EOP006** · Video local server & notifications (LVNS)	**1**
■		**ECV169** · Junction box with 24-pin PCB ECV169	**11**

Cabling

- Bus 2x2x0.8 mm · RS485 + 12-48 VDC · daisy chain along corridor ceiling
- UTP Cat6 · device signal → PCB (terminals / RJ45 / RJ12)
- UTP Cat6 · handset disconnection → PCB B

Layout per floor plan plans_2D_EN; wall devices enlarged. Bed call on the side wall at each bed head (h 1.15 m), presence/cancel inside next to the exit door (h 1.35 m), corridor light above the door (h 2.42 m), PCBs in the corridor ceiling, pull-cords h 1.85 m. Nurse desk on iPad. PoE switch, UPS, rack, Wi-Fi, cabling and boxes not included.