

DEVICES · EQUIPOS · ציוד

- **TAB** · Door tablet (iPad / Android) – call and voice, h 1.40 m
  Door tablet – call and voice · טאבלט כניסה – שיחה וקול · טאבלט כניסה – שיחה וקול
- **VOZ** · Voice panel with buttons ACE82182451 – living room and bedrooms, h 1.20–1.30 m
  Voice panel with buttons – living room and bedrooms · פנל לחצנים – סלון וחדרי שינה · פנל לחצנים – סלון וחדרי שינה
- Call pear next to the bed (bedrooms)
  Call pear next to the bed (bedrooms) · כפתור ליד המיטה (חדרי שינה)
- **TI / TD** · Pull-cord ACE40320303W – toilet and shower, h 1.85 m
  Pull-cord – toilet and shower, h 1.85 m · חבל משיכה מהרצפה – שירותים ומקלחת · חבל משיכה – שירותים ומקלחת · גובה 1.85 מ׳
- **LP** · Corridor light ACE41020309 – above each public toilet door
  Corridor light – above each public toilet door · מנורה קריאה מעל דלת – כל שירותים ציבוריים · מנורה קריאה מעל דלת – כל שירותים ציבוריים
- **LC** · LCom ACE71610003 – apartment hub (ceiling)
  LCom – apartment hub (ceiling) · LCom – מרכזת דירתית (בתקרה) · LCom – מרכזת דירתית (בתקרה)
- **GAB** 12U floor rack: 2 Buscomm ACE70810000 + PoE switch ACEUCM6302
  Floor rack: 2 Buscomm + PoE switch · ארון רצפה 12U · 2 Buscomm + מתג PoE


QUANTITIES PER FLOOR × 8 FLOORS

Code	Device	Per floor	8 floors
TAB	Door tablet	4	32
VOZ	Voice panel with buttons	10	80
TI/TD	Pull-cord (toilet + shower)	17	136
LP	Corridor light (public toilet)	1	8
LC	LCom	5	40
BC	Buscomm	2	16
SW	PoE switch	1	8

NOTES · NOTAS

1. Base: architectural plan L5 (typical floor) – all 8 floors are identical: 4 apartments per floor, 32 in total.
2. Apartments x01 and x02: 1 bedroom, living room with kitchen and 2 bathrooms. Apartments x03 and x04: 2 bedrooms and 2 bathrooms.
3. Tablet at the door of each apartment (iPad / Android) to call and talk to the nurse.
4. Voice panel with buttons (ACE82182451) in the living room and in each bedroom; in bedrooms, with a pear next to the bed.
5. Pull-cords (ACE40320303W) at the toilet and shower of every bathroom, at 1.85 m.
6. One public toilet per floor in the common room: pull-cord + corridor light above the door. With the 2 on GF, 10 public toilets in total.
7. Floor rack in the service corridor next to the lifts (Tripp Lite 12U, as in the IT plan).
8. Locations per the client's marks on plan L2 (nt = voice panel, tab = tablet): see sheet 03.

MOUNTING HEIGHTS

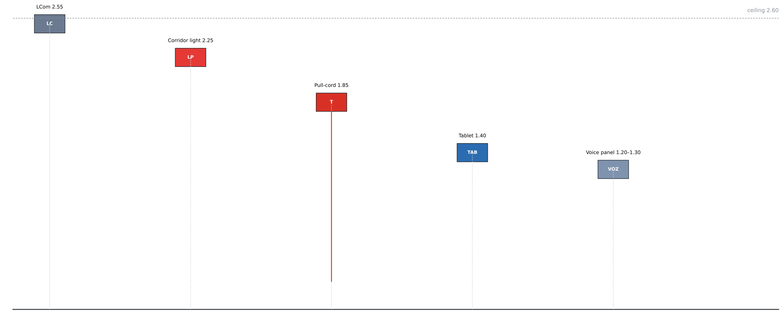



Pull-cord · Door tablet (iPad / Android) · Corridor light · Voice panel with buttons

MIGDALEI YAM A TIJON · ASSISTED LIVING

Nurse call – GF + 8 floors · 32 apartments

System: ACE BG · Advantecnia Prepared by: Telab International

TYPICAL FLOOR F1–F8 · NURSE CALL

SCALE · ESCALA	DATE · FECHA	REV	SHEET
1:60	15/10/2026	B	01

Base: architect's plan L5 (Massad Oz / Triplet) · dimensions in m

A1 format · Rev. B – on the real plan

שירותים קריאת אחות



Pull-cord

Code	**ACE40320303W**
Location	Toilet and shower of every bathroom and the 10 public toilets
Height	**1.85 m**
Quantity	**138**

1

טבלט אנדרואיד קריאת אחות



Door tablet (iPad / Android)

Code	**Advantecnia TV**
Location	In the lobby, next to each apartment door
Height	**1.40 m**
Quantity	**32**

2

NOTES · NOTAS

1. Reference photos from ACE BG / Advantecnia, with their title.

2. Pull-cord: red cord with handle, reachable from the floor.

3. The door tablet calls and talks to the nurse.

4. The corridor light turns on when someone calls from the public toilet.

5. The panel has a red call button, a blue (left) and a green (right) button and a speaker to talk.

6. Also in each apartment: LCom ACE71610003 in the ceiling.

7. On GF: Android desk phone ACE52190200 at the nurse desk.

מנורה קריאת אחות



Corridor light

Code	**ACE41020309**
Location	Above each public toilet door
Height	**2.25 m**
Quantity	**10**

3

פנל קריאת אחות



Voice panel with buttons

Code	**ACE82182451**
Location	Living room and each bedroom (with pear in bedrooms)
Height	**1.20–1.30 m**
Quantity	**80**

4

MIGDALEI YAM A TIJON · ASSISTED LIVING

Nurse call – GF + 8 floors · 32 apartments


System: ACE BG · Advantecnia Prepared by: Telab International

SYSTEM DEVICES

SCALE · ESCALA	DATE · FECHA	REV	SHEET
S/E	**15/10/2026**	**B**	**02**

Base: architect's plan LS (Massad Oz / Triplet) · dimensions in m

A1 format · Rev. B – on the real plan

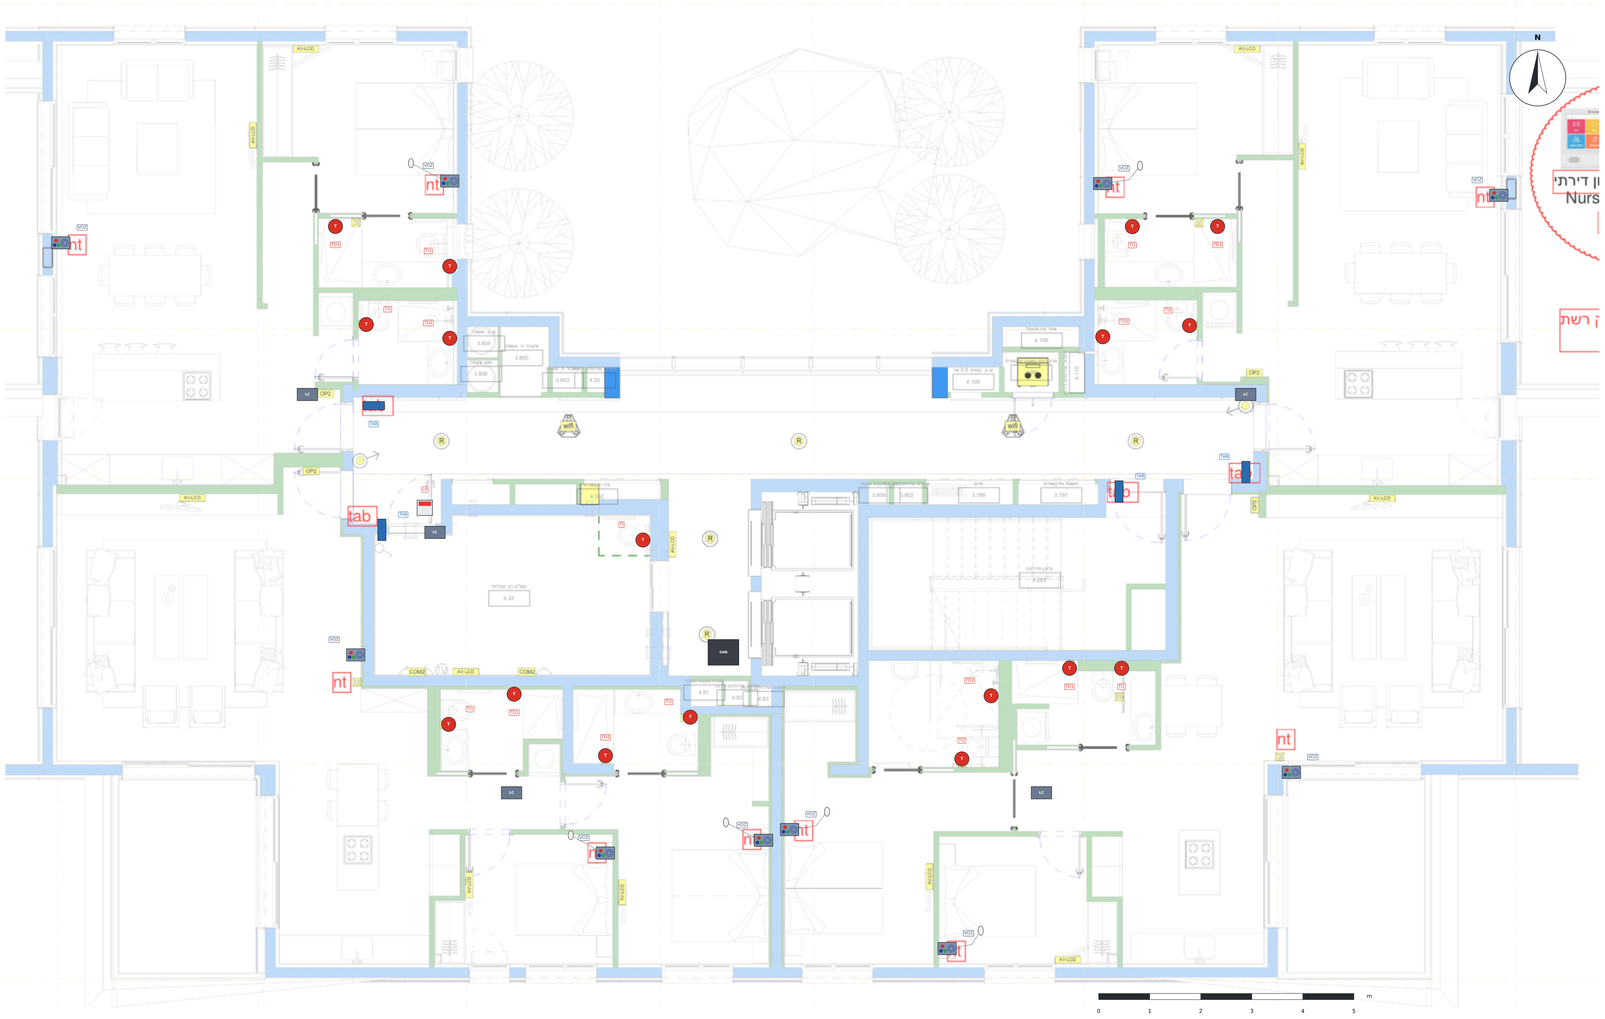

NOTES · NOTAS

1. Background: the client's IT plan L2 with their red marks:
«nt» = voice panel and «tab» = door tablet.

2. On top, in colour: the devices of this proposal.
Each panel and tablet is where the client marked it.

3. The yellow ⊠ squares in the L2 bathrooms
are the pull-cords (toilet and shower).

4. The 4 tablets are in the lobby, next to each
apartment door, as in the «tab» marks.

5. Plans L2 and L5 (base of this proposal) share
the same structure; L5 is the typical floor for floors 1 to 8.

DEVICES · EQUIPOS · דגמים

TAB · Door tablet (iPad / Android) – call and voice, h 1.40 m
Door tablet – call and voice · טאבלט דלת – שיחה וקול · הרמה מהרצפה 1.40 מ'

VOZ · Voice panel with buttons ACE82182451 – living room and bedrooms, h 1.20–1.30 m
Voice panel with buttons – living room and bedrooms · פנל קריאה עם כפתורים – בסלון ובחדרי שינה · הרמה מהרצפה 1.20–1.30 מ'

Call pear next to the bed (bedrooms)
Call pear next to the bed (bedrooms) · נורית ליד מיטה (בחדרי שינה)

T / TD · Pull-cord ACE40320303W – toilet and shower, h 1.85 m
Pull-cord – toilet and shower, h 1.85 m · חבל משיכה בשירותים ובמקלחת – הרמה מהרצפה 1.85 מ'

LP · Corridor light ACE41020309 – above each public toilet door
Corridor light – above each public toilet door · גוף תאורה במסדרון – מעל כל דלת שירותים ציבוריים

שירותים קריאת אחות



Pull-cord

טבלט אנדרואיד קריאת אחות



Door tablet (iPad / Android)

מנורה קריאת אחות



Corridor light

פנל קריאת אחות



Voice panel with buttons

MIGDALEI YAM A TIJON · ASSISTED LIVING

Nurse call – GF + 8 floors · 32 apartments


System: ACE BG · Advantecnia Prepared by: Telab International

CLIENT MARKS (PLAN L2) AND PROPOSAL

SCALE · ESCALA	DATE · FECHA	REV	SHEET
1:60	**15/10/2026**	**B**	**03**

Base: architect's plan L5 (Massad Oz / Triplet) · dimensions in m

A1 format · Rev. B – on the real plan

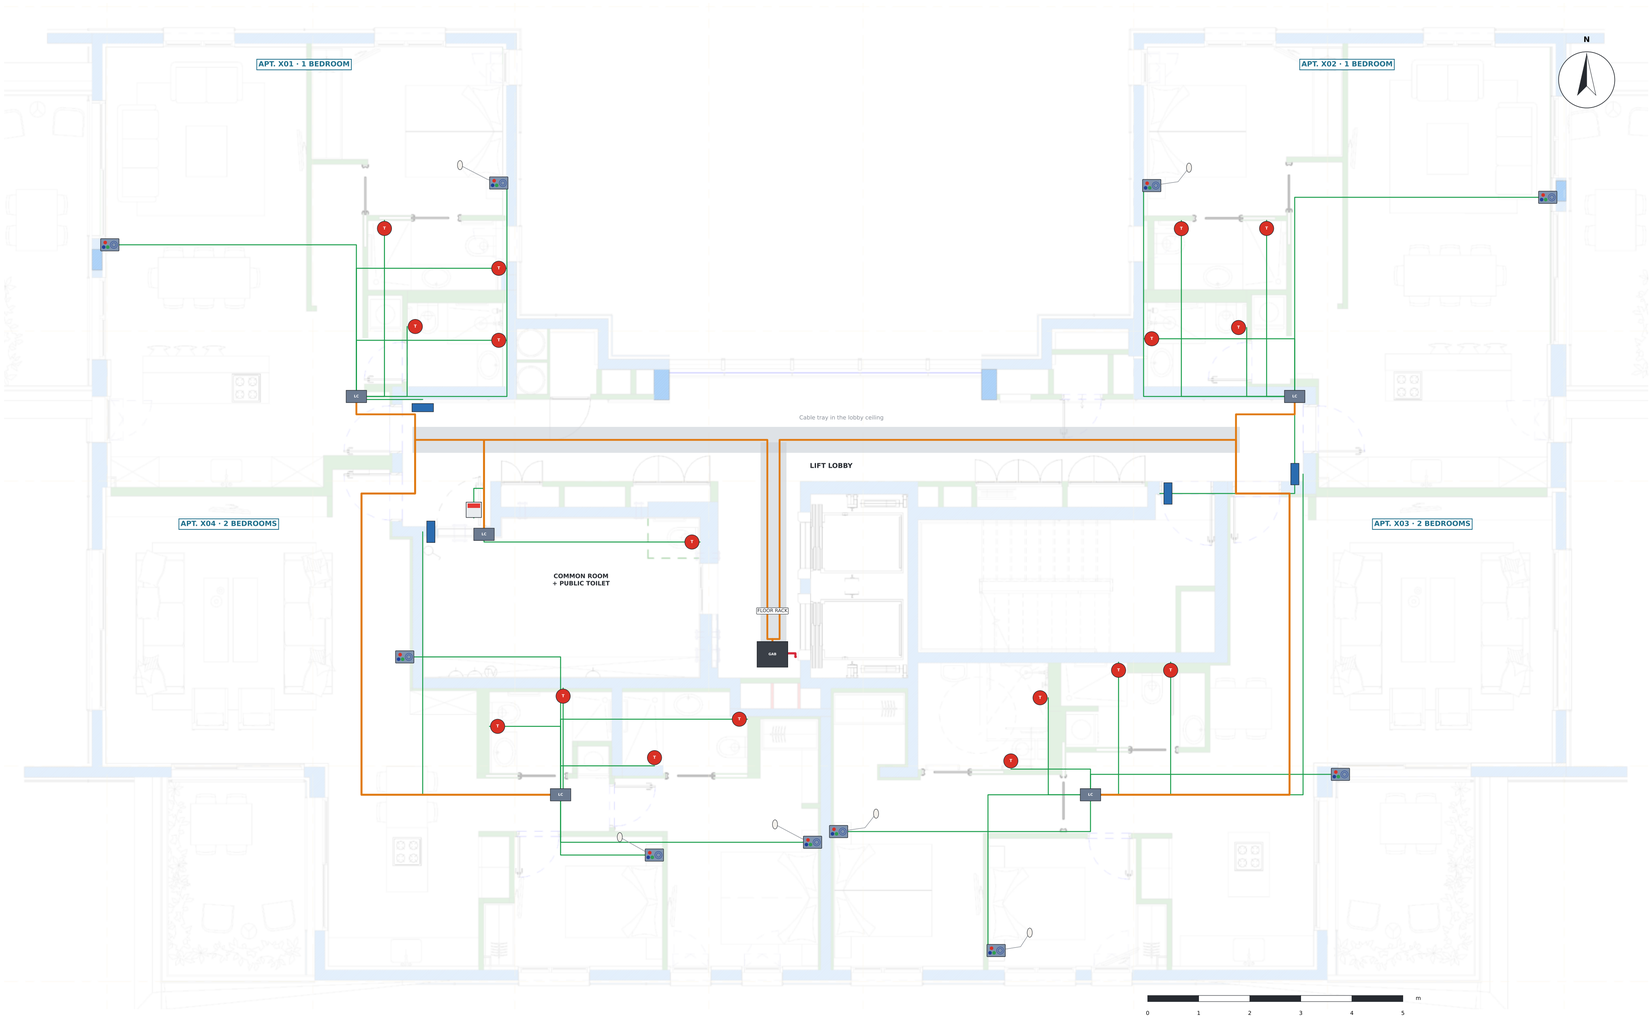

WIRING · CABLEADO · סוגיות

Cat6 radial: each device → its apartment LCom
Cat6 radial: each device → apartment LCom · Cat6 רדיאלי: כל התקן → LCom הדירה

Cat6 / Cat7 chain: LCom → LCom → rack Buscomm
Cat6 / Cat7 chain: LCom → LCom → Buscomm · Cat6 / Cat7 שרשרת: LCom ← LCom ← Buscomm

Cat6A / Cat7 network: Buscomm → switch → riser → GF server
Cat6A / Cat7 network: Buscomm → switch → riser → GF server · Cat6A / Cat7 רשת: Buscomm ← נתב ← רייזר ← שרת

TYPICAL FLOOR LENGTHS (no spare)

Cat6 radial inside the apartments	**183 m**
Cat6 / Cat7 chain LCom → Buscomm	**82 m**
Cat6A / Cat7 rack and riser	**4 m**

NOTES · NOTAS

1. Each device runs radially (Cat6) to its apartment LCom, in the hall ceiling.
2. The LComs are chained along the lobby tray to the floor rack:
x01 → x04 → common room → Buscomm 1 · x02 → x03 → Buscomm 2.
3. The floor PoE switch runs up the Cat6A / Cat7 riser to
the GF server.
4. Everything is PoE: no 230 V needed for the apartment devices.

NOTES · NOTAS

1. Base: architectural plan L5 (typical floor) – all 8 floors are identical: 4 apartments per floor, 32 in total.
2. Apartments x01 and x02: 1 bedroom, living room with kitchen and 2 bathrooms. Apartments x03 and x04: 2 bedrooms and 2 bathrooms.
3. Tablet at the door of each apartment (iPad / Android) to call and talk to the nurse.
4. Voice panel with buttons (ACE82182451) in the living room and in each bedroom; in bedrooms, with a pear next to the bed.
5. Pull-cords (ACE40320303W) at the toilet and shower of every bathroom, at 1.85 m.
6. One public toilet per floor in the common room: pull-cord + corridor light above the door. With the 2 on GF, 10 public toilets in total.
7. Floor rack in the service corridor next to the lifts (Tripp Lite 12U, as in the IT plan).
8. Locations per the client's marks on plan L2 (nt = voice panel, tab = tablet): see sheet 03.

MIGDALEI YAM A TIJON · ASSISTED LIVING

Nurse call – GF + 8 floors · 32 apartments


System: ACE BG · Advantecnia Prepared by: Telab International

TYPICAL FLOOR F1–F8 · WIRING

SCALE · ESCALA	DATE · FECHA	REV	SHEET
1:60	**15/10/2026**	**B**	**04**

Base: architect's plan L5 (Massad Oz / Triplet) · dimensions in m

A1 format · Rev. B – on the real plan

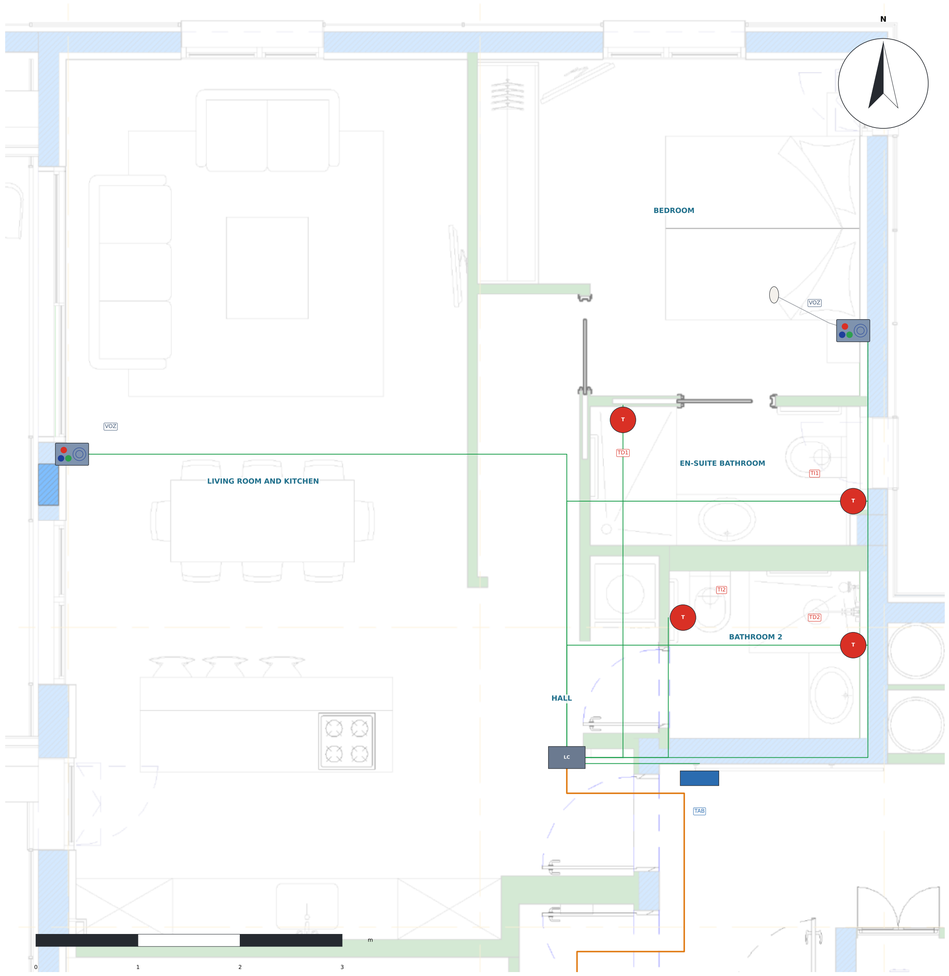

APARTMENT DEVICES

ID	Device	Room	Height
TAB	Door tablet	Hall	1.40 m
VOZ-S	Voice panel with buttons	Living room and kitchen	1,30 m
VOZ-D	Voice panel with buttons + pear	Bedroom	1,20 m
TI1	Pull-cord	En-suite bathroom	1.85 m
TD1	Pull-cord	En-suite bathroom	1.85 m
TI2	Pull-cord	Bathroom 2	1.85 m
TD2	Pull-cord	Bathroom 2	1.85 m
LCOM	LCom ACE71610003	Hall	2,55 m

SYMBOLS · SÍMBOLOS · סימנים

TAB · Door tablet (iPad / Android) – call and voice, h 1.40 m
Door tablet – call and voice · טבלט כניסה – שיחה וקול

VOZ · Voice panel with buttons ACE82182451 – living room and bedrooms, h 1.20–1.30 m
Voice panel with buttons – living room and bedrooms · לוח פיקוד עם כפתורים – סלון וחדרי שינה

Call pear next to the bed (bedrooms)
Call pear next to the bed (bedrooms) · המחמה ליד המיטה (חדרי שינה)

TI / TD · Pull-cord ACE40320303W – toilet and shower, h 1.85 m
Pull-cord – toilet and shower, h 1.85 m · חבל משיכה – שירותים ומקלחת, גובה 1.85 מ'

LP · Corridor light ACE41020309 – above each public toilet door
Corridor light – above each public toilet door · מנורת מסדרון – מעל כל דלת שירותים ציבוריים

LC · LCom ACE71610003 – apartment hub (ceiling)
LCom – apartment hub (ceiling) · LCom – בית רכזת (בתקרה)

NOTES · NOTAS

1. Apartment x02 mirrors x01 (same devices).
2. Tablet in the lobby, next to the front door (client's «tab» mark).
3. Voice panel in the living room and in the bedroom (with pear next to the bed).
4. 2 bathrooms: pull-cord at the toilet and at the shower of each (4 pull-cords).
5. Everything runs radially in Cat6 to the hall LCom.

שירותים קריאת אחות



Pull-cord

טבלט אנדרואיד קריאת אחות



Door tablet (iPad / Android)

מנורה קריאת אחות



Corridor light

פנל קריאת אחות



Voice panel with buttons

MIGDALEI YAM A TIJON · ASSISTED LIVING

Nurse call – GF + 8 floors · 32 apartments

System: ACE BG · Advantecnia Prepared by: Telab International

1-BEDROOM APT. (x01 / x02)

SCALE · ESCALA	DATE · FECHA	REV	SHEET
1:30	15/10/2026	B	05

Base: architect's plan LS (Massad Oz / Triplet) · dimensions in m

A1 format · Rev. B – on the real plan



APARTMENT DEVICES

ID	Device	Room	Height
TAB	Door tablet	Hall	1.40 m
VOZ-S	Voice panel with buttons	Living room	1,30 m
VOZ-D1	Voice panel with buttons + pear	Bedroom 1	1,20 m
VOZ-D2	Voice panel with buttons + pear	Bedroom 2	1,20 m
TI1	Pull-cord	Bathroom 1	1.85 m
TD1	Pull-cord	Bathroom 1	1.85 m
TI2	Pull-cord	Bathroom 2	1.85 m
TD2	Pull-cord	Bathroom 2	1.85 m
LCOM	LCom ACE71610003	Hall	2,55 m

SYMBOLS · SÍMBOLOS · סימנים

TAB · Door tablet (iPad / Android) – call and voice, h 1.40 m
Door tablet – call and voice · Tableta de puerta – llamada y voz · טבלט דלת – שיחה וקול

VOZ · Voice panel with buttons ACE82182451 – living room and bedrooms, h 1.20–1.30 m
Voice panel with buttons · Panel de voz con botones · לוח קול עם לחצנים

Call pear next to the bed (bedrooms)
Call pear next to the bed (bedrooms) · Pera de llamada junto a la cama · אגס קריאה ליד המיטה

TI / TD · Pull-cord ACE40320303W – toilet and shower, h 1.85 m
Pull-cord – toilet and shower, h 1.85 m · Cordón de tracción – baño y ducha, h 1.85 m · חבל משיכה – שירותים ומקלחת, 1.85 מ׳

LP · Corridor light ACE41020309 – above each public toilet door
Corridor light – above each public toilet door · Luz de pasillo – encima de cada puerta de baño público · מנורת מסדרון – מעל כל דלת שירותים ציבוריים

LC · LCom ACE71610003 – apartment hub (ceiling)
LCom – apartment hub (ceiling) · LCom – concentrador de apartamento (techo) · LCom – רכזת דירה (בתקרה)

NOTES · NOTAS

1. Apartment x03 has the same devices (bathrooms laid out differently).
2. Tablet in the lobby, next to the front door (client's «tab» mark).
3. Voice panel in the living room and in both bedrooms (with pear next to the bed).
4. 2 bathrooms: pull-cord at the toilet and at the shower of each (4 pull-cords).
5. Everything runs radially in Cat6 to the LCom in the bedroom corridor.

שירותים קריאת אחות



Pull-cord

טבלט אנדרואיד קריאת אחות



Door tablet (iPad / Android)

מנורה קריאת אחות



Corridor light

פנל קריאת אחות



Voice panel with buttons

MIGDALEI YAM A TIJON · ASSISTED LIVING

Nurse call – GF + 8 floors · 32 apartments


System: ACE BG · Advantecnia Prepared by: Telab International

2-BEDROOM APT. (x04 / x03)


SCALE · ESCALA	DATE · FECHA	REV	SHEET
1:35	15/10/2026	B	06

Base: architect's plan LS (Massad Oz / Triplet) · dimensions in m

A1 format · Rev. B – on the real plan

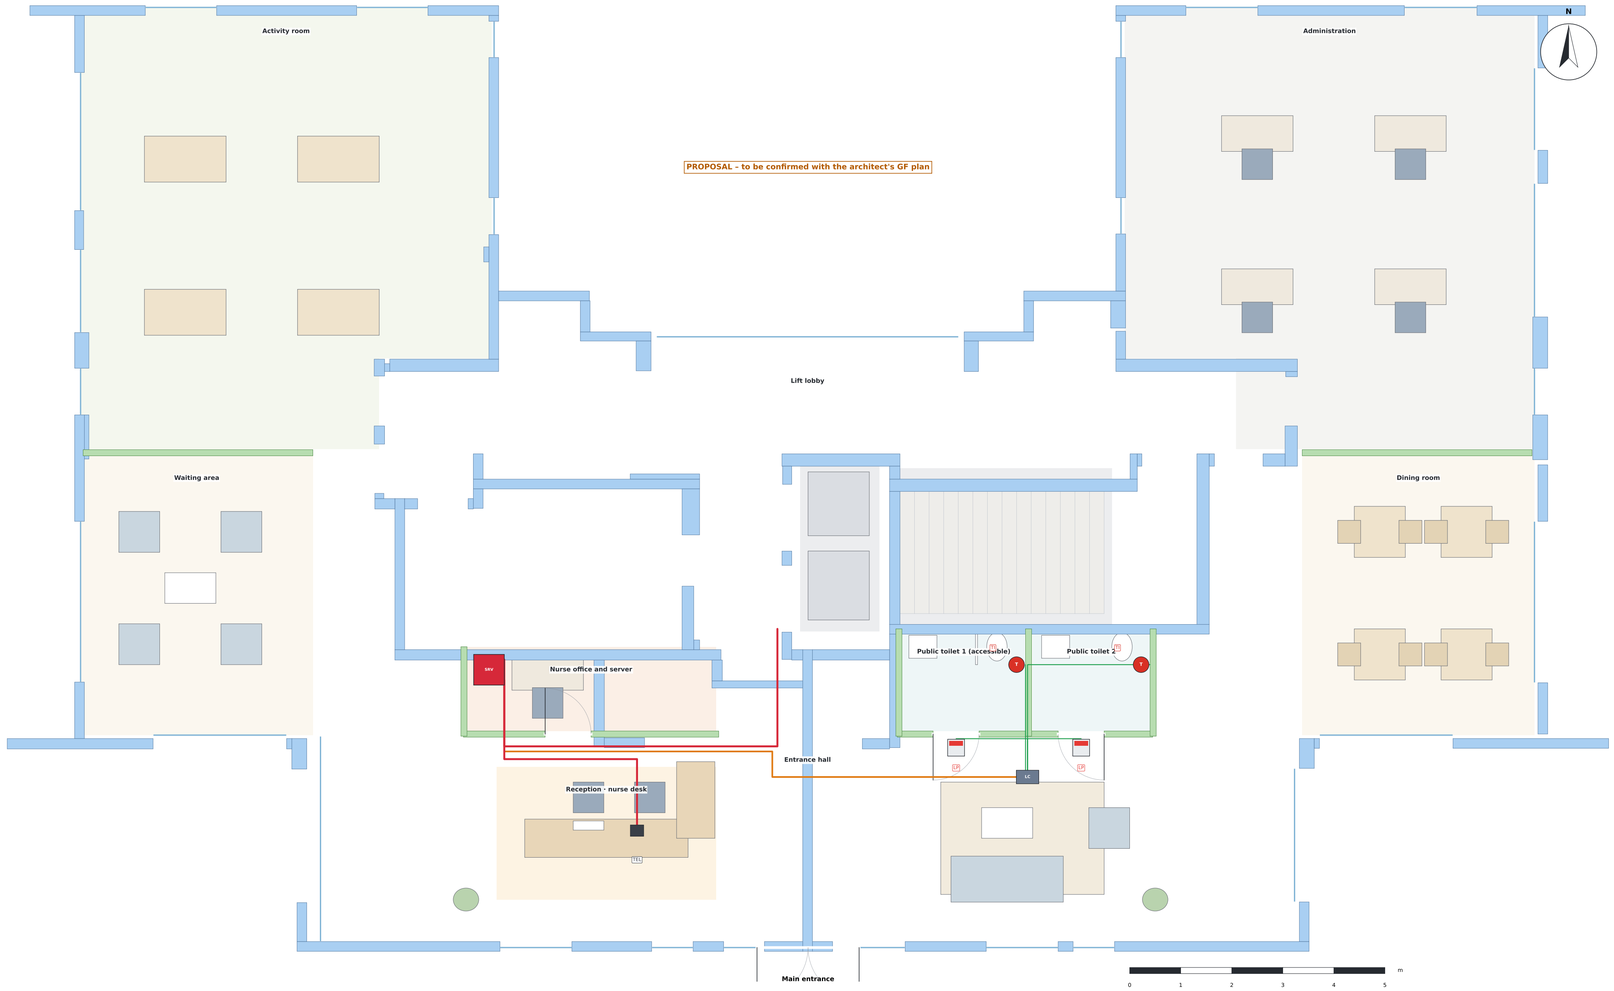

DETAIL · RECEPTION AND NURSE DESK (1:40)

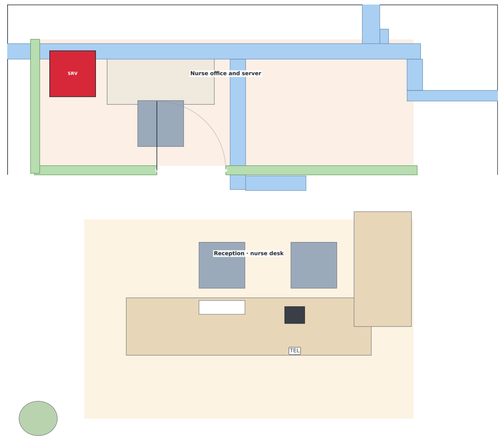

NOTES · NOTAS

1. Nurse desk at reception, facing the entrance and the lifts.
2. On the desk: Android desk phone ACE52190200 (receives calls and voice).
3. Behind the desk: nurse office with the main rack: server ACE51010103, PoE switch ACEUCM6302 and GF Buscomm.
4. 2 public toilets on GF: pull-cord next to the toilet and corridor light above each door.
5. The riser from the 8 floors runs down the core to the main rack.
6. Proposed GF layout: to be adjusted when the architect's plan arrives.

SYMBOLS · SÍMBOLOS · סמלים

- **T** — TI / TD · Pull-cord ACE40320303W – toilet and shower, h 1.85 m
  Pull-cord – toilet and shower, h 1.85 m · מתקן חבל – שירותים ומקלחת, גובה 1.85 מ'
- **LP** — LP · Corridor light ACE41020309 – above each public toilet door
  Corridor light – above each public toilet door · מיקרוגל מיקרוגל לך תוך לעמ – גריסטס תיראנ
- **LC** — LC · LCom ACE71610003 – apartment hub (ceiling)
  LCom – apartment hub (ceiling) · LCom – הרכזת הדירה (בתוכ
- **TEL** — TEL · Android desk phone ACE52190200
  Android desk phone · רשתיבא שלחוש טלפון
- **SRV** — SRV · GF rack: server ACE51010103 + switch + Buscomm
  GF rack: server + switch + Buscomm · מתקנים + מתג + מחשב עבור עבור בקא

MIGDALEI YAM A TIJON · ASSISTED LIVING

Nurse call – GF + 8 floors · 32 apartments

System: ACE BG · Advantecnia Prepared by: Telab International

GROUND FLOOR · LOBBY AND NURSE DESK

SCALE · ESCALA	DATE · FECHA	REV	SHEET
1:60	15/10/2026	B	07


Base: architect's plan LS (Massad Oz / Triplet) · dimensions in m

A1 format · Rev. B – on the real plan

A · BUILDING GF + 8 FLOORS



B · TOPOLOGY OF ONE APARTMENT

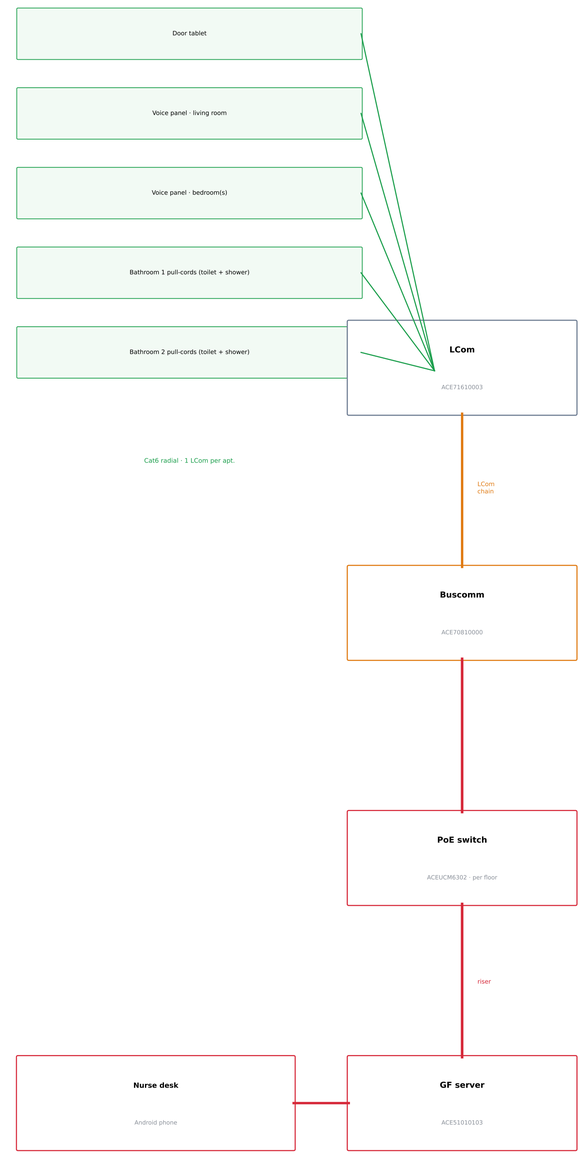

NOTES · NOTAS

1. 8 identical floors with 4 apartments (2 one-bedroom and 2 two-bedroom).
2. On each floor: rack with 2 Buscomm and a PoE switch.
3. Chain 1: x01 → x04 → public toilet. Chain 2: x02 → x03.
4. The switches run up the riser to the main GF rack.
5. Calls arrive by voice on the Android phone at the nurse desk.
6. The whole system is PoE.
7. Preliminary quantities: validate with Advantecnia and on site.

MIGDALEI YAM A TIJON · ASSISTED LIVING

Nurse call – GF + 8 floors · 32 apartments

System: ACE BG · Advantecnia Prepared by: Telab International

RISER DIAGRAM AND TOPOLOGY

SCALE · ESCALA	DATE · FECHA	REV	SHEET
S/E	15/10/2026	B	08

Base: architect's plan LS (Massad Oz / Triplet) · dimensions in m

A1 format · Rev. B – on the real plan

BILL OF MATERIALS – WHOLE BUILDING (GF + 8 floors · 32 apartments · 10 public toilets)

Code	Description	Qty.	Remark
IN THE APARTMENTS (32)			
TAB	Door tablet (iPad / Android) – call and voice	**32**	1 per apartment
VOZ	Voice call panel with buttons – ACE82182451	**80**	living room + each bedroom
TI/TD	Pull-cord – ACE40320303W (toilet and shower)	**128**	4 per apartment
LC	LCom – ACE71610003	**32**	1 per apartment
PUBLIC TOILETS (10)			
T	Pull-cord – ACE40320303W	**10**	8 floors + 2 on GF
LP	Corridor light – ACE41020309	**10**	above each door
LC	LCom – ACE71610003	**9**	1 per floor + 1 on GF
RACKS AND HEAD-END			
BC	Buscomm – ACE70810000	**17**	2 per floor + 1 on GF
SW	PoE switch – ACEUCM6302	**9**	1 per floor + GF
GAB	12U wall rack (Tripp Lite SRW12US) with patch panel	**8**	1 per floor
GAB-PB	Main floor-standing rack with UPS	**1**	GF
SRV	Server + Advantecnia software – ACE51010103	**1**	GF
TEL	Android desk phone – ACE52190200	**1**	nurse desk
CABLES (+ 15 % spare)			
—	Cat6 radial inside the apartments (green)	**1700 m**	183 m per floor
—	Cat6 / Cat7 chain LCom → Buscomm (orange)	**780 m**	82 m per floor
—	Cat6A / Cat7 racks and riser (red)	**100 m**	includes riser

NOTES · NOTAS

1. Quantities calculated from the model (typical floor × 8 + GF).

2. Cable lengths measured on the drawn route, + 15 %.

3. Prices: per current Advantecnia price list.

4. Validate on site before purchasing.

MIGDALEI YAM A TIJON · ASSISTED LIVING

Nurse call – GF + 8 floors · 32 apartments


System: ACE BG · Advantecnia Prepared by: Telab International

BILL OF MATERIALS

SCALE · ESCALA	DATE · FECHA	REV	SHEET
S/E	15/10/2026	B	09

Base: architect's plan LS (Massad Oz / Triplet) · dimensions in m

A1 format · Rev. B – on the real plan

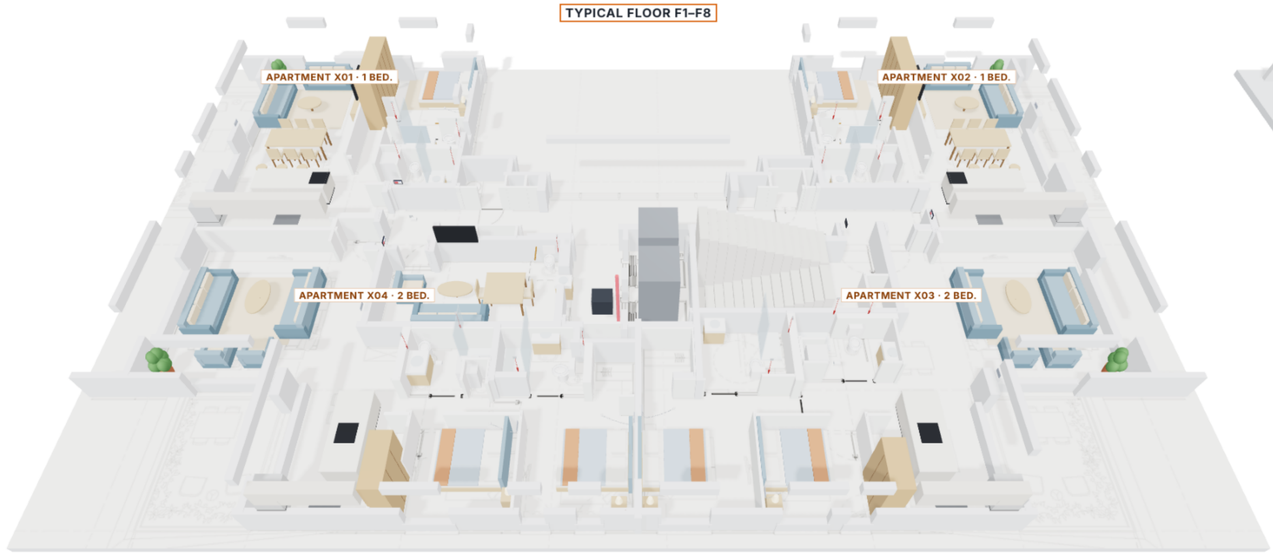


A · Typical floor – 4 apartments



B · Door tablet




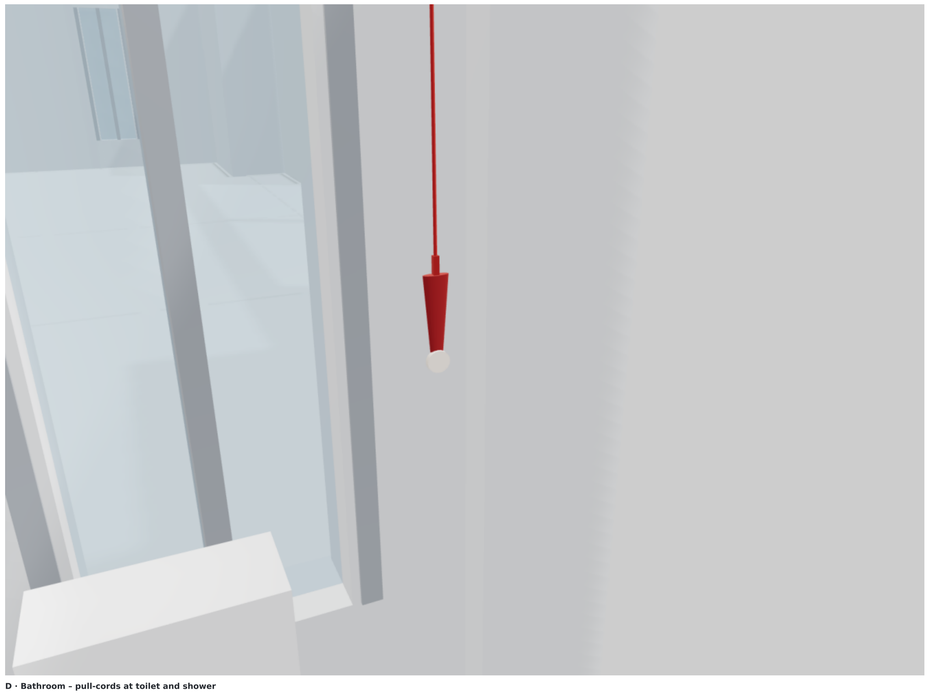

D · Bathroom – pull-cords at toilet and shower



E · GF – nurse desk

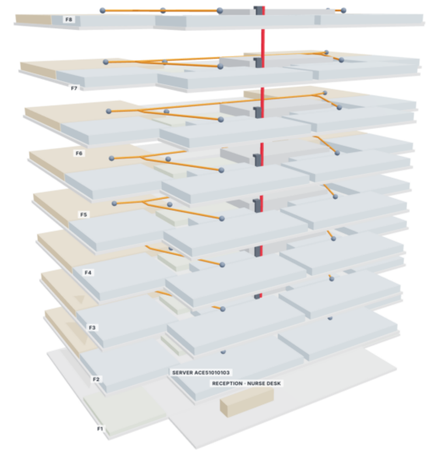

F · Building GF + 8 floors

MIGDALEI YAM A TIJON · ASSISTED LIVING

Nurse call – GF + 8 floors · 32 apartments


System: ACE BG · Advantecnia Prepared by: Telab International

3D VIEWS

SCALE · ESCALA	DATE · FECHA	REV	SHEET
S/E	15/10/2026	B	10

Base: architect's plan LS (Massad Oz / Triplet) · dimensions in m

A1 format · Rev. B – on the real plan

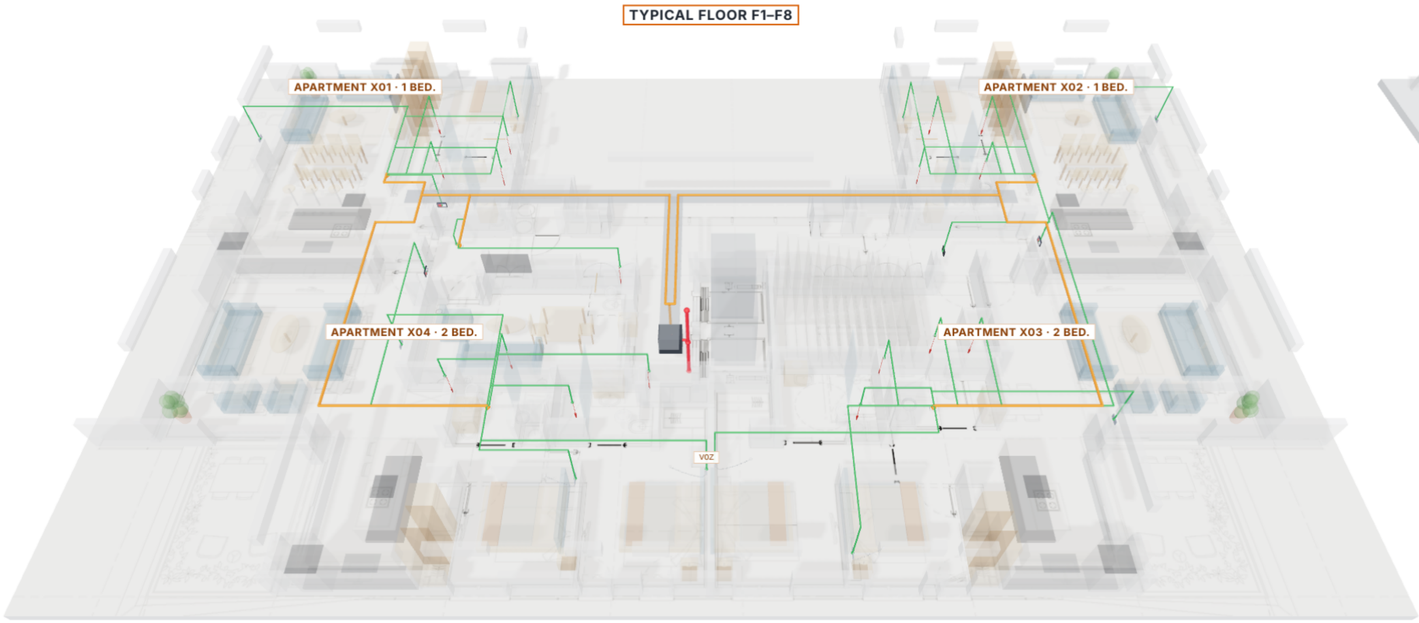

A · Typical floor – wiring (green radial · orange LCom chain · red network)



B · Ground floor – lobby and reception



C · Living room – voice panel with buttons

COLOURS · COLORES · סיעבג

- Cat6 radial: each device → its apartment LCom
  Cat6 radial: each device → apartment LCom · Cat6 רדיאל: כל מכשיר → LCom של הדירה
- Cat6 / Cat7 chain: LCom → LCom → rack Buscomm
  Cat6 / Cat7 chain: LCom → LCom → Buscomm · Cat6 / Cat7 שרשרת: LCom ← LCom ← Buscomm
- Cat6A / Cat7 network: Buscomm → switch → riser → GF server
  Cat6A / Cat7 network: Buscomm → switch → riser → GF server · Cat6A / Cat7 רשת: Buscomm ← נתב ← רייזר ← שרת

MIGDALEI YAM A TIJON · ASSISTED LIVING

Nurse call – GF + 8 floors · 32 apartments

System: ACE BG · Advantecnia Prepared by: Telab International

3D VIEWS – WIRING

SCALE · ESCALA	DATE · FECHA	REV	SHEET
S/E	15/10/2026	B	11

Base: architect's plan LS (Massad Oz / Triplet) · dimensions in m

A1 format · Rev. B – on the real plan