

EQUIPOS · DEVICES · ציוד

- **TAB** · Tablet de la puerta (iPad / Android) – llamada y voz, h 1,40 m
  Door tablet – call and voice · טאבלט בדלת – שיחה וקול · טאבלט בדלת – שיחה וקול
- **VOZ** · Panel con voz y botones ACE82182451 – salón y dormitorios, h 1,20–1,30 m
  Voice panel with buttons – living room and bedrooms · לוח קול עם לחצנים – סלון וחדרי שינה · לוח קול עם לחצנים – סלון וחדרי שינה
- Pera de llamada junto a la cama (en los dormitorios)
  Call pear next to the bed (bedrooms) · נורת קריאה ליד המיטה · נורת קריאה ליד המיטה
- **TI / TD** · Tirador de baño ACE40320303W – inodoro y ducha, h 1,85 m
  Pull-cord – toilet and shower, h 1.85 m · חבל משיכה – שירותים ומקלחת, גובה 1.85 מ' · חבל משיכה – שירותים ומקלחת, גובה 1.85 מ'
- **LP** · Luz de pasillo ACE41020309 – sobre la puerta de cada baño público
  Corridor light – above each public toilet door · תאורת מסדרון – מעל דלת כל שירותים ציבוריים · תאורת מסדרון – מעל דלת כל שירותים ציבוריים
- **LC** · LCom ACE71610003 – concentrador del departamento (cielorraso)
  LCom – apartment hub (ceiling) · LCom – מרכז דירתי (תקרה) · LCom – מרכז דירתי (תקרה)
- **GAB** · Gabinete de piso 12U: 2 Buscomm ACE70810000 + switch PoE ACEUCM6302
  Floor rack: 2 Buscomm + PoE switch · ארון קומה: 2 Buscomm + מתג PoE


CANTIDADES POR PISO × 8 PISOS

Código	Equipo	Por piso	8 pisos
TAB	Tablet de la puerta	4	32
VOZ	Panel con voz y botones	10	80
TI/TD	Tirador de baño (inodoro + ducha)	17	136
LP	Luz de pasillo (baño público)	1	8
LC	LCom	5	40
BC	Buscomm	2	16
SW	Switch PoE	1	8

NOTAS · NOTES

1. Base: plano de arquitectura L5 (piso tipo) – los 8 pisos son iguales: 4 departamentos por piso, 32 en total.
2. Departamentos x01 y x02: 1 habitación, salón con cocina y 2 baños. Departamentos x03 y x04: 2 habitaciones y 2 baños.
3. Tablet en la puerta de cada departamento (iPad / Android) para llamar y hablar con enfermería.
4. Panel con voz y botones (ACE82182451) en el salón y en cada dormitorio; en el dormitorio, con pera junto a la cama.
5. Tiradores de baño (ACE40320303W) en el inodoro y en la ducha de todos los baños, a 1,85 m.
6. Baño público por piso en la sala común: tirador + luz de pasillo sobre la puerta. Con los 2 de PB suman 10 baños públicos.
7. Gabinete de piso en el pasillo de servicio junto a los ascensores (Tripp Lite 12U, como en el plano IT).
8. Ubicaciones según las marcas del cliente en el plano L2 (nt = panel con voz, tab = tablet): ver lámina 03.

ALTURAS DE MONTAJE

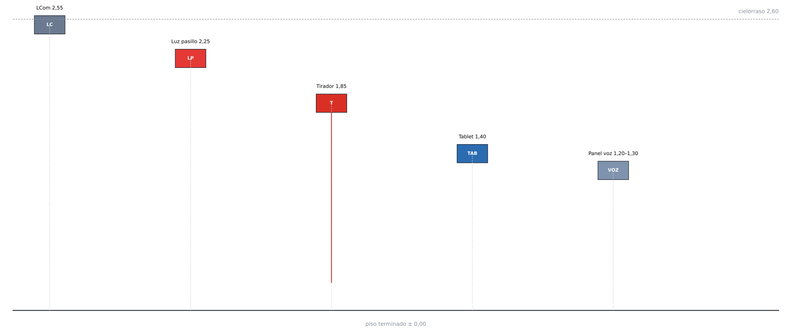



Tirador de baño



Tablet en la puerta (iPad / Android)



Luz de pasillo



Panel con voz y botones

MIGDALEI YAM A TIJON · VIVIENDA TUTELADA

Llamada de enfermería – PB + 8 pisos · 32 departamentos

Sistema: ACE BG · Advantecnia Elaboró: Telab International

PISO TIPO P1–P8 · LLAMADA DE ENFERMERÍA

Typical floor F1–F8 · nurse call

ESCALA · SCALE	FECHA · DATE	REV	LÁMINA
1:60	15/10/2026	B	01

Base: plano del arquitecto L5 (Massad Oz / Triplet) · cotas en metros

Formato A1 · Rev. B – sobre plano real

שירותים קריאת אחות



Tirador de baño

Código	**ACE40320303W**
Ubicación	Inodoro y ducha de cada baño y de los 10 baños públicos
Altura	**1,85 m**
Cantidad	**138**

1

טבלט אנדרואיד קריאת אחות



Tablet en la puerta (iPad / Android)

Código	**Advantecnia TV**
Ubicación	En el lobby, junto a la puerta de cada departamento
Altura	**1,40 m**
Cantidad	**32**

2

NOTAS · NOTES

1. Fotos de referencia de ACE BG / Advantecnia, con su título.

2. Tirador: cordón rojo con empuñadura, alcanzable desde el piso.

3. La tablet de la puerta llama y habla con enfermería.

4. La luz de pasillo se enciende cuando llaman desde el baño público.

5. El panel tiene botón rojo de llamada, botón azul (izq.) y verde (der.) y altavoz para hablar.

6. Además en cada departamento: LCom ACE71610003 en el cielorraso.

7. En PB: teléfono de escritorio Android ACE52190200 en el desk de enfermería.

מנורה קריאת אחות



Luz de pasillo

Código	**ACE41020309**
Ubicación	Sobre la puerta de cada baño público
Altura	**2,25 m**
Cantidad	**10**

3

פנל קריאת אחות



Panel con voz y botones

Código	**ACE82182451**
Ubicación	Salón y cada dormitorio (en el dormitorio, con pera)
Altura	**1,20–1,30 m**
Cantidad	**80**

4

MIGDALEI YAM A TIJON · VIVIENDA TUTELADA

Llamada de enfermería – PB + 8 pisos · 32 departamentos

Sistema: ACE BG · Advantecnia Elaboró: Telab International


EQUIPOS DEL SISTEMA

System devices

ESCALA · SCALE	FECHA · DATE	REV	LÁMINA
S/E	15/10/2026	B	02

Base: plano del arquitecto L5 (Massad Oz / Triplet) · cotas en metros

Formato A1 · Rev. B – sobre plano real

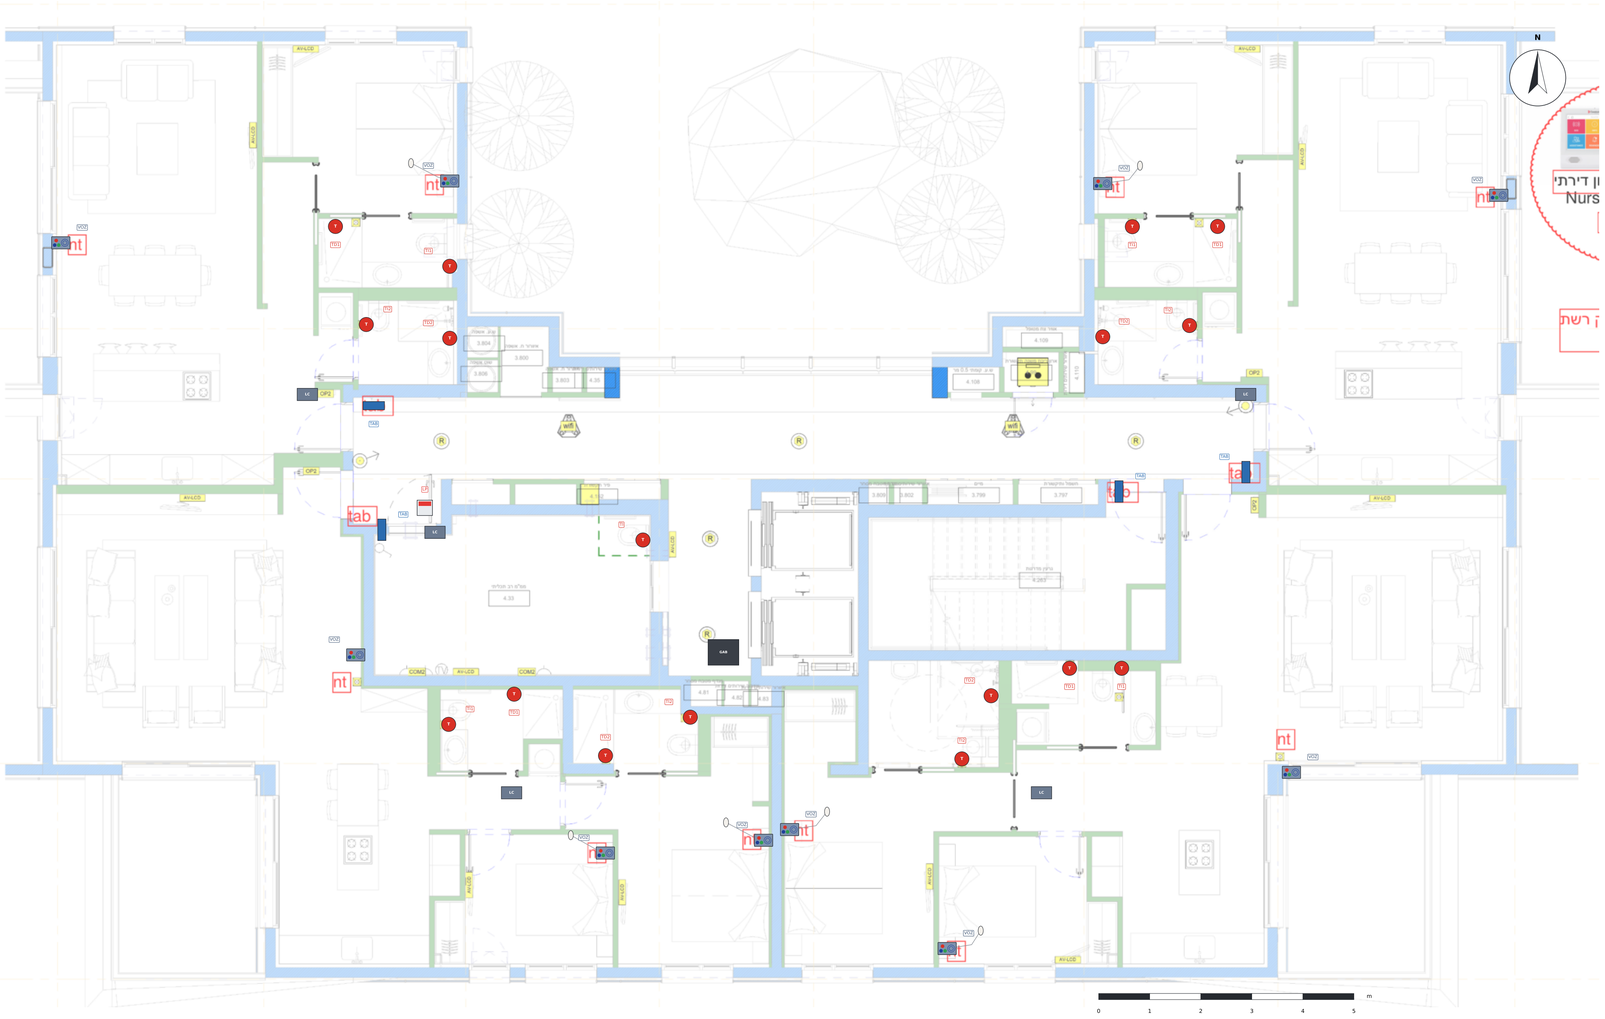

NOTAS · NOTES

1. Fondo: plano IT L2 del cliente con sus marcas en rojo: «nt» = panel con voz y «tab» = tablet de la puerta.

2. Encima, en color: los equipos de esta propuesta. Cada panel y cada tablet está donde el cliente lo marcó.

3. Los cuadrados amarillos ⊠ de los baños del plano L2 son los tiradores (inodoro y ducha).

4. Las 4 tablets quedan en el lobby, junto a la puerta de cada departamento, como en las marcas «tab».

5. El plano L2 y el L5 (base de esta propuesta) tienen la misma estructura; L5 es el piso tipo de los pisos 1 a 8.

EQUIPOS · DEVICES · דגיג

- **TAB** · Tablet de la puerta (iPad / Android) – llamada y voz, h 1,40 m
  Door tablet – call and voice · טאבלט ליד הדלת – שיחה וקול · 1.40 מ׳
- **VOZ** · Panel con voz y botones ACE82182451 – salón y dormitorios, h 1,20–1,30 m
  Voice panel with buttons – living room and bedrooms · פנל דיבור עם כפתורים – סלון וחדרי שינה · 1.20–1.30 מ׳
- Pera de llamada junto a la cama (en los dormitorios)
  Call pear next to the bed (bedrooms) · כפתור לידי מיטה – חדרי שינה
- **TI / TD** · Tirador de baño ACE40320303W – inodoro y ducha, h 1,85 m
  Pull-cord – toilet and shower, h 1.85 m · חבל משיכה בשירותים ובמקלחת – לחצן חירום · 1.85 מ׳
- **LP** · Luz de pasillo ACE41020309 – sobre la puerta de cada baño público
  Corridor light – above each public toilet door · מנורת מסדרון מעל כל דלת שירותים ציבוריים · מעל הדלת

שירותים קריאת אחות



Tirador de baño

טבלט אנדרואיד קריאת אחות



Tablet en la puerta (iPad / Android)

מנורה קריאת אחות



Luz de pasillo

פנל קריאת אחות



Panel con voz y botones

MIGDALEI YAM A TIJON · VIVIENDA TUTELADA

Llamada de enfermería – PB + 8 pisos · 32 departamentos

Sistema: ACE BG · Advantecnia Elaboró: Telab International


MARCAS DEL CLIENTE (PLANO L2) Y PROPUESTA

Client marks (plan L2) and proposal

ESCALA · SCALE	FECHA · DATE	REV	LÁMINA
1:60	15/10/2026	B	03

Base: plano del arquitecto L5 (Massad Oz / Triplet) · cotas en metros

Formato A1 · Rev. B – sobre plano real

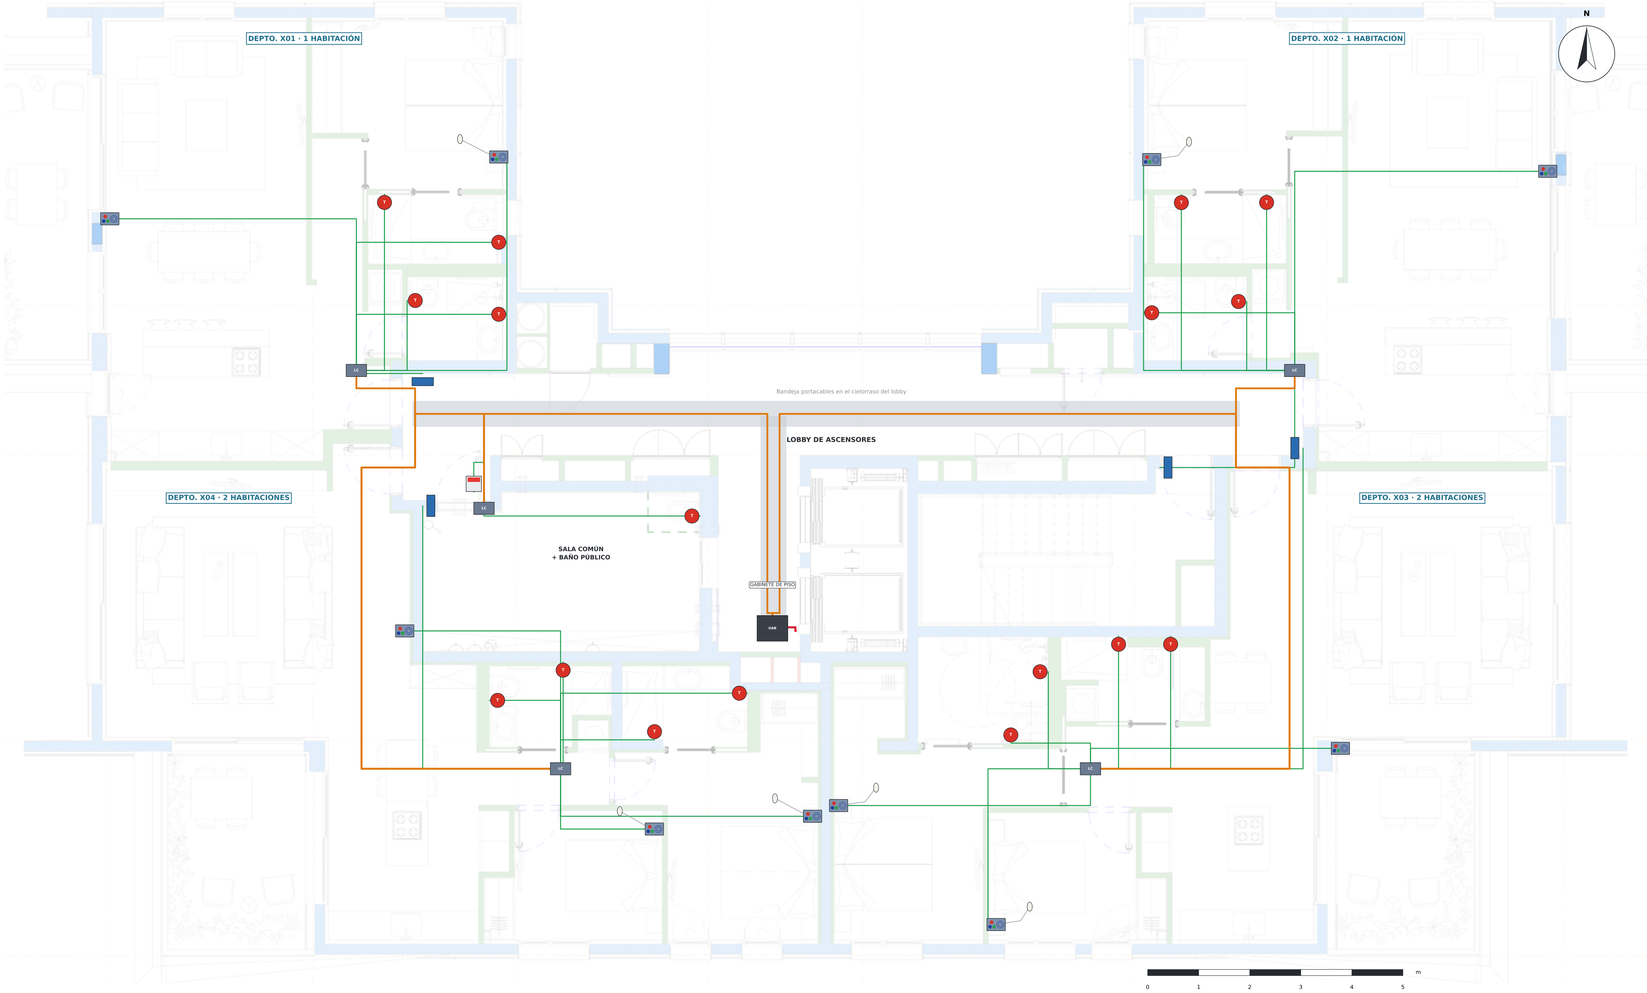

CABLEADO · WIRING · סוגיות

- Cat6 radial: cada equipo → LCom de su departamento
  Cat6 radial: each device → apartment LCom · Cat6 רדיאלי: כל מכשיר → LCom הדירה
- Cat6 / Cat7 cadena: LCom → LCom → Buscomm del gabinete
  Cat6 / Cat7 chain: LCom → LCom → Buscomm · Cat6 / Cat7 שרשרת: LCom ← LCom ← Buscomm
- Cat6A / Cat7 red: Buscomm → switch → montante → servidor PB
  Cat6A / Cat7 network: Buscomm → switch → riser → GF server · Cat6A / Cat7 רשת: Buscomm ← נתב ← עמוד ← שרת

LONGITUDES DEL PISO TIPO (sin reserva)

Cat6 radial dentro de los departamentos	**183 m**
Cat6 / Cat7 cadena LCom → Buscomm	**82 m**
Cat6A / Cat7 gabinete y montante	**4 m**

NOTAS · NOTES

1. Cada equipo va radial (Cat6) al LCom de su departamento, en el cielorraso del hall.
2. Los LCom se encadenan por la bandeja del lobby hasta el gabinete del piso: x01 → x04 → sala común → Buscomm 1 · x02 → x03 → Buscomm 2.
3. El switch PoE del piso sube por el montante Cat6A / Cat7 hasta el servidor de PB.
4. Todo es PoE: no hace falta 230 V en los equipos de los departamentos.

NOTAS · NOTES

1. Base: plano de arquitectura L5 (piso tipo) – los 8 pisos son iguales: 4 departamentos por piso, 32 en total.
2. Departamentos x01 y x02: 1 habitación, salón con cocina y 2 baños. Departamentos x03 y x04: 2 habitaciones y 2 baños.
3. Tablet en la puerta de cada departamento (iPad / Android) para llamar y hablar con enfermería.
4. Panel con voz y botones (ACE82182451) en el salón y en cada dormitorio; en el dormitorio, con pera junto a la cama.
5. Tiradores de baño (ACE40320303W) en el inodoro y en la ducha de todos los baños, a 1,85 m.
6. Baño público por piso en la sala común: tirador + luz de pasillo sobre la puerta. Con los 2 de PB suman 10 baños públicos.
7. Gabinete de piso en el pasillo de servicio junto a los ascensores (Tripp Lite 12U, como en el plano IT).
8. Ubicaciones según las marcas del cliente en el plano L2 (nt = panel con voz, tab = tablet): ver lámina 03.

MIGDALEI YAM A TIJON · VIVIENDA TUTELADA

Llamada de enfermería – PB + 8 pisos · 32 departamentos

Sistema: ACE BG · Advantecnia Elaboró: Telab International


PISO TIPO P1–P8 · CABLEADO

Typical floor F1–F8 · wiring

ESCALA · SCALE	FECHA · DATE	REV	LÁMINA
1:60	**15/10/2026**	**B**	**04**

Base: plano del arquitecto L5 (Massad Oz / Triplet) · cotas en metros

Formato A1 · Rev. B – sobre plano real

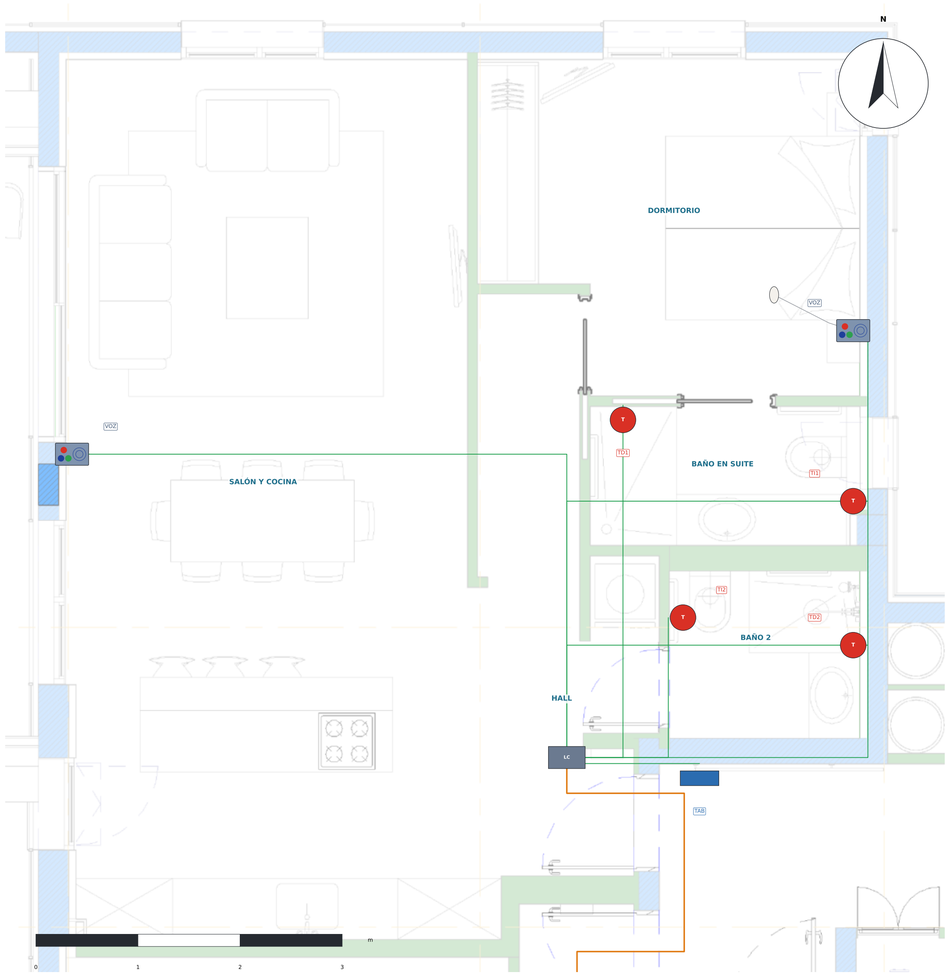

EQUIPOS DEL DEPARTAMENTO

ID	Equipo	Local	Altura
TAB	Tablet de la puerta	Hall	1,40 m
VOZ-S	Panel voz y botones	Salón y cocina	1,30 m
VOZ-D	Panel voz y botones + pera	Dormitorio	1,20 m
TI1	Tirador de baño	Baño en suite	1,85 m
TD1	Tirador de baño	Baño en suite	1,85 m
TI2	Tirador de baño	Baño 2	1,85 m
TD2	Tirador de baño	Baño 2	1,85 m
LCOM	LCom ACE71610003	Hall	2,55 m

SÍMBOLOS · SYMBOLS · סימנים

TAB · Tablet de la puerta (iPad / Android) – llamada y voz, h 1,40 m
Door tablet – call and voice · דגם ראיין – התקנה וקלאנט

VOZ · Panel con voz y botones ACE82182451 – salón y dormitorios, h 1,20–1,30 m
Voice panel with buttons – living room and bedrooms · דגם ידידותי בלוח – סלון וחדרי שינה

Pera de llamada junto a la cama (en los dormitorios)
Call pear next to the bed (bedrooms) · הנחיה ליד המיטה בחדר

TI / TD · Tirador de baño ACE40320303W – inodoro y ducha, h 1,85 m
Pull-cord – toilet and shower, h 1.85 m · מתקן משיכה לשירותים ולמקלחת – לגובה 1.85 מ'

LP · Luz de pasillo ACE41020309 – sobre la puerta de cada baño público
Corridor light – above each public toilet door · מיקום בחלק העליון של דלת כל שירותים ציבוריים

LC · LCom ACE71610003 – concentrador del departamento (cielorraso)
LCom – apartment hub (ceiling) · LCom – ריכוז הדירה (בתקרה)

NOTAS · NOTES

1. El departamento x02 es el espejo del x01 (misma dotación).
2. Tablet en el lobby, junto a la puerta de entrada (marca «tab» del cliente).
3. Panel con voz en el salón y en el dormitorio (con pera junto a la cama).
4. 2 baños: tirador en el inodoro y en la ducha de cada uno (4 tiradores).
5. Todo va radial en Cat6 al LCom del hall.

שירותים קריאת אחות



Tirador de baño

טבלט אנדרואיד קריאת אחות



Tablet en la puerta (iPad / Android)

מנורה קריאת אחות



Luz de pasillo

פנל קריאת אחות



Panel con voz y botones

MIGDALEI YAM A TIJON · VIVIENDA TUTELADA

Llamada de enfermería – PB + 8 pisos · 32 departamentos

Sistema: ACE BG · Advantecnia Elaboró: Telab International

DEPTO. 1 HABITACIÓN (x01 / x02)

1-bedroom apartment (x01 / x02)

ESCALA · SCALE	FECHA · DATE	REV	LÁMINA
1:30	15/10/2026	B	05

Base: plano del arquitecto L5 (Massad Oz / Triplet) · cotas en metros

Formato A1 · Rev. B – sobre plano real



EQUIPOS DEL DEPARTAMENTO

ID	Equipo	Local	Altura
TAB	Tablet de la puerta	Hall	1,40 m
VOZ-S	Panel voz y botones	Salón	1,30 m
VOZ-D1	Panel voz y botones + pera	Dormitorio 1	1,20 m
VOZ-D2	Panel voz y botones + pera	Dormitorio 2	1,20 m
TI1	Tirador de baño	Baño 1	1,85 m
TD1	Tirador de baño	Baño 1	1,85 m
TI2	Tirador de baño	Baño 2	1,85 m
TD2	Tirador de baño	Baño 2	1,85 m
LCOM	LCom ACE71610003	Hall	2,55 m

SÍMBOLOS · SYMBOLS · סימנים

TAB · Tablet de la puerta (iPad / Android) – llamada y voz, h 1,40 m
Door tablet – call and voice · טאבלט בפתח – שיחה וקול · גובה 1.40 מ׳

VOZ · Panel con voz y botones ACE82182451 – salón y dormitorios, h 1,20–1,30 m
Voice panel with buttons – living room and bedrooms · לוח קול עם לחצנים – סלון וחדרי שינה · גובה 1.20–1.30 מ׳

Pera de llamada junto a la cama (en los dormitorios)
Call pear next to the bed (bedrooms) · כפתור חיווי ליד מיטה · ליד המיטות

TI / TD · Tirador de baño ACE40320303W – inodoro y ducha, h 1,85 m
Pull-cord – toilet and shower, h 1.85 m · חבל משיכה – אסלה ומקלחת · גובה 1.85 מ׳

LP · Luz de pasillo ACE41020309 – sobre la puerta de cada baño público
Corridor light – above each public toilet door · נורת מסדרון – מעל דלת כל שירותי ציבור

LC · LCom ACE71610003 – concentrador del departamento (cielorraso)
LCom – apartment hub (ceiling) · LCom – מרכזיה בתוך הדירה (בתקרה)

NOTAS · NOTES

1. El departamento x03 tiene la misma dotación (baños con otra distribución).
2. Tablet en el lobby, junto a la puerta de entrada (marca «tab» del cliente).
3. Panel con voz en el salón y en los 2 dormitorios (con pera junto a la cama).
4. 2 baños: tirador en el inodoro y en la ducha de cada uno (4 tiradores).
5. Todo va radial en Cat6 al LCom del pasillo de los dormitorios.

שירותים קריאת אחות



Tirador de baño

טבלט אנדרואיד קריאת אחות



Tablet en la puerta (iPad / Android)

מנורה קריאת אחות



Luz de pasillo

פנל קריאת אחות



Panel con voz y botones

MIGDALEI YAM A TIJON · VIVIENDA TUTELADA

Llamada de enfermería – PB + 8 pisos · 32 departamentos

Sistema: ACE BG · Advantecnia Elaboró: Telab International


DEPTO. 2 HABITACIONES (x04 / x03)

2-bedroom apartment (x04 / x03)


ESCALA · SCALE	FECHA · DATE	REV	LÁMINA
1:35	15/10/2026	B	06

Base: plano del arquitecto L5 (Massad Oz / Triplet) · cotas en metros

Formato A1 · Rev. B – sobre plano real

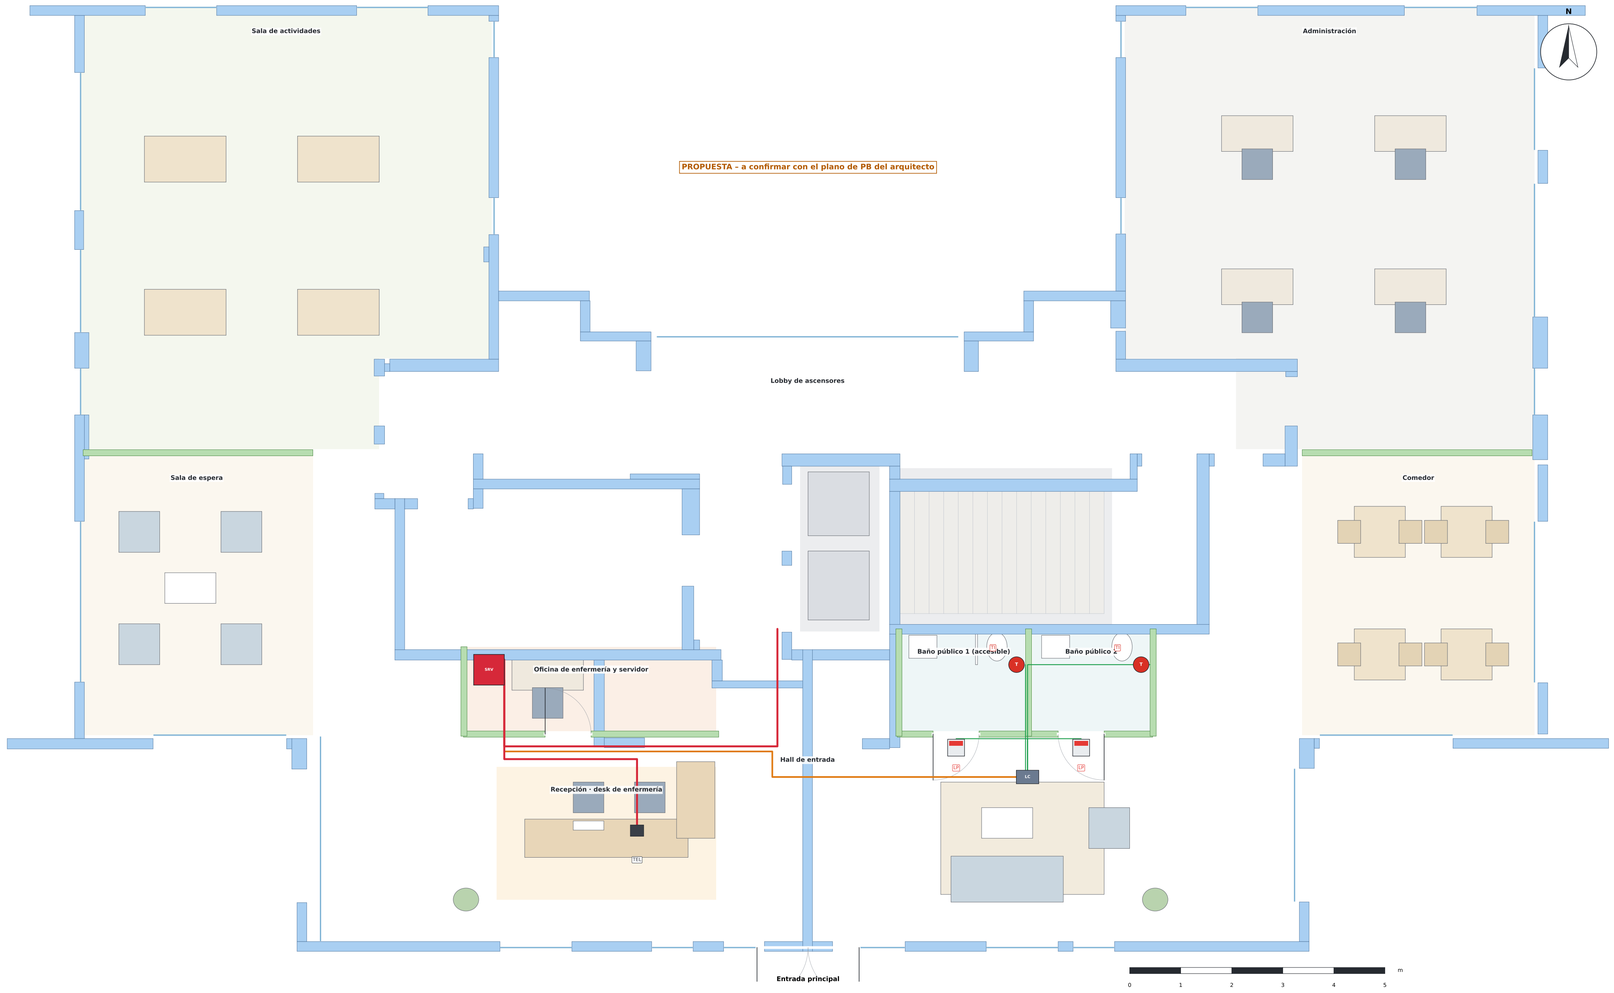

DETALLE · RECEPCIÓN Y DESK DE ENFERMERÍA (1:40)

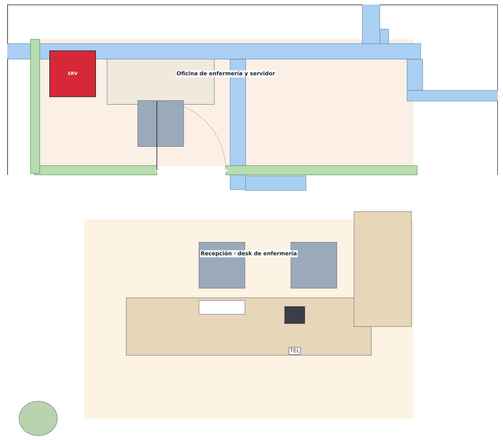

NOTAS · NOTES

1. Desk de enfermería en la recepción, frente a la entrada y a los ascensores.
2. Sobre el desk: teléfono de escritorio Android ACE52190200 (recibe llamadas y voz).
3. Detrás del desk: oficina de enfermería con el gabinete principal: servidor ACE51010103, switch PoE ACEUCM6302 y Buscomm de PB.
4. 2 baños públicos en PB: tirador junto al inodoro y luz de pasillo sobre cada puerta.
5. El montante de los 8 pisos baja por el núcleo hasta el gabinete principal.
6. Distribución de PB propuesta: se ajusta cuando llegue el plano del arquitecto.

SÍMBOLOS · SYMBOLS · סימלים

- **TI / TD** · Tirador de baño ACE40320303W – inodoro y ducha, h 1,85 m
  Pull-cord · toilet and shower, h 1.85 m · מתקן חירום: חלקלק תלוי – קרוב האסלה ומקלחת, גובה 1.85 מ'
- **LP** · Luz de pasillo ACE41020309 – sobre la puerta de cada baño público
  Corridor light · above each public toilet door · מיקרוקיר מסוג יקר תלוי – בגישה לכל שירותים ציבוריים
- **LC** · LCom ACE71610003 · concentrador del departamento (cielorraso)
  LCom – apartment hub (ceiling) · LCom · רכזת (קונצ'רטו) בדירה (תקרה)
- **TEL** · Teléfono de escritorio Android ACE52190200
  Android desk phone · טלפון שולחני מבוסס אנדרואיד
- **SRV** · Gabinete PB: servidor ACE51010103 + switch + Buscomm
  SP rack: server + switch + Buscomm · ארון שרתים קומתי: שרת + מתג + Buscomm

MIGDALEI YAM A TIJON · VIVIENDA TUTELADA

Llamada de enfermería – PB + 8 pisos · 32 departamentos

Sistema: ACE BG · Advantecnia Elaboró: Telab International

PLANTA BAJA · LOBBY Y DESK DE ENFERMERÍA

Ground floor · lobby and nurse desk

ESCALA · SCALE	FECHA · DATE	REV	LÁMINA
1:60	15/10/2026	B	07


Base: plano del arquitecto L5 (Massad Oz / Triplet) · cotas en metros

Formato A1 · Rev. B - sobre plano real

A · EDIFICIO PB + 8 PISOS



B · TOPOLOGÍA DE UN DEPARTAMENTO

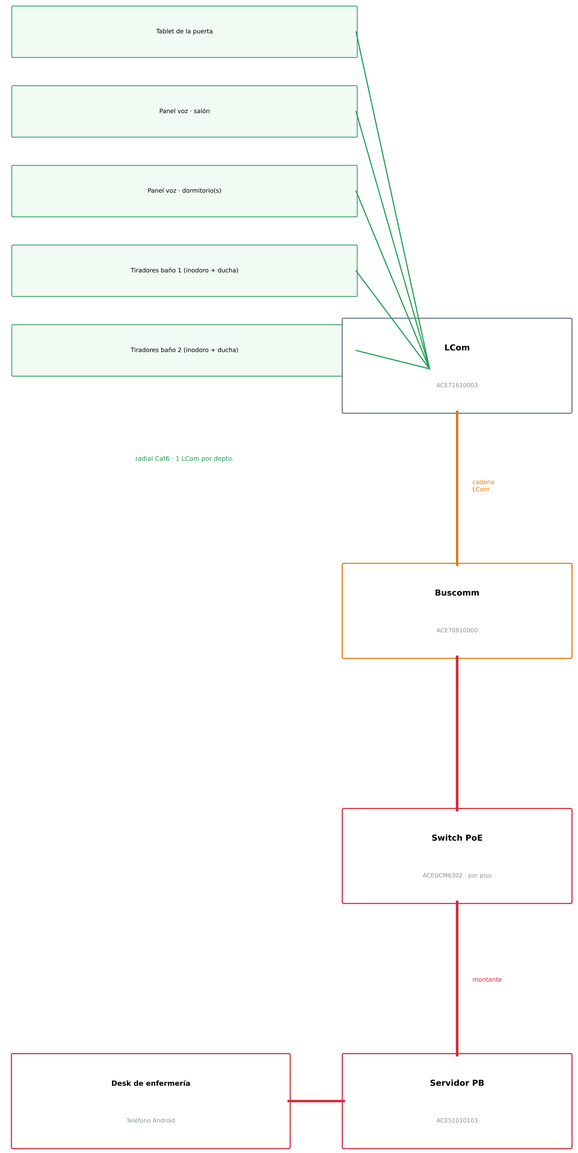

NOTAS · NOTES

1. 8 pisos iguales con 4 departamentos (2 de 1 habitación y 2 de 2).
2. En cada piso: gabinete con 2 Buscomm y un switch PoE.
3. Cadena 1: x01 → x04 → baño público. Cadena 2: x02 → x03.
4. Los switches suben por el montante hasta el gabinete principal de PB.
5. Las llamadas llegan por voz al teléfono Android del desk de enfermería.
6. Todo el sistema es PoE.
7. Cantidades de anteproyecto: validar con Advantecnia y en obra.

MIGDALEI YAM A TIJON · VIVIENDA TUTELADA

Llamada de enfermería – PB + 8 pisos · 32 departamentos

Sistema: ACE BG · Advantecnia Elaboró: Telab International

ESQUEMA VERTICAL Y TOPOLOGÍA

Riser diagram and topology

ESCALA · SCALE	FECHA · DATE	REV	LÁMINA
S/E	15/10/2026	B	08

Base: plano del arquitecto L5 (Massad Oz / Triplet) · cotas en metros

Formato A1 · Rev. B – sobre plano real

LISTA DE MATERIALES – EDIFICIO COMPLETO (PB + 8 pisos · 32 departamentos · 10 baños públicos)

Código	Descripción	Cant.	Observación
EN LOS DEPARTAMENTOS (32)			
TAB	Tablet de la puerta (iPad / Android) – llamada y voz	**32**	1 por departamento
VOZ	Panel de llamada con voz y botones – ACE82182451	**80**	salón + cada dormitorio
TI/TD	Tirador de baño – ACE40320303W (inodoro y ducha)	**128**	4 por departamento
LC	LCom – ACE71610003	**32**	1 por departamento
BAÑOS PÚBLICOS (10)			
T	Tirador de baño – ACE40320303W	**10**	8 pisos + 2 en PB
LP	Luz de pasillo – ACE41020309	**10**	sobre cada puerta
LC	LCom – ACE71610003	**9**	1 por piso + 1 en PB
GABINETES Y CENTRAL			
BC	Buscomm – ACE70810000	**17**	2 por piso + 1 en PB
SW	Switch PoE – ACEUCM6302	**9**	1 por piso + PB
GAB	Gabinete mural 12U (Tripp Lite SRW12US) con patch panel	**8**	1 por piso
GAB-PB	Gabinete principal de piso con UPS	**1**	PB
SRV	Servidor + software Advantecnia – ACE51010103	**1**	PB
TEL	Teléfono de escritorio Android – ACE52190200	**1**	desk de enfermería
CABLES (+ 15 % de reserva)			
—	Cat6 radial dentro de los departamentos (verde)	**1700 m**	183 m por piso
—	Cat6 / Cat7 cadena LCom → Buscomm (naranja)	**780 m**	82 m por piso
—	Cat6A / Cat7 gabinetes y montante (rojo)	**100 m**	incluye montante

NOTAS · NOTES

1. Cantidades calculadas del modelo (piso tipo × 8 + PB).
2. Longitudes de cable medidas sobre el recorrido dibujado, + 15 %.
3. Precios: según lista vigente de Advantecnia.
4. Validar en obra antes de comprar.

MIGDALEI YAM A TIJON · VIVIENDA TUTELADA

Llamada de enfermería – PB + 8 pisos · 32 departamentos

Sistema: ACE BG · Advantecnia Elaboró: Telab International


LISTA DE MATERIALES

Bill of materials

ESCALA · SCALE	FECHA · DATE	REV	LÁMINA
S/E	15/10/2026	B	09

Base: plano del arquitecto L5 (Massad Oz / Triplet) · cotas en metros

Formato A1 · Rev. B – sobre plano real

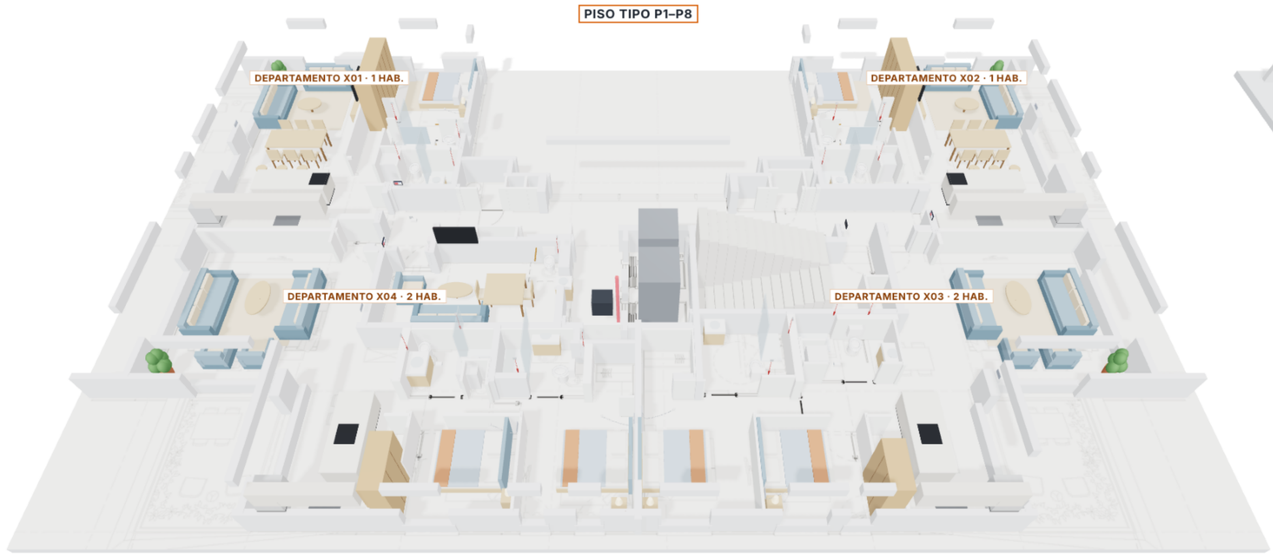


A · Piso tipo – 4 departamentos



B · Tablet de la puerta




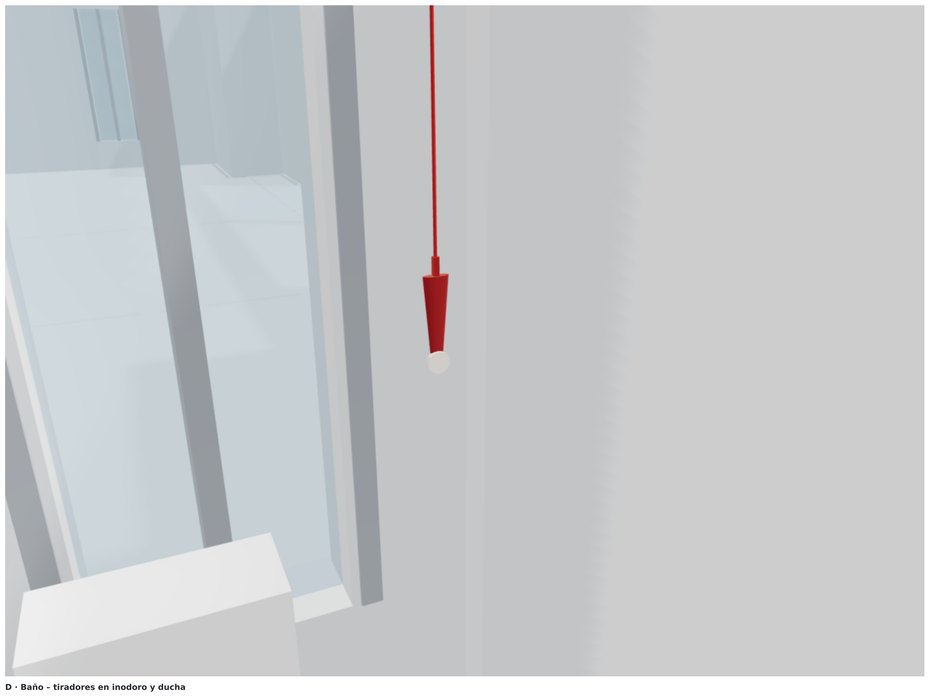

D · Baño – tiradores en inodoro y ducha



E · PB – desk de enfermería

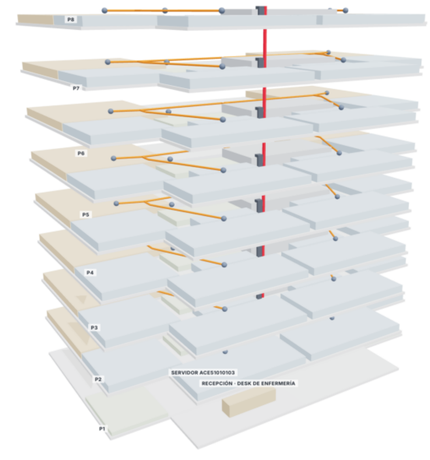

F · Edificio PB + 8 pisos

MIGDALEI YAM A TIJON · VIVIENDA TUTELADA

Llamada de enfermería – PB + 8 pisos · 32 departamentos

Sistema: ACE BG · Advantecnia Elaboró: Telab International


VISTAS 3D

3D views

ESCALA · SCALE	FECHA · DATE	REV	LÁMINA
S/E	15/10/2026	B	10

Base: plano del arquitecto L5 (Massad Oz / Triplet) · cotas en metros

Formato A1 · Rev. B – sobre plano real

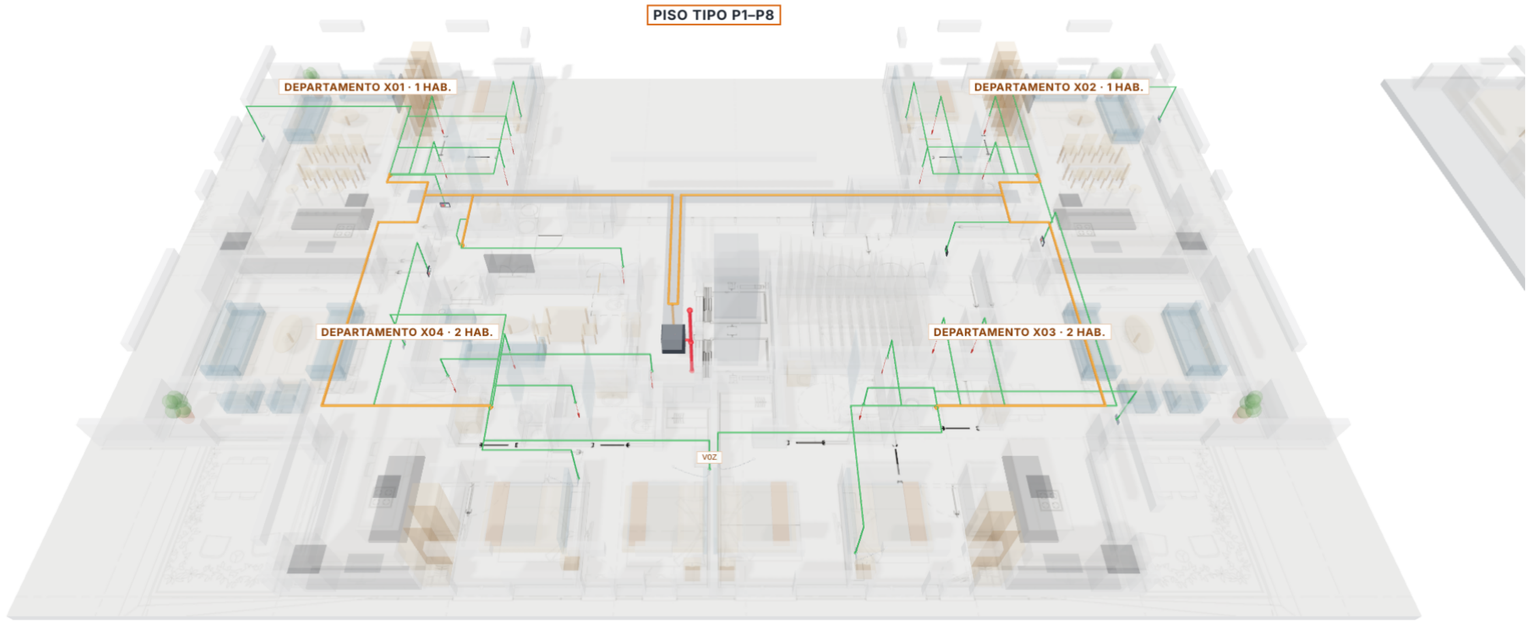

A · Piso tipo – cableado (verde radial · naranja cadena LCom · rojo red)



B · Planta baja – lobby y recepción



C · Salón – panel con voz y botones

COLORES · COLOURS · סיענב

Cat6 radial: cada equipo → LCom de su departamento
Cat6 radial: each device → apartment LCom · Cat6 רדיאל: כל מכשיר → LCom של הדירה

Cat6 / Cat7 cadena: LCom → LCom → Buscomm del gabinete
Cat6 / Cat7 chain: LCom → LCom → Buscomm · Cat6 / Cat7 שרשרת: LCom ← LCom ← Buscomm

Cat6A / Cat7 red: Buscomm → switch → montante → servidor PB
Cat6A / Cat7 network: Buscomm → switch → riser → GF server · Cat6A / Cat7 רשת: Buscomm ← מתג ← ריסר ← שרת

MIGDALEI YAM A TIJON · VIVIENDA TUTELADA

Llamada de enfermería – PB + 8 pisos · 32 departamentos

Sistema: ACE BG · Advantecnia Elaboró: Telab International

VISTAS 3D – CABLEADO

3D views – wiring

ESCALA · SCALE	FECHA · DATE	REV	LÁMINA
S/E	15/10/2026	B	11

Base: plano del arquitecto L5 (Massad Oz / Triplet) · cotas en metros

Formato A1 · Rev. B – sobre plano real