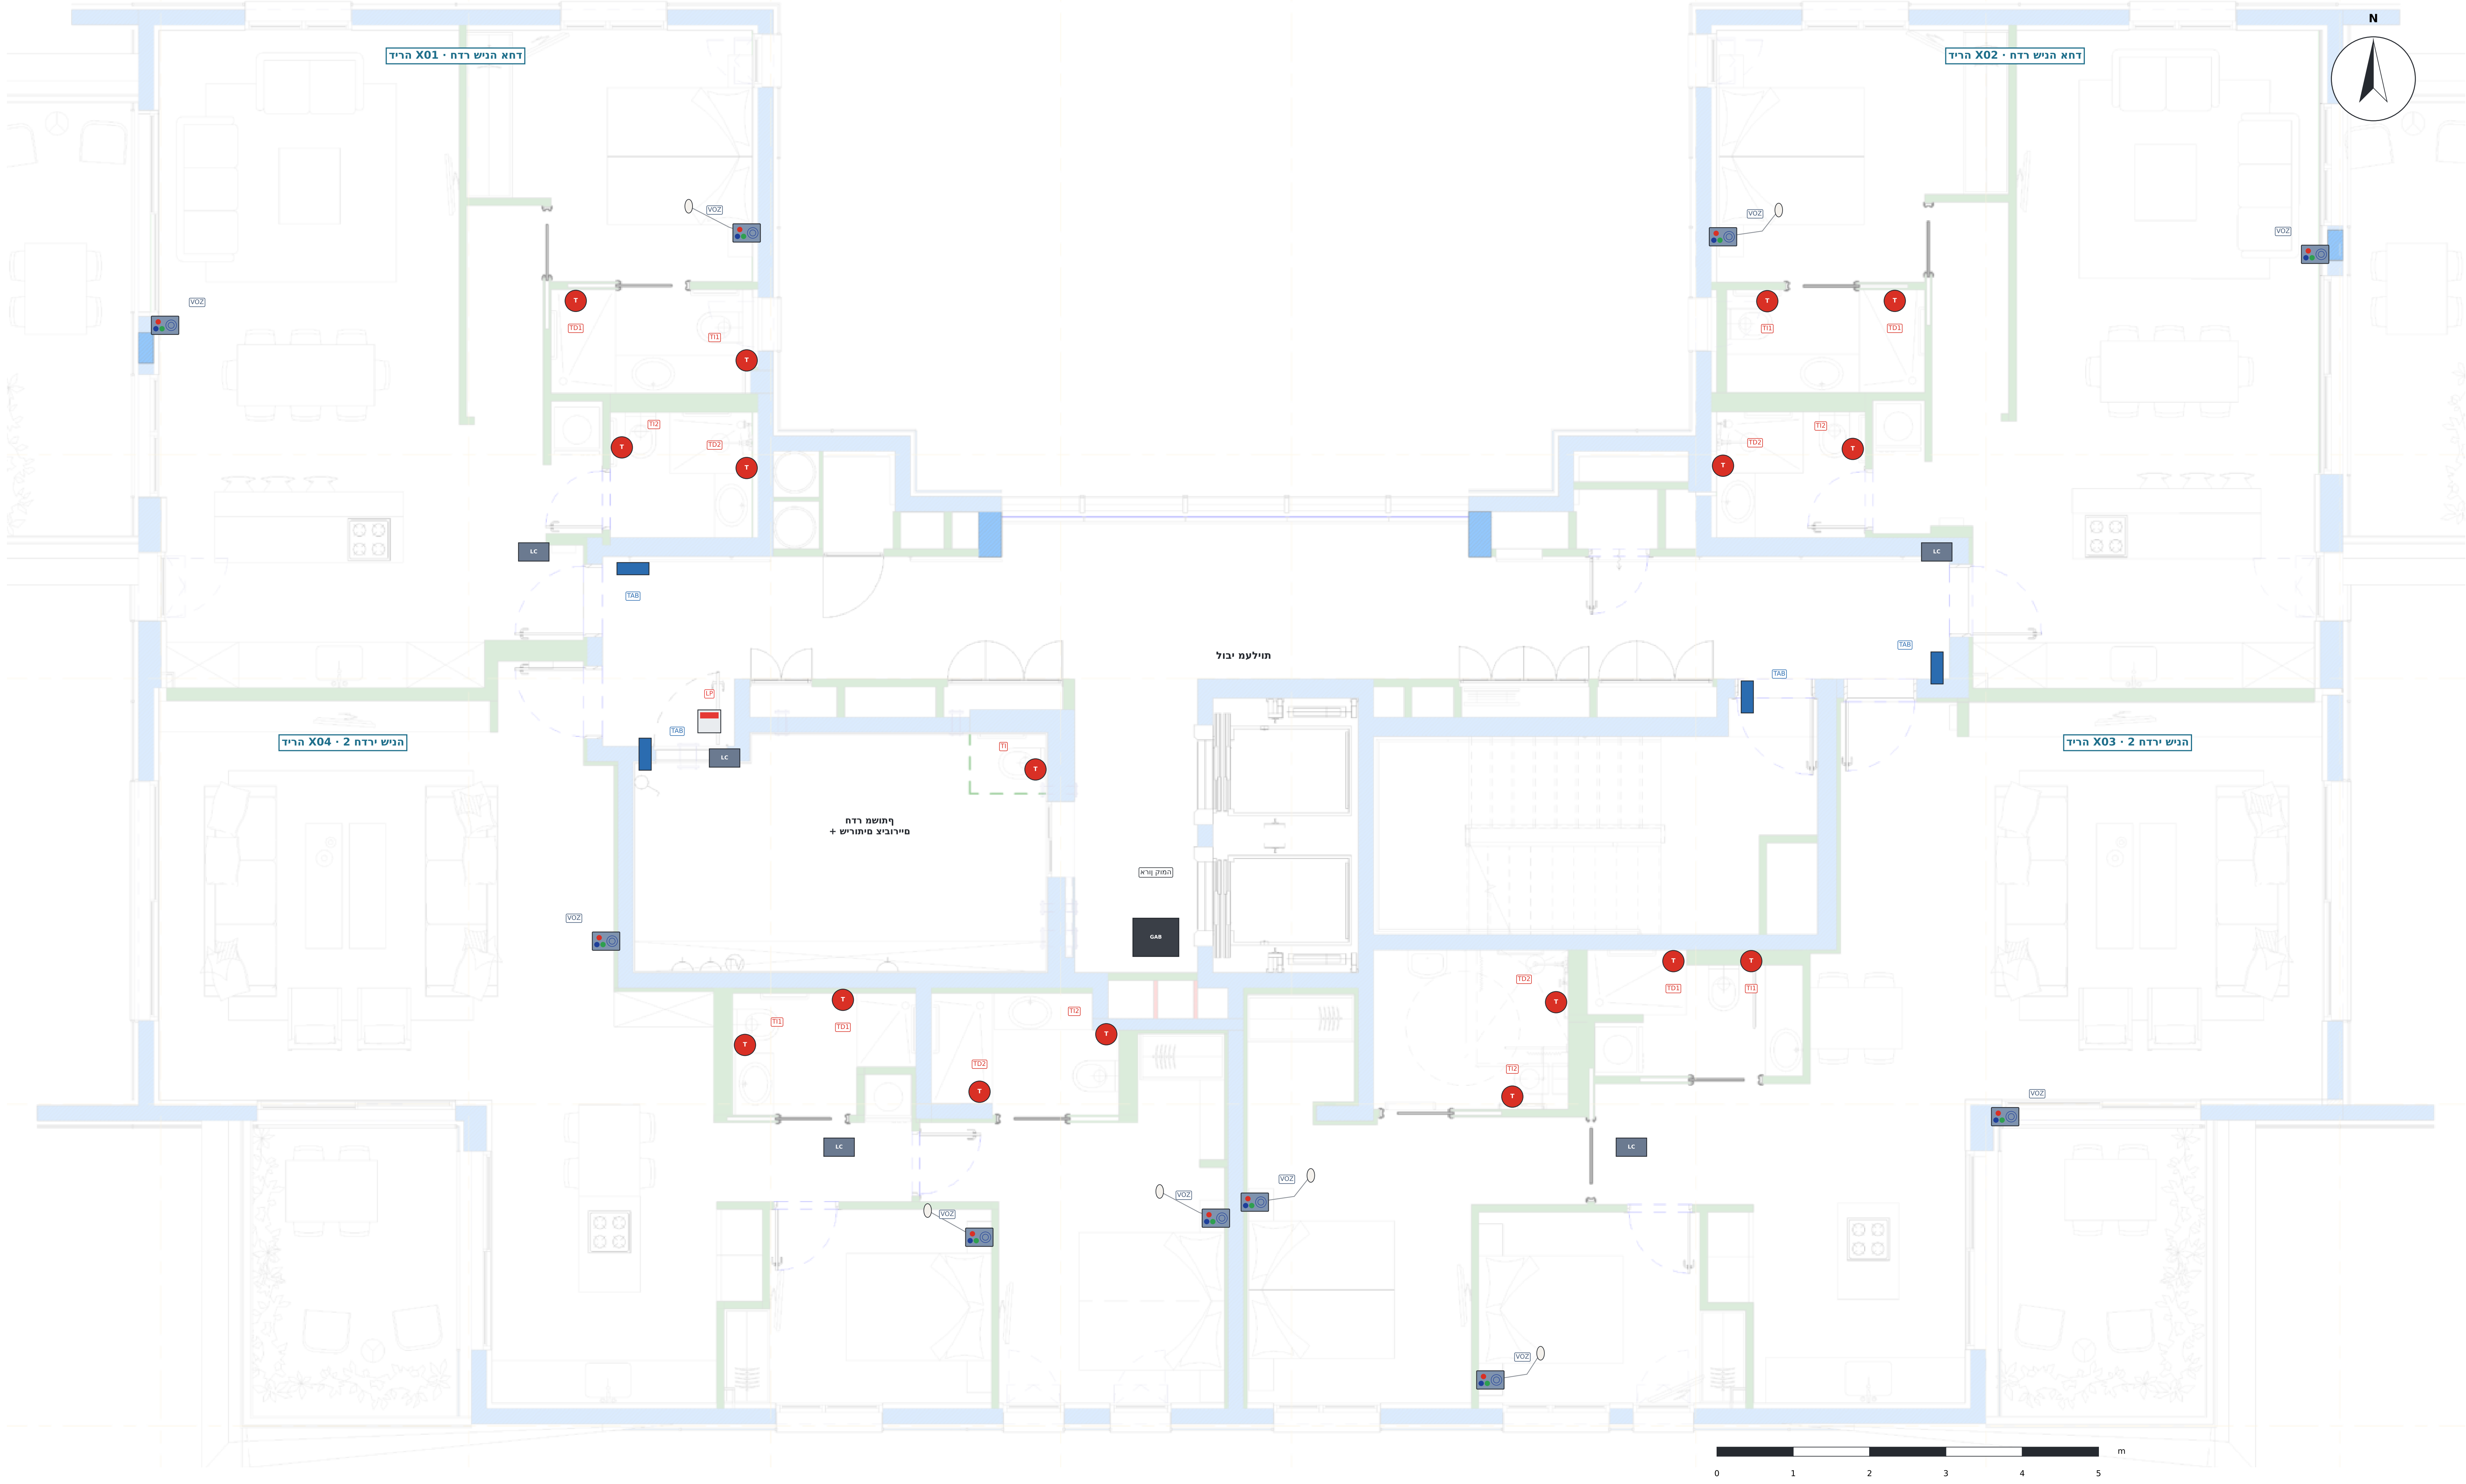
N
דירה X01 · חדר שינה אחד
דירה X02 · חדר שינה אחד
דירה X04 · 2 חדרי שינה
דירה X03 · 2 חדרי שינה
לובי מעליות
חדר משותף
+ שירותים ציבוריים
ארון קומה
GAB
LC
TAB
VOZ
LP
TI
TD
TD2
T
0
1
2
3
4
5
m

DEVICES · EQUIPOS · ציוד

🟦	TAB · טאבלט בכניסה (iPad / אנדרואיד) – קריאה ודיבור, גובה 1.40 מ' Door tablet – call and voice · טאבלט בכניסה – קריאה ודיבור
VOZ	VOZ · פנל קולי עם לחצנים ACE82182451 – סלון וחדרי שינה, גובה 1.20–1.30 מ' Voice panel with buttons – living room and bedrooms · פנל קולי עם לחצנים – סלון וחדרי שינה
○	אגס קריאה ליד המיטה (בחדרי השינה) Call pear next to the bed (bedrooms) · אגס קריאה ליד המיטה
T	TI / TD · חבל משיכה ACE40320303W – אסלה ומקלחת, גובה 1.85 מ' Pull-cord – toilet and shower, h 1.85 m · חבל משיכה – אסלה ומקלחת, גובה 1.85 מ'
🟥	LP · מנורת מסדרון ACE41020309 – מעל דלת כל שירותים ציבוריים Corridor light – above each public toilet door · מנורת מסדרון – מעל דלת כל שירותים ציבוריים
LC	LC · LCom ACE71610003 – רכזת דירה (תקרה) LCom – apartment hub (ceiling) · LCom – רכזת דירה (תקרה)
GAB	ארון קומה 12U: 2 Buscomm ACE70810000 + מתג PoE ACEUCM6302 Floor rack: 2 Buscomm + PoE switch · ארון קומה: 2 Buscomm + מתג PoE

כמויות לקומה × 8 קומות

קוד	התקן	לקומה	8 קומות
TAB	טאבלט בכניסה	4	32
VOZ	פנל קולי עם לחצנים	10	80
TI/TD	חבל משיכה (אסלה + מקלחת)	17	136
LP	מנורת מסדרון (שירותים ציבוריים)	1	8
LC	LCom	5	40
BC	Buscomm	2	16
SW	מתג PoE	1	8

NOTES · הערות

1. בסיס: תוכנית אדריכלית L5 (קומה טיפוסית) – 8 קומות זהות: 4 דירות בקומה, 32 בסך הכול.
2. דירות x01 ו-x02: חדר שינה אחד, סלון עם מטבח ו-2 חדרי רחצה. דירות x03 ו-x04: 2 חדרי שינה ו-2 חדרי רחצה.
3. טאבלט בכניסה לכל דירה (iPad / אנדרואיד) לקריאה ולדיבור עם האחות.
4. פנל קולי עם לחצנים (ACE82182451) בסלון ובכל חדר שינה; בחדר השינה עם אגס ליד המיטה.
5. חבל משיכה (ACE40320303W) באסלה ובמקלחת בכל חדרי הרחצה, בגובה 1.85 מ'.
6. שירותים ציבוריים בכל קומה בחדר המשותף: חבל משיכה + מנורת מסדרון מעל הדלת. עם 2 בקרקע – 10 שירותים ציבוריים.
7. ארון קומה במסדרון השירות ליד המעליות (Tripp Lite 12U, כמו בתוכנית ה-IT).
8. מיקומים לפי סימוני הלקוח בתוכנית L2 (nt = פנל קולי, tab = טאבלט): ראו גיליון 03.

גובהי התקנה

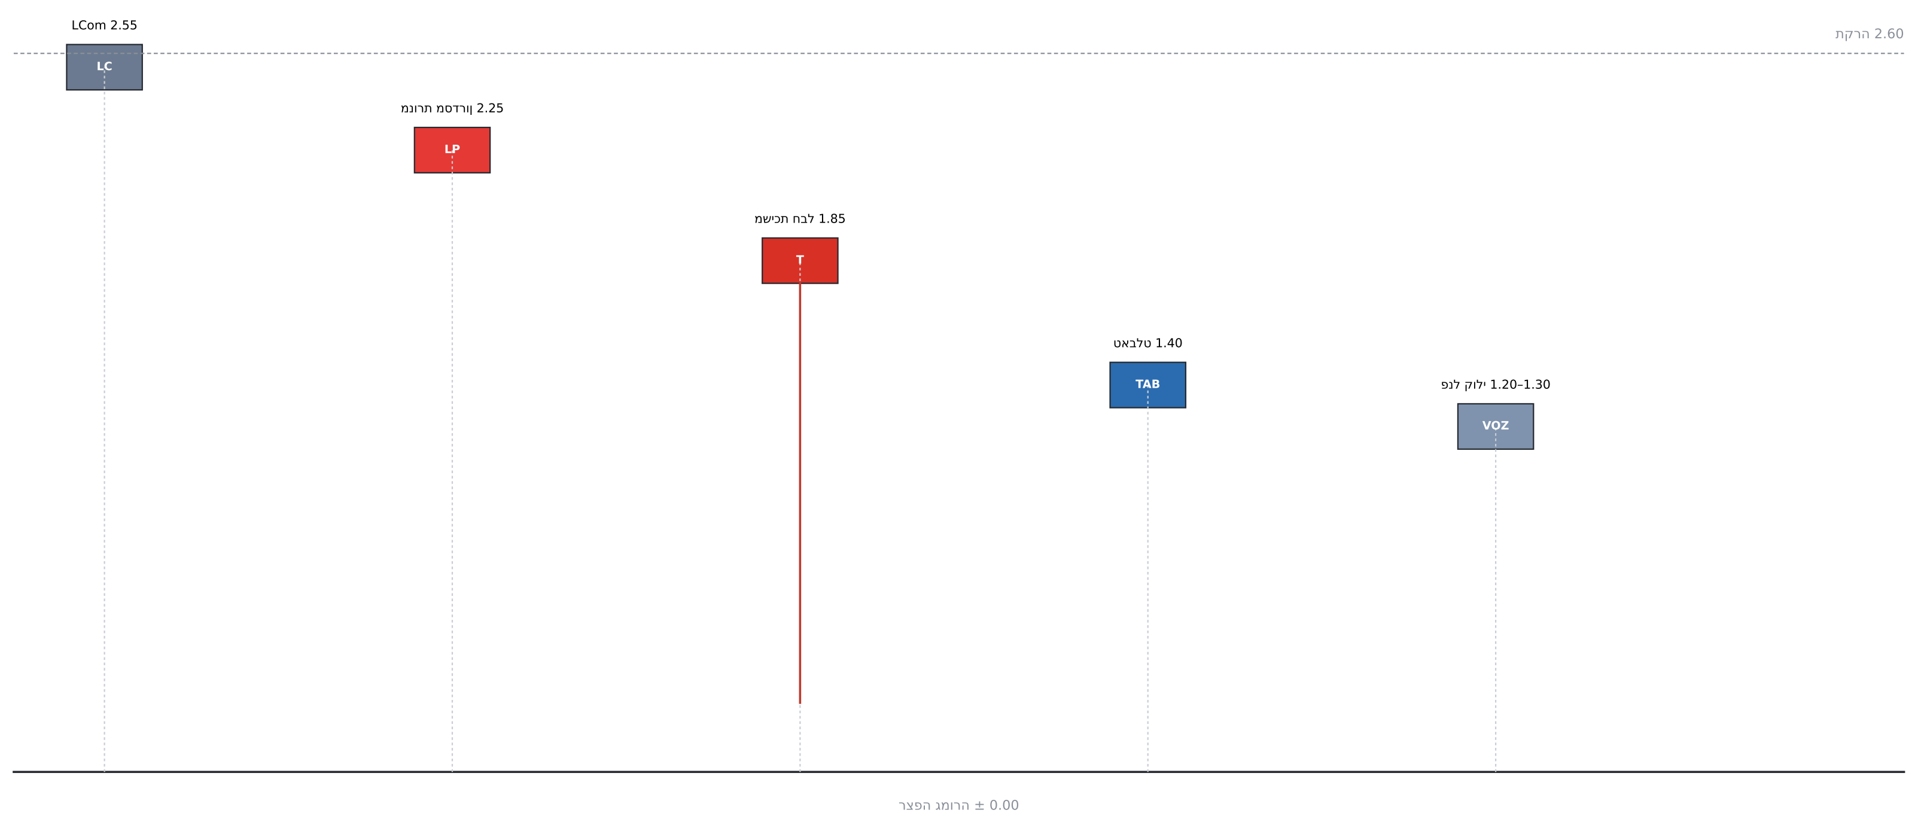

שירותים קריאת אחות

חבל משיכה

טבלט אנדרואיד קריאת אחות
Advantecnia
Llamada de enfermera

טאבלט בכניסה (iPad / אנדרואיד)

מנורה קריאת אחות

מנורת מסדרון

פנל קריאת אחות

פנל קולי עם לחצנים

מגדלי ים התיכון · דיור מוגן
32 דירות · 8 קומות + קרקע – קריאת אחות
מערכת: ACE BG · Advantecnia   הוכן ע"י: Telab International

קומה טיפוסית 1–8 · קריאת אחות

Typical floor F1–F8 · nurse call

SCALE · קנה מידה	DATE · תאריך	REV	גיליון
1:60	15/10/2026	B	01

בסיס: תוכנית האדריכל L5 (מסד עוז / Triplet) · מידות במטרים
פורמט A1 · מהדורה B – על התוכנית האמיתית

שירותים קריאת אחות

לבח תכישמ

דוק	**ACE40320303W**
םוקימ	םיירוביצה םיתורישה 10-בו הצחר רדח לכב תחלקמו הלסא
הבוג	**1.85 מ'**
תומכ	**138**

1

TV
Advantecnia
04:56 a. m.
Hospital
Llamada de enfermera
Salud y bienestar

הסינכב טלבאט (iPad / דיאורדנא)

דוק	**Advantecnia TV**
םוקימ	הריד לכ תלד דיל ,יבולב
הבוג	**1.40 מ'**
תומכ	**32**

2

מנורה קריאת אחות

וורדסמ תרונמ

דוק	**ACE41020309**
םוקימ	םיירוביצ םיתוריש לכ תלד לעמ
הבוג	**2.25 מ'**
תומכ	**10**

3

פנל קריאת אחות

םינצחל םע ילוק לנפ

דוק	**ACE82182451**
םוקימ	וולס וכל רדח הניש (רבחב הנישה םע סגא)
הבוג	**1.20–1.30 מ'**
תומכ	**80**

4

NOTES · תורעה

/ ACE BG 1. לש סוחיי תונומת
Advantecnia, םע תרתוכה והלש.

2. תכישמ לבח: לבח אודמ םע תידי,
הפצרהמ םג שיגנ.

3. הסינכב טלבאטה ארוק רבדמו
םע תוחאה.

4. תרונמ וורדסמה תקלדנ םיארוקשכ
םהשירותיםה םיירוביצה.

5. לנפב וצחל הארק אודמ,
וצחל לוחכ (לאמש) קוריו (וימי)
רובידל לוקמרו.

LCom :6. הריד לכב ףסונב
ACE71610003 הרקתב.

7. בקרקע: ופלט ינחלוש דיאורדנא
ACE52190200 תדמעב תוחאה.

וגומ רויד · וכיתה םי ילדגמ

קראית תוחא – קרקע + 8 תומוק · 32 תוריד

תכרעמ: ACE BG · Advantecnia   Telab International :וכוה ע"י

תכרעמה דויצ

System devices

SCALE · הדימ הנק	DATE · ךיראת	REV	וויליג
S/E	**15/10/2026**	**B**	**02**

סיסב: תוכנית האדריכל L5 (זוג דסמ / Triplet) · םירטמב תודימ

טמרופ A1 · הרודהמ B – לע התוכנית תיתימאה

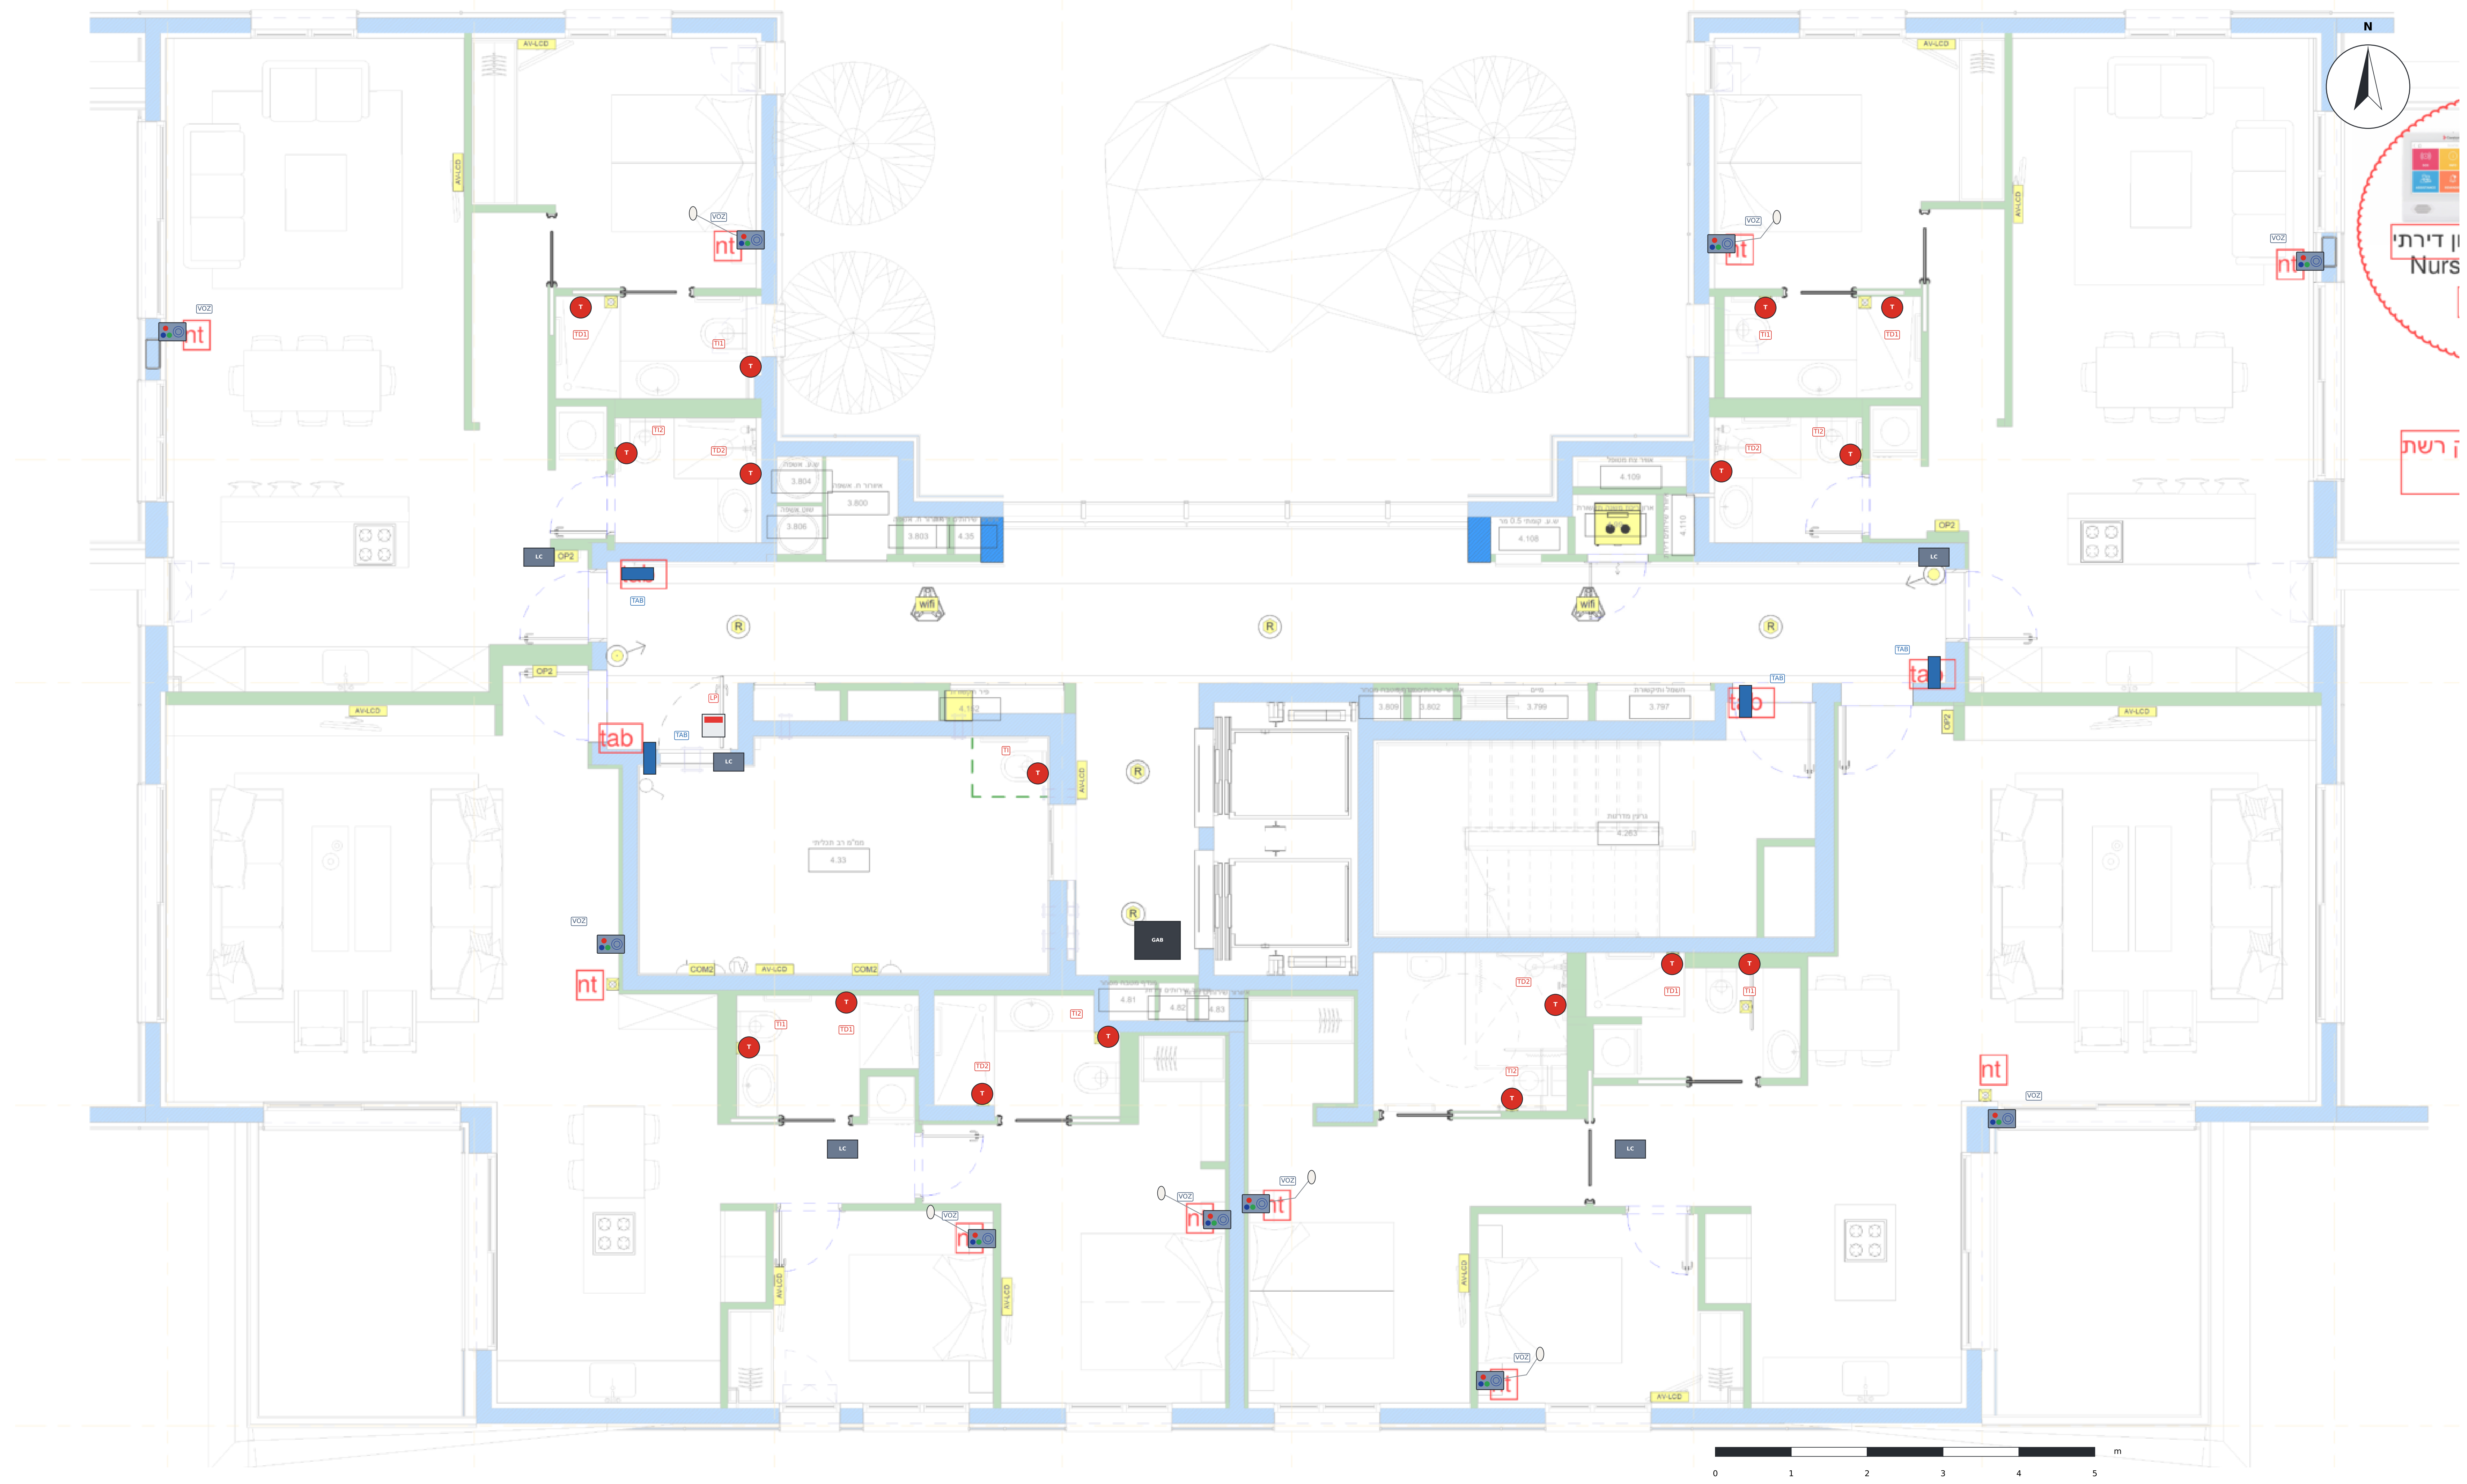

NOTES · תורעה

1. רקע: תינכות IT L2 לש חוקלה םע םיסומינים ולש םודאב:
«nt» = לנפ קולי ו-«tab» = טלבאט הסינככ.

2. לעמ, עבצב: הציוד הבהעה וז.
לכ לנפ וכל טלבאט םיאצמנ םוקמב שהלקוח םיס|ן.

L2 3. םירבועיה םיבוהצה ☒ ירדחב הרחצה תובכונית
הם םשיכות החבל (תחלקמו הלסא).

4. 4 םיטלבאטה ,יבולב ,דיל דלת לכ הריד,
.«tab» ומכ םינומיסי

5. תוינכותל L2 ו-L5 (העצההה סיסב) אותו מבנהה;
L5 8 איה הקומה תיסופיטה לקומות 1 דע.

DEVICES · EQUIPOS · דויצ

🟦	TAB · טלבאט הסינככ (iPad / דיאורדנא) – קריאה ודיבור, גובה 1.40 מ' Door tablet – call and voice · טלבאט הסינככ – קריאה ודיבור
▨	VOZ · פנל קולי עם לחצנים ACE82182451 – סלון וחדרי שינה, גובה 1.20–1.30 מ' Voice panel with buttons – living room and bedrooms · פנל קולי עם לחצנים – סלון וחדרי שינה
○	אגס קריאה ליד המיטה (בחדרי שינה) Call pear next to the bed (bedrooms) · אגס קריאה ליד המיטה
T	TI / TD · משיכת חבל ACE40320303W – אסלה ומקלחת, גובה 1.85 מ' Pull-cord – toilet and shower, h 1.85 m · משיכת חבל – אסלה ומקלחת, גובה 1.85 מ'
🟥	LP · מנורת מסדרון ACE41020309 – מעל דלת כל שירותים ציבוריים Corridor light – above each public toilet door · מנורת מסדרון – מעל דלת כל שירותים ציבוריים

פנל קריאת אחות

מינצחל םע ילוק לנפ

מנורה קריאת אחות

ןורדסמ תרונמ

טבלט אנדרואיד קריאת אחות

Advantecnia
Llamada de enfermera
Hospital
Salud y bienestar

(דיאורדנא / iPad) הסינככ טלבאט

שירותים קריאת אחות

לבח תכישמ

ןגומ רויד · ןוכיתה םי ילדגמ

תוריד 32 · תומוק 8 + עקרק – תוחא תאירק

ACE BG · Advantecnia :תכרעמ   Telab International :ןכוה ע"י

העצההו (תינכות L2) חוקלה ינומיס

Client marks (plan L2) and proposal

SCALE · הדימ הנק	DATE · ךיראת	REV	ןוילג
1:60	**15/10/2026**	**B**	**03**

סיסב: תינכות לכירדאה L5 (זוע דסמ / Triplet) · םירטמב תודימ

טמרופ A1 · הרודהמ B – לע התינכותה תיתימאה

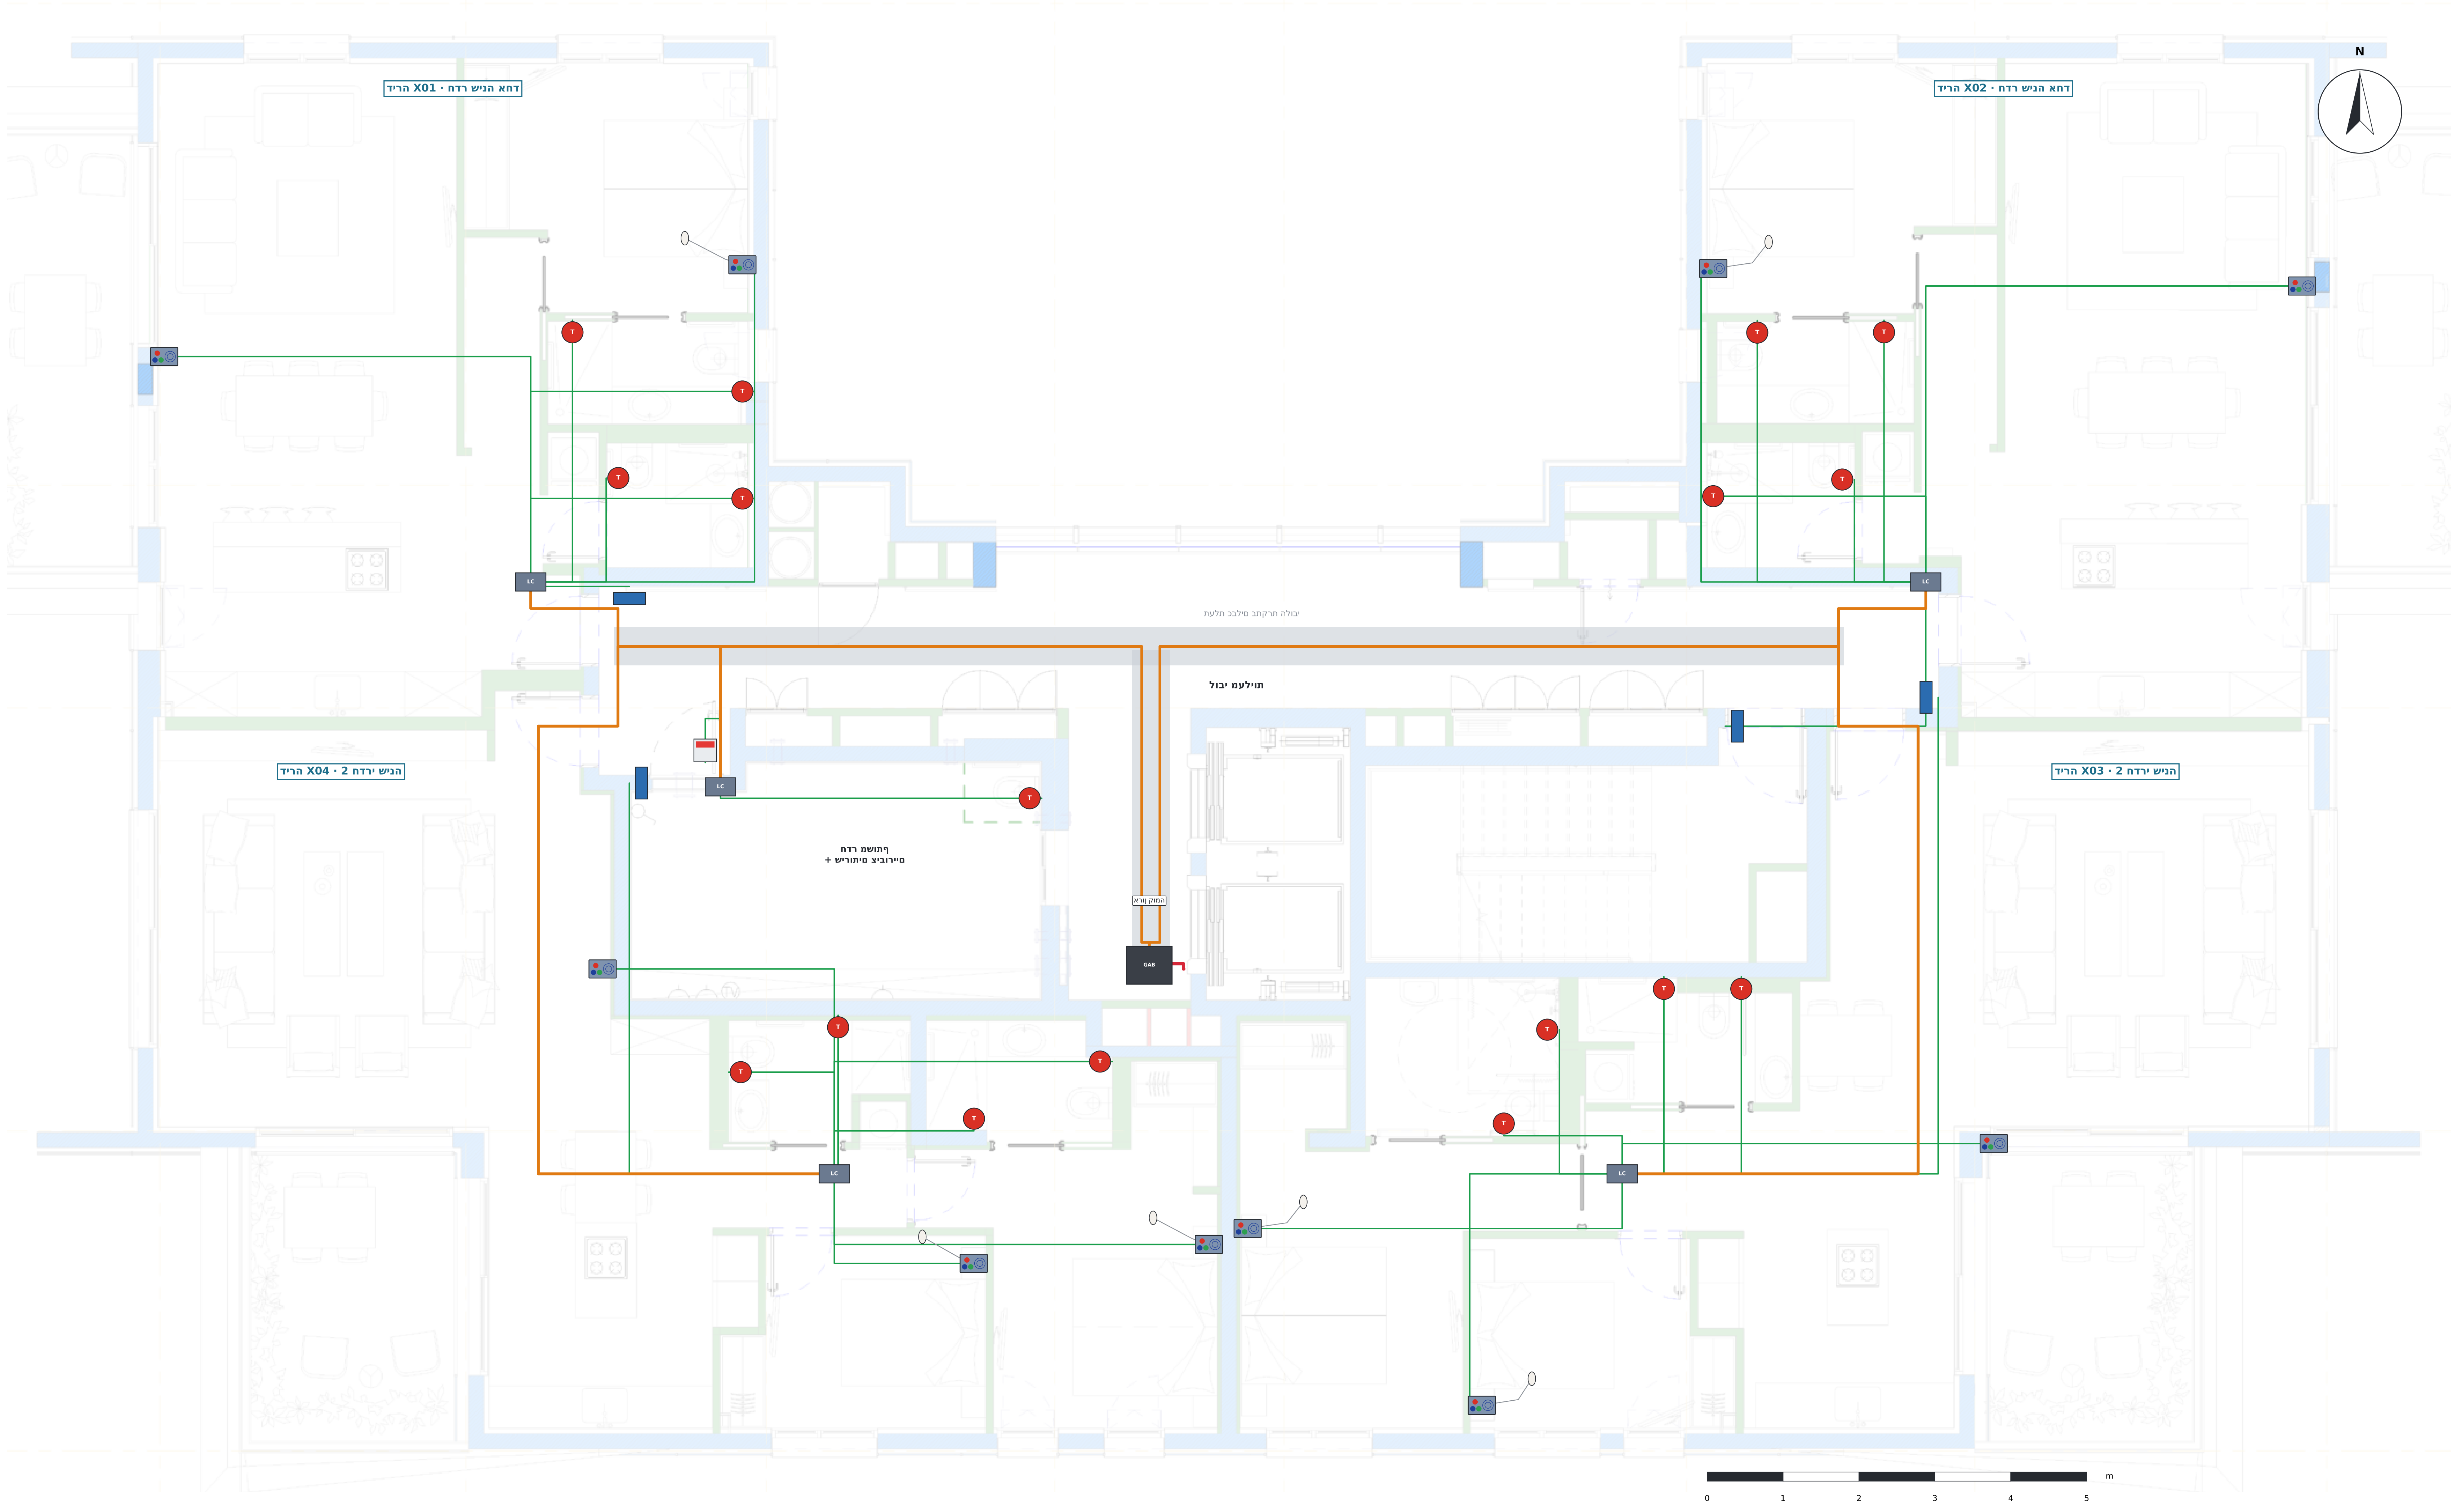

NOTES · הערות

1. בסיס: תוכנית אדריכלית L5 (קומה טיפוסית) – 8 קומות זהות: 4 דירות בקומה, 32 בסך הכול.

2. דירות x01 ו-x02: חדר שינה אחד, סלון עם מטבח ו-2 חדרי רחצה. דירות x03 ו-x04: 2 חדרי שינה ו-2 חדרי רחצה.

3. טאבלט בכניסה לכל דירה (iPad / אנדרואיד) לקריאה ולדיבור עם האחות.

4. פנל קולי עם לחצנים (ACE82182451) בסלון ובכל חדר שינה; בחדר השינה עם אגס ליד המיטה.

5. משיכות חבל (ACE40320303W) באסלה ובמקלחת בכל חדרי הרחצה, בגובה 1.85 מ'.

6. שירותים ציבוריים בכל קומה בחדר המשותף: משיכת חבל + מנורת מסדרון מעל הדלת. עם 2 בקרקע – 10 שירותים ציבוריים.

7. ארון קומה במסדרון השירות ליד המעליות (Tripp Lite 12U, כמו בתוכנית ה-IT).

8. מיקומים לפי סימוני הלקוח בתוכנית L2 (nt = פנל קולי, tab = טאבלט): ראו גיליון 03.

WIRING · CABLEADO · חיווט

🟩 Cat6 רדיאלי: כל התקן ← LCom של הדירה
Cat6 radial: each device → apartment LCom · Cat6 רדיאלי: כל התקן ← LCom של הדירה

🟧 Cat6 / Cat7 שרשרת: LCom ← LCom ← Buscomm בארון
Cat6 / Cat7 chain: LCom → LCom → Buscomm · Cat6 / Cat7 שרשרת: LCom ← LCom ← Buscomm

🟥 Cat6A / Cat7 רשת: Buscomm ← מתג ← עמוד ← שרת קרקע
Cat6A / Cat7 network: Buscomm → switch → riser → GF server · Cat6A / Cat7 רשת: Buscomm ← מתג ← עמוד ← שרת

אורכים בקומה טיפוסית (ללא רזרבה)

🟩	Cat6 רדיאלי בתוך הדירות	**183 m**
🟧	Cat6 / Cat7 שרשרת LCom ← Buscomm	**82 m**
🟥	Cat6A / Cat7 ארון ועמוד	**4 m**

NOTES · הערות

1. כל התקן מחובר רדיאלית (Cat6) ל-LCom של הדירה, בתקרת המבואה.

2. יחידות ה-LCom משורשרות לאורך תעלת הלובי עד ארון הקומה:
x01 ← x04 ← חדר משותף ← Buscomm 1 · x02 ← x03 ← Buscomm 2.

3. מתג ה-PoE של הקומה מחובר דרך עמוד Cat6A / Cat7 עד
השרת בקומת הקרקע.

4. הכול PoE: אין צורך ב-230V להתקני הדירות.

מגדלי ים התיכון · דיור מוגן
32 דירות · 8 קומות + קרקע – קריאת אחות
הוכן ע"י: Telab International   מערכת: ACE BG · Advantecnia

קומה טיפוסית 1–8 · חיווט

Typical floor F1–F8 · wiring

SCALE · קנה מידה
1:60

DATE · תאריך
15/10/2026

REV
B

גיליון
04

בסיס: תוכנית האדריכל L5 (מסד עוז / Triplet) · מידות במטרים
פורמט A1 · מהדורה B – על התוכנית האמיתית

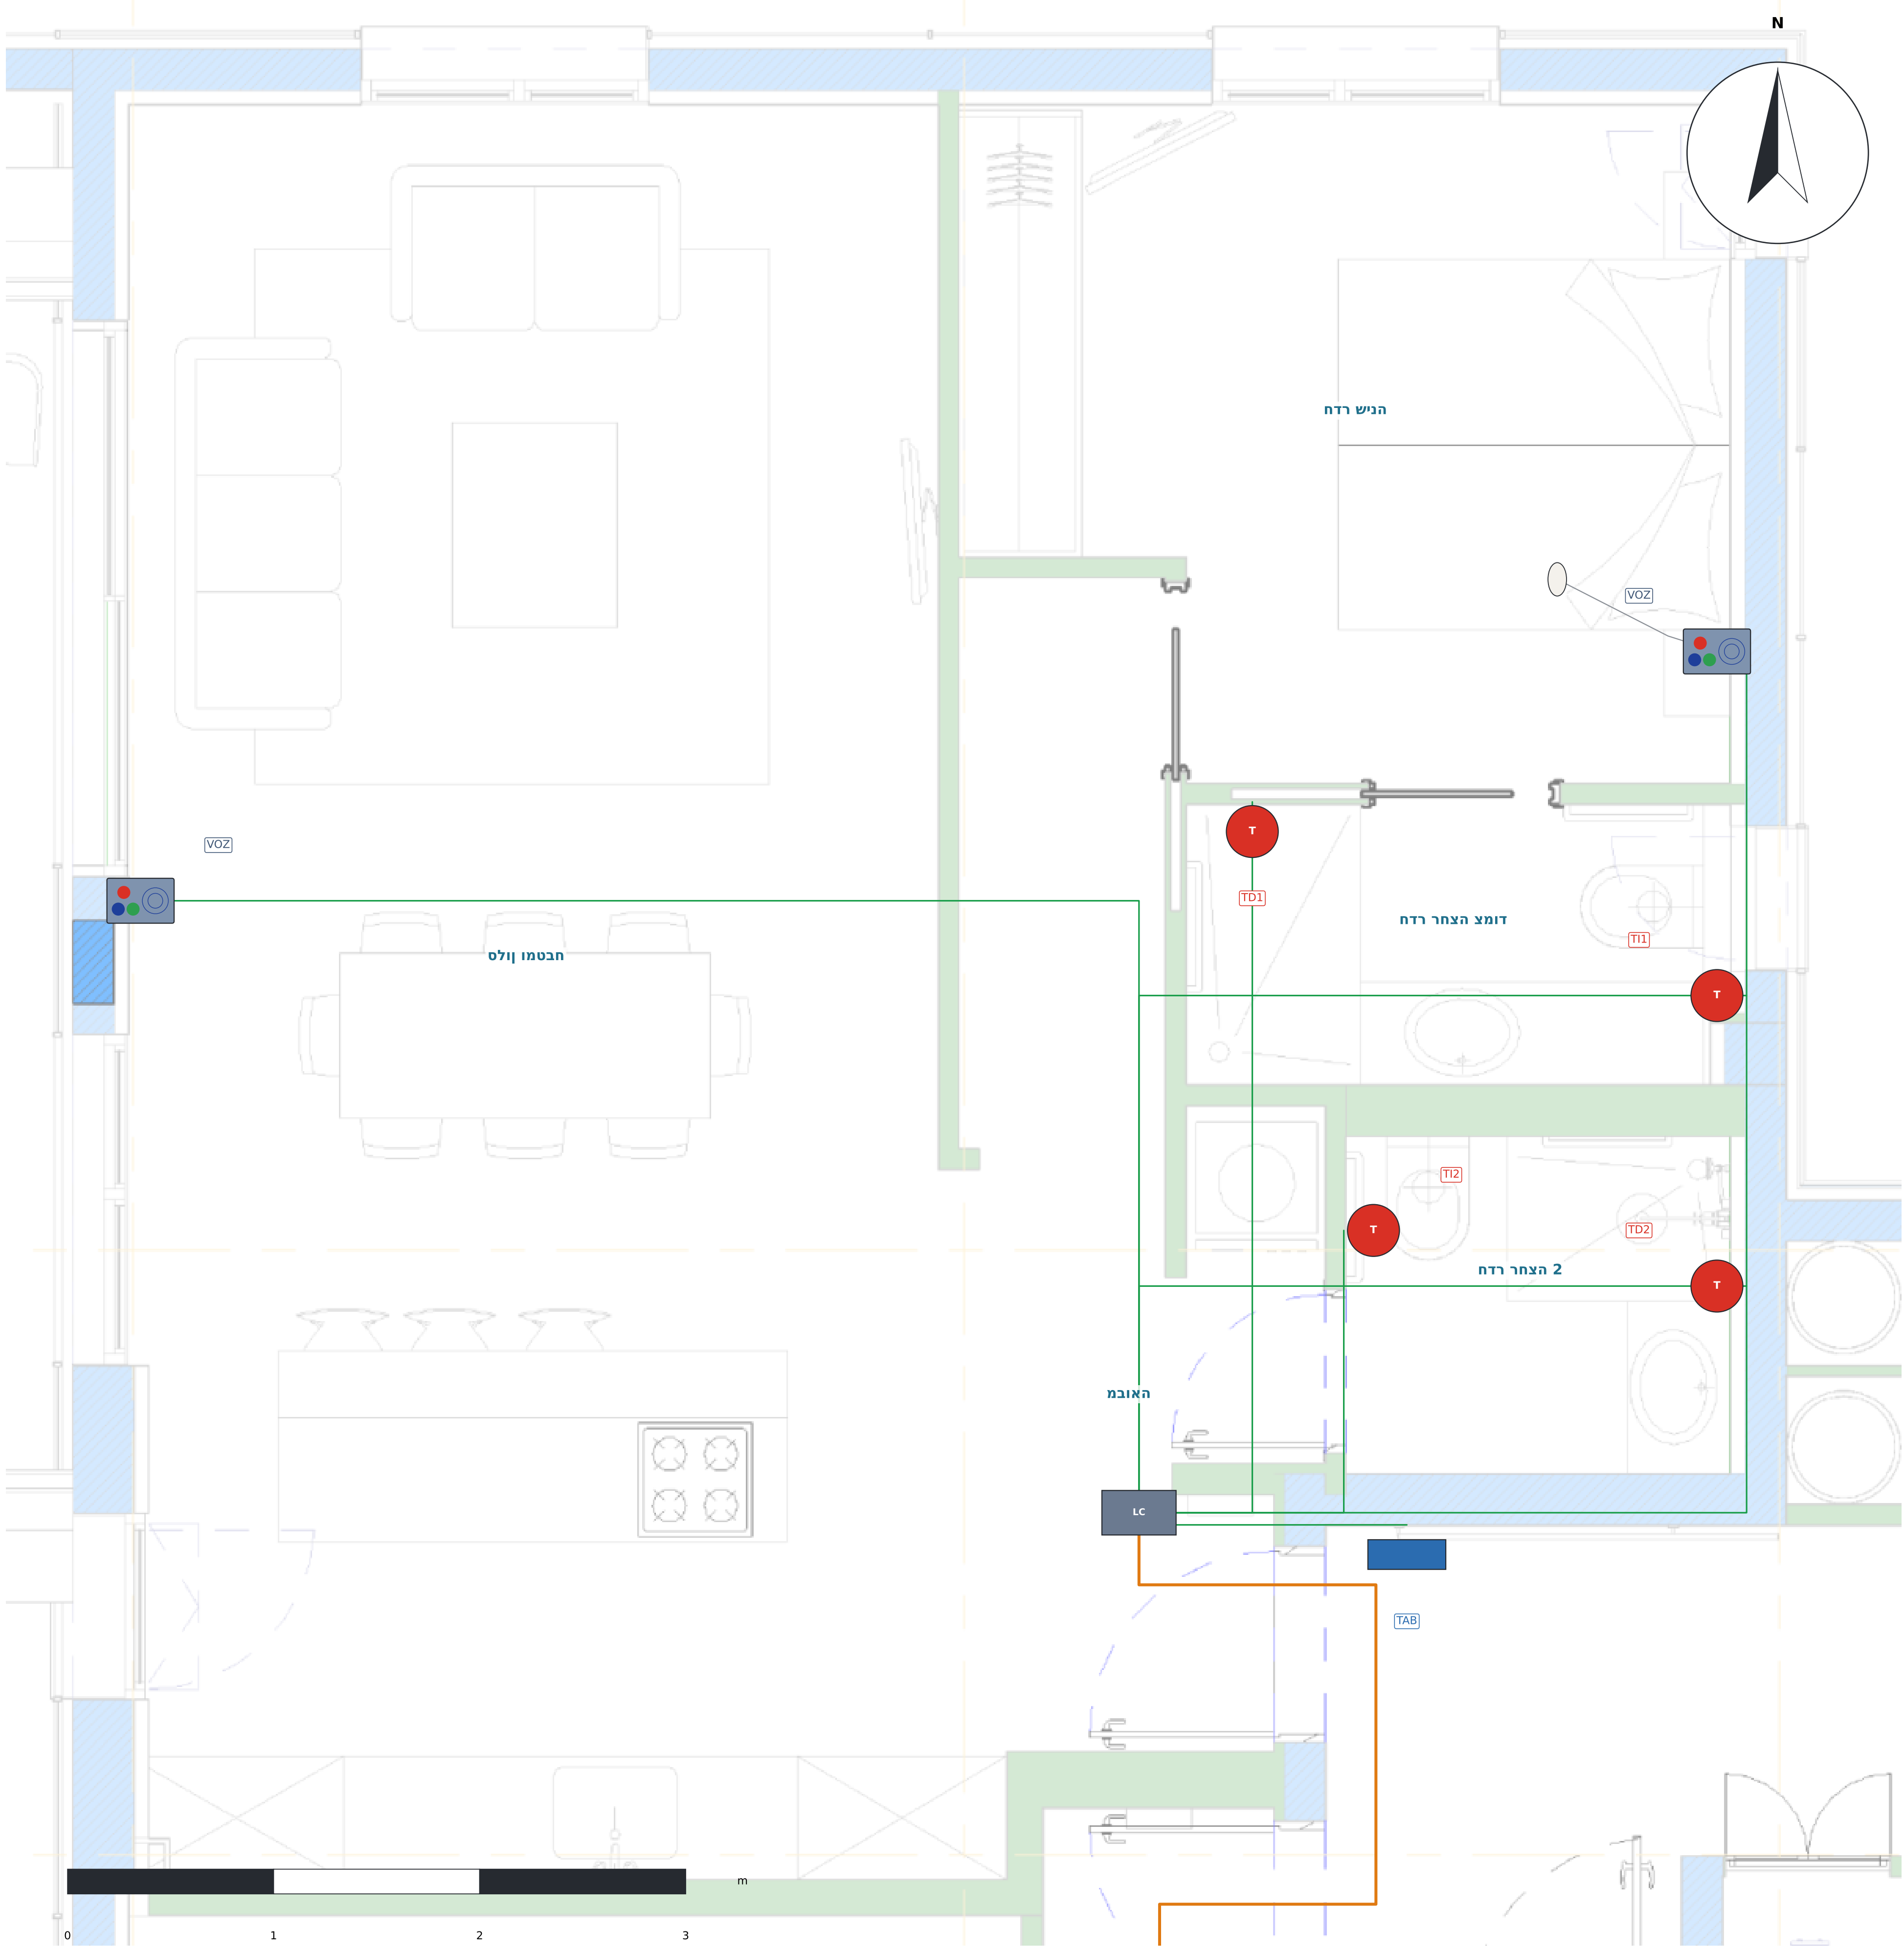
N
הניש רדח
VOZ
VOZ
TD1
TI1
דומצ הצחר רדח
חבטמו ןולס
TI2
TD2
2 הצחר רדח
האובמ
LC
TAB
T
0
1
2
3
m

הרידה דויצ

ID	הקתה	רדח	הבוג
TAB	הסינכב טלבאט	האובמ	1.40 מ'
VOZ-S	סינצחל םע ילוק לנפ	חבטמו ןולס	1,30 m
VOZ-D	סגא + סינצחל םע ילוק לנפ	הניש רדח	1,20 m
TI1	לבח תכישמ	דומצ הצחר רדח	1.85 מ'
TD1	לבח תכישמ	דומצ הצחר רדח	1.85 מ'
TI2	לבח תכישמ	2 הצחר רדח	1.85 מ'
TD2	לבח תכישמ	2 הצחר רדח	1.85 מ'
LCOM	LCom ACE71610003	האובמ	2,55 m

SYMBOLS · SÍMBOLOS · םילמס

🟦	TAB · הסינכב טלבאט (iPad / דיאורדנא) – רובידו האירק ,הבוג 1.40 מ' Door tablet – call and voice · הסינכב טלבאט – רובידו האירק
VOZ	VOZ · סינצחל םע ילוק לנפ ACE82182451 – ןולס ירדחו הניש ,הבוג 1.20–1.30 מ' Voice panel with buttons – living room and bedrooms · סינצחל םע ילוק לנפ – ןולס ירדחו הניש
○	סגא האירק דיל הטימה (הנישה ירדחב) Call pear next to the bed (bedrooms) · סגא האירק דיל הטימה
T	TI / TD · לבח תכישמ ACE40320303W – הלסא תחלקמו ,הבוג 1.85 מ' Pull-cord – toilet and shower, h 1.85 m · לבח תכישמ – הלסא תחלקמו ,הבוג 1.85 מ'
🟥	LP · ןורדסמ תרונמ ACE41020309 – םעל תלד לכ םיתוריש םייבוביצ Corridor light – above each public toilet door · ןורדסמ תרונמ – םעל תלד לכ םיתוריש םייבוביצ
LC	LC · LCom ACE71610003 – הרידה זכרמ (הרקת) LCom – apartment hub (ceiling) · LCom – הרידה זכרמ (הרקת)

NOTES · תורעה

1. הריד x02 איה תנומת יאר לש x01 (דויצ ותוא).
2. טלבאט יבולב, דיל תלד הסינכה (ןומיס «tab» לש חוקלה).
3. לנפ ילוק ןולסב רדחבו הנישה (םע סגא דיל הטימה).
4. 2 ירדח הצחר: תכישמ לבח הלסאב תחלקמבו לכב דחא (4 תוכישמ לבח).
5. לוכה רבוחמ תילאידר ב-Cat6 ל-LCom האובמב.

שירותים קריאת אחות

לבח תכישמ

טבלט אנדרואיד קריאת אחות
Advantecnia
Llamada de enfermera
Hospital
Salud y bienestar

הסינכב טלבאט (iPad / דיאורדנא)

מנורה קריאת אחות

ןורדסמ תרונמ

פנל קריאת אחות

סינצחל םע ילוק לנפ

ןגומ רויד · ןוכיתה םי ילדגמ
תוריד 32 · תומוק 8 + עקרק – תוחא תאירק
Telab International :ןכוה ע"י   ACE BG · Advantecnia :תכרעמ

(x01 / x02) דחא הניש רדח תריד
1-bedroom apartment (x01 / x02)

SCALE · הדימ הנק: **1:30**
DATE · ךיראת: **15/10/2026**
REV: **B**
ןוילג: **05**

סיסב: לכירדאה תינכות L5 (זוע דסמ / Triplet) · םירטמב תודימ
טמרופ A1 · הרודהמ B – לע התינכות תיתימאה

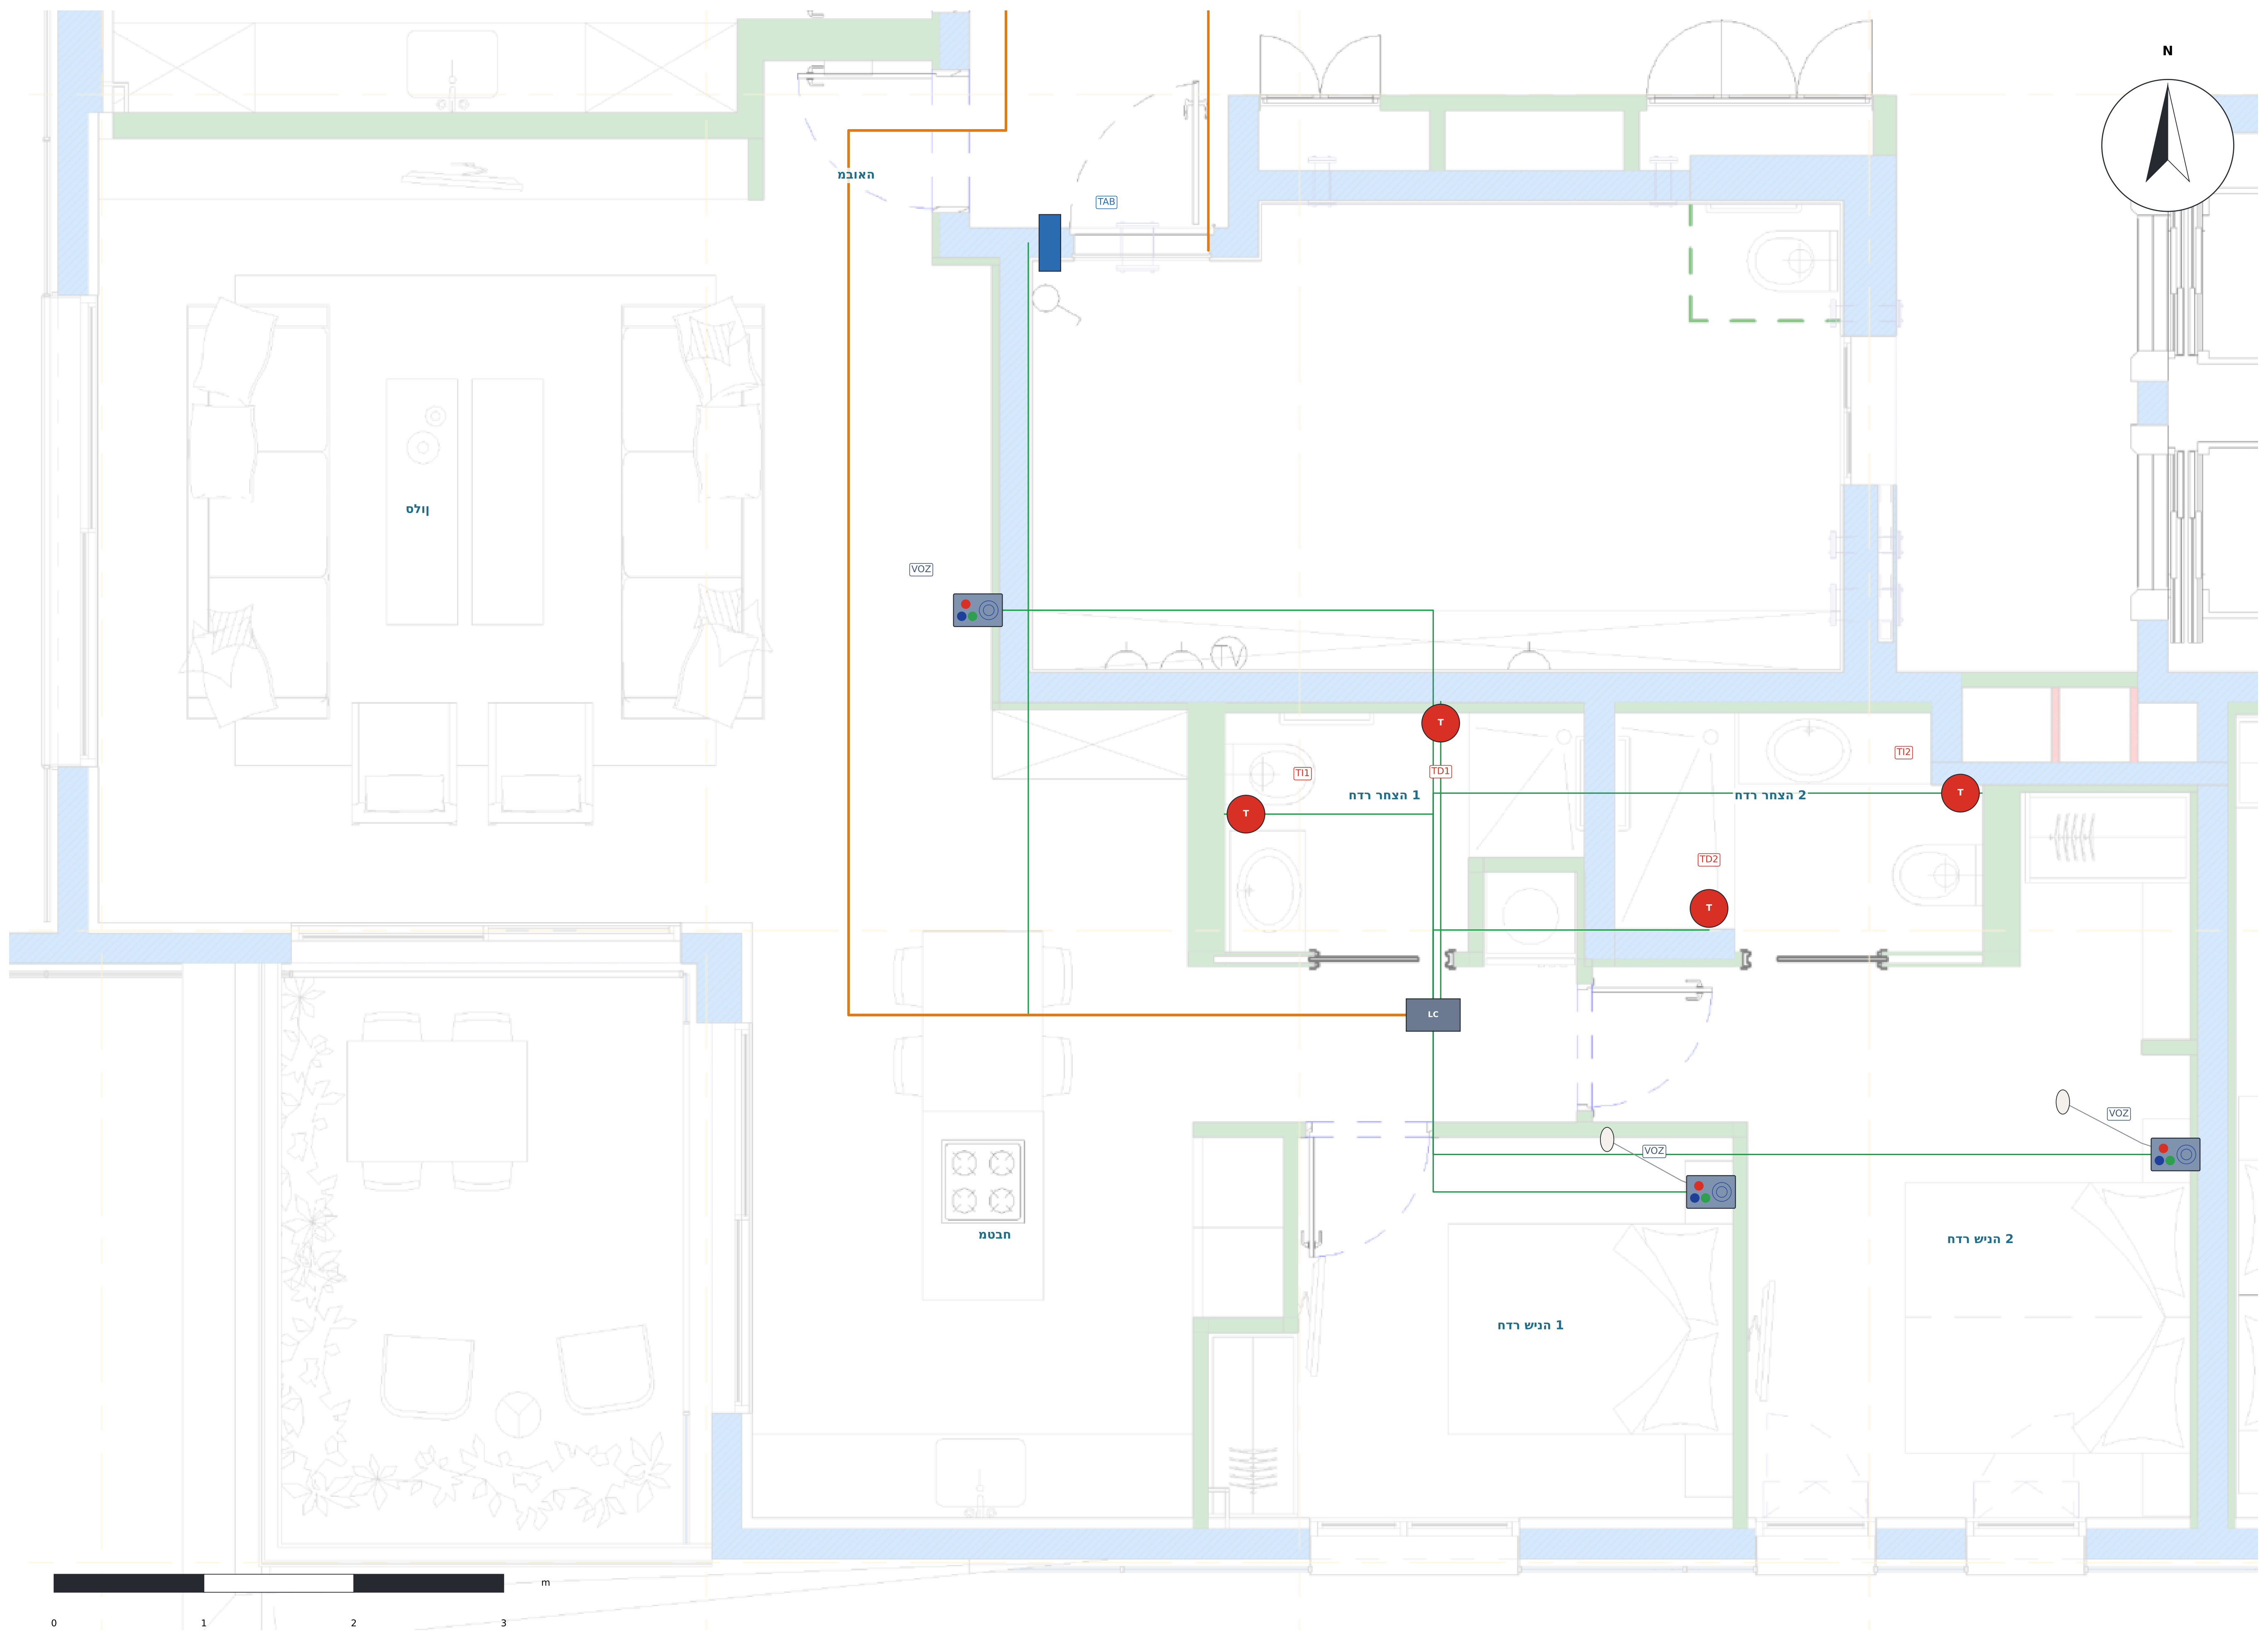
N
האובמ
TAB
ןולס
VOZ
הצחר ירדח 1
הצחר ירדח 2
TI1
TD1
TI2
TD2
T
LC
חבטמ
הניש רדח 1
הניש רדח 2
0
1
2
3
m

הרידה דויצ

ID	ןקתה	רדח	הבוג
TAB	הסינכב טלבאט	האובמ	1.40 מ'
VOZ-S	סינצחל םע ילוק לנפ	ןולס	1,30 m
VOZ-D1	סגא + סינצחל םע ילוק לנפ	הניש רדח 1	1,20 m
VOZ-D2	סגא + סינצחל םע ילוק לנפ	הניש רדח 2	1,20 m
TI1	לבח תכישמ	הצחר רדח 1	1.85 מ'
TD1	לבח תכישמ	הצחר רדח 1	1.85 מ'
TI2	לבח תכישמ	הצחר רדח 2	1.85 מ'
TD2	לבח תכישמ	הצחר רדח 2	1.85 מ'
LCOM	LCom ACE71610003	האובמ	2,55 m

SYMBOLS · SÍMBOLOS · םילמס

🟦	TAB · הסינכב טלבאט (iPad / דיאורדנא) – הקירא רובידו, הבוג 1.40 מ' Door tablet – call and voice · הסינכב טלבאט – הקירא רובידו
VOZ	VOZ · לנפ ילוק םע לחצנים ACE82182451 – ןולס ירדחו הניש, הבוג 1.20–1.30 מ' Voice panel with buttons – living room and bedrooms · לנפ ילוק םע םינצחל – ןולס ירדחו הניש
⬯	סגא הקירא דיל הטימה (ירדחב הנישה) Call pear next to the bed (bedrooms) · סגא הקירא דיל הטימה
T	TI / TD · לבח תכישמ ACE40320303W – אסלה ומקלחת, הבוג 1.85 מ' Pull-cord – toilet and shower, h 1.85 m · לבח תכישמ – אסלה ומקלחת, הבוג 1.85 מ'
🟥	LP · הנורת םסדרוןו ACE41020309 – לעמ דלת לכ םיתורש םייבוריצ Corridor light – above each public toilet door · הנורת םסדרוןו – לעמ דלת לכ םיתורש םייבוריצ
LC	LC · LCom ACE71610003 – זכרמ הרידה (הרקת) LCom – apartment hub (ceiling) · LCom – זכרמ הרידה (הרקת)

NOTES · תורעה

1. הרידב x03 דויצ ותוא (ירדח הצחרה הפריסב הנוש).
2. טלבאט יבולב, דיל תלד הסינכה (ןומיס «tab» לש הלקוח).
3. לנפ ילוק ןולסב ינשבו ירדח הנישה (םע סגא דיל הטימה).
4. 2 ירדח הצחר: תכישמ לבח הלסאב ובמקלחת לכב דחא (4 תוכישמ לבח).
5. לוכה רבוחמ תילאידר ב-Cat6 ל-LCom ןודסמב ירדח הנישה.

פנל קריאת אחות

סינצחל םע ילוק לנפ

מנורה קריאת אחות

ןודסמ תרונמ

טבלט אנדרואיד קריאת אחות
Advantecnia
Llamada de enfermera
Hospital
Salud y bienestar

הסינכב טלבאט (iPad / דיאורדנא)

שירותים קריאת אחות

לבח תכישמ

ןגומ רויד · ןוכיתה םי ילדגמ

תוריד 32 · תומוק 8 + עקרק – תוחא תאירק

Telab International :הוכןן ע"י   ACE BG · Advantecnia :תכרעמ

(x04 / x03) הניש ירדח ינש תריד

2-bedroom apartment (x04 / x03)

SCALE · הדימ הנק	DATE · ךיראת	REV	ןוילג
1:35	15/10/2026	B	06

סיסב: לכירדאה תינכות L5 (זוע דסמ / Triplet) · םירטמב תודימ

טמרופ A1 · הרודהמ B – לע תינכותה תיתימאה

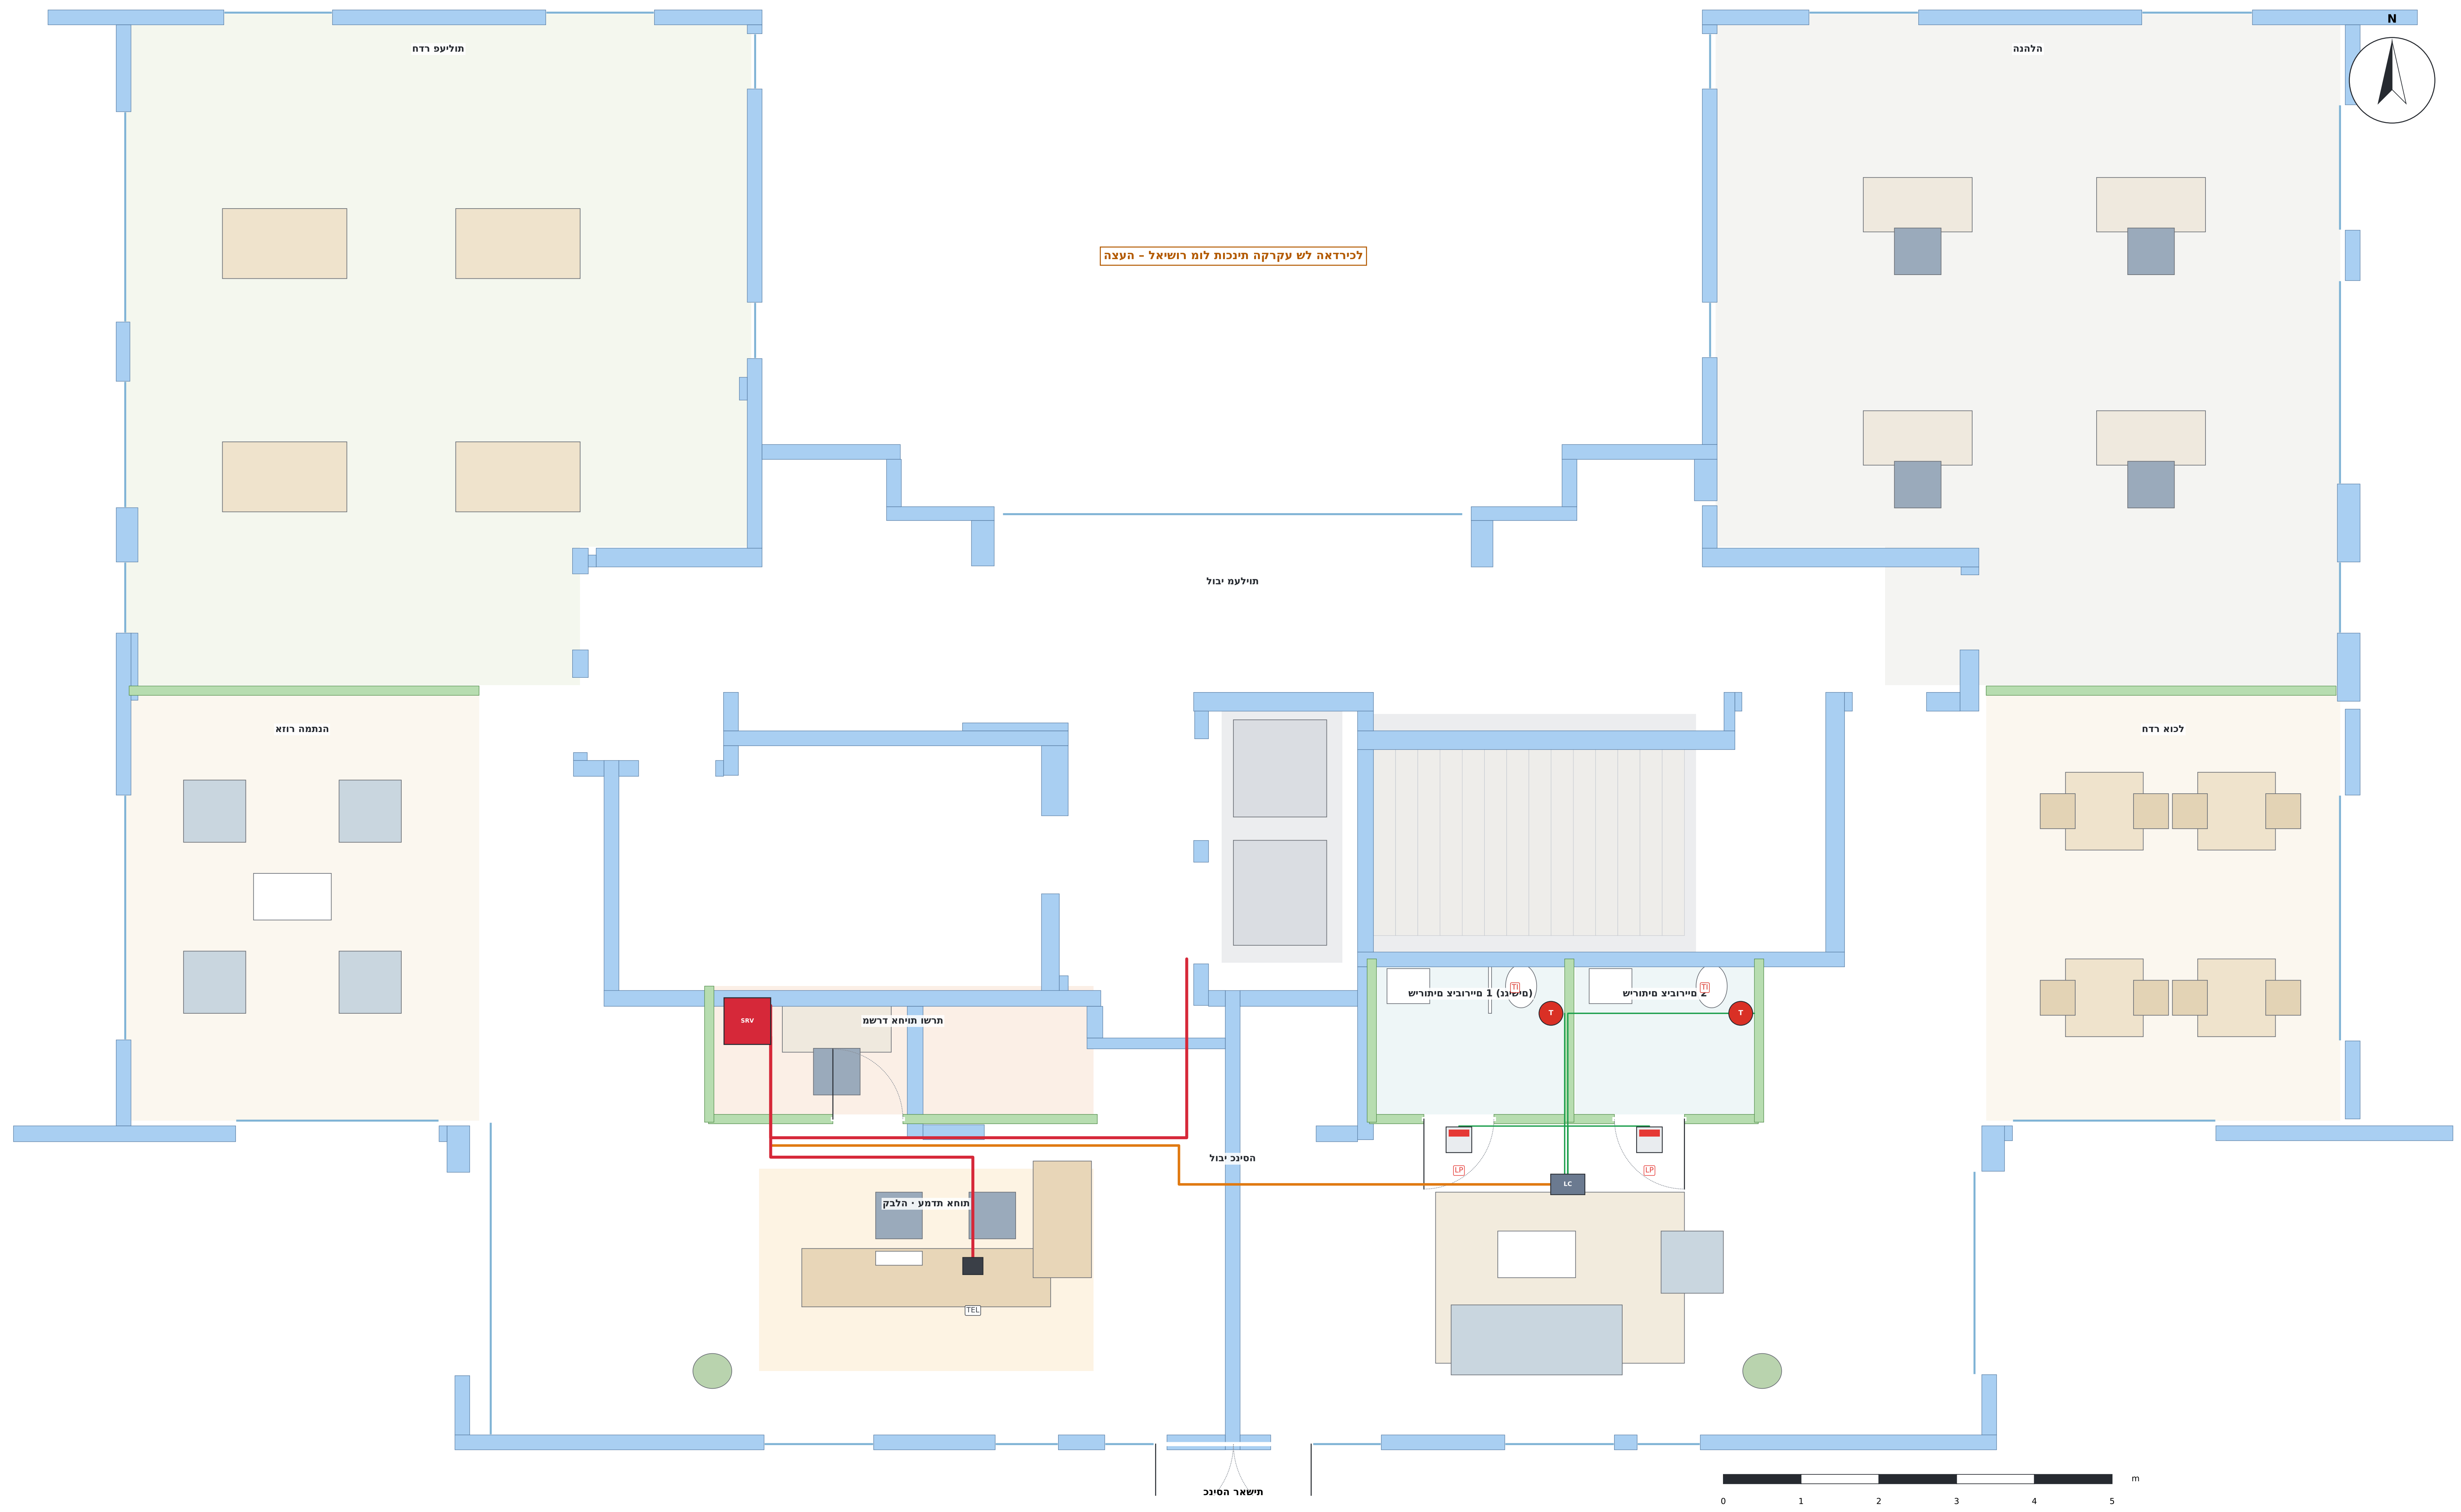
תוליעפ רדח
הלהנה
N
לכירדאה לש עקרקה תינכות לומ רושיאל – העצה
תוילעמ יבול
הנתמה רוזא
לכוא רדח
SRV
תרשו תויחא דרשמ
סיוריבצ םיתוריש 1 (םישגנ)
2 םיירוביצ םיתוריש
TI
T
LP
LC
הסינכ יבול
קבלה · תדמע תוחא
TEL
תישאר הסינכ
0
1
2
3
4
5
m

פרט · קבלה ועמדת אחות (1:40)

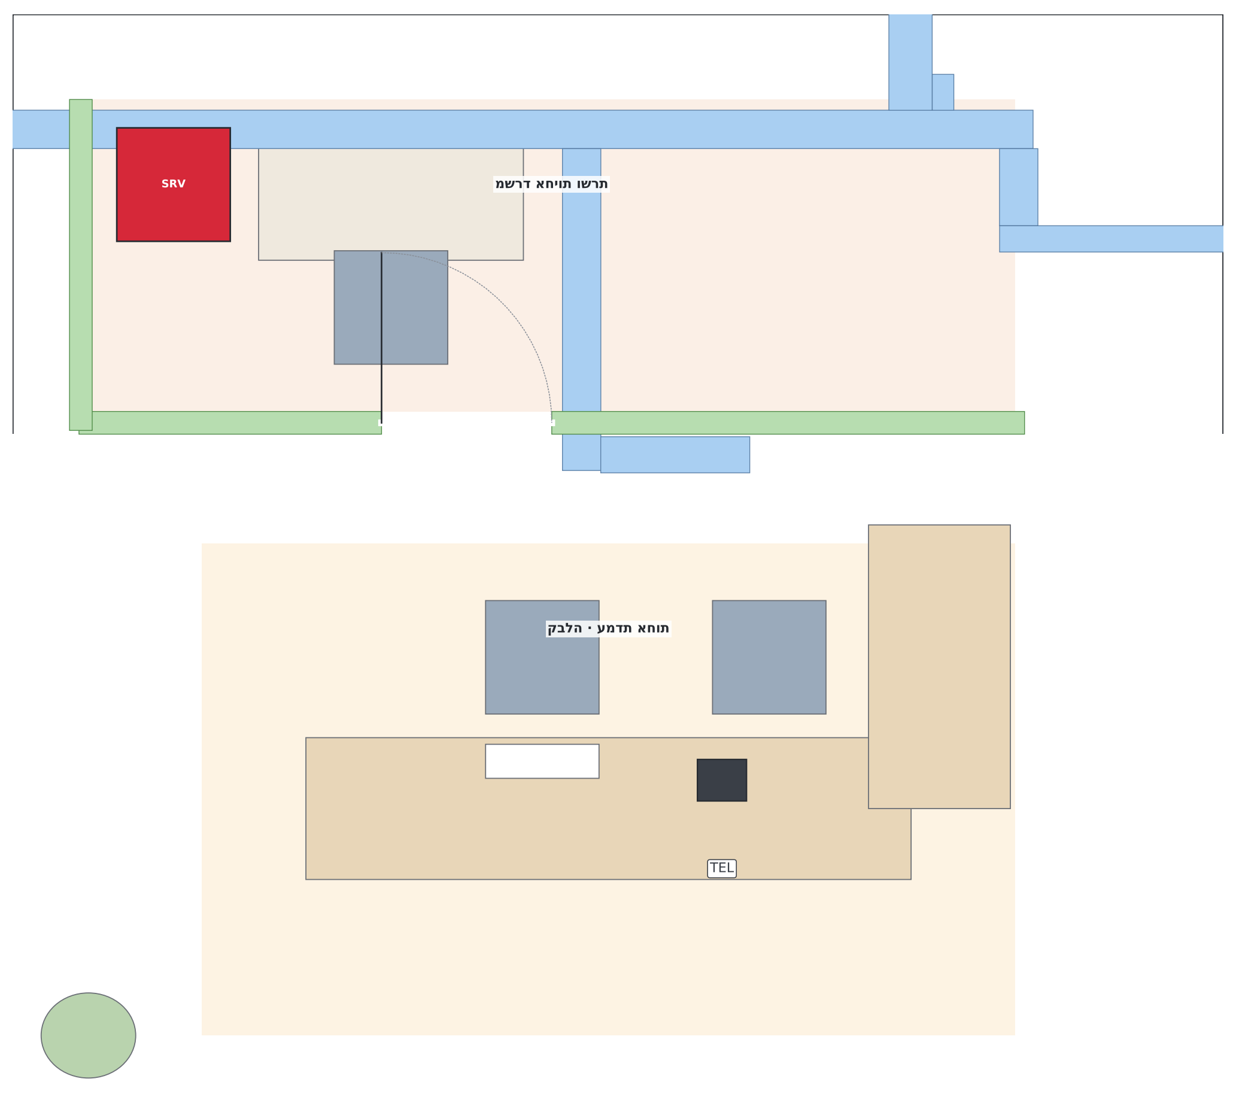
SRV
משרד אחיות ושרת
קבלה · עמדת אחות
TEL

NOTES · הערות

1. עמדת האחות בקבלה, מול הכניסה והמעליות.

ACE52190200 2. על העמדה: טלפון שולחני אנדרואיד (מקבל קריאות ווידאו).

3. מאחורי העמדה: משרד האחיות עם ארון השרת: שרת ACE51010103, מתג PoE ACEUCM6302 ו-Buscomm של הקרקע.

4. 2 שירותים ציבוריים בקרקע: משיכת חבל ליד האסלה ומנורת מסדרון מעל כל דלת.

5. עמוד מ-8 קומות יורד בגרעין עד הארון הראשי.

6. פריסת קרקע מוצעת: כשתתגבש התוכנית של האדריכל.

SYMBOLS · SÍMBOLOS · סמלים

T — TI / TD · משיכת חבל ACE40320303W – אסלה ומקלחת, גובה 1.85 מ'
Pull-cord – toilet and shower, h 1.85 m · משיכת חבל – אסלה ומקלחת, גובה 1.85 מ'

LC — LC · LCom ACE71610003 – מרכז דירה (תקרה)
LCom – apartment hub (ceiling) · LCom – מרכז דירה (תקרה)

SRV — SRV · ארון קרקע: שרת ACE51010103 + מתג + Buscomm
GF rack: server + switch + Buscomm · ארון קרקע: שרת + מתג + Buscomm

🟥 — LP · מנורת מסדרון ACE41020309 – מעל דלת כל שירותים ציבוריים
Corridor light – above each public toilet door · מנורת מסדרון – מעל דלת כל שירותים ציבוריים

TEL — TEL · טלפון שולחני אנדרואיד ACE52190200
Android desk phone · טלפון שולחני אנדרואיד

מגדלי ים התיכון · דיור מוגן
קריאת אחות – קרקע + 8 קומות · 32 דירות
Telab International :לקוח ע"י   ACE BG · Advantecnia :מערכת

קומת קרקע · לובי ועמדת אחות

Ground floor · lobby and nurse desk

SCALE · קנה מידה	DATE · תאריך	REV	גיליון
1:60	15/10/2026	B	07

בסיס: תוכנית האדריכל L5 (מסד עוז / Triplet) · מידות במטרים
פורמט A1 · מהדורה B – על התוכנית האמיתית

א · בניין קרקע + 8 קומות

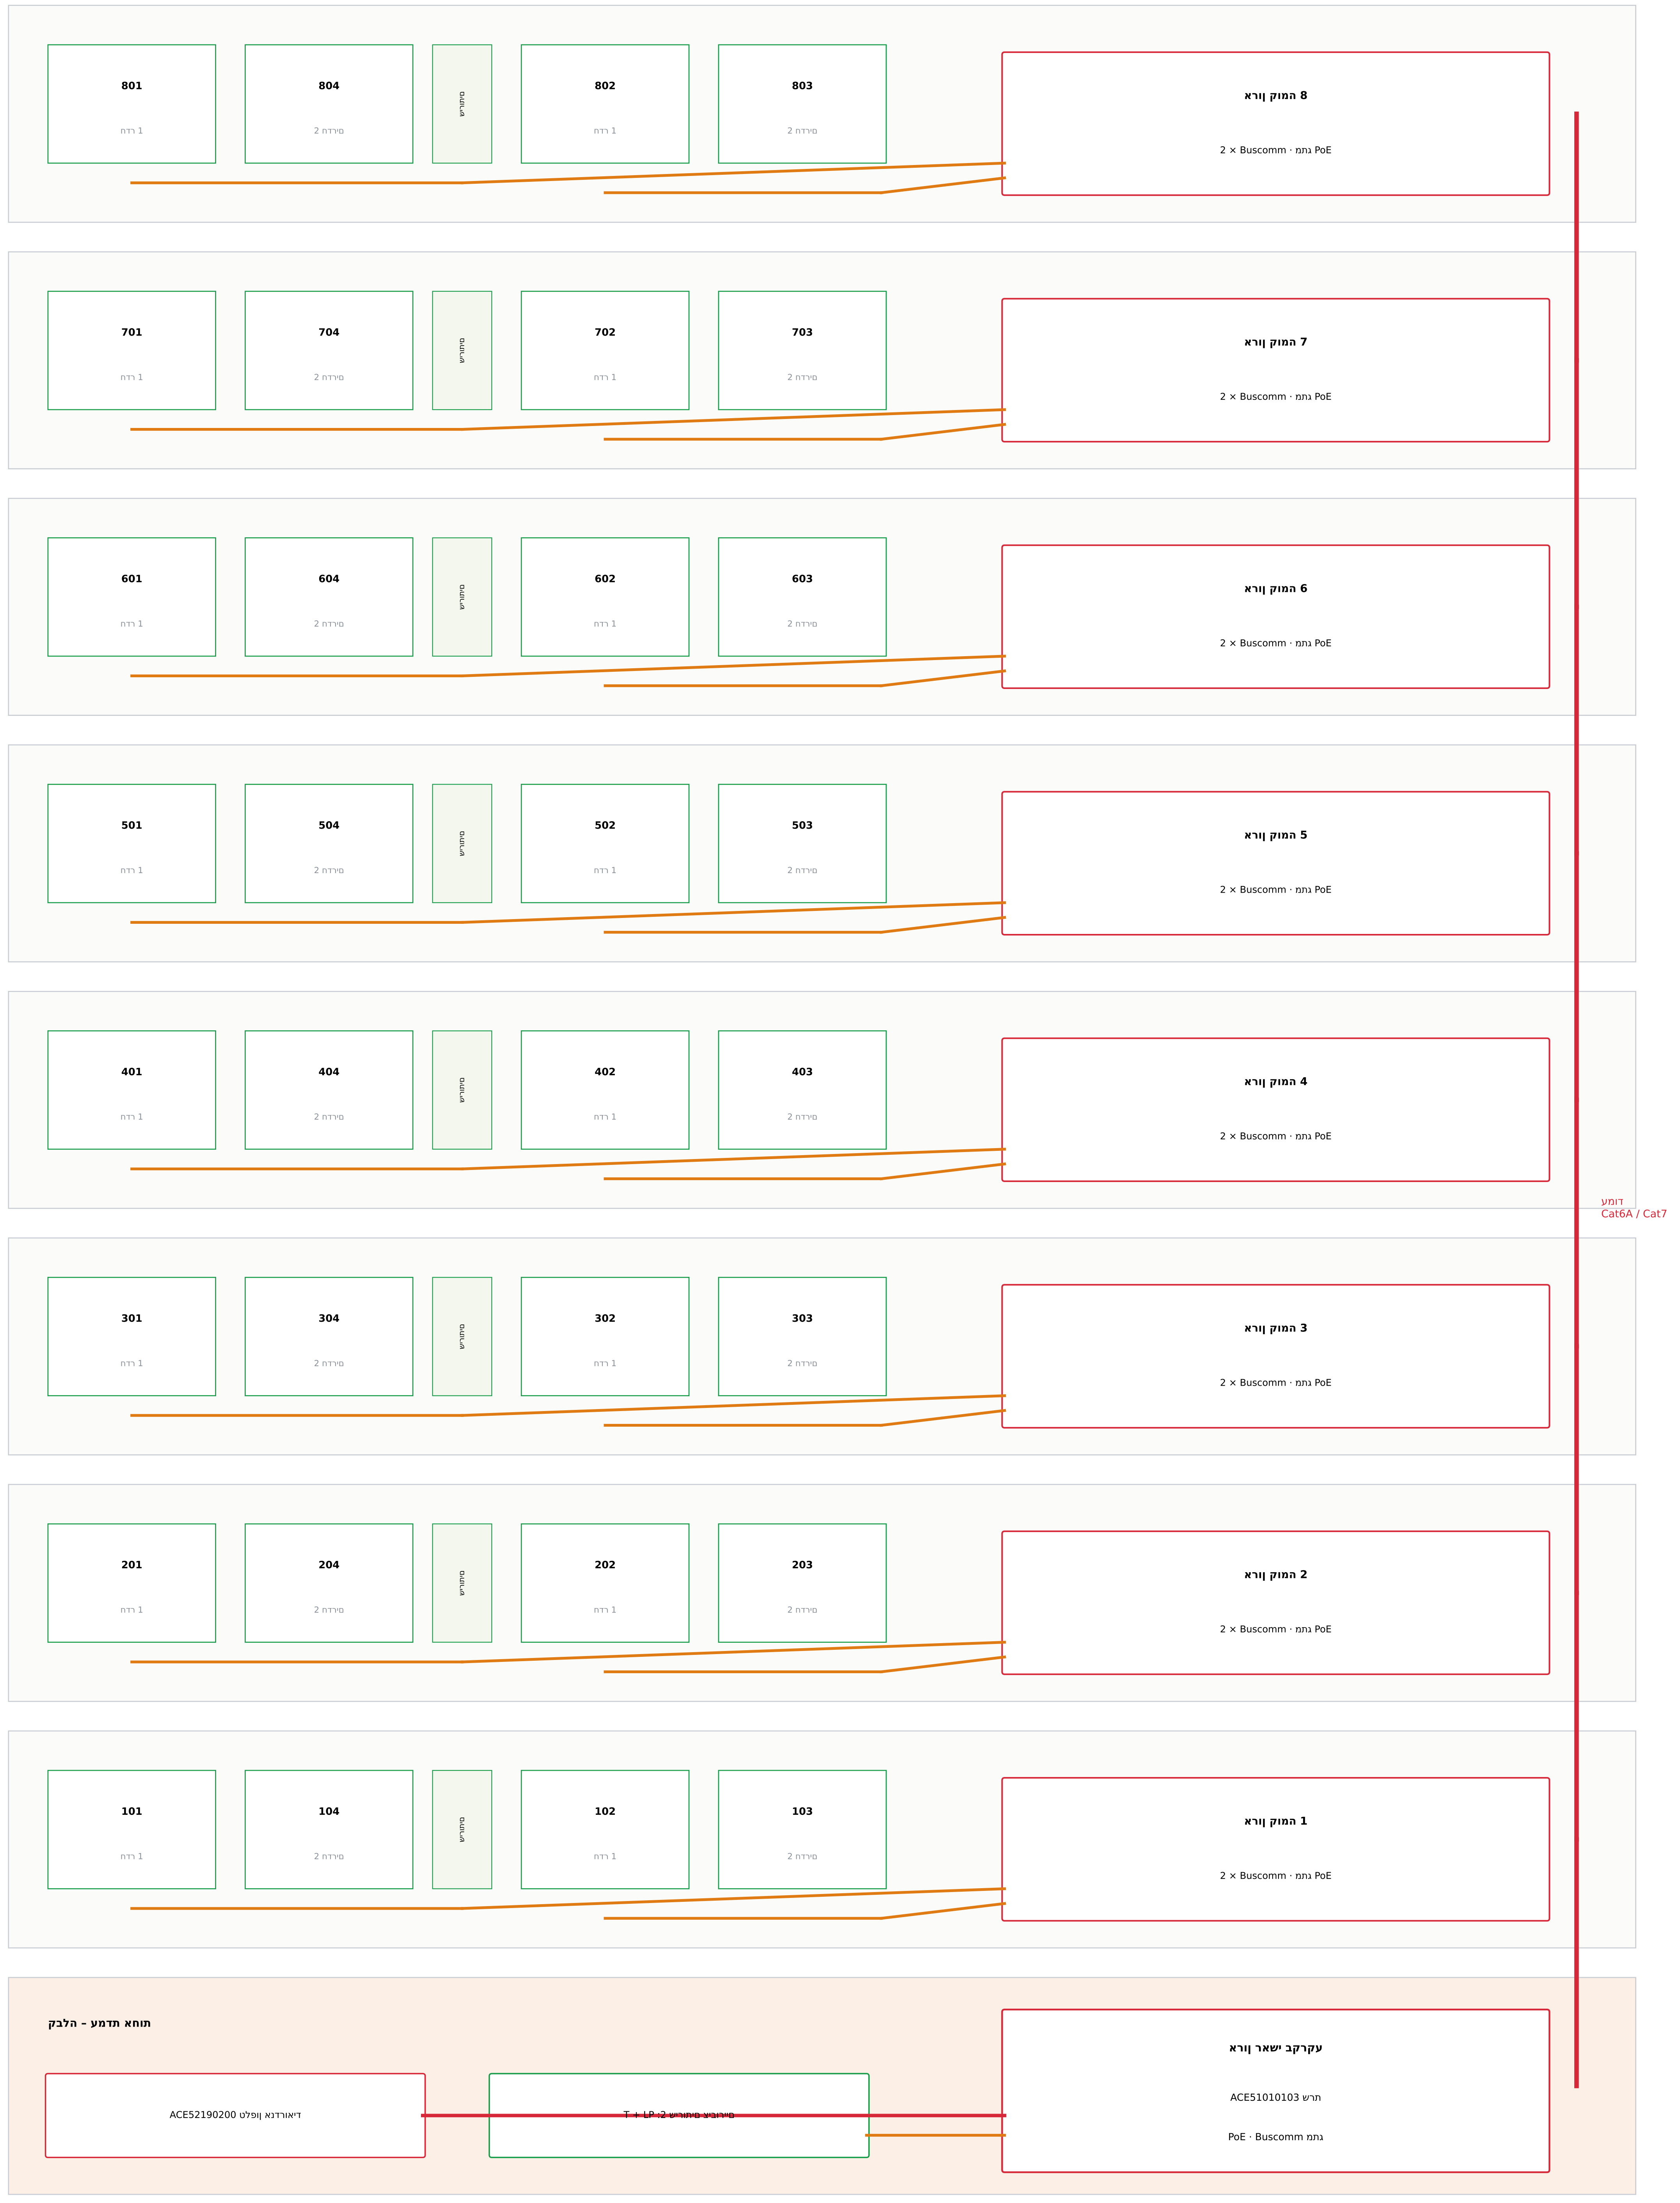
קומה 8
801
חדר 1
804
2 חדרים
שירותים
802
חדר 1
803
2 חדרים
ארון קומה 8
2 × Buscomm · מתג PoE
קומה 7
701
704
702
703
ארון קומה 7
קומה 6
601
604
602
603
ארון קומה 6
קומה 5
501
504
502
503
ארון קומה 5
קומה 4
401
404
402
403
ארון קומה 4
קומה 3
301
304
302
303
ארון קומה 3
קומה 2
201
204
202
203
ארון קומה 2
קומה 1
101
104
102
103
ארון קומה 1
עמוד
Cat6A / Cat7
קרקע
קבלה – עמדת אחות
טלפון אנדרואיד ACE52190200
שירותים ציבוריים: 2 T + LP
ארון ראשי בקרקע
שרת ACE51010103
Buscomm · מתג PoE

ב · טופולוגיה של דירה

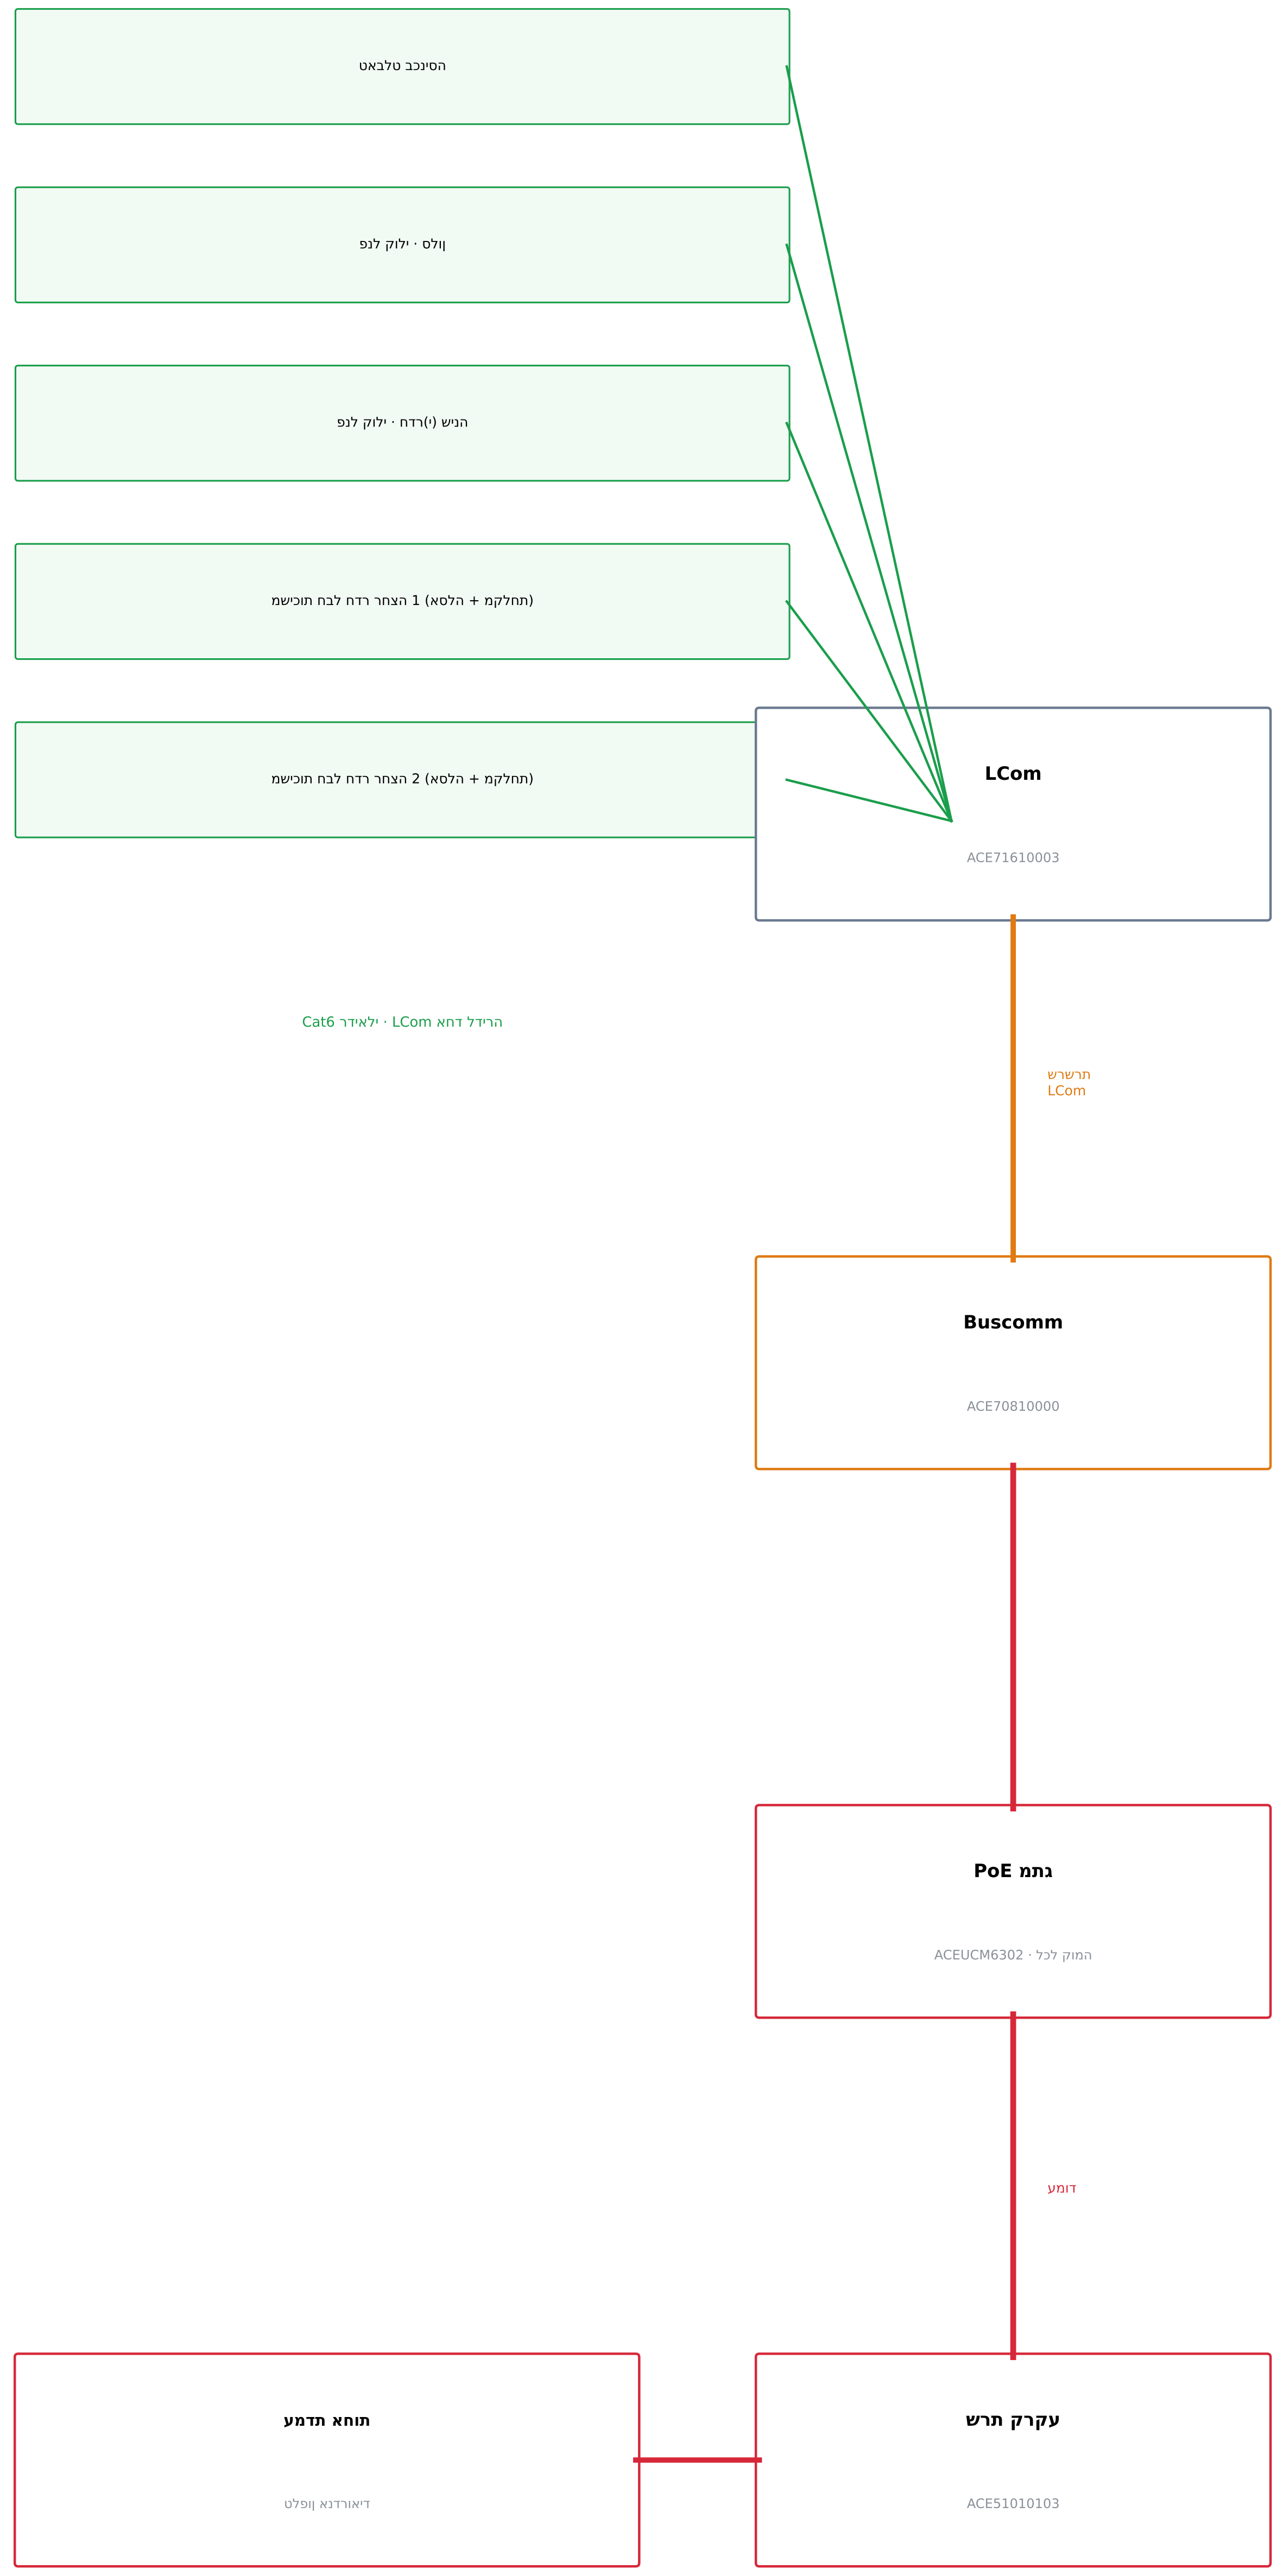
טאבלט בכניסה
פנל קולי · סלון
פנל קולי · חדר(י) שינה
משיכות חבל חדר רחצה 1 (אסלה + מקלחת)
משיכות חבל חדר רחצה 2 (אסלה + מקלחת)
LCom
ACE71610003
Cat6 רדיאלי · LCom אחד לדירה
שרשרת LCom
Buscomm
ACE70810000
מתג PoE
ACEUCM6302 · לכל קומה
עמוד
עמדת אחות
טלפון אנדרואיד
שרת קרקע
ACE51010103

NOTES · הערות

1. 8 קומות זהות עם 4 דירות
(2 דירות חדר שינה אחד ו-2 דירות שני חדרי שינה).

2. בכל קומה: ארון עם 2 Buscomm
ומתג PoE.

3. שרשרת 1: x01 ← x04 ← שירותים ציבוריים.
שרשרת 2: x02 ← x03.

4. המתגים מחוברים דרך העמוד
עד הארון הראשי בקרקע.

5. הקריאות מגיעות בדיבור לטלפון
האנדרואיד בעמדת האחות.

6. כל המערכת PoE.

7. כמויות ראשוניות: לאמת
מול Advantecnia ובאתר.

מגדלי ים התיכון · דיור מוגן
קריאת אחות – קרקע + 8 קומות · 32 דירות
הוכן ע"י: Telab International   מערכת: ACE BG · Advantecnia

תרשים אנכי וטופולוגיה
Riser diagram and topology

SCALE · קנה מידה	DATE · תאריך	REV	גיליון
S/E	**15/10/2026**	**B**	**08**

בסיס: תוכניות האדריכל L5 (מסד עוז / Triplet) · מידות במטרים
פורמט A1 · מהדורה B – על התוכניות האמיתיות

רשימת חומרים – כל הבניין (קרקע + 8 קומות · 32 דירות · 10 שירותים ציבוריים)

קוד	תיאור	כמות	הערה
בדירות (32)			
TAB	טאבלט בכניסה (iPad / אנדרואיד) – קריאה ודיבור	**32**	1 לכל דירה
VOZ	ACE82182451 – פנל קריאה קולי עם לחצנים	**80**	כל חדר שינה + סלון
TI/TD	משיכת חבל – ACE40320303W (אסלה ומקלחת)	**128**	4 לכל דירה
LC	LCom – ACE71610003	**32**	1 לכל דירה
שירותים ציבוריים (10)			
T	ACE40320303W – משיכת חבל	**10**	8 קומות + 2 בקרקע
LP	ACE41020309 – מנורת מסדרון	**10**	מעל כל דלת
LC	LCom – ACE71610003	**9**	1 לכל קומה + 1 בקרקע
ארונות ומרכזייה			
BC	Buscomm – ACE70810000	**17**	2 לכל קומה + 1 בקרקע
SW	PoE – ACEUCM6302 מתג	**9**	1 לכל קומה + קרקע
GAB	ארון ריק 12U (Tripp Lite SRW12US) עם פאץ' פאנל	**8**	1 לכל קומה
GAB-PB	UPS ארון ראשי עומד עם	**1**	קרקע
SRV	Advantecnia – ACE51010103 שרת + תוכנה	**1**	קרקע
TEL	ACE52190200 – טלפון שולחני אנדרואיד	**1**	עמדת אחות
כבלים (+ 15% רזרבה)			
—	Cat6 רדיאלי בתוך הדירות (ירוק)	**1700 m**	183 מ' לקומה
—	Cat6 / Cat7 שרשרת LCom ← Buscomm (כתום)	**780 m**	82 מ' לקומה
—	Cat6A / Cat7 ארונות ועמוד (אדום)	**100 m**	כולל עמוד

NOTES · הערות

1. כמויות מחושבות מהמודל (קומה טיפוסית × 8 + קרקע).
2. אורכי כבל נמדדו על התוואי המשורטט, + 15%.
3. מחירים: לפי מחירון Advantecnia העדכני.
4. לאמת באתר לפני רכישה.

מגדלי ים התיכון · דיור מוגן
קריאת אחות – קרקע + 8 קומות · 32 דירות
הוכן ע"י: Telab International   מערכת: ACE BG · Advantecnia

רשימת חומרים
Bill of materials

SCALE · קנה מידה	DATE · תאריך	REV	גיליון
S/E	**15/10/2026**	**B**	**09**

בסיס: תוכניות אדריכל L5 (מסד זוג / Triplet) · מידות במטרים
פורמט A1 · מהדורה B – על התוכניות האמיתיות

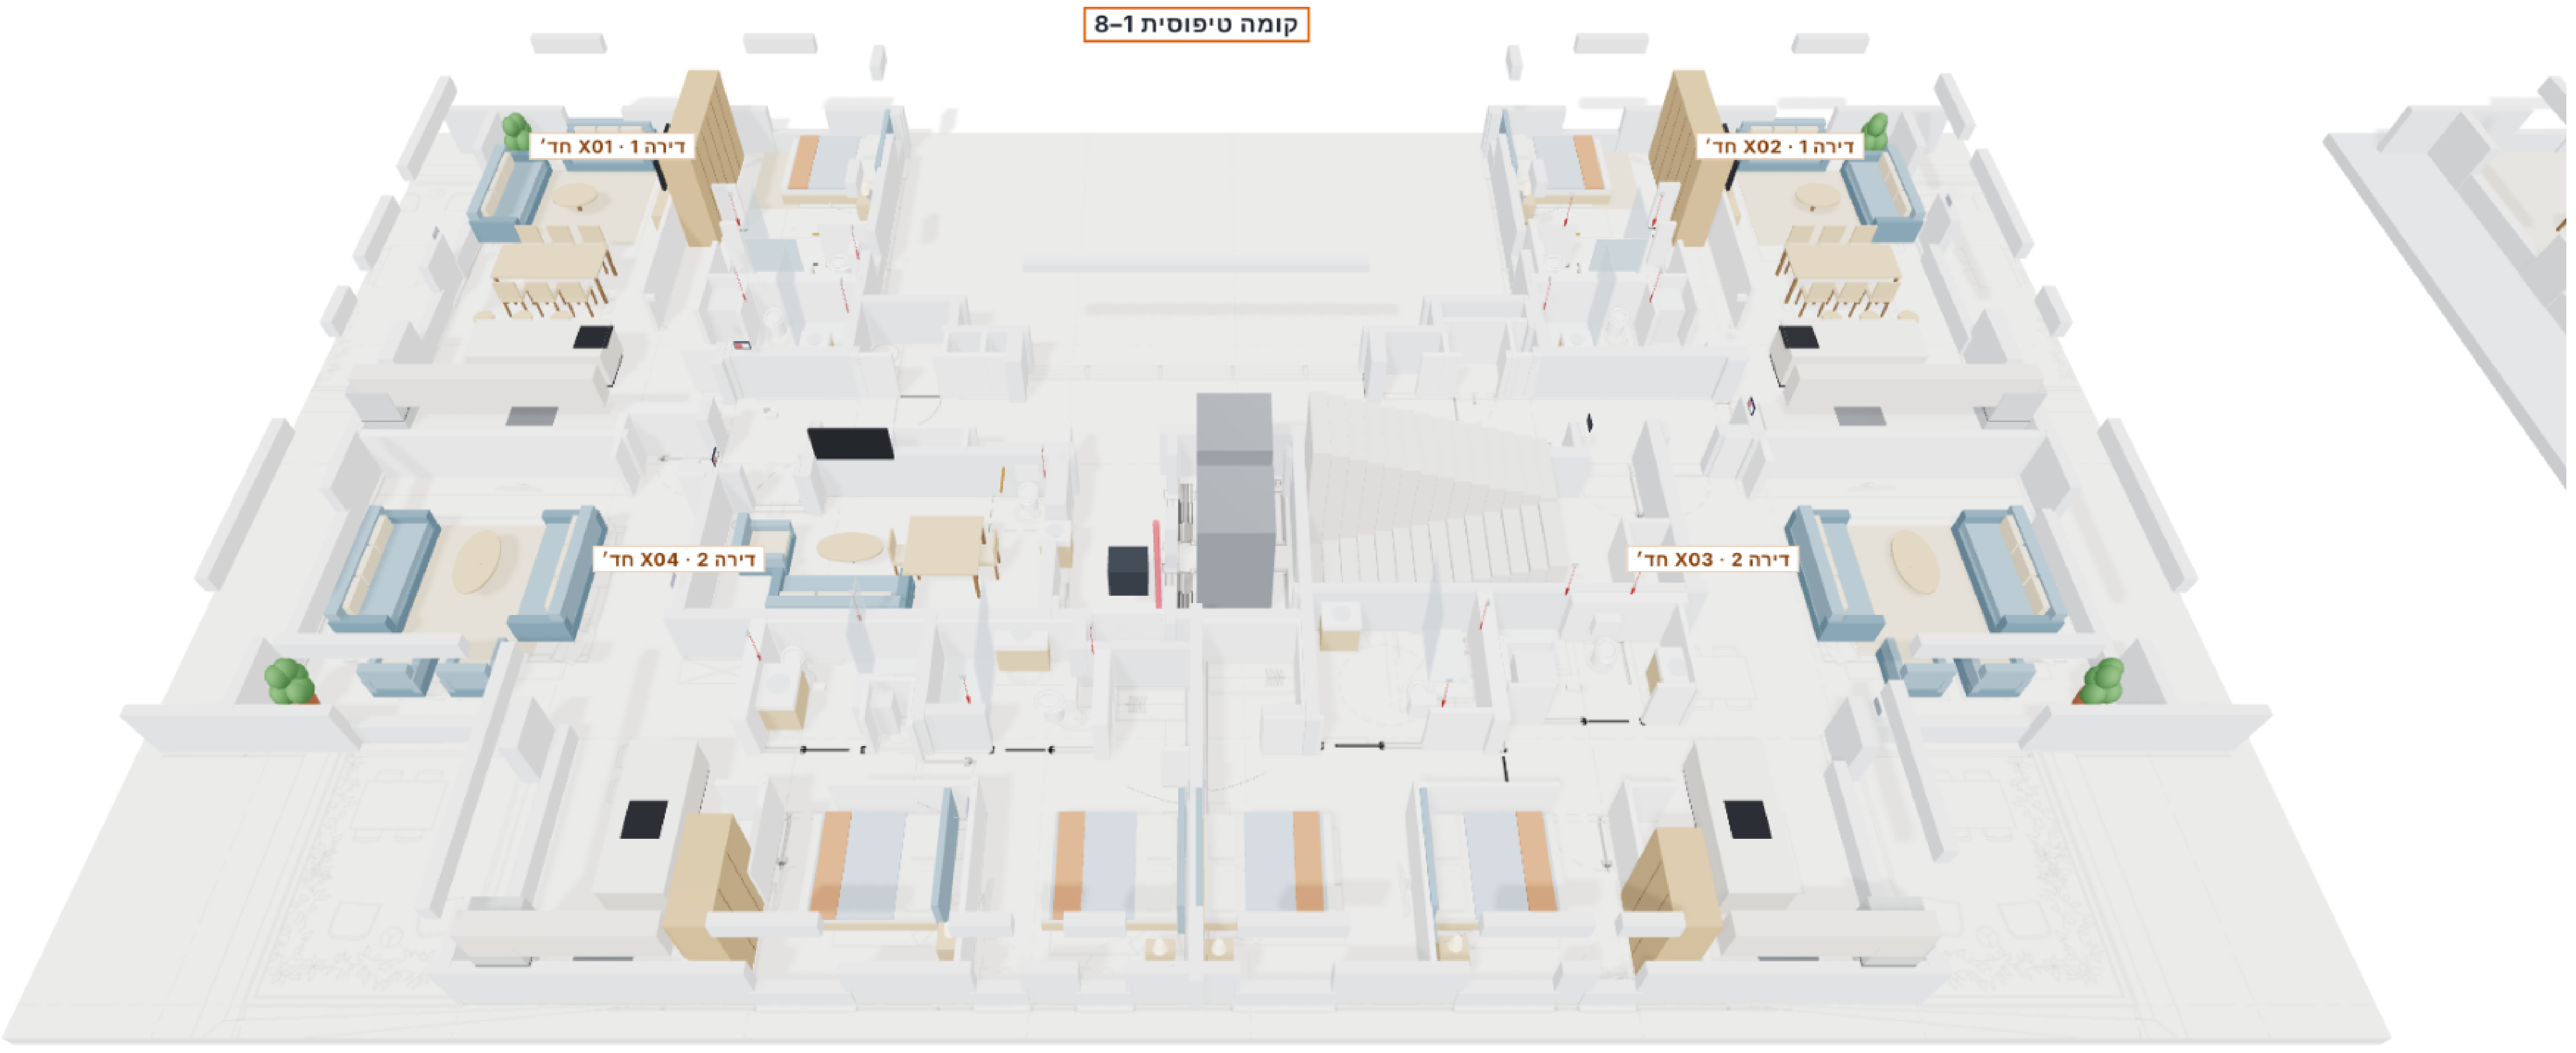
קומה טיפוסית 1–8
דירה 1 · X01 חד׳
דירה 1 · X02 חד׳
דירה 2 · X04 חד׳
דירה 2 · X03 חד׳

א · קומה טיפוסית – 4 דירות

ב · טאבלט בכניסה

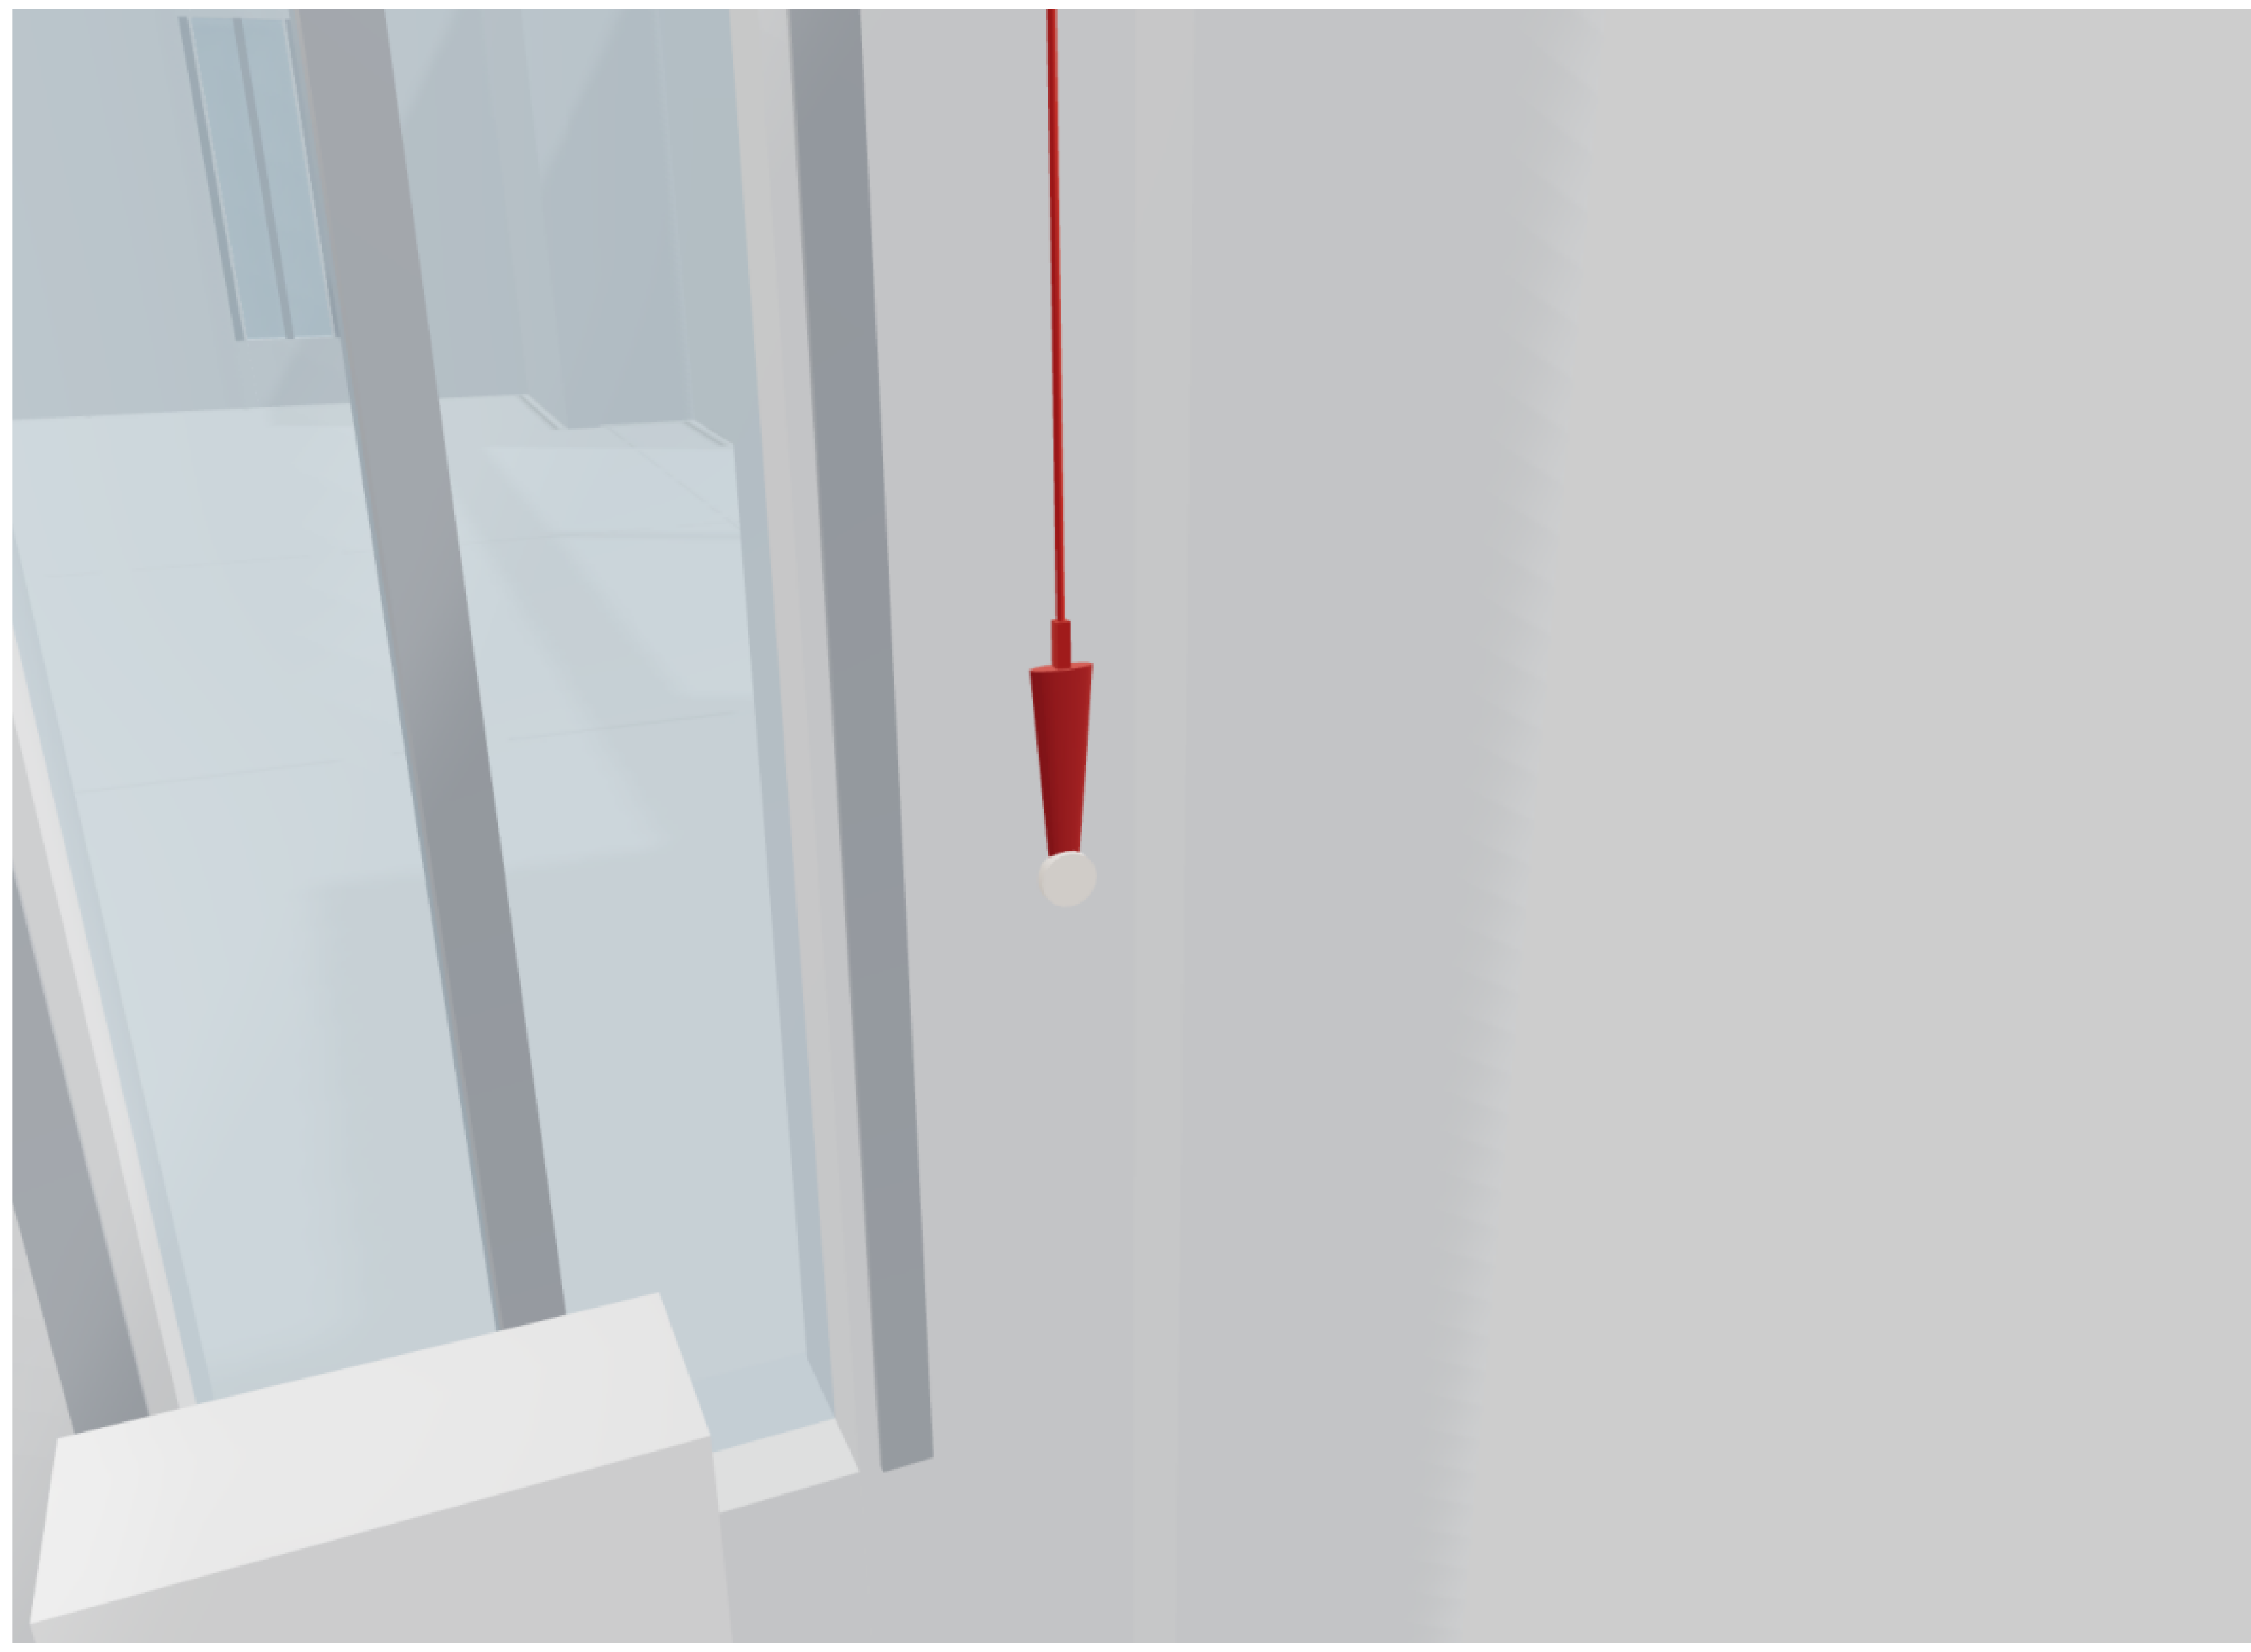

ד · חדר רחצה – משיכות חבל באסלה ובמקלחת

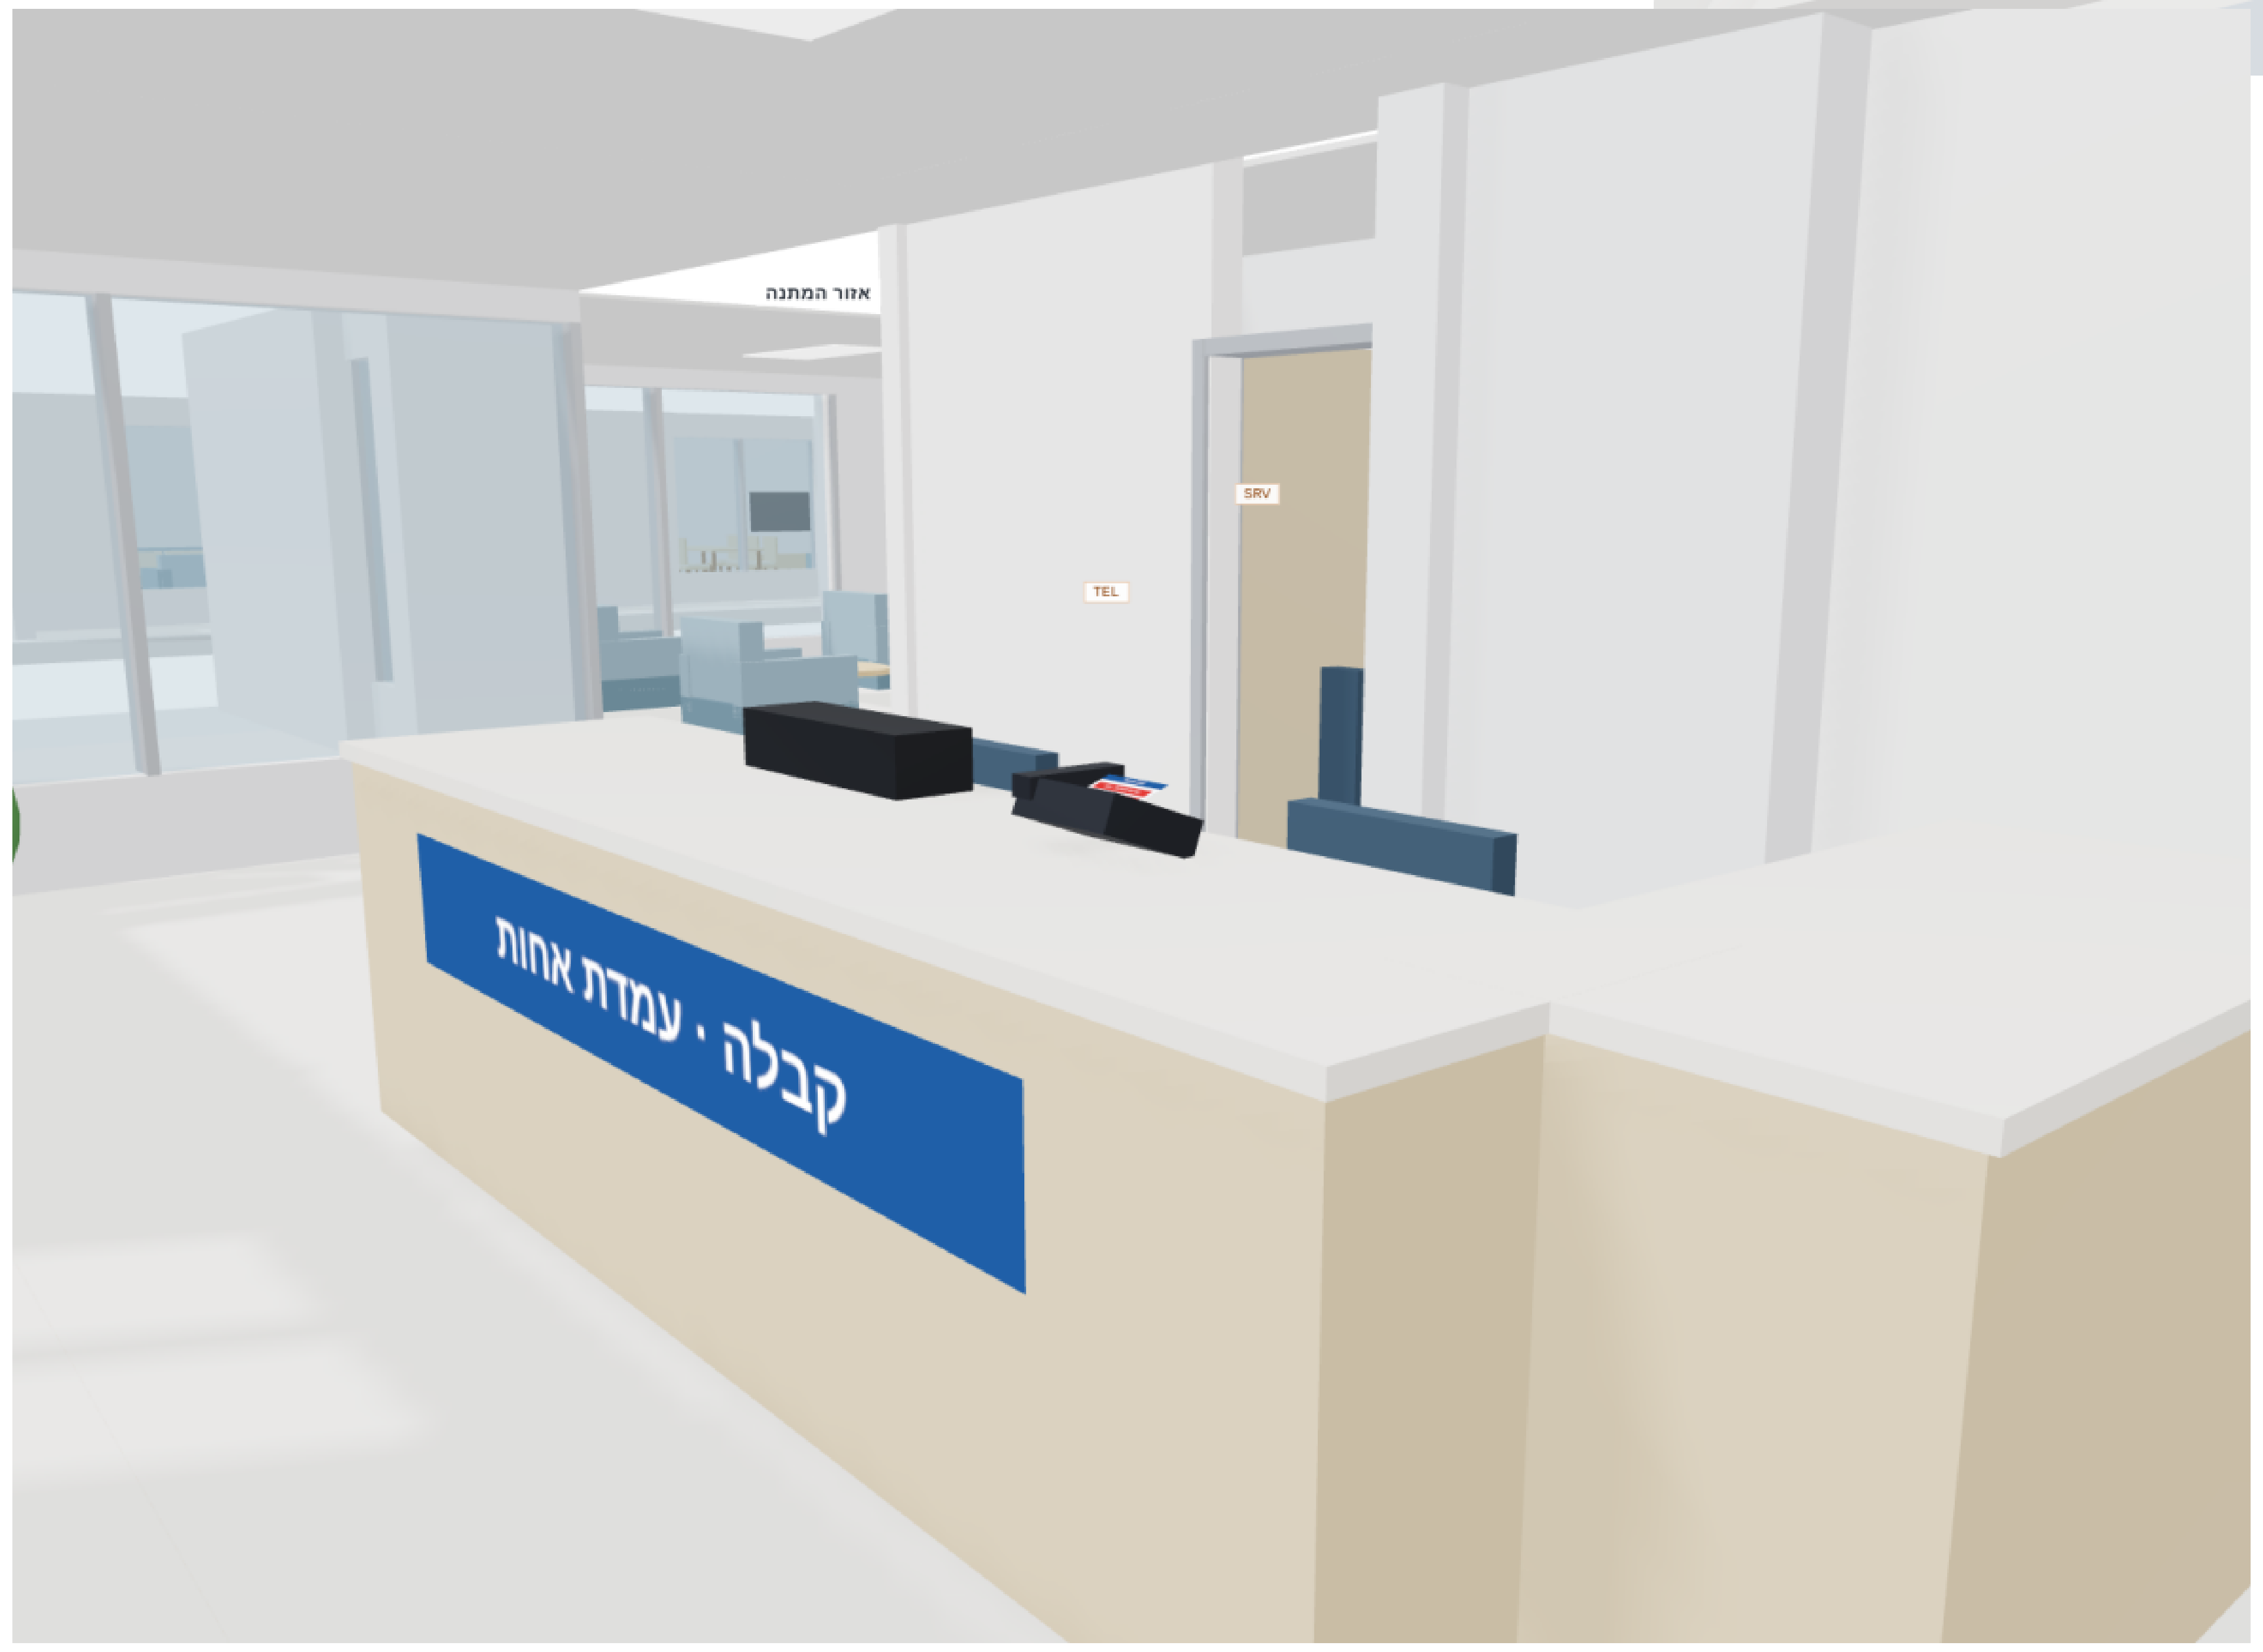
אזור המתנה
TEL
SRV
קבלה · עמדת אחות

ה · קרקע – עמדת אחות

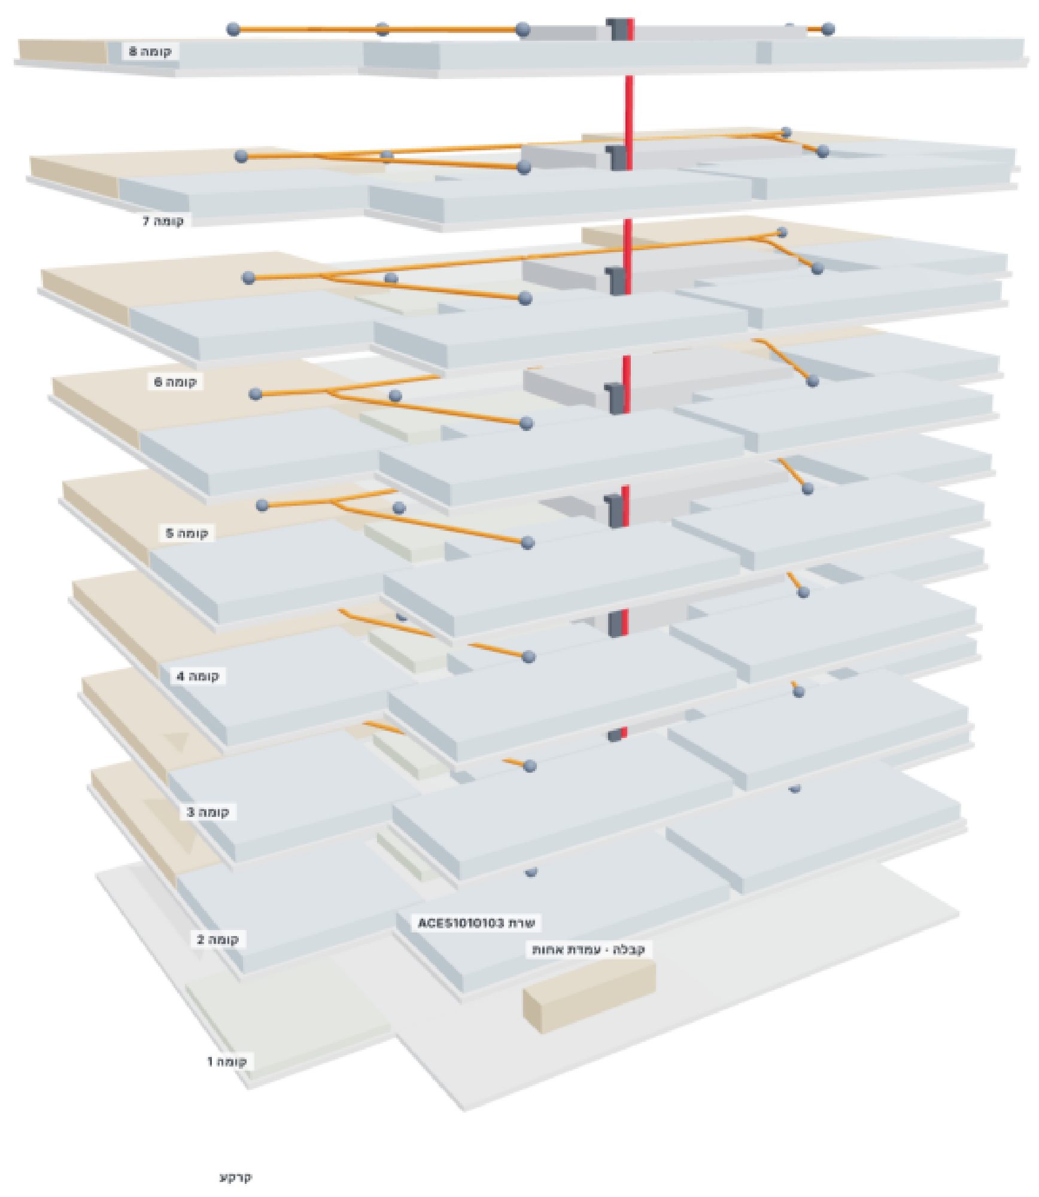
קומה 8
קומה 7
קומה 6
קומה 5
קומה 4
קומה 3
קומה 2
קומה 1
קרקע
קבלה · עמדת אחות

ו · בניין קרקע + 8 קומות

מגדלי ים התיכון · דיור מוגן

קריאת אחות – קרקע + 8 קומות · 32 דירות

מערכת: ACE BG · Advantecnia   הוכן ע"י: Telab International

מבטים תלת-ממדיים

3D views

SCALE · קנה מידה	DATE · תאריך	REV	גיליון
S/E	15/10/2026	B	10

בסיס: תוכנית האדריכל L5 (מסד זוג / Triplet) · מידות במטרים

פורמט A1 · מהדורה B – על התוכנית האמיתית

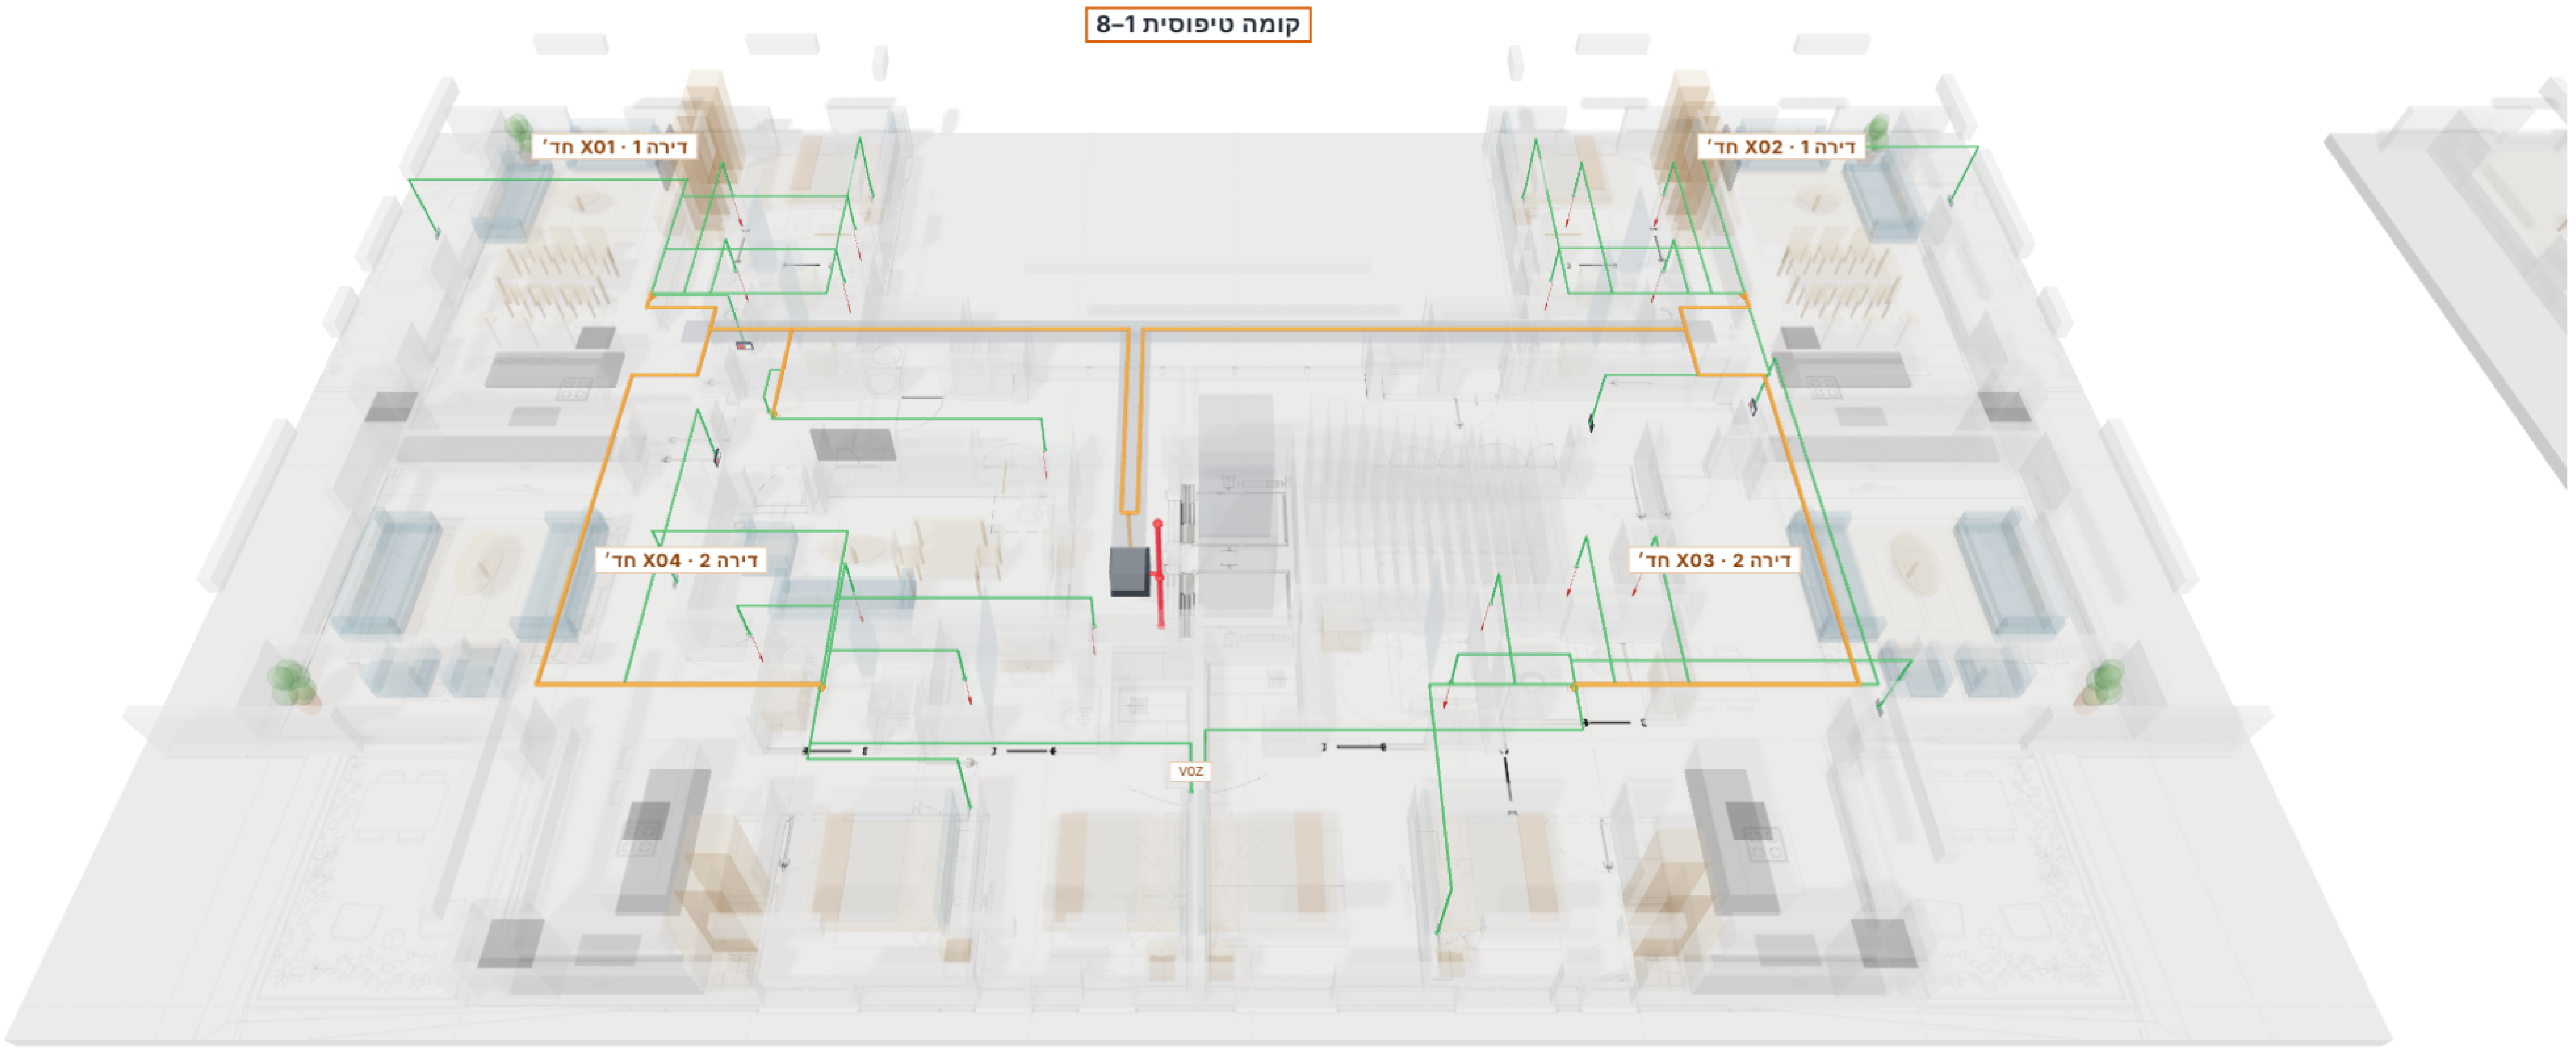

(תשר םודא · LCom תרשרש םותכ · ילאידר קורי) טוויח – תיסופיט המוק · א

הלבקו יבול – עקרק תמוק · ב

םינצחל םע ילוק לנפ – ןולס · ג

COLOURS · COLORES · םיעבצ

🟩	Cat6 ילאידר: ןקתה לכ ← LCom הרידה לש Cat6 radial: each device → apartment LCom · Cat6 ילאידר: ןקתה לכ ← LCom הרידה לש
🟧	Cat6 / Cat7 תרשרש: LCom ← LCom ← Buscomm ןוראב Cat6 / Cat7 chain: LCom → LCom → Buscomm · Cat6 / Cat7 תרשרש: LCom ← LCom ← Buscomm
🟥	Cat6A / Cat7 תשר: Buscomm ← גתמ ← דומע ← תרש עקרק Cat6A / Cat7 network: Buscomm → switch → riser → GF server · Cat6A / Cat7 תשר: Buscomm ← גתמ ← דומע ← תרש

ןגומ רויד · ןוכיתה םי ילדגמ

תוריד 32 · תומוק 8 + עקרק – תוחא תאירק

Telab International :ןכוה ע"י ACE BG · Advantecnia :תכרעמ

טוויח – םיידממ-תלת םיטבמ

3D views – wiring

SCALE · הדימ הנק	DATE · ךיראת	REV	ןוילג
S/E	15/10/2026	B	11

סיסב: תוינכות לכירדאה L5 (זוע דסמ / Triplet) · םירטמב תודימ

טמרופ A1 · הרודהמ B – לע תוינכותה תיתימאה