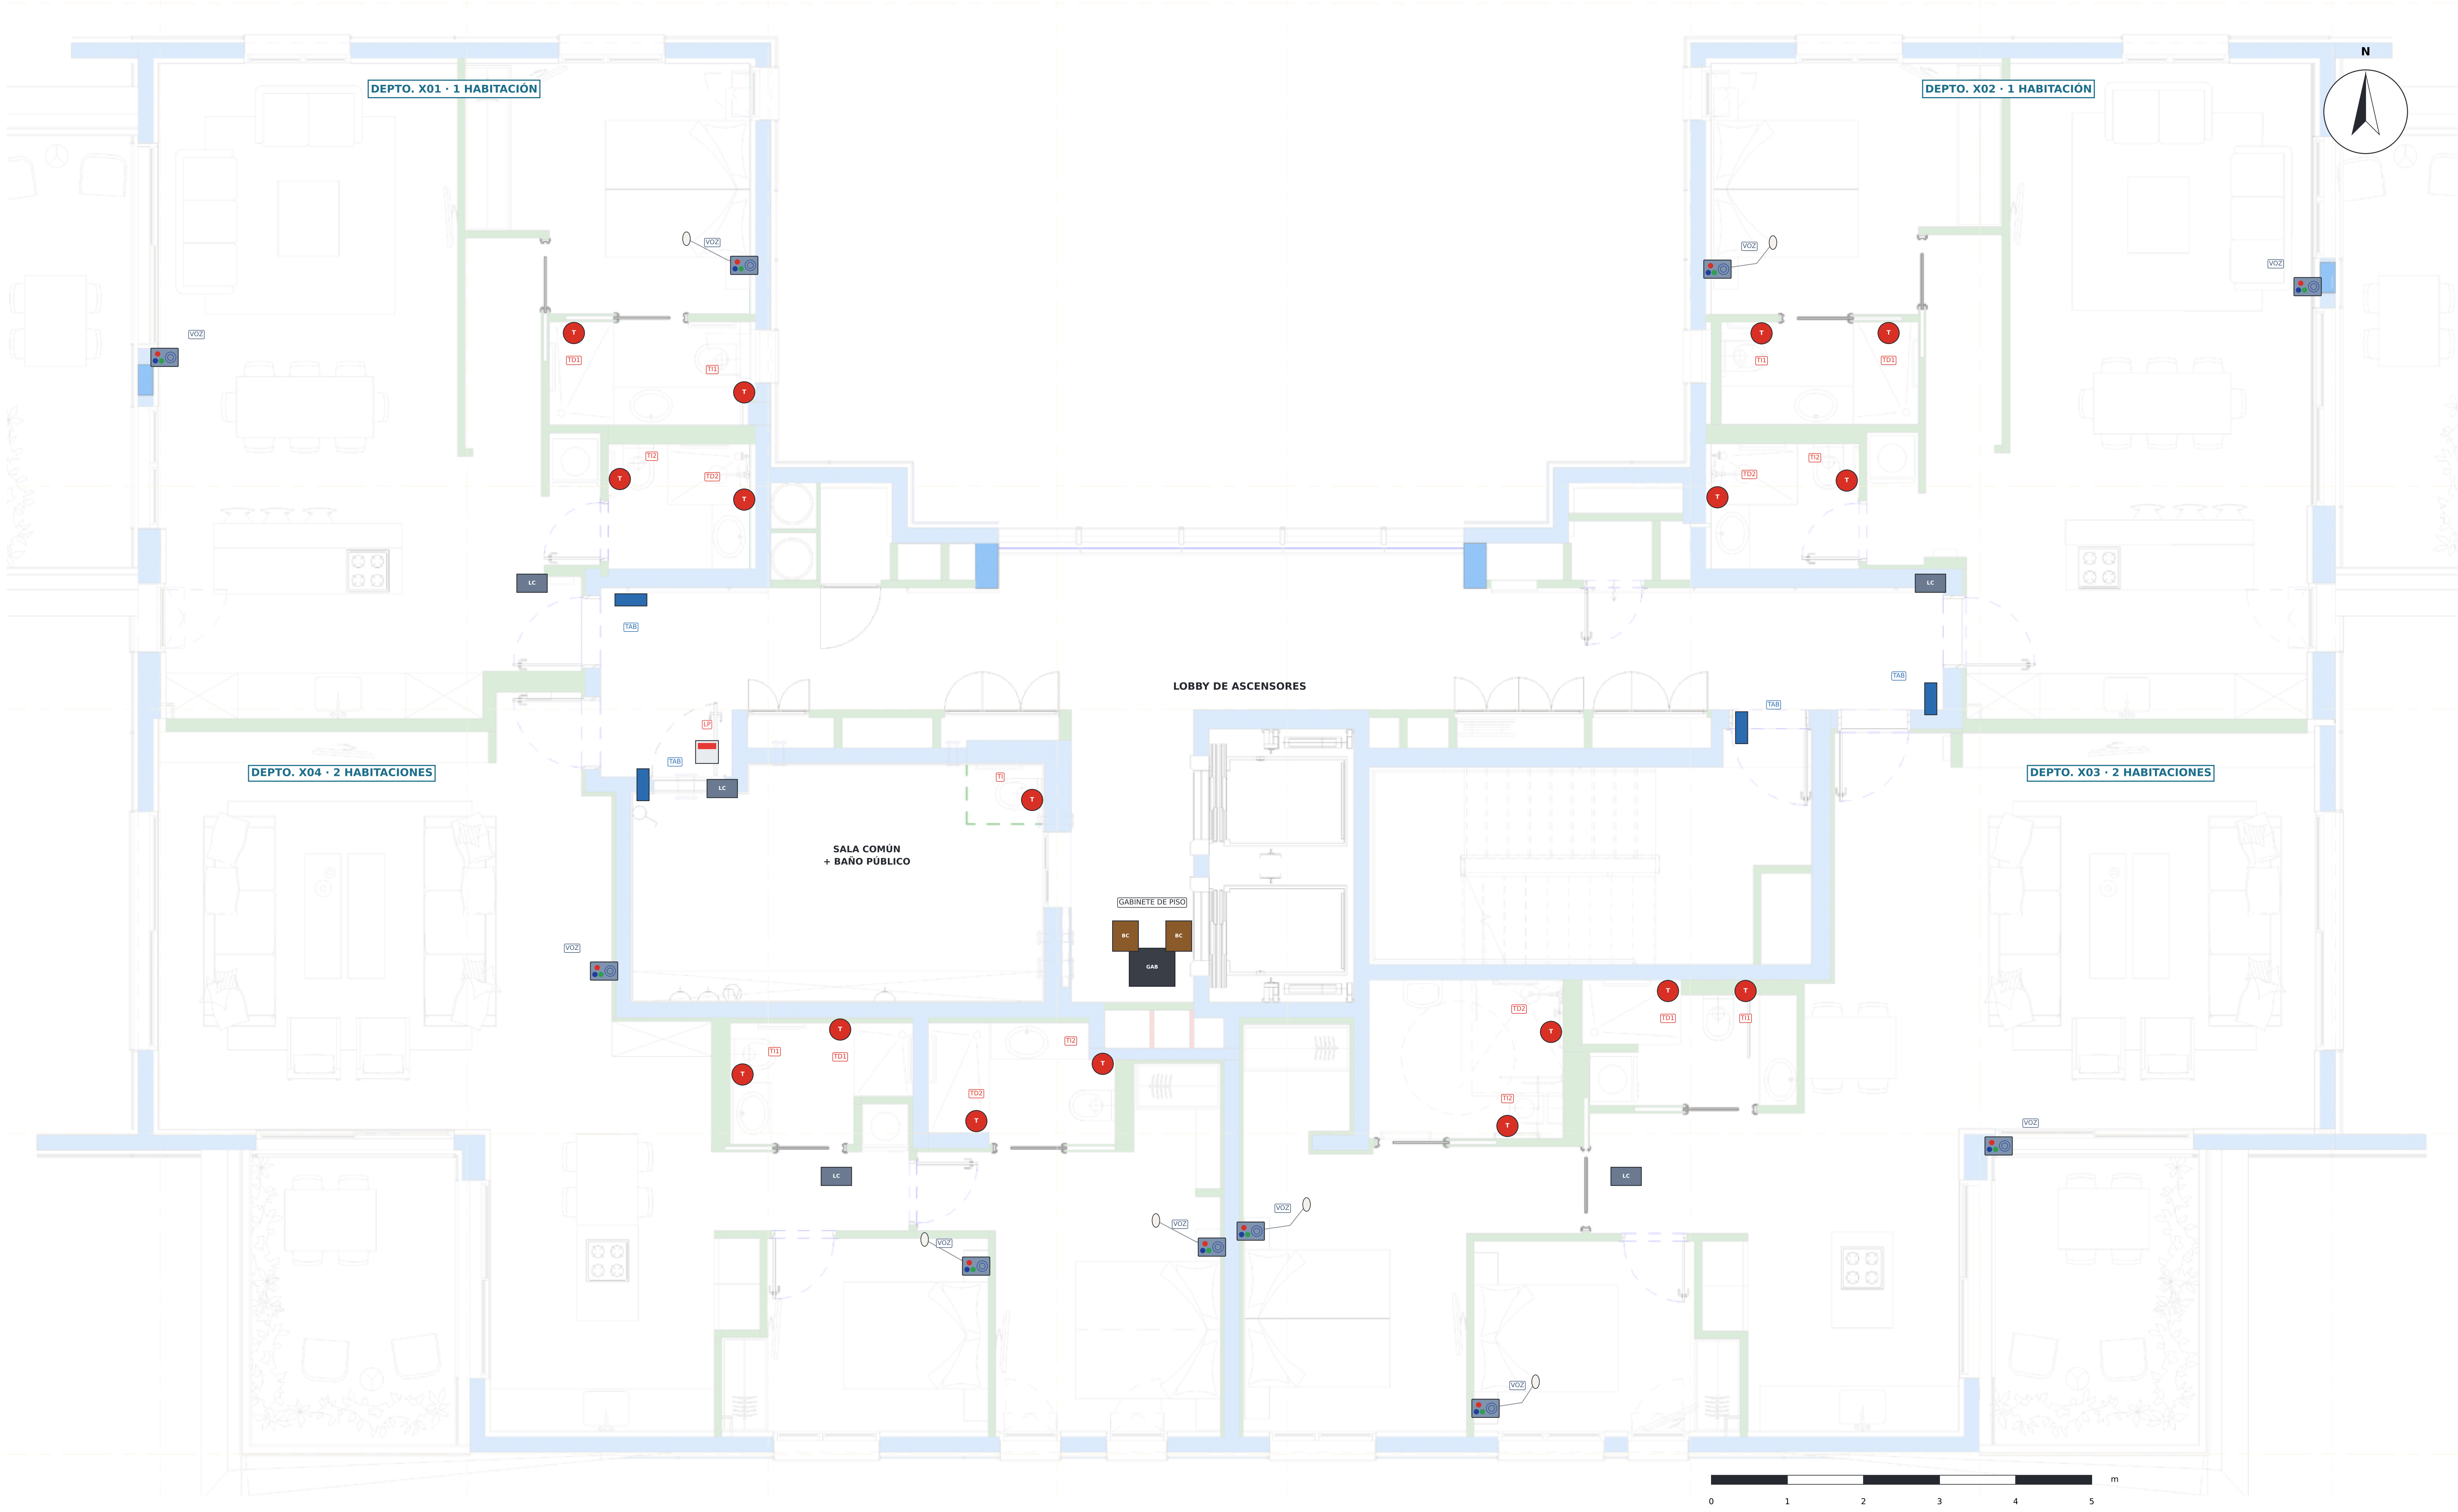
N
DEPTO. X01 · 1 HABITACIÓN
DEPTO. X02 · 1 HABITACIÓN
DEPTO. X03 · 2 HABITACIONES
DEPTO. X04 · 2 HABITACIONES
LOBBY DE ASCENSORES
SALA COMÚN + BAÑO PÚBLICO
GABINETE DE PISO
GAB
BC
LC
TAB
VOZ
T
0
1
2
3
4
5
m

**EQUIPOS · DEVICES · דויצ**

| | |
|---|---|
| 🟦 | TAB · Tablet de la puerta (iPad / Android) – llamada y voz, h 1,40 m<br>Door tablet – call and voice · רובידו האירק – הסינכב טלבאט |
| VOZ | VOZ · Panel con voz y botones ACE82182451 – salón y dormitorios, h 1,20–1,30 m<br>Voice panel with buttons – living room and bedrooms · הניש ירדחו ןולס – םינצחל םע ילוק לנפ |
| ○ | Pera de llamada junto a la cama (en los dormitorios)<br>Call pear next to the bed (bedrooms) · הטימה דיל האירק סגא |
| T | TI / TD · Tirador de baño ACE40320303W – inodoro y ducha, h 1,85 m<br>Pull-cord – toilet and shower, h 1.85 m · משח תכישמ – לבה ואסלה תחלקמו, גובה 1.85 מ' |
| 🟥 | LP · Luz de pasillo ACE41020309 – sobre la puerta de cada baño público<br>Corridor light – above each public toilet door · םיירוביצ םיתוריש לכ תלד לעמ – ןורדסמ תרונמ |
| LC | LC · LCom ACE71610003 – concentrador del departamento (cielorraso)<br>LCom – apartment hub (ceiling) · LCom – הרידה זכרמ (הרקת) |
| BC | BC · BoxCom ACE70810000 – concentrador en bus de varios deptos. (techo)<br>BoxCom – bus hub for several apartments (ceiling) · BoxCom – תוריד המכל סאב זכרמ (הרקת) |
| GAB | Gabinete de piso 12U: switch PoE D-Link DES-1210-28P (24 puertos PoE)<br>Floor rack: D-Link DES-1210-28P PoE switch · ארון קומה: מתג PoE D-Link DES-1210-28P |

**CANTIDADES POR PISO × 8 PISOS**

| Código | Equipo | Por piso | 8 pisos |
|---|---|---|---|
| TAB | Tablet de la puerta | 4 | 32 |
| VOZ | Panel con voz y botones | 10 | 80 |
| TI/TD | Tirador de baño (inodoro + ducha) | 17 | 136 |
| LP | Luz de pasillo (baño público) | 1 | 8 |
| LC | LCom | 5 | 40 |
| BC | BoxCom | 2 | 16 |
| SW | Switch PoE | 1 | 8 |

**NOTAS · NOTES**

1. Base: plano de arquitectura L5 (piso tipo) – los 8 pisos son iguales: 4 departamentos por piso, 32 en total.
2. Departamentos x01 y x02: 1 habitación, salón con cocina y 2 baños. Departamentos x03 y x04: 2 habitaciones y 2 baños.
3. Tablet en la puerta de cada departamento (iPad / Android) para llamar y hablar con enfermería.
4. Panel con voz y botones (ACE82182451) en el salón y en cada dormitorio; en el dormitorio, con pera junto a la cama.
5. Tiradores de baño (ACE40320303W) en el inodoro y en la ducha de todos los baños, a 1,85 m.
6. Baño público por piso en la sala común: tirador + luz de pasillo sobre la puerta. Con los 2 de PB suman 10 baños públicos.
7. Gabinete de piso junto a los ascensores con el switch PoE D-Link DES-1210-28P; los 2 BoxCom van en el techo, al lado.
8. Ubicaciones según las marcas del cliente en el plano L2 (nt = panel con voz, tab = tablet): ver lámina 03.

**ALTURAS DE MONTAJE**

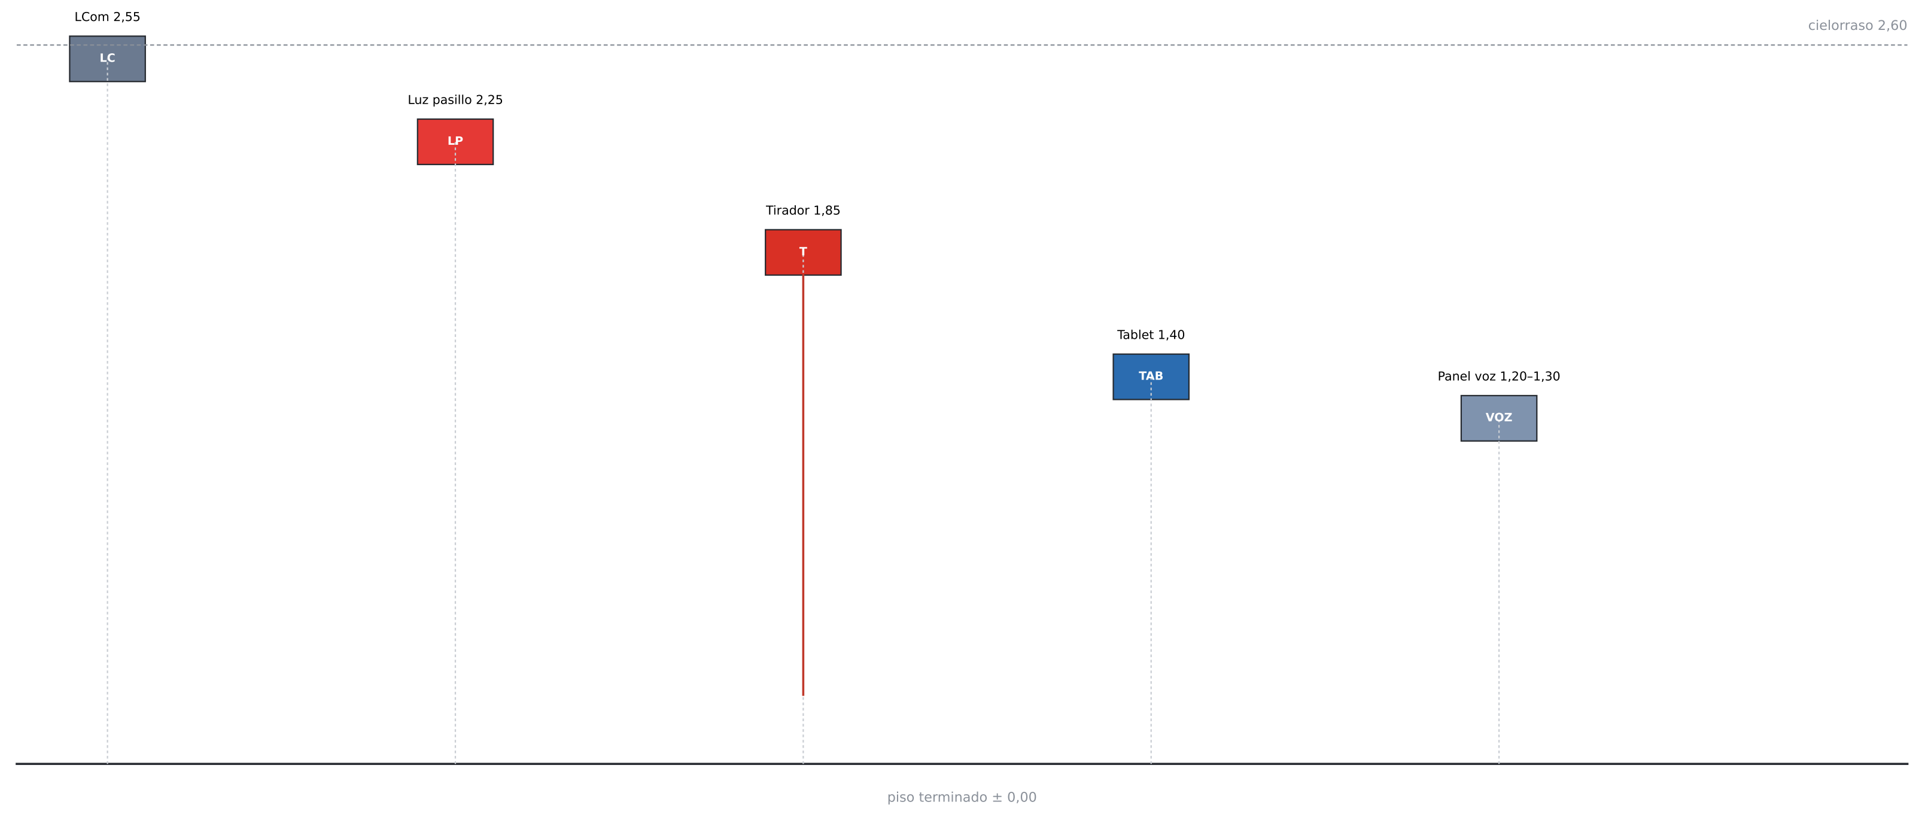
LCom 2,55
LC
cielorraso 2,60
Luz pasillo 2,25
LP
Tirador 1,85
T
Tablet 1,40
TAB
Panel voz 1,20–1,30
VOZ
piso terminado ± 0,00

שירותים קריאת אחות

Tirador de baño

טבלט אנדרואיד קריאת אחות

Tablet en la puerta (iPad / Android)

מנורה קריאת אחות

Luz de pasillo

פנל קריאת אחות

Panel con voz y botones

**MIGDALEI YAM A TIJON · VIVIENDA TUTELADA**

Llamada de enfermería – PB + 8 pisos · 32 departamentos

Sistema: ACE BG · Advantecnia      Elaboró: Telab International

## PISO TIPO P1–P8 · LLAMADA DE ENFERMERÍA

Typical floor F1–F8 · nurse call

| ESCALA · SCALE | FECHA · DATE | REV | LÁMINA |
|---|---|---|---|
| 1:60 | 15/10/2026 | B | 01 |

Base: plano del arquitecto L5 (Massad Oz / Triplet) · cotas en metros

Formato A1 · Rev. B – sobre plano real

שירותים קריאת אחות

**Tirador de baño**

| | |
|---|---|
| Código | **ACE40320303W** |
| Ubicación | Inodoro y ducha de cada baño y de los 10 baños públicos |
| Altura | **1,85 m** |
| Cantidad | **138** |

1

טבלט אנדרואיד קריאת אחות
Advantecnia
Llamada de enfermera
Hospital
Salud y bienestar

**Tablet en la puerta (iPad / Android)**

| | |
|---|---|
| Código | **Advantecnia TV** |
| Ubicación | En el lobby, junto a la puerta de cada departamento |
| Altura | **1,40 m** |
| Cantidad | **32** |

2

מנורה קריאת אחות

**Luz de pasillo**

| | |
|---|---|
| Código | **ACE41020309** |
| Ubicación | Sobre la puerta de cada baño público |
| Altura | **2,25 m** |
| Cantidad | **10** |

3

פנל קריאת אחות

**Panel con voz y botones**

| | |
|---|---|
| Código | **ACE82182451** |
| Ubicación | Salón y cada dormitorio (en el dormitorio, con pera) |
| Altura | **1,20–1,30 m** |
| Cantidad | **80** |

4

GRANDSTREAM
HD

**Teléfono del desk (Android)**

| | |
|---|---|
| Código | **Grandstream** |
| Ubicación | Desk de enfermería en PB · PoE directo al switch |
| Altura | **sobre el desk** |
| Cantidad | **1** |

5

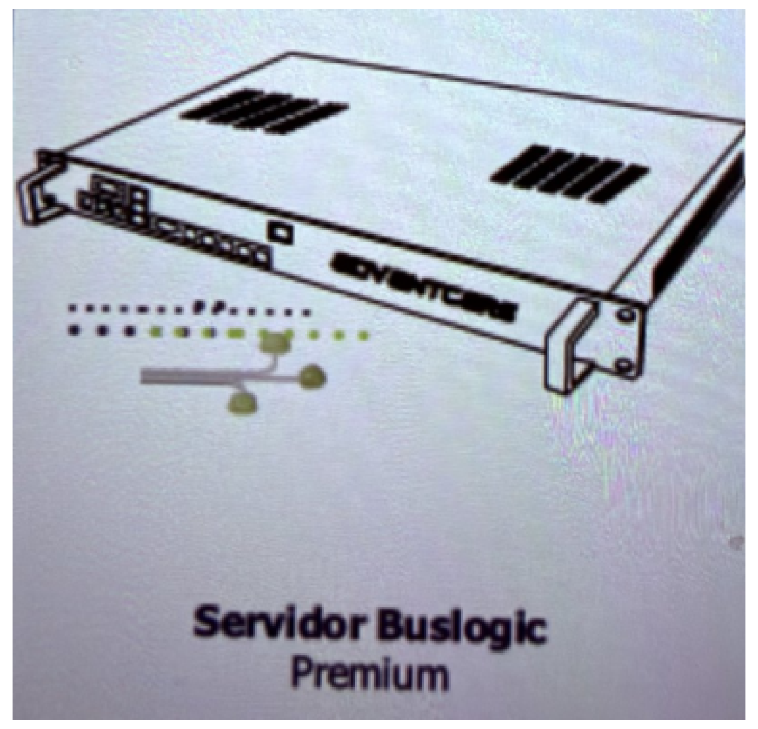

**Servidor Buslogic Premium**

| | |
|---|---|
| Código | **Advantcare** |
| Ubicación | Gabinete principal de PB |
| Altura | **en gabinete** |
| Cantidad | **1** |

6

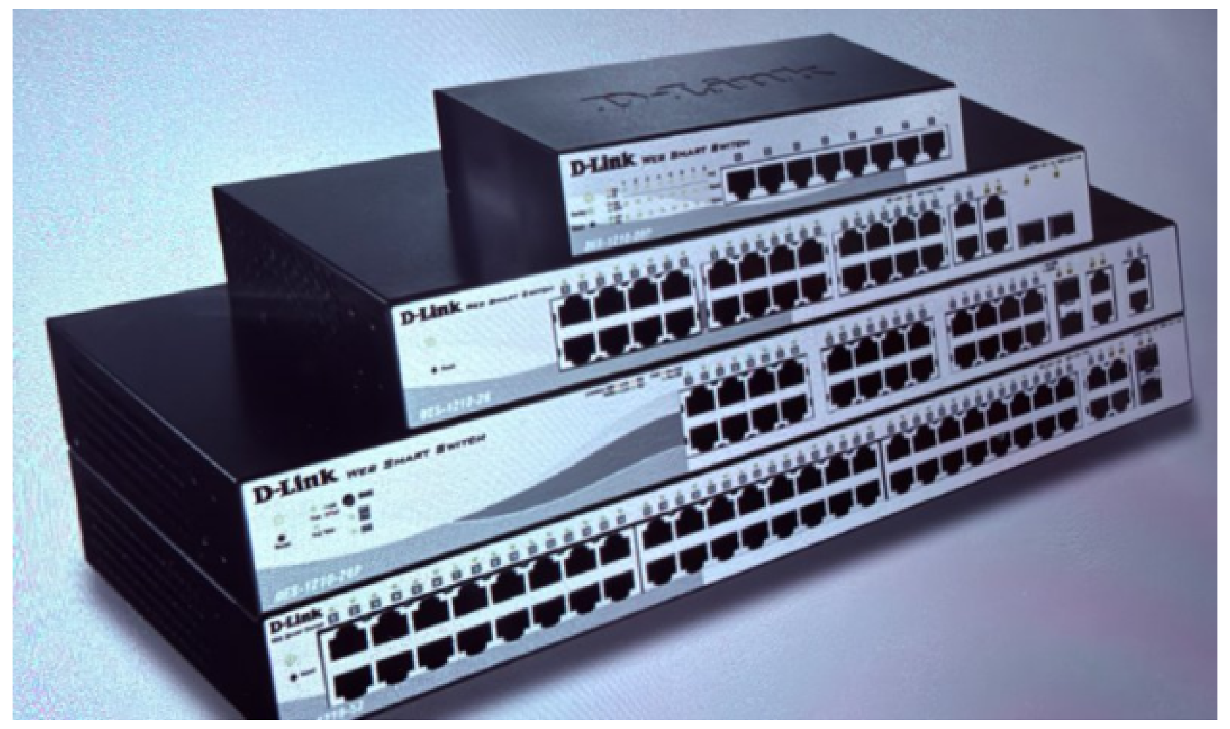

**Switch PoE de 24 puertos**

| | |
|---|---|
| Código | **D-Link DES-1210-28P** |
| Ubicación | Gabinete de cada piso y de PB |
| Altura | **en gabinete** |
| Cantidad | **9** |

7

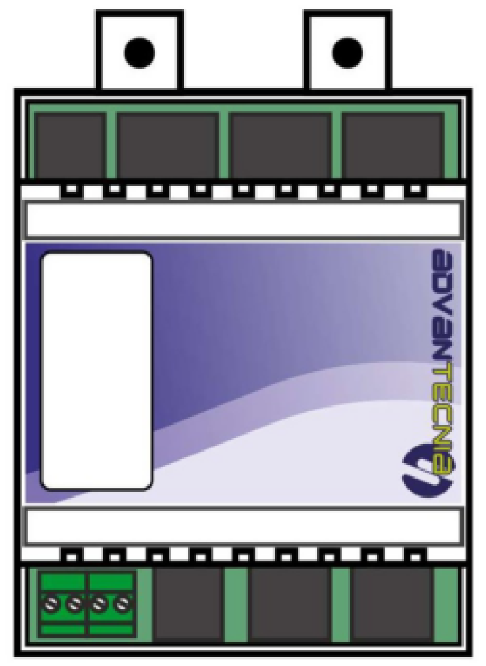

**LCom – concentrador radial**

| | |
|---|---|
| Código | **ACE71610003** |
| Ubicación | Techo de cada departamento y baños públicos |
| Altura | **2,55 m** |
| Cantidad | **41** |

8

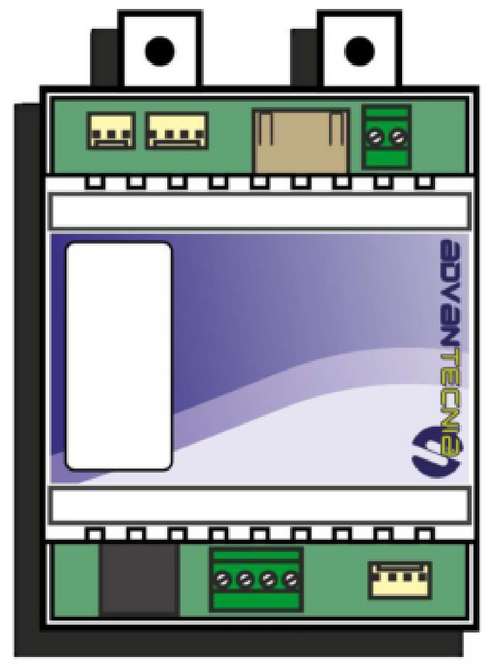

**BoxCom – concentrador en bus**

| | |
|---|---|
| Código | **ACE70810000** |
| Ubicación | Techo junto al gabinete: une varios deptos. |
| Altura | **2,55 m** |
| Cantidad | **17** |

9

**NOTAS · NOTES**

1. Fotos de referencia de ACE BG / Advantecnia, con su título.
2. Tirador: cordón rojo con empuñadura, alcanzable desde el piso.
3. La tablet de la puerta llama y habla con enfermería.
4. La luz de pasillo se enciende cuando llaman desde el baño público.
5. El panel tiene botón rojo de llamada, botón azul (izq.) y verde (der.) y altavoz para hablar.
6. Cadena: equipos → LCom (radial) → BoxCom (bus) → switch PoE → servidor.
7. El teléfono del desk va directo al switch PoE.

**TELÉFONO DEL DESK – QUÉ COLOR SE VE**

| | | |
|---|---|---|
| 🟥 | Alarma (tirador / SOS) | **Rojo** |
| 🟩 | Botón verde 1 vez: presencia | **Verde** |
| ⬜ | Botón verde otra vez: cancela llamada o alarma | **Se borra** |
| 🟦 | Botón azul: llamada de médico (blue call) | **Azul** |
| 🟧 | Llamada de voz | **Amarillo / naranja** |

**MIGDALEI YAM A TIJON · VIVIENDA TUTELADA**
Llamada de enfermería – PB + 8 pisos · 32 departamentos
Sistema: ACE BG · Advantecnia    Elaboró: Telab International

## EQUIPOS DEL SISTEMA

System devices

| ESCALA · SCALE | FECHA · DATE | REV | LÁMINA |
|---|---|---|---|
| **S/E** | **15/10/2026** | **B** | **02** |

Base: plano del arquitecto L5 (Massad Oz / Triplet) · cotas en metros
Formato A1 · Rev. B – sobre plano real

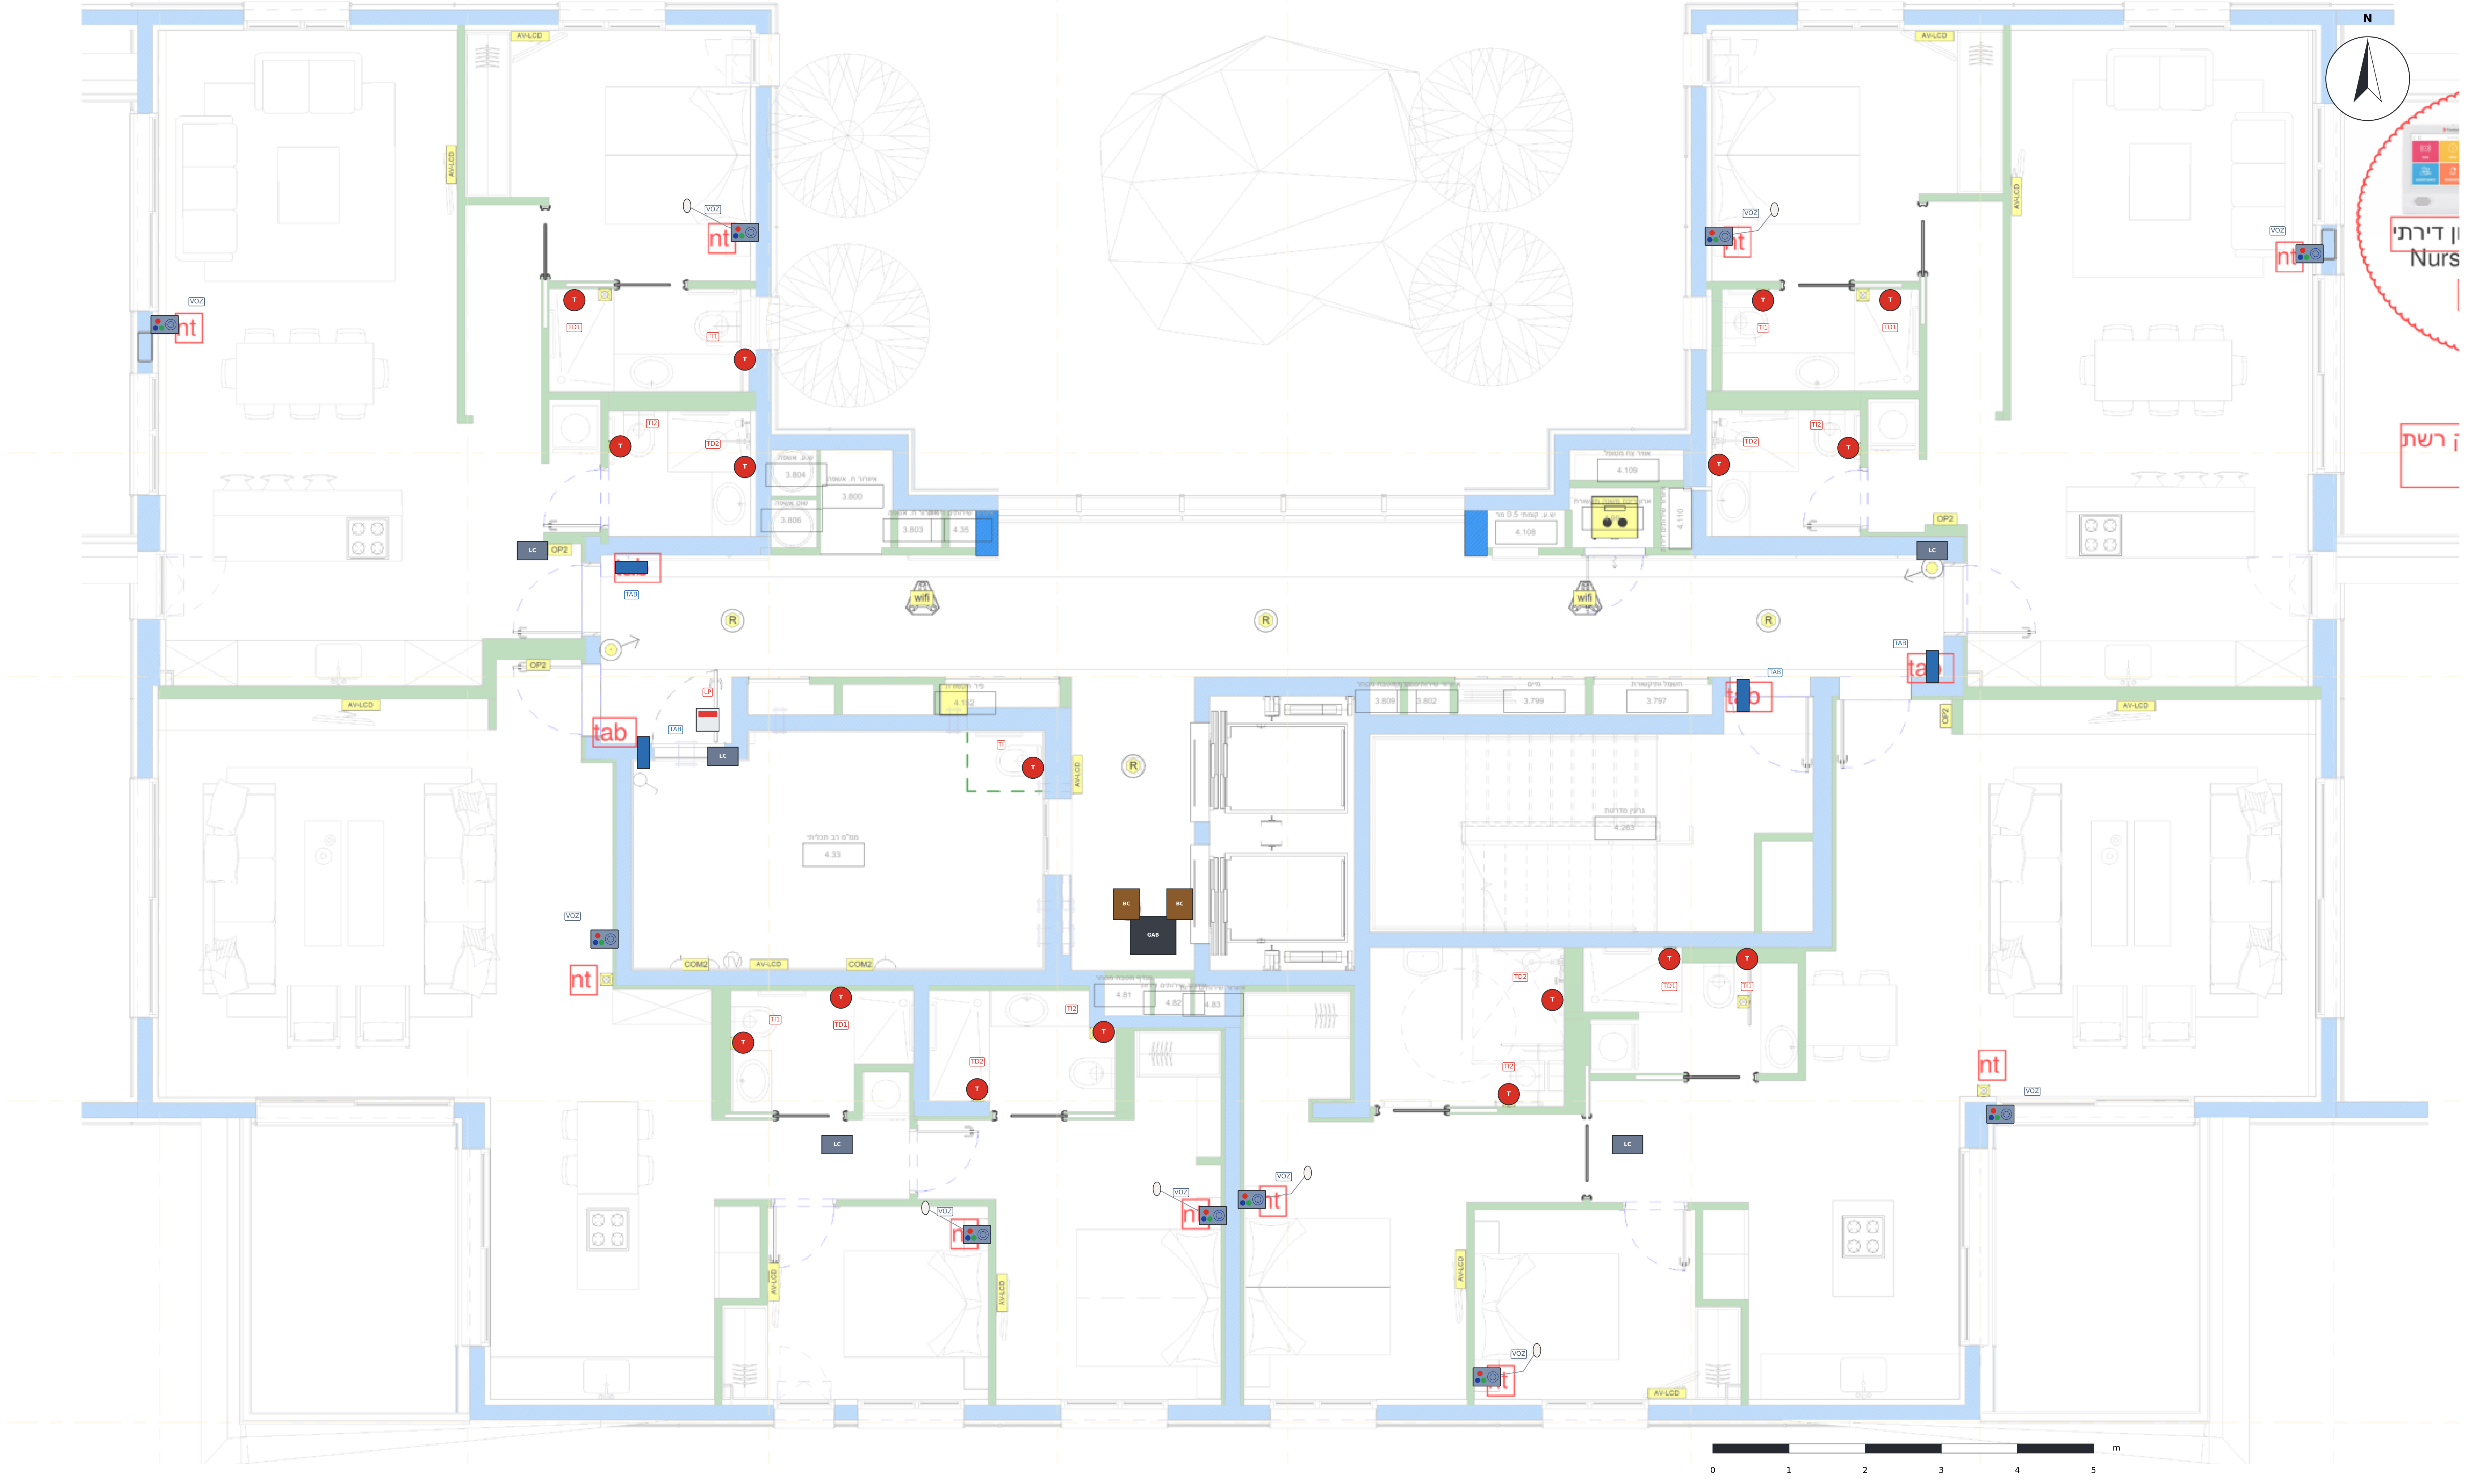

## NOTAS · NOTES

1. Fondo: plano IT L2 del cliente con sus marcas en rojo: «nt» = panel con voz y «tab» = tablet de la puerta.
2. Encima, en color: los equipos de esta propuesta. Cada panel y cada tablet está donde el cliente lo marcó.
3. Los cuadrados amarillos ⊠ de los baños del plano L2 son los tiradores (inodoro y ducha).
4. Las 4 tablets quedan en el lobby, junto a la puerta de cada departamento, como en las marcas «tab».
5. El plano L2 y el L5 (base de esta propuesta) tienen la misma estructura; L5 es el piso tipo de los pisos 1 a 8.

## EQUIPOS · DEVICES · דויצ

- TAB · Tablet de la puerta (iPad / Android) – llamada y voz, h 1,40 m
  Door tablet – call and voice · רובידו האירק – הסינכב טלבאט
- VOZ · Panel con voz y botones ACE82182451 – salón y dormitorios, h 1,20–1,30 m
  Voice panel with buttons – living room and bedrooms · הניש ירדחו ןולס – םינצחל םע ילוק לנפ
- Pera de llamada junto a la cama (en los dormitorios)
  Call pear next to the bed (bedrooms) · הטימה דיל האירק סגא
- TI / TD · Tirador de baño ACE40320303W – inodoro y ducha, h 1,85 m
  Pull-cord – toilet and shower, h 1.85 m · משחת הבל – אסלה ומקלחת, גובה 1.85 מ'
- LP · Luz de pasillo ACE41020309 – sobre la puerta de cada baño público
  Corridor light – above each public toilet door · םיירוביצ םיתוריש לכ תלד לעמ – ןורדסמ תרונמ

שירותים קריאת אחות

Tirador de baño

טבלט אנדרואיד קריאת אחות

Tablet en la puerta (iPad / Android)

מנורה קריאת אחות

Luz de pasillo

פנל קריאת אחות

Panel con voz y botones

**MIGDALEI YAM A TIJON · VIVIENDA TUTELADA**

Llamada de enfermería – PB + 8 pisos · 32 departamentos

Sistema: ACE BG · Advantecnia      Elaboró: Telab International

### MARCAS DEL CLIENTE (PLANO L2) Y PROPUESTA

Client marks (plan L2) and proposal

| ESCALA · SCALE | FECHA · DATE | REV | LÁMINA |
|---|---|---|---|
| **1:60** | **15/10/2026** | **B** | **03** |

Base: plano del arquitecto L5 (Massad Oz / Triplet) · cotas en metros

Formato A1 · Rev. B – sobre plano real

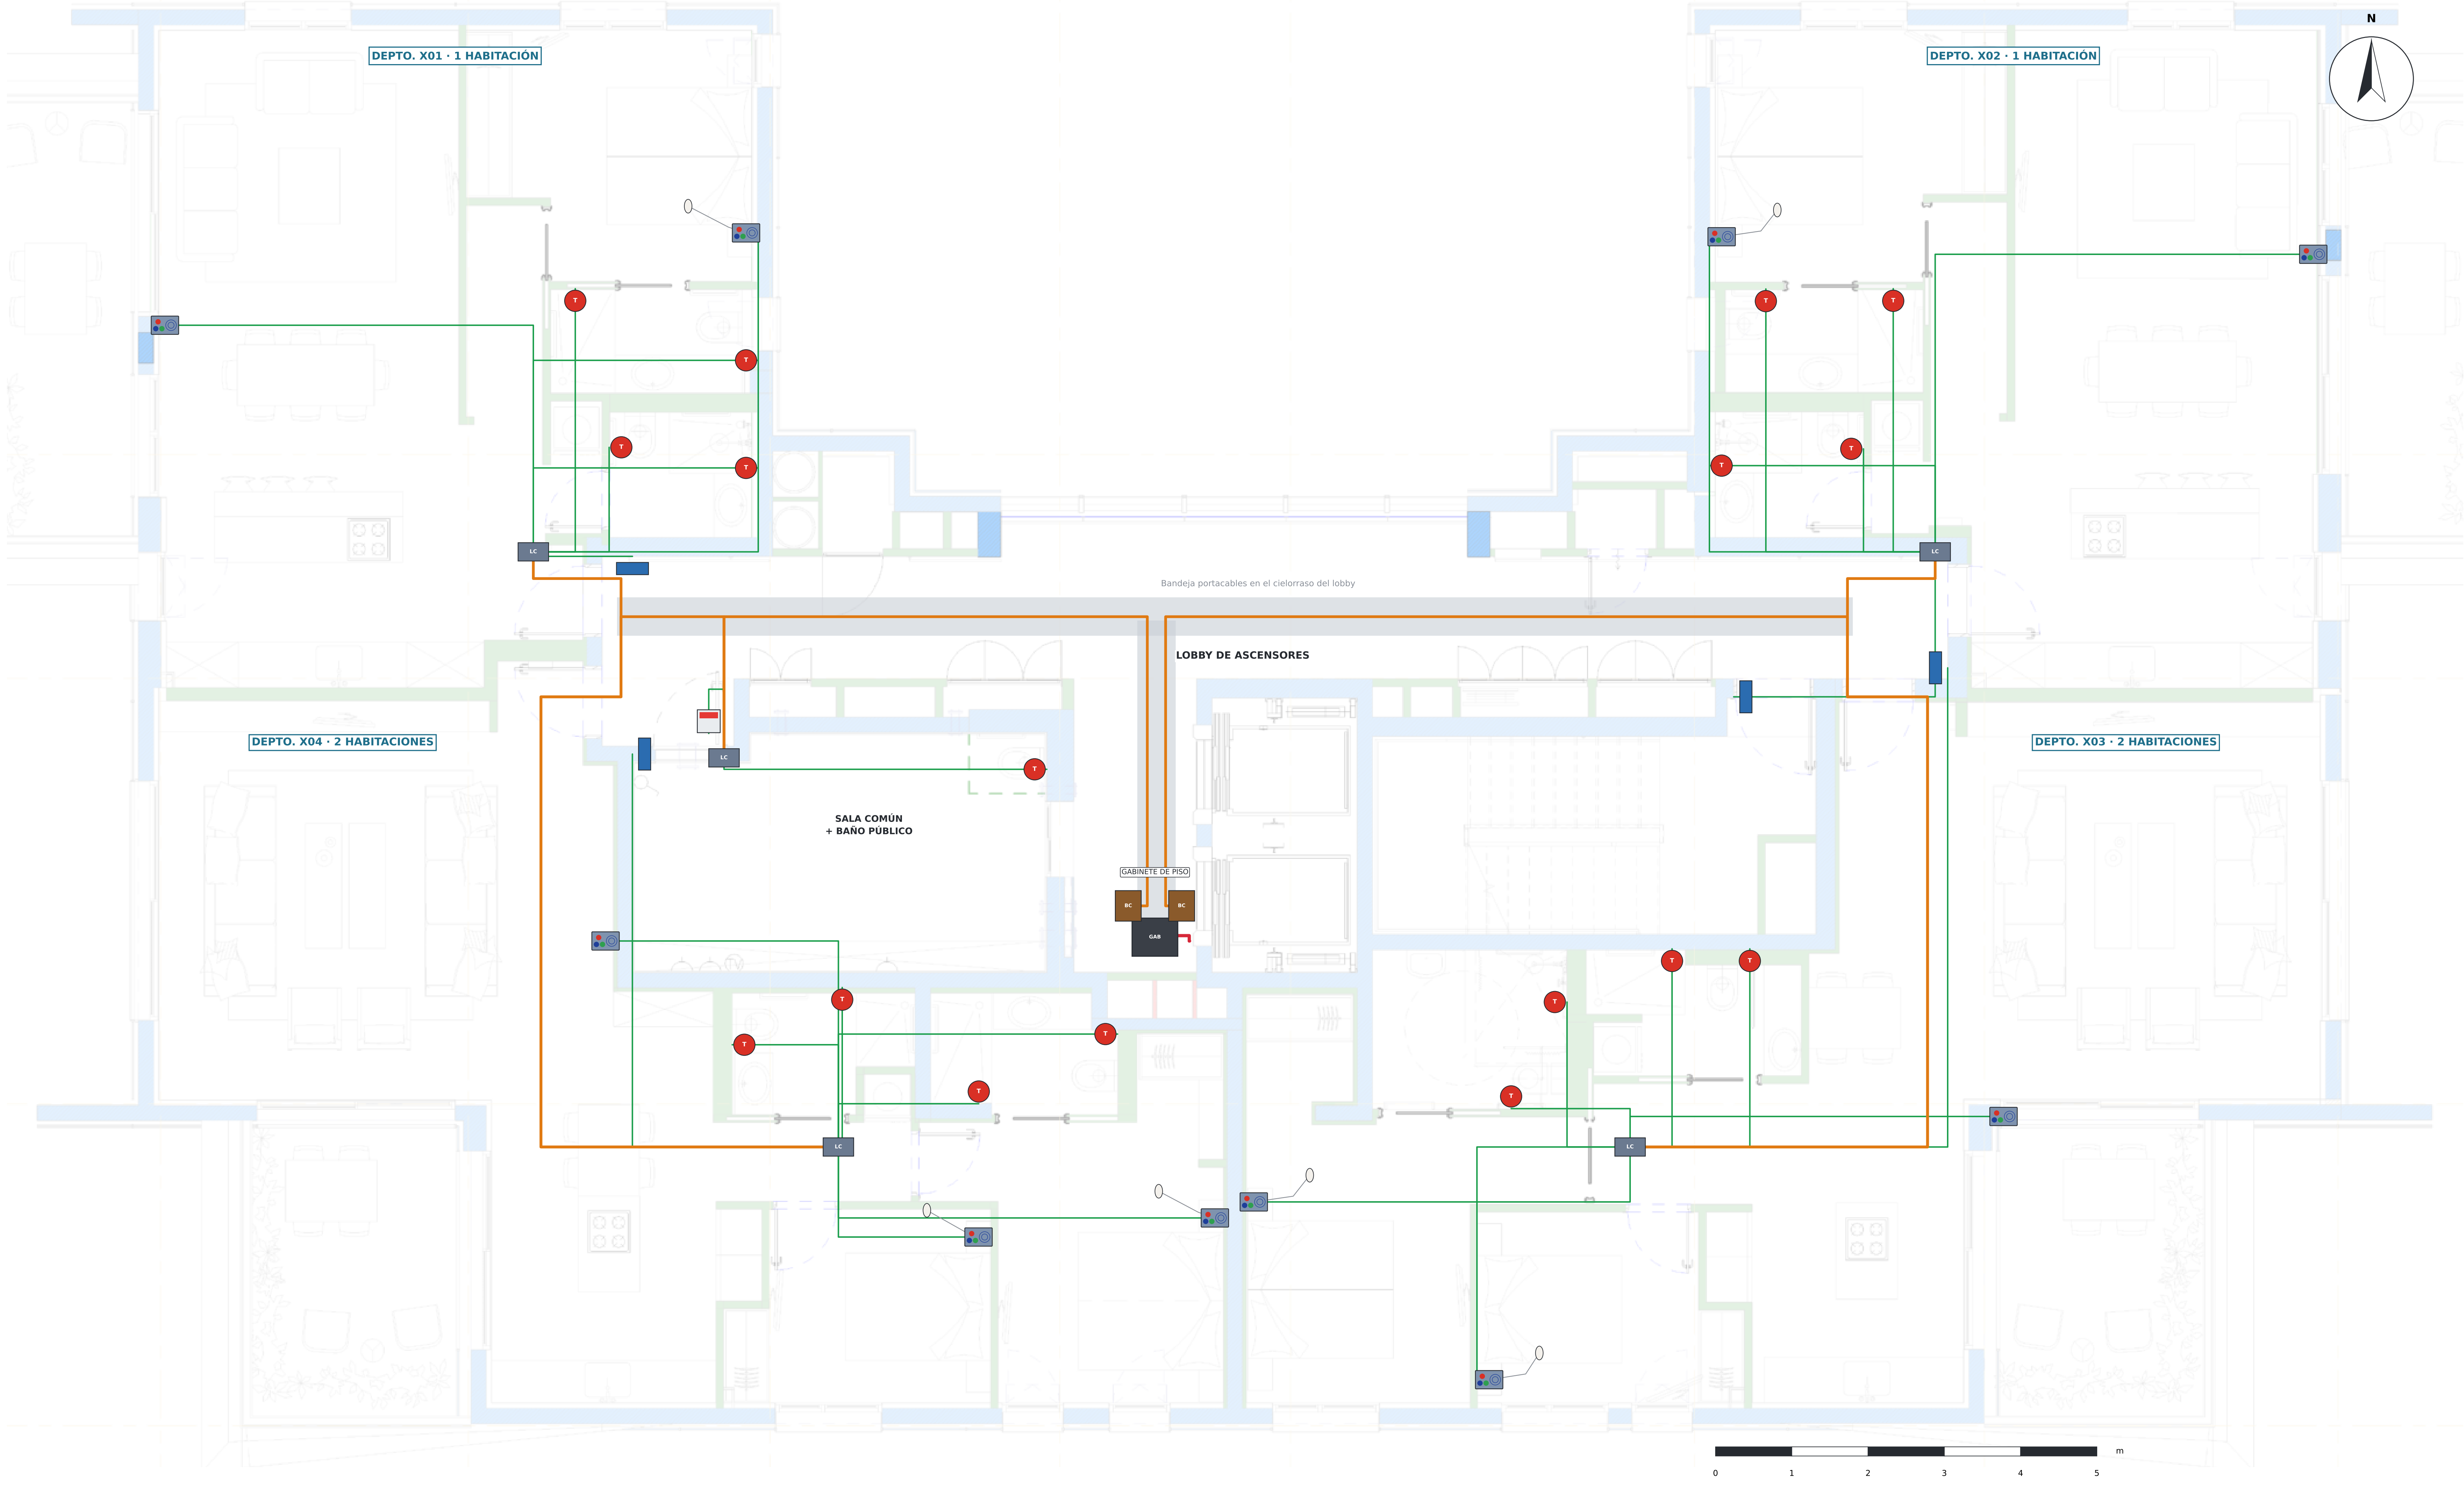
DEPTO. X01 · 1 HABITACIÓN
DEPTO. X02 · 1 HABITACIÓN
DEPTO. X04 · 2 HABITACIONES
DEPTO. X03 · 2 HABITACIONES
N
Bandeja portacables en el cielorraso del lobby
LOBBY DE ASCENSORES
SALA COMÚN
+ BAÑO PÚBLICO
GABINETE DE PISO
BC
BC
GAB
LC
T
0
1
2
3
4
5
m

## CABLEADO · WIRING · חיווט

🟩 Cat6 radial: cada equipo → LCom de su departamento
Cat6 radial: each device → apartment LCom · Cat6 רדיאלי: כל התקן ← LCom של הדירה

🟧 Cat6 / Cat7 cadena: LCom → LCom → BoxCom del techo
Cat6 / Cat7 chain: LCom → LCom → BoxCom · Cat6 / Cat7 שרשרת: LCom ← LCom ← BoxCom

🟥 Cat6A / Cat7 red: BoxCom → switch PoE → montante → servidor PB
Cat6A / Cat7 network: BoxCom → switch → riser → GF server · Cat6A / Cat7 רשת: BoxCom ← מתג ← עמוד ← שרת

## LONGITUDES DEL PISO TIPO (sin reserva)

| | | |
|---|---|---|
| 🟩 | Cat6 radial dentro de los departamentos | **183 m** |
| 🟧 | Cat6 / Cat7 cadena LCom → BoxCom | **80 m** |
| 🟥 | Cat6A / Cat7 gabinete y montante | **7 m** |

## NOTAS · NOTES

1. Cada equipo va radial (Cat6) al LCom de su departamento, en el cielorraso del hall.
2. Los LCom se encadenan por la bandeja del lobby hasta los BoxCom del techo, junto al gabinete: x01 → x04 → sala común → BoxCom 1 · x02 → x03 → BoxCom 2.
3. Los BoxCom bajan al switch PoE del gabinete; el switch sube por el montante Cat6A / Cat7 hasta el servidor de PB.
4. Todo es PoE: no hace falta 230 V en los equipos de los departamentos.

## NOTAS · NOTES

1. Base: plano de arquitectura L5 (piso tipo) – los 8 pisos son iguales: 4 departamentos por piso, 32 en total.
2. Departamentos x01 y x02: 1 habitación, salón con cocina y 2 baños. Departamentos x03 y x04: 2 habitaciones y 2 baños.
3. Tablet en la puerta de cada departamento (iPad / Android) para llamar y hablar con enfermería.
4. Panel con voz y botones (ACE82182451) en el salón y en cada dormitorio; en el dormitorio, con pera junto a la cama.
5. Tiradores de baño (ACE40320303W) en el inodoro y en la ducha de todos los baños, a 1,85 m.
6. Baño público por piso en la sala común: tirador + luz de pasillo sobre la puerta. Con los 2 de PB suman 10 baños públicos.
7. Gabinete de piso junto a los ascensores con el switch PoE D-Link DES-1210-28P; los 2 BoxCom van en el techo, al lado.
8. Ubicaciones según las marcas del cliente en el plano L2 (nt = panel con voz, tab = tablet): ver lámina 03.

**MIGDALEI YAM A TIJON · VIVIENDA TUTELADA**
Llamada de enfermería – PB + 8 pisos · 32 departamentos
Sistema: ACE BG · Advantecnia    Elaboró: Telab International

# PISO TIPO P1–P8 · CABLEADO

Typical floor F1–F8 · wiring

| ESCALA · SCALE | FECHA · DATE | REV | LÁMINA |
|---|---|---|---|
| **1:60** | **15/10/2026** | **B** | **04** |

Base: plano del arquitecto L5 (Massad Oz / Triplet) · cotas en metros
Formato A1 · Rev. B – sobre plano real

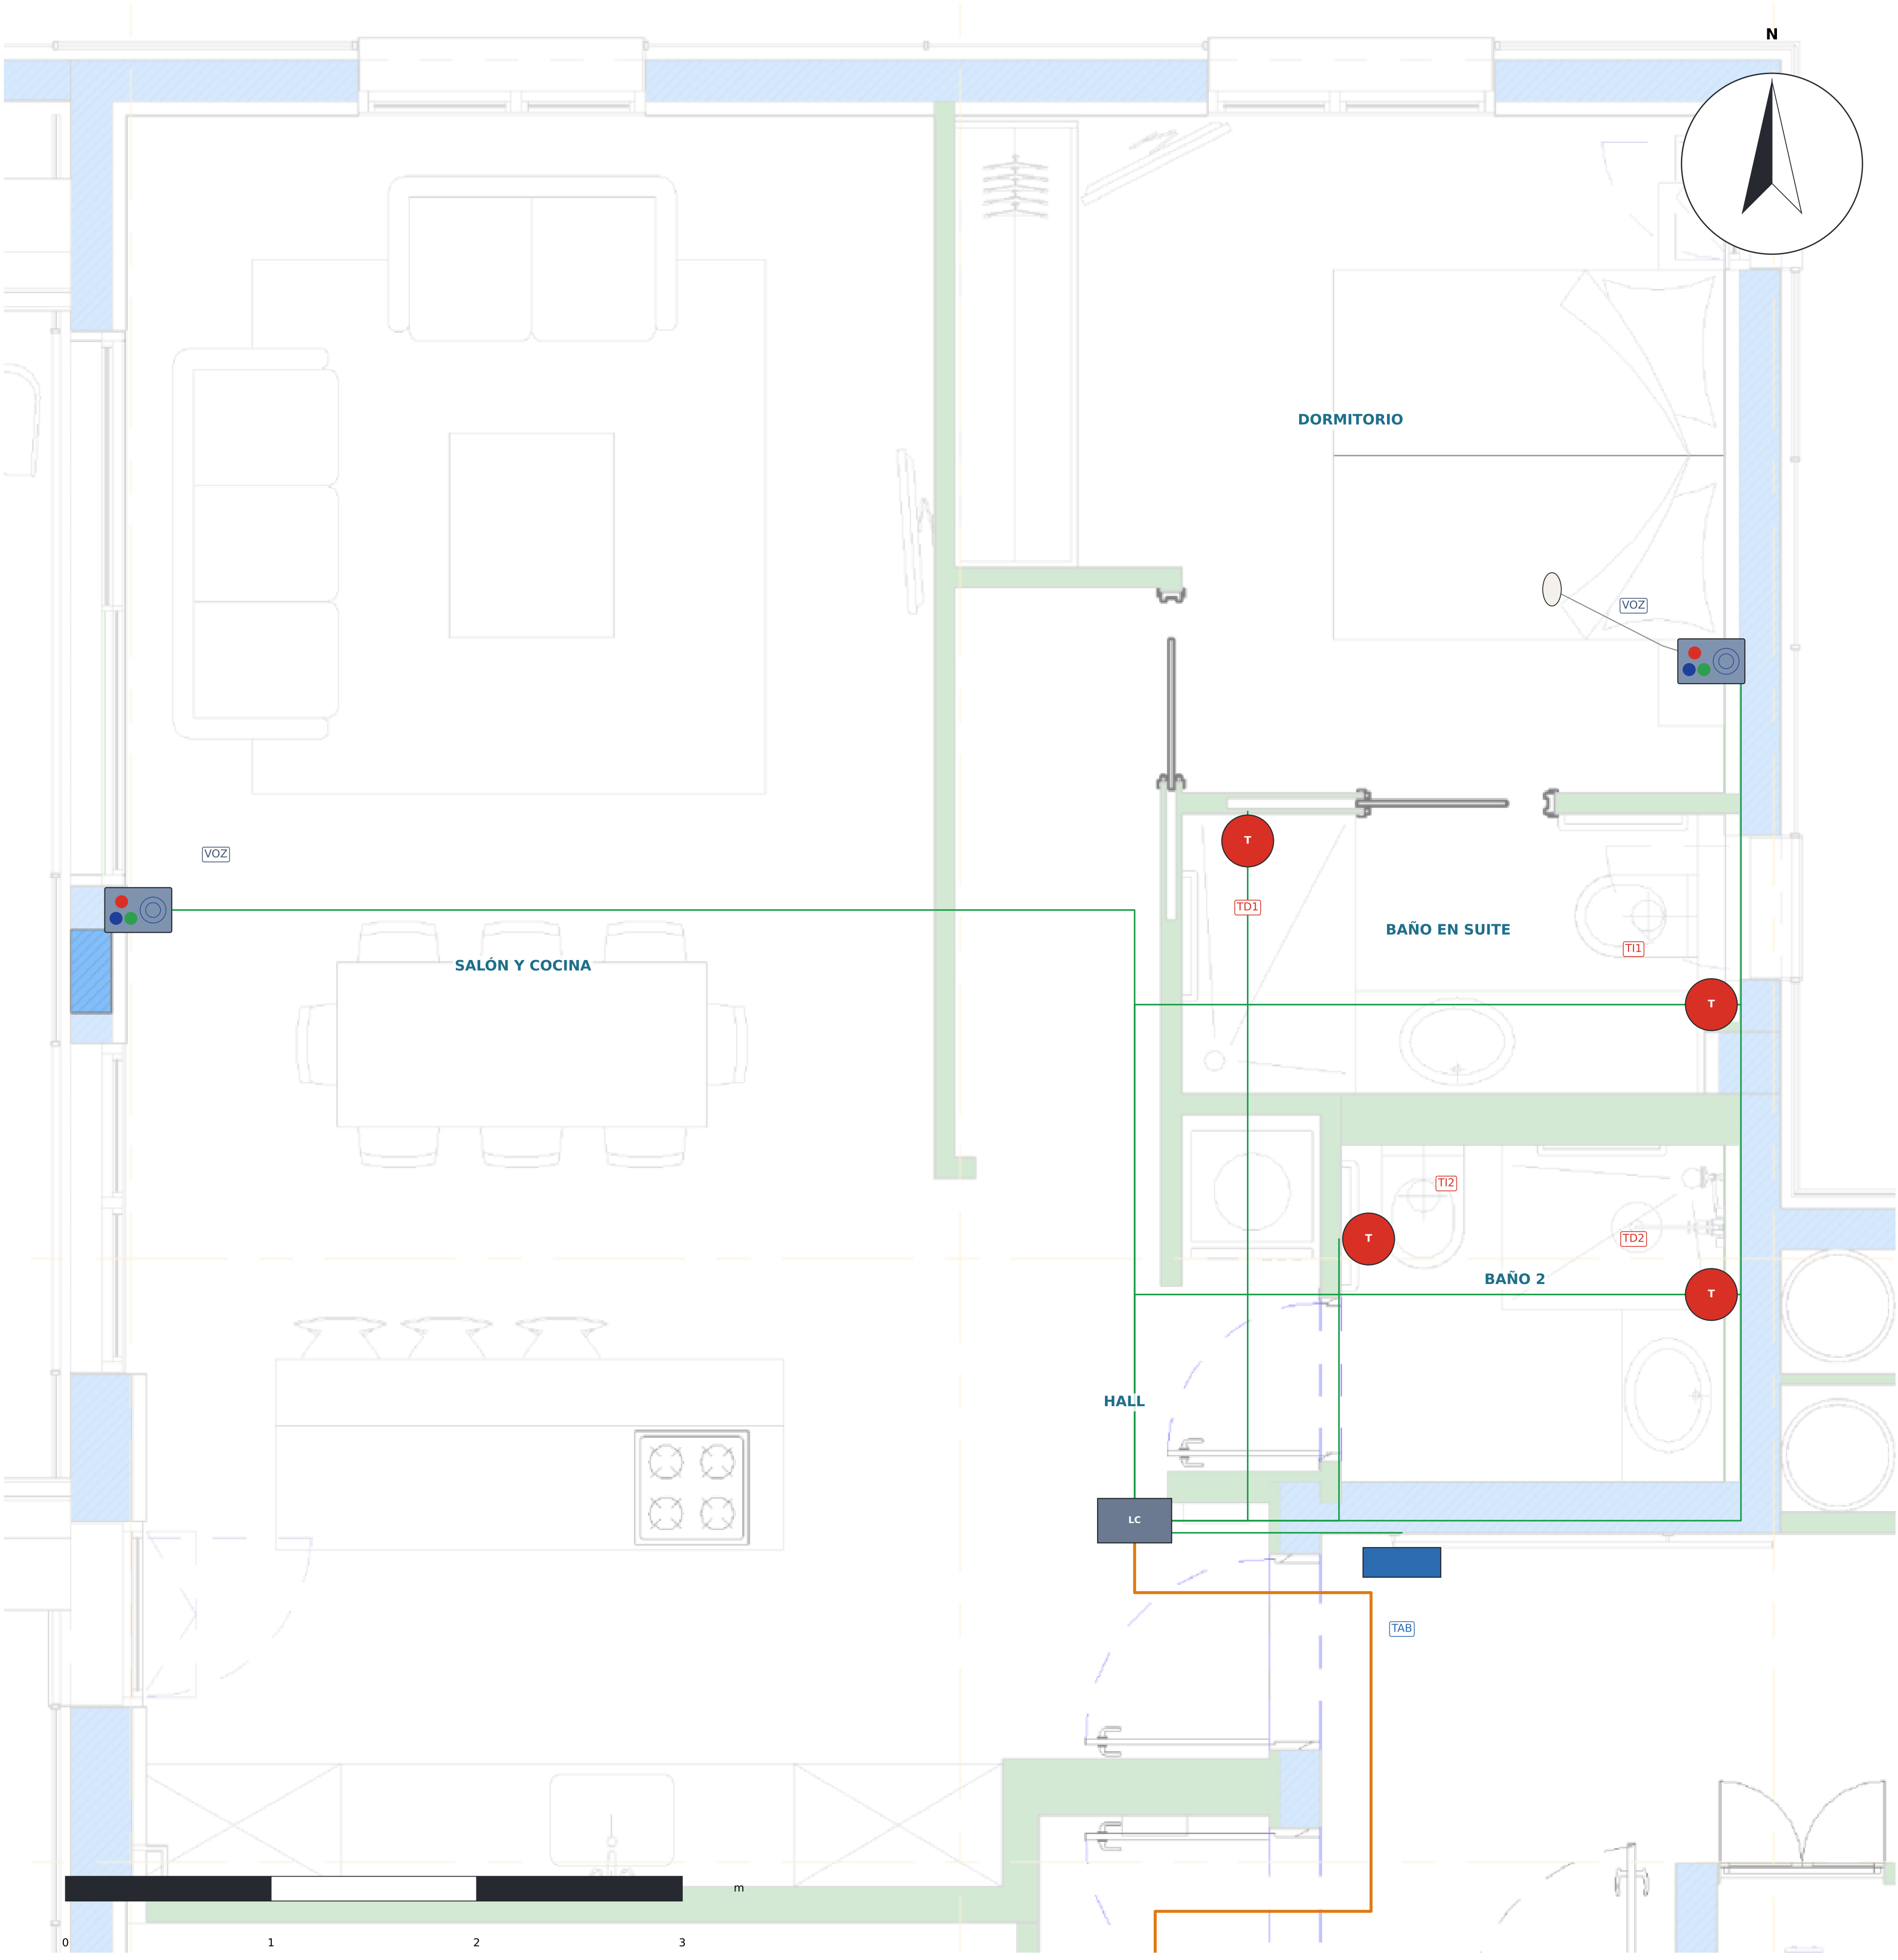

**EQUIPOS DEL DEPARTAMENTO**

| ID | Equipo | Local | Altura |
|---|---|---|---|
| TAB | Tablet de la puerta | Hall | 1,40 m |
| VOZ-S | Panel voz y botones | Salón y cocina | 1,30 m |
| VOZ-D | Panel voz y botones + pera | Dormitorio | 1,20 m |
| TI1 | Tirador de baño | Baño en suite | 1,85 m |
| TD1 | Tirador de baño | Baño en suite | 1,85 m |
| TI2 | Tirador de baño | Baño 2 | 1,85 m |
| TD2 | Tirador de baño | Baño 2 | 1,85 m |
| LCOM | LCom ACE71610003 | Hall | 2,55 m |

**SÍMBOLOS · SYMBOLS · סמלים**

| | |
|---|---|
| 🟦 | TAB · Tablet de la puerta (iPad / Android) – llamada y voz, h 1,40 m<br>Door tablet – call and voice · טאבלט בכניסה – קריאה ודיבור |
| ● | VOZ · Panel con voz y botones ACE82182451 – salón y dormitorios, h 1,20–1,30 m<br>Voice panel with buttons – living room and bedrooms · פנל קולי עם לחצנים – סלון וחדרי שינה |
| ○ | Pera de llamada junto a la cama (en los dormitorios)<br>Call pear next to the bed (bedrooms) · אגס קריאה ליד המיטה |
| T | TI / TD · Tirador de baño ACE40320303W – inodoro y ducha, h 1,85 m<br>Pull-cord – toilet and shower, h 1.85 m · משיכת חבל – אסלה ומקלחת, גובה 1.85 מ' |
| 🟥 | LP · Luz de pasillo ACE41020309 – sobre la puerta de cada baño público<br>Corridor light – above each public toilet door · מנורת מסדרון – מעל דלת כל שירותים ציבוריים |
| LC | LC · LCom ACE71610003 – concentrador del departamento (cielorraso)<br>LCom – apartment hub (ceiling) · LCom – מרכז הדירה (תקרה) |
| BC | BC · BoxCom ACE70810000 – concentrador en bus de varios deptos. (techo)<br>BoxCom – bus hub for several apartments (ceiling) · BoxCom – מרכז באס לכמה דירות (תקרה) |

**NOTAS · NOTES**

1. El departamento x02 es el espejo del x01 (misma dotación).
2. Tablet en el lobby, junto a la puerta de entrada (marca «tab» del cliente).
3. Panel con voz en el salón y en el dormitorio (con pera junto a la cama).
4. 2 baños: tirador en el inodoro y en la ducha de cada uno (4 tiradores).
5. Todo va radial en Cat6 al LCom del hall.

שירותים קריאת אחות

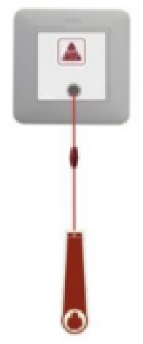

Tirador de baño

טבלט אנדרואיד קריאת אחות

Advantecnia
Llamada de enfermera
Hospital
Salud y bienestar

Tablet en la puerta (iPad / Android)

מנורה קריאת אחות

Luz de pasillo

פנל קריאת אחות

Panel con voz y botones

**MIGDALEI YAM A TIJON · VIVIENDA TUTELADA**

Llamada de enfermería – PB + 8 pisos · 32 departamentos

Sistema: ACE BG · Advantecnia    Elaboró: Telab International

**DEPTO. 1 HABITACIÓN (x01 / x02)**

1-bedroom apartment (x01 / x02)

| ESCALA · SCALE | FECHA · DATE | REV | LÁMINA |
|---|---|---|---|
| **1:30** | **15/10/2026** | **B** | **05** |

Base: plano del arquitecto L5 (Massad Oz / Triplet) · cotas en metros

Formato A1 · Rev. B – sobre plano real

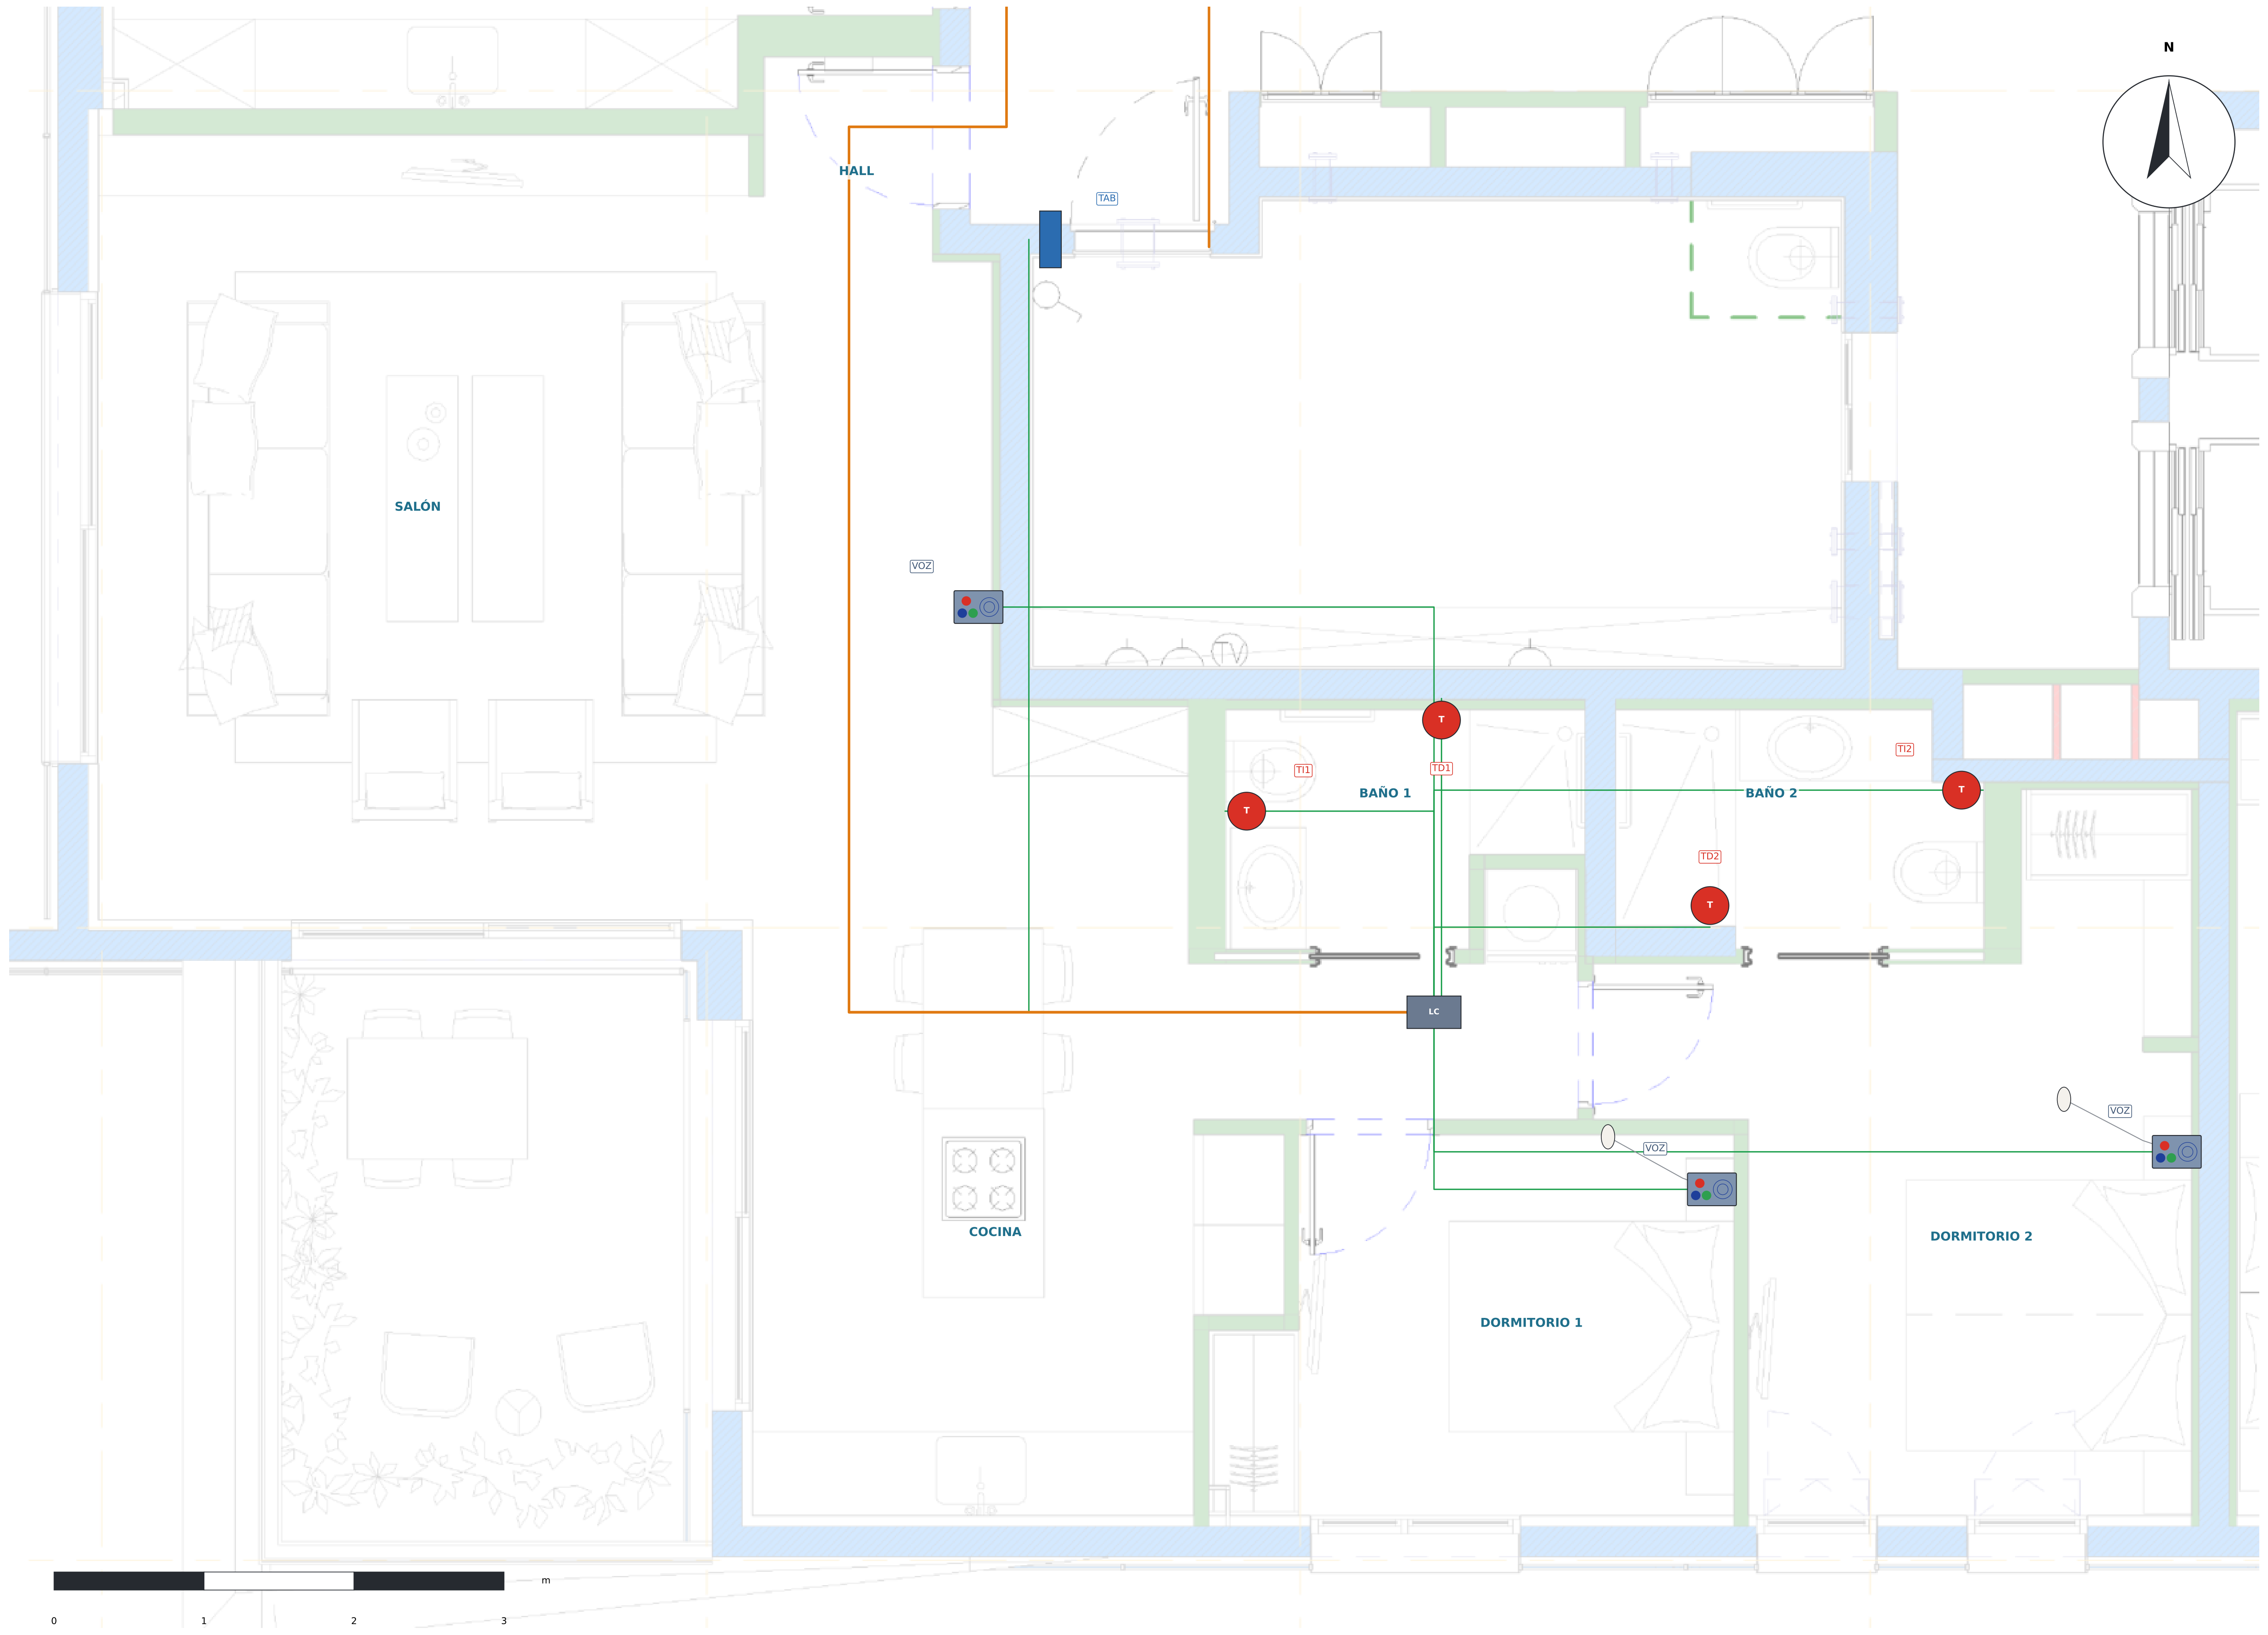

## EQUIPOS DEL DEPARTAMENTO

| ID | Equipo | Local | Altura |
|---|---|---|---|
| TAB | Tablet de la puerta | Hall | 1,40 m |
| VOZ-S | Panel voz y botones | Salón | 1,30 m |
| VOZ-D1 | Panel voz y botones + pera | Dormitorio 1 | 1,20 m |
| VOZ-D2 | Panel voz y botones + pera | Dormitorio 2 | 1,20 m |
| TI1 | Tirador de baño | Baño 1 | 1,85 m |
| TD1 | Tirador de baño | Baño 1 | 1,85 m |
| TI2 | Tirador de baño | Baño 2 | 1,85 m |
| TD2 | Tirador de baño | Baño 2 | 1,85 m |
| LCOM | LCom ACE71610003 | Hall | 2,55 m |

## SÍMBOLOS · SYMBOLS · םילמס

| | |
|---|---|
| 🟦 | TAB · Tablet de la puerta (iPad / Android) – llamada y voz, h 1,40 m<br>Door tablet – call and voice · רובידו האירק – הסינכב טלבאט |
| ▣ | VOZ · Panel con voz y botones ACE82182451 – salón y dormitorios, h 1,20–1,30 m<br>Voice panel with buttons – living room and bedrooms · הניש ירדחו ןולס – מינצחל םע ילוק לנפ |
| ⬯ | Pera de llamada junto a la cama (en los dormitorios)<br>Call pear next to the bed (bedrooms) · הטימה דיל האירק סגא |
| T | TI / TD · Tirador de baño ACE40320303W – inodoro y ducha, h 1,85 m<br>Pull-cord – toilet and shower, h 1.85 m · 'מ 1.85 הבוג ,תחלקמו הלסא – לבח תכישמ |
| ▭ | LP · Luz de pasillo ACE41020309 – sobre la puerta de cada baño público<br>Corridor light – above each public toilet door · םיירוביצ םיתורש לכ תלד לעמ – ןורדסמ תרונמ |
| LC | LC · LCom ACE71610003 – concentrador del departamento (cielorraso)<br>LCom – apartment hub (ceiling) · LCom – הרידה זכרמ (הרקת) |
| BC | BC · BoxCom ACE70810000 – concentrador en bus de varios deptos. (techo)<br>BoxCom – bus hub for several apartments (ceiling) · BoxCom – תוריד המכל סאב זכרמ (הרקת) |

## NOTAS · NOTES

1. El departamento x03 tiene la misma dotación (baños con otra distribución).
2. Tablet en el lobby, junto a la puerta de entrada (marca «tab» del cliente).
3. Panel con voz en el salón y en los 2 dormitorios (con pera junto a la cama).
4. 2 baños: tirador en el inodoro y en la ducha de cada uno (4 tiradores).
5. Todo va radial en Cat6 al LCom del pasillo de los dormitorios.

שירותים קריאת אחות

Tirador de baño

טבלט אנדרואיד קריאת אחות
Advantecnia
Llamada de enfermera
Hospital

Tablet en la puerta (iPad / Android)

מנורה קריאת אחות

Luz de pasillo

פנל קריאת אחות

Panel con voz y botones

**MIGDALEI YAM A TIJON · VIVIENDA TUTELADA**

Llamada de enfermería – PB + 8 pisos · 32 departamentos

Sistema: ACE BG · Advantecnia     Elaboró: Telab International

## DEPTO. 2 HABITACIONES (x04 / x03)

2-bedroom apartment (x04 / x03)

| ESCALA · SCALE | FECHA · DATE | REV | LÁMINA |
|---|---|---|---|
| **1:35** | **15/10/2026** | **B** | **06** |

Base: plano del arquitecto L5 (Massad Oz / Triplet) · cotas en metros

Formato A1 · Rev. B – sobre plano real

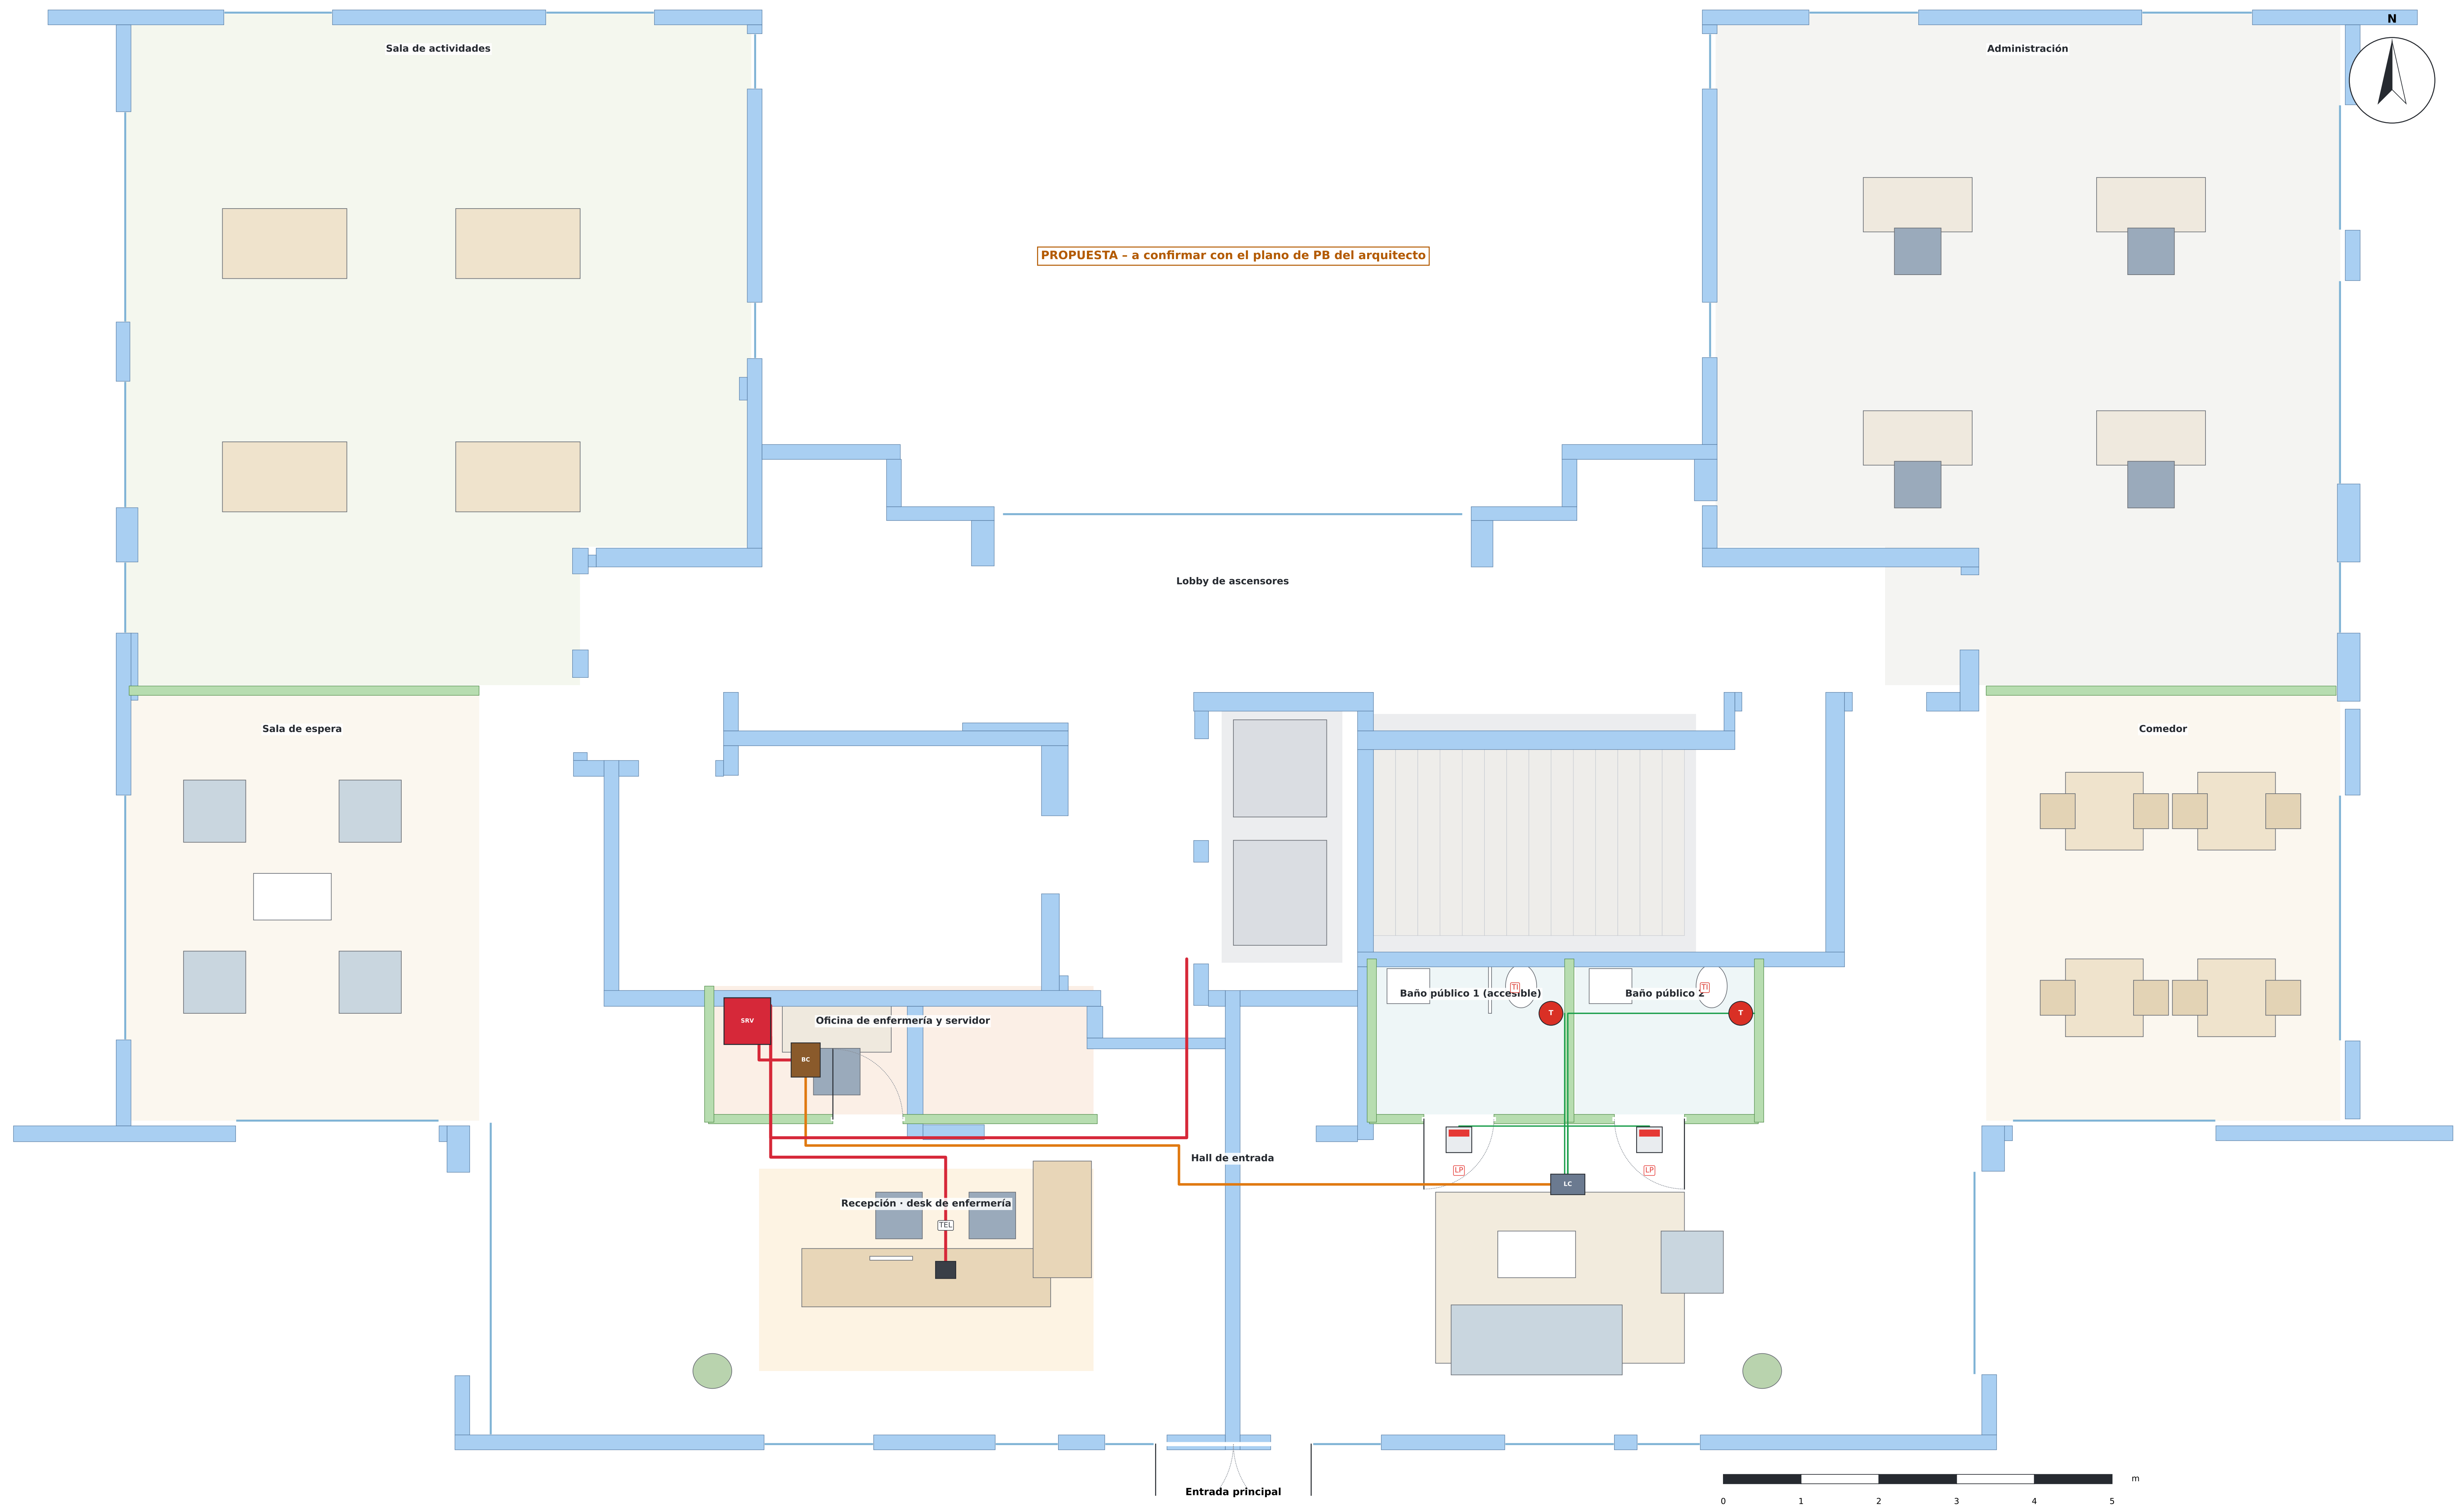
N
Sala de actividades
Administración
Lobby de ascensores
Sala de espera
Comedor
Oficina de enfermería y servidor
SRV
BC
Baño público 1 (accesible)
Baño público 2
TI
T
LP
LC
Hall de entrada
Recepción · desk de enfermería
TEL
Entrada principal
0
1
2
3
4
5
m

PROPUESTA – a confirmar con el plano de PB del arquitecto

### DETALLE · RECEPCIÓN Y DESK DE ENFERMERÍA (1:40)

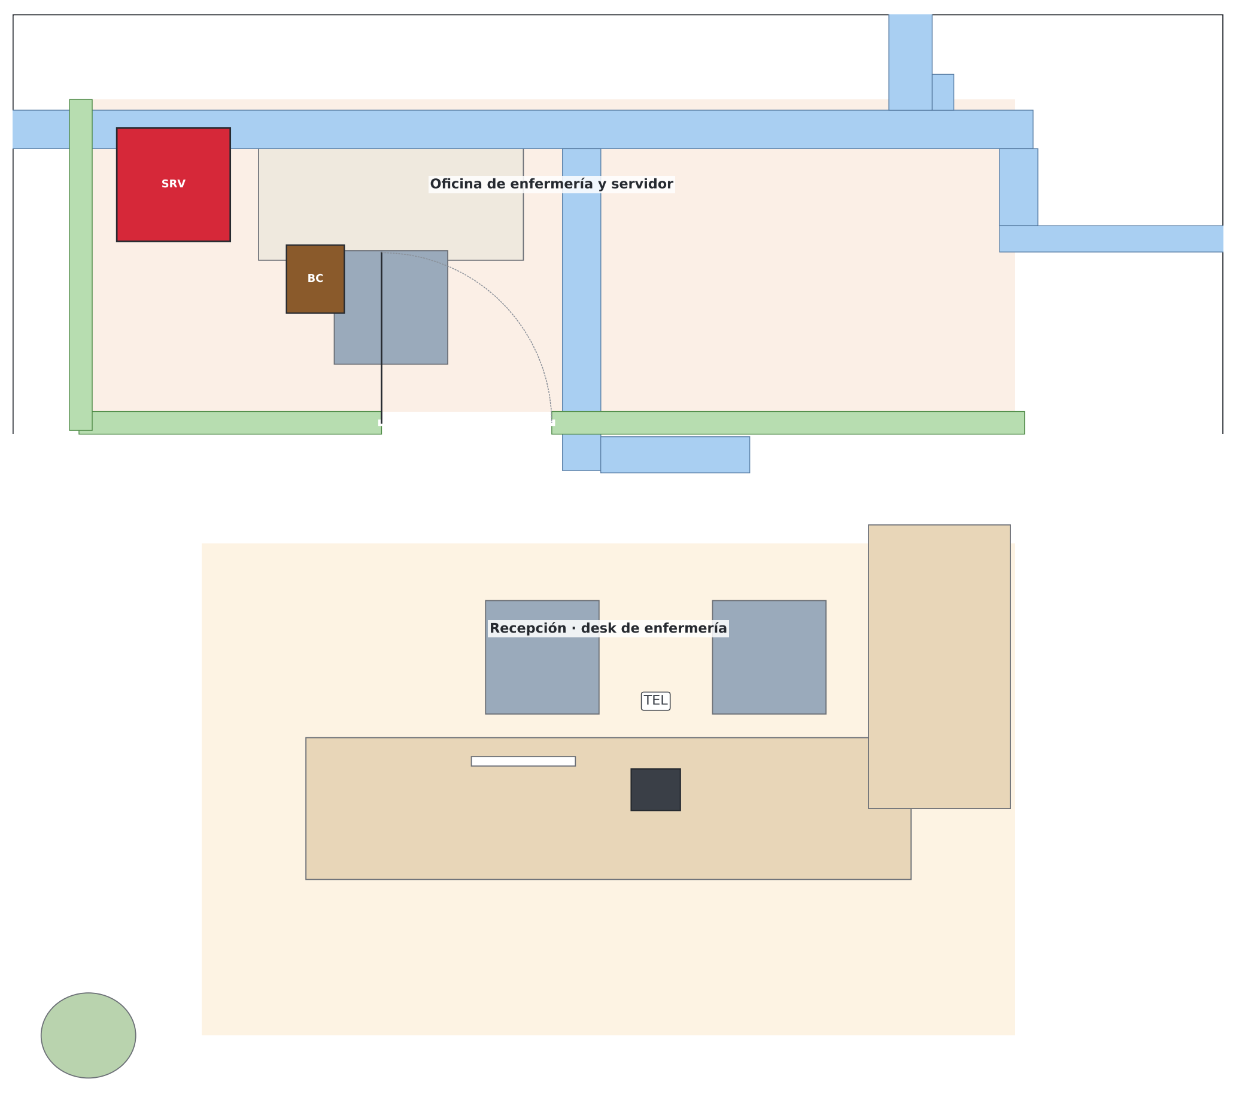
SRV
BC
Oficina de enfermería y servidor
Recepción · desk de enfermería
TEL

### NOTAS · NOTES

1. Desk de enfermería en la recepción, frente a la entrada y a los ascensores.
2. Sobre el desk: teléfono Grandstream Android, conectado directo al switch PoE. Cada llamada se ve con su color.
3. Detrás del desk: oficina con el gabinete principal: servidor Buslogic Premium y switch PoE D-Link. BoxCom de PB en el techo.
4. 2 baños públicos en PB: tirador junto al inodoro y luz de pasillo sobre cada puerta.
5. El montante de los 8 pisos baja por el núcleo hasta el gabinete principal.
6. Distribución de PB propuesta: se ajusta cuando llegue el plano del arquitecto.

### SÍMBOLOS · SYMBOLS · סמלים

| | |
|---|---|
| T | TI / TD · Tirador de baño ACE40320303W – inodoro y ducha, h 1,85 m<br>Pull-cord – toilet and shower, h 1.85 m · משיכת חבל – אסלה ומקלחת, גובה 1.85 מ' |
| LC | LC · LCom ACE71610003 – concentrador del departamento (cielorraso)<br>LCom – apartment hub (ceiling) · LCom – מרכז הדירה (תקרה) |
| SRV | SRV · Gabinete PB: servidor Buslogic Premium + switch PoE D-Link<br>GF rack: Buslogic Premium server + D-Link PoE switch · ארון קרקע: שרת Buslogic Premium + מתג PoE D-Link |
| 🟥 | LP · Luz de pasillo ACE41020309 – sobre la puerta de cada baño público<br>Corridor light – above each public toilet door · מנורת מסדרון – מעל דלת כל שירותים ציבוריים |
| TEL | TEL · Teléfono Grandstream Android – PoE directo al switch<br>Grandstream Android phone – PoE straight to the switch · טלפון Grandstream אנדרואיד – PoE ישירות למתג |
| BC | BC · BoxCom ACE70810000 – concentrador en bus de varios deptos. (techo)<br>BoxCom – bus hub for several apartments (ceiling) · BoxCom – מרכז באס לכמה דירות (תקרה) |

### TELÉFONO DEL DESK – QUÉ COLOR SE VE

| | | |
|---|---|---|
| 🟥 | Alarma (tirador / SOS) | **Rojo** |
| 🟩 | Botón verde 1 vez: presencia | **Verde** |
| ⬜ | Botón verde otra vez: cancela llamada o alarma | **Se borra** |
| 🟦 | Botón azul: llamada de médico (blue call) | **Azul** |
| 🟧 | Llamada de voz | **Amarillo / naranja** |

**MIGDALEI YAM A TIJON · VIVIENDA TUTELADA**

Llamada de enfermería – PB + 8 pisos · 32 departamentos

Sistema: ACE BG · Advantecnia  Elaboró: Telab International

## PLANTA BAJA · LOBBY Y DESK DE ENFERMERÍA

Ground floor · lobby and nurse desk

| ESCALA · SCALE | FECHA · DATE | REV | LÁMINA |
|---|---|---|---|
| **1:60** | **15/10/2026** | **B** | **07** |

Base: plano del arquitecto L5 (Massad Oz / Triplet) · cotas en metros

Formato A1 · Rev. B – sobre plano real

## A · EDIFICIO PB + 8 PISOS

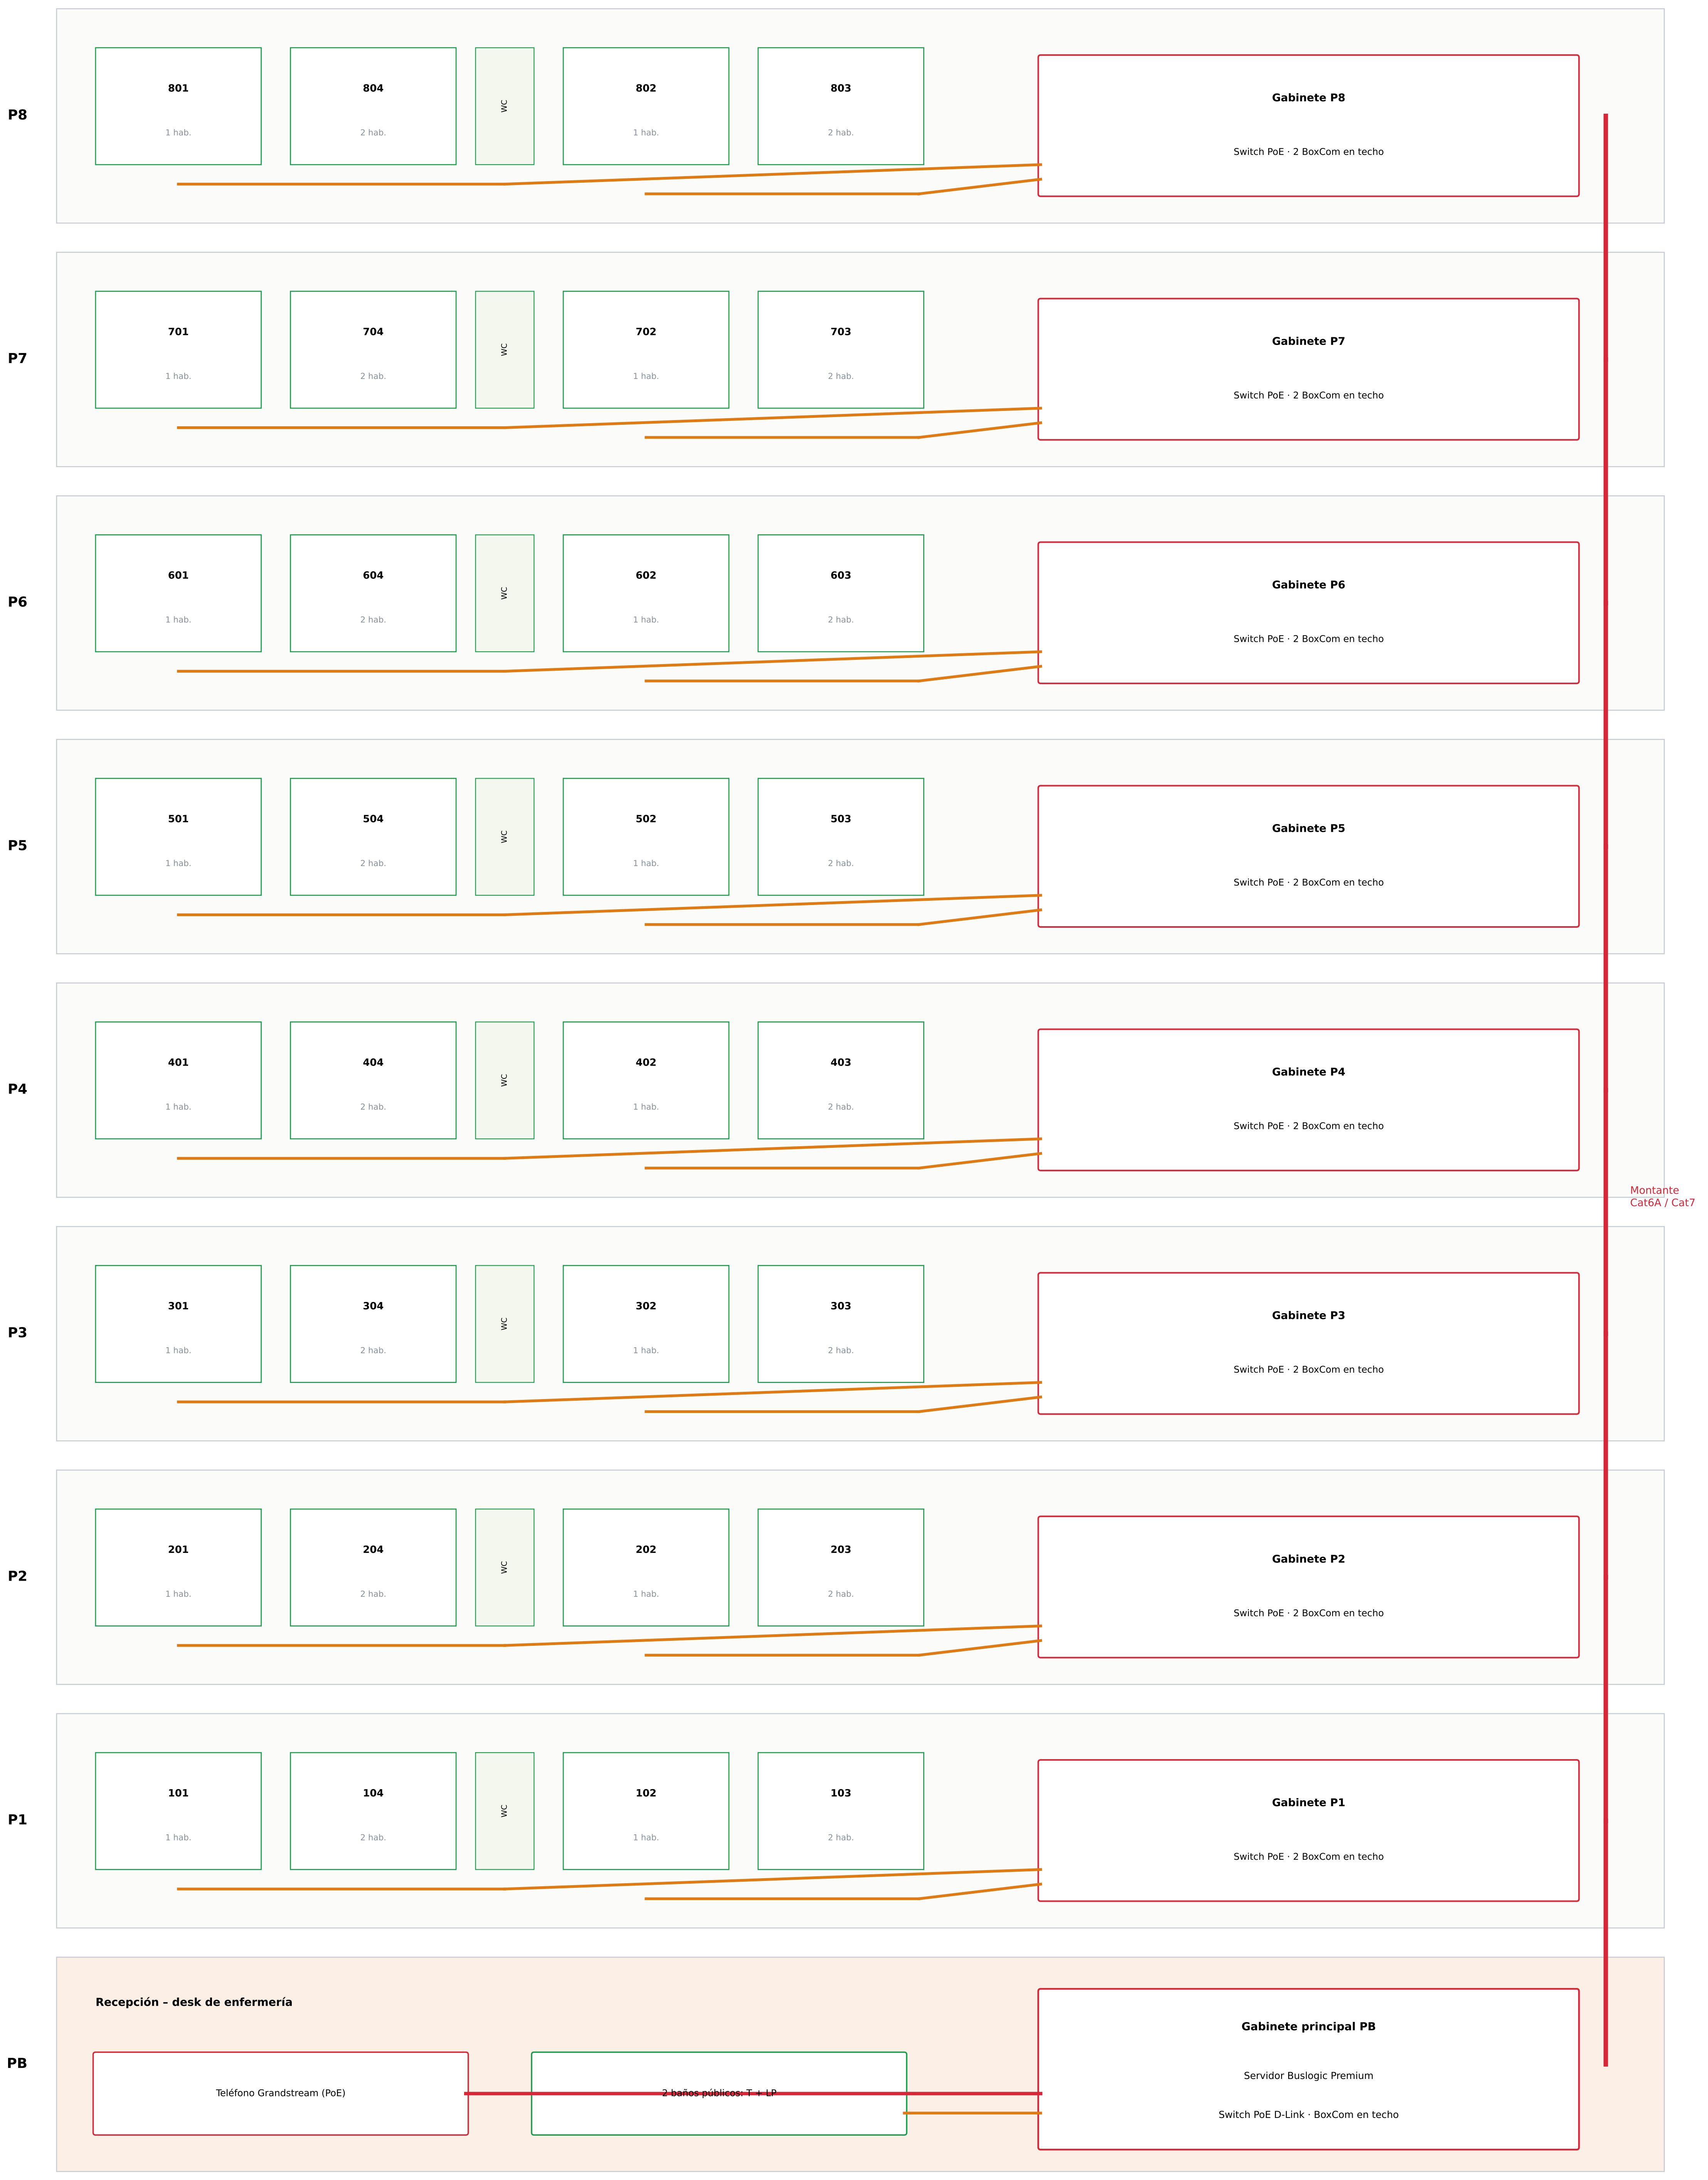
P8
801
1 hab.
804
2 hab.
WC
802
1 hab.
803
2 hab.
Gabinete P8
Switch PoE · 2 BoxCom en techo
P7
701
1 hab.
704
2 hab.
WC
702
1 hab.
703
2 hab.
Gabinete P7
Switch PoE · 2 BoxCom en techo
P6
601
1 hab.
604
2 hab.
WC
602
1 hab.
603
2 hab.
Gabinete P6
Switch PoE · 2 BoxCom en techo
P5
501
1 hab.
504
2 hab.
WC
502
1 hab.
503
2 hab.
Gabinete P5
Switch PoE · 2 BoxCom en techo
P4
401
1 hab.
404
2 hab.
WC
402
1 hab.
403
2 hab.
Gabinete P4
Switch PoE · 2 BoxCom en techo
Montante
Cat6A / Cat7
P3
301
1 hab.
304
2 hab.
WC
302
1 hab.
303
2 hab.
Gabinete P3
Switch PoE · 2 BoxCom en techo
P2
201
1 hab.
204
2 hab.
WC
202
1 hab.
203
2 hab.
Gabinete P2
Switch PoE · 2 BoxCom en techo
P1
101
1 hab.
104
2 hab.
WC
102
1 hab.
103
2 hab.
Gabinete P1
Switch PoE · 2 BoxCom en techo
PB
Recepción – desk de enfermería
Teléfono Grandstream (PoE)
2 baños públicos: T + LP
Gabinete principal PB
Servidor Buslogic Premium
Switch PoE D-Link · BoxCom en techo

## B · TOPOLOGÍA DE UN DEPARTAMENTO

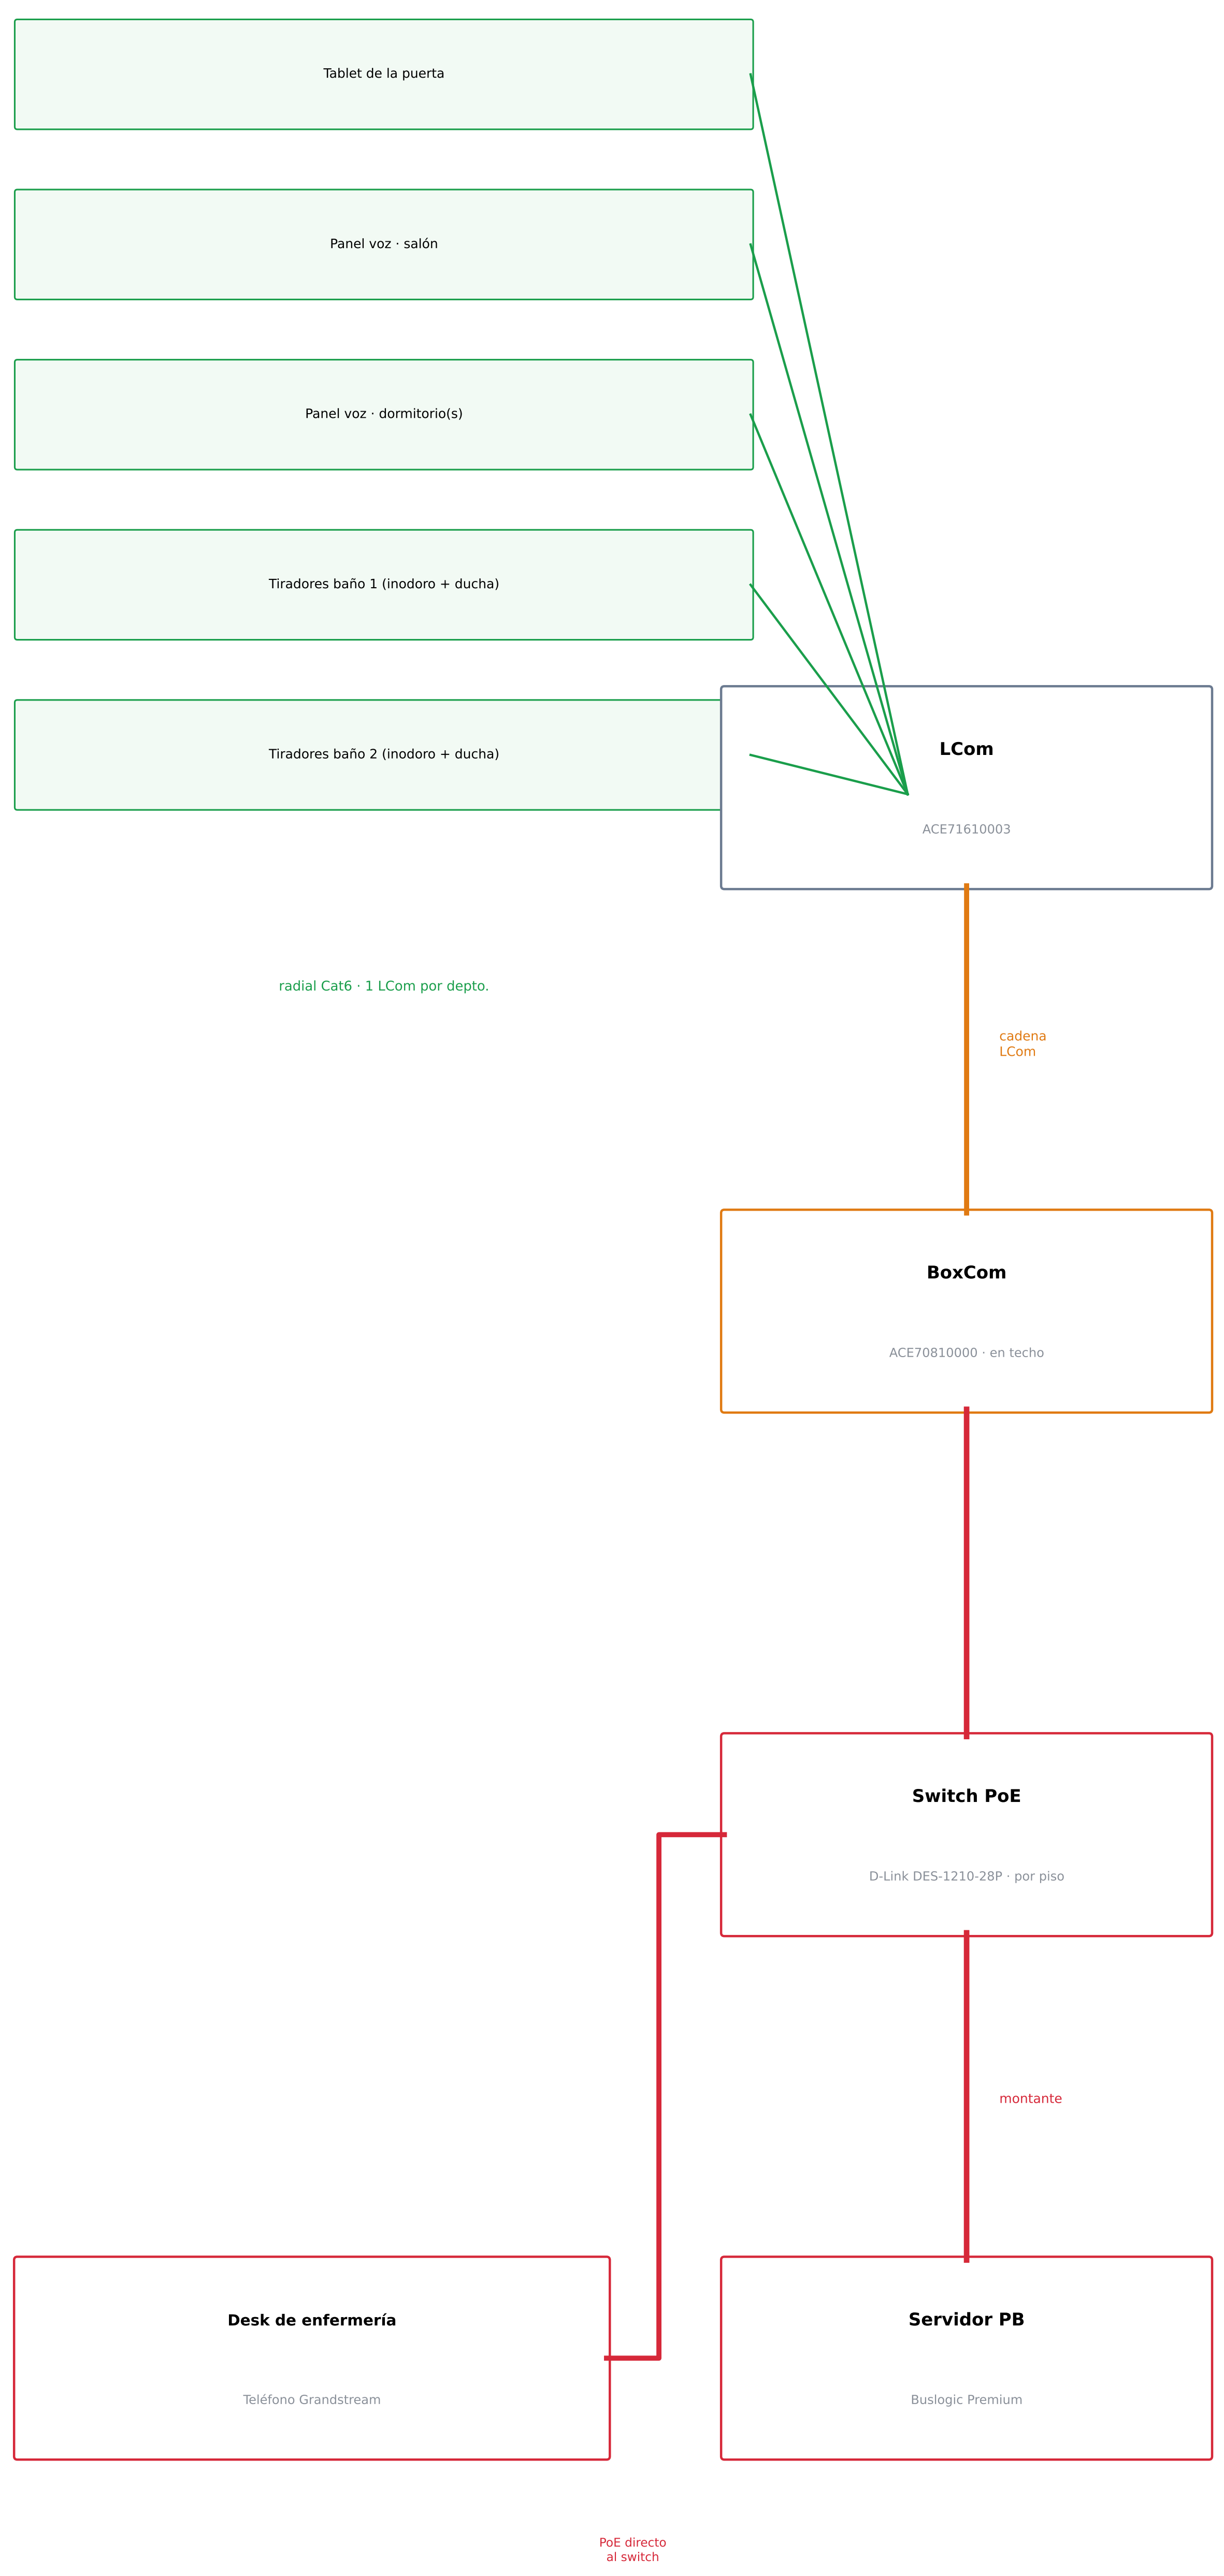
Tablet de la puerta
Panel voz · salón
Panel voz · dormitorio(s)
Tiradores baño 1 (inodoro + ducha)
Tiradores baño 2 (inodoro + ducha)
LCom
ACE71610003
radial Cat6 · 1 LCom por depto.
cadena
LCom
BoxCom
ACE70810000 · en techo
Switch PoE
D-Link DES-1210-28P · por piso
montante
Desk de enfermería
Teléfono Grandstream
Servidor PB
Buslogic Premium
PoE directo
al switch

**NOTAS · NOTES**

1. 8 pisos iguales con 4 departamentos (2 de 1 habitación y 2 de 2).
2. En cada piso: 2 BoxCom en el techo y un gabinete con el switch PoE.
3. Cadena 1: x01 → x04 → baño público. Cadena 2: x02 → x03.
4. Los switches suben por el montante hasta el gabinete principal de PB.
5. El teléfono Grandstream del desk va directo al switch PoE y muestra cada llamada con su color.
6. Todo el sistema es PoE.
7. Cantidades de anteproyecto: validar con Advantecnia y en obra.

**MIGDALEI YAM A TIJON · VIVIENDA TUTELADA**

Llamada de enfermería – PB + 8 pisos · 32 departamentos

Sistema: ACE BG · Advantecnia   Elaboró: Telab International

# ESQUEMA VERTICAL Y TOPOLOGÍA

Riser diagram and topology

| ESCALA · SCALE | FECHA · DATE | REV | LÁMINA |
|---|---|---|---|
| **S/E** | **15/10/2026** | **B** | **08** |

Base: plano del arquitecto L5 (Massad Oz / Triplet) · cotas en metros

Formato A1 · Rev. B – sobre plano real

## LISTA DE MATERIALES – EDIFICIO COMPLETO (PB + 8 pisos · 32 departamentos · 10 baños públicos)

| Código | Descripción | Cant. | Observación |
|---|---|---|---|
| **EN LOS DEPARTAMENTOS (32)** | | | |
| TAB | Tablet de la puerta (iPad / Android) – llamada y voz | **32** | 1 por departamento |
| VOZ | Panel de llamada con voz y botones – ACE82182451 | **80** | salón + cada dormitorio |
| TI/TD | Tirador de baño – ACE40320303W (inodoro y ducha) | **128** | 4 por departamento |
| LC | LCom – ACE71610003 | **32** | 1 por departamento |
| **BAÑOS PÚBLICOS (10)** | | | |
| T | Tirador de baño – ACE40320303W | **10** | 8 pisos + 2 en PB |
| LP | Luz de pasillo – ACE41020309 | **10** | sobre cada puerta |
| LC | LCom – ACE71610003 | **9** | 1 por piso + 1 en PB |
| **GABINETES Y CENTRAL** | | | |
| BC | BoxCom – ACE70810000 (en el techo) | **17** | 2 por piso + 1 en PB |
| SW | Switch PoE 24 puertos – D-Link DES-1210-28P | **9** | 1 por piso + PB |
| GAB | Gabinete mural 12U con patch panel (para el switch) | **8** | 1 por piso |
| GAB-PB | Gabinete principal de piso con UPS | **1** | PB |
| SRV | Servidor Buslogic Premium (Advantcare) con software | **1** | PB |
| TEL | Teléfono Grandstream Android (PoE, colores por tipo de llamada) | **1** | desk de enfermería |
| **CABLES (+ 15 % de reserva)** | | | |
| — | Cat6 radial dentro de los departamentos (verde) | **1700 m** | 183 m por piso |
| — | Cat6 / Cat7 cadena LCom → BoxCom (naranja) | **750 m** | 80 m por piso |
| — | Cat6A / Cat7 gabinetes y montante (rojo) | **130 m** | incluye montante |

**NOTAS · NOTES**

1. Cantidades calculadas del modelo (piso tipo × 8 + PB).
2. Longitudes de cable medidas sobre el recorrido dibujado, + 15 %.
3. Precios: según lista vigente de Advantecnia.
4. Validar en obra antes de comprar.

**MIGDALEI YAM A TIJON · VIVIENDA TUTELADA**
Llamada de enfermería – PB + 8 pisos · 32 departamentos
Sistema: ACE BG · Advantecnia   Elaboró: Telab International

**LISTA DE MATERIALES**
Bill of materials

| ESCALA · SCALE | FECHA · DATE | REV | LÁMINA |
|---|---|---|---|
| **S/E** | **15/10/2026** | **B** | **09** |

Base: plano del arquitecto L5 (Massad Oz / Triplet) · cotas en metros
Formato A1 · Rev. B – sobre plano real

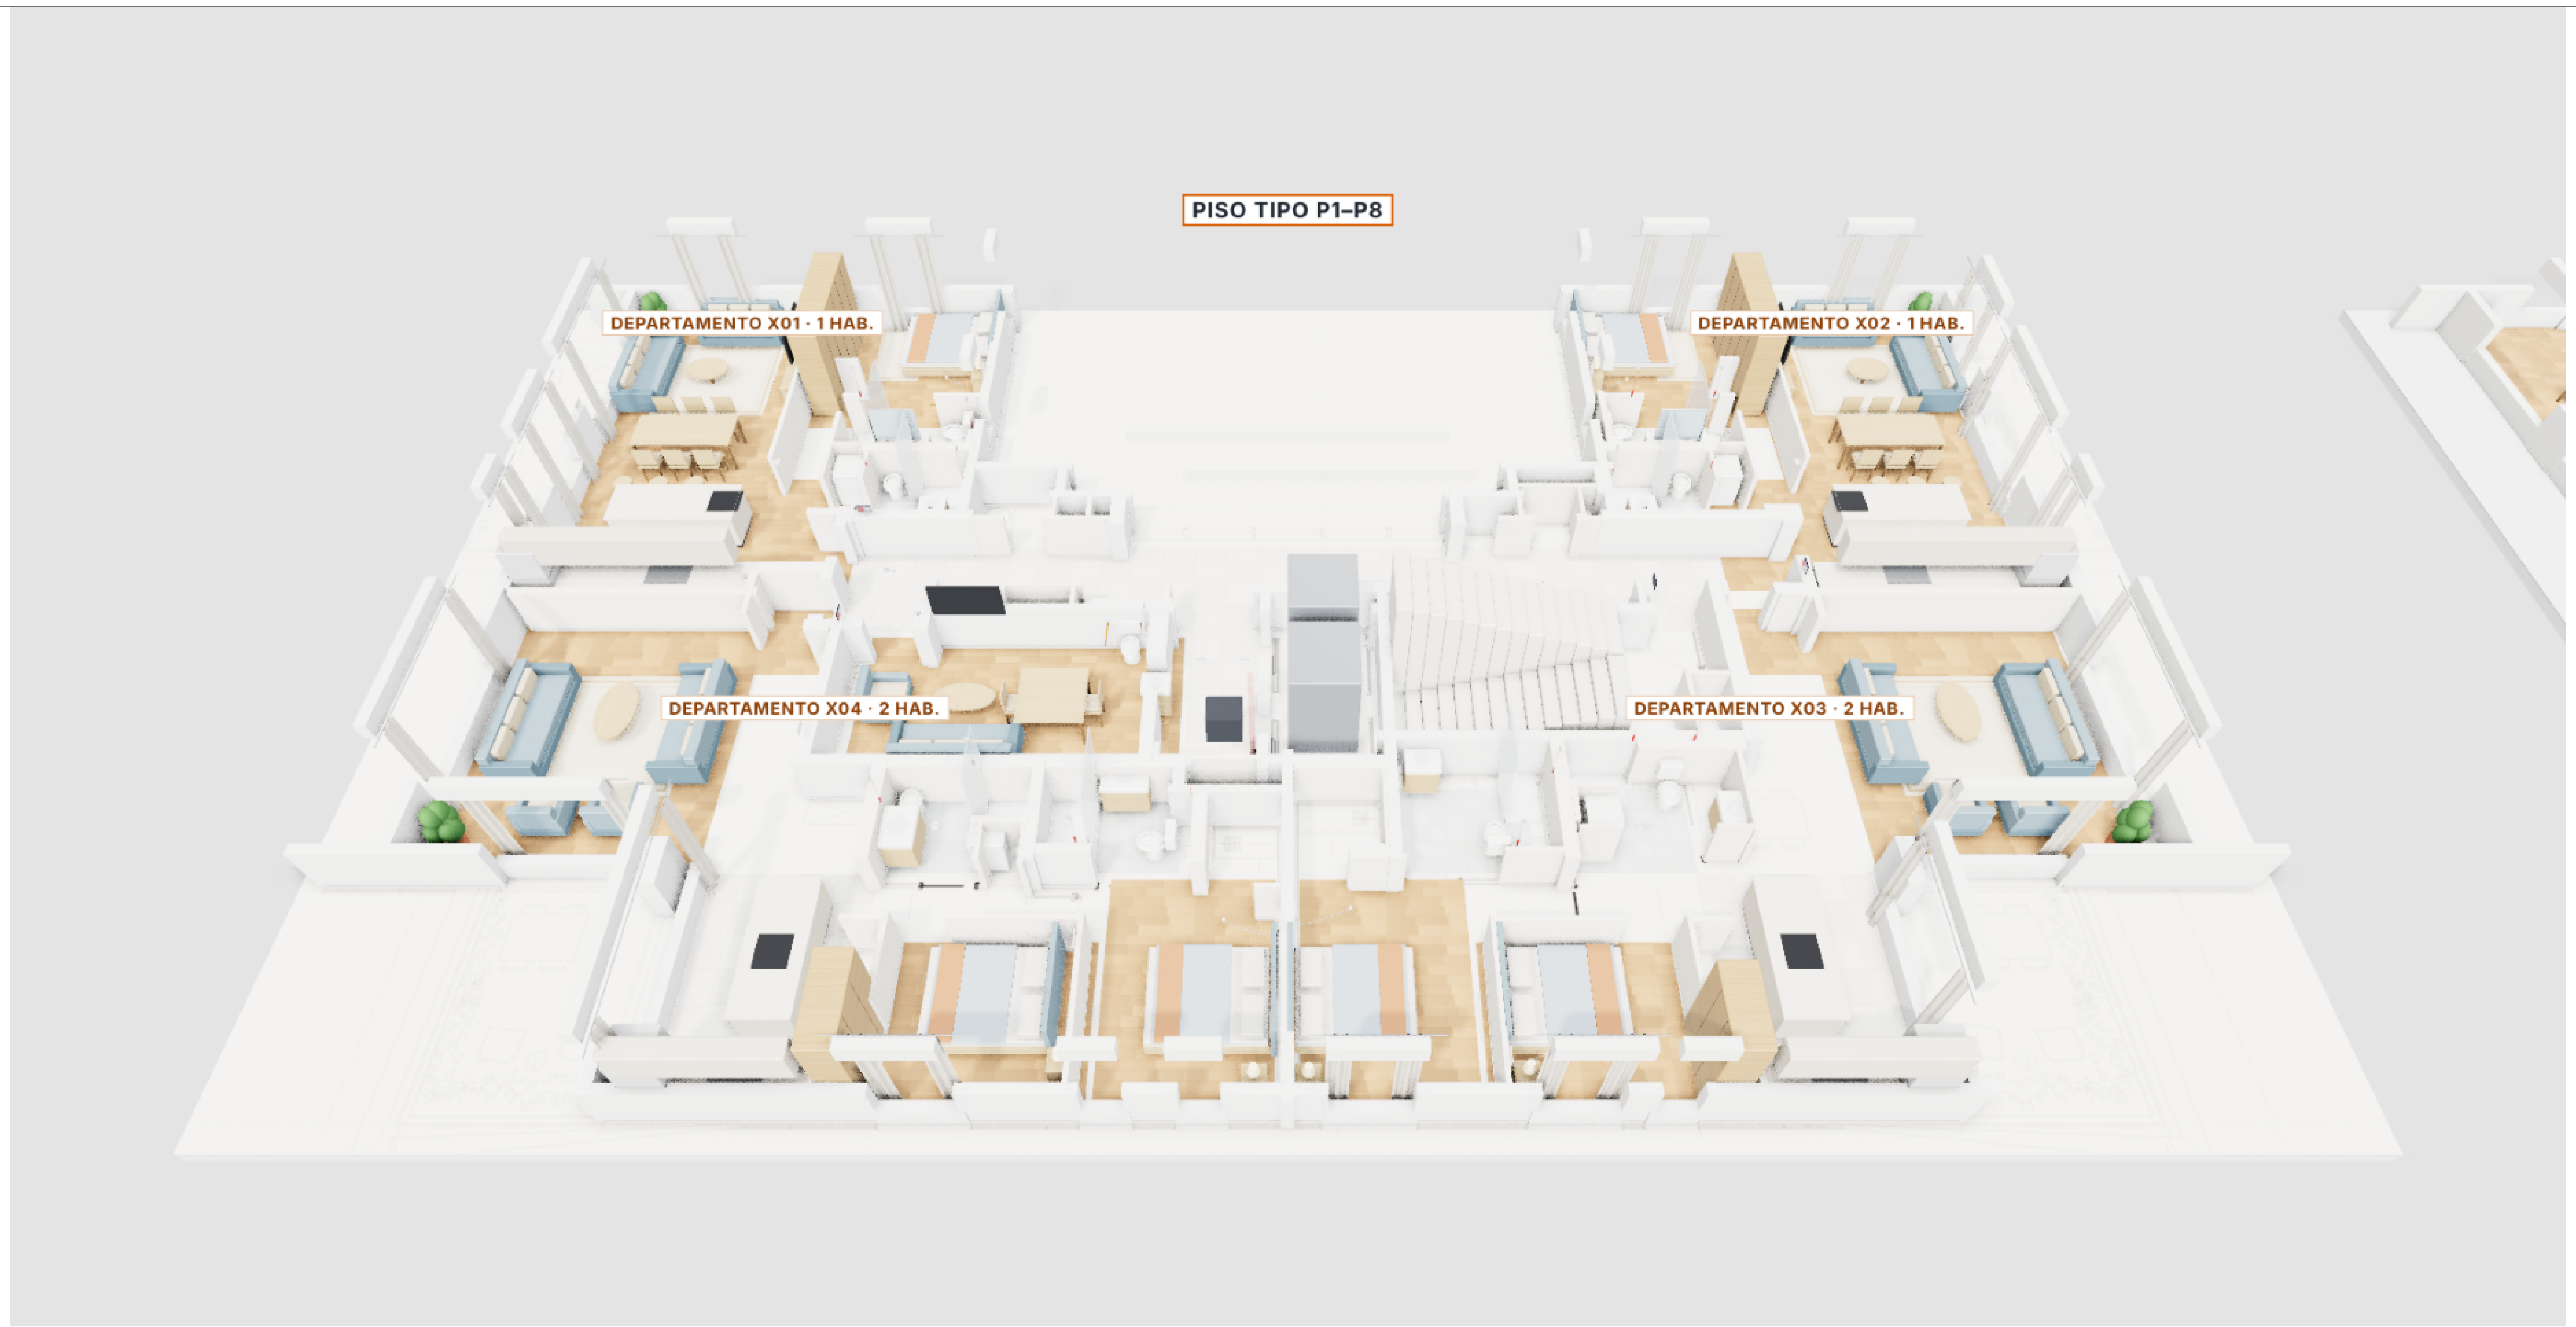
PISO TIPO P1–P8
DEPARTAMENTO X01 · 1 HAB.
DEPARTAMENTO X02 · 1 HAB.
DEPARTAMENTO X04 · 2 HAB.
DEPARTAMENTO X03 · 2 HAB.

A · Piso tipo – 4 departamentos

B · Tablet de la puerta

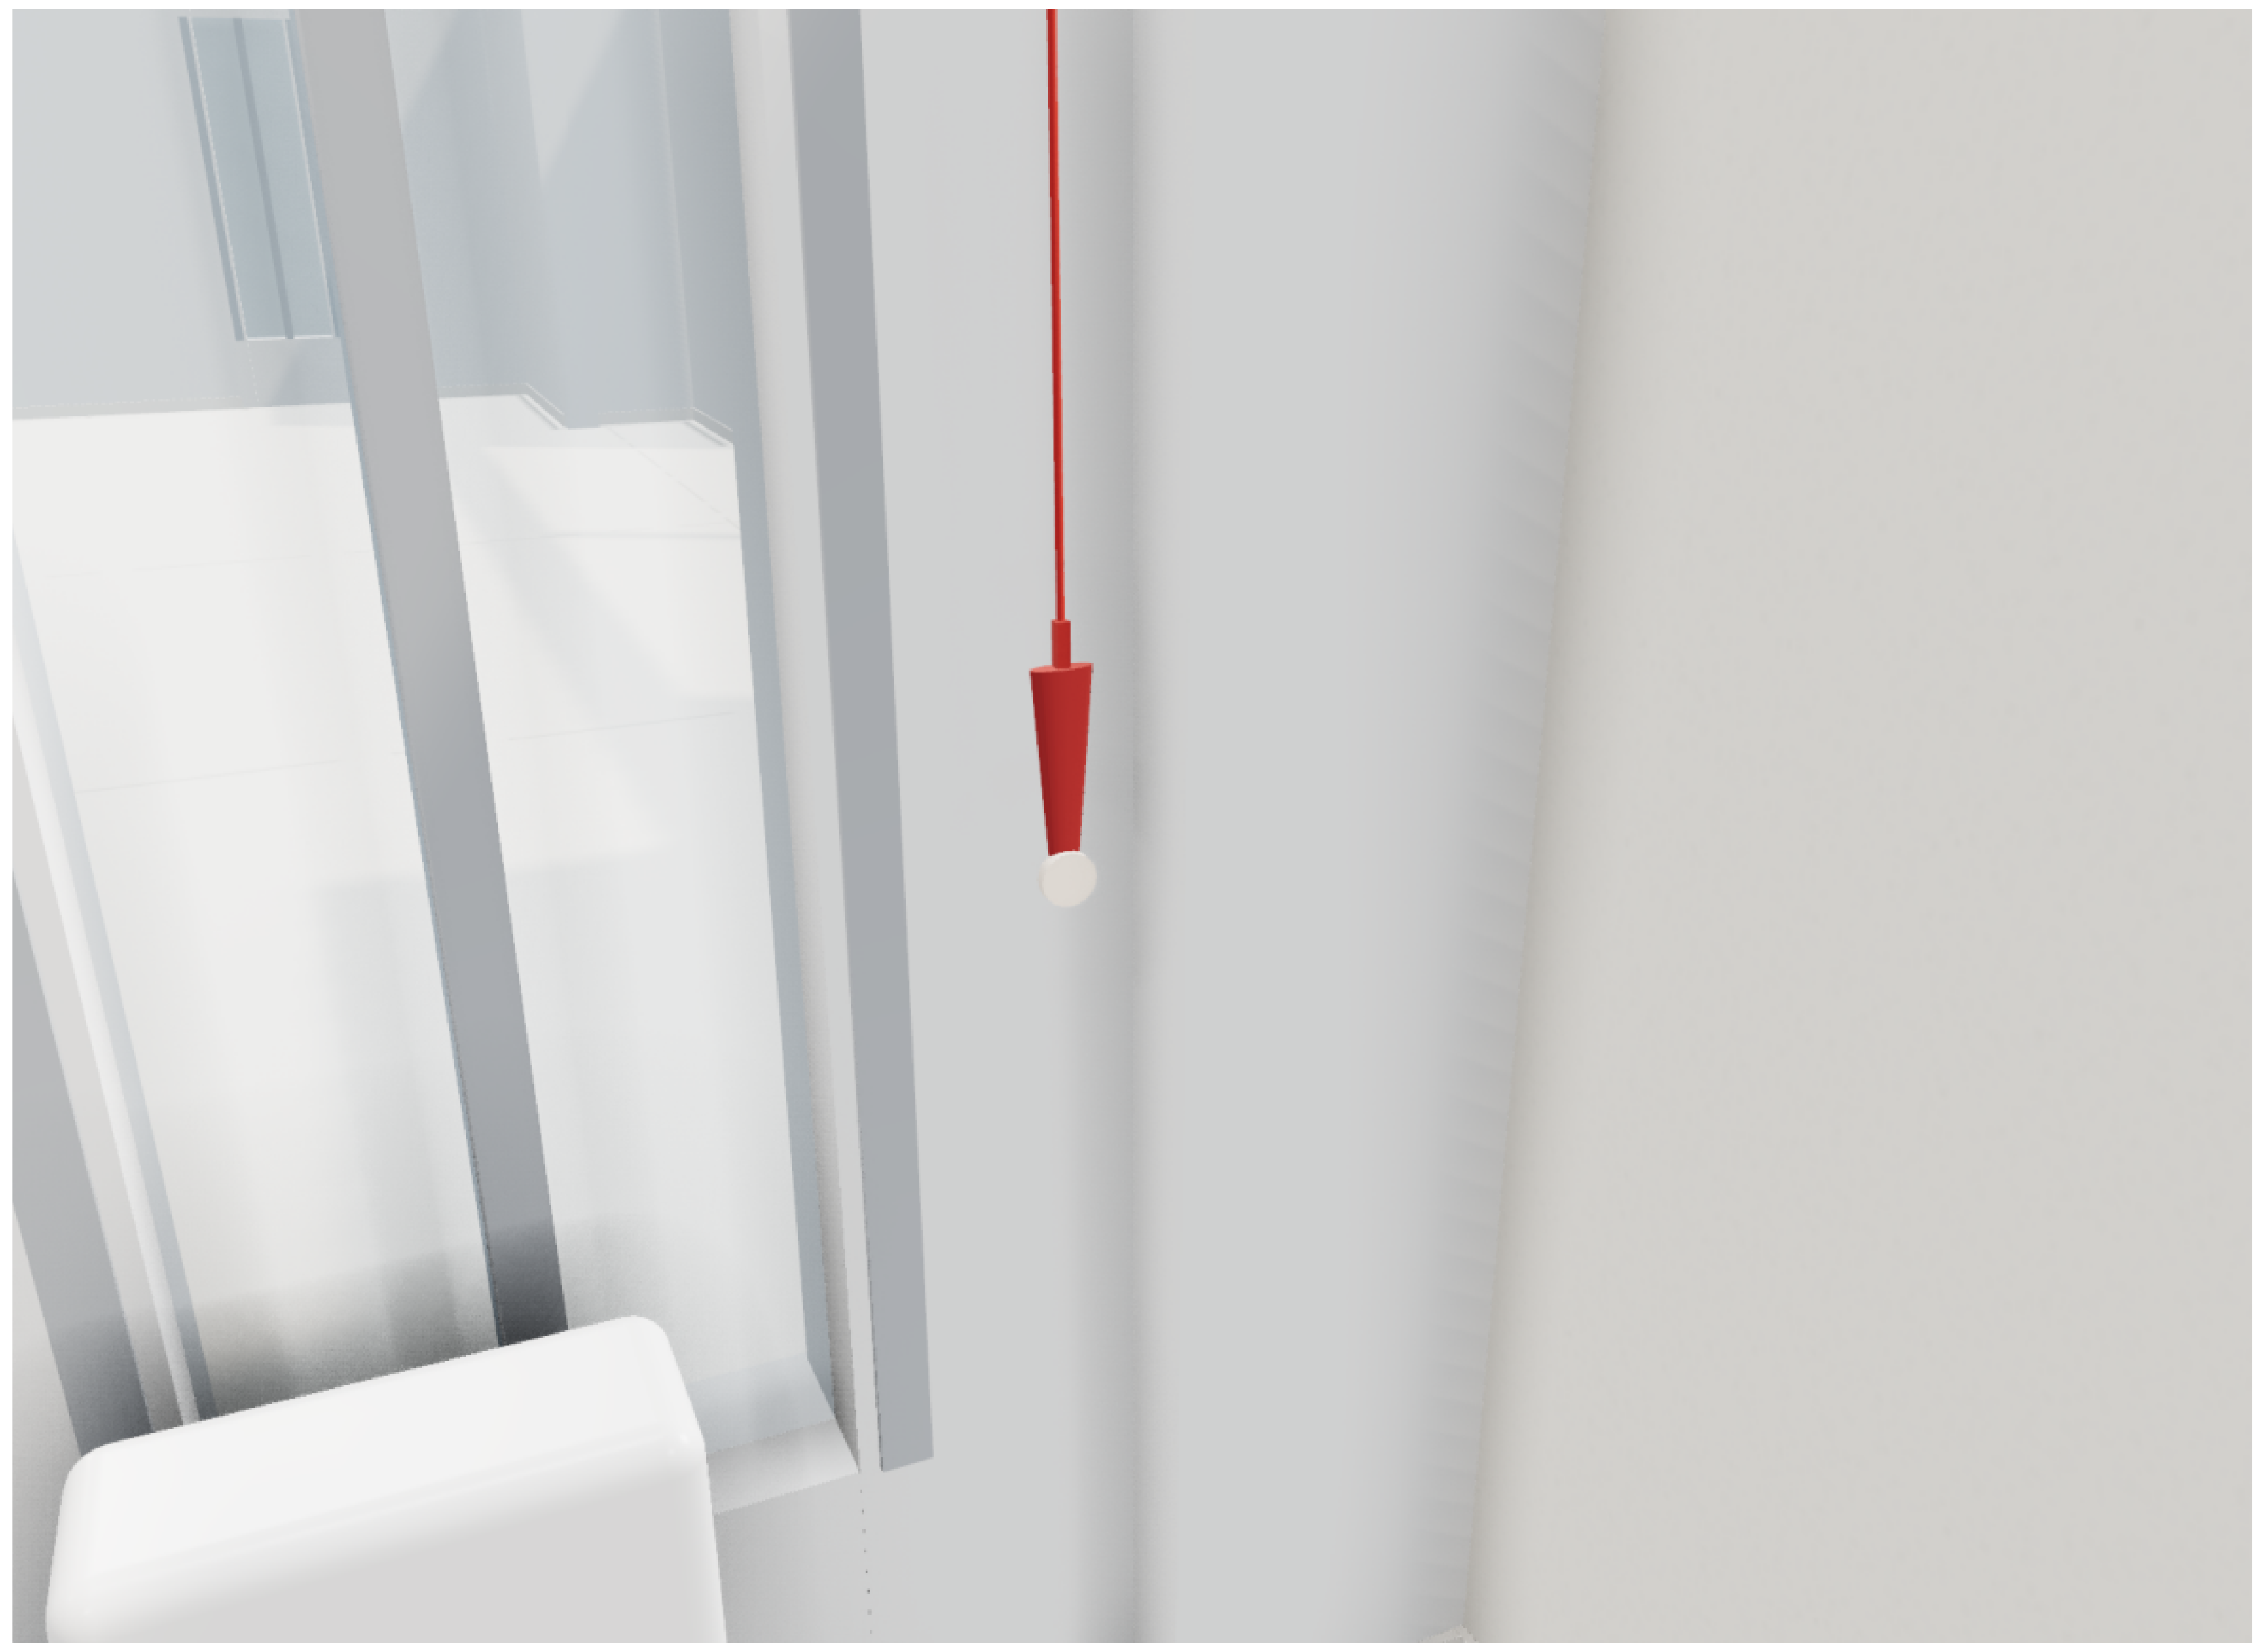

D · Baño – tiradores en inodoro y ducha

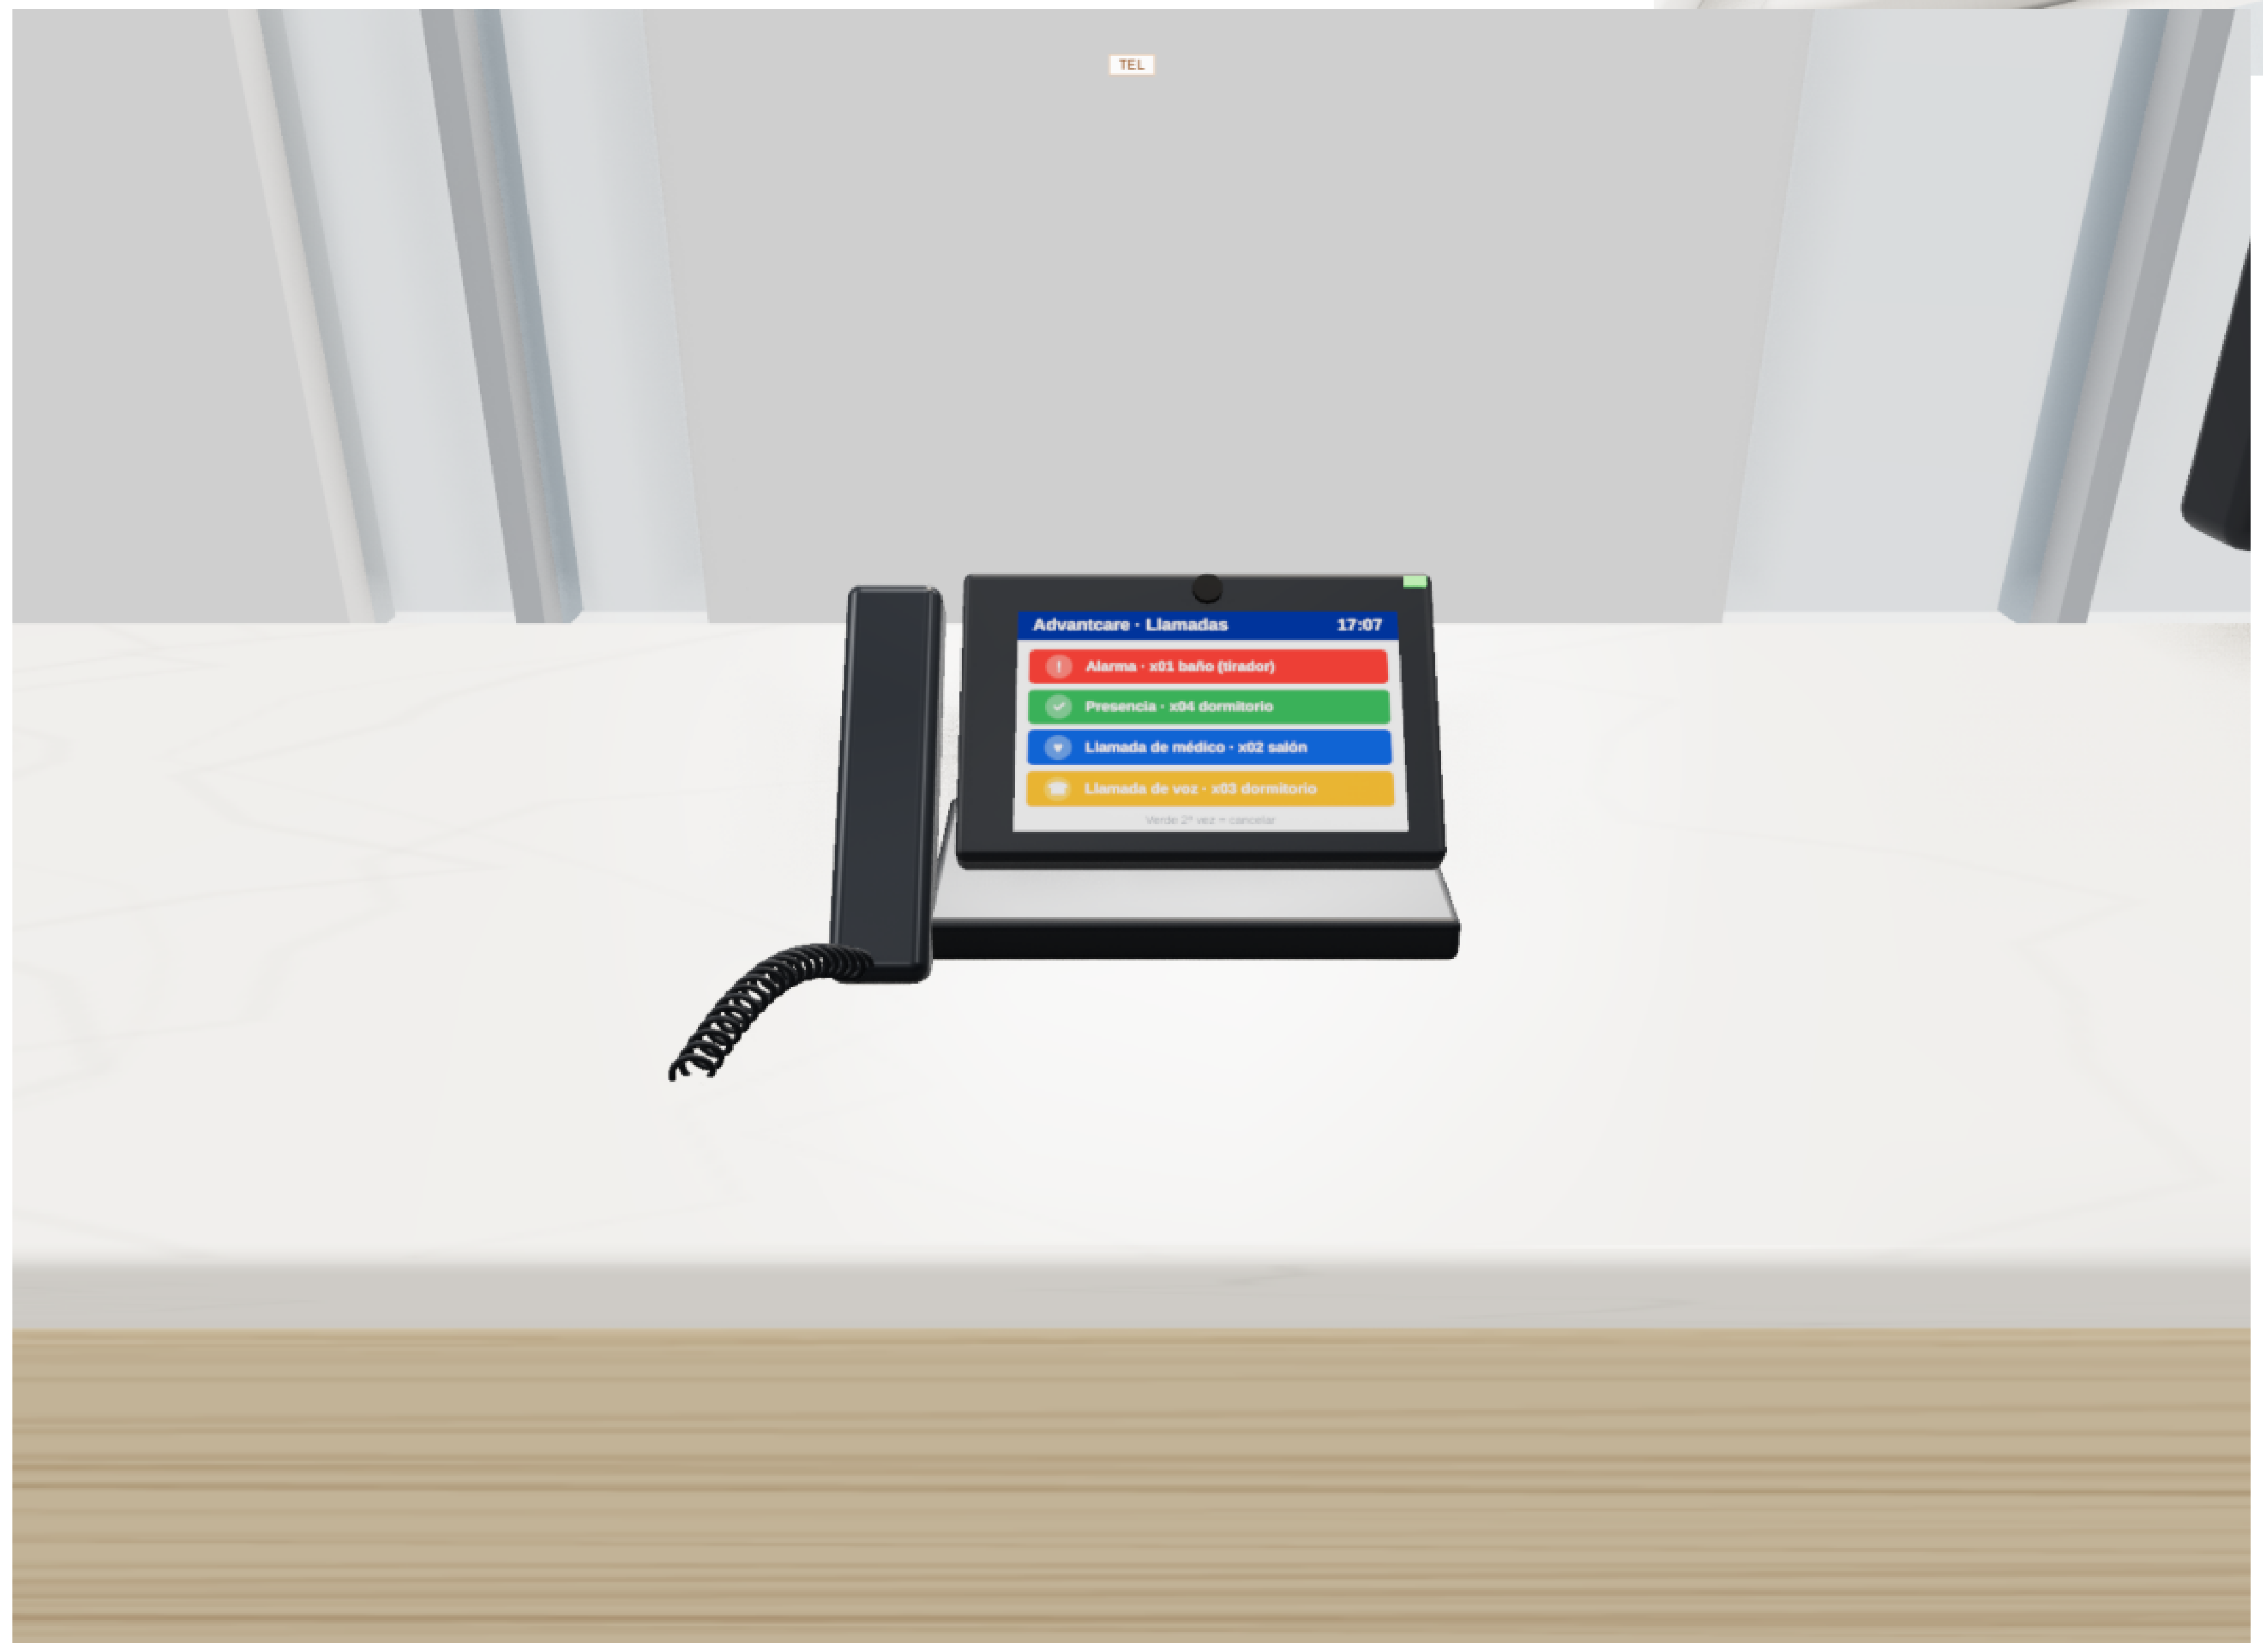

Advantcare · Llamadas 17:07

Alarma · x01 baño (tirador)

Presencia · x04 dormitorio

Llamada de médico · x02 salón

Llamada de voz · x03 dormitorio

Verde 2ª vez = cancelar

E · PB – desk de enfermería

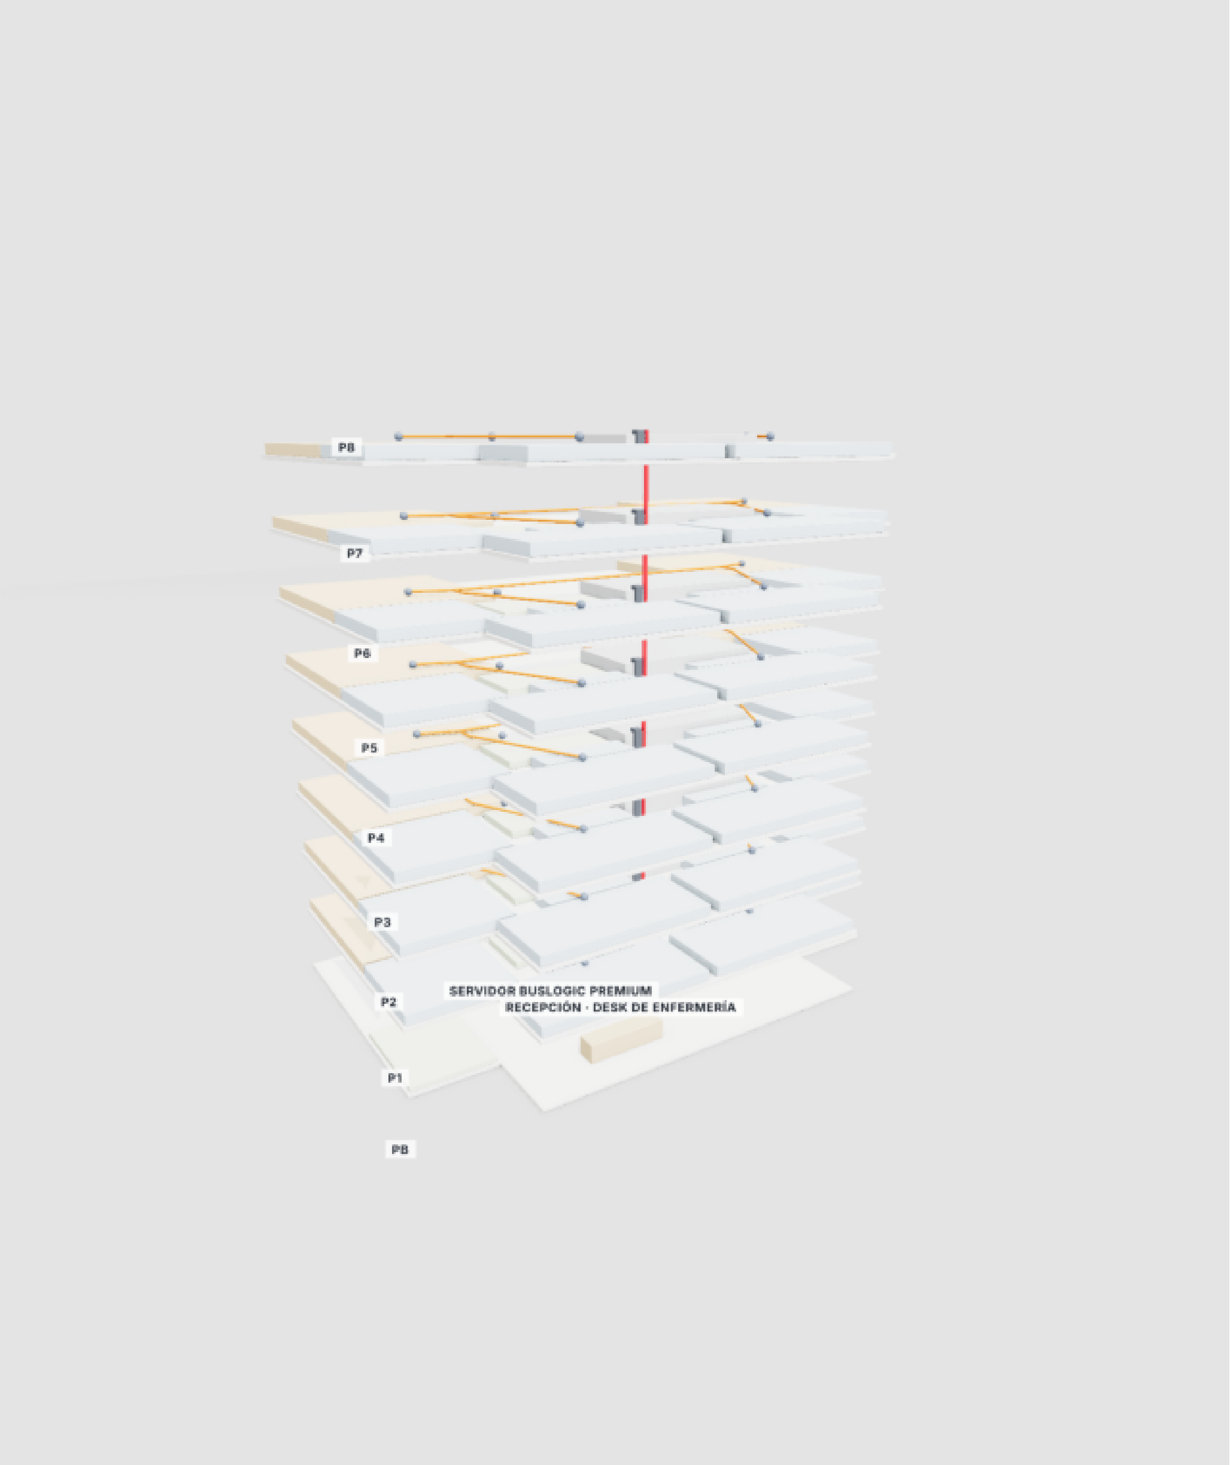
P8
P7
P6
P5
P4
P3
P2
P1
PB
SERVIDOR BUSLOGIC PREMIUM
RECEPCIÓN · DESK DE ENFERMERÍA

F · Edificio PB + 8 pisos

**MIGDALEI YAM A TIJON · VIVIENDA TUTELADA**

Llamada de enfermería – PB + 8 pisos · 32 departamentos

Sistema: ACE BG · Advantecnia Elaboró: Telab International

## VISTAS 3D

3D views

| ESCALA · SCALE | FECHA · DATE | REV | LÁMINA |
|---|---|---|---|
| **S/E** | **15/10/2026** | **B** | **10** |

Base: plano del arquitecto L5 (Massad Oz / Triplet) · cotas en metros

Formato A1 · Rev. B – sobre plano real

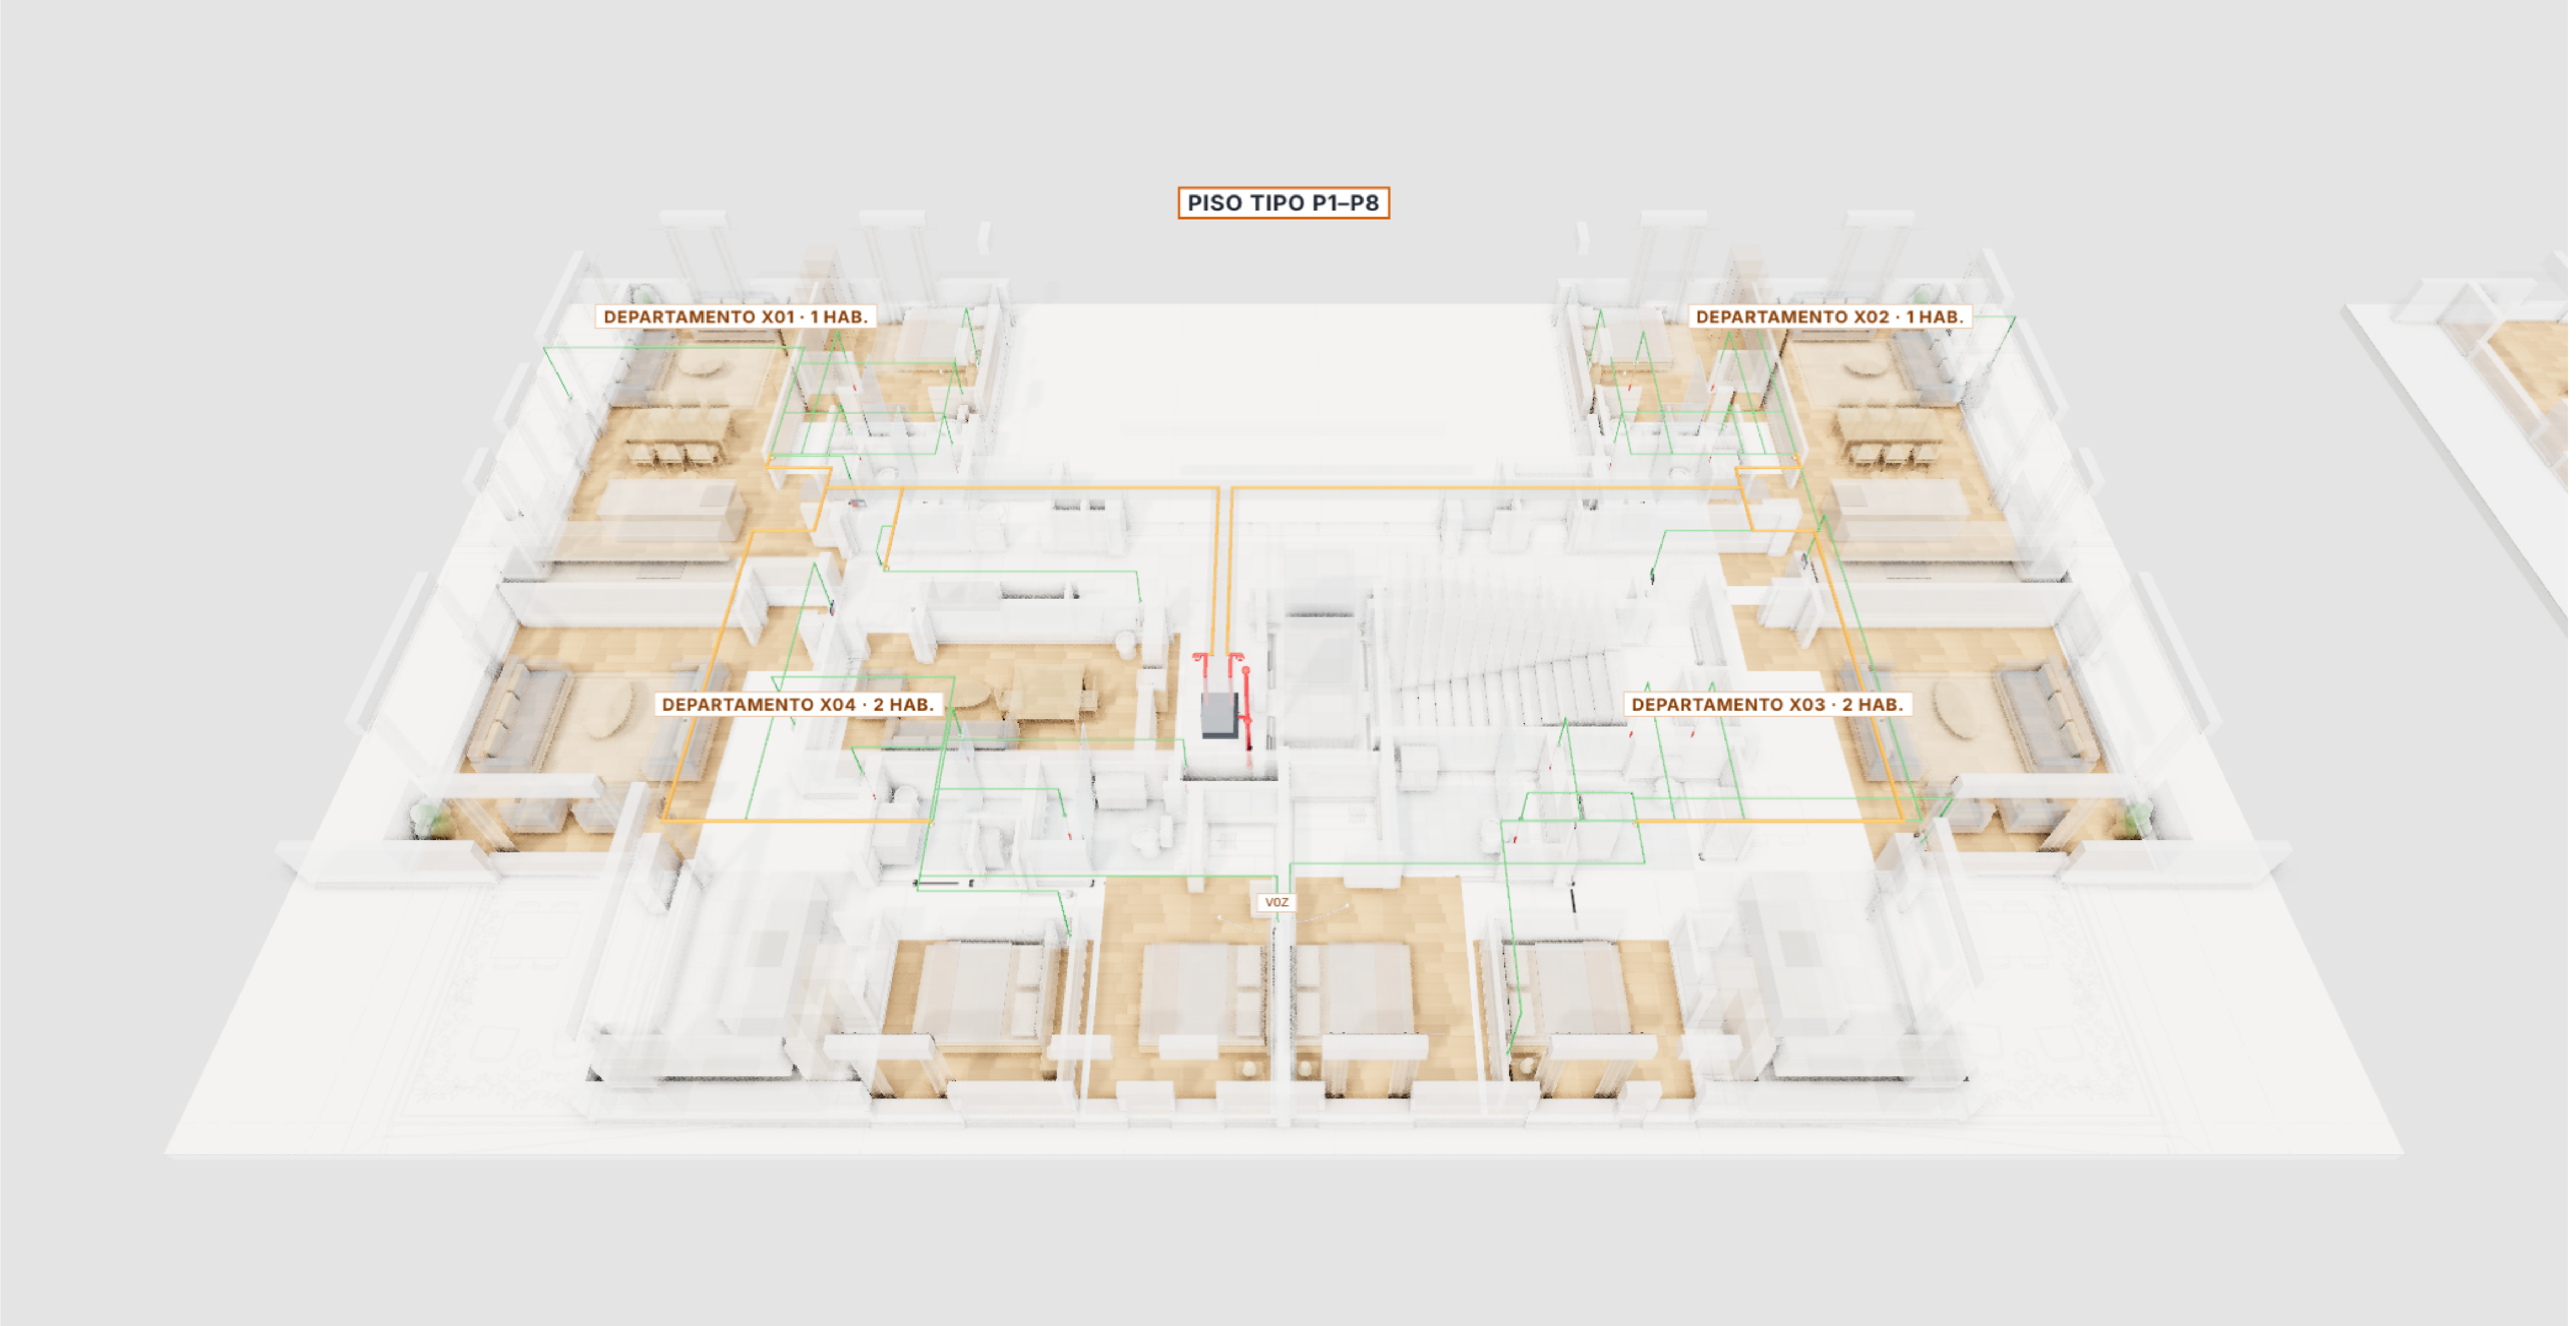
PISO TIPO P1–P8
DEPARTAMENTO X01 · 1 HAB.
DEPARTAMENTO X02 · 1 HAB.
DEPARTAMENTO X04 · 2 HAB.
DEPARTAMENTO X03 · 2 HAB.
VOZ

A · Piso tipo – cableado (verde radial · naranja cadena LCom · rojo red)

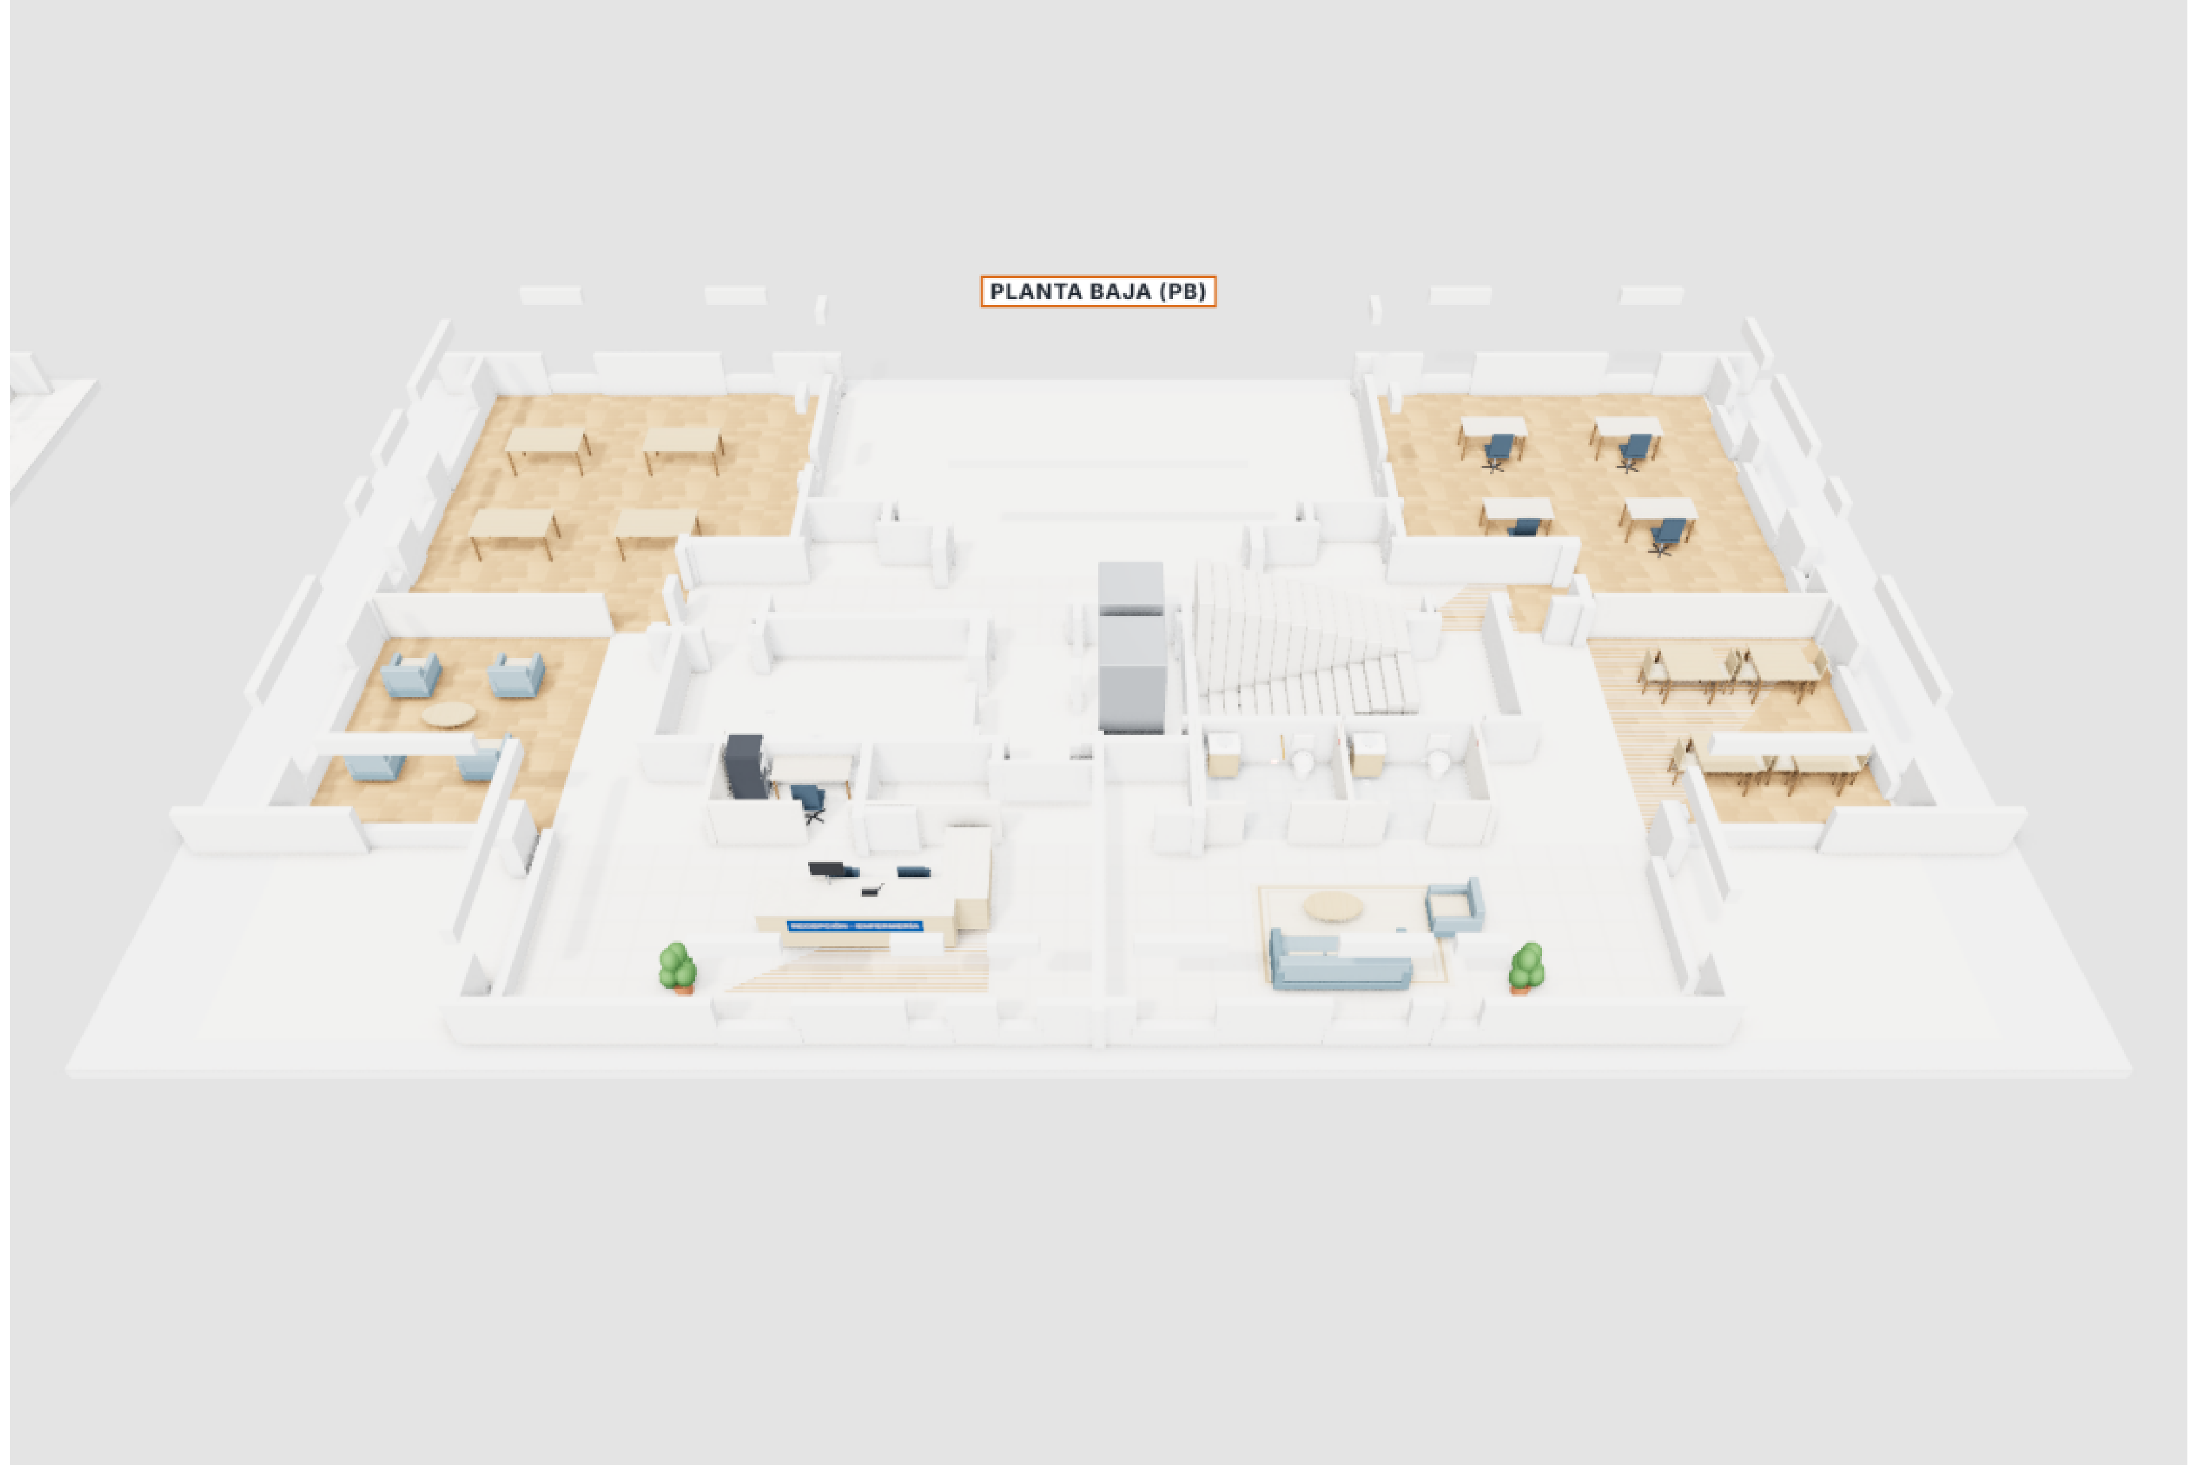
PLANTA BAJA (PB)

B · Planta baja – lobby y recepción

C · Salón – panel con voz y botones

**COLORES · COLOURS · םיעבצ**

| | |
|---|---|
| 🟩 | Cat6 radial: cada equipo → LCom de su departamento<br>Cat6 radial: each device → apartment LCom · Cat6 ילאידר: לכ ןקתה ← LCom לש הרידה |
| 🟧 | Cat6 / Cat7 cadena: LCom → LCom → BoxCom del techo<br>Cat6 / Cat7 chain: LCom → LCom → BoxCom · Cat6 / Cat7 תרשרש: LCom ← LCom ← BoxCom |
| 🟥 | Cat6A / Cat7 red: BoxCom → switch PoE → montante → servidor PB<br>Cat6A / Cat7 network: BoxCom → switch → riser → GF server · Cat6A / Cat7 תשר: BoxCom ← גתמ ← דומע ← תרש |

**MIGDALEI YAM A TIJON · VIVIENDA TUTELADA**

Llamada de enfermería – PB + 8 pisos · 32 departamentos

Sistema: ACE BG · Advantecnia    Elaboró: Telab International

## VISTAS 3D – CABLEADO

3D views – wiring

| ESCALA · SCALE | FECHA · DATE | REV | LÁMINA |
|---|---|---|---|
| S/E | 15/10/2026 | B | 11 |

Base: plano del arquitecto L5 (Massad Oz / Triplet) · cotas en metros

Formato A1 · Rev. B – sobre plano real