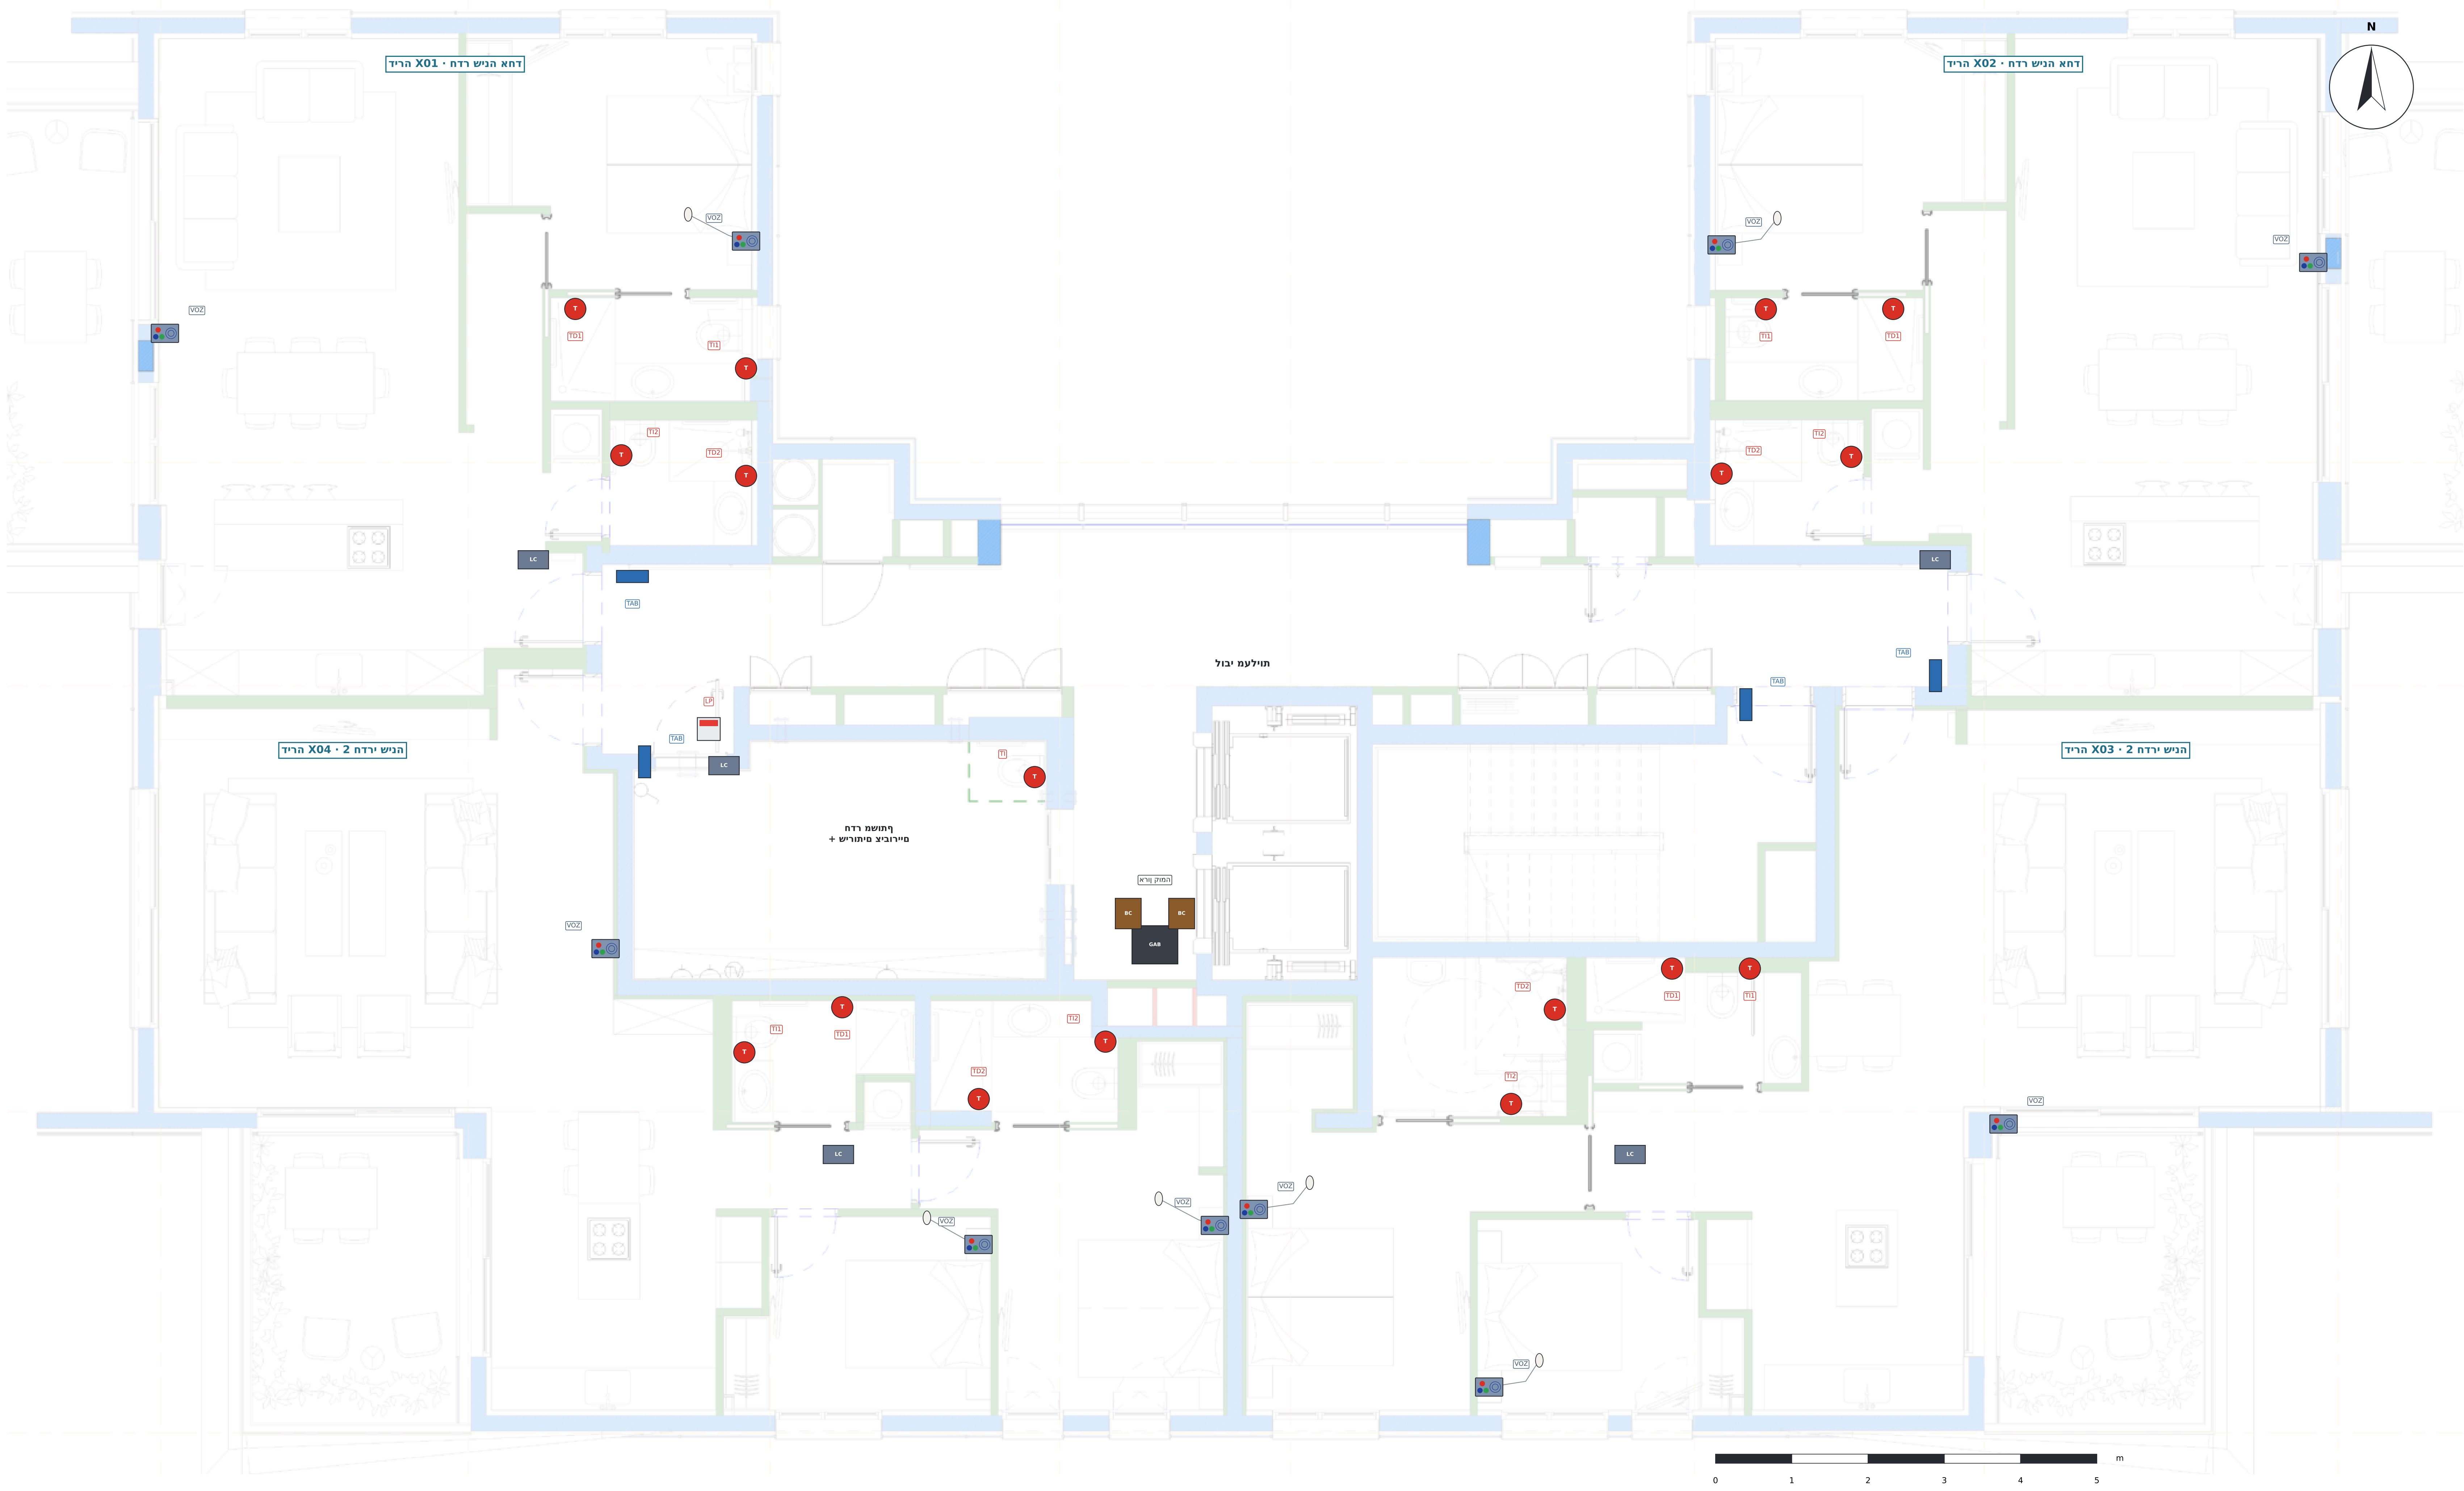
N
הריד X01 · דחא הניש רדח
הריד X02 · דחא הניש רדח
הריד X04 · 2 הניש ירדח
הריד X03 · 2 הניש ירדח
תוילעמ יבול
ףתושמ רדח
+ םיירוביצ םיתוריש
המוק ןורא
VOZ
TAB
LC
LP
TI
TI1
TI2
TD1
TD2
T
BC
GAB
m
0
1
2
3
4
5

DEVICES · EQUIPOS · ץיוד

▬	TAB · הסינכב טלבאט (iPad / דיאורדנא) – רובידו האירק, הבוג 1.40 מ' Door tablet – call and voice · הסינכב טלבאט – רובידו האירק
VOZ	VOZ · םינצחל םע ילוק לנפ ACE82182451 – ןולס ירדחו הניש, הבוג 1.20–1.30 מ' Voice panel with buttons – living room and bedrooms · ןולס ירדחו הניש – םינצחל םע ילוק לנפ
⬯	אגס האירק דיל הטימה (ירדחב הנישה) Call pear next to the bed (bedrooms) · אגס האירק דיל הטימה
T	TI / TD · תכישמ לבח ACE40320303W – הלסא ומקלחת, הבוג 1.85 מ' Pull-cord – toilet and shower, h 1.85 m · תכישמ לבח – הלסא ומקלחת, הבוג 1.85 מ'
LP	LP · תרונמ ןורדסמ ACE41020309 – לעמ תלד לכ םיתוריש םיירוביצ Corridor light – above each public toilet door · תרונמ ןורדסמ – לעמ תלד לכ םיתוריש םיירוביצ
LC	LC · LCom ACE71610003 – זכרמ הרידה (הרקת) LCom – apartment hub (ceiling) · LCom – זכרמ הרידה (הרקת)
BC	BC · BoxCom ACE70810000 – זכרמ סאב המכל תוריד (הרקת) BoxCom – bus hub for several apartments (ceiling) · BoxCom – זכרמ סאב המכל תוריד (הרקת)
GAB	(PoE תואיצי PoE D-Link DES-1210-28P (24 12: גתמU ןורא המוק Floor rack: D-Link DES-1210-28P PoE switch · ןורא המוק: גתמ PoE D-Link DES-1210-28P

תומוק 8 × המוקל תויומכ

דוק	רואית	המוקל	תומוק 8
TAB	הסינכב טלבאט	4	32
VOZ	םינצחל םע ילוק לנפ	10	80
TI/TD	תכישמ לבח (הלסא + תחלקמ)	17	136
LP	תרונמ ןורדסמ (םיתוריש םיירוביצ)	1	8
LC	LCom	5	40
BC	BoxCom	2	16
SW	PoE גתמ	1	8

NOTES · תורעה

1. סיסב: תונכות תילכירדא L5 (תיסופיט המוק) – 8 תומוקה תוהז: 4 תוריד המוקב, 32 ךסב לוכה.
2. תוריד x01 ו-x02: רדח הניש דחא, ןולס םע חבטמ ו-2 ירדח הצחר. תוריד x03 ו-x04: 2 ירדח הניש ו-2 ירדח הצחר.
3. טלבאט הסינכב לכל הריד (iPad / דיאורדנא) לקירא האירק ולדיבור םע תואחה.
4. לנפ ילוק םע םינצחל (ACE82182451) ןולסב ובכל רדח הניש; רדחב הנישה םע אגס דיל הטימה.
5. תוכישמ לבח (ACE40320303W) הלסאב ובמקלחת לכב ירדח הרחצה, הבוגב 1.85 מ'.
6. םיתוריש םיירוביצ לכב המוק רדחב המשותף: תכישמ לבח + תרונמ ןורדסמ לעמ הלדת. םע 2 עקרקב – 10 םיתוריש םיירוביצ.
7. ןורא המוק דיל המעליות םע גתמ PoE D-Link DES-1210-28P; 2 ה-BoxCom הרקתב דיל.
8. םימוקימ יפל םינומיס הלוקח תונכותב L2 (nt = לנפ ילוק, tab = טלבאט): ואר ןויליג 03.

הנקתה יהבוג

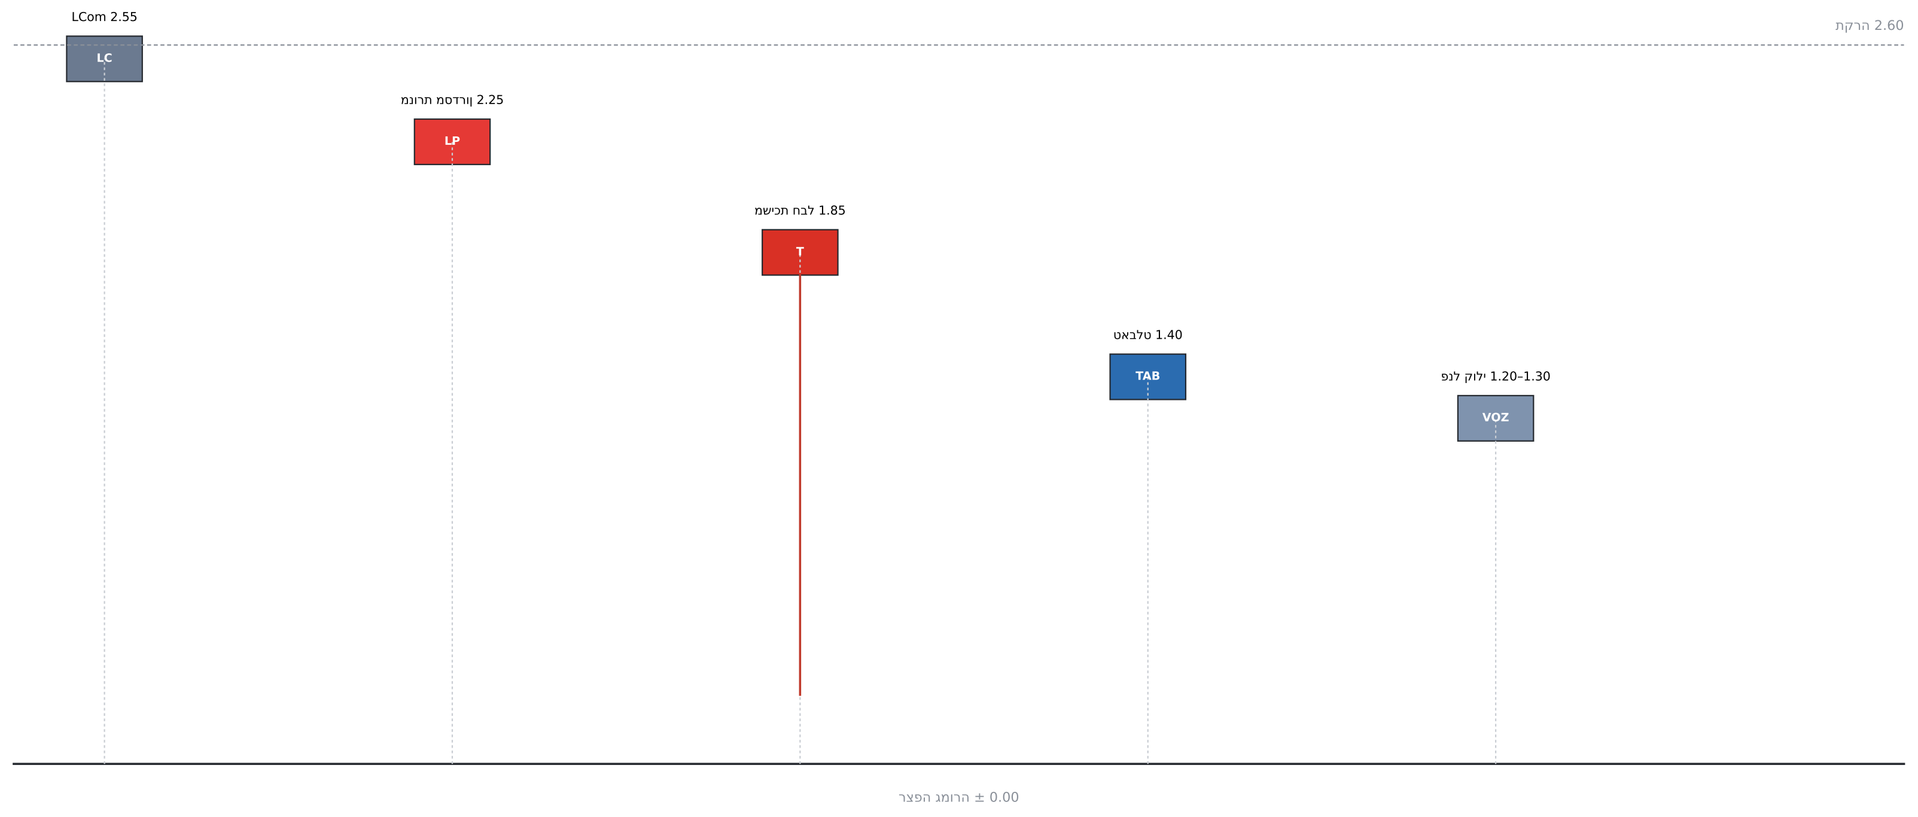
LCom 2.55
LC
הרקת 2.60
2.25 ןורדסמ תרונמ
LP
1.85 תכישמ לבח
T
1.40 טלבאט
TAB
1.20–1.30 לנפ ילוק
VOZ
הפצר גמורה ± 0.00

שירותים קריאת אחות

לבח תכישמ

טבלט אנדרואיד קריאת אחות
Advantecnia

הסינכב טלבאט (iPad / דיאורדנא)

מנורה קריאת אחות

ןורדסמ תרונמ

פנל קריאת אחות

םינצחל םע ילוק לנפ

ןגומ רויד · ןוכיתה םי ילדגמ

תוריד 32 · תומוק 8 + עקרק – תוחא תאירק

Telab International :הכון ע"י ACE BG · Advantecnia :תכרעמ

תוחא תאירק · 1–8 תיסופיט המוק

Typical floor F1–F8 · nurse call

SCALE · הדימ הנק	DATE · ךיראת	REV	ןויליג
1:60	15/10/2026	B	01

סיסב: תונכות לכירדאה L5 (זוע דסמ / Triplet) · םירטמב תודימ

טמרופ A1 · הרודהמ B – לע תונכותה תיתימאה

שירותים קריאת אחות

משיכת חבל

קוד	**ACE40320303W**
מיקום	אסלה ומקלחת בכל חדר רחצה וב-10 השירותים הציבוריים
גובה	**1.85 מ'**
כמות	**138**

1

טבלט אנדרואיד קריאת אחות
Advantecnia
TV
Llamada de enfermera
Hospital
Salud y bienestar

טאבלט בכניסה (אנדרואיד / iPad)

קוד	**Advantecnia TV**
מיקום	בלובי, ליד דלת כל דירה
גובה	**1.40 מ'**
כמות	**32**

2

מנורה קריאת אחות

מנורת מסדרון

קוד	**ACE41020309**
מיקום	מעל דלת כל שירותים ציבוריים
גובה	**2.25 מ'**
כמות	**10**

3

פנל קריאת אחות

פנל קולי עם לחצנים

קוד	**ACE82182451**
מיקום	סלון וכל חדר שינה (בחדר השינה עם אגס)
גובה	**1.20–1.30 מ'**
כמות	**80**

4

GRANDSTREAM
HD

טלפון עמדה (אנדרואיד)

קוד	**Grandstream**
מיקום	עמדת אחות בקרקע · PoE ישירות למתג
גובה	**על העמדה**
כמות	**1**

5

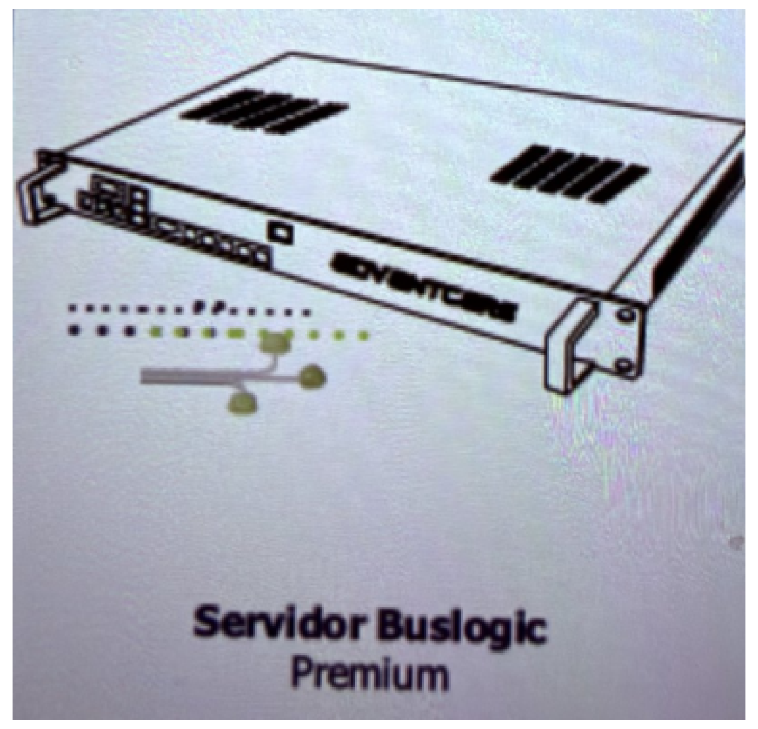
Servidor Buslogic
Premium

שרת Buslogic Premium

קוד	**Advantcare**
מיקום	ארון ראשי בקרקע
גובה	**בארון**
כמות	**1**

6

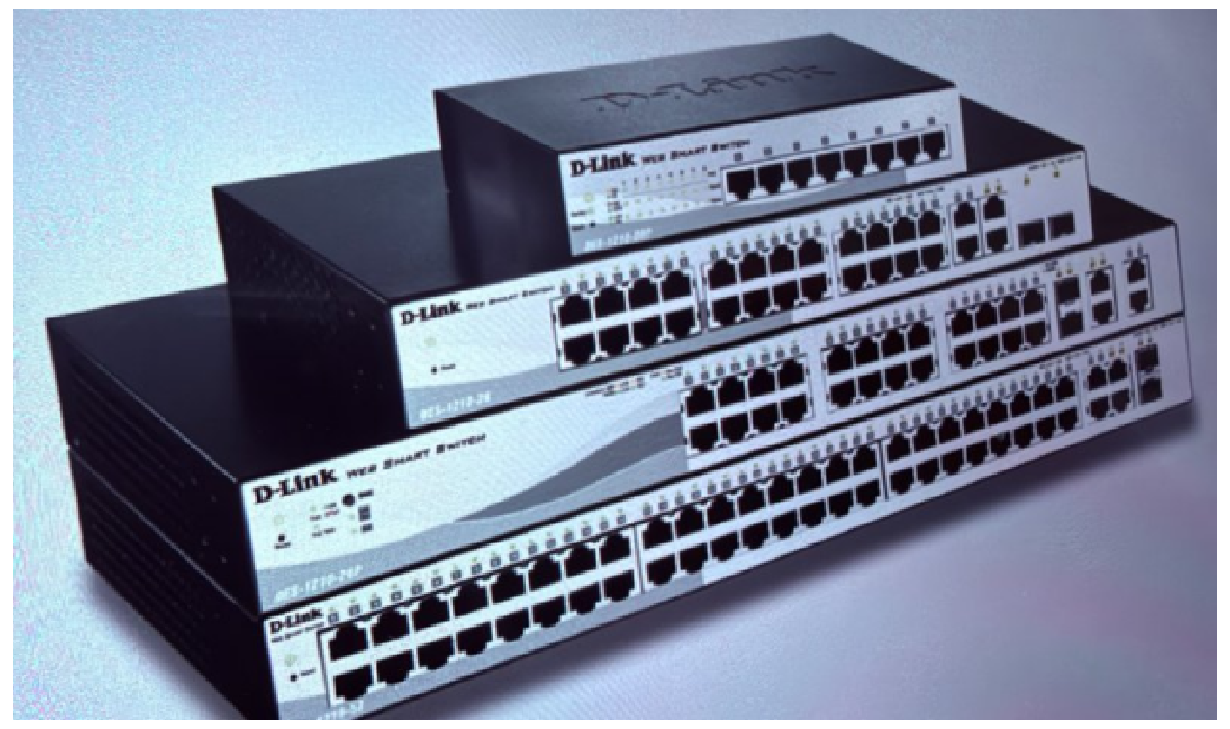

מתג PoE עם 24 יציאות

קוד	**D-Link DES-1210-28P**
מיקום	ארון בכל קומה ובקרקע
גובה	**בארון**
כמות	**9**

7

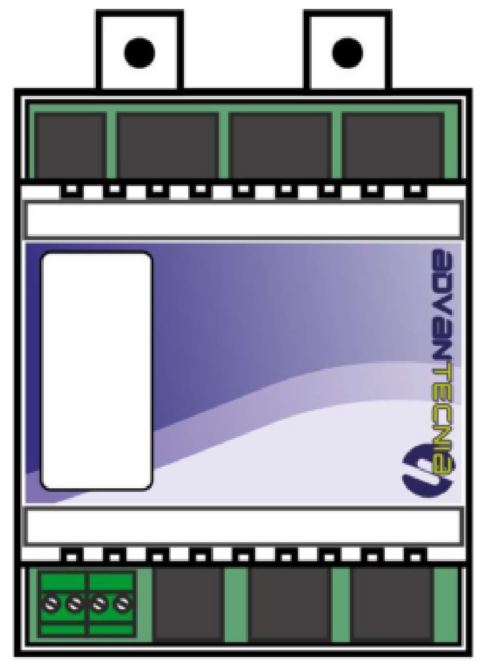
advantecnia

מרכז רדיאלי – LCom

קוד	**ACE71610003**
מיקום	תקרת כל דירה והשירותים הציבוריים
גובה	**2,55 m**
כמות	**41**

8

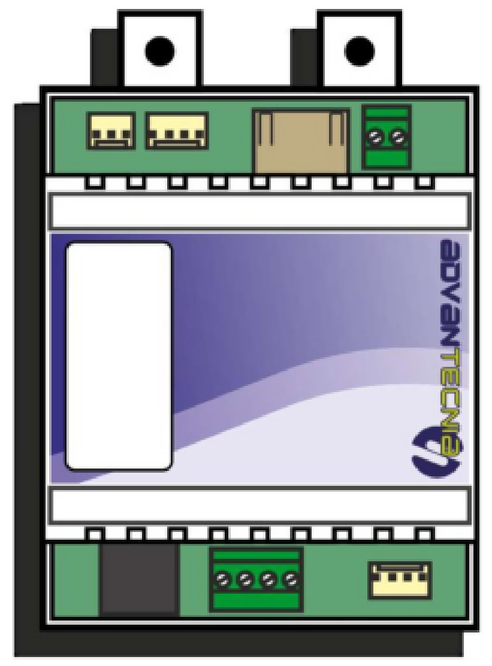
advantecnia

מרכז באס – BoxCom

קוד	**ACE70810000**
מיקום	תקרה ליד הארון: מחבר כמה דירות
גובה	**2,55 m**
כמות	**17**

9

NOTES · הערות

1. תמונות ייחוס של ACE BG / Advantecnia, עם הכותרת שלהן.

2. משיכת חבל: חבל אדום עם ידית, נגיש גם מהרצפה.

3. טאבלט בכניסה קורא ומדבר עם האחות.

4. מנורת המסדרון נדלקת כשקוראים מהשירותים הציבוריים.

5. בפנל לחצן קריאה אדום, לחצן כחול (שמאל) וירוק (ימין) ורמקול לדיבור.

6. שרשרת: התקנים ← LCom (רדיאלי) ← BoxCom (באס) ← מתג PoE ← שרת.

7. טלפון העמדה מחובר ישירות למתג ה-PoE.

טלפון העמדה – איזה צבע מוצג

🟥	הזעקה (משיכה / SOS)	אדום
🟩	נוכחות: לחצן ירוק פעם אחת	ירוק
⬜	מבטל קריאה או הזעקה: לחצן ירוק שוב	נמחק
🟦	קריאת רופא: לחצן כחול (blue call)	כחול
🟧	שיחה קולית	כתום / צהוב

מגדלי הים התיכון · דיור מוגן

32 דירות · 8 קומות + קרקע – קריאת אחות

מערכת: ACE BG · Advantecnia   הוכן ע"י: Telab International

ציוד המערכת

System devices

SCALE · קנה מידה	DATE · תאריך	REV	גיליון
S/E	15/10/2026	B	02

בסיס: תוכניות האדריכל L5 (זוג מסד / Triplet) · מידות במטרים

פורמט A1 · מהדורה B – על התוכנית האמיתית

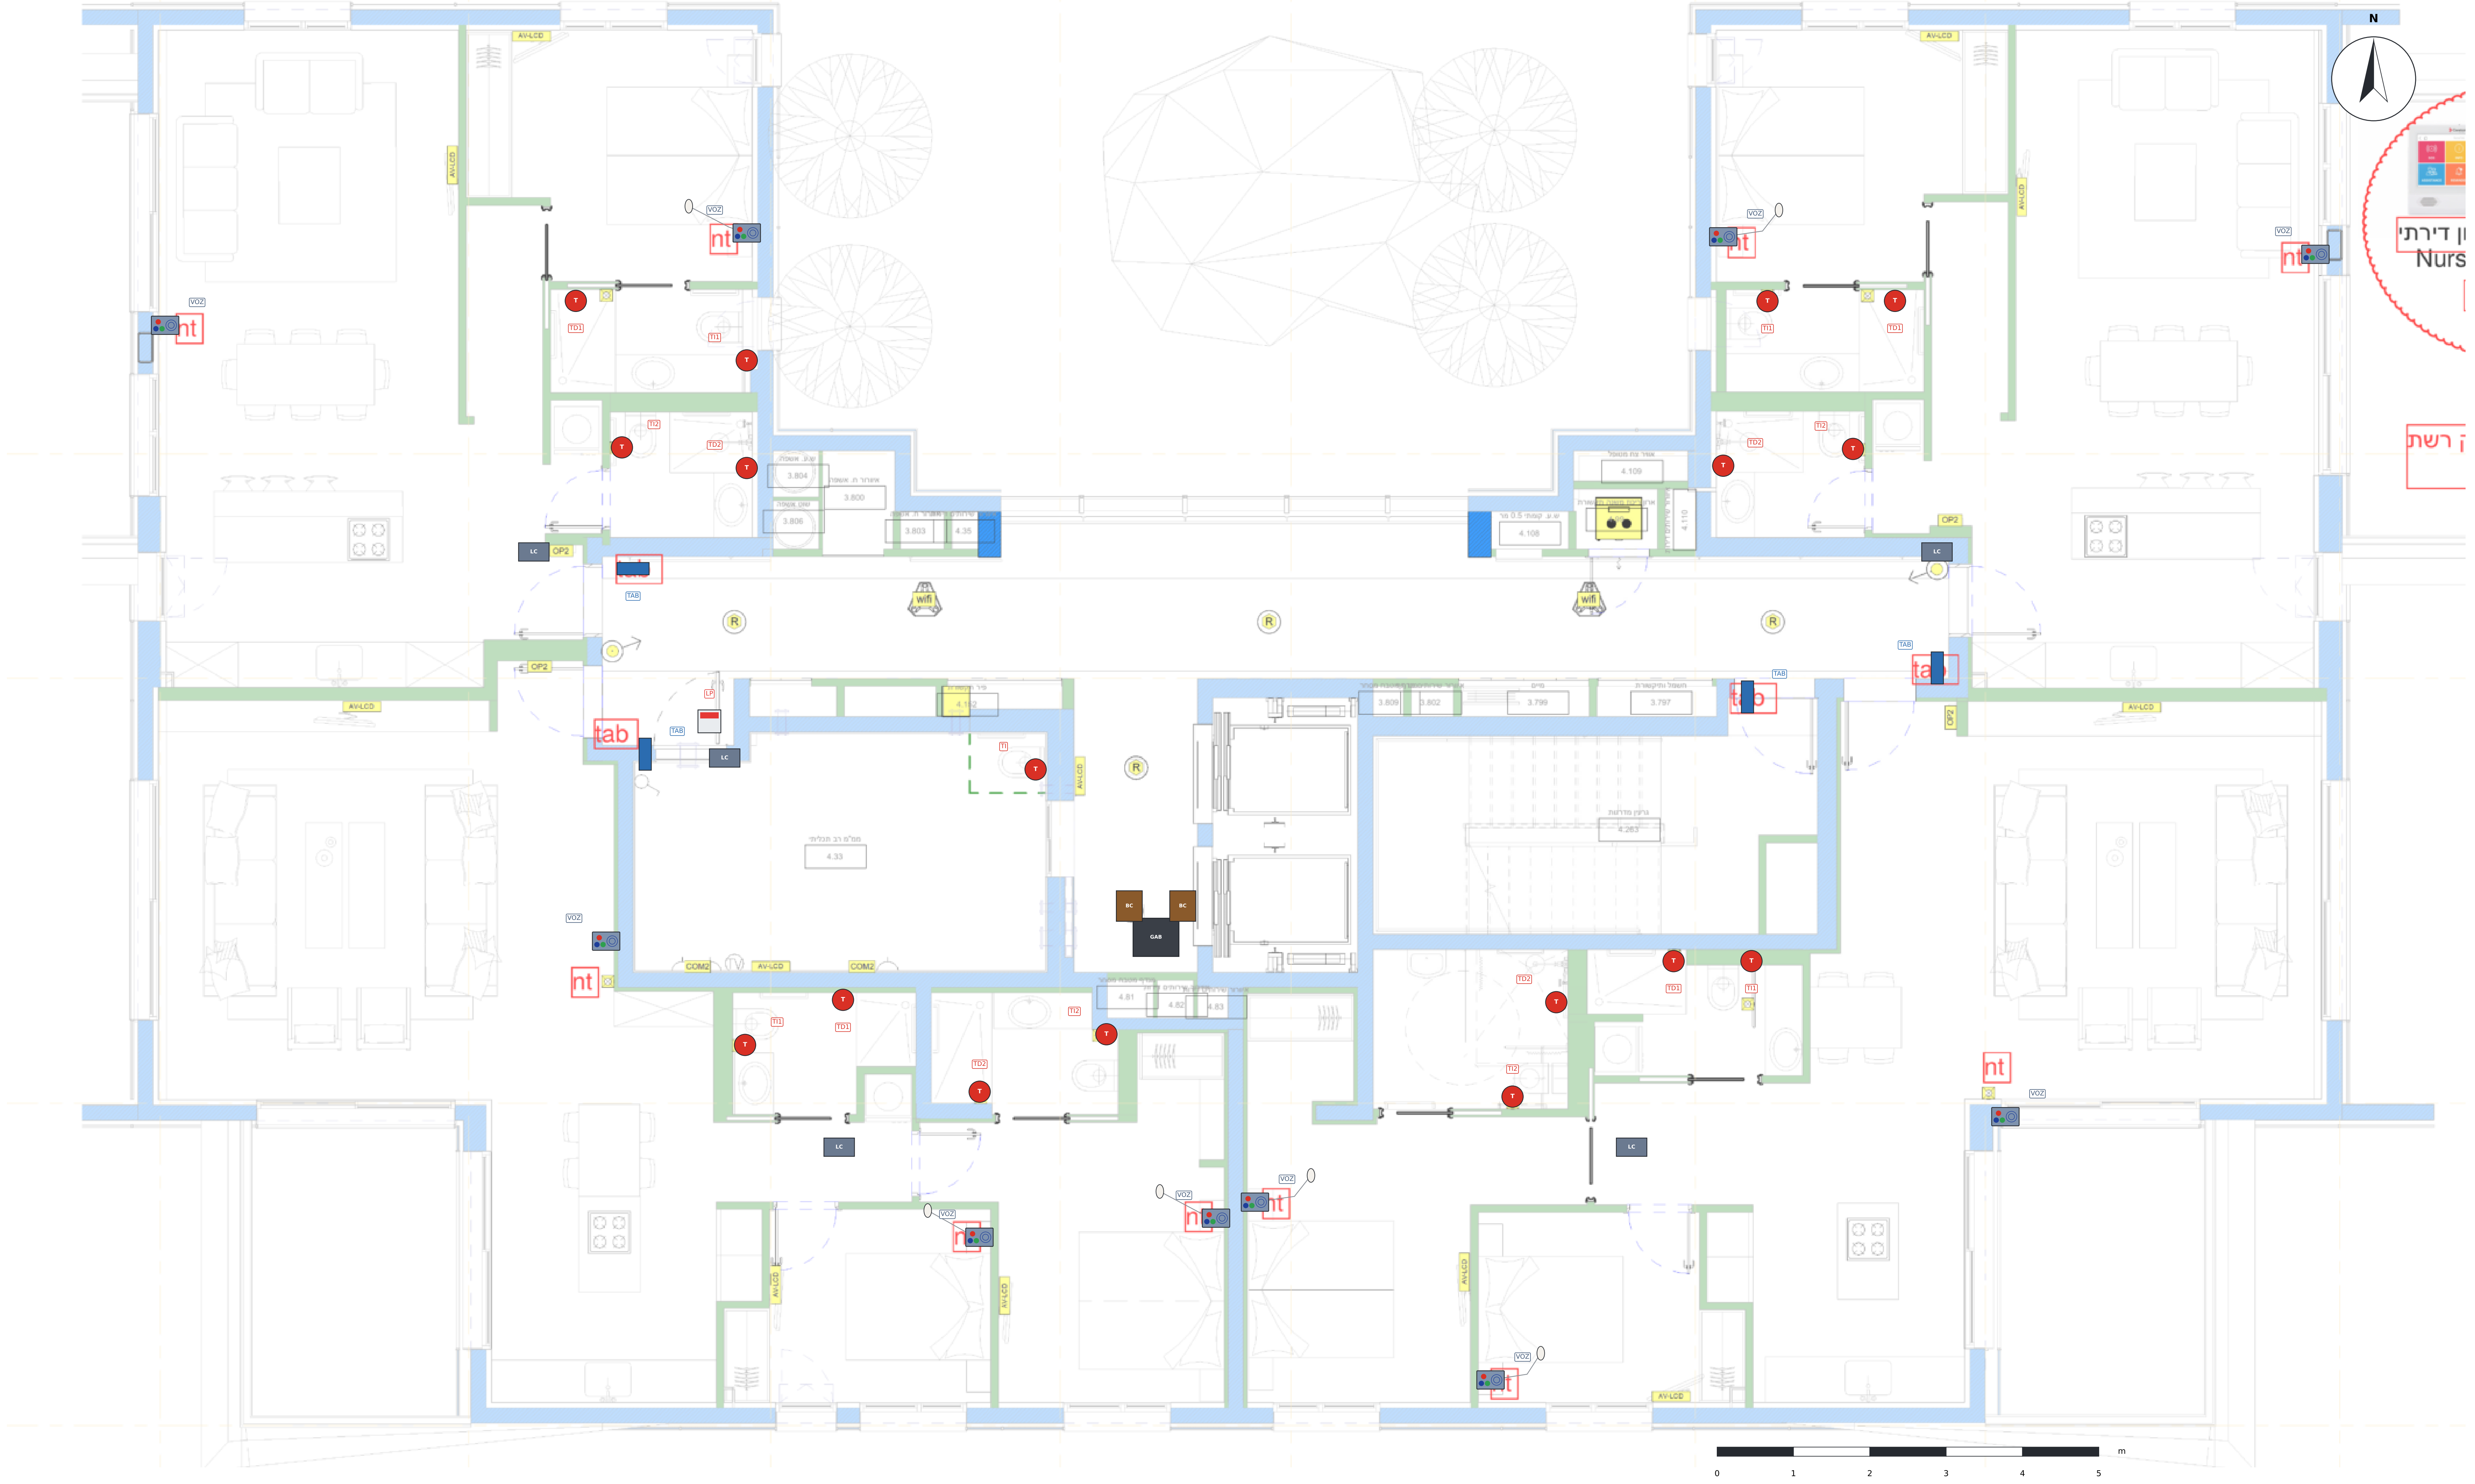

NOTES · תורעה

1. רקע: תינכות IT L2 לש חוקלה םע םינומיסה ולש םודאב:
«nt» = לנפ ילוק ו-«tab» = טלבאט הסינכב.

2. לעמ, עבצב: הזיוד העצהב וז.
לכ לנפ ילוקו טלבאט םיאצמנ םוקמב שהלקוח םימ|.

L2 3. הריבועים םיבוהצה ⊠ ירדחב הרחצה תינכותב
הם תוכישמ לבחה (תחלקמו הלסא).

4. 4 םיטלבאטה יבולב, לכ תלד ליד הריד,
.«tab» ומכ ינומיס

5. תוינכותל L2 ו-L5 (העצהה סיסב) אותו הנבמ;
L5 8 איה הקומה תיסופיטה לקומות 1 דע.

DEVICES · EQUIPOS · דויצ

🟦	TAB · טלבאט הסינכב (iPad / דיאורדנא) – רובידו האירק, הבוג 1.40 מ' Door tablet – call and voice · טלבאט הסינכב – רובידו האירק
▦	VOZ · םינצחל םע ילוק לנפ ACE82182451 – ןולס ירדחו הניש, הבוג 1.20–1.30 מ' Voice panel with buttons – living room and bedrooms · ןולס ירדחו הניש – םינצחל םע ילוק לנפ
○	הטימה דיל האירק סגא (הנישה ירדחב) Call pear next to the bed (bedrooms) · הטימה דיל האירק סגא
T	TI / TD · לבח תכישמ ACE40320303W – הלסא תחלקמו, הבוג 1.85 מ' Pull-cord – toilet and shower, h 1.85 m · לבח תכישמ – הלסא תחלקמו, הבוג 1.85 מ'
🟥	LP · תרונמ ןורדסמ ACE41020309 – לעמ תלד לכ םיתוריש םייזוביצ Corridor light – above each public toilet door · תרונמ ןורדסמ – לעמ תלד לכ םיתוריש םייזוביצ

שירותים קריאת אחות

לבח תכישמ

טבלט אנדרואיד קריאת אחות

Advantecnia
Llamada de enfermera
Hospital
Salud y bienestar

(דיאורדנא / iPad) טלבאט הסינכב

מנורה קריאת אחות

ןורדסמ תרונמ

פנל קריאת אחות

םינצחל םע ילוק לנפ

ןגומ רויד · ןוכיתה םי ילדגמ

תוריד 32 · תומוק 8 + עקרק – תוחא תאירק

Telab International :ןכוה י"ע   ACE BG · Advantecnia :תכרעמ

העצההו (תינכות L2) חוקלה ינומיס

Client marks (plan L2) and proposal

SCALE · הדימ הנק	DATE · ךיראת	REV	ןוילג
1:60	15/10/2026	B	03

בסיס: תינכות לכירדאה L5 (זוע דסמ / Triplet) · םירטמב תודימ

טמרופ A1 · הרודהמ B – לע תינכותה תיתימאה

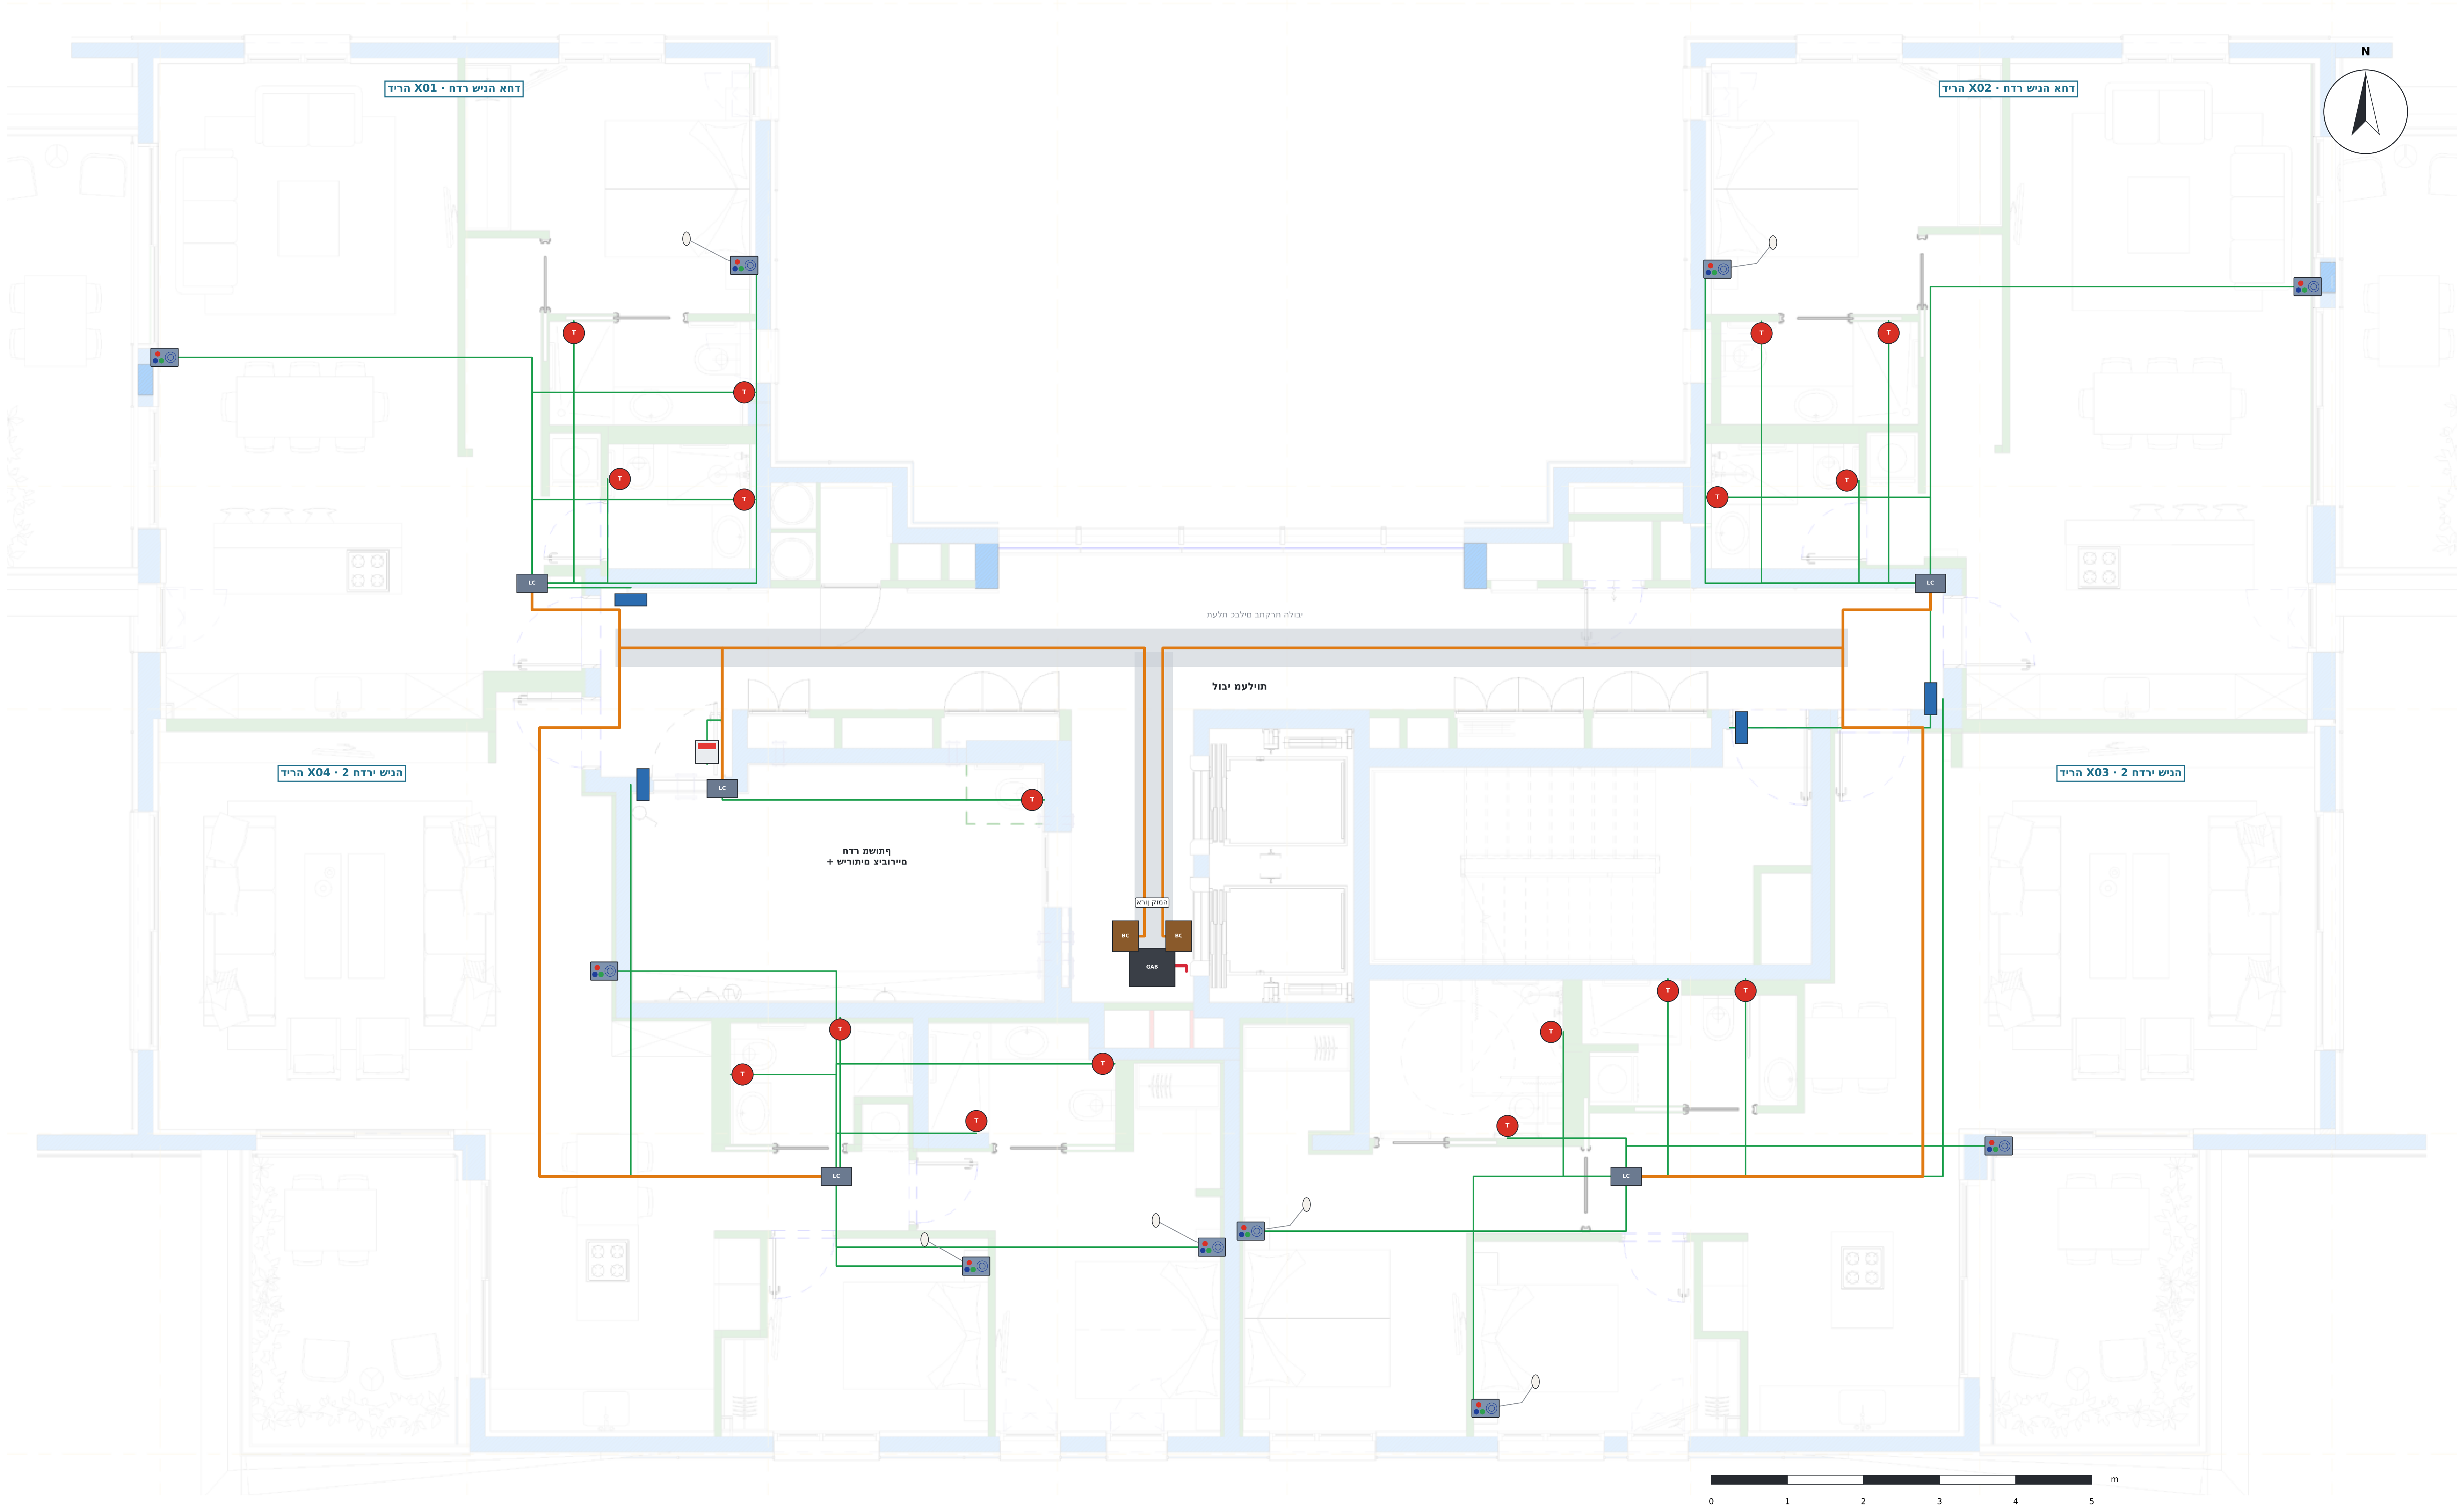

WIRING · CABLEADO · טוויח

🟩 Cat6 ילאידר: לכ ןקתה ← LCom לש הרידה
Cat6 radial: each device → apartment LCom · Cat6 ילאידר: לכ ןקתה ← LCom לש הרידה

🟧 Cat6 / Cat7 תרשרש: LCom ← LCom ← BoxCom הרקתב
Cat6 / Cat7 chain: LCom → LCom → BoxCom · Cat6 / Cat7 תרשרש: LCom ← LCom ← BoxCom

🟥 Cat6A / Cat7 תשר: BoxCom ← גתמ PoE ← דומע ← תרש עקרק
Cat6A / Cat7 network: BoxCom → switch → riser → GF server · Cat6A / Cat7 תשר: BoxCom ← גתמ ← דומע ← תרש

םיכרוא בקומה תיסופיט (אלל רזבה)

🟩	Cat6 ילאידר ךותב הרידות	**183 m**
🟧	Cat6 / Cat7 תרשרש LCom ← BoxCom	**80 m**
🟥	Cat6A / Cat7 ןורא ועמוד	**7 m**

NOTES · תורעה

1. לכ ןקתה רבוחמ תילאידר (Cat6) ל-LCom לש הרידה, בתקרת האובמה.

2. ה-LCom םירשורשמ תבלעתה יבולה דע ה-BoxCom בתקרה,
.BoxCom 1 · x02 ← x03 ← BoxCom 2 ← רדח םתושף ← x01 ← x04 :ליד הארון

3. ה-BoxCom םירדוי גתמל ה-PoE בארון; גתמה עולה
דומעב Cat6A / Cat7 דע תרשה בקרקע.

4. לוכה PoE: ןיא ךרוצ ב-230V ינקתהל הרידות.

NOTES · תורעה

1. סיסב: תינכות תילכירדא L5 (המוק תיסופיט) – 8 תומוקה תוהז: 4 תוריד המוקב, 32 ךסב הכול.
2. תוריד x01 ו-x02: רדח הניש דחא, ןולס םע חבטמ ו-2 ירדח הצחר. תוריד x03 ו-x04: 2 ירדח הניש ו-2 ירדח הצחר.
3. טלבאט הסינכב לכל הריד (iPad / דיאורדנא) הריקבל ורובידלו םע תוחאה.
4. לנפ ילוק םע םינצחל (ACE82182451) ןולסב ובכל רדח הניש; בחדר השינה םע גאס דיל הטימה.
5. תוכישמ לבח (ACE40320303W) הלסאב ובמקלחת לכב ירדח הצחרה, הבוגב 1.85 מ'.
6. םיתוריש םייריבוצ לכב המוק רדחב השמותף: תכישמ לבח + תרונמ ןורדסמ לעמ הלדת. םע 2 בקרקע – 10 םיתוריש םייריבוצ.
7. ןורא המוק דיל תוילעמה םע גתמ PoE D-Link DES-1210-28P; 2 ה-BoxCom הרקתב ודיל.
8. םימוקימ יפל ינומיס הלקוח תוכינתב L2 (nt = לנפ ילוק, tab = טלבאט): ואר ןוילג 03.

ןגומ רויד · ןוכיתה םי ילדגמ

תוריד 32 · תומוק 8 + עקרק – תוחא תאירק

Telab International :ןכוה ע"י   ACE BG · Advantecnia :תכרעמ

טוויח · 1–8 תיסופיט המוק

Typical floor F1–F8 · wiring

SCALE · הדימ הנק	DATE · ךיראת	REV	ןוילג
1:60	**15/10/2026**	**B**	**04**

סיסב: תינכות לכירדאה L5 (זוע דסמ / Triplet) · םירטמב תודימ

טמרופ A1 · הרודהמ B – לע תינכותה תיתימאה

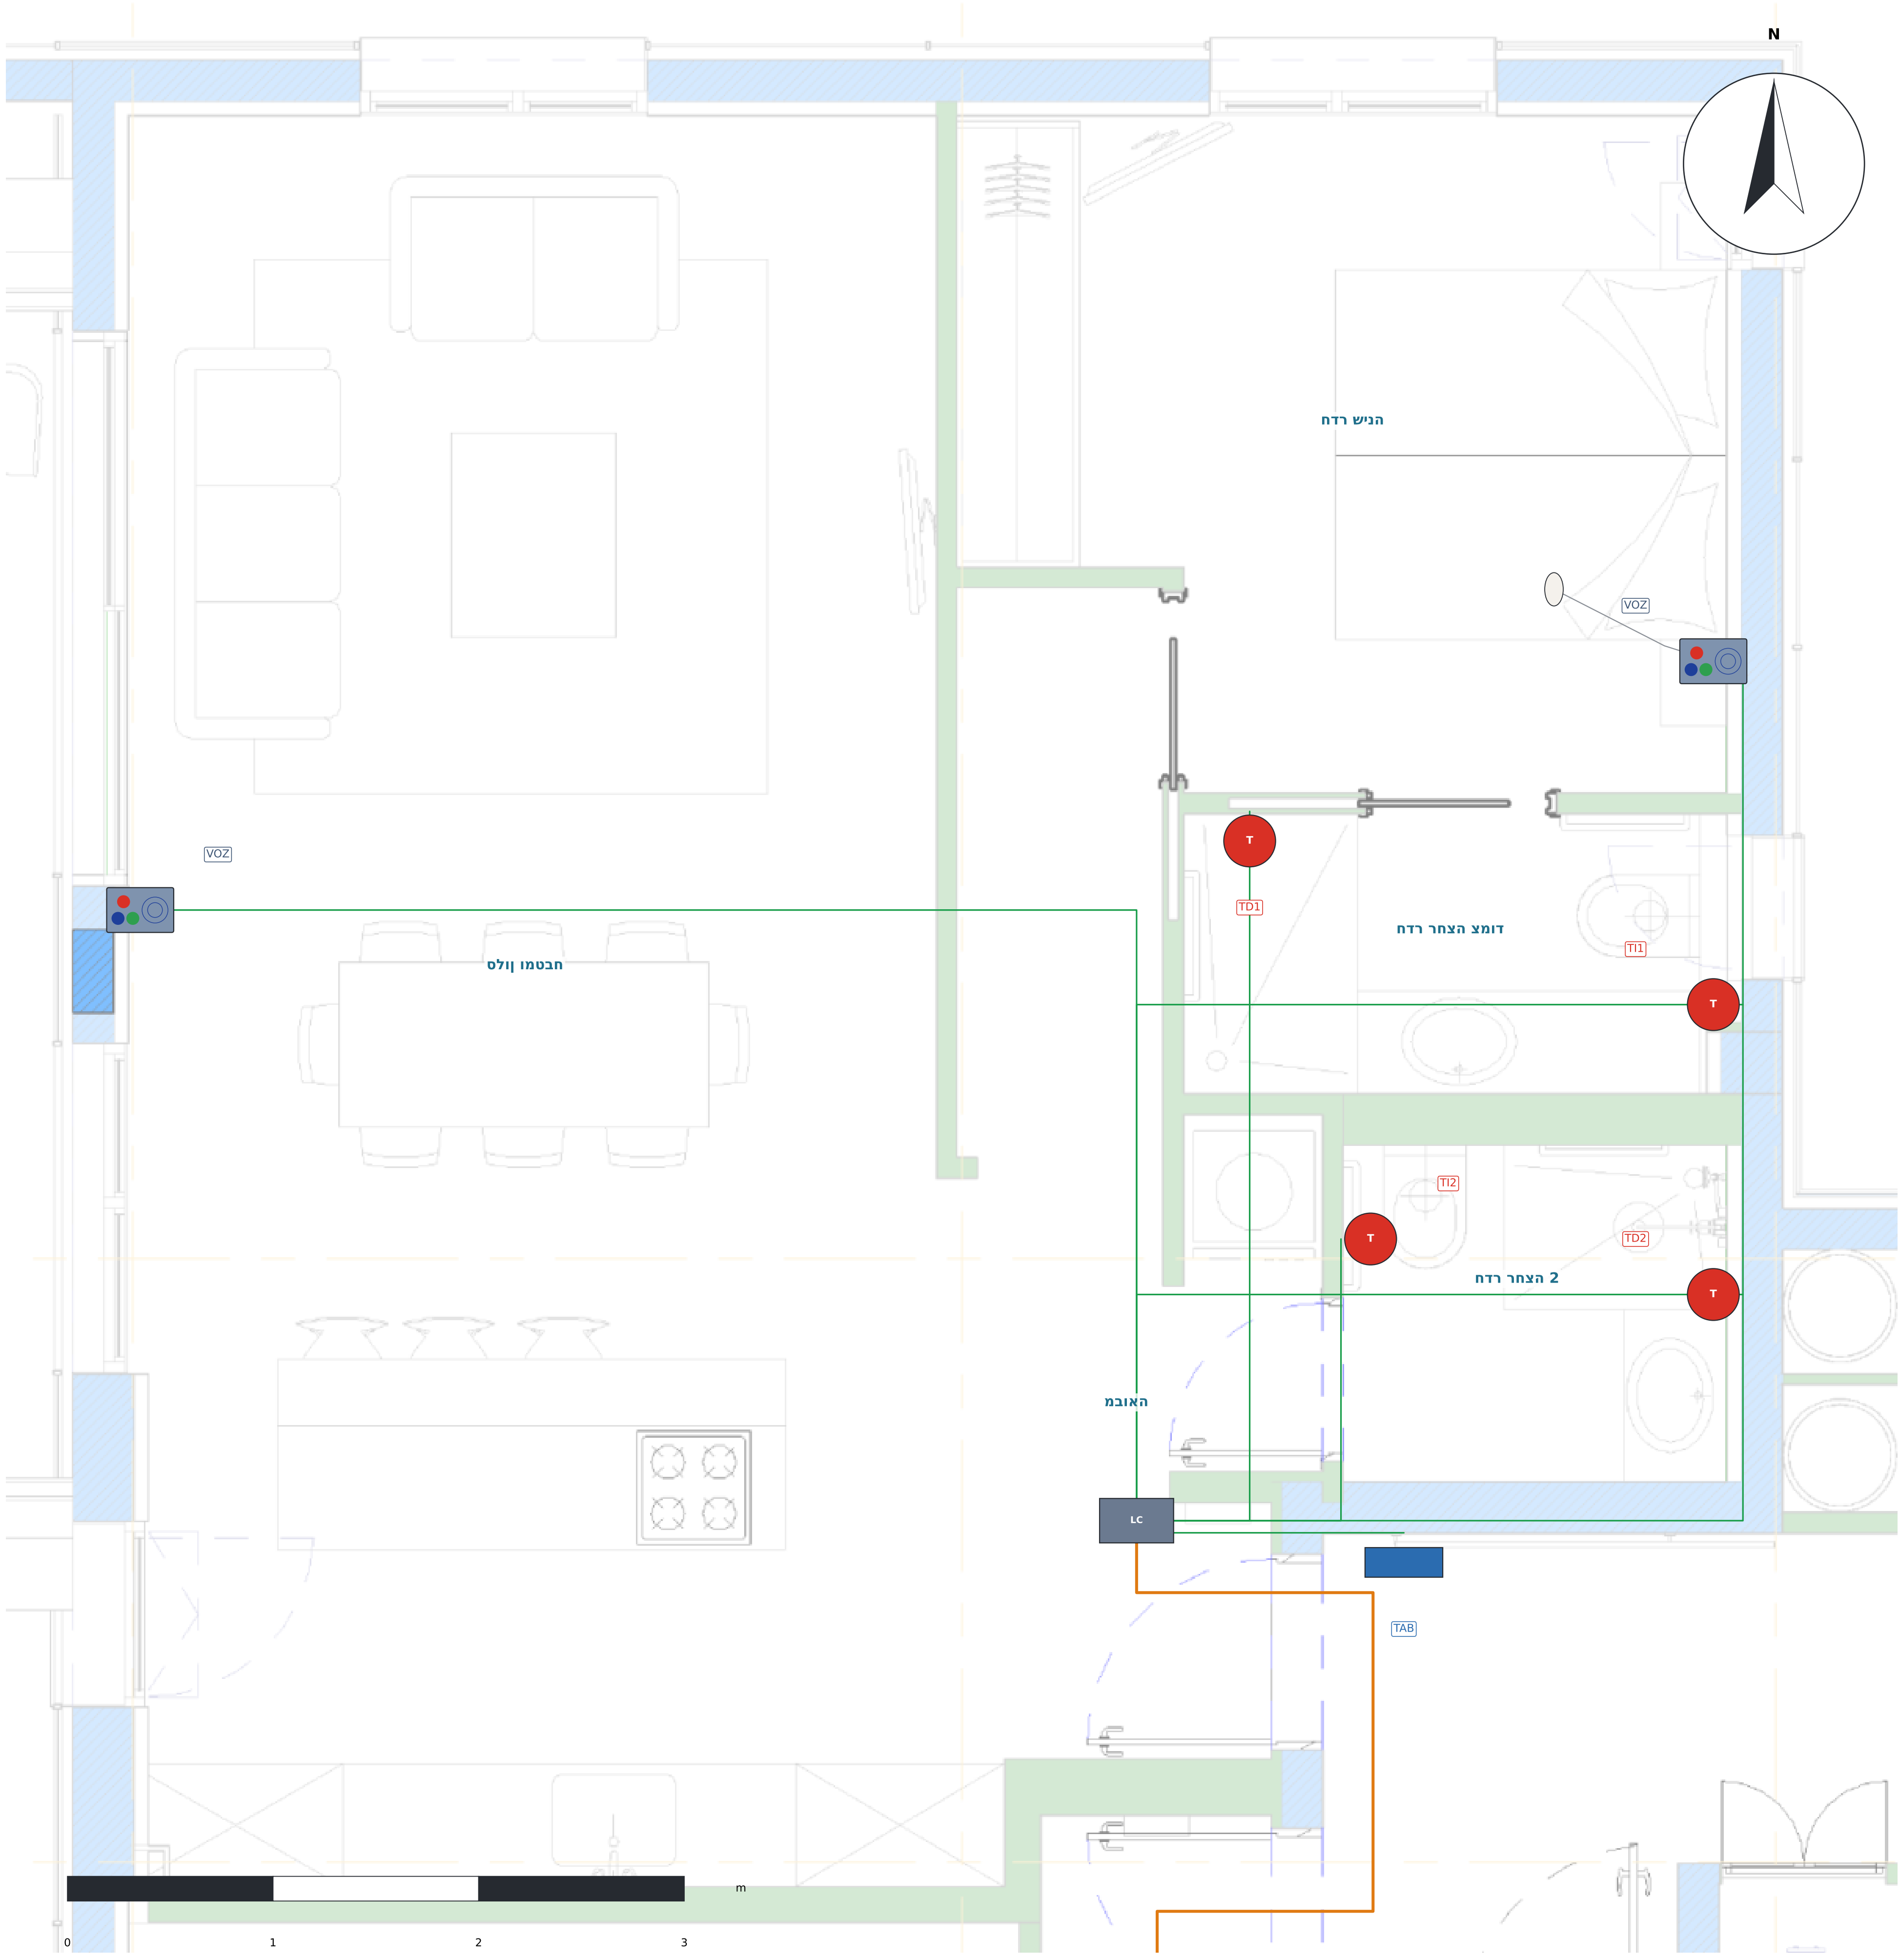

הרידה דויצ

ID	ןקתה	רדח	הבוג
TAB	הסינכב טלבאט	האובמ	1.40 מ'
VOZ-S	פנל קולי עם לחצנים	חבטמו וולס	1,30 m
VOZ-D	פנל קולי עם לחצנים + אגס	הניש רדח	1,20 m
TI1	לבח תכישמ	דומצ הצחר רדח	1.85 מ'
TD1	לבח תכישמ	דומצ הצחר רדח	1.85 מ'
TI2	לבח תכישמ	2 הצחר רדח	1.85 מ'
TD2	לבח תכישמ	2 הצחר רדח	1.85 מ'
LCOM	LCom ACE71610003	האובמ	2,55 m

SYMBOLS · SÍMBOLOS · םילמס

🟦	TAB · הסינכב טלבאט (iPad / דיאורדנא) – רובידו האירק, הבוג 1.40 מ' Door tablet – call and voice · הסינכב טלבאט – רובידו האירק
▦	VOZ · פנל קולי עם לחצנים ACE82182451 – וולס ירדחו הניש, הבוג 1.20–1.30 מ' Voice panel with buttons – living room and bedrooms · פנל קולי עם לחצנים – וולס ירדחו הניש
○	אגס קריאה דיל הטימה (הנישה ירדחב) Call pear next to the bed (bedrooms) · אגס קריאה דיל הטימה
T	TI / TD · לבח תכישמ ACE40320303W – הלסא ומקלחת, הבוג 1.85 מ' Pull-cord – toilet and shower, h 1.85 m · לבח תכישמ – הלסא ומקלחת, הבוג 1.85 מ'
🟥	LP · ןורדסמ תרונמ ACE41020309 – מעל דלת לכ שירותים ציבוריים Corridor light – above each public toilet door · ןורדסמ תרונמ – מעל דלת לכ שירותים ציבוריים
LC	LC · LCom ACE71610003 – הרידה זכרמ (הרקת) LCom – apartment hub (ceiling) · LCom – הרידה זכרמ (הרקת)
BC	BC · BoxCom ACE70810000 – תוריד המכל סאב זכרמ (הרקת) BoxCom – bus hub for several apartments (ceiling) · BoxCom – תוריד המכל סאב זכרמ (הרקת)

NOTES · תורעה

1. הריד x02 איה תנומת יאר לש x01 (דויצ ותוא).
2. טלבאט יבולב, דיל תלד הסינכה (ןומיס «tab» לש חוקלה).
3. פנל קולי ןולסב רדחבו הנישה (עם אגס דיל הטימה).
4. 2 ירדח הצחר: תכישמ לבח הלסאב ומקלחתב לכב דחא (4 תוכישמ לבח).
5. לוכה רבוחמ תילאידר ב-Cat6 ל-LCom האובמב.

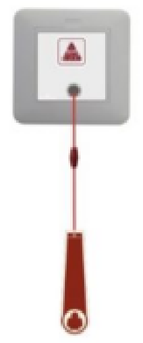
שירותים קריאת אחות

לבח תכישמ

טבלט אנדרואיד קריאת אחות

הסינכב טלבאט (iPad / דיאורדנא)

מנורה קריאת אחות

ןורדסמ תרונמ

פנל קריאת אחות

פנל קולי עם לחצנים

ןגומ רויד · ןוכיתה םי ילדגמ
תוריד 32 · תומוק 8 + עקרק – תוחא תאירק
Telab International :ןכוה ע"י ACE BG · Advantecnia :תכרעמ

(x01 / x02) דחא הניש רדח תריד

1-bedroom apartment (x01 / x02)

SCALE · הדימ הנק	DATE · ךיראת	REV	ןוילג
1:30	**15/10/2026**	**B**	**05**

סיסב: לכירדאה תינכות L5 (זוע דסמ / Triplet) · םירטמב תודימ
טמרופ A1 · הרודהמ B – לע התינכות תיתימאה

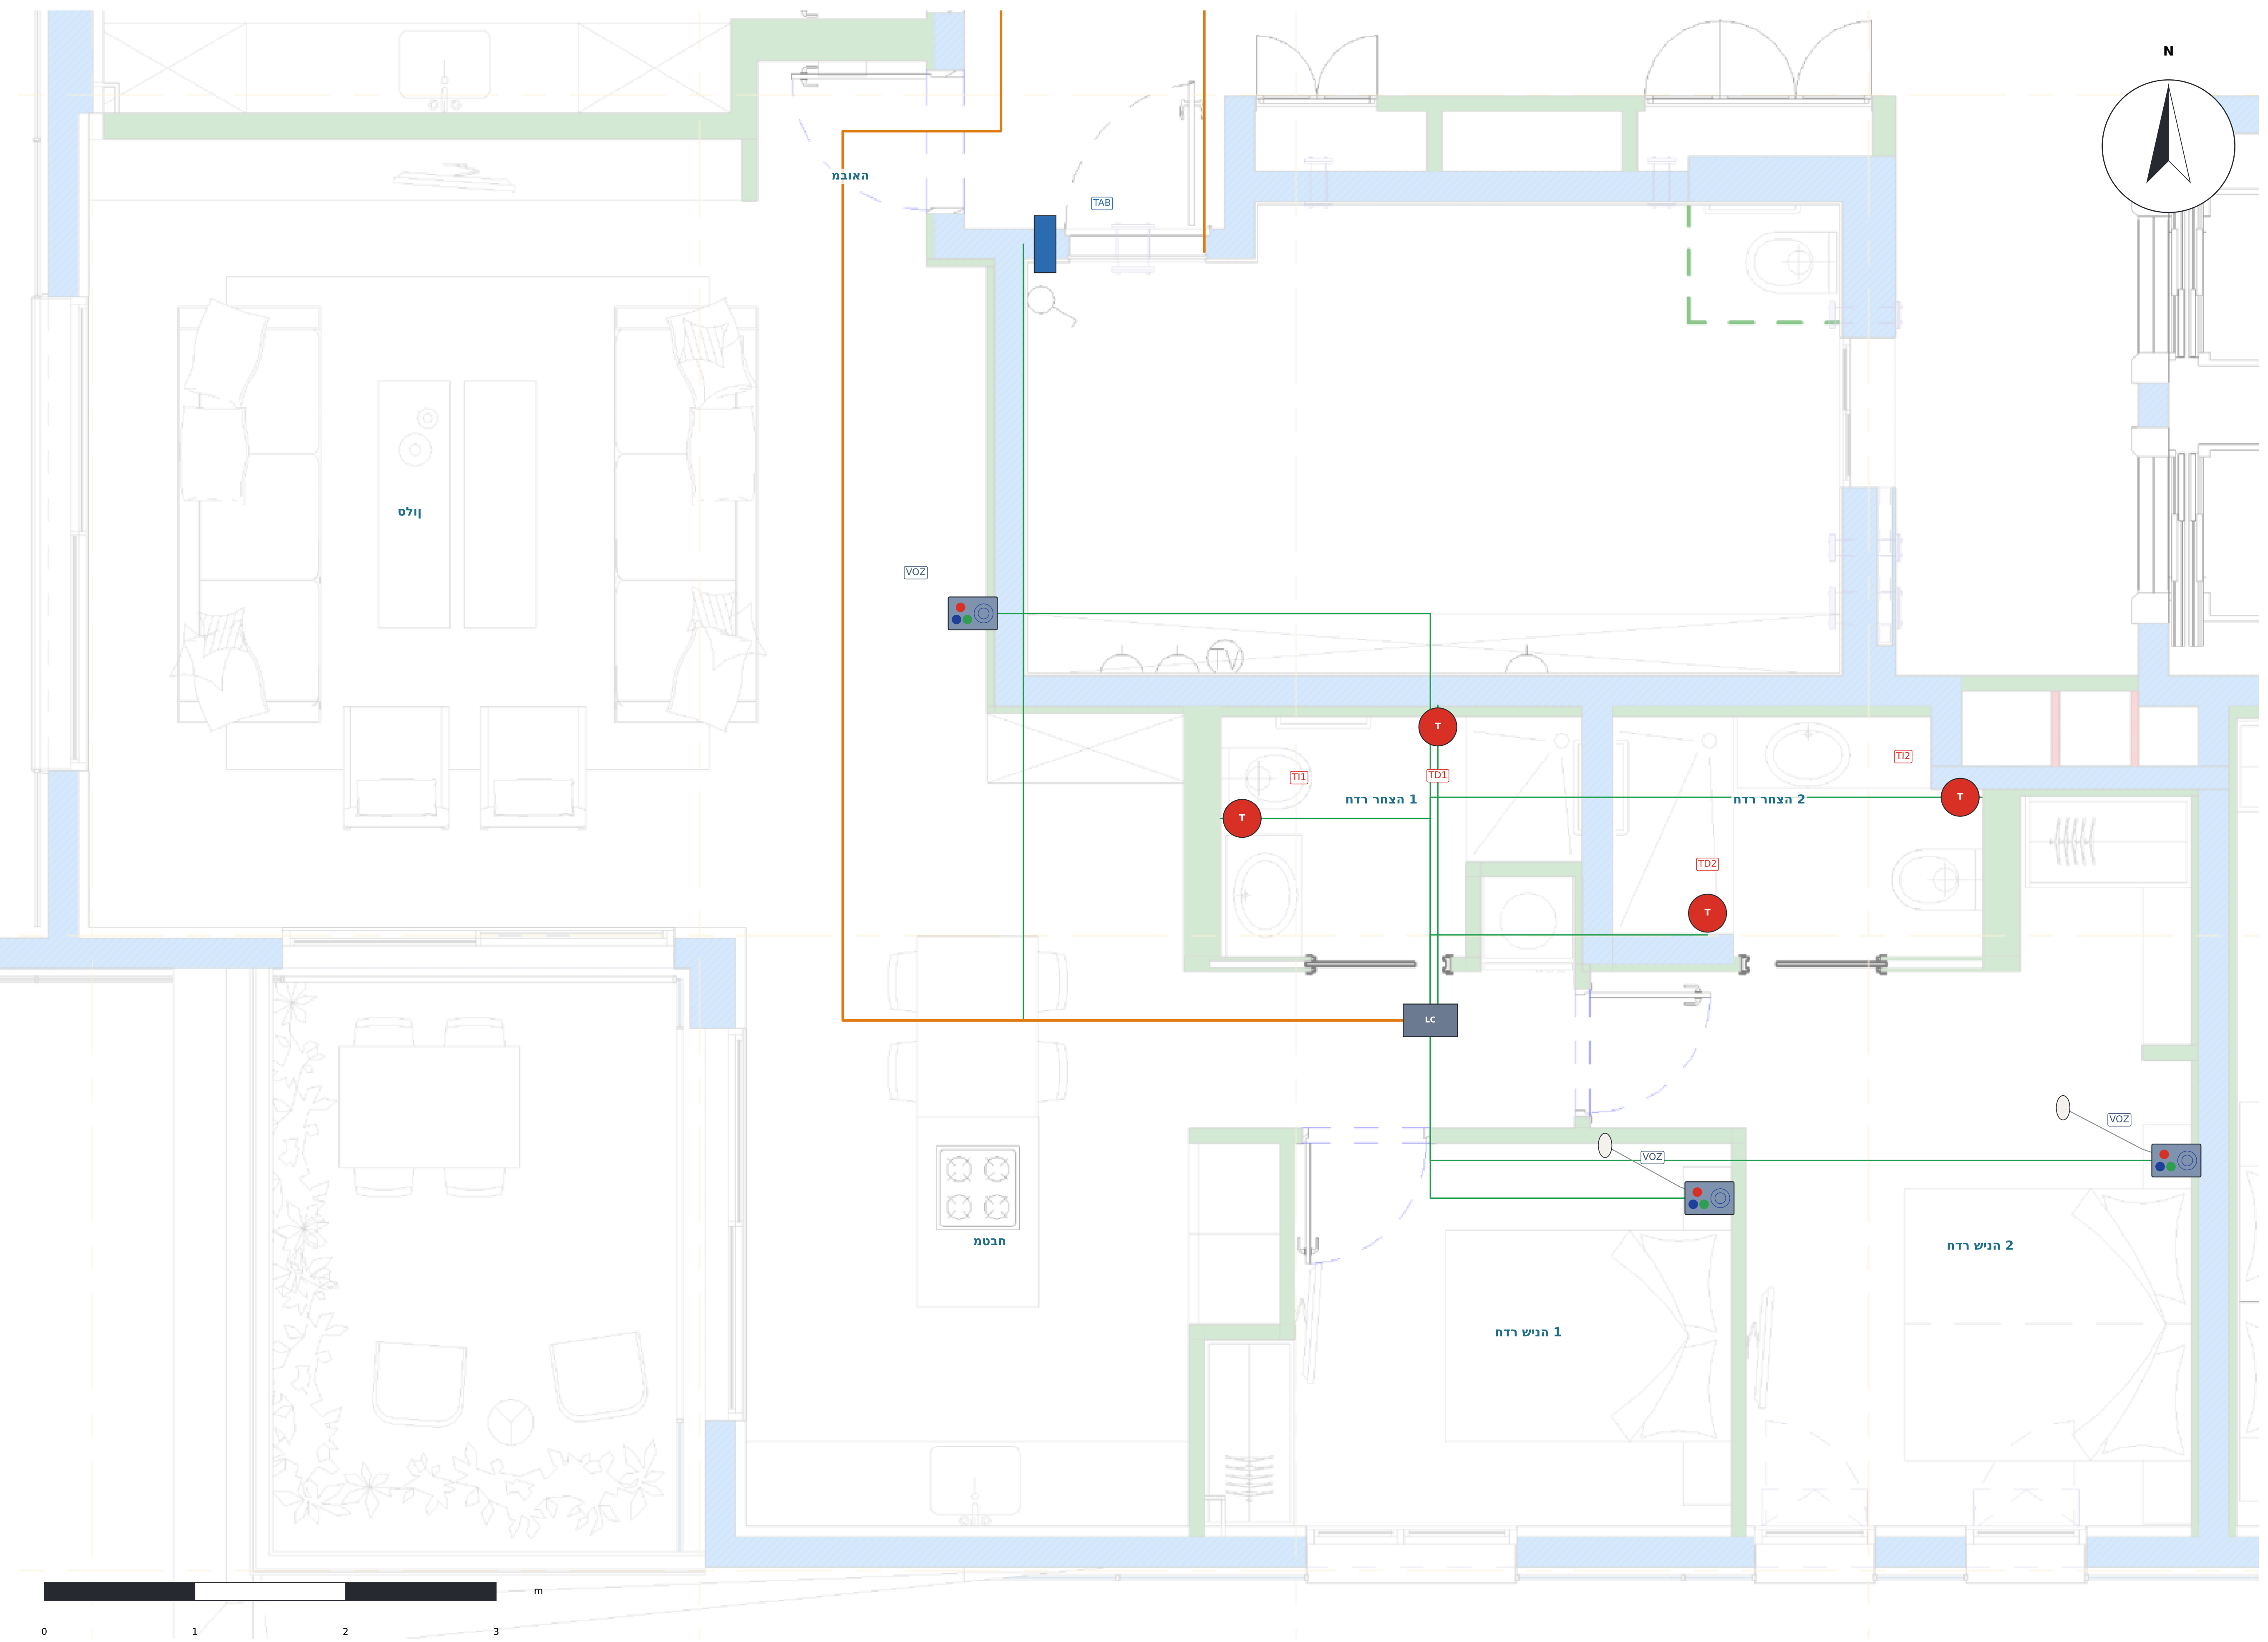
N
האובמ
TAB
ןולס
VOZ
הצחר רדח 1
הצחר רדח 2
TI1
TD1
TI2
TD2
T
LC
חבטמ
הניש רדח 1
הניש רדח 2
0
1
2
3
m

הרידה דויצ

ID	ןקתה	רדח	הבוג
TAB	הסינכב טלבאט	האובמ	1.40 מ'
VOZ-S	םינצחל םע ילוק לנפ	ןולס	1,30 m
VOZ-D1	סגא + םינצחל םע ילוק לנפ	הניש רדח 1	1,20 m
VOZ-D2	סגא + םינצחל םע ילוק לנפ	הניש רדח 2	1,20 m
TI1	לבח תכישמ	הצחר רדח 1	1.85 מ'
TD1	לבח תכישמ	הצחר רדח 1	1.85 מ'
TI2	לבח תכישמ	הצחר רדח 2	1.85 מ'
TD2	לבח תכישמ	הצחר רדח 2	1.85 מ'
LCOM	LCom ACE71610003	האובמ	2,55 m

SYMBOLS · SÍMBOLOS · םילמס

🟦	TAB · הסינכב טלבאט (iPad / דיאורדנא) – רובידו האירק ,הבוג 1.40 מ' Door tablet – call and voice · הסינכב טלבאט – רובידו האירק
▨	VOZ · םינצחל םע ילוק לנפ ACE82182451 – ןולס ירדחו הניש ,הבוג 1.20–1.30 מ' Voice panel with buttons – living room and bedrooms · םינצחל םע ילוק לנפ – ןולס ירדחו הניש
○	הטימה דיל האירק סגא (הנישה ירדחב) Call pear next to the bed (bedrooms) · הטימה דיל האירק סגא
T	TI / TD · לבח תכישמ ACE40320303W – הלסא תחלקמו ,הבוג 1.85 מ' Pull-cord – toilet and shower, h 1.85 m · לבח תכישמ – הלסא תחלקמו ,הבוג 1.85 מ'
🟥	LP · ןורדסמ תרונמ ACE41020309 – לעמ תלד לכ יתורש םיירוביצ Corridor light – above each public toilet door · ןורדסמ תרונמ – לעמ תלד לכ יתורש םיירוביצ
LC	LC · LCom ACE71610003 – הרידה זכרמ (הרקת) LCom – apartment hub (ceiling) · LCom – הרידה זכרמ (הרקת)
BC	BC · BoxCom ACE70810000 – סאב זכרמ לכמה תוריד (הרקת) BoxCom – bus hub for several apartments (ceiling) · BoxCom – סאב זכרמ לכמה תוריד (הרקת)

NOTES · תורעה

1. הרידב x03 דויצ ותוא (ירדח הצחרה הסירפב הנוש).
2. טלבאט ,יבולב דיל תלד הסינכה (ןומיס «tab» לש חוקלה).
3. לנפ ילוק ןולסב ינשבו ירדח הנישה (םע סגא דיל הטימה).
4. 2 ירדח הצחר: תכישמ לבח הלסאב תחלקמבו לכב דחא (4 תוכישמ לבח).
5. לוכה רבוחמ תילאידר ב-Cat6 ל-LCom ןורדסמב ירדח הנישה.

שירותים קריאת אחות
לבח תכישמ

טבלט אנדרואיד קריאת אחות
Advantecnia
TV
Llamada de enfermera
Hospital
Salud y bienestar
הסינכב טלבאט (iPad / דיאורדנא)

מנורה קריאת אחות
ןורדסמ תרונמ

פנל קריאת אחות
םינצחל םע ילוק לנפ

ןגומ רויד · ןוכיתה םי ילדגמ
תוריד 32 · תומוק 8 + עקרק – תוחא תאירק
Telab International :ןכוה י"ע   ACE BG · Advantecnia :תכרעמ

(x04 / x03) הניש ירדח ינש תריד
2-bedroom apartment (x04 / x03)

SCALE · הדימ הנק	DATE · ךיראת	REV	ןויליג
1:35	15/10/2026	B	06

סיסב: תונכות הלכירדאה L5 (םדמ זוע / Triplet) · םירטמב תודימ
טמרופ A1 · הרודהמ B – לע תונכותה תיתימאה

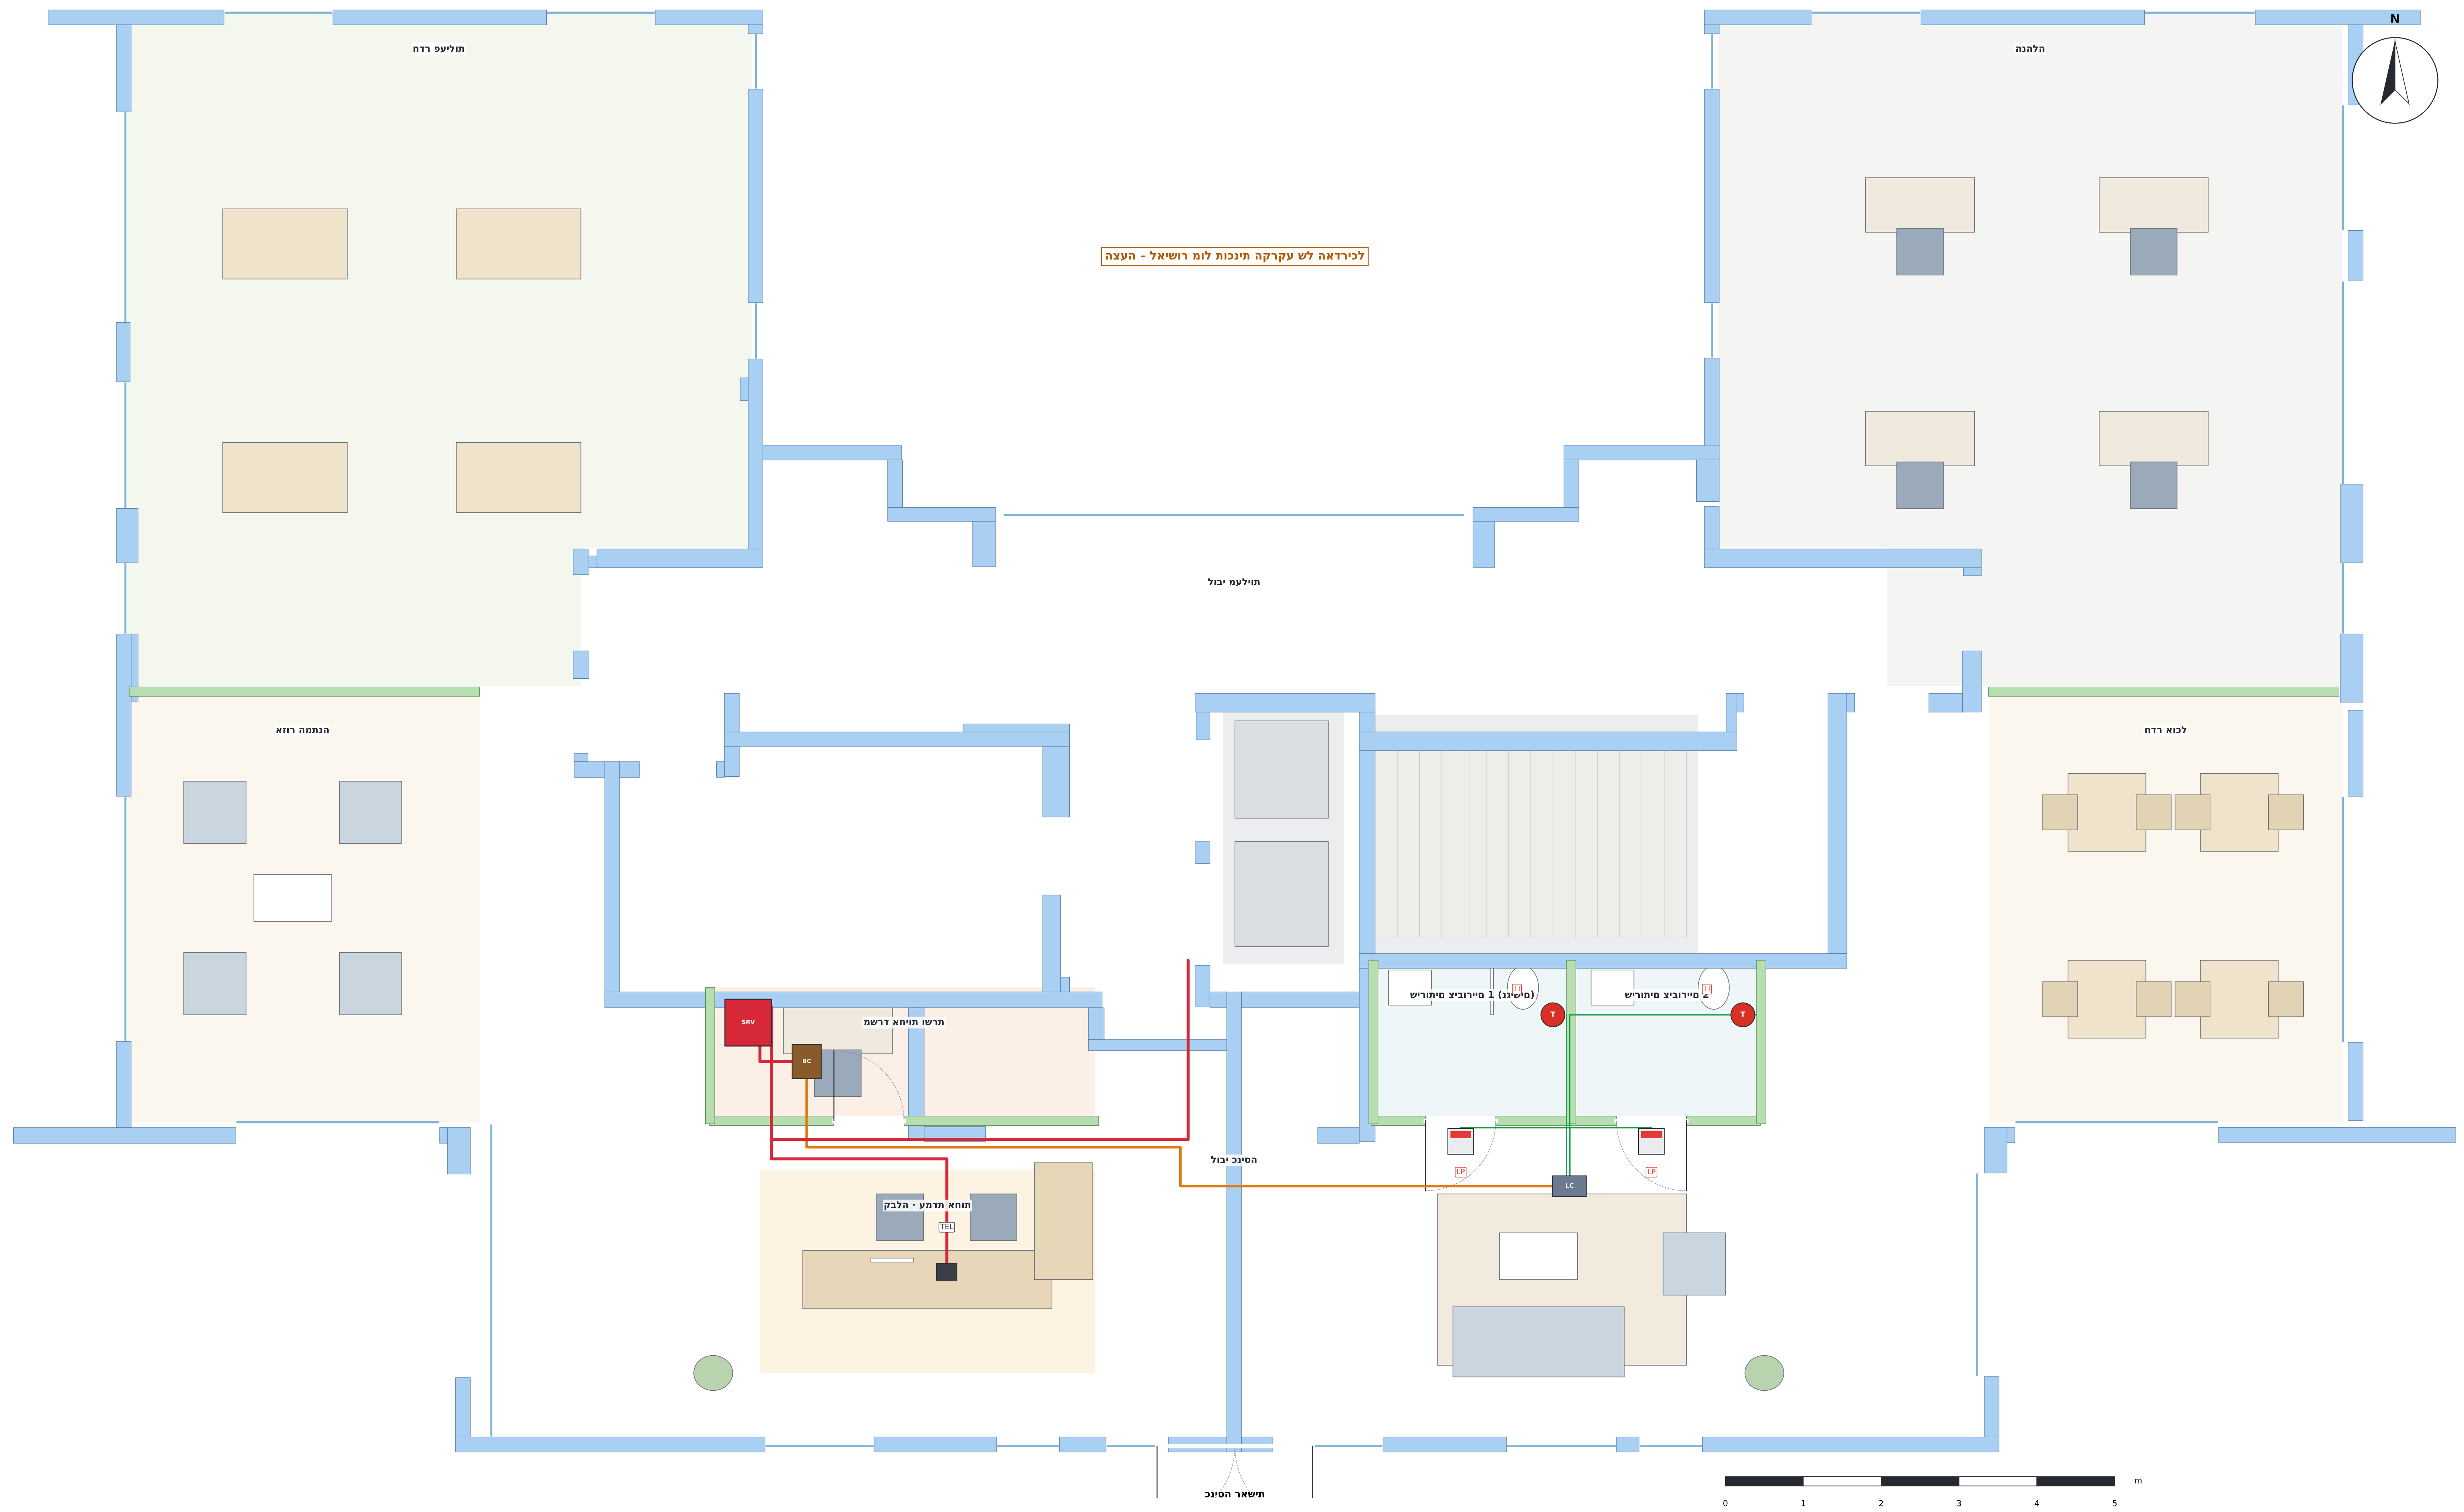

תוליעפ רדח
הלהנה
N
לכירדאה לש עקרקה תינכות לומ רושיאל – העצה
תוילעמ יבול
הנתמה רוזא
לכוא רדח
משרד אחיות ושרת
SRV
BC
קבלה · עמדת אחות
TEL
שירותים ציבוריים 1 (נגישים)
שירותים ציבוריים 2
T
TI
LP
LC
הסינכ יבול
תישאר הסינכ
0
1
2
3
4
5
m

טרפ · תוחא תדמעו הלבק (1:40)

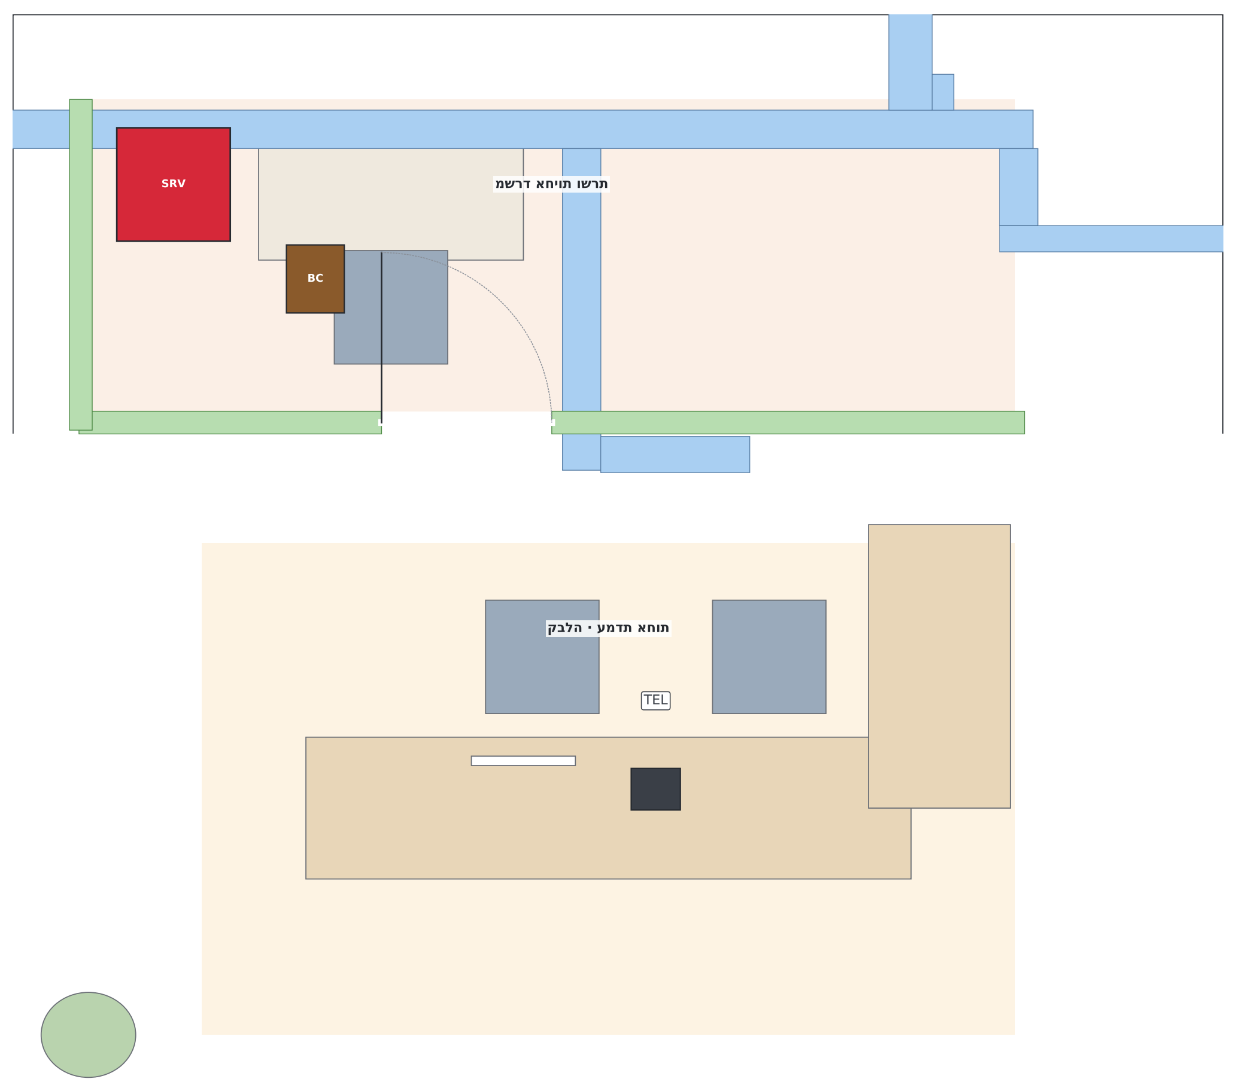

SRV
BC
משרד אחיות ושרת
קבלה · עמדת אחות
TEL

NOTES · תורעה

1. תוילעמהו הסינכה לומ ,הלבקב תוחאה תדמע.
2. לע הדמעה: ןופלט Grandstream דיאורדנא, רבוחמ ישירות למתג ה-PoE. לכ הארק תגצומ עבצב הלש.
3. מאחורי הדמעה: משרד עם ארון השרת: שרת Buslogic Premium ומתג PoE D-Link. BoxCom לש הקרקע בתקרה.
4. 2 שירותים ציבוריים בקרקע: משיכת חבל ליד האסלה ומנורת מסדרון מעל כל דלת.
5. העמוד מ-8 קומות דרך גרעין עד הארון הראשי.
6. פרטים קרקע מוצעת: תשכגע ןדכות לש תוכניתה לכירדאה.

SYMBOLS · SÍMBOLOS · םילמס

- **T** TI / TD · משיכת חבל ACE40320303W – אסלה ומקלחת, גובה 1.85 מ'
  Pull-cord – toilet and shower, h 1.85 m · משיכת חבל – אסלה ומקלחת, גובה 1.85 מ'
- **LC** LC · LCom ACE71610003 – מרכז הרידה (הרקת)
  LCom – apartment hub (ceiling) · LCom – מרכז הרידה (הרקת)
- **SRV** SRV · ארון קרקע: שרת Buslogic Premium + מתג PoE D-Link
  GF rack: Buslogic Premium server + D-Link PoE switch · ארון קרקע: שרת Buslogic Premium + מתג PoE D-Link
- 🟥 LP · מנורת מסדרון ACE41020309 – מעל דלת כל שירותים ציבוריים
  Corridor light – above each public toilet door · מנורת מסדרון – מעל דלת כל שירותים ציבוריים
- **TEL** TEL · ןופלט Grandstream דיאורדנא – PoE ישירות למתג
  Grandstream Android phone – PoE straight to the switch · ןופלט Grandstream דיאורדנא – PoE ישירות למתג
- **BC** BC · BoxCom ACE70810000 – מרכז באס לכמה דירות (הרקת)
  BoxCom – bus hub for several apartments (ceiling) · BoxCom – מרכז באס לכמה דירות (הרקת)

ןופלט הדמעה – הזיא עבצ גצומ

🟥	(SOS / הכישמ) הקעזא	מודא
🟩	תוחכונ: תחא םעפ קורי ןצחל	קורי
⬜	הקעזא וא הארקל לטבמ: בוש קורי ןצחל	קחמנ
🟦	(blue call) לוחכ ןצחל: הארק תאירק	לוחכ
🟧	תילוק החיש	מותכ / בוהצ

ןגומ רויד · ןוכיתה םי ילדגמ
תוריד 32 · תומוק 8 + עקרק – תוחא תאירק
Telab International :ןכוה ע"י ACE BG · Advantecnia :תכרעמ

תוחא תדמעו יבול · עקרק תמוק

Ground floor · lobby and nurse desk

SCALE · הדימ הנק	DATE · ךיראת	REV	ןוילג
1:60	15/10/2026	B	07

בסיס: תוכנית תינכות לכירדאה L5 (זוג דסמ / Triplet) · םירטמב תודימ
פורמט A1 · הרודהמ B – לע התוכנית תיתימאה

א · ןיינב עקרק + 8 תומוק

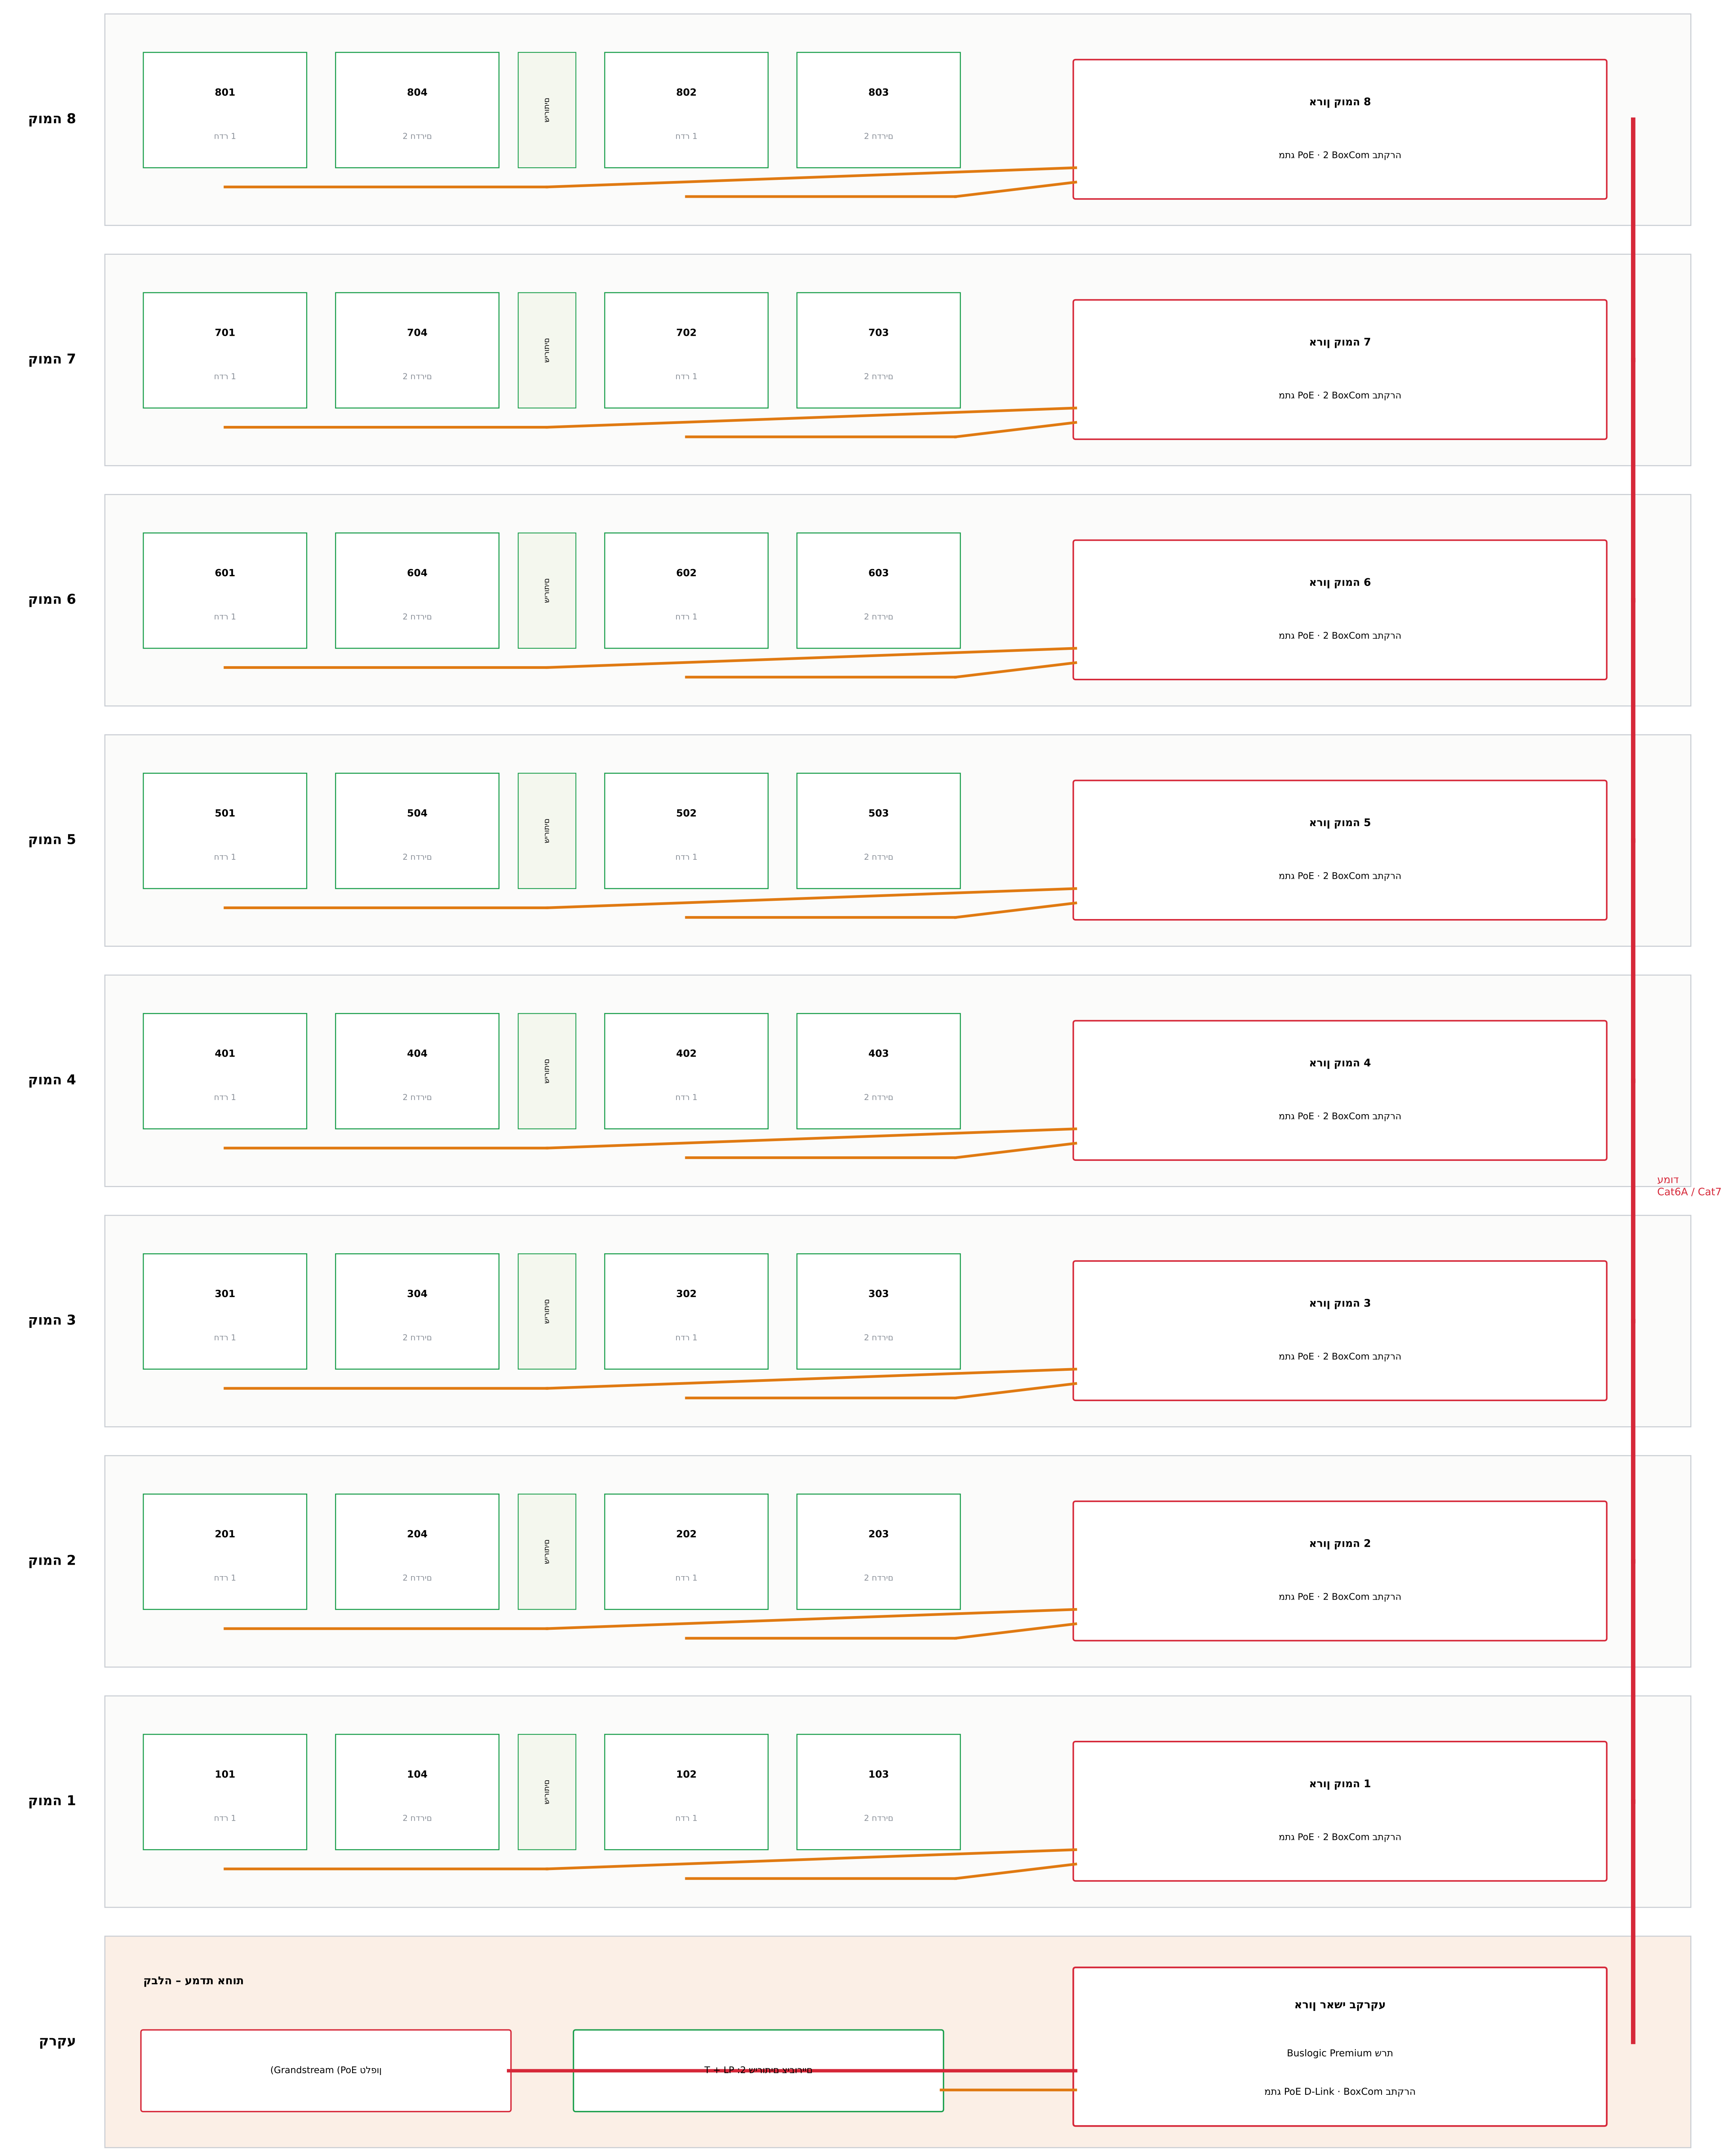
8 המוק
801
1 רדח
804
2 םירדח
םיתוריש
802
1 רדח
803
2 םירדח
8 המוק ןורא
גתמ PoE · 2 BoxCom הרקתב
7 המוק
701
704
702
703
7 המוק ןורא
6 המוק
601
604
602
603
6 המוק ןורא
5 המוק
501
504
502
503
5 המוק ןורא
4 המוק
401
404
402
403
4 המוק ןורא
3 המוק
301
304
302
303
3 המוק ןורא
2 המוק
201
204
202
203
2 המוק ןורא
1 המוק
101
104
102
103
1 המוק ןורא
עקרק
תוחא תדמע – הלבק
(Grandstream (PoE ןופלט
T + LP :2 םיתוריש םיירוביצ
עקרקב ישאר ןורא
Buslogic Premium תרש
גתמ PoE D-Link · BoxCom הרקתב
דומע
Cat6A / Cat7

ב · הריד לש היגולופוט

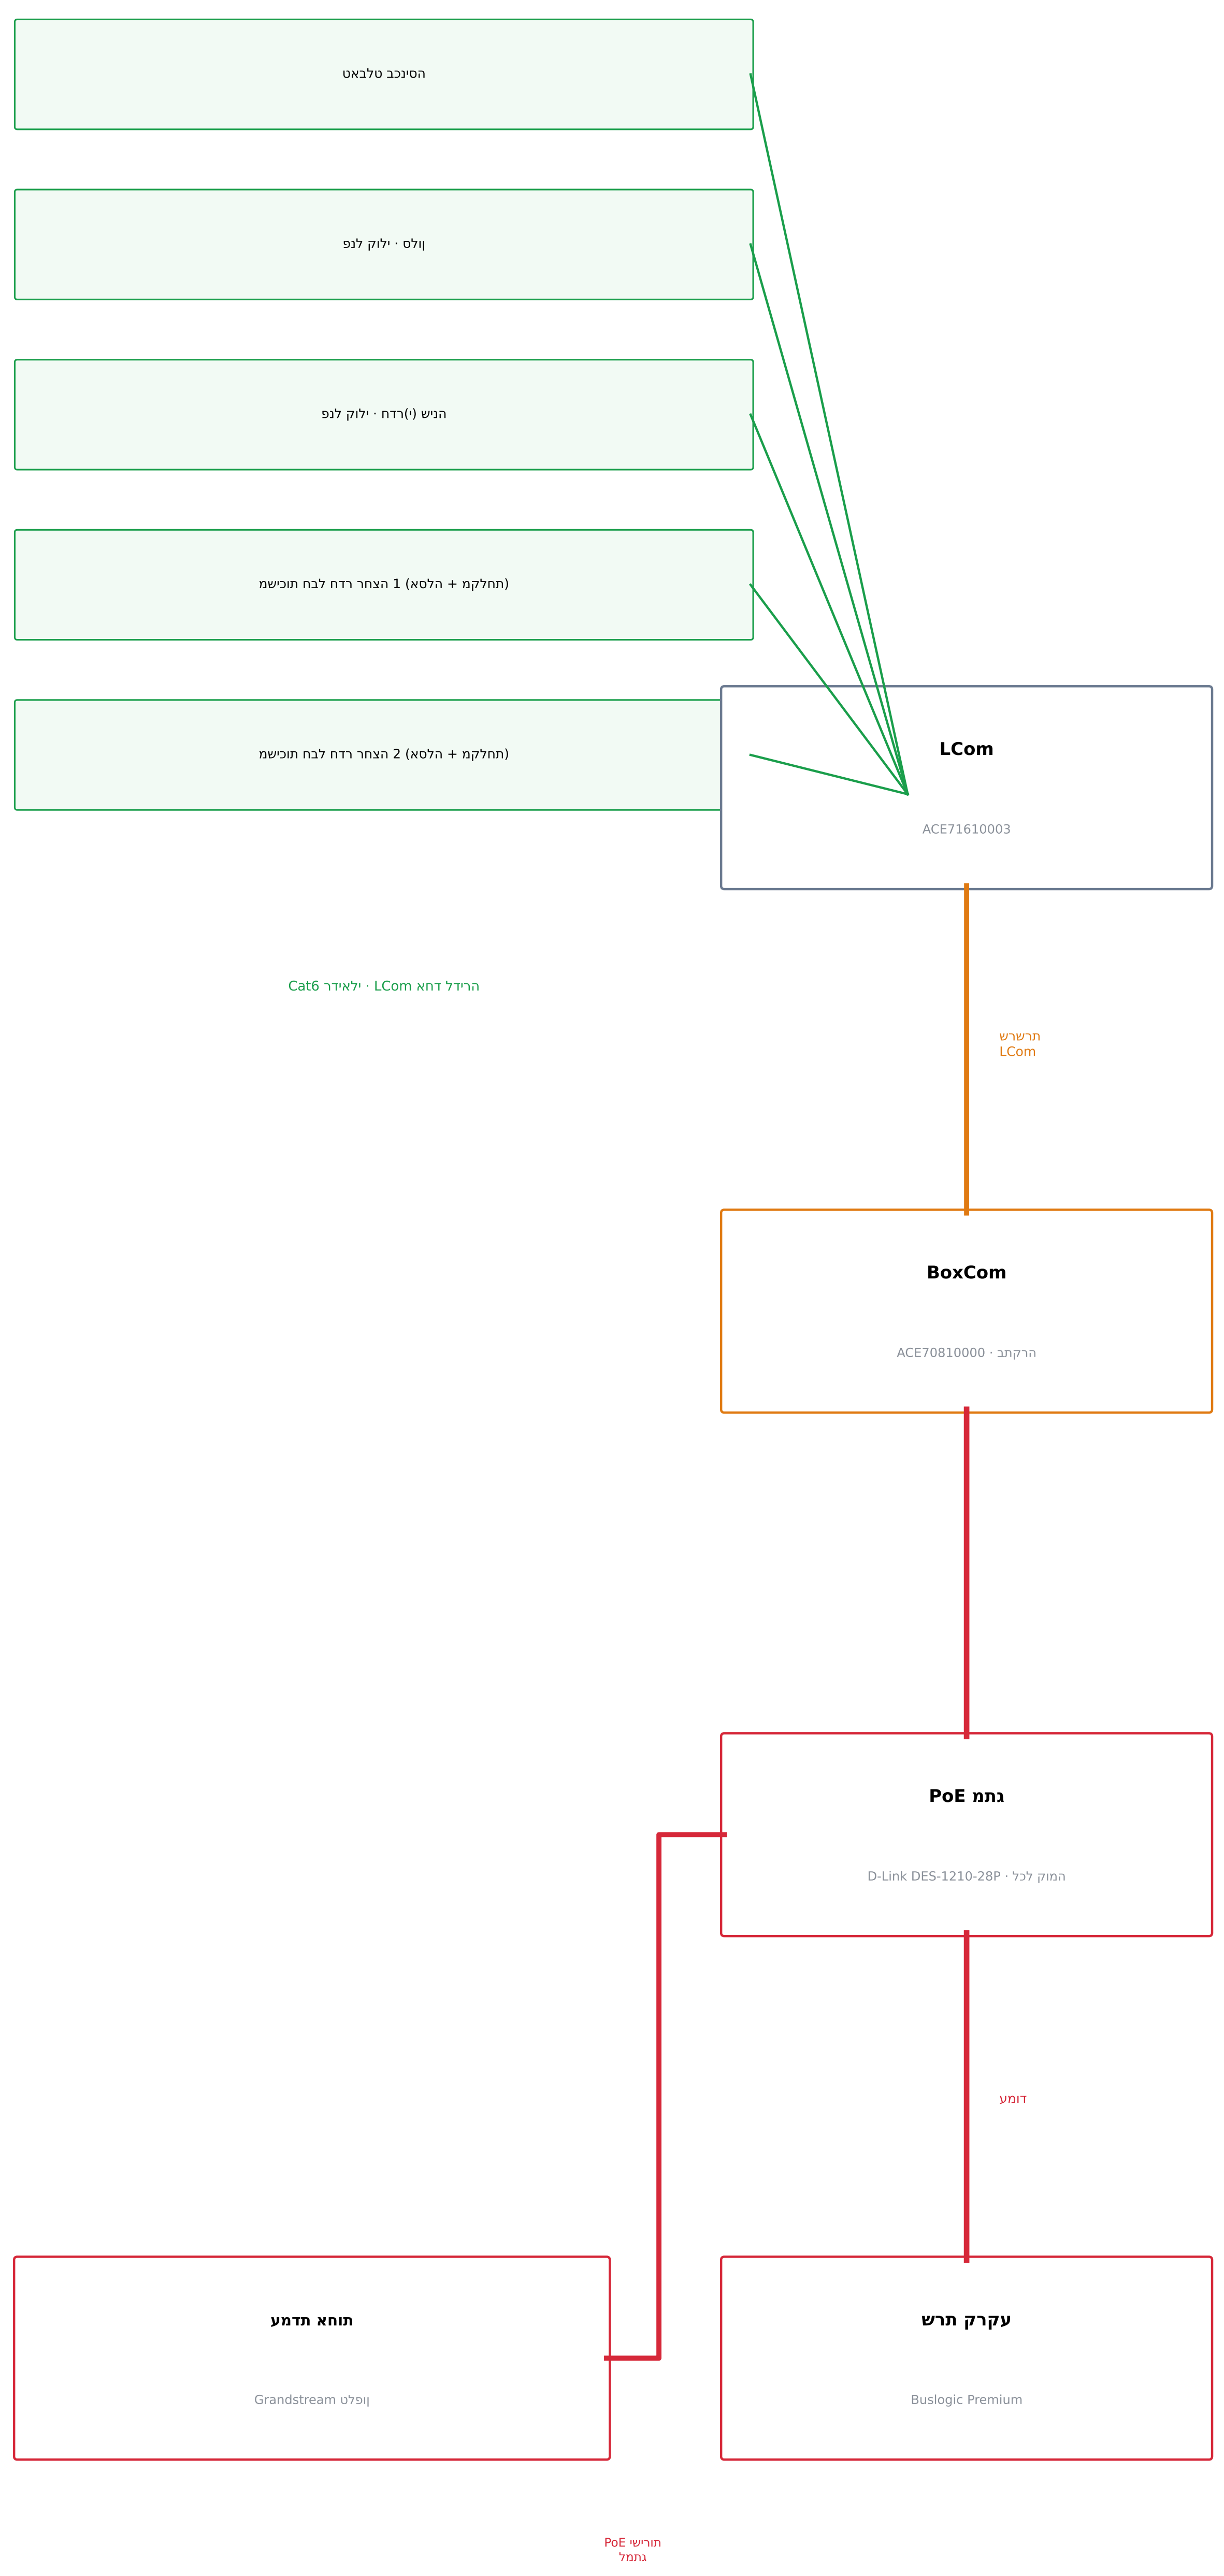
טאבלט הסינכב
ןולס · ילוק לנפ
הניש (י)רדח · ילוק לנפ
תוכישמ לבח רדח הצחר 1 (הלסא + תחלקמ)
תוכישמ לבח רדח הצחר 2 (הלסא + תחלקמ)
LCom
ACE71610003
Cat6 ידיאלי · LCom דחא הרידל
תרשרש
LCom
BoxCom
ACE70810000 · הרקתב
PoE גתמ
D-Link DES-1210-28P · לכל המוק
דומע
תוחא תדמע
Grandstream ןופלט
עקרק תרש
Buslogic Premium
PoE תורישי
גתמל

NOTES · תורעה

1. 8 תומוק תוהז םע 4 תוריד
(2 תוריד רדח הניש דחא ו-2 תוריד ינש ירדח הניש).

2. לכב המוק: BoxCom 2 הרקתב
.PoE-ה גתמ םע ןוראו

3. תרשרש x01 ← x04 :1 ← םיתוריש םיירוביצ.
.x02 ← x03 :2 תרשרש

4. םיגתמה םירבוחמ ךרד דומעה
דע ןוראה ישארה עקרקב.

5. ןופלט ה-Grandstream הדמעב רבוחמ
תורישי גתמל ה-PoE גיצמו
לכ האירק עבצב הלש.

.PoE 6. לכ תכרעמה

7. תומיוכ תוינושאר: תמאל
לומ Advantecnia רתאבו.

ןגומ רויד · ןוכיתה םי ילדגמ

תוריד 32 · תומוק 8 + עקרק – תוחא תאירק

Telab International :ןוכה ע"י   ACE BG · Advantecnia :תכרעמ

היגולופוטו יכנא םישרת

Riser diagram and topology

SCALE · הדימ הנק	DATE · ךיראת	REV	ןוילג
S/E	**15/10/2026**	**B**	**08**

סיסב: תוינכות הארדיכל L5 (זוג דסמ / Triplet) · םירטמב תודימ

טמרופ A1 · הרודהמ B – לע תוינכותה תויתימאה

רשימת חומרים – כל הבניין (קרקע + 8 תומוק · 32 תוריד · 10 םיתוריש םייֵרוביצ)

דוק	רואית	תומכ	הרעה
תורידב (32)			
TAB	הסינכב טלבאט (iPad / דיאורדנא) – רובידו האירק	**32**	1 הריד לכל
VOZ	ACE82182451 – סינצחל םע ילוק האירק לנפ	**80**	הניש רדח לכ + וולס
TI/TD	משכית לבח – ACE40320303W (תחלקמו הלסא)	**128**	4 הריד לכל
LC	LCom – ACE71610003	**32**	1 הריד לכל
שירותים ציבוריים (10)			
T	ACE40320303W – משכית לבח	**10**	8 תומוק + 2 עקרקב
LP	ACE41020309 – מנורת מסדרון	**10**	תלד לכ לעמ
LC	LCom – ACE71610003	**9**	1 לכל המוק + 1 עקרקב
ארונות ומרכזייה			
BC	BoxCom – ACE70810000 (הרקתב)	**17**	2 המוקל + 1 עקרקב
SW	D-Link DES-1210-28P – תואיצי PoE 24 גתמ	**9**	1 לכל המוק + עקרק
GAB	ארון ריק 12U םע פאנל 'ץאפ (גתמל)	**8**	1 לכל המוק
GAB-PB	UPS ארון ישאר םע דמוע	**1**	עקרק
SRV	שרת Buslogic Premium (Advantcare) םע הנכות	**1**	עקרק
TEL	טלפון Grandstream דיאורדנא (PoE, עבצ יפל גוס האירק)	**1**	תוחא תדמע
כבלים (+ 15% הברזר)			
—	Cat6 רדיאלי בתוך הדירות (קורי)	**1700 m**	183 מ' המוקל
—	Cat6 / Cat7 שרשרת LCom ← BoxCom (מותכ)	**750 m**	80 מ' המוקל
—	Cat6A / Cat7 ארונות ועמוד (אודם)	**130 m**	דומע ללוכ

NOTES · תורעה

1. כמויות מחושבות מהמודל (המוק תיסופיט × 8 + עקרק).
2. אורכי כבל נמדדו על התוואי המשורטט, + 15%.
3. מחירים: לפי מחירון Advantecnia ינכדעה.
4. לאמת באתר לפני רכישה.

מגדלי ים התיכון · דיור מוגן

קריאת אחות – קרקע + 8 קומות · 32 דירות

Telab International :ץוע ןוכי"ע   ACE BG · Advantecnia :תכרעמ

רשימת חומרים

Bill of materials

SCALE · קנה מידה	DATE · תאריך	REV	גיליון
S/E	**15/10/2026**	**B**	**09**

בסיס: תכנית אדריכלית L5 (דסמ זוע / Triplet) · מידות במטרים

פורמט A1 · מהדורה B – על התכנית האמיתית

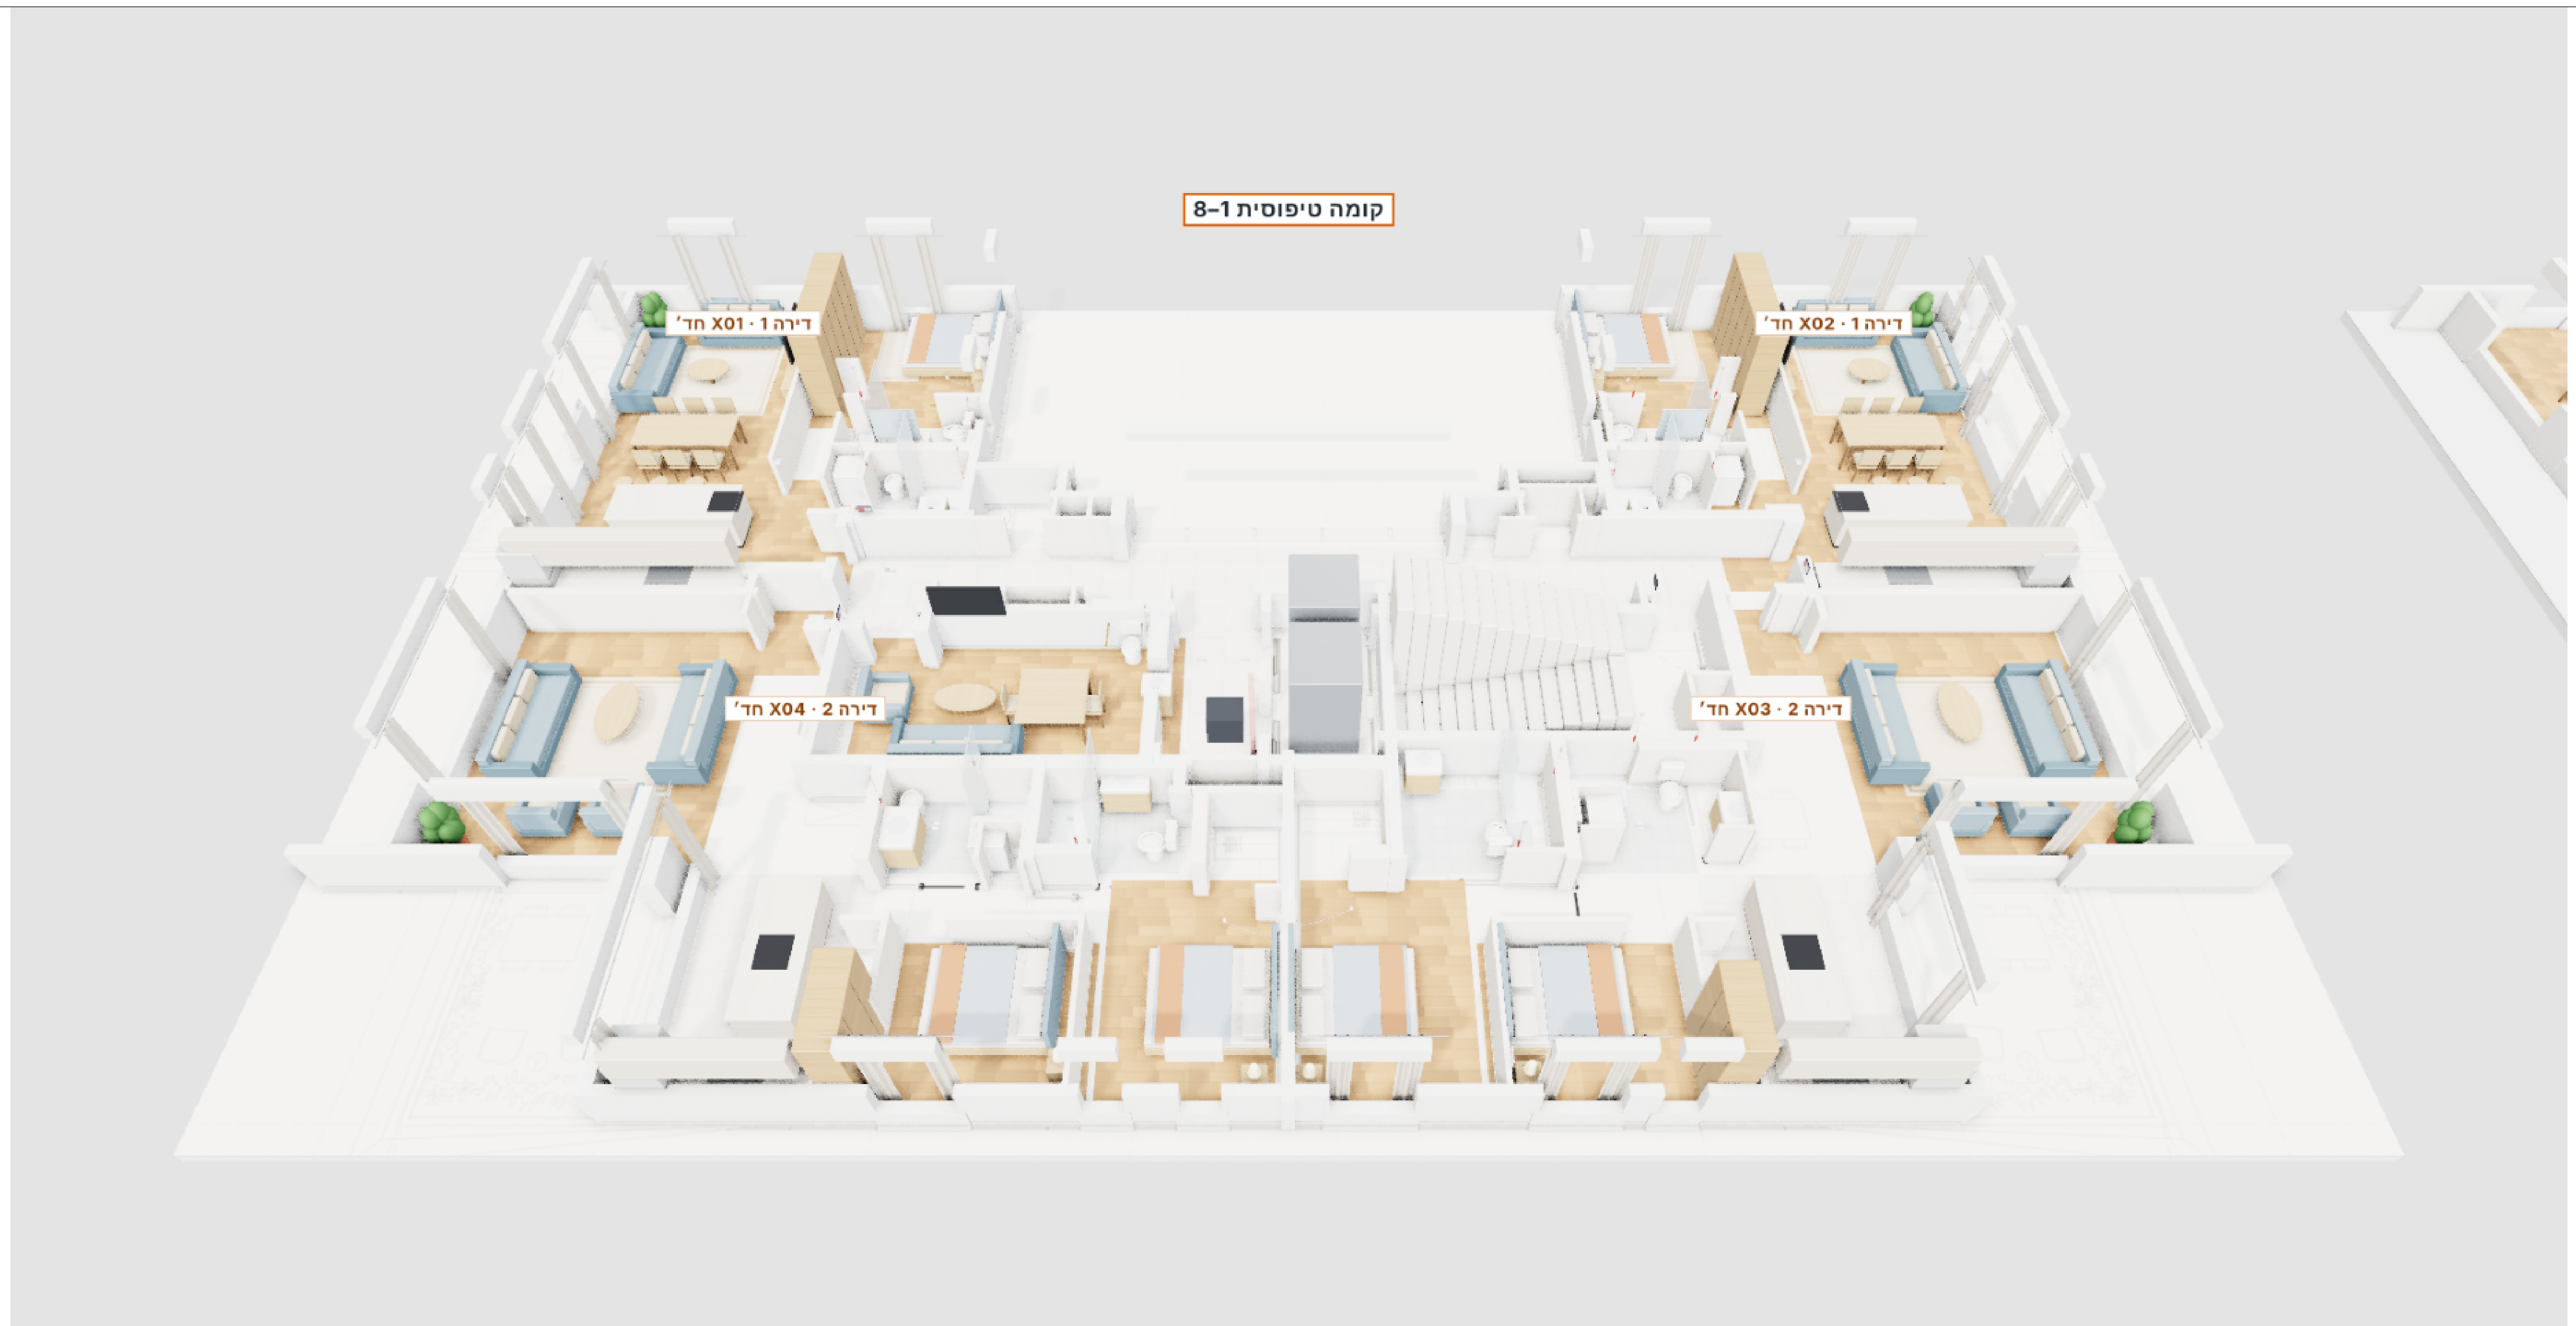
קומה טיפוסית 1–8
דירה 1 · X01 חד'
דירה 1 · X02 חד'
דירה 2 · X04 חד'
דירה 2 · X03 חד'

א · קומה טיפוסית – 4 דירות

ב · טאבלט בכניסה

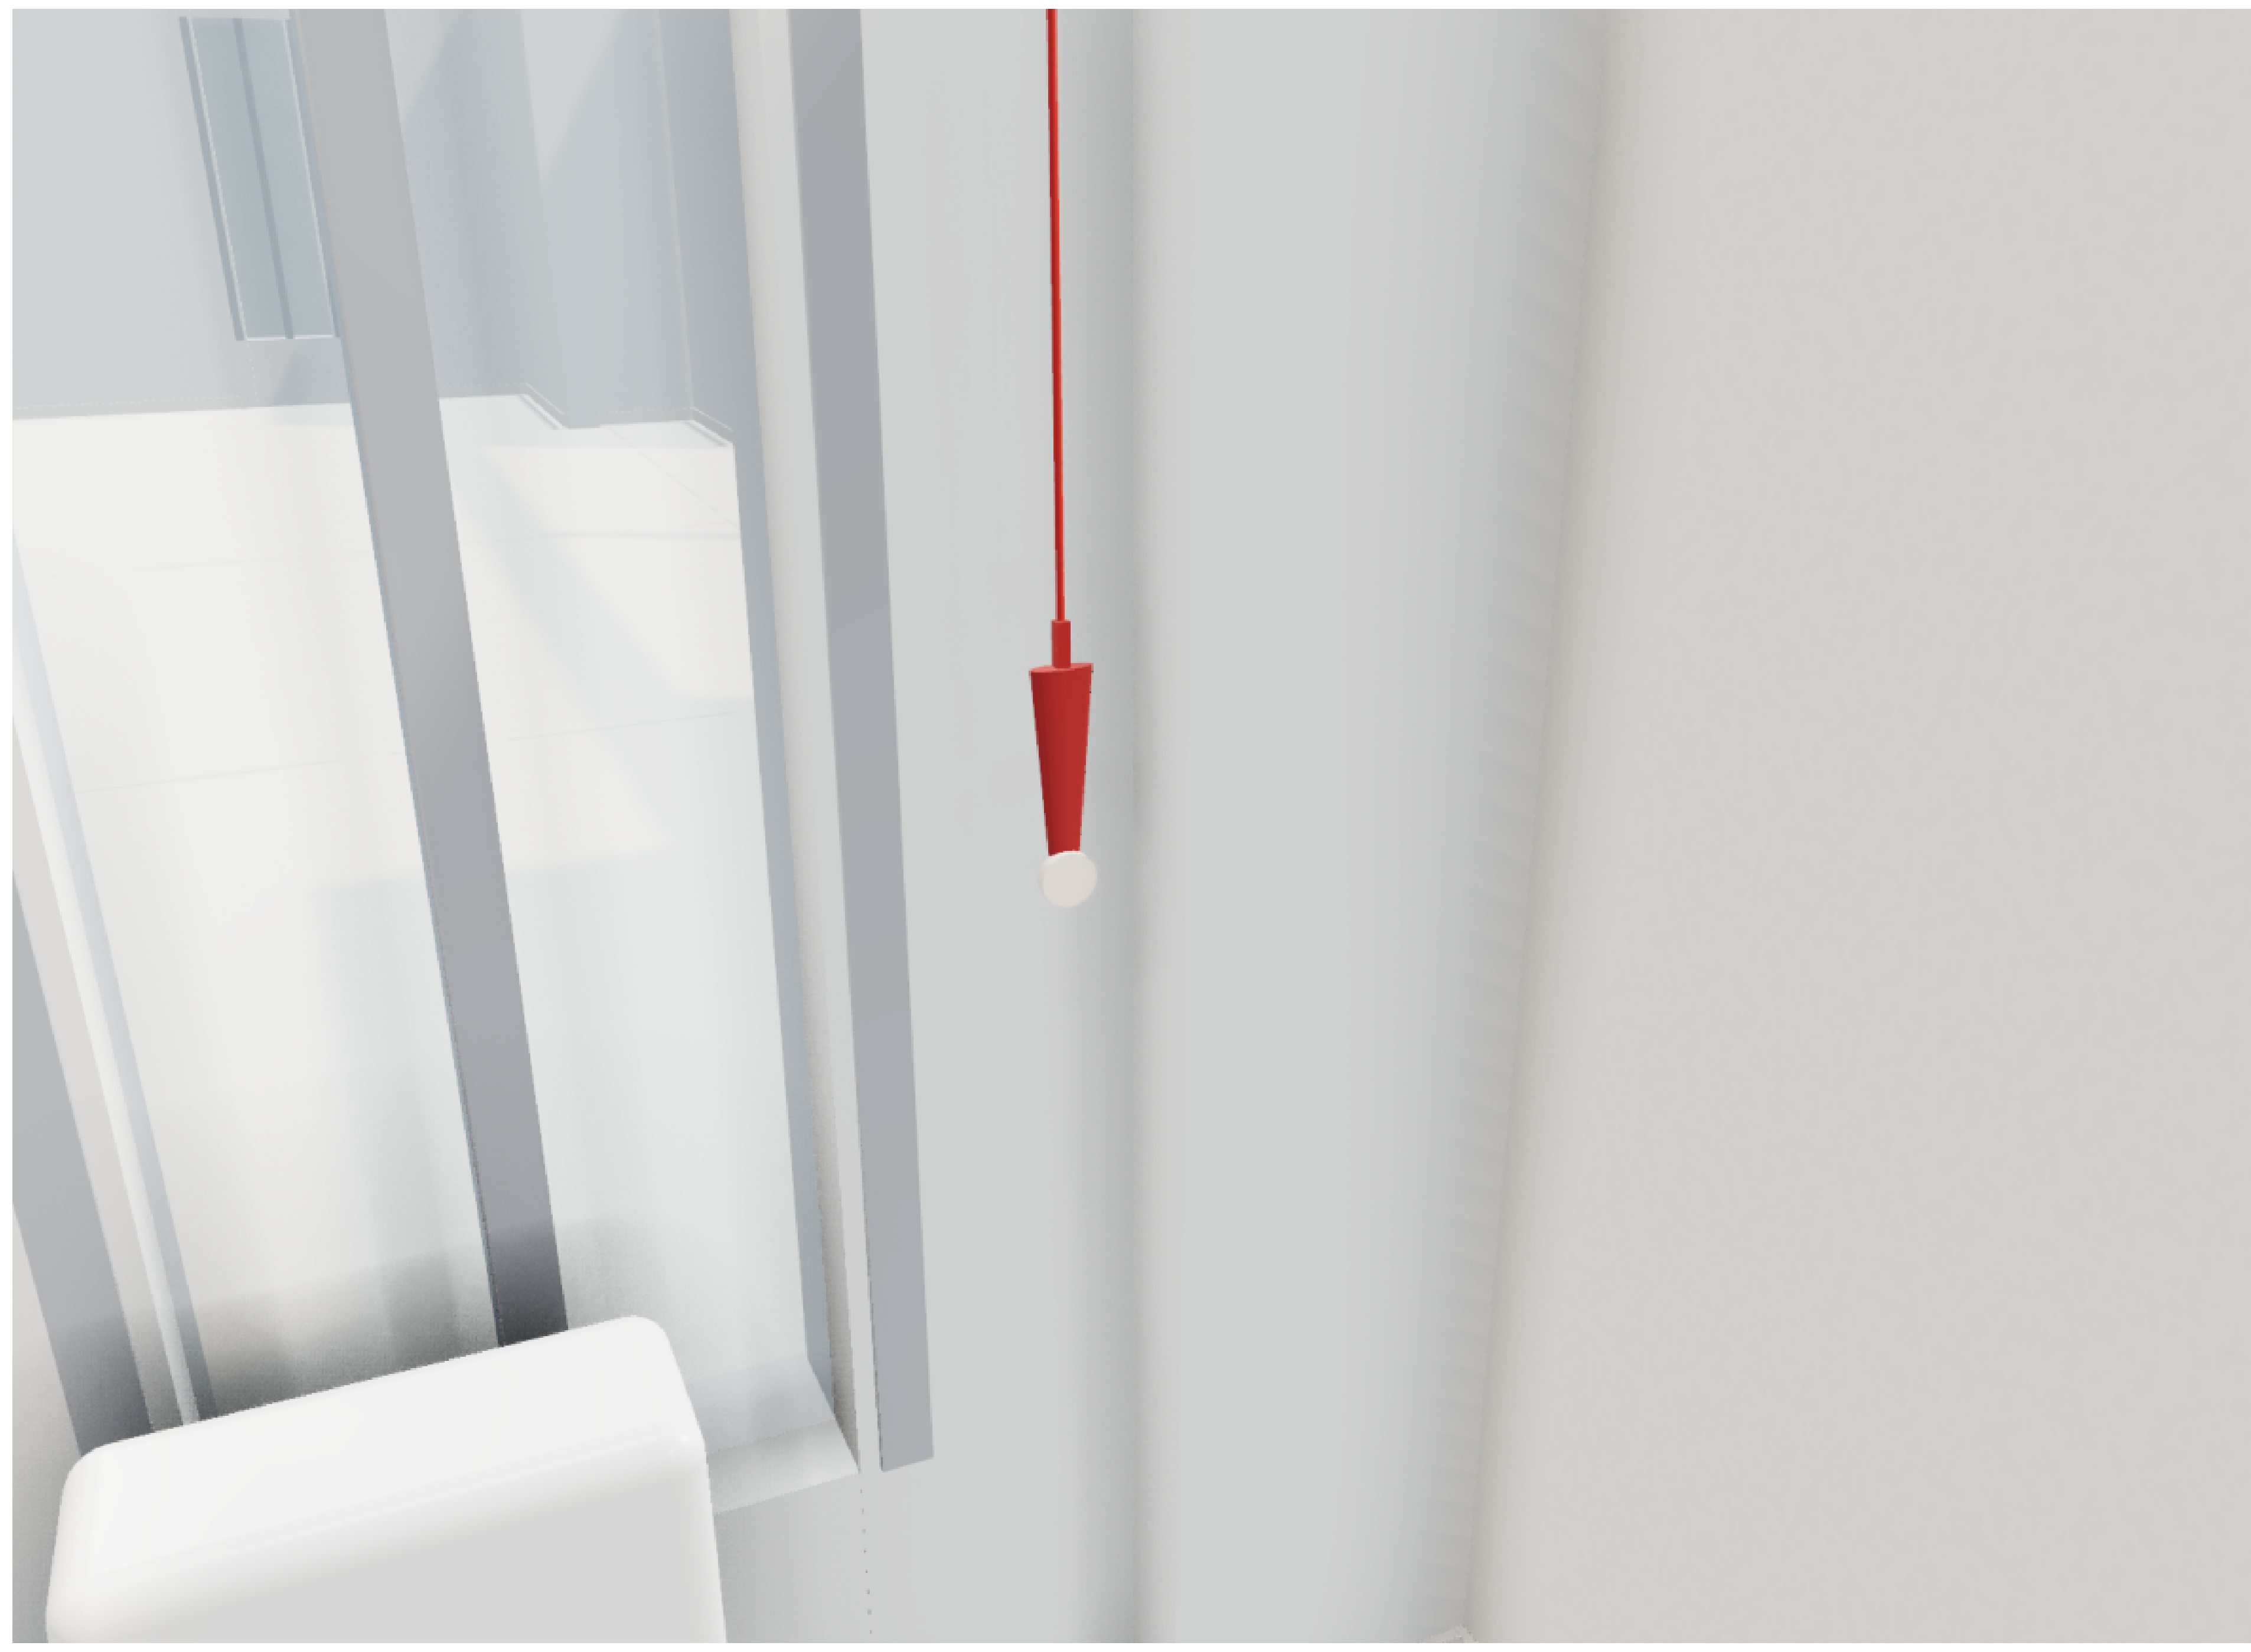

ד · חדר רחצה – משיכות חבל באסלה ובמקלחת

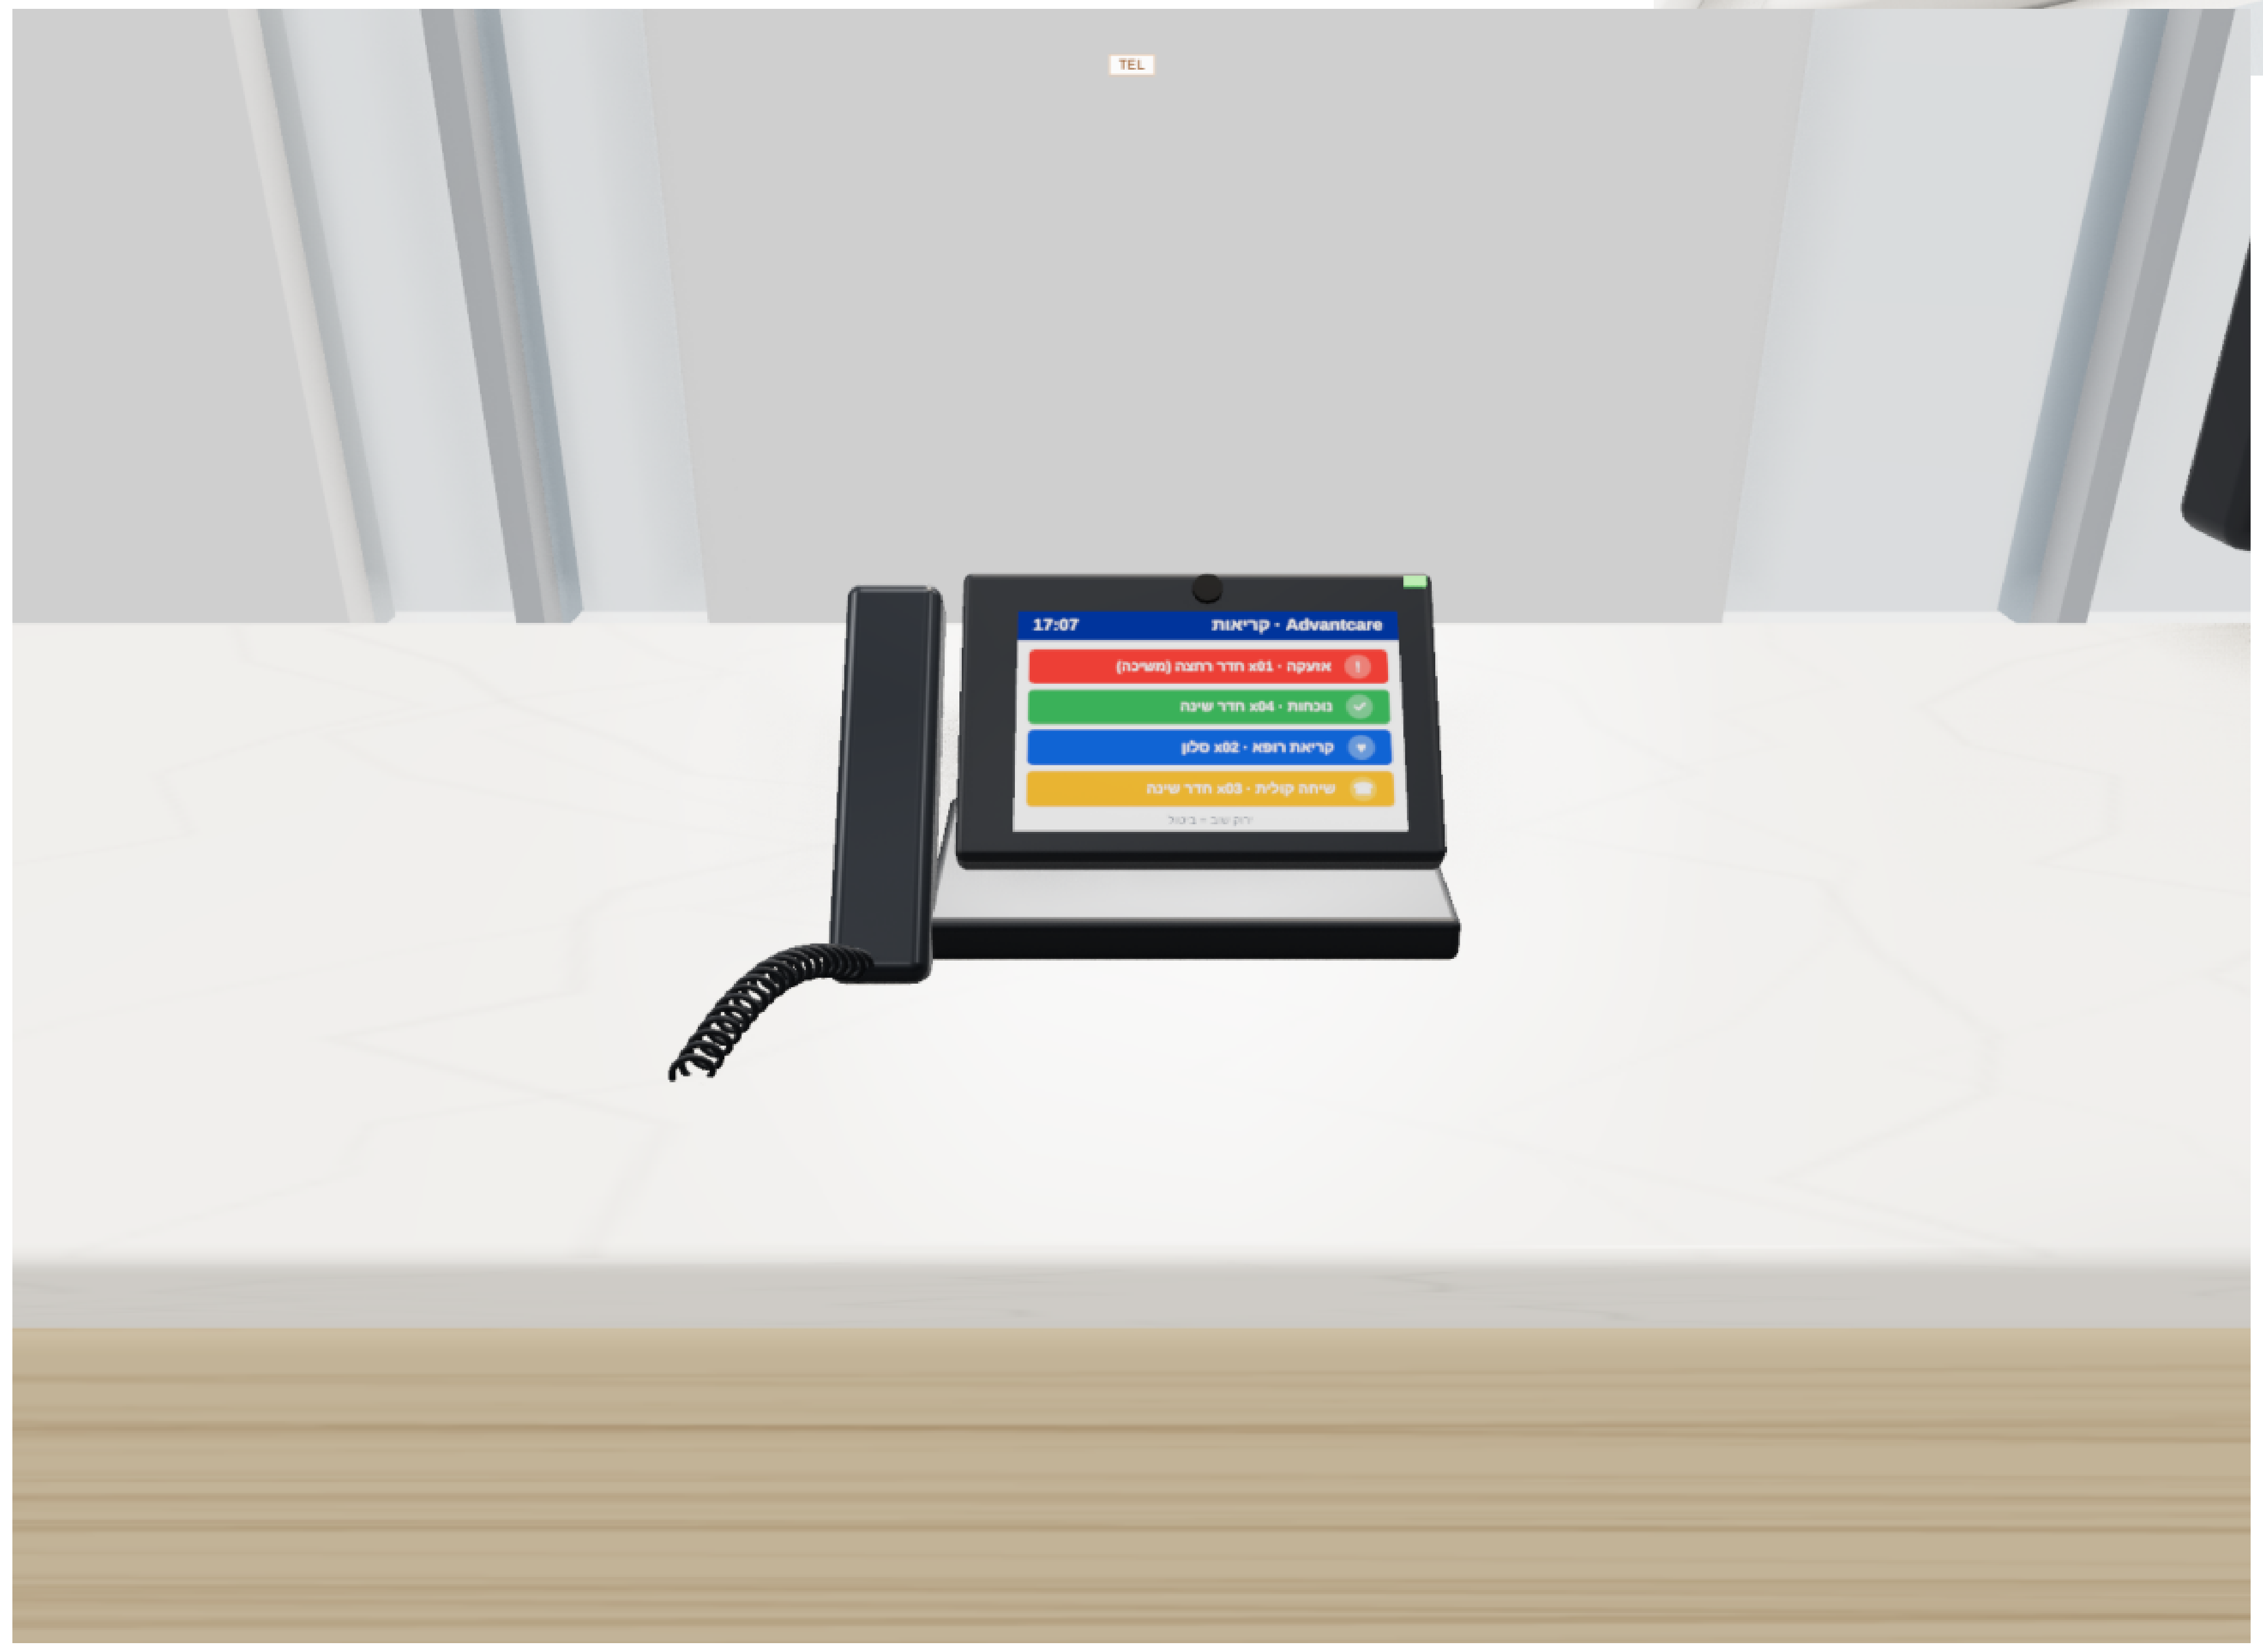

Advantcare · קריאות 17:07

- אתנקה · x01 חדר רחצה (משיכה)
- נוכחות · x04 חדר שינה
- קריאת רופא · x02 סלון
- שיחה קולית · x03 חדר שינה

ה · קרקע – עמדת אחות

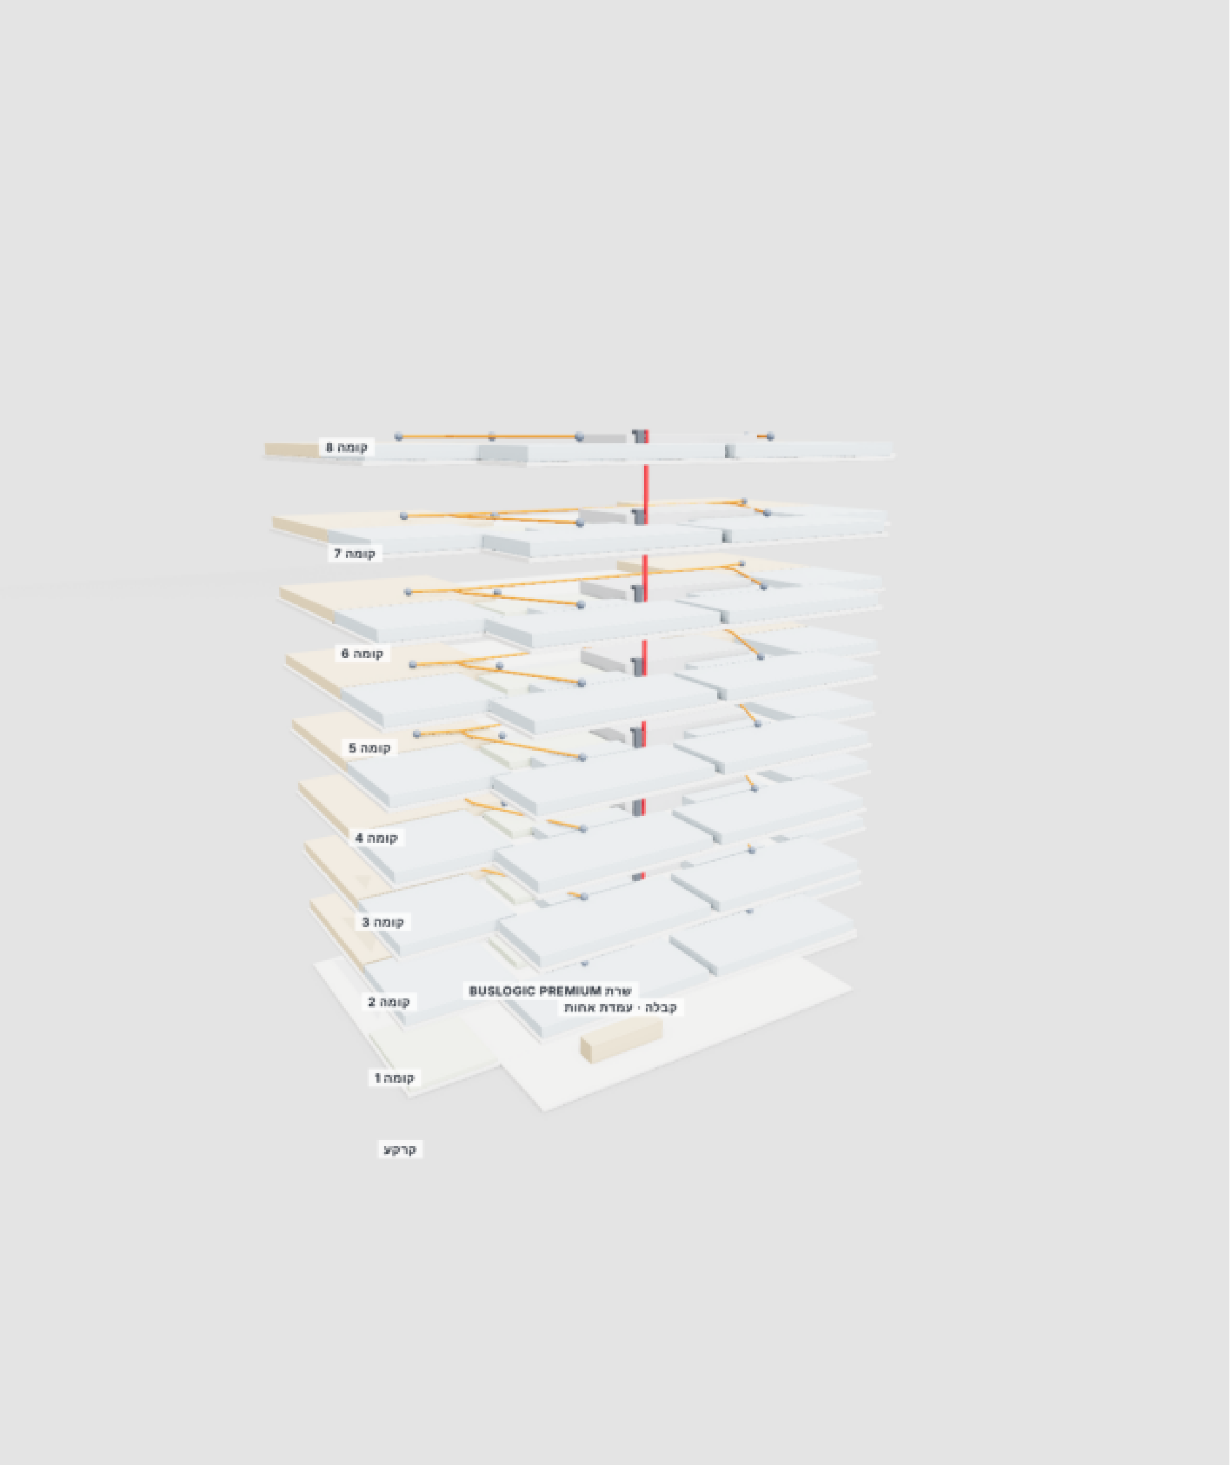
קומה 8
קומה 7
קומה 6
קומה 5
קומה 4
קומה 3
קומה 2
קומה 1
קרקע
שרת BUSLOGIC PREMIUM
קבלה · עמדת אחות

ו · בניין קרקע + 8 קומות

מגדלי הים התיכון · דיור מוגן

32 דירות · 8 קומות + קרקע – קריאת אחות

מערכת: ACE BG · Advantecnia   הוכן ע"י: Telab International

מבטים תלת-ממדיים

3D views

SCALE · קנה מידה	DATE · תאריך	REV	גיליון
S/E	**15/10/2026**	**B**	**10**

בסיס: תוכנית האדריכל L5 (מסד עוז / Triplet) · מידות במטרים

פורמט A1 · מהדורה B – על התוכנית האמיתית

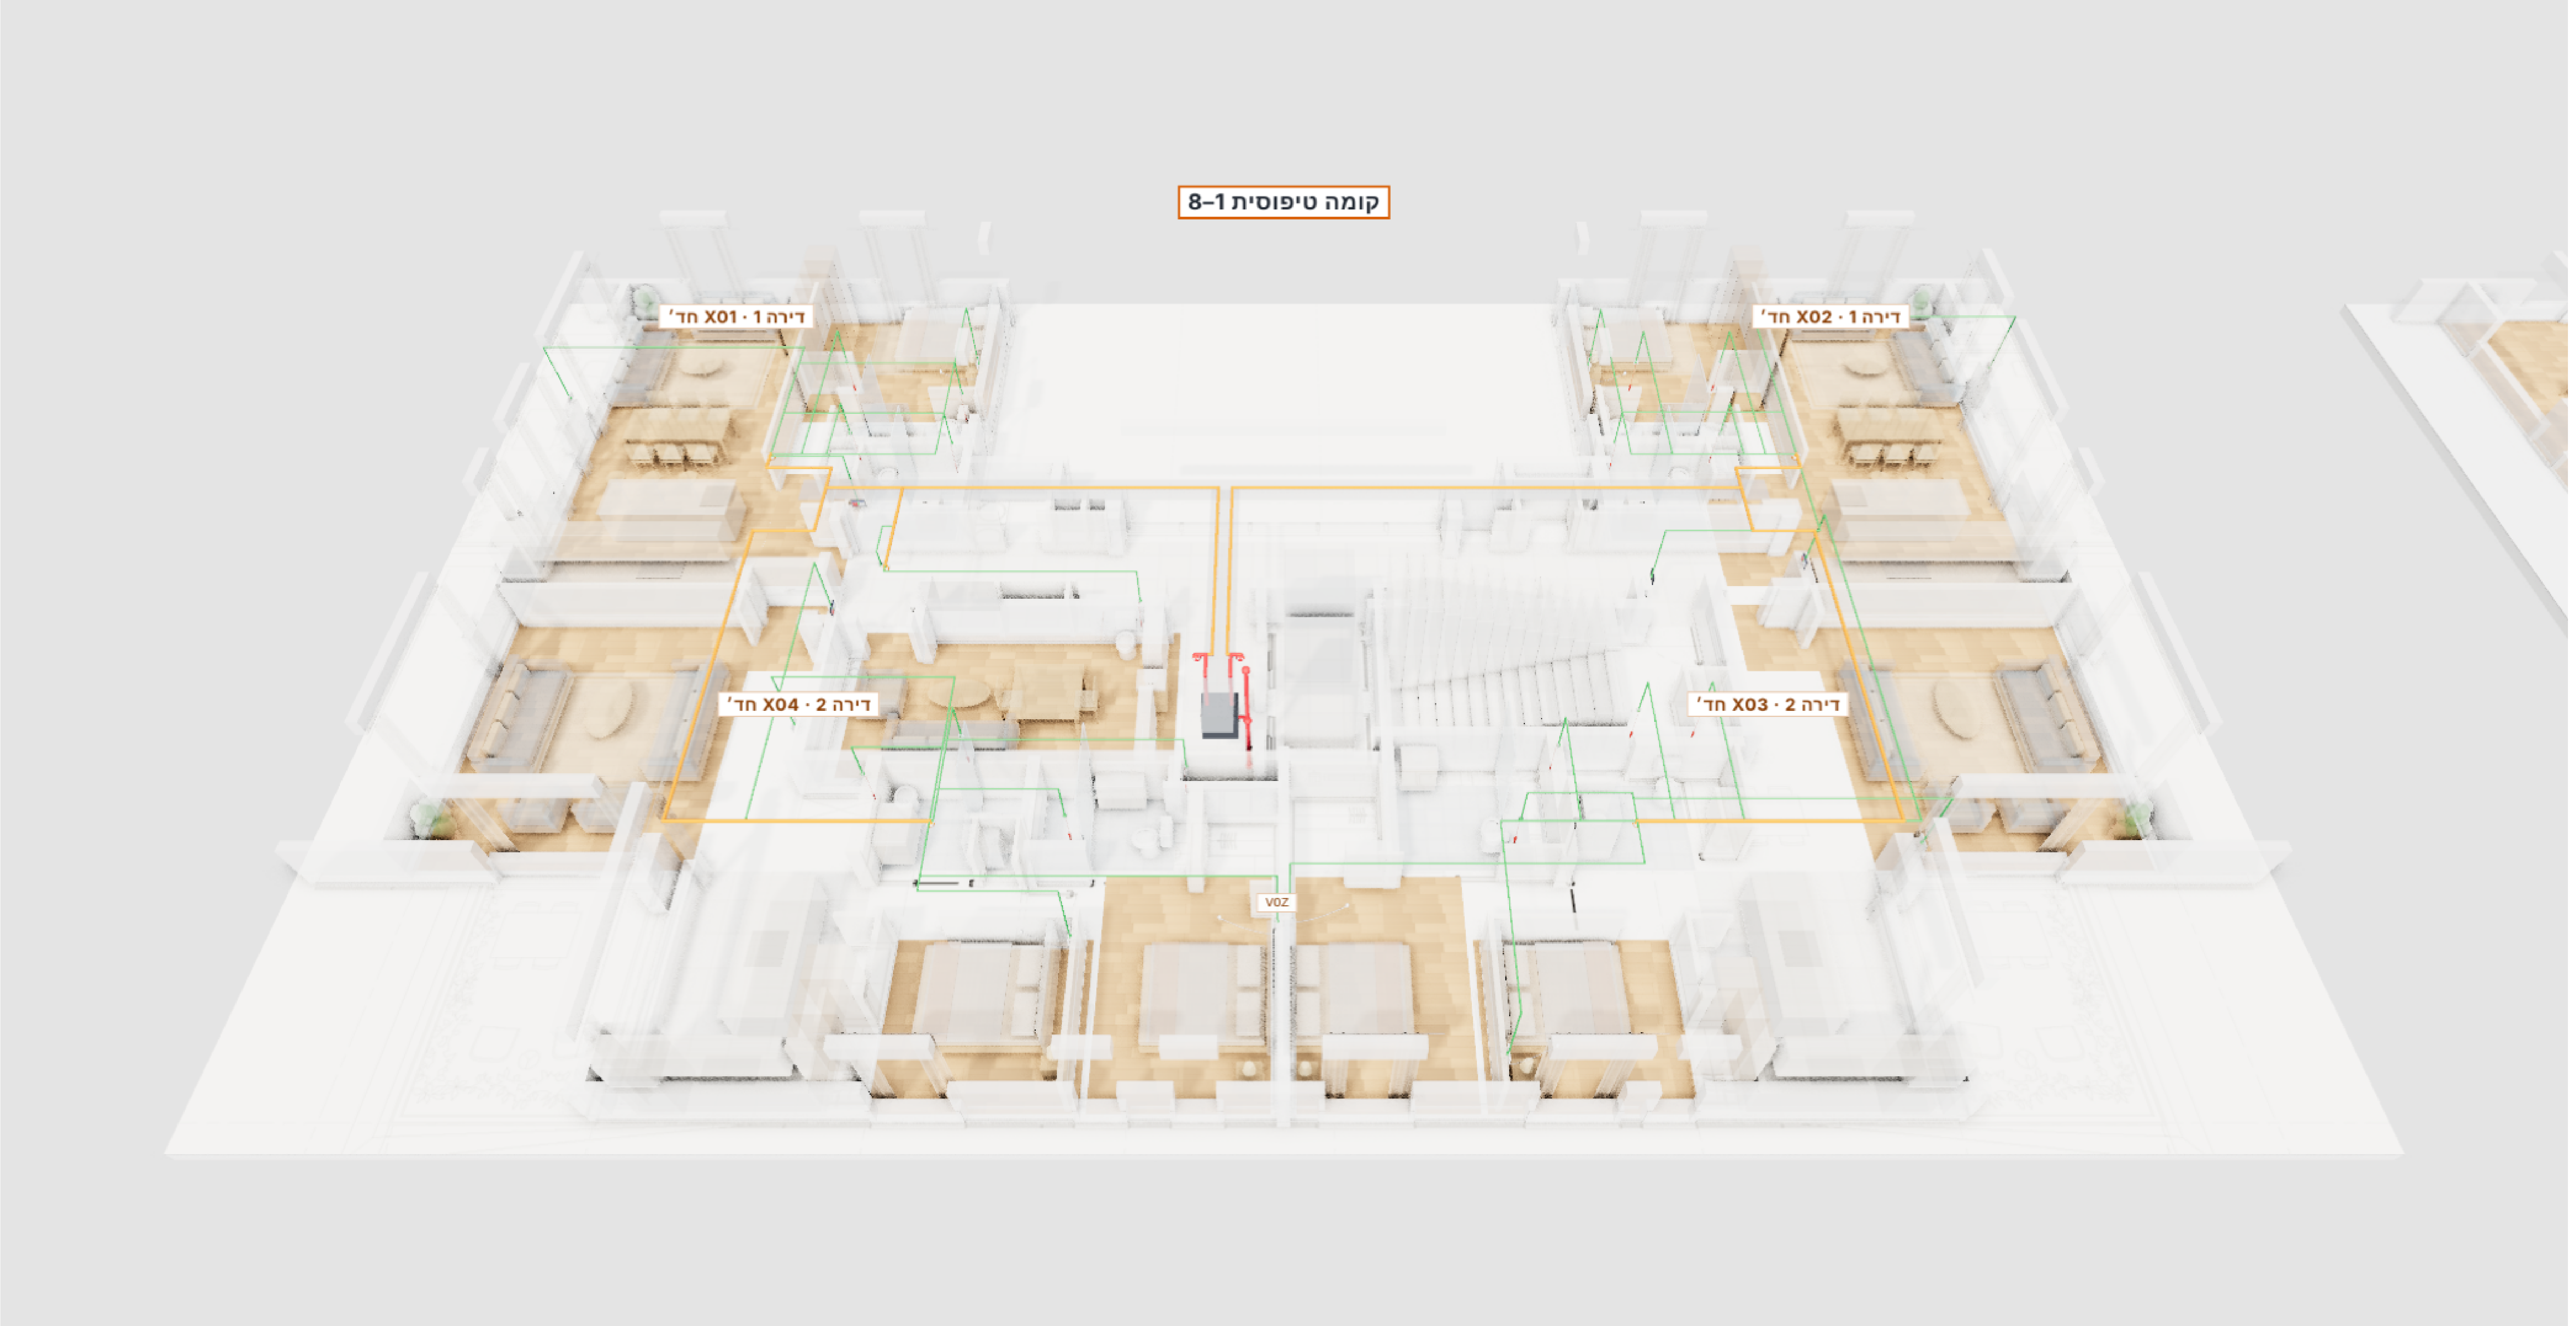

(תשר םודא · LCom תרשרש םותכ · ילאידר קורי) טוויח – תיסופיט המוק · א

הלבקו יבול – עקרק תמוק · ב

םינצחל םע ילוק לנפ – ןולס · ג

COLOURS · COLORES · םיעבצ

🟩 Cat6 ילאידר: לכ ןקתה ← LCom הרידה לש
Cat6 radial: each device → apartment LCom · Cat6 ילאידר: לכ ןקתה ← LCom הרידה לש

🟧 Cat6 / Cat7 תרשרש: LCom ← LCom ← BoxCom הרקתב
Cat6 / Cat7 chain: LCom → LCom → BoxCom · Cat6 / Cat7 תרשרש: LCom ← LCom ← BoxCom

🟥 Cat6A / Cat7 תשר: BoxCom ← גתמ PoE ← דומע ← תרש עקרק
Cat6A / Cat7 network: BoxCom → switch → riser → GF server · Cat6A / Cat7 תשר: BoxCom ← גתמ ← דומע ← תרש

ןגומ רויד · ןוכיתה םי ילדגמ
קריאת אחות – קרקע + 8 תומוק · 32 תוריד
Telab International :ןכוה ע"י   ACE BG · Advantecnia :תכרעמ

טוויח – םיידממ-תלת םיטבמ

3D views – wiring

SCALE · הדימ הנק	DATE · ךיראת	REV	ןוילג
S/E	15/10/2026	B	11

בסיס: תונכות הארדיכל L5 (זוג דסמ / Triplet) · םירטמב תודימ
טמרופ A1 · הרודהמ B – לע התוכנות תיתימאה