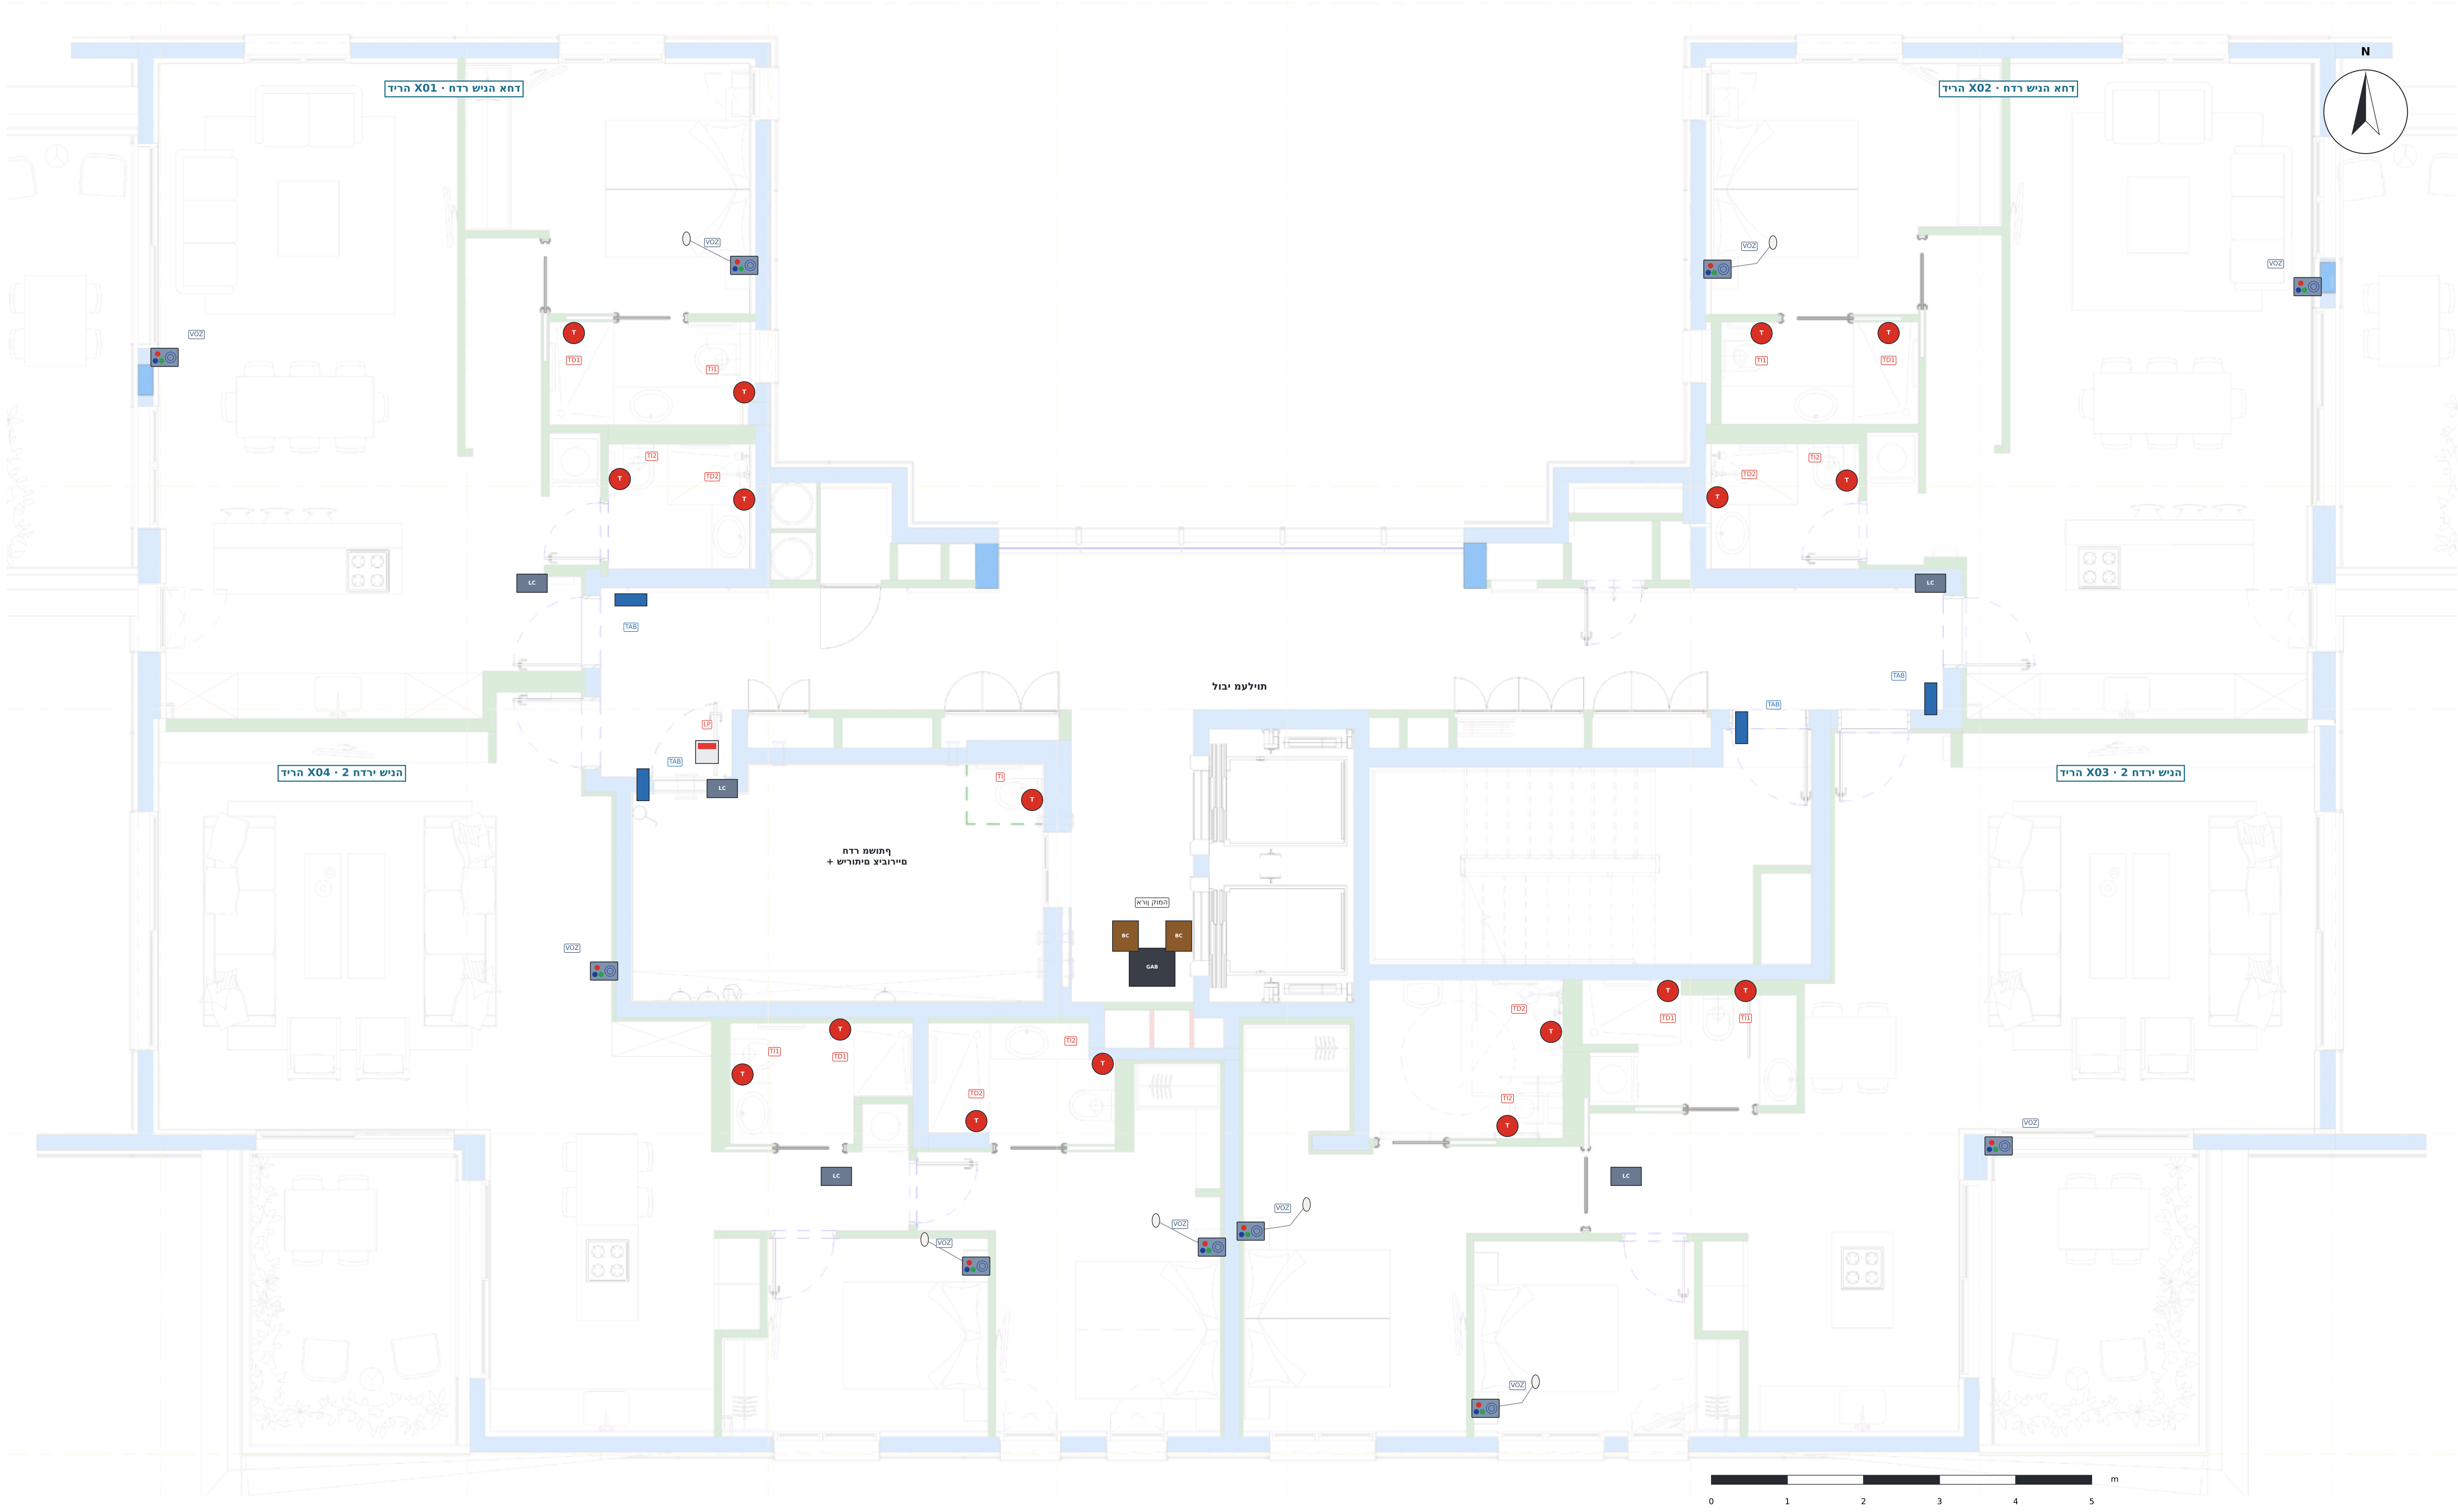
דירה X01 · חדר שינה אחד
דירה X02 · חדר שינה אחד
דירה X04 · 2 חדרי שינה
דירה X03 · 2 חדרי שינה
לובי מעליות
חדר משותף
+ שירותים ציבוריים
ארון קומה
N
VOZ
TAB
LC
LP
BC
GAB
T
TI
TI1
TI2
TD1
TD2
0
1
2
3
4
5
m

DEVICES · EQUIPOS · דויץ

▬	TAB · טאבלט בכניסה (iPad / אנדרואיד) – קריאה ודיבור, גובה 1.40 מ' Door tablet – call and voice · טאבלט בכניסה – קריאה ודיבור
VOZ	VOZ · פנל קולי עם לחצנים ACE82182451 – סלון וחדרי שינה, גובה 1.20–1.30 מ' Voice panel with buttons – living room and bedrooms · פנל קולי עם לחצנים – סלון וחדרי שינה
○	אגס קריאה ליד המיטה (בחדרי השינה) Call pear next to the bed (bedrooms) · אגס קריאה ליד המיטה
T	TI / TD · משיכת חבל ACE40320303W – אסלה ומקלחת, גובה 1.85 מ' Pull-cord – toilet and shower, h 1.85 m · משיכת חבל – אסלה ומקלחת, גובה 1.85 מ'
🟥	LP · מנורת מסדרון ACE41020309 – מעל דלת כל שירותים ציבוריים Corridor light – above each public toilet door · מנורת מסדרון – מעל דלת כל שירותים ציבוריים
LC	LC · LCom ACE71610003 – מרכז הדירה (תקרה) LCom – apartment hub (ceiling) · LCom – מרכז הדירה (תקרה)
BC	BC · BoxCom ACE70810000 – מרכז באס לכמה דירות (תקרה) BoxCom – bus hub for several apartments (ceiling) · BoxCom – מרכז באס לכמה דירות (תקרה)
GAB	ארון קומה 12U: מתג PoE D-Link DES-1210-28P (24 יציאות PoE) Floor rack: D-Link DES-1210-28P PoE switch · ארון קומה: מתג PoE D-Link DES-1210-28P

כמויות לקומה × 8 קומות

קוד	התקן	לקומה	8 קומות
TAB	טאבלט בכניסה	4	32
VOZ	פנל קולי עם לחצנים	10	80
TI/TD	משיכת חבל (אסלה + מקלחת)	17	136
LP	מנורת מסדרון (שירותים ציבוריים)	1	8
LC	LCom	5	40
BC	BoxCom	2	16
SW	מתג PoE	1	8

NOTES · הערות

1. בסיס: תוכניות אדריכליות L5 (קומה טיפוסית) – 8 קומות זהות: 4 דירות בקומה, 32 בסך הכול.
2. דירות x01 ו-x02: חדר שינה אחד, סלון עם מטבח ו-2 חדרי רחצה. דירות x03 ו-x04: 2 חדרי שינה ו-2 חדרי רחצה.
3. טאבלט בכניסה לכל דירה (iPad / אנדרואיד) לקריאה ודיבור עם האחות.
4. פנל קולי עם לחצנים (ACE82182451) בסלון ובכל חדר שינה; בחדר השינה עם אגס ליד המיטה.
5. משיכות חבל (ACE40320303W) באסלה ובמקלחת בכל חדרי הרחצה, בגובה 1.85 מ'.
6. שירותים ציבוריים בכל קומה בחדר המשותף: משיכת חבל + מנורת מסדרון מעל הדלת. עם 2 בקרקע – 10 שירותים ציבוריים.
7. ארון קומה ליד המעליות עם מתג PoE D-Link DES-1210-28P; 2 ה-BoxCom בתקרה לידו.
8. מיקומים לפי סימוני הלקוח בתוכניות L2 (nt = פנל קולי, tab = טאבלט): ראו גיליון 03.

גובהי התקנה

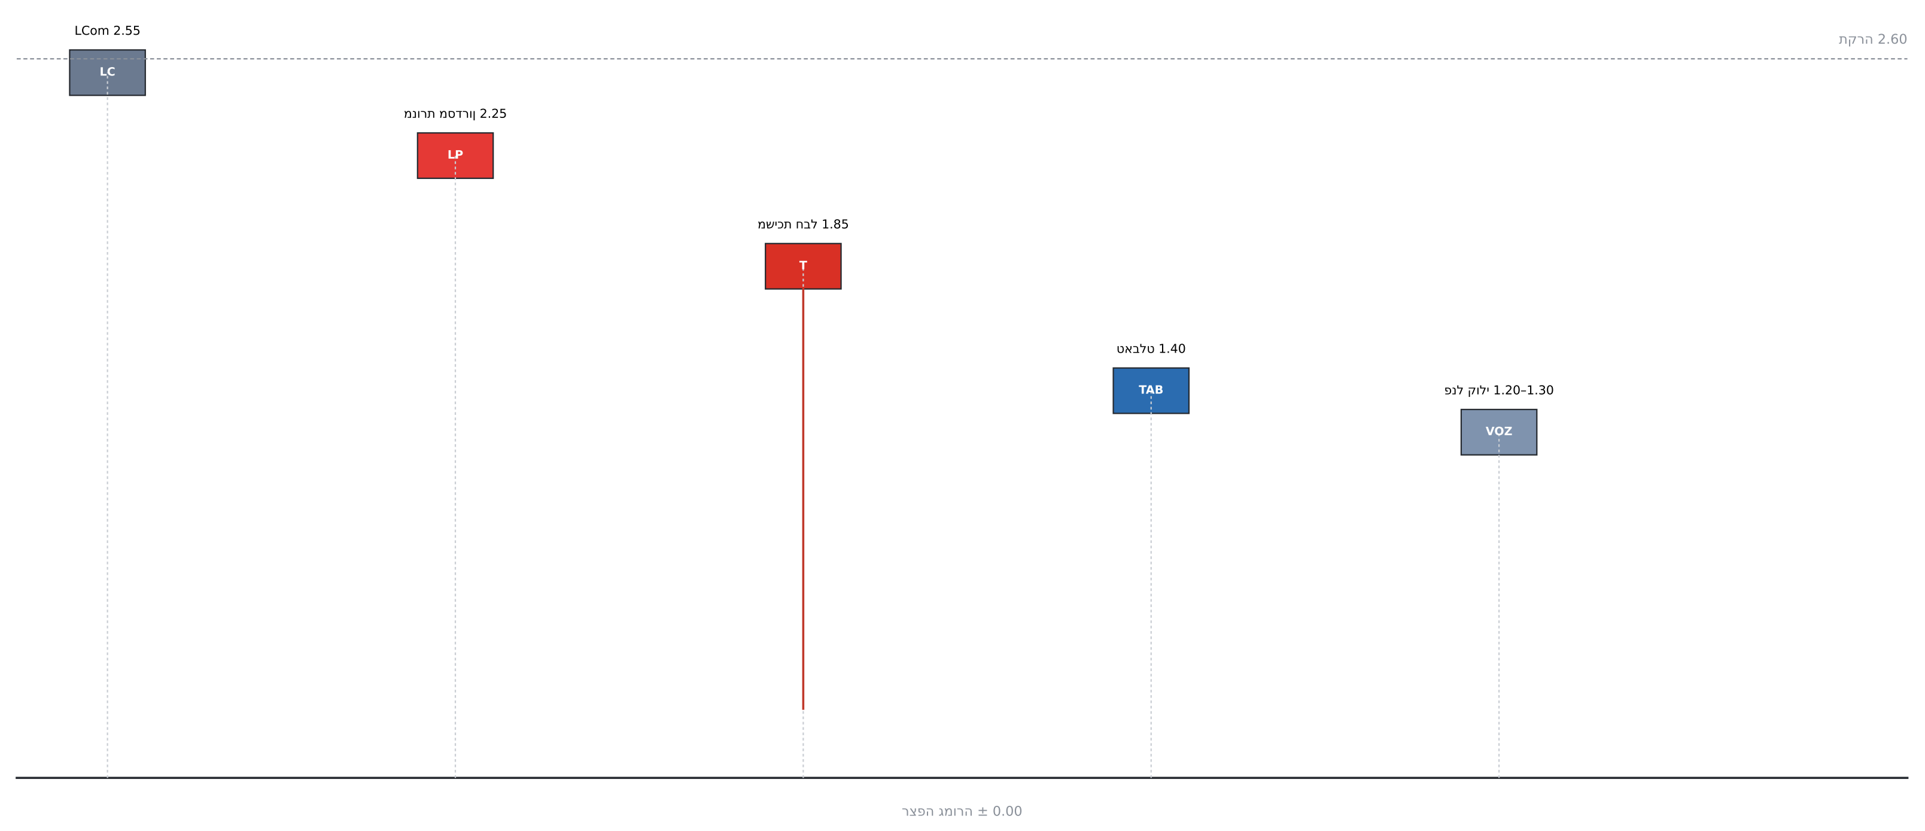
LCom 2.55
LC
מנורת מסדרון 2.25
LP
משיכת חבל 1.85
T
טאבלט 1.40
TAB
פנל קולי 1.20–1.30
VOZ
תקרה 2.60
רצפה גמורה ± 0.00

פנל קריאת אחות

פנל קולי עם לחצנים

מנורה קריאת אחות

מנורת מסדרון

טבלט אנדרואיד קריאת אחות
Advantecnia
Llamada de enfermera

טאבלט בכניסה (iPad / אנדרואיד)

שירותים קריאת אחות

משיכת חבל

מגדלי הים התיכון · דיור מוגן

32 דירות · 8 קומות + קרקע – קריאת אחות

Telab International :הוכן ע"י   ACE BG · Advantecnia :מערכת

קריאת אחות · 1–8 קומה טיפוסית

Typical floor F1–F8 · nurse call

SCALE · קנה מידה	DATE · תאריך	REV	גיליון
1:60	15/10/2026	B	01

בסיס: תוכניות אדריכל L5 (מסד זוג / Triplet) · מידות במטרים

פורמט A1 · מהדורה B – על התוכנית האמיתית

שירותים קריאת אחות

לבח תכישמ

דוק	**ACE40320303W**
םוקימ	םיירוביצה םיתורישה 10-בו הצחר רדח לכב תחלקמו הלסא
הבוג	**1.85 'מ**
תומכ	**138**

1

טבלט אנדרואיד קריאת אחות

TV
Advantecnia
Llamada de enfermera
Hospital
Salud y bienestar

הסינכב טלבאט (iPad / דיאורדנא)

דוק	**Advantecnia TV**
םוקימ	הריד לכ תלד דיל ,יבולב
הבוג	**1.40 'מ**
תומכ	**32**

2

מנורה קריאת אחות

ןורדסמ תרונמ

דוק	**ACE41020309**
םוקימ	םיירוביצ םיתוריש לכ תלד לעמ
הבוג	**2.25 'מ**
תומכ	**10**

3

פנל קריאת אחות

םינצחל םע ילוק לנפ

דוק	**ACE82182451**
םוקימ	ןולס וכל רדח הניש (רדחב הנישה םע אגס)
הבוג	**1.20–1.30 'מ**
תומכ	**80**

4

GRANDSTREAM
HD

ןופלט הדמעה (דיאורדנא)

דוק	**Grandstream**
םוקימ	עמדת תוחא בקרקע · PoE גתמל תורישי
הבוג	**הדמעה לע**
תומכ	**1**

5

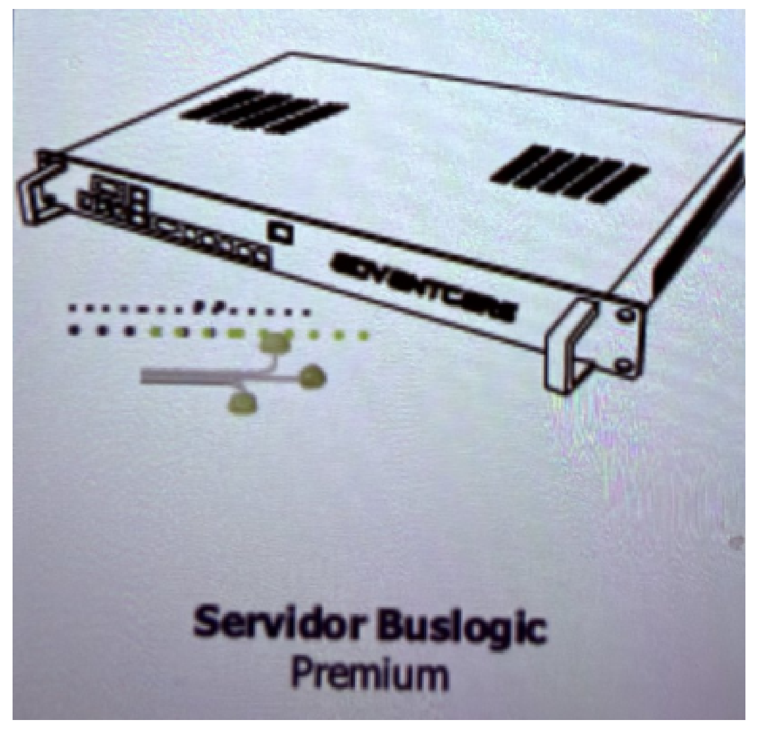

Buslogic Premium תרש

דוק	**Advantcare**
םוקימ	עקרקב ישאר ןורא
הבוג	**ןוראב**
תומכ	**1**

6

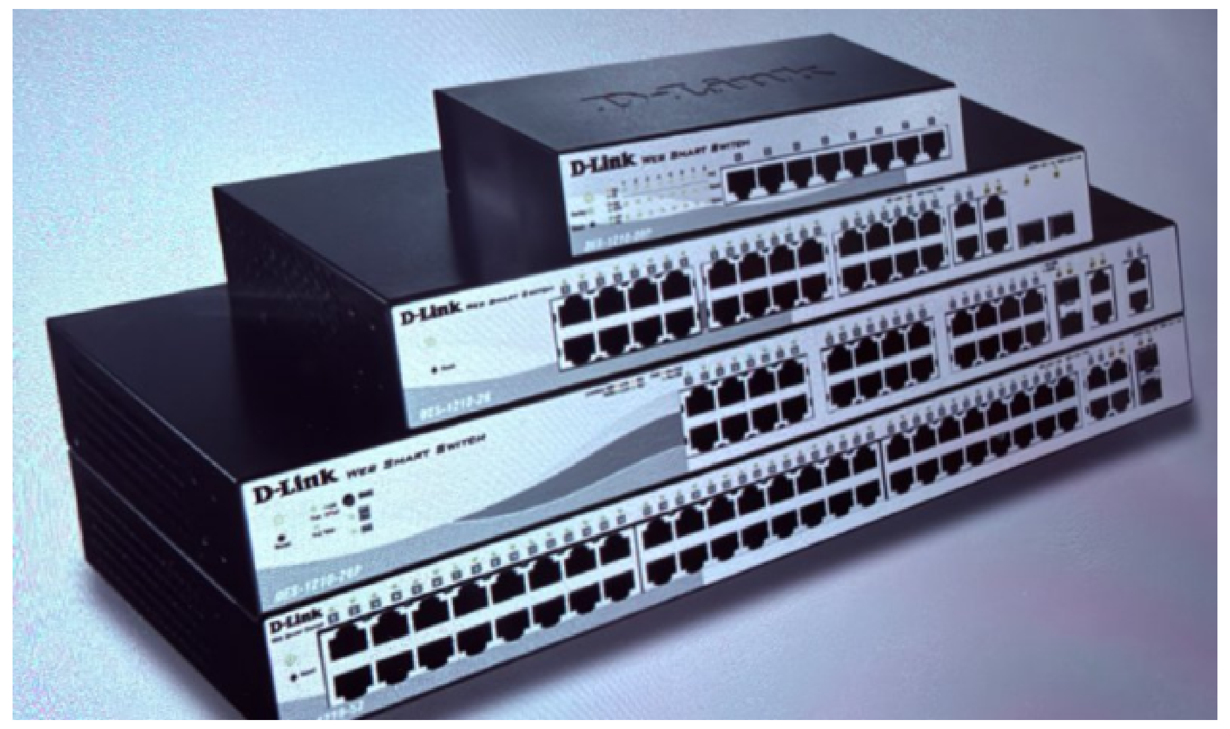

תואיצי 24 םע PoE גתמ

דוק	**D-Link DES-1210-28P**
םוקימ	עקרקבו המוק לכב ןורא
הבוג	**ןוראב**
תומכ	**9**

7

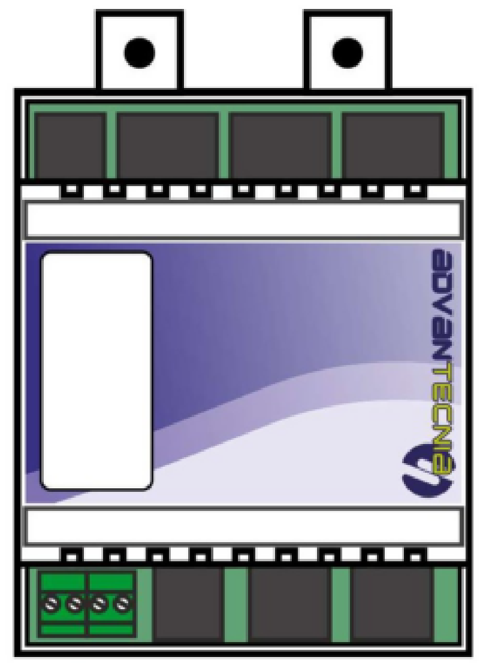

LCom – ילאידר זכרמ

דוק	**ACE71610003**
םוקימ	םיירוביצה םיתורישהו הריד לכ תרקת
הבוג	**2,55 m**
תומכ	**41**

8

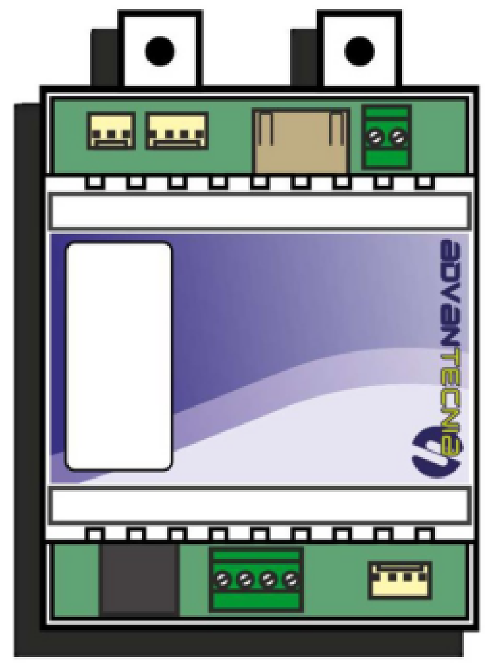

BoxCom – זכרמ סאב

דוק	**ACE70810000**
םוקימ	תוריד המכ רבחמ :ןוראה דיל הרקת
הבוג	**2,55 m**
תומכ	**17**

9

NOTES · תורעה

/ ACE BG 1. לש סוחיי תונומת
Advantecnia, םע תרתוכה ןהלש.

2. לבח תכישמ: לבח אדוום םע ידית,
נגיש םג המצרהה.

3. רבדמו ארוק הסינכב טלבאטה
םע האחות.

4. םיארוקשכ תקלדנ ןורדסמה תרונמ
םיירוביצה םיתורישהמ.

5. םודא האירק ןצחל לנפב,
ןצחל לוחכ (לאמש) קוריו (ןימי)
רובידל לוקמרו.

6. תרשרש: םינקתה ← LCom (ילאידר) ←
BoxCom (סאב) ← גתמ PoE ← תרש.

7. ןופלט הדמעה רבוחמ תורישי
.PoE-ה גתמל

ןופלט הדמעה – הזיא עבצ גצומ

🟥	(SOS / הכישמ) הקעזא	םודא
🟩	ןצחל ירוק םעפ תחא: תוחכונ	קורי
⬜	ןצחל ירוק בוש: לטבמ האירק וא הקעזא	םנחק
🟦	(blue call) ןצחל לוחכ: תאירק רופא	לוחכ
🟧	שיחה קולית	םותכ / בוהצ

ןגומ רויד · ןוכיתה םי ילדגמ

תוריד 32 · תומוק 8 + עקרק – תוחא תאירק

Telab International :הכון ע"י   ACE BG · Advantecnia :תכרעמ

תכרעמה דויצ

System devices

SCALE · הנק הדימ	DATE · ךיראת	REV	ןוילג
S/E	15/10/2026	B	02

סיסב: תוניכת האדרילכ L5 (םסד עוז / Triplet) · םידות במטריםמ

טמרופ A1 · הרודהמ B – לע תוניכתה תיתימאה

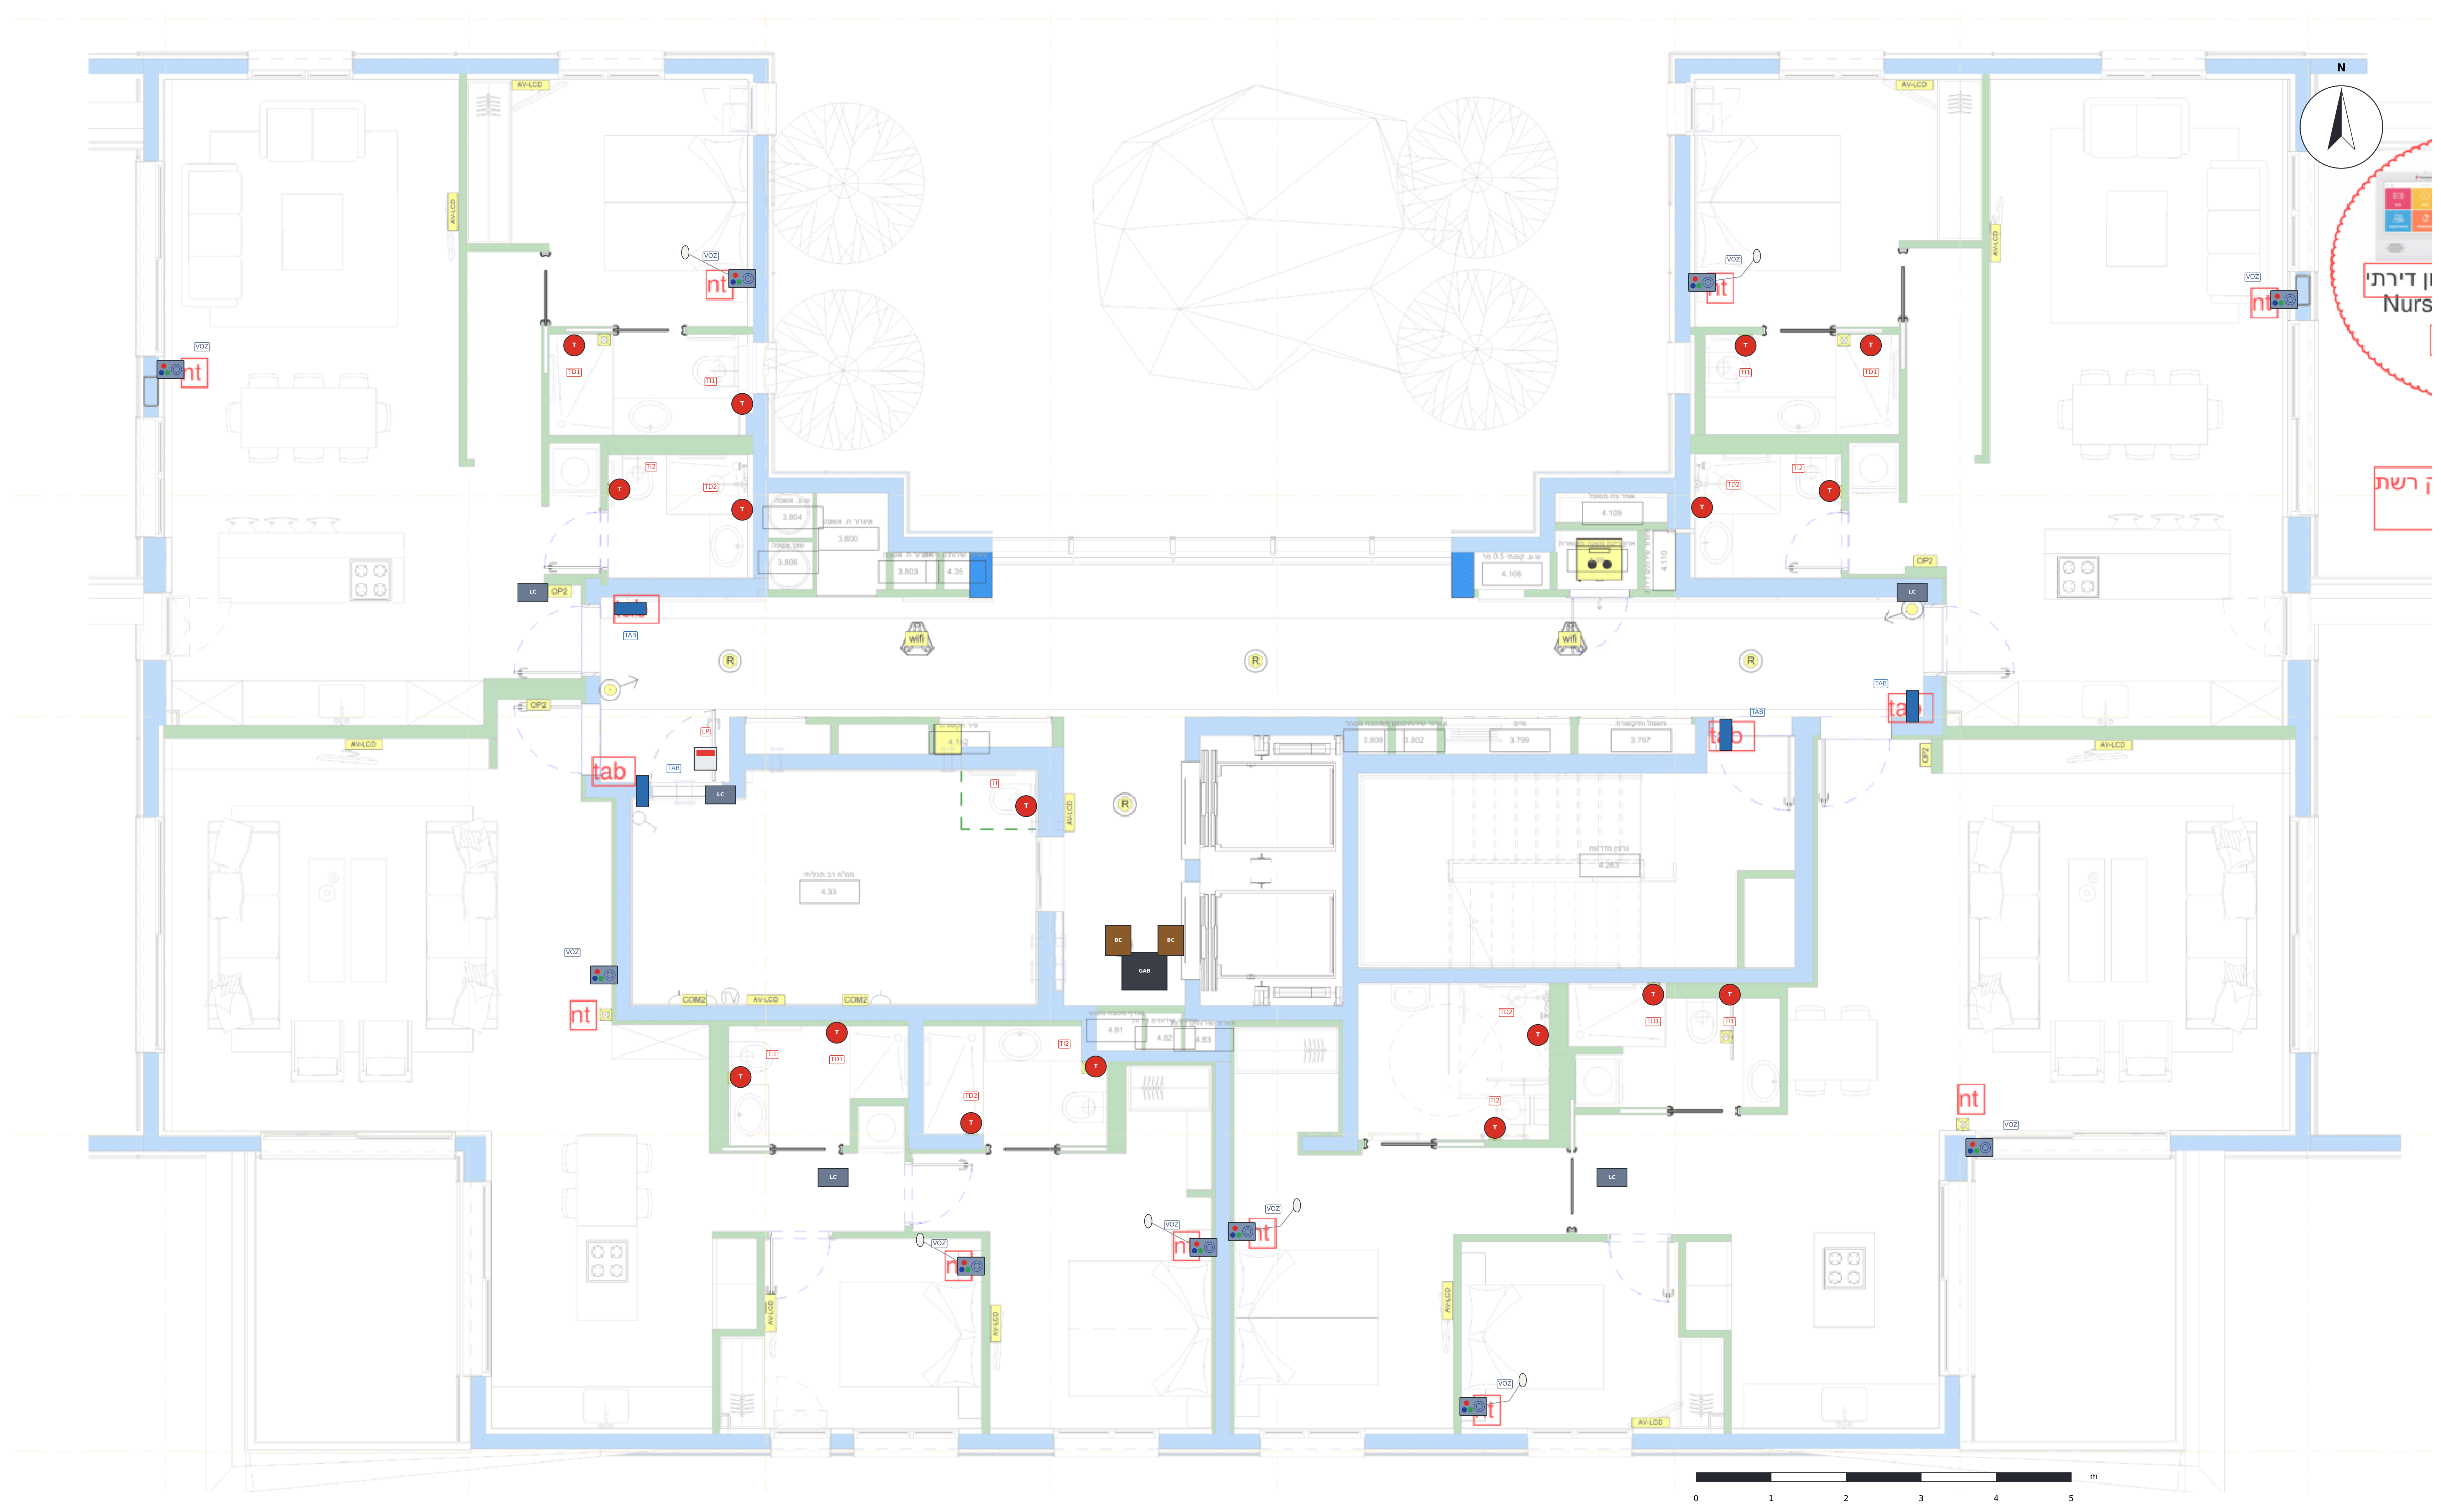
N
nt
tab
VOZ
T
R
wifi
CP2
AV+LCD
COM2
Nurs
0
1
2
3
4
5
m

NOTES · תורעה

1. עקר: תינכות IT L2 לש חוקלה םע םינומיס ולש םודאב:
«nt» = לנפ קילוי ו-«tab» = טלבאט הסינכב.

2. לעמ, בצבע: הציוד ההעצה וז.
לכ לנפ וכל טלבאט םיאצמנ םוקמב שהקלוח סימן.

L2 3. הריבועים םיבוהצה ☒ ירדחב הצהרה תינכותב
הם תוכישמ לבחה (אסלה ומקלחת).

4. 4 םיטלבאטה יבולב, ליד תלד לכ הריד,
.«tab» ומכ םינומיס

5. תוינכותל L2 ו-L5 (סיסב ההצעה) ותוא הנבמ;
L5 8 איה הקומה תיסופיטה תומוקל 1 דע.

DEVICES · EQUIPOS · דויצ

🟦	TAB · טלבאט הסינכב (iPad / דיאורדנא) – רובידו האירק, הבוג 1.40 מ' Door tablet – call and voice · רובידו האירק – טלבאט הסינכב
▨	VOZ · לנפ קילוי םע לחצנים ACE82182451 – סלון ירדחו הניש, הבוג 1.20–1.30 מ' Voice panel with buttons – living room and bedrooms · לנפ קילוי םע םינצחל – סלון ירדחו הניש
○	סגא האירק ליד הטימה (הנישה ירדחב) Call pear next to the bed (bedrooms) · סגא האירק ליד הטימה
T	TI / TD · לבח תכישמ ACE40320303W – אסלה ומקלחת, הבוג 1.85 מ' Pull-cord – toilet and shower, h 1.85 m · לבח תכישמ – אסלה ומקלחת, הבוג 1.85 מ'
🟥	LP · תרונמ םסדרוןו ACE41020309 – לעמ דלת לכ שירותים ציבוריים Corridor light – above each public toilet door · תרונמ םסדרוןו – לעמ דלת לכ שירותים ציבוריים

שירותים קריאת אחות

לבח תכישמ

טבלט אנדרואיד קריאת אחות
Advantecnia
Llamada de enfermera
Hospital
Salud y bienestar

טלבאט הסינכב (iPad / דיאורדנא)

מנורה קריאת אחות

תרונמ םסדרוןו

פנל קריאת אחות

לנפ קילוי םע לחצנים

ןגומ רויד · ןוכיתה םי ילדגמ

תוריד 32 · תומוק 8 + עקרק – תוחא תאירק

Telab International :ןכוה ע"י ACE BG · Advantecnia :תכרעמ

העצההו (תינכות L2) חוקלה ינומיס

Client marks (plan L2) and proposal

SCALE · הדימ הנק	DATE · ךיראת	REV	ןוילג
1:60	15/10/2026	B	03

בסיס: תינכות לכירדאה L5 (זוג דסמ / Triplet) · םירטמב תודימ

טמרופ A1 · הרודהמ B – לע התינכות תיתימאה

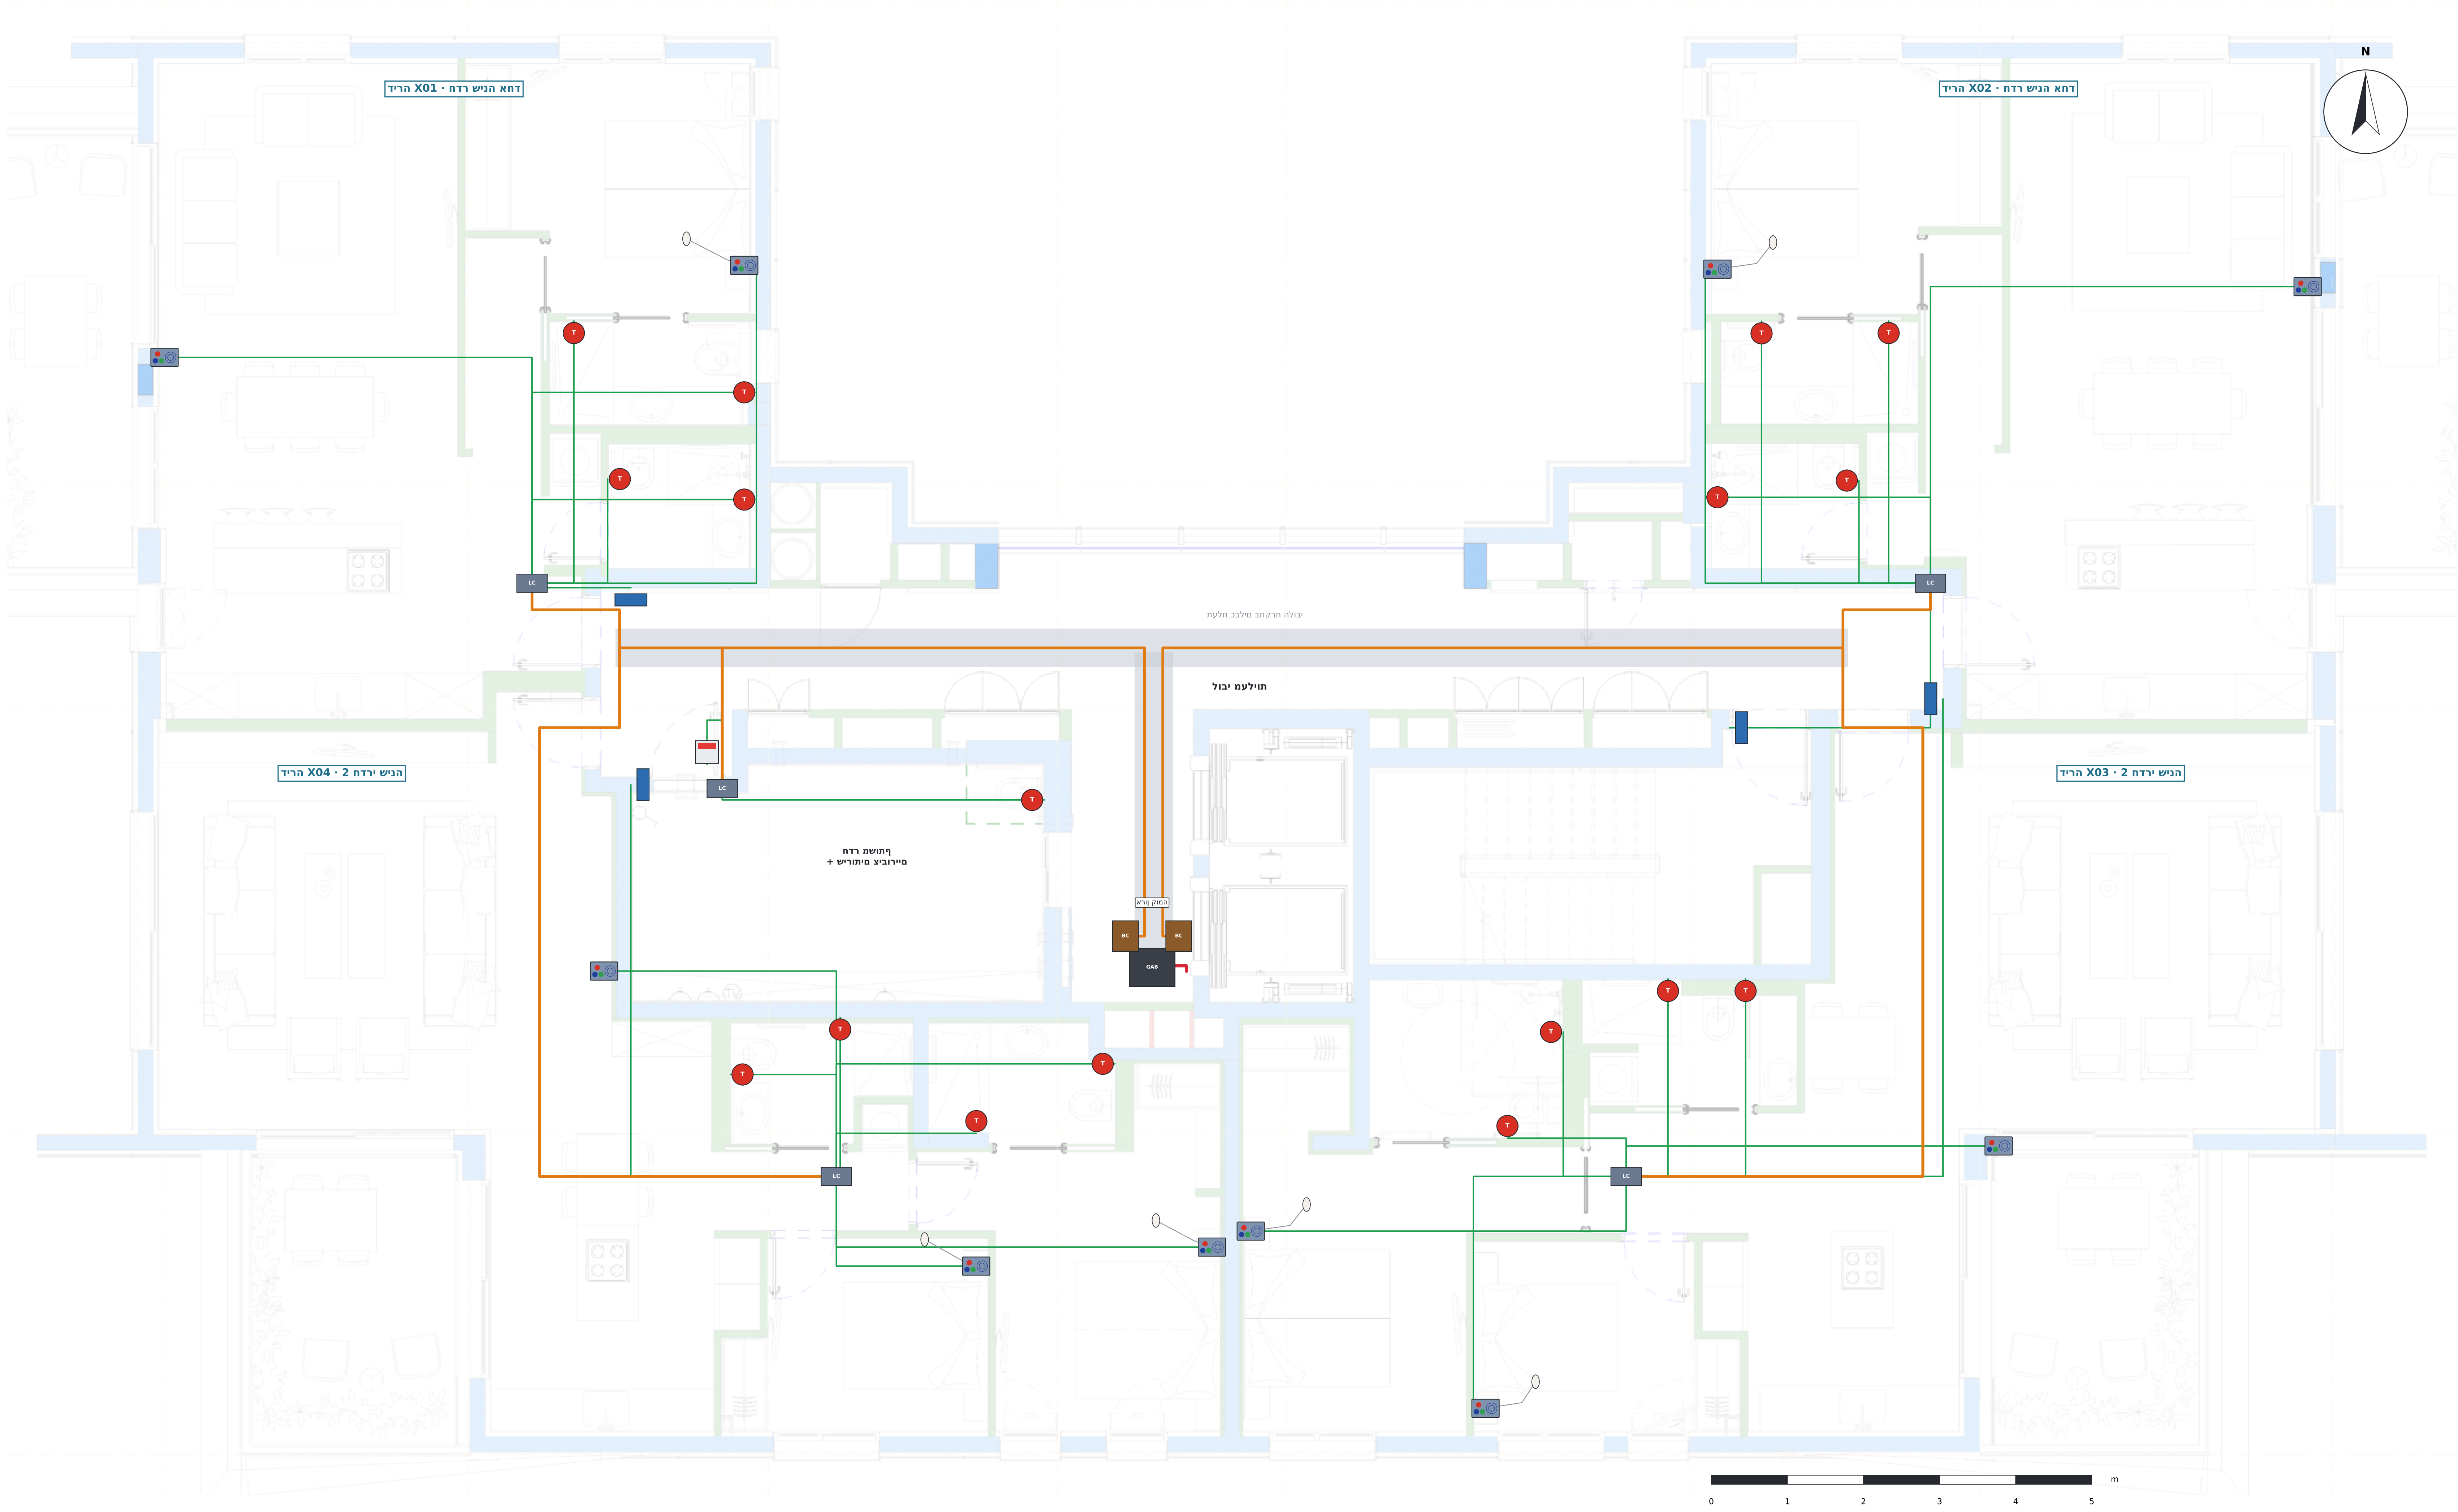

WIRING · CABLEADO · טוויח

🟩 Cat6 ילאידר: לכ ןקתה ← LCom הרידה לש
Cat6 radial: each device → apartment LCom · Cat6 ילאידר: לכ ןקתה ← LCom הרידה לש

🟧 Cat6 / Cat7 תרשרש: LCom ← LCom ← BoxCom הרקתב
Cat6 / Cat7 chain: LCom → LCom → BoxCom · Cat6 / Cat7 תרשרש: LCom ← LCom ← BoxCom

🟥 Cat6A / Cat7 תשר: BoxCom ← גתמ PoE ← דומע ← תרש עקרק
Cat6A / Cat7 network: BoxCom → switch → riser → GF server · Cat6A / Cat7 תשר: BoxCom ← גתמ ← דומע ← תרש

םיכרוא המוקב תיסופיט (אלל הברזה)

🟩	Cat6 ילאידר ךותב הרידה	**183 m**
🟧	Cat6 / Cat7 תרשרש LCom ← BoxCom	**80 m**
🟥	Cat6A / Cat7 ןורא דומעו	**7 m**

NOTES · תורעה

1. לכ ןקתה רבוחמ תילאידר (Cat6) ל-LCom הרידה לש, הרקתב האובמה.
2. ה-LCom םירשורשמ תלעתב הלוביב דע ה-BoxCom הרקתב,
ןוראה דיל: x04 ← x01 ← ךתושמ רדח ← BoxCom 2 ← x03 ← x02 · BoxCom 1.
3. ה-BoxCom םידרוי גתמל ה-PoE ןוראב; הלוע גתממה
דומעב Cat6A / Cat7 דע תרשה עקרקב.
4. לוכה PoE: ןיא ךרוצ ב-230V ינקתהל הרידה.

NOTES · תורעה

1. סיסב: תינכות תילכירדא L5 (תיסופיט המוק) – 8 תומוקה תוהז: 4 תוריד המוקב, 32 ךסב הכול.
2. תוריד x01 ו-x02: רדח הניש דחא, ןולס םע חבטמ ו-2 ירדח הצחר. תוריד x03 ו-x04: 2 ירדח הניש ו-2 ירדח הצחר.
3. טלבאט הסינכב לכל הריד (iPad / דיאורדנא) האירקל ולדיבור םע האחות.
4. לנפ ילוק םע םינצחל (ACE82182451) ןולסב לכבו רדח הניש; רדחב הנישה םע אגס דיל הטימה.
5. תוכישמ לבח (ACE40320303W) הלסאב ובמקלחת לכב ירדח הצחרה, הבוגב 1.85 מ'.
6. םיתוריש םייביצ לכב המוק רדחב ךתושמה: תכישמ לבח + תרונמ ןורדסמ לעמ הלדת. םע 2 עקרקב – 10 םיתוריש םייביצ.
7. ןורא המוק דיל תוילעמה םע גתמ PoE D-Link DES-1210-28P; 2 ה-BoxCom הרקתב ודיל.
8. םימוקימ יפל ינומיס הלקוח תוניכותב L2 (nt = לנפ ילוק, tab = טלבאט): ןאר ןויליג 03.

ןגומ רויד · ןוכיתה םי ילדגמ
קראיה תוחא – עקרק + 8 תומוק · 32 תוריד
Telab International :ע"י ןכוה ACE BG · Advantecnia :תכרעמ

טוויח · 1–8 תיסופיט המוק
Typical floor F1–F8 · wiring

SCALE · הדימ הנק	DATE · ךיראת	REV	ןויליג
1:60	**15/10/2026**	**B**	**04**

סיסב: תינכות לכירדאה L5 (זוע דסמ / Triplet) · םירטמב תודימ
טמרופ A1 · הרודהמ B – לע תינכותה תיתימאה

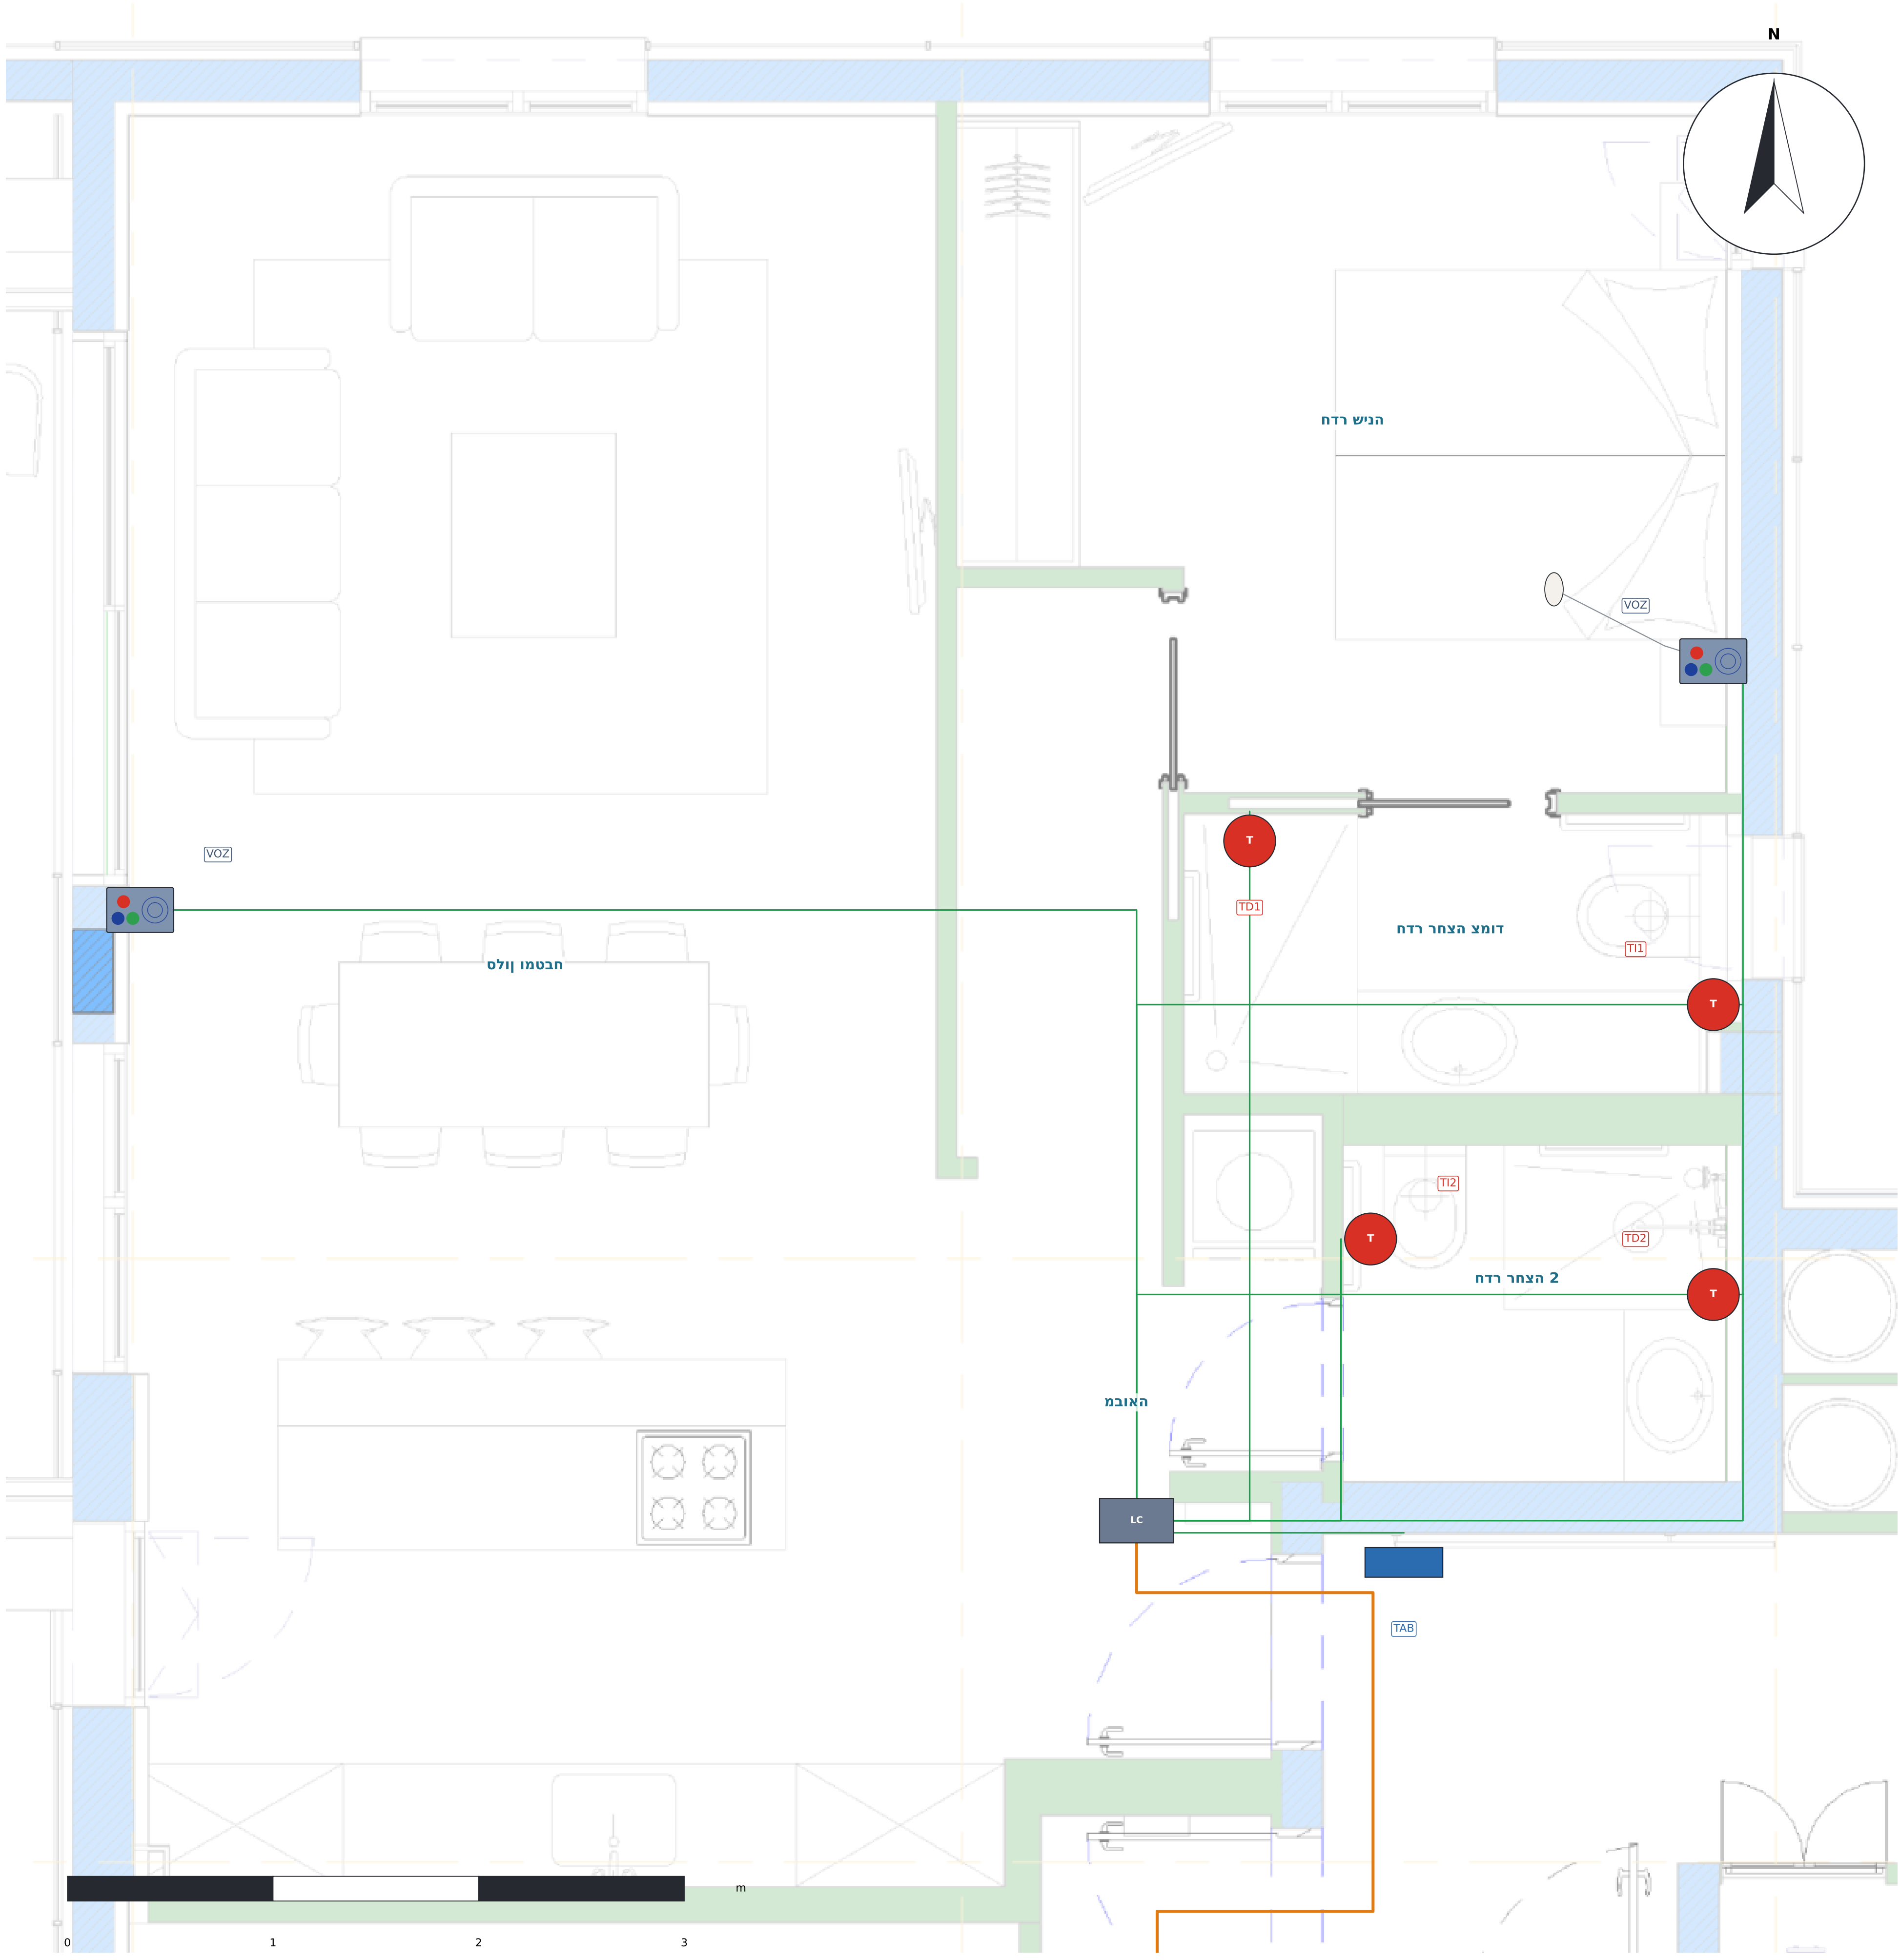

ציוד הדירה

ID	התקן	חדר	גובה
TAB	טאבלט בכניסה	מבואה	1.40 מ'
VOZ-S	פנל קולי עם לחצנים	סלון ומטבח	1,30 m
VOZ-D	פנל קולי עם לחצנים + אגס	חדר שינה	1,20 m
TI1	משיכת חבל	חדר רחצה צמוד	1.85 מ'
TD1	משיכת חבל	חדר רחצה צמוד	1.85 מ'
TI2	משיכת חבל	חדר רחצה 2	1.85 מ'
TD2	משיכת חבל	חדר רחצה 2	1.85 מ'
LCOM	LCom ACE71610003	מבואה	2,55 m

SYMBOLS · SÍMBOLOS · סמלים

- 🟦 TAB · טאבלט בכניסה (iPad / אנדרואיד) – קריאה ודיבור, גובה 1.40 מ'
  Door tablet – call and voice · טאבלט בכניסה – קריאה ודיבור
- VOZ · פנל קולי עם לחצנים ACE82182451 – סלון וחדרי שינה, גובה 1.20–1.30 מ'
  Voice panel with buttons – living room and bedrooms · פנל קולי עם לחצנים – סלון וחדרי שינה
- אגס קריאה ליד המיטה (בחדרי השינה)
  Call pear next to the bed (bedrooms) · אגס קריאה ליד המיטה
- T TI / TD · משיכת חבל ACE40320303W – אסלה ומקלחת, גובה 1.85 מ'
  Pull-cord – toilet and shower, h 1.85 m · משיכת חבל – אסלה ומקלחת, גובה 1.85 מ'
- LP · מנורת מסדרון ACE41020309 – מעל דלת כל שירותים ציבוריים
  Corridor light – above each public toilet door · מנורת מסדרון – מעל דלת כל שירותים ציבוריים
- LC LC · LCom ACE71610003 – מרכז הדירה (תקרה)
  LCom – apartment hub (ceiling) · LCom – מרכז הדירה (תקרה)
- BC BC · BoxCom ACE70810000 – מרכז באס לכמה דירות (תקרה)
  BoxCom – bus hub for several apartments (ceiling) · BoxCom – מרכז באס לכמה דירות (תקרה)

NOTES · הערות

1. דירה x02 היא תמונת ראי של x01 (אותו ציוד).
2. טאבלט בלובי, ליד דלת הכניסה (סימון «tab» של הלקוח).
3. פנל קולי בסלון ובחדר השינה (עם אגס ליד המיטה).
4. חדרי רחצה 2: משיכת חבל באסלה ובמקלחת בכל אחד (4 משיכות חבל).
5. הכול מחובר רדיאלית ב-Cat6 ל-LCom במבואה.

שירותים קריאת אחות

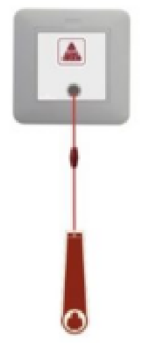

משיכת חבל

טבלט אנדרואיד קריאת אחות

Advantecnia
Llamada de enfermera

טאבלט בכניסה (iPad / אנדרואיד)

מנורה קריאת אחות

מנורת מסדרון

פנל קריאת אחות

פנל קולי עם לחצנים

מגדלי ים התיכון · דיור מוגן
32 דירות · 8 קומות + קרקע – קריאת אחות
מערכת: ACE BG · Advantecnia   הוכן ע"י: Telab International

דירת חדר שינה אחד (x01 / x02)

1-bedroom apartment (x01 / x02)

SCALE · קנה מידה	DATE · תאריך	REV	גיליון
1:30	**15/10/2026**	**B**	**05**

בסיס: תוכנית האדריכל L5 (מסד עוז / Triplet) · מידות במטרים
פורמט A1 · מהדורה B – על התוכנית האמיתית

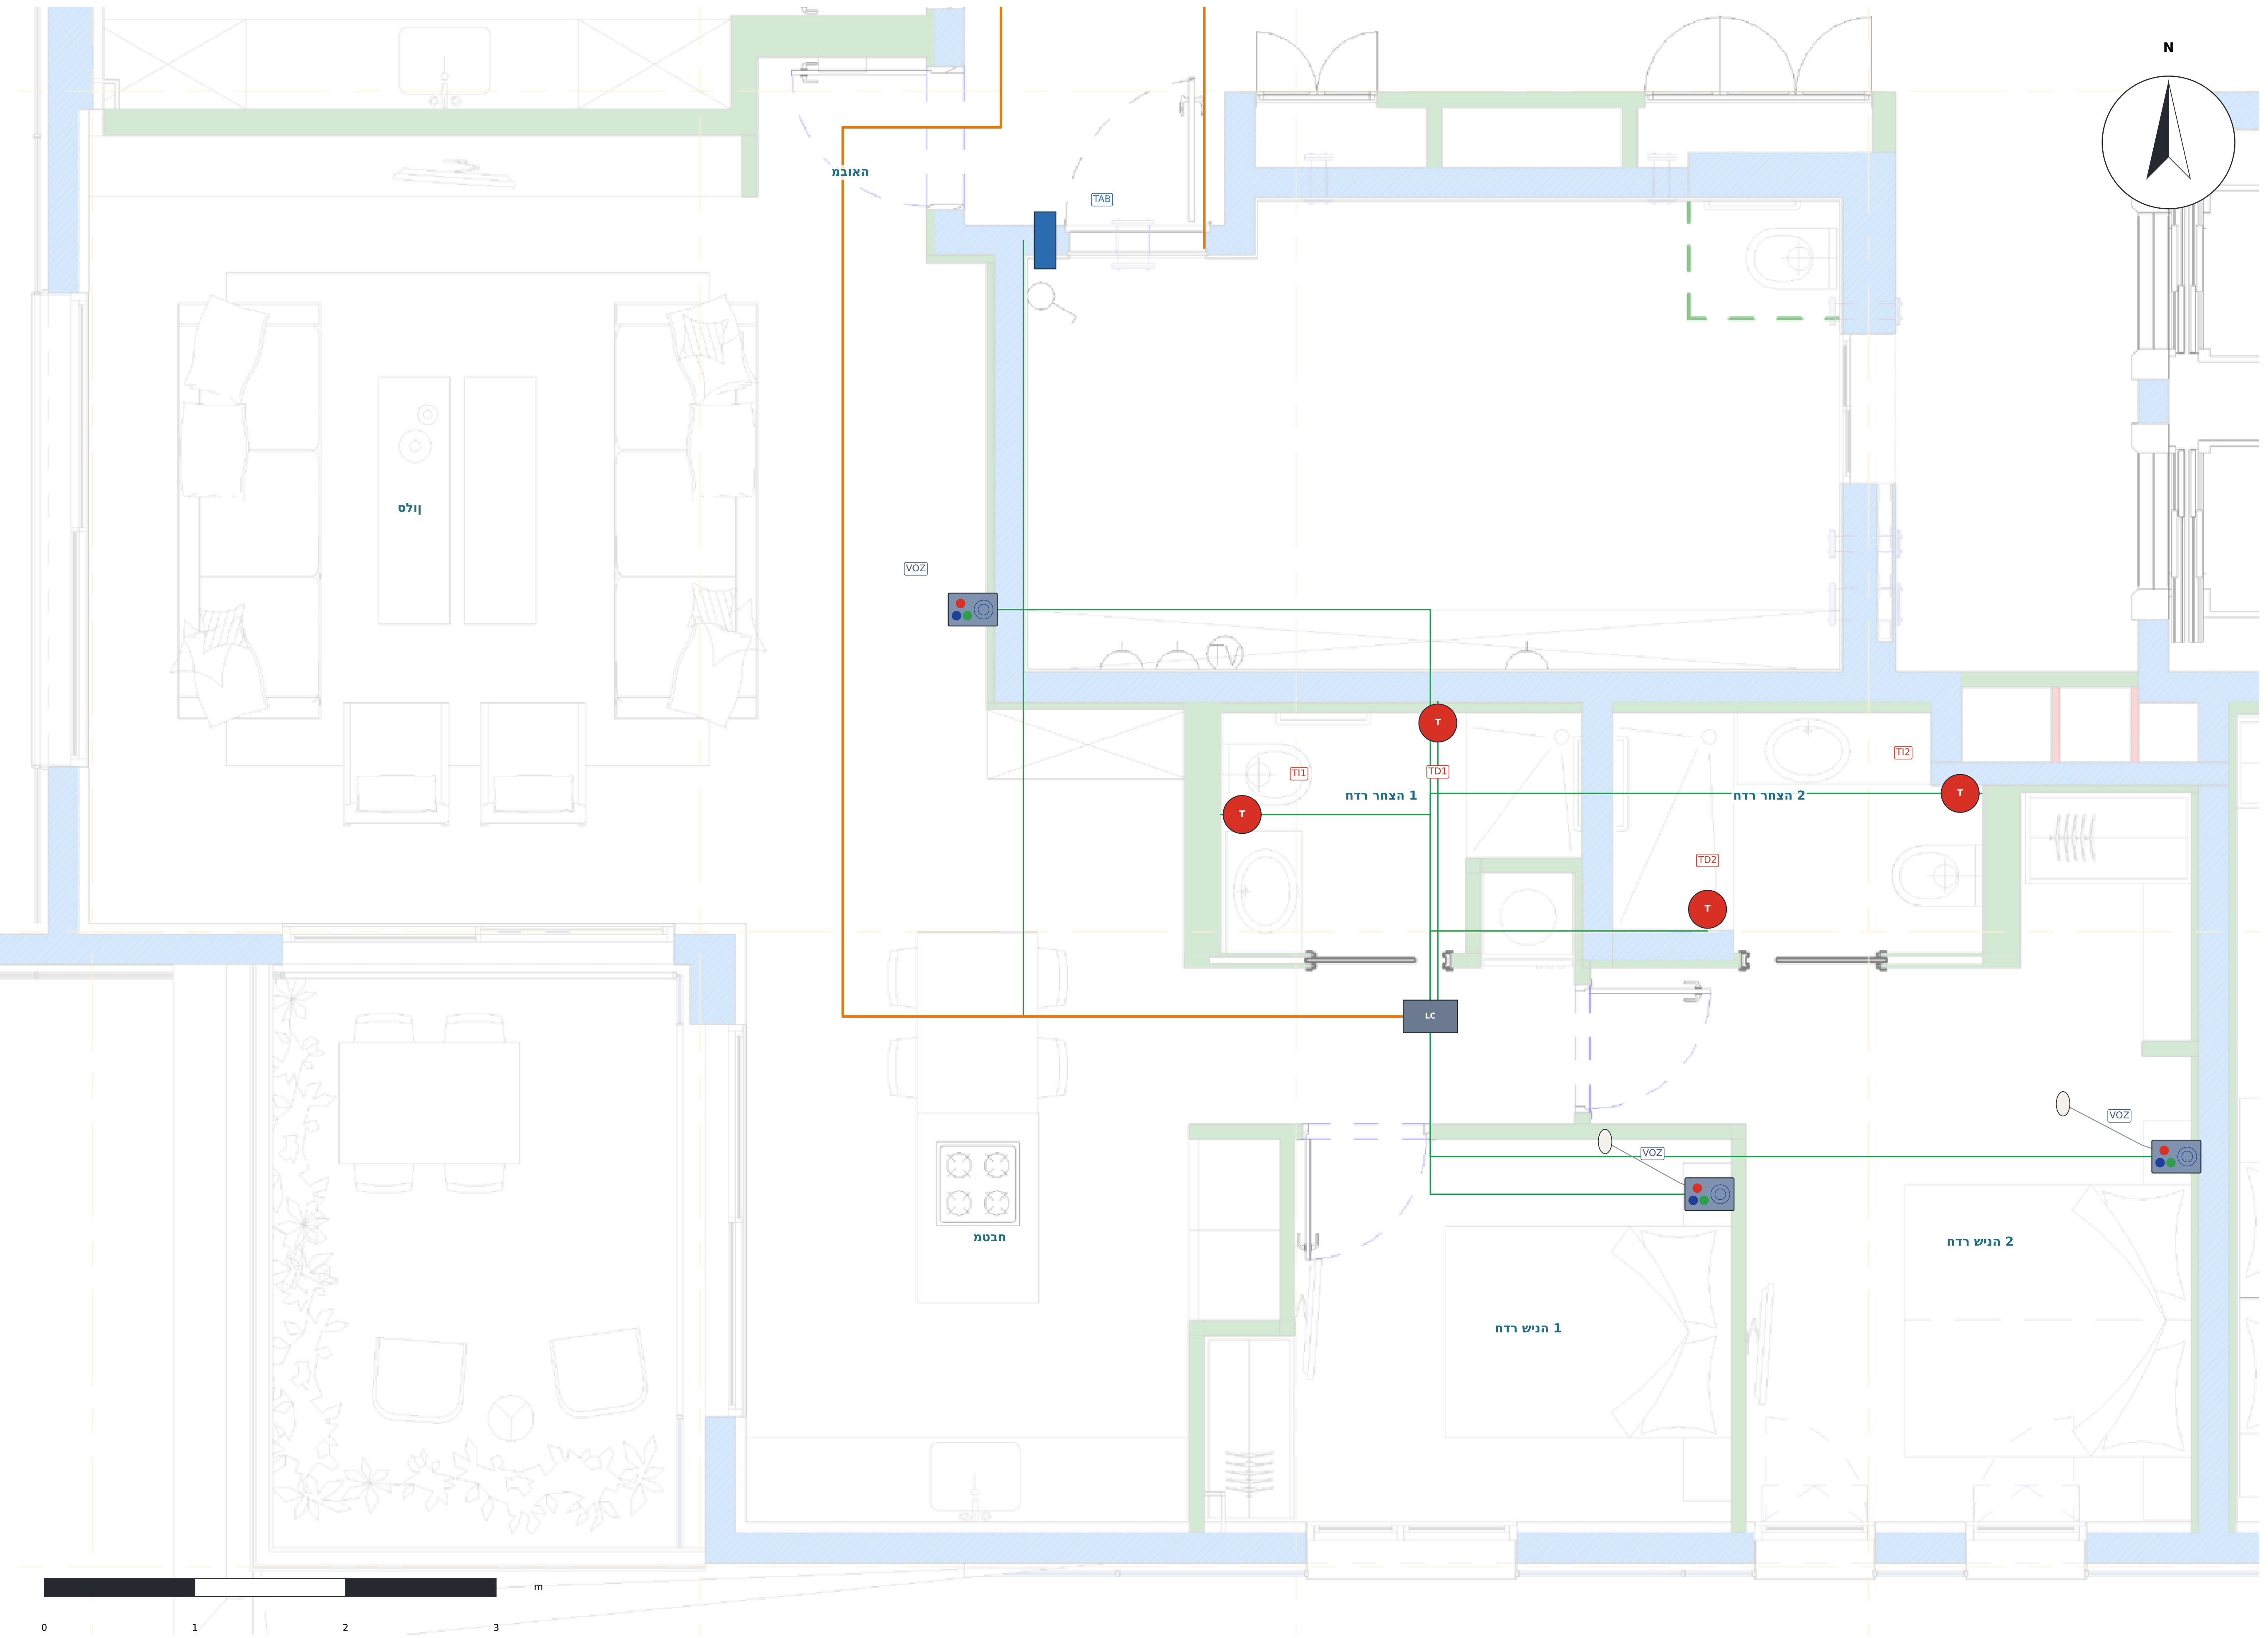
N
האובמ
TAB
ןולס
VOZ
T
TI1
TD1
הצחר ךדח 1
הצחר ךדח 2
TI2
TD2
LC
VOZ
חבטמ
הניש ךדח 1
הניש ךדח 2
m
0
1
2
3

הרידה דויצ

ID	ןקתה	רדח	הבוג
TAB	הסינכב טלבאט	האובמ	1.40 מ'
VOZ-S	םינצחל םע ילוק לנפ	ןולס	1,30 m
VOZ-D1	םינצחל םע ילוק לנפ + סגא	הניש רדח 1	1,20 m
VOZ-D2	םינצחל םע ילוק לנפ + סגא	הניש רדח 2	1,20 m
TI1	לבח תכישמ	הצחר רדח 1	1.85 מ'
TD1	לבח תכישמ	הצחר רדח 1	1.85 מ'
TI2	לבח תכישמ	הצחר רדח 2	1.85 מ'
TD2	לבח תכישמ	הצחר רדח 2	1.85 מ'
LCOM	LCom ACE71610003	האובמ	2,55 m

SYMBOLS · SÍMBOLOS · םילמס

- ▬ TAB · הסינכב טלבאט (iPad / דיאורדנא) – רובידו האירק ,הבוג 1.40 מ'
  Door tablet – call and voice · הסינכב טלבאט – רובידו האירק
- ▣ VOZ · םינצחל םע ילוק לנפ ACE82182451 – ןולס ירדחו הניש ,הבוג 1.20–1.30 מ'
  Voice panel with buttons – living room and bedrooms · םינצחל םע ילוק לנפ – ןולס ירדחו הניש
- ○ הטימה דיל האירק סגא (הנישה ירדחב)
  Call pear next to the bed (bedrooms) · הטימה דיל האירק סגא
- T TI / TD · לבח תכישמ ACE40320303W – הלסא תחלקמו ,הבוג 1.85 מ'
  Pull-cord – toilet and shower, h 1.85 m · לבח תכישמ – הלסא תחלקמו ,הבוג 1.85 מ'
- ▭ LP · ןורדסמ תרונמ ACE41020309 – םיירוביצ םיתורש לכ תלד לעמ
  Corridor light – above each public toilet door · ןורדסמ תרונמ – םיירוביצ םיתורש לכ תלד לעמ
- LC LC · LCom ACE71610003 – הרידה זכרמ (הרקת)
  LCom – apartment hub (ceiling) · LCom – הרידה זכרמ (הרקת)
- BC BC · BoxCom ACE70810000 – תוריד המכל סאב זכרמ (הרקת)
  BoxCom – bus hub for several apartments (ceiling) · BoxCom – תוריד המכל סאב זכרמ (הרקת)

NOTES · תורעה

1. הרידב x03 דויצ ותוא (הצחרה ירדח הסירפב הנוש).
2. טלבאט יבולב ,הסינכה תלד דיל (ןומיס «tab» לש חוקלה).
3. לנפ ילוק ןולסב ינשבו הנישה ירדח (םע סגא דיל הטימה).
4. 2 הצחר ירדח: תכישמ לבח הלסאב תחלקמבו לכב דחא (4 תוכישמ לבח).
5. לוכה רבוחמ תילאידר ב-Cat6 ל-LCom ןורדסמב הנישה ירדח.

שירותים קריאת אחות

לבח תכישמ

טבלט אנדרואיד קריאת אחות
Advantecnia
Llamada de enfermera
Hospital
Salud y bienestar

הסינכב טלבאט (iPad / דיאורדנא)

מנורה קריאת אחות

ןורדסמ תרונמ

פנל קריאת אחות

םינצחל םע ילוק לנפ

ןגומ רויד · ןוכיתה םי ילדגמ

תוריד 32 · תומוק 8 + עקרק – תוחא תאירק

Telab International :ןכוה י"ע   ACE BG · Advantecnia :תכרעמ

(x04 / x03) הניש ירדח ינש תריד

2-bedroom apartment (x04 / x03)

SCALE · הדימ הנק	DATE · ךיראת	REV	ןוילג
1:35	15/10/2026	B	06

בסיס: תוניכת לכירדאה L5 (זוע דסמ / Triplet) · םירטמב תודימ

טמרופ A1 · הרודהמ B – לע תונכותה תיתימאה

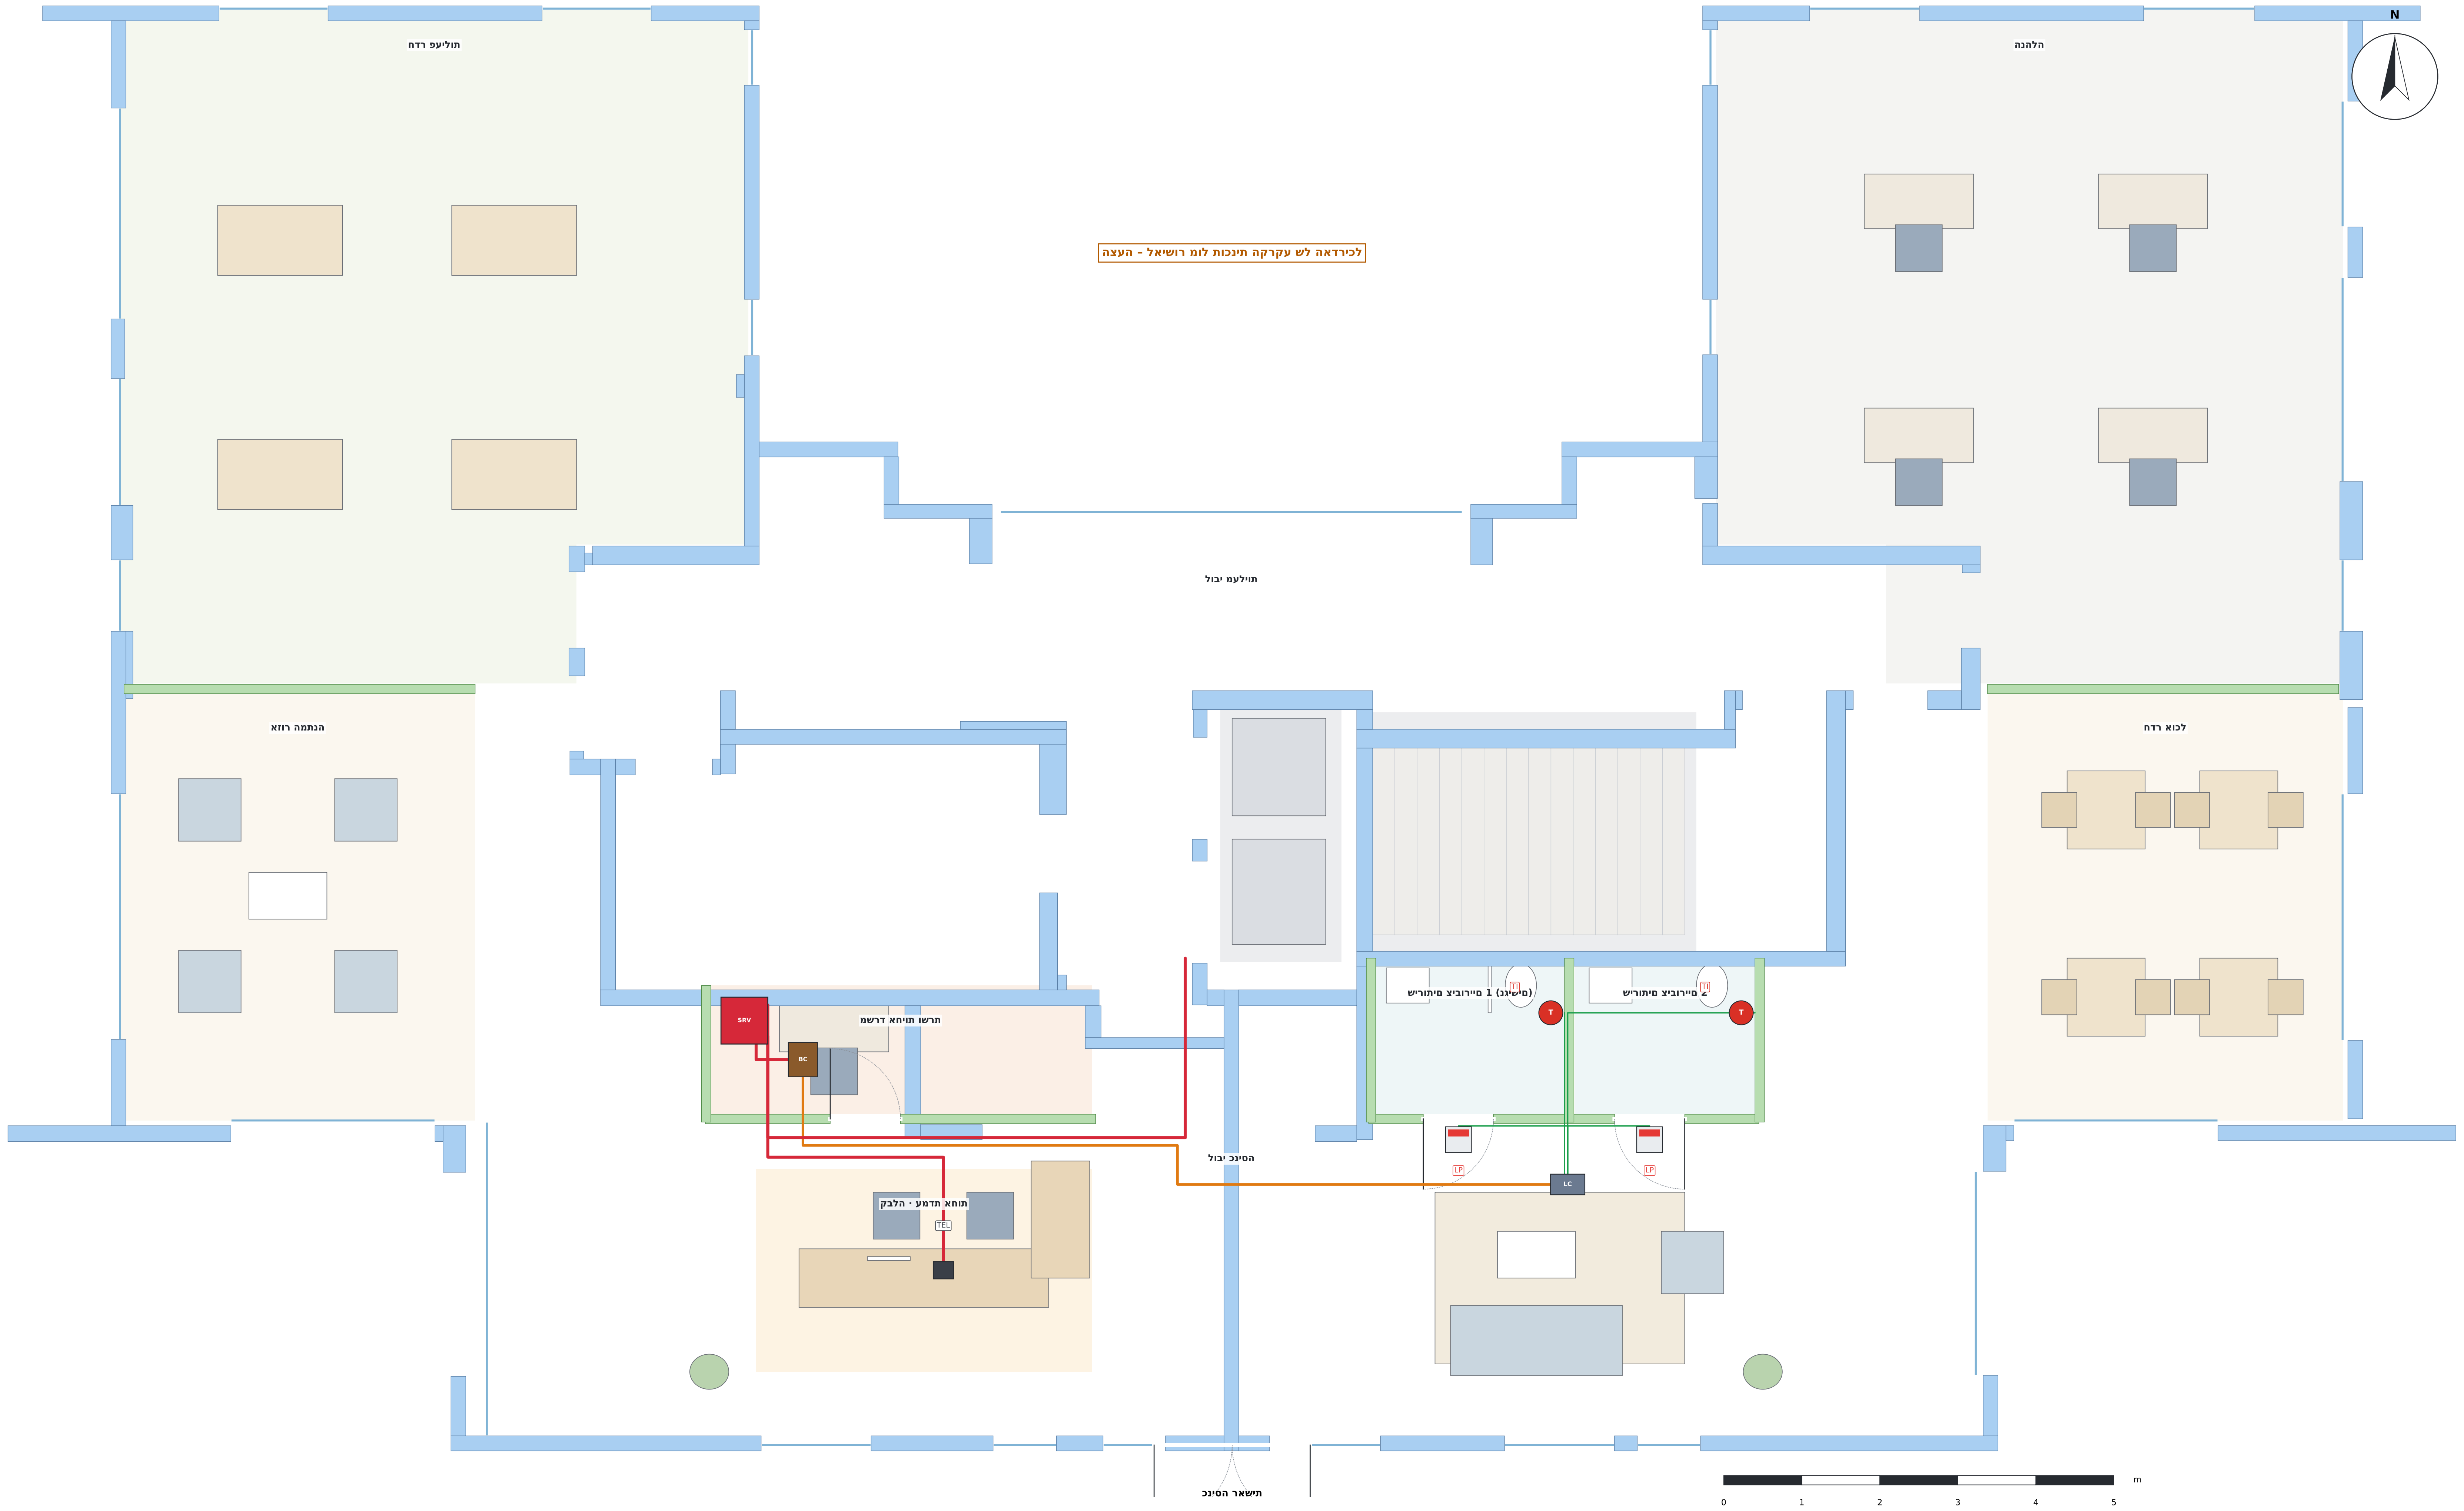
חדר פעילות
הצעה – לאישור מול תוכנית הקרקע של האדריכל
הנהלה
N
לובי מעליות
אזור המתנה
חדר אוכל
SRV
BC
משרד אחיות ושרת
שירותים ציבוריים 1 (נגישים)
שירותים ציבוריים 2
TI
T
LP
LC
לובי כניסה
קבלה · עמדת אחות
TEL
כניסה ראשית
0
1
2
3
4
5
m

פרט · קבלה ועמדת אחות (1:40)

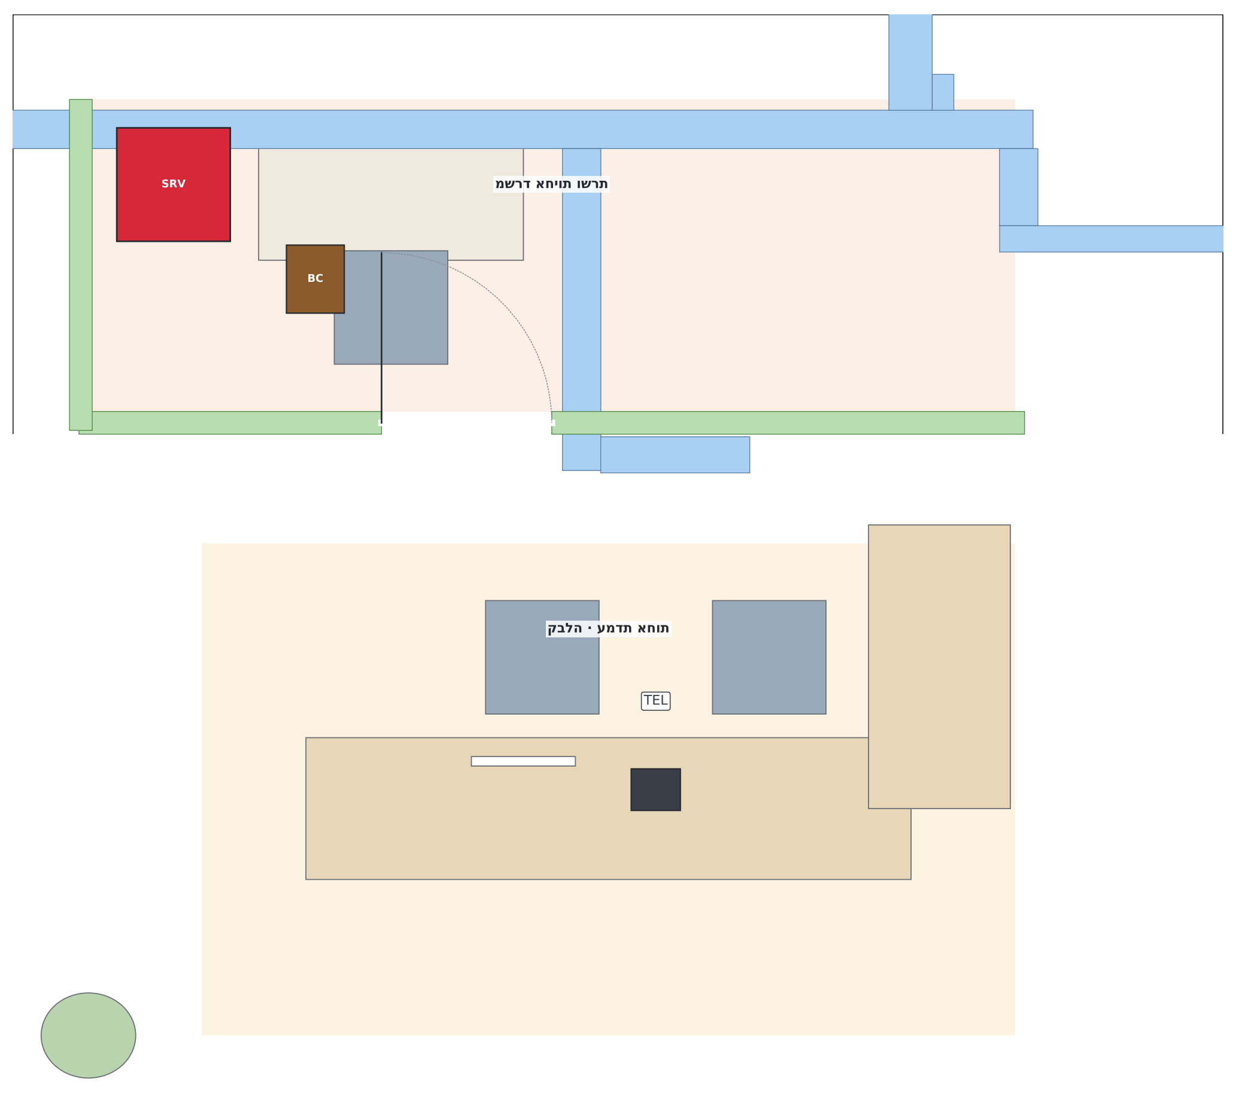
SRV
BC
משרד אחיות ושרת
קבלה · עמדת אחות
TEL

NOTES · הערות

1. עמדת האחות בקבלה, מול הכניסה והמעליות.
2. על העמדה: טלפון Grandstream אנדרואיד, מחובר ישירות למתג ה-PoE. כל קריאה מוצגת בצבע שלה.
3. מאחורי העמדה: משרד עם הארון הראשי: שרת Buslogic Premium ומתג PoE D-Link. BoxCom של הקרקע בתקרה.
4. 2 שירותים ציבוריים בקרקע: משיכת חבל ליד האסלה ומנורת מסדרון מעל כל דלת.
5. העמוד מ-8 הקומות יורד בגרעין עד הארון הראשי.
6. פריסת קרקע מוצעת: תעודכן כשתגיע התוכנית של האדריכל.

SYMBOLS · SÍMBOLOS · סמלים

T — TI / TD · משיכת חבל ACE40320303W – אסלה ומקלחת, גובה 1.85 מ'
Pull-cord – toilet and shower, h 1.85 m · משיכת חבל – אסלה ומקלחת, גובה 1.85 מ'

LP · מנורת מסדרון ACE41020309 – מעל דלת כל שירותים ציבוריים
Corridor light – above each public toilet door · מנורת מסדרון – מעל דלת כל שירותים ציבוריים

LC — LC · LCom ACE71610003 – מרכז הדירה (תקרה)
LCom – apartment hub (ceiling) · LCom – מרכז הדירה (תקרה)

TEL — TEL · טלפון Grandstream אנדרואיד – PoE ישירות למתג
Grandstream Android phone – PoE straight to the switch · טלפון Grandstream אנדרואיד – PoE ישירות למתג

SRV — SRV · ארון קרקע: שרת Buslogic Premium + מתג PoE D-Link
GF rack: Buslogic Premium server + D-Link PoE switch · ארון קרקע: שרת Buslogic Premium + מתג PoE D-Link

BC — BC · BoxCom ACE70810000 – מרכז באס לכמה דירות (תקרה)
BoxCom – bus hub for several apartments (ceiling) · BoxCom – מרכז באס לכמה דירות (תקרה)

טלפון העמדה – איזה צבע מוצג

🟥	אזעקה (משיכה / SOS)	אדום
🟩	נוכחות: לחצן ירוק פעם אחת	ירוק
▨	לחצן ירוק שוב: מבטל קריאה או אזעקה	נמחק
🟦	קריאת רופא: לחצן כחול (blue call)	כחול
🟧	שיחה קולית	כתום / צהוב

מגדלי ים התיכון · דיור מוגן
קריאת אחות – קרקע + 8 קומות · 32 דירות
מערכת: ACE BG · Advantecnia   הוכן ע"י: Telab International

קומת קרקע · לובי ועמדת אחות

Ground floor · lobby and nurse desk

SCALE · קנה מידה	DATE · תאריך	REV	גיליון
1:60	15/10/2026	B	07

בסיס: תוכנית האדריכל L5 (מסד זוג / Triplet) · מידות במטרים
פורמט A1 · מהדורה B – על התוכנית האמיתית

א · בניין קרקע + 8 קומות

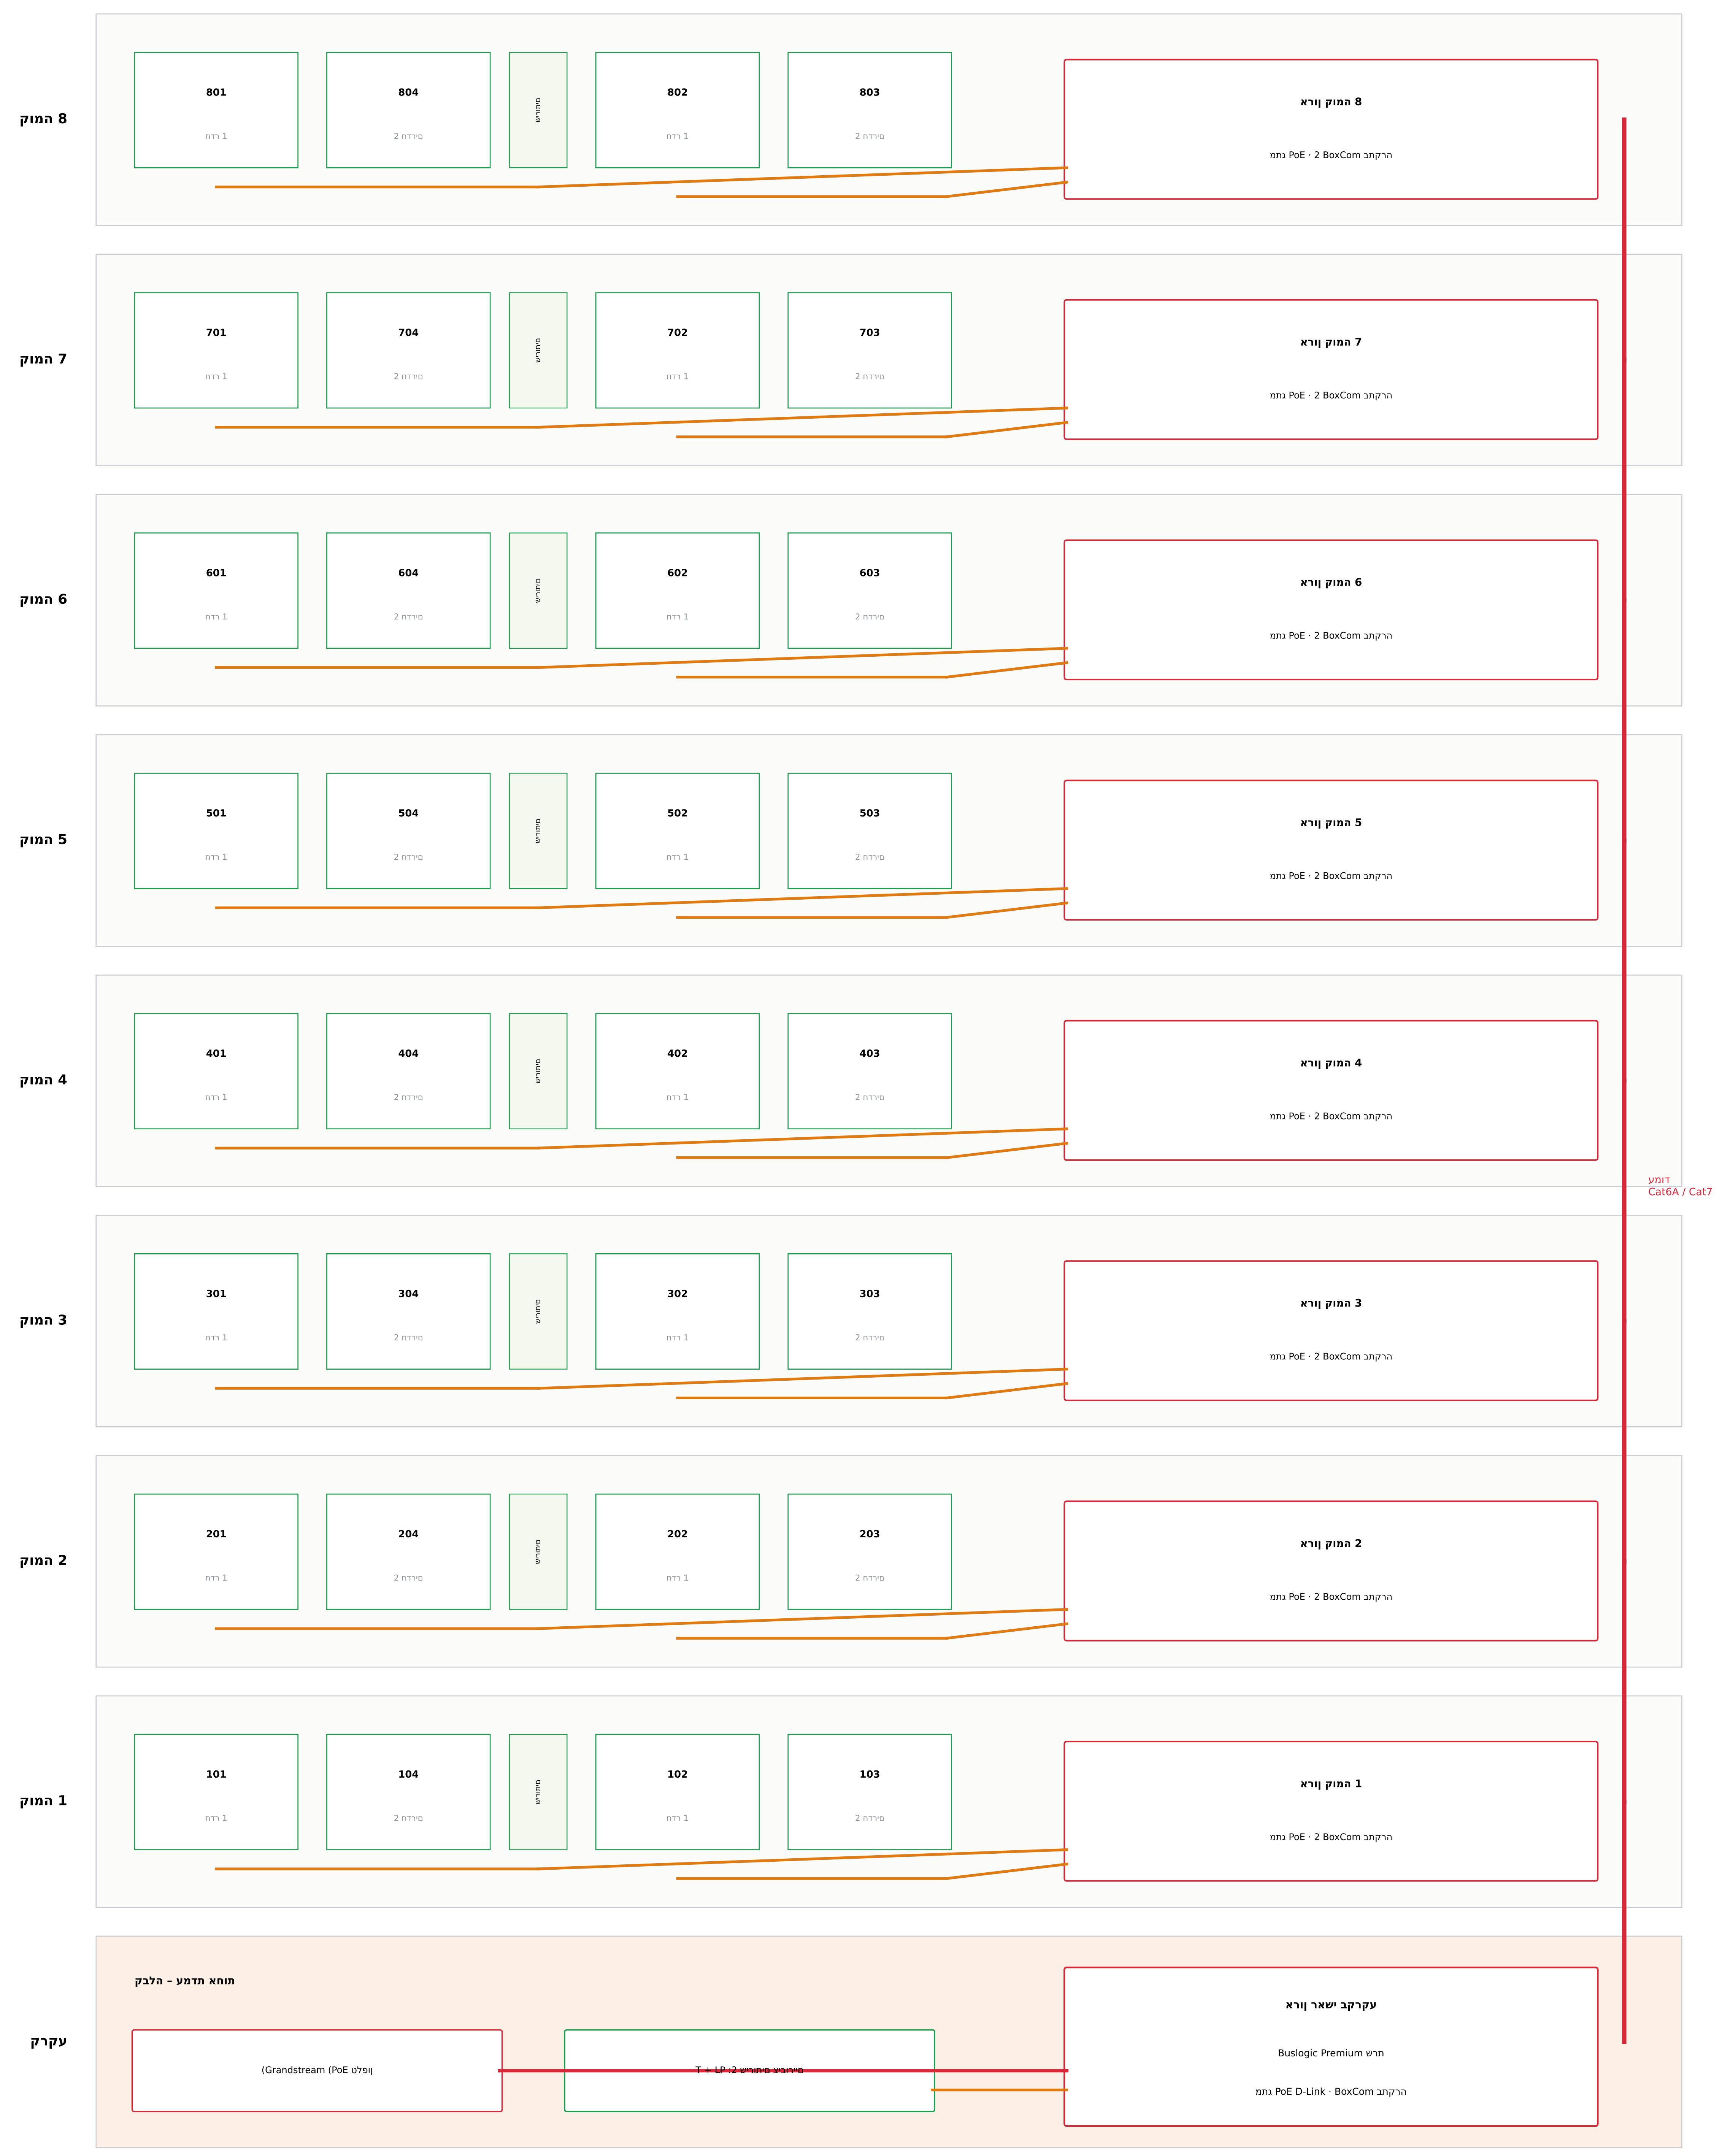
קומה 8
801
דירה 1
804
2 חדרים
שירותים
802
דירה 1
803
2 חדרים
ארון קומה 8
2 BoxCom בתקרה · מתג PoE
קומה 7
701
704
702
703
ארון קומה 7
קומה 6
601
604
602
603
ארון קומה 6
קומה 5
501
504
502
503
ארון קומה 5
קומה 4
401
404
402
403
ארון קומה 4
קומה 3
301
304
302
303
ארון קומה 3
קומה 2
201
204
202
203
ארון קומה 2
קומה 1
101
104
102
103
ארון קומה 1
עמוד
Cat6A / Cat7
קרקע
קבלה – עמדת אחות
טלפון Grandstream (PoE)
שירותים ציבוריים 2: LP + T
ארון ראשי בקרקע
שרת Buslogic Premium
BoxCom בתקרה · D-Link מתג PoE

ב · טופולוגיה של דירה

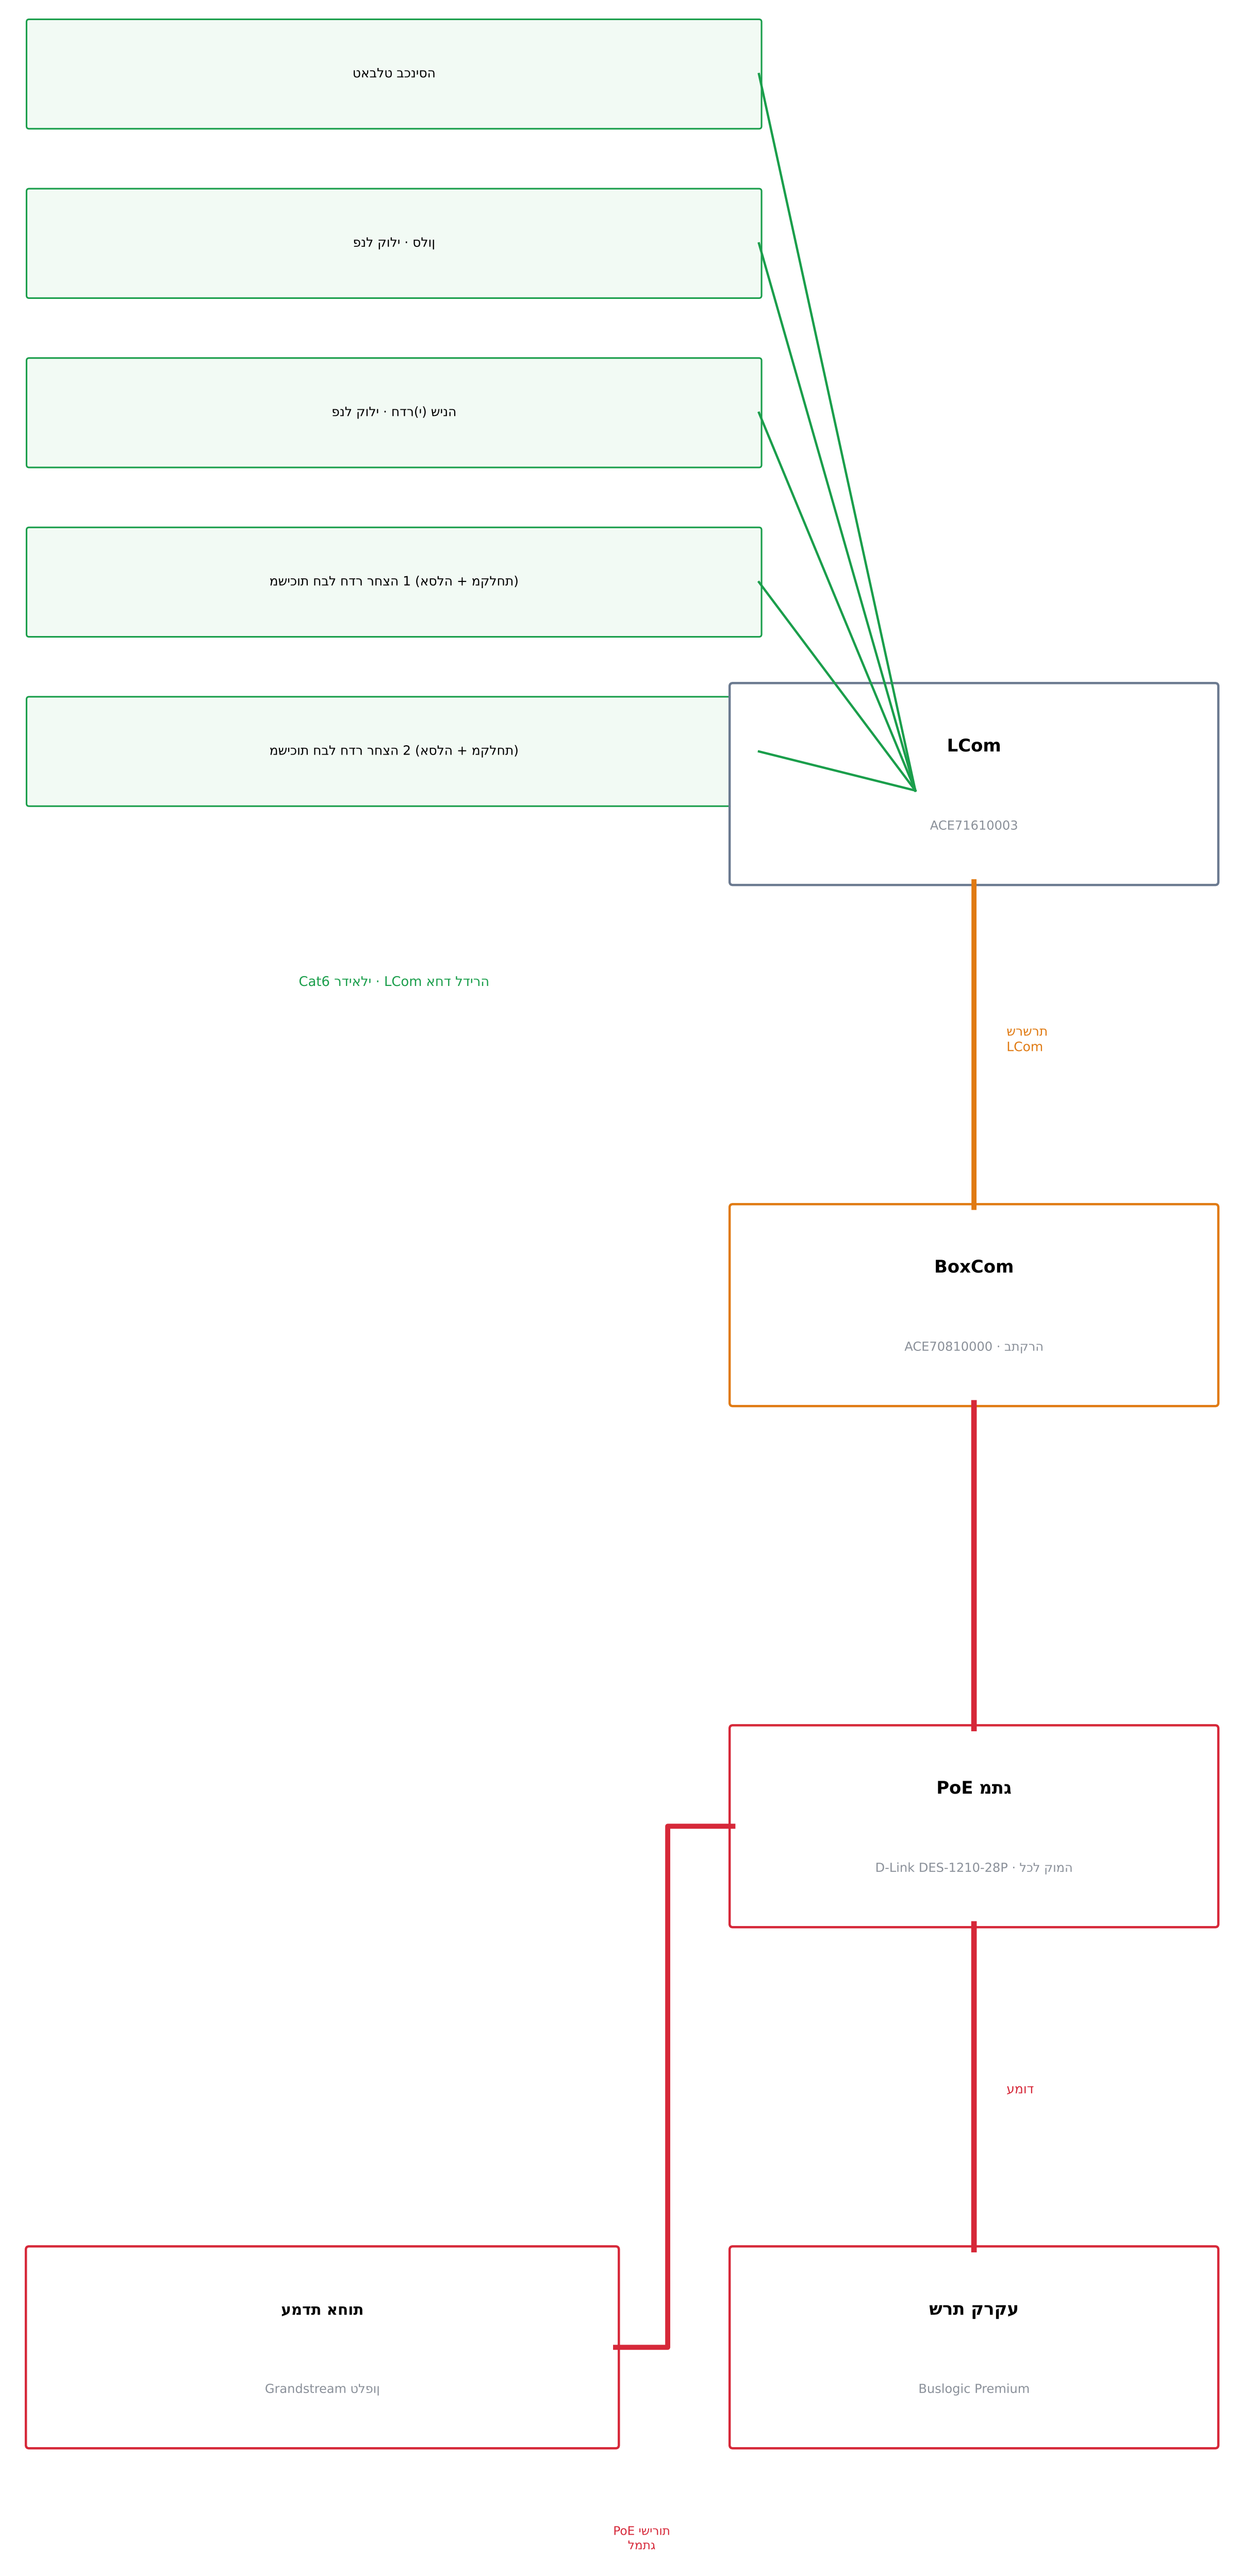
טאבלט בכניסה
סלון · לחצן ליד
חדר(י) שינה · לחצן ליד
מקלחת + אסלה) 1 חדר רחצה בכבל משיכה)
מקלחת + אסלה) 2 חדר רחצה בכבל משיכה)
LCom
ACE71610003
הדירה דרך LCom · אלחוטי Cat6
שרשרת
LCom
BoxCom
ACE70810000 · בתקרה
מתג PoE
D-Link DES-1210-28P · לכל קומה
עמוד
עמדת אחות
טלפון Grandstream
שרת קרקע
Buslogic Premium
PoE ישירות
למתג

NOTES · הערות

1. 8 קומות זהות עם 4 דירות
(2 דירות חדר שינה אחד ו-2 דירות שני חדרי שינה).

2. בכל קומה: 2 BoxCom בתקרה
.PoE-וארון עם מתג ה

3. שרשרת x01 ← x04 :1 ← שירותים ציבוריים.
.x02 ← x03 :2 שרשרת

4. המתגים מחוברים דרך העמוד
עד הארון הראשי בקרקע.

5. טלפון ה-Grandstream בעמדה מחובר
ישירות למתג ה-PoE ומציג
כל קריאה בצבע שלה.

.PoE 6. כל המערכת

7. כמויות ראשוניות: לאמת
מול Advantecnia באתר.

מגדלי ים התיכון · דיור מוגן
קריאת אחות – קרקע + 8 קומות · 32 דירות
הוכן ע"י: Telab International   מערכת: ACE BG · Advantecnia

תרשים אנכי וטופולוגיה

Riser diagram and topology

SCALE · קנה מידה	DATE · תאריך	REV	גיליון
S/E	15/10/2026	B	08

בסיס: תוכנית אדריכלית L5 (מסד זוג / Triplet) · מידות במטרים
פורמט A1 · מהדורה B – על התוכנית האמיתית

רשימת חומרים – כל הבניין (קרקע + 8 קומות · 32 דירות · 10 שירותים ציבוריים)

קוד	תיאור	כמות	הערה
בדירות (32)			
TAB	טאבלט בכניסה (iPad / אנדרואיד) – קריאה ודיבור	**32**	1 לכל דירה
VOZ	ACE82182451 – פנל קריאה קולי עם לחצנים	**80**	סלון + כל חדר שינה
TI/TD	משיכת חבל – ACE40320303W (אסלה ומקלחת)	**128**	4 לכל דירה
LC	LCom – ACE71610003	**32**	1 לכל דירה
שירותים ציבוריים (10)			
T	ACE40320303W – משיכת חבל	**10**	8 קומות + 2 בקרקע
LP	ACE41020309 – מנורת מסדרון	**10**	מעל כל דלת
LC	LCom – ACE71610003	**9**	1 לכל קומה + 1 בקרקע
ארונות ומרכזייה			
BC	BoxCom – ACE70810000 (בתקרה)	**17**	2 לקומה + 1 בקרקע
SW	D-Link DES-1210-28P – מתג 24 יציאות PoE	**9**	1 לכל קומה + קרקע
GAB	ארון קיר 12U עם פאץ' פאנל (למתג)	**8**	1 לכל קומה
GAB-PB	ארון ראשי עומד עם UPS	**1**	קרקע
SRV	שרת Buslogic Premium (Advantcare) עם תוכנה	**1**	קרקע
TEL	טלפון Grandstream אנדרואיד (PoE, צבע לפי סוג קריאה)	**1**	עמדת אחות
כבלים (+ 15% רזרבה)			
—	Cat6 רדיאלי בתוך הדירה (ירוק)	**1700 m**	183 מ' לקומה
—	Cat6 / Cat7 שרשרת LCom ← BoxCom (כתום)	**750 m**	80 מ' לקומה
—	Cat6A / Cat7 עמוד ארונות (אדום)	**130 m**	כולל עמוד

NOTES · הערות

1. כמויות מחושבות מהמודל (קומה טיפוסית × 8 + קרקע).
2. אורכי כבל נמדדו על התוואי המשורטט, + 15%.
3. מחירים: לפי מחירון Advantecnia העדכני.
4. לאמת באתר לפני רכישה.

מגדלי ים התיכון · דיור מוגן
32 דירות · 8 קומות + קרקע – קריאת אחות
מערכת: ACE BG · Advantecnia   הוכן ע"י: Telab International

רשימת חומרים
Bill of materials

SCALE · קנה מידה	DATE · תאריך	REV	גיליון
S/E	**15/10/2026**	**B**	**09**

בסיס: תוכנית האדריכל L5 (מסד זוג / Triplet) · מידות במטרים
פורמט A1 · מהדורה B – על התוכנית האמיתית

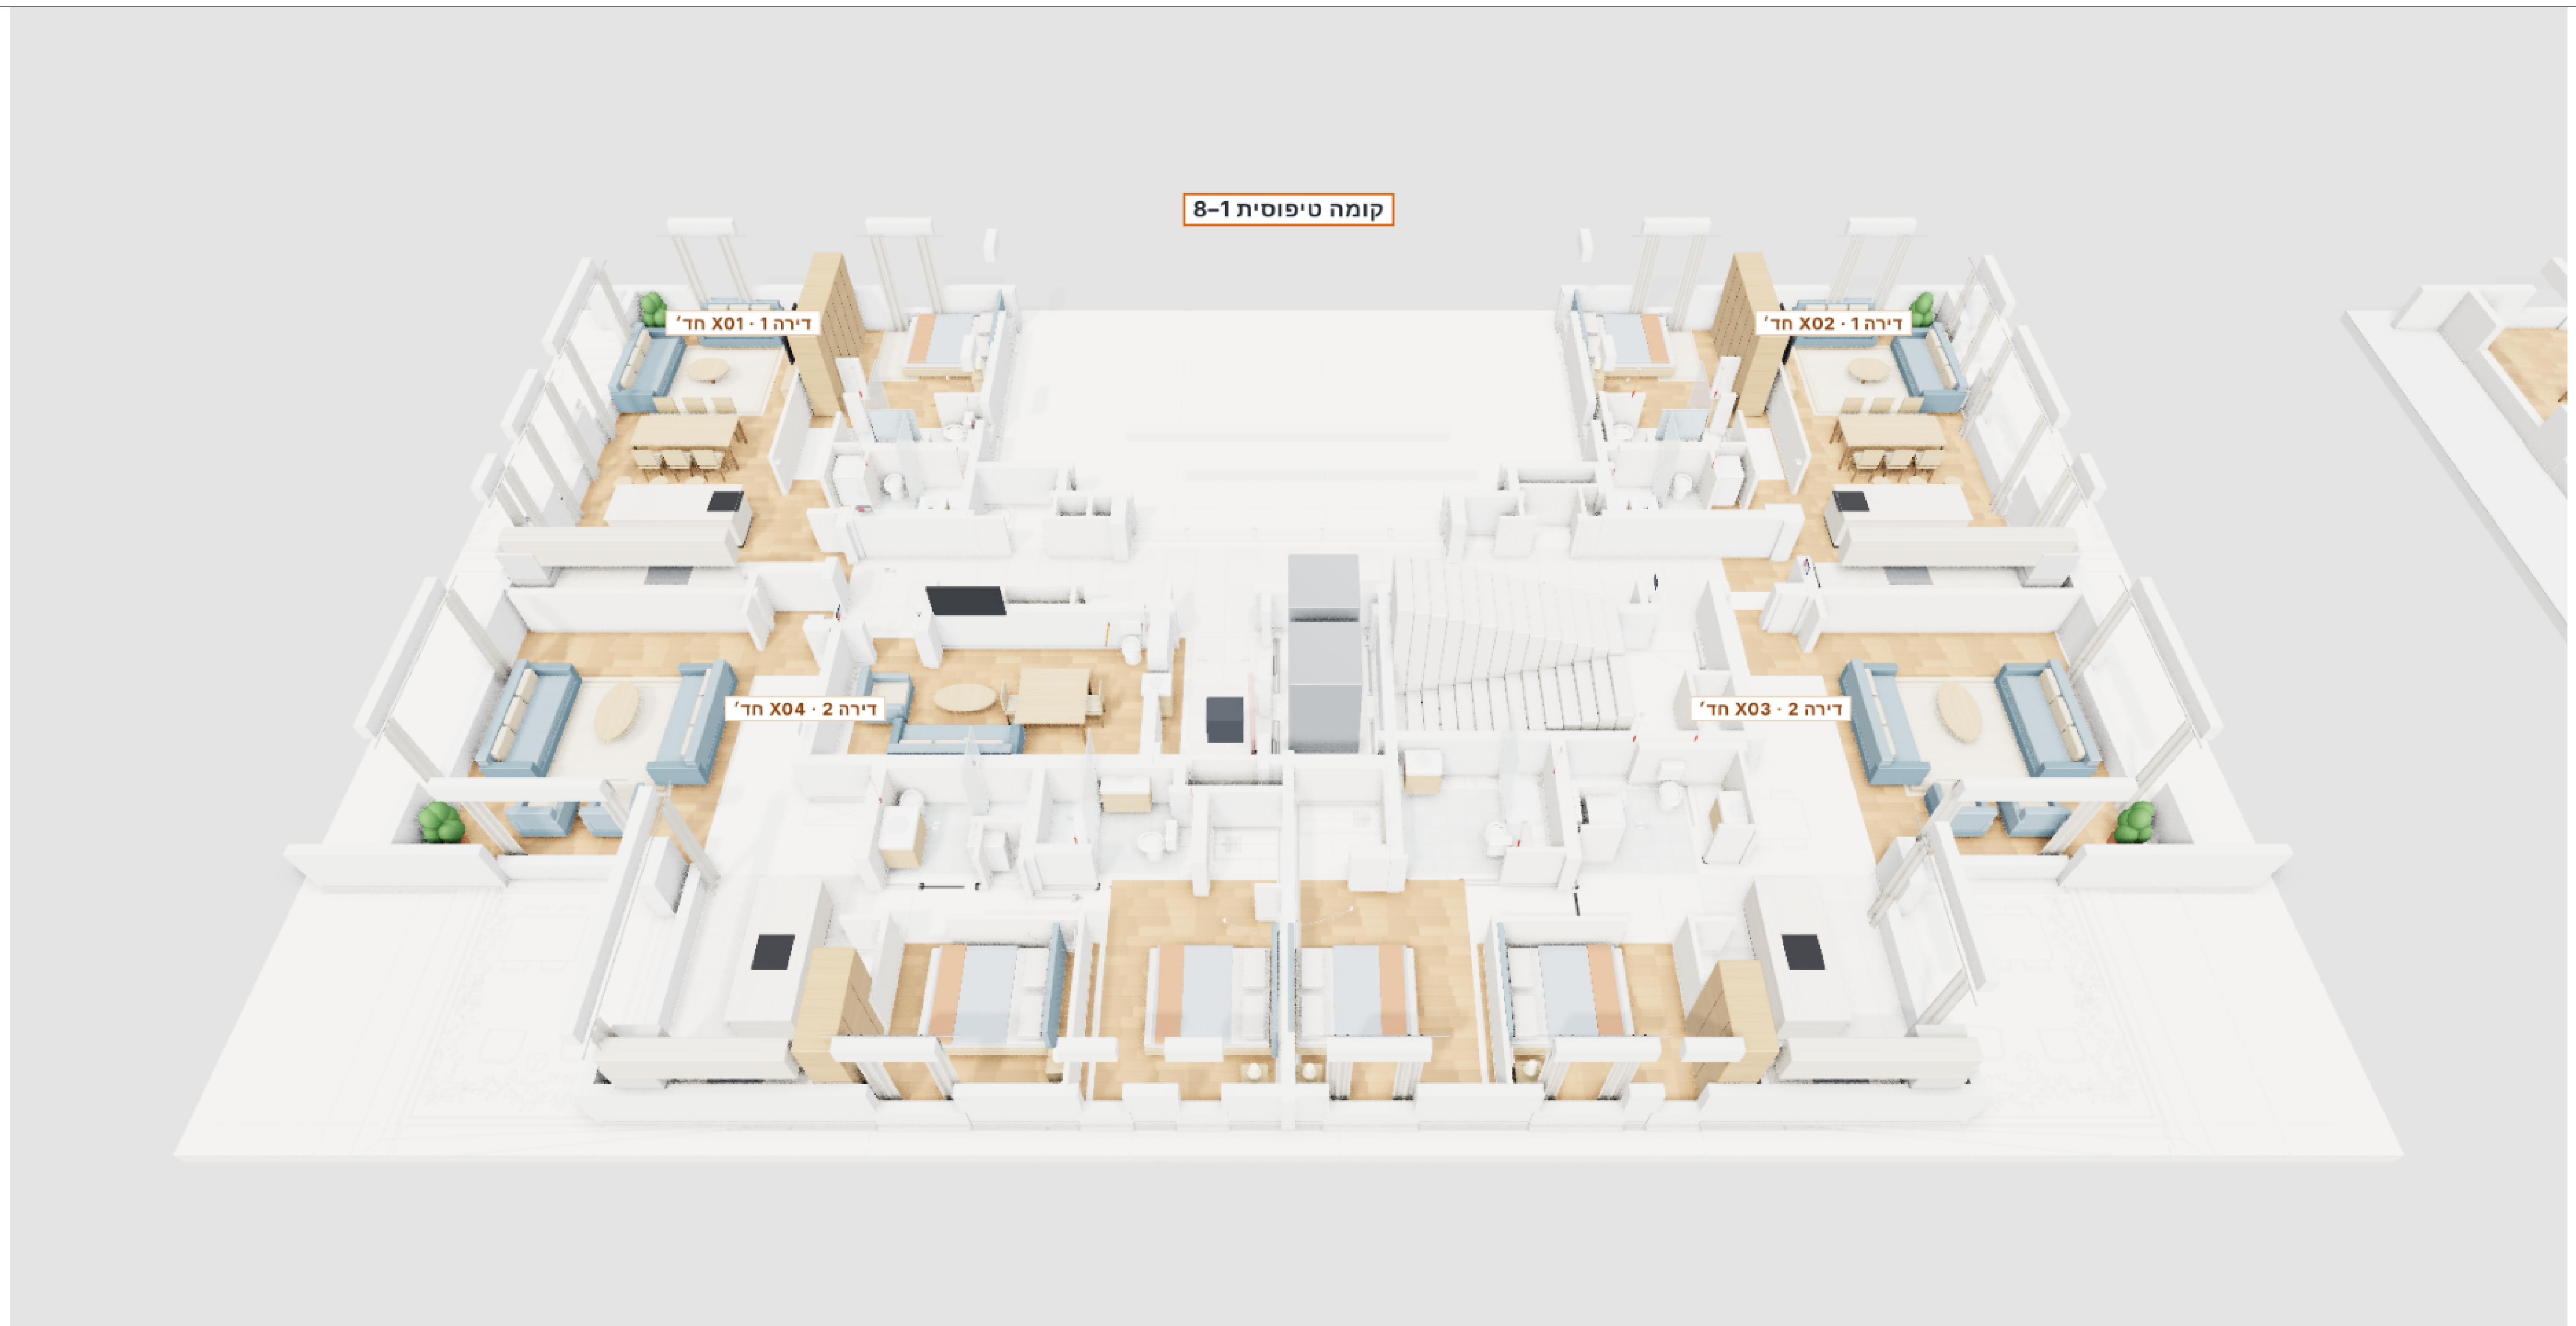
קומה טיפוסית 1–8
דירה 1 · X01 חד׳
דירה 1 · X02 חד׳
דירה 2 · X04 חד׳
דירה 2 · X03 חד׳

א · קומה טיפוסית – 4 דירות

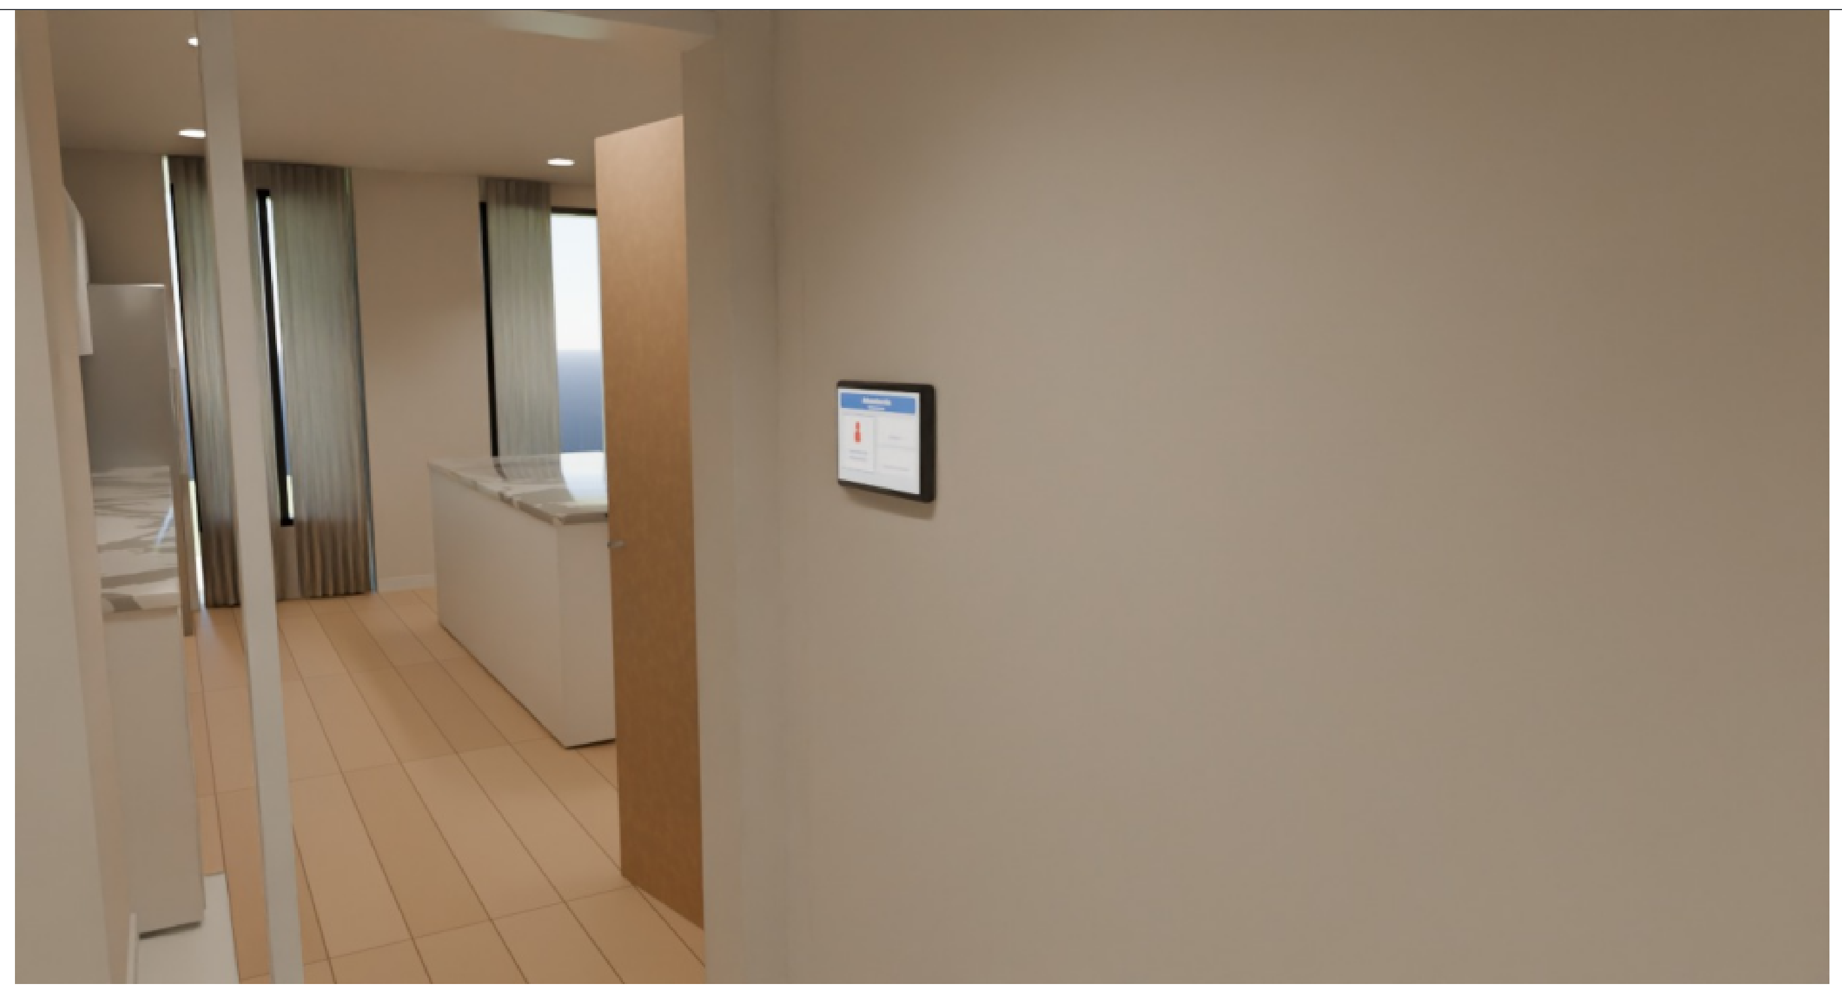

ב · טאבלט בכניסה

ג · חדר שינה – פנל קולי ואגס

ד · חדר רחצה – משיכות חבל באסלה ובמקלחת

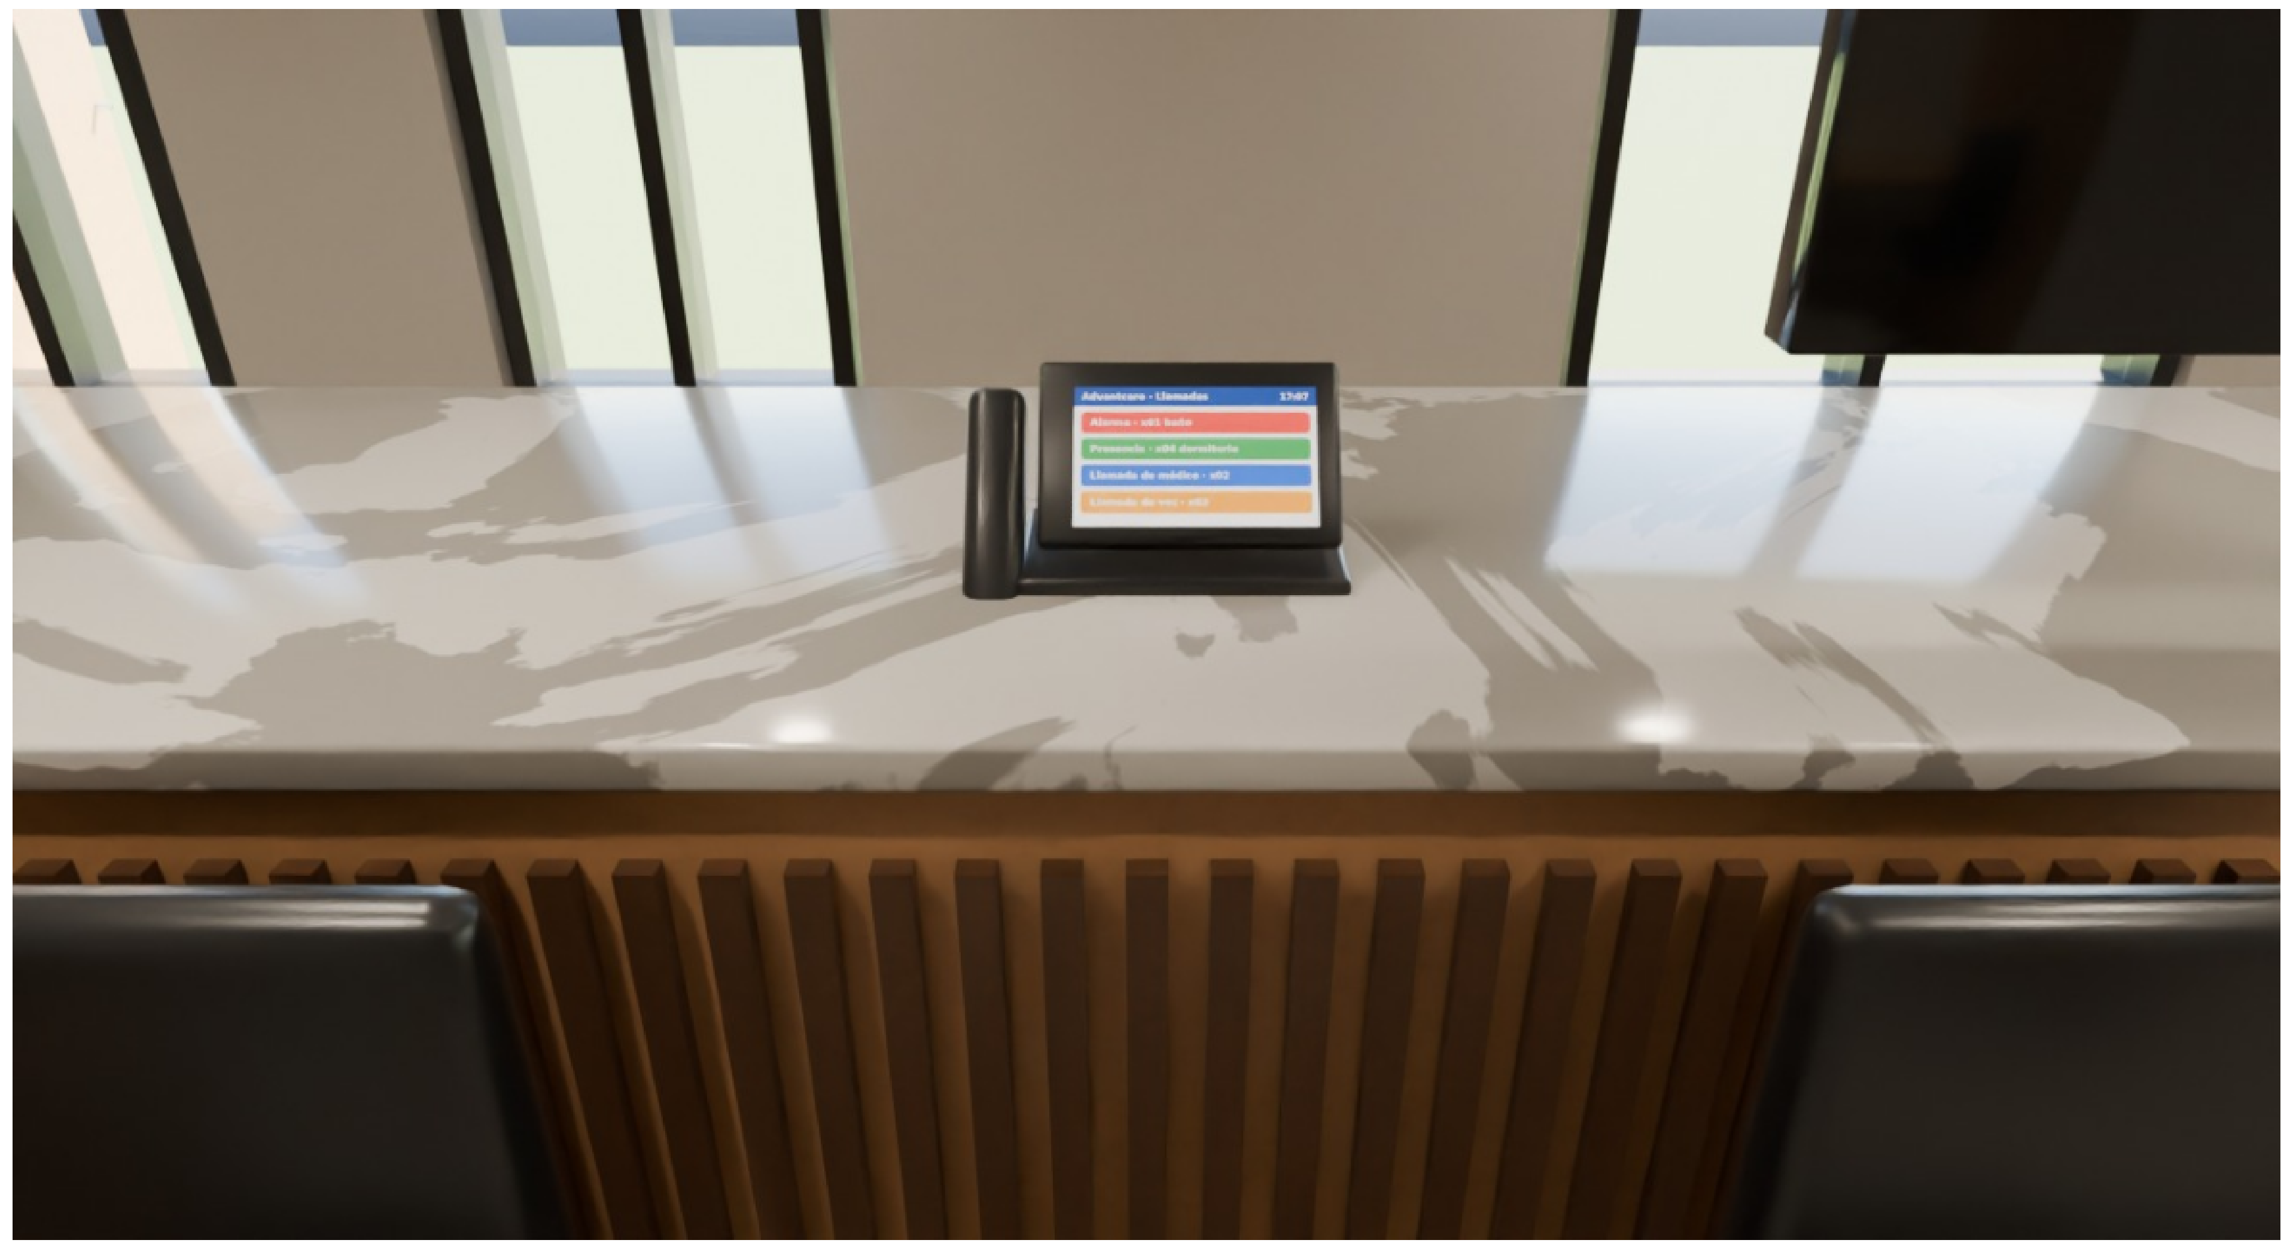
Advantcare · Llamadas
17:07
Alarma · x01 baño
Presencia · x04 dormitorio
Llamada de médico · x02
Llamada de voz · x03

ה · קרקע – עמדת אחות

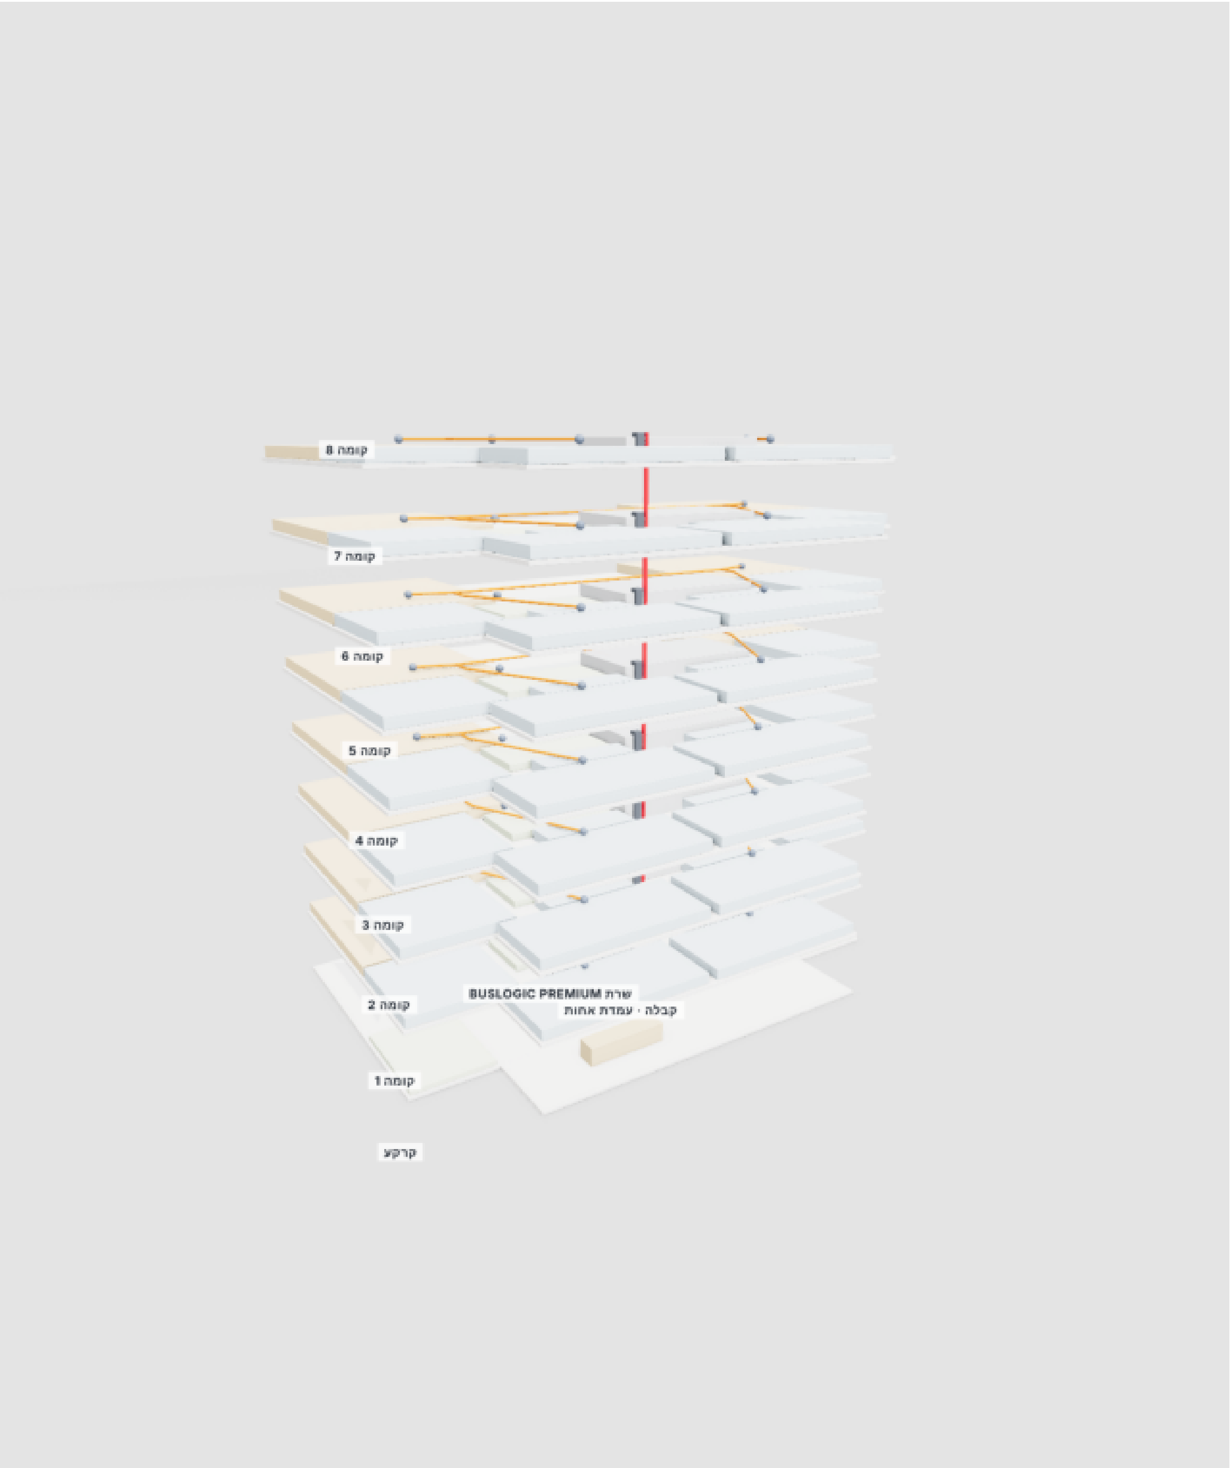
קומה 8
קומה 7
קומה 6
קומה 5
קומה 4
קומה 3
קומה 2
קומה 1
קרקע
שרת BUSLOGIC PREMIUM
קבלה · עמדת אחות

ו · בניין קרקע + 8 קומות

מגדלי ים התיכון · דיור מוגן
קריאת אחות – קרקע + 8 קומות · 32 דירות
הוכן ע"י: Telab International
מערכת: ACE BG · Advantecnia

מבטים תלת-ממדיים

3D views

SCALE · קנה מידה
S/E

DATE · תאריך
15/10/2026

REV
B

גיליון
10

בסיס: תוכנית האדריכל L5 (זוג דסמ / Triplet) · מידות במטרים
פורמט A1 · מהדורה B – על התוכנית האמיתית

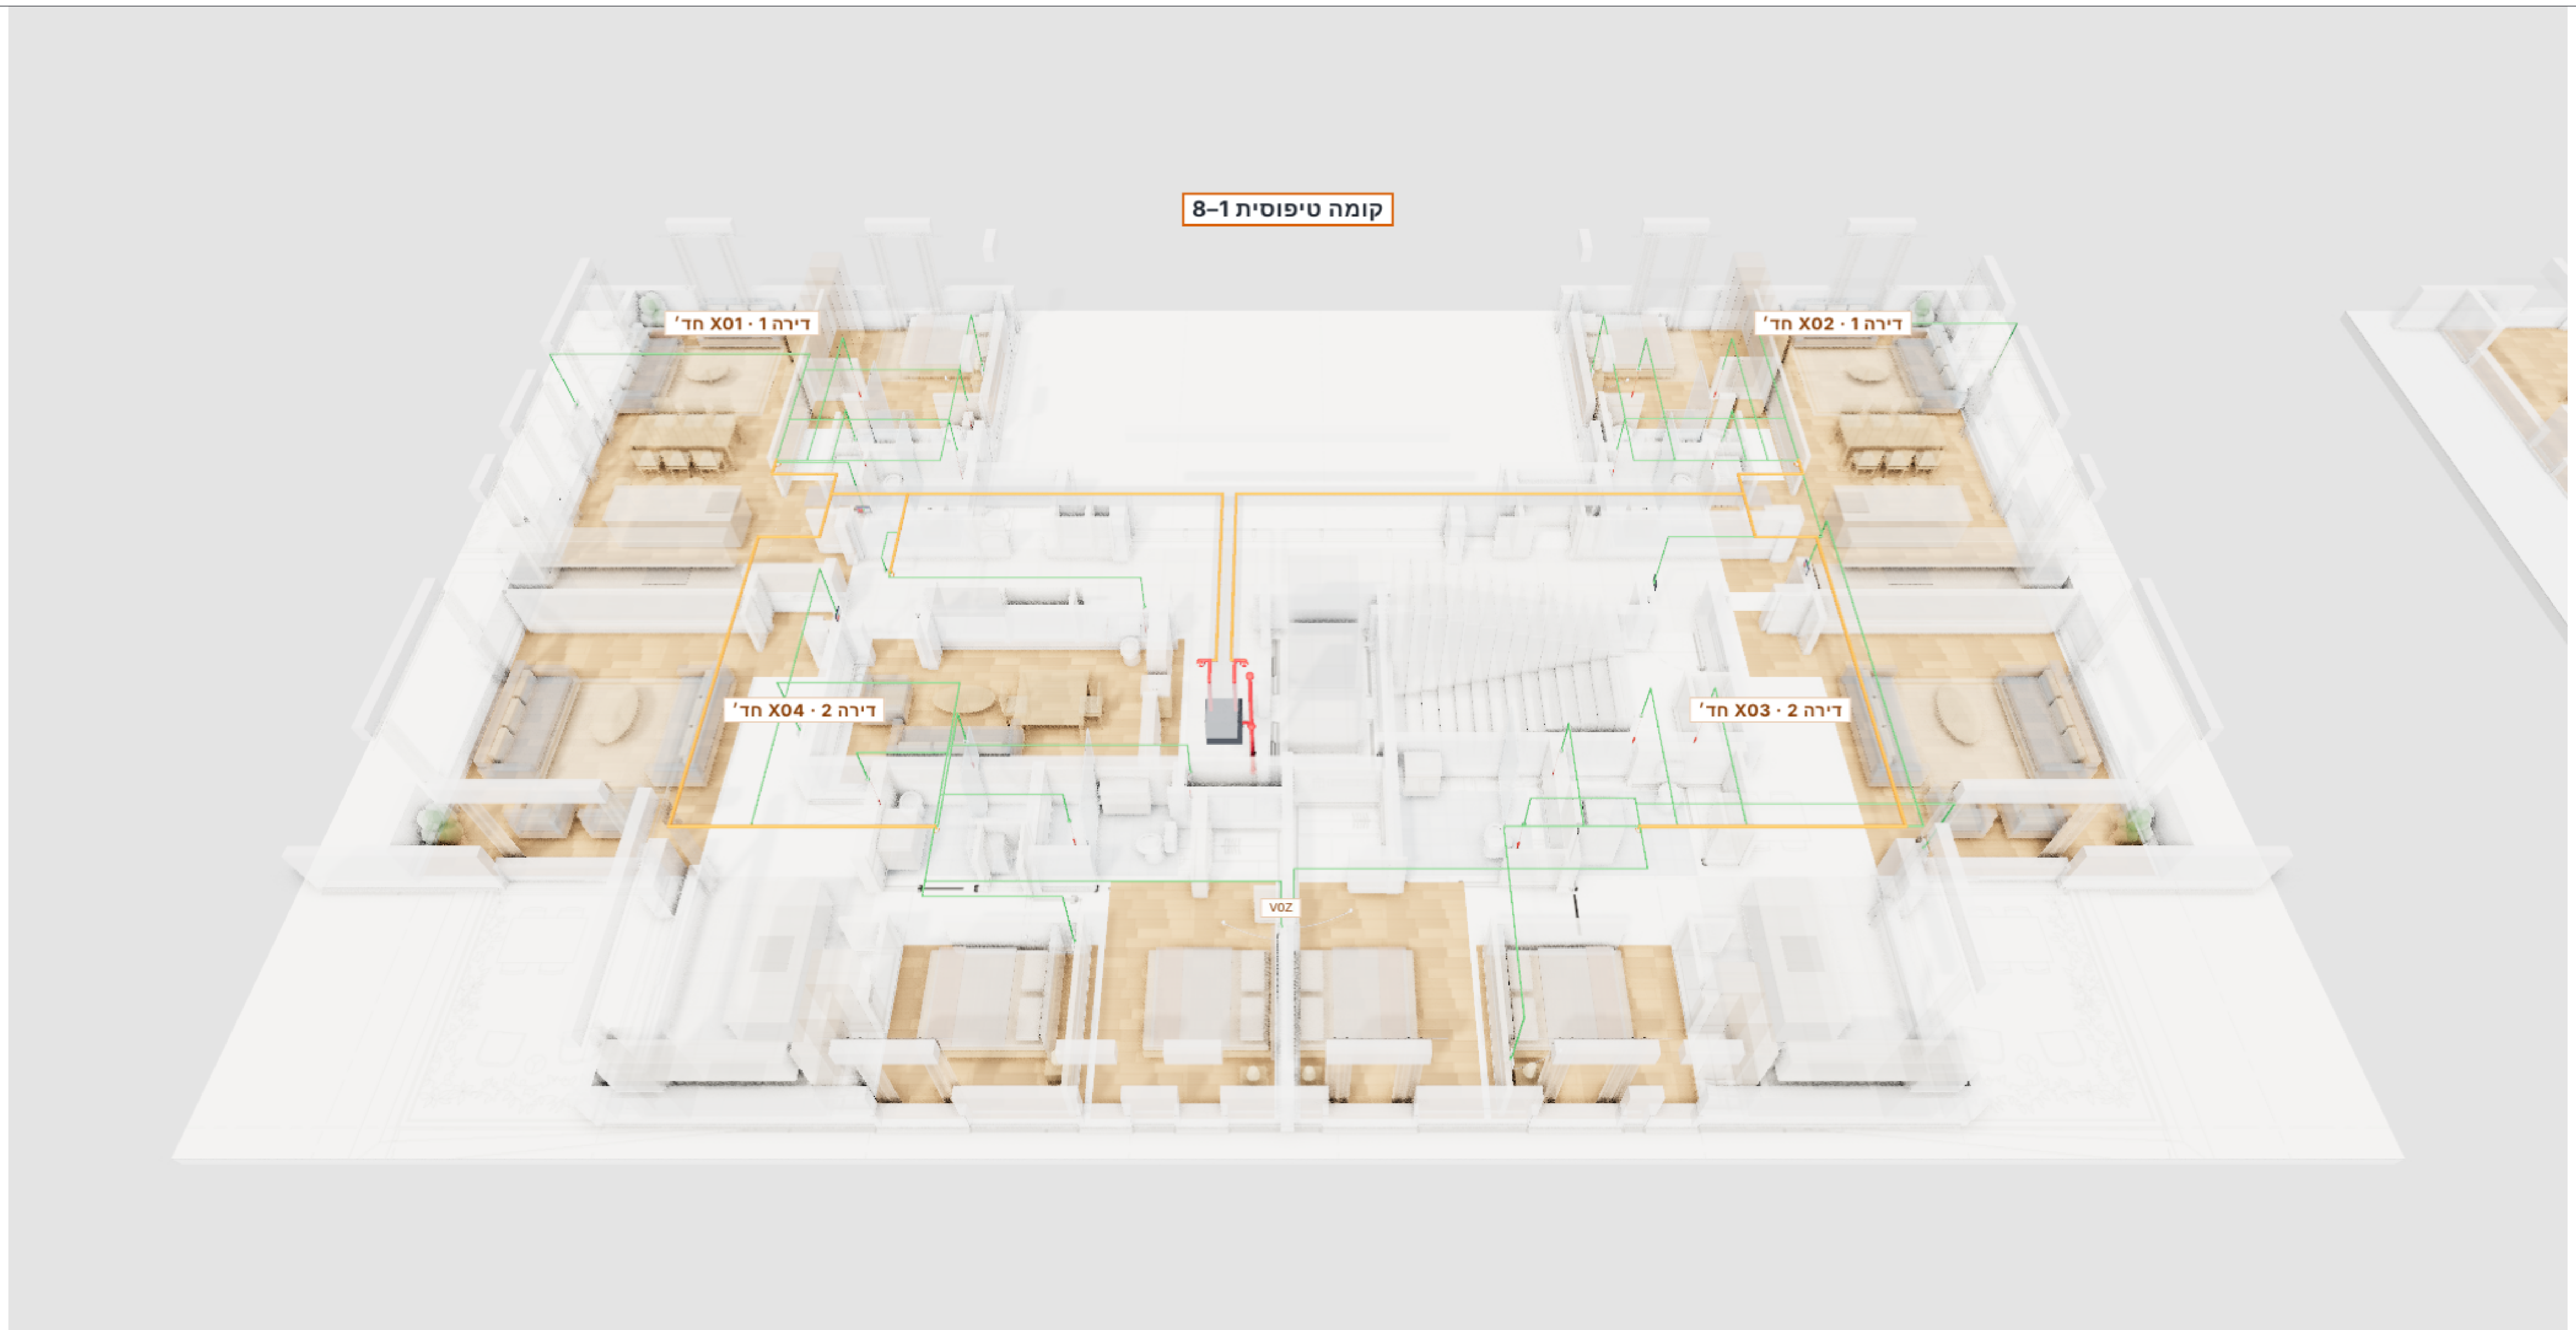

(תשר םודא · LCom תרשרש םותכ · ילאידר קורי) טוויח – תיסופיט המוק · א

COLOURS · COLORES · םיעבצ

🟩 Cat6 ילאידר: לכ ןקתה ← LCom לש הרידה
Cat6 radial: each device → apartment LCom · Cat6 ילאידר: לכ ןקתה ← LCom לש הרידה

🟧 Cat6 / Cat7 תרשרש: LCom ← LCom ← BoxCom הרקתב
Cat6 / Cat7 chain: LCom → LCom → BoxCom · Cat6 / Cat7 תרשרש: LCom ← LCom ← BoxCom

🟥 Cat6A / Cat7 תשר: BoxCom ← גתמ PoE ← דומע ← תרש עקרק
Cat6A / Cat7 network: BoxCom → switch → riser → GF server · Cat6A / Cat7 תשר: BoxCom ← גתמ ← דומע ← תרש

הלבקו יבול – עקרק תמוק · ב

םינצחל םע ילוק לנפ – ןולס · ג

ןגומ רויד · ןוכיתה םי ילדגמ
תוריד 32 · תומוק 8 + עקרק – תוחא תאירק
Telab International :ץעויי ןכוה"י ACE BG · Advantecnia :תכרעמ

טוויח – םיידממ-תלת םיטבמ
3D views – wiring

SCALE · הדימ הנק
S/E
DATE · ךיראת
15/10/2026
REV
B
ןוילג
11

סיסב: תונכות הארדיכל L5 (זוע דסמ / Triplet) · םירטמב תודימ
טמרופ A1 · הרודהמ B – לע התוכנות תואמיתי

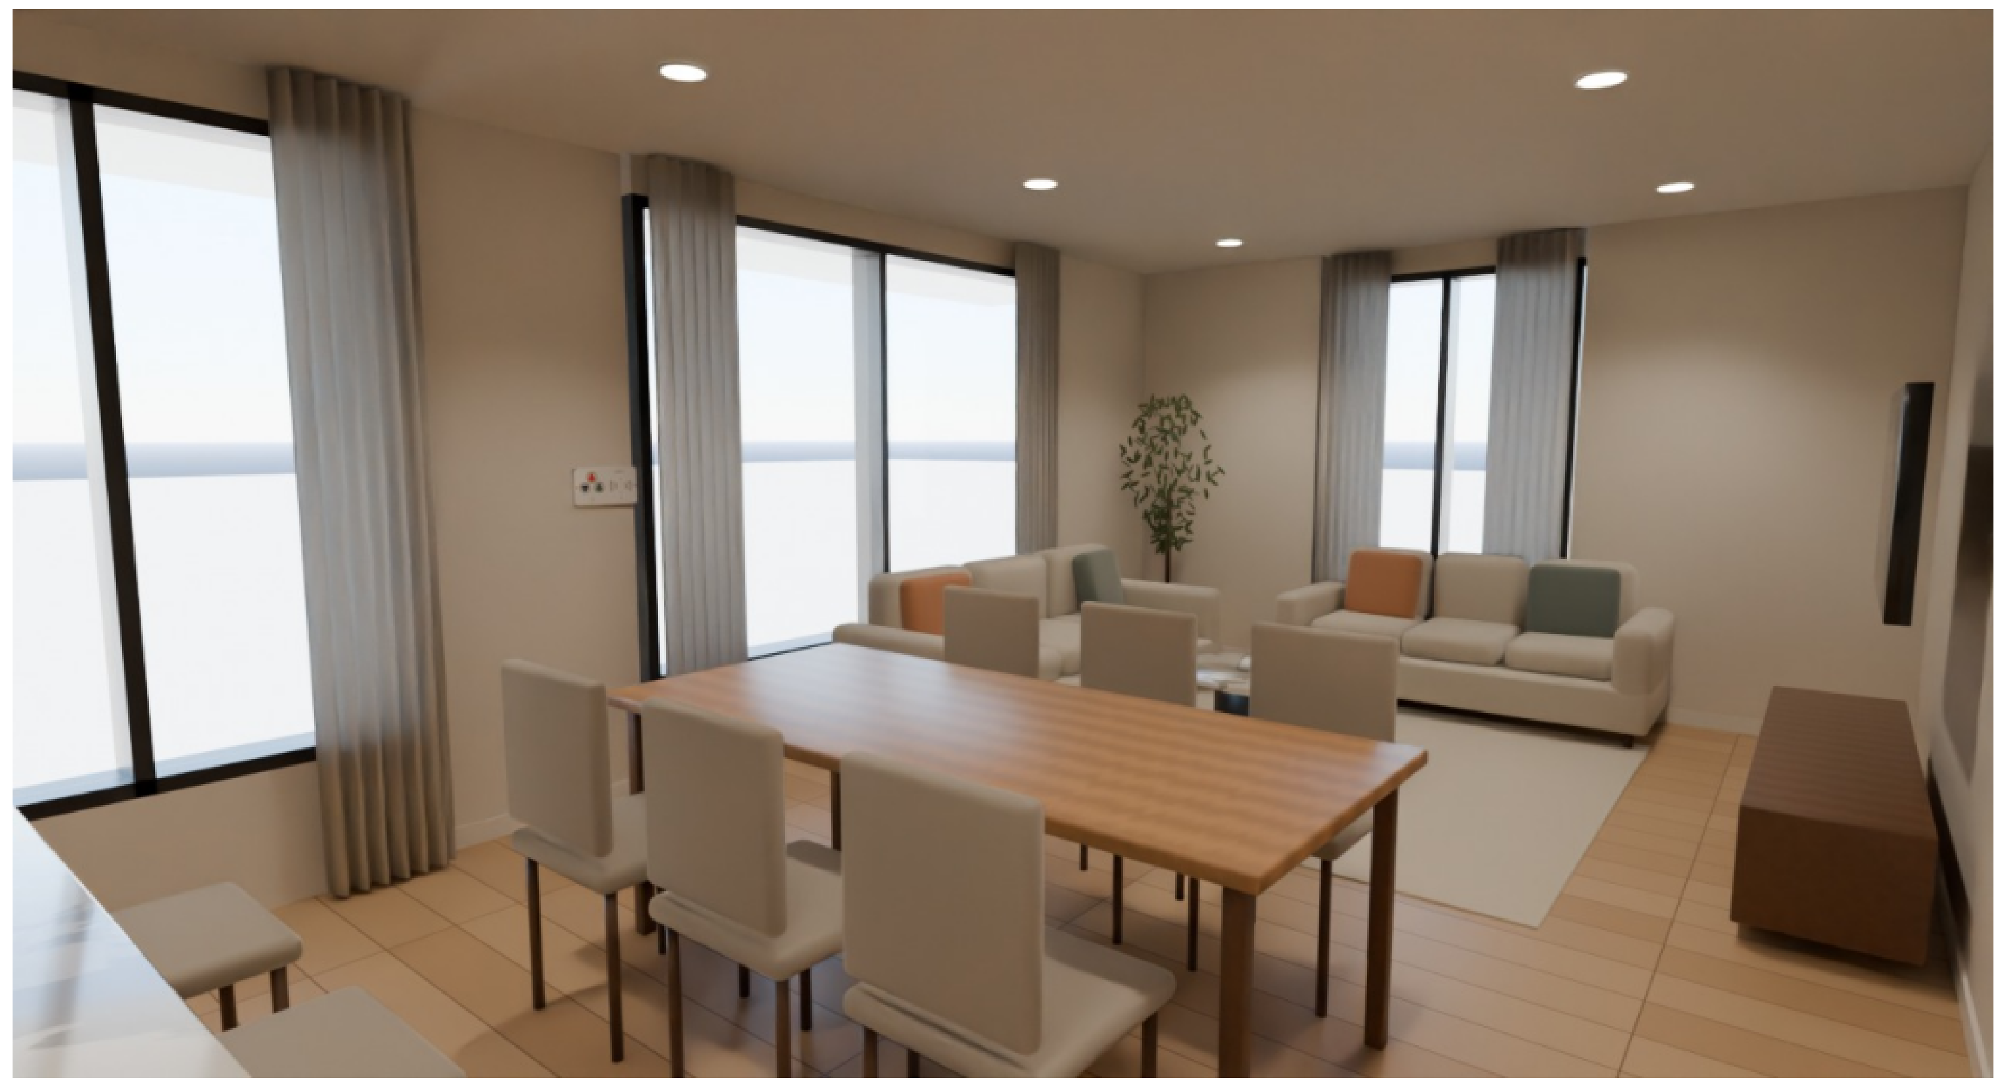
ילוק האירק לנפ – ןולס · א

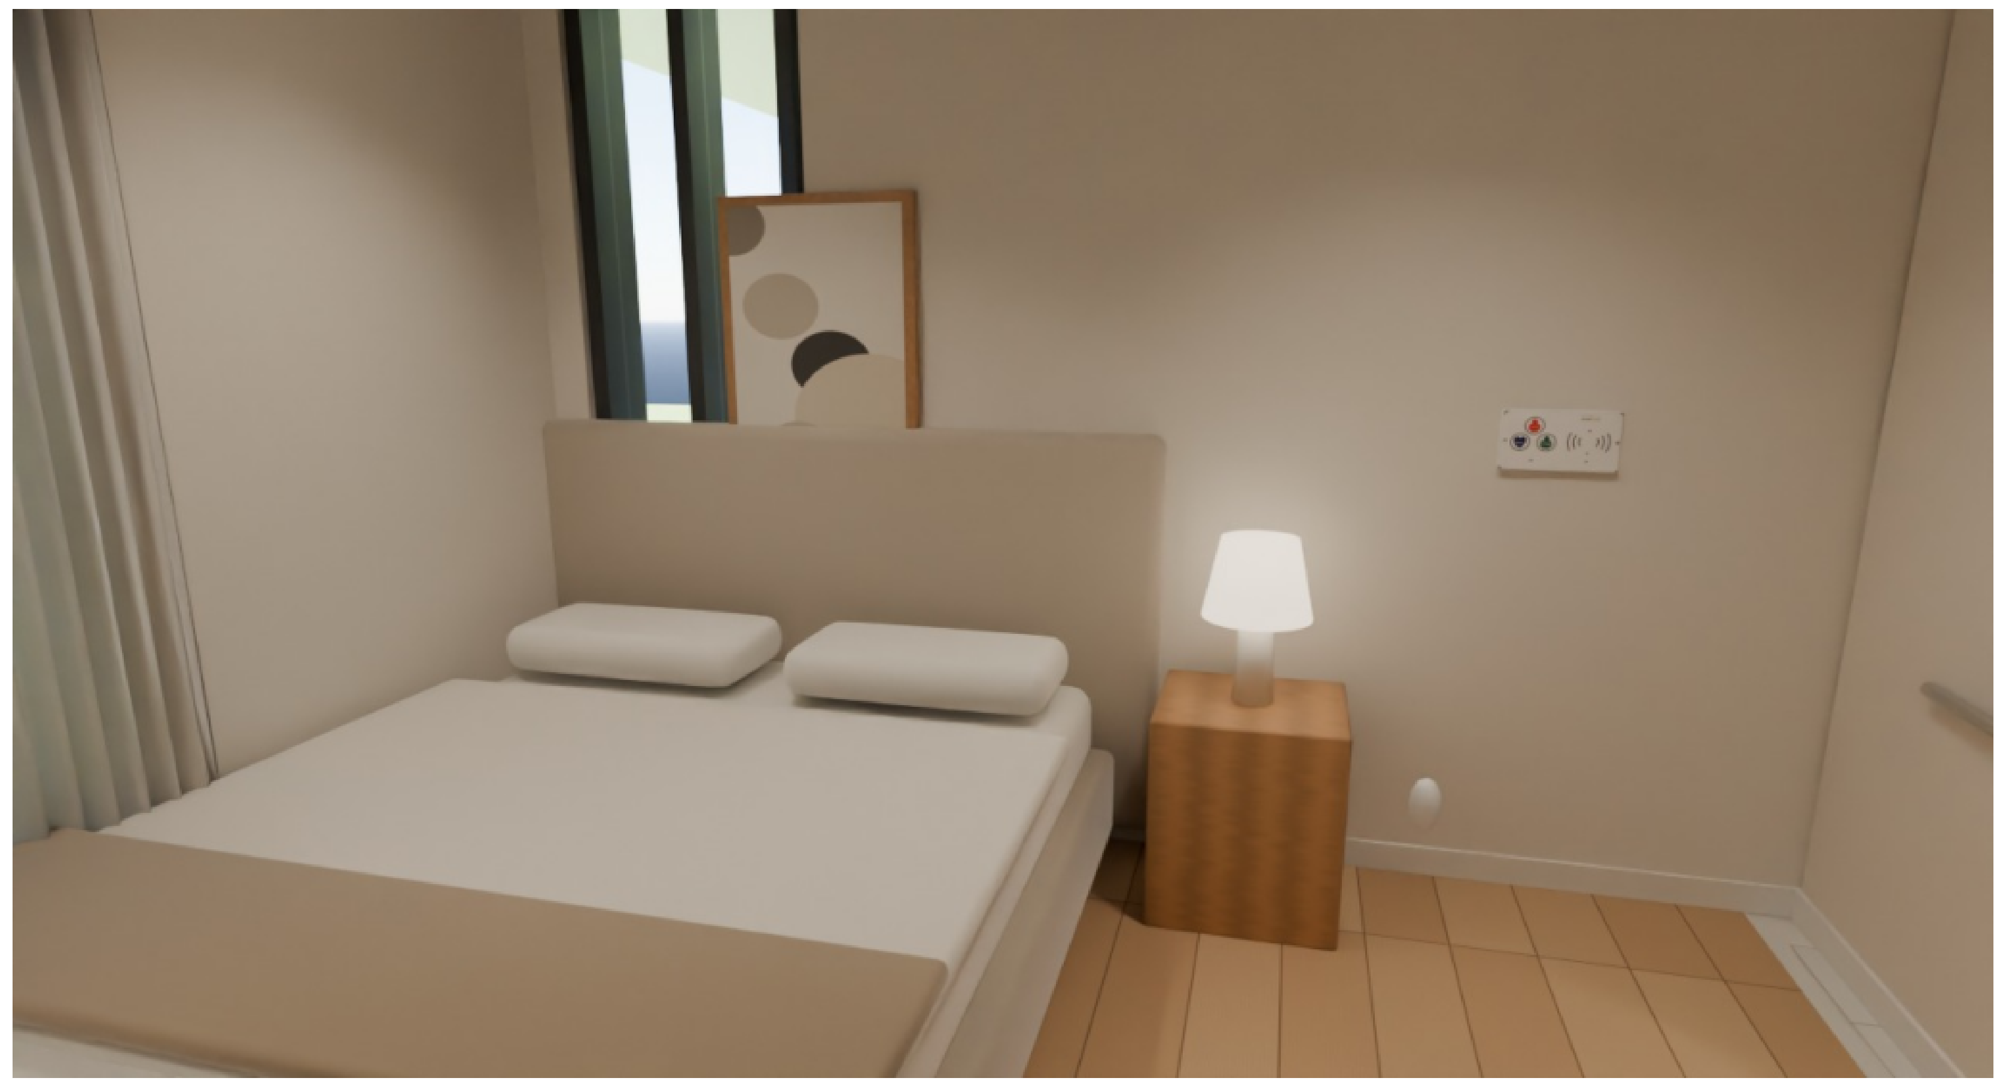
סגאו ילוק לנפ – הניש רדח · ב

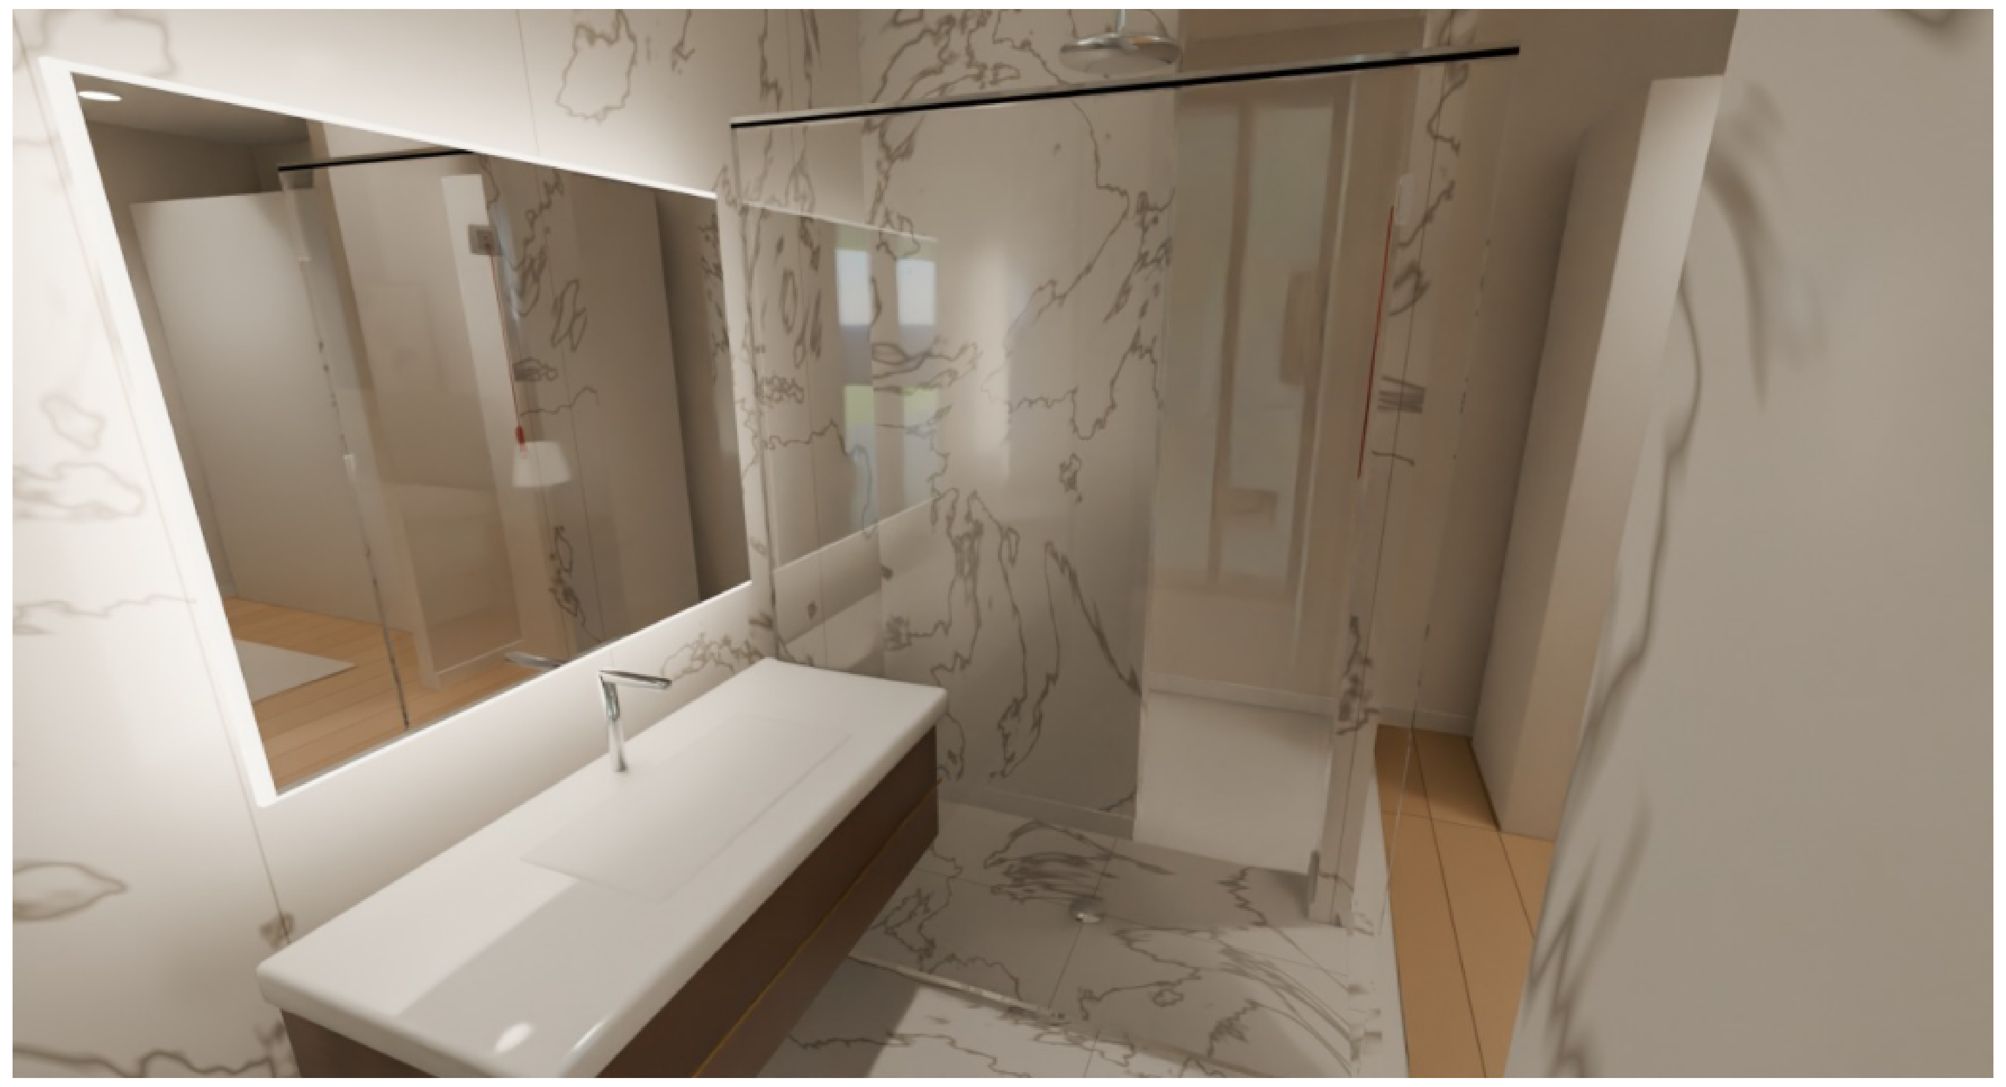
SOS תכישמ – הצחר רדח · ג

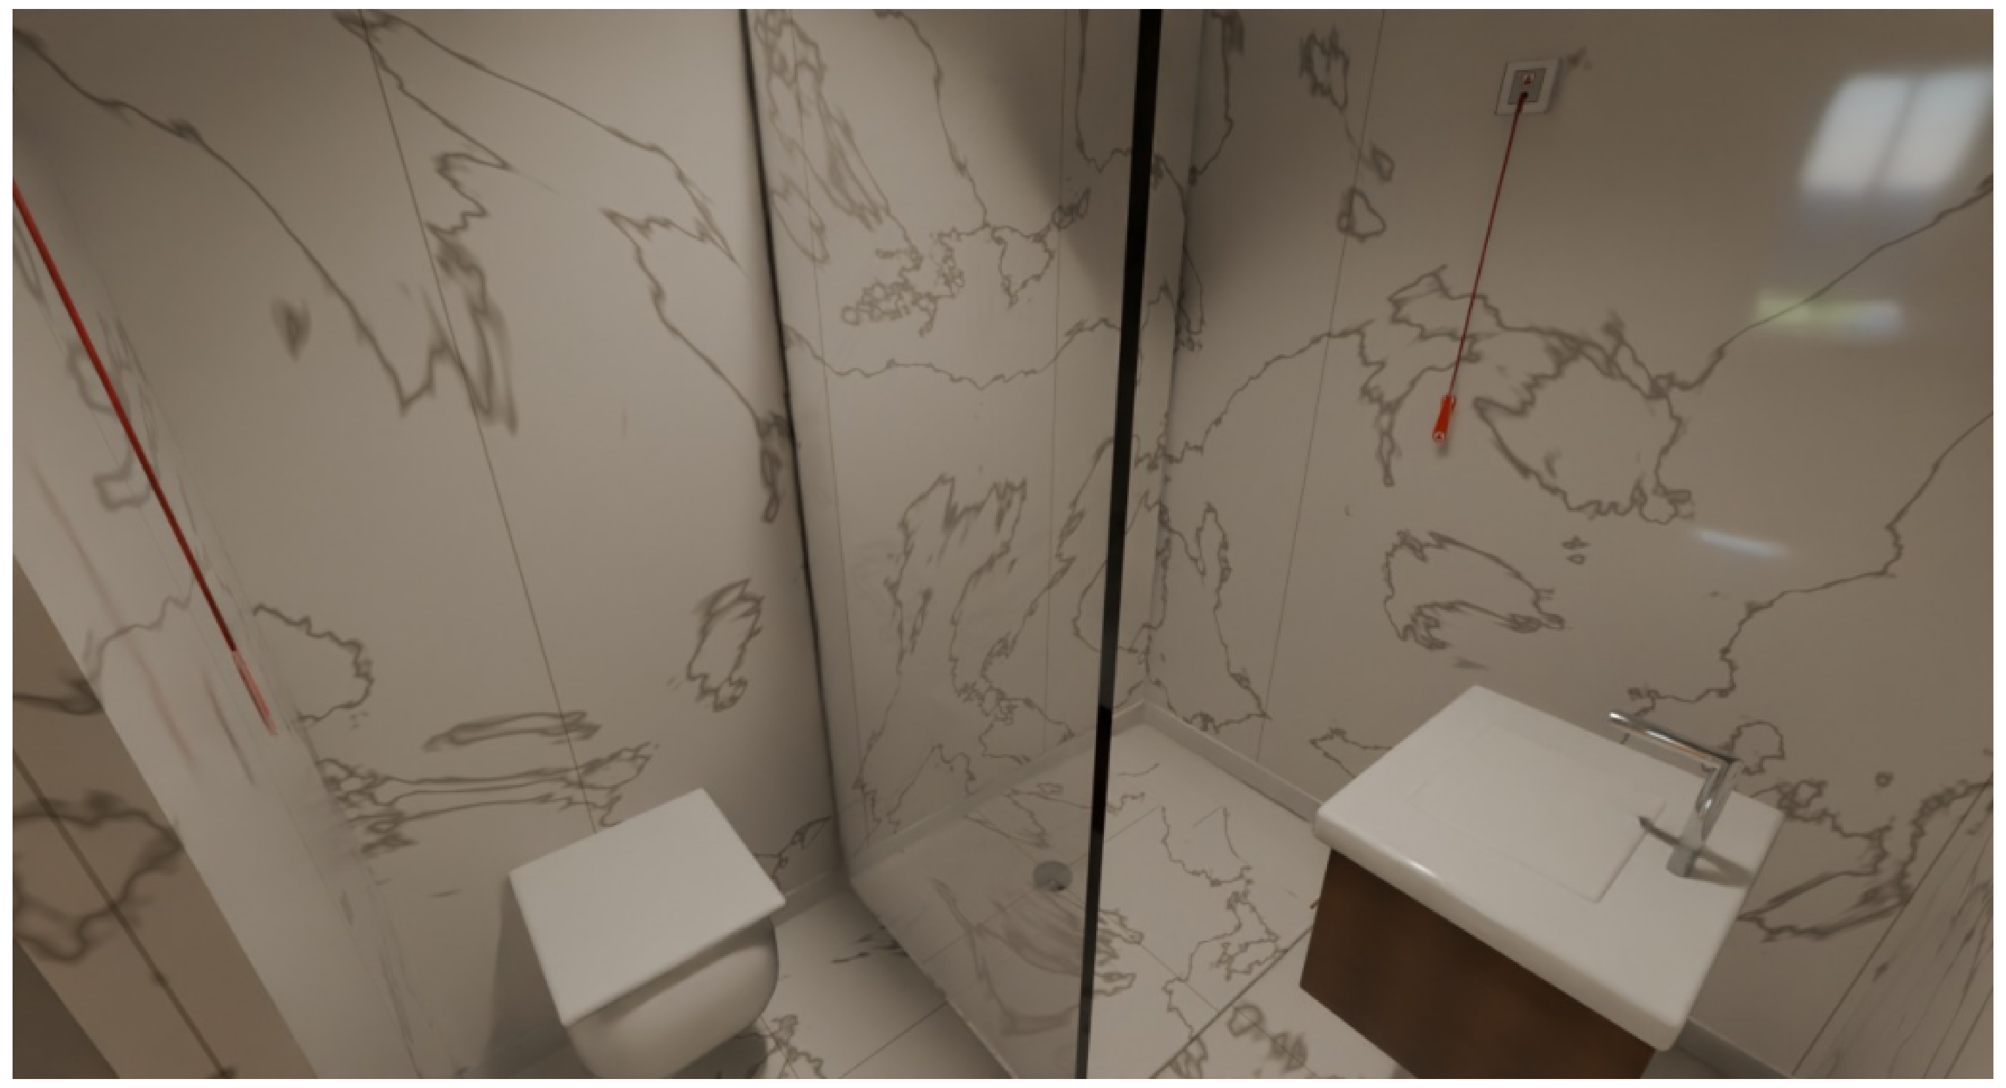
תחלקמבו הלסאב הכישמ – 2 הצחר רדח · ד

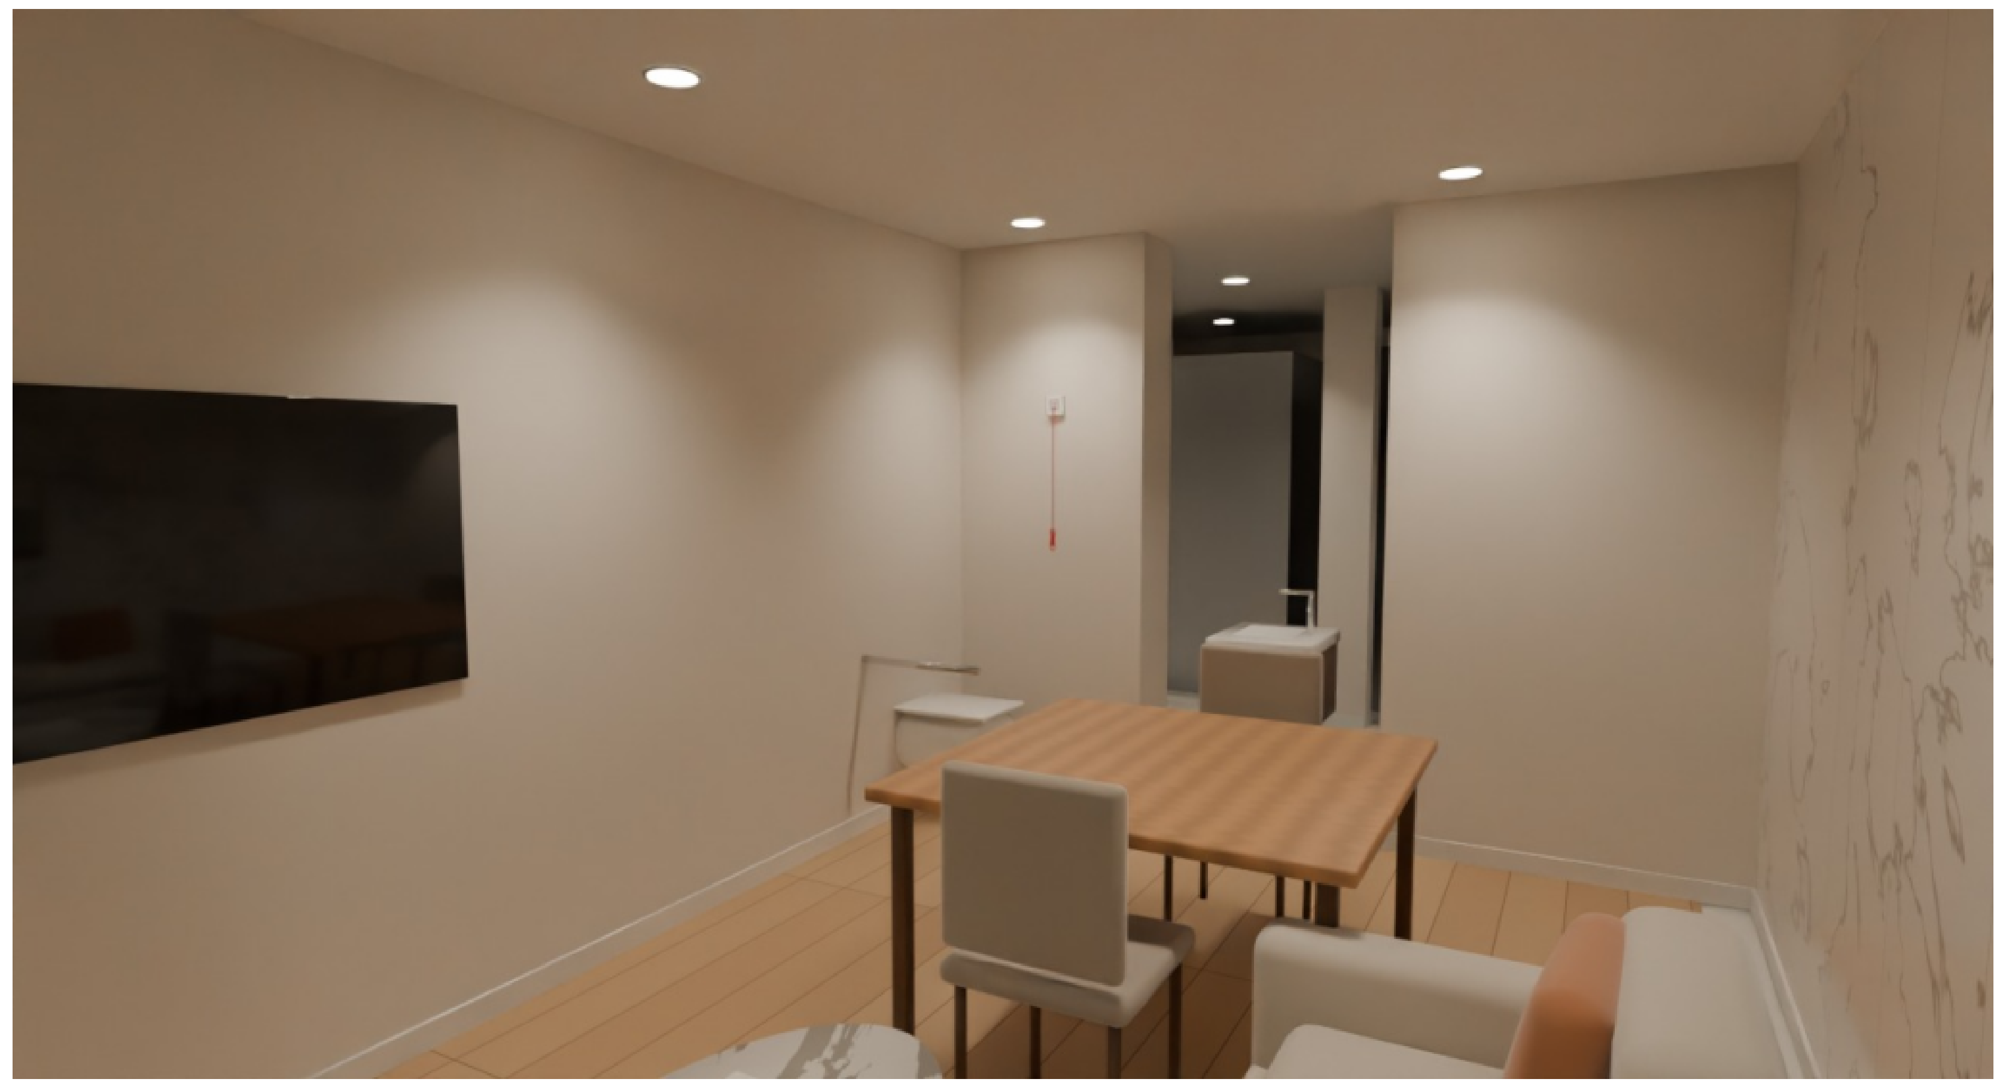
םיירוביצ םיתוריש – ךתושמ רדח · ה

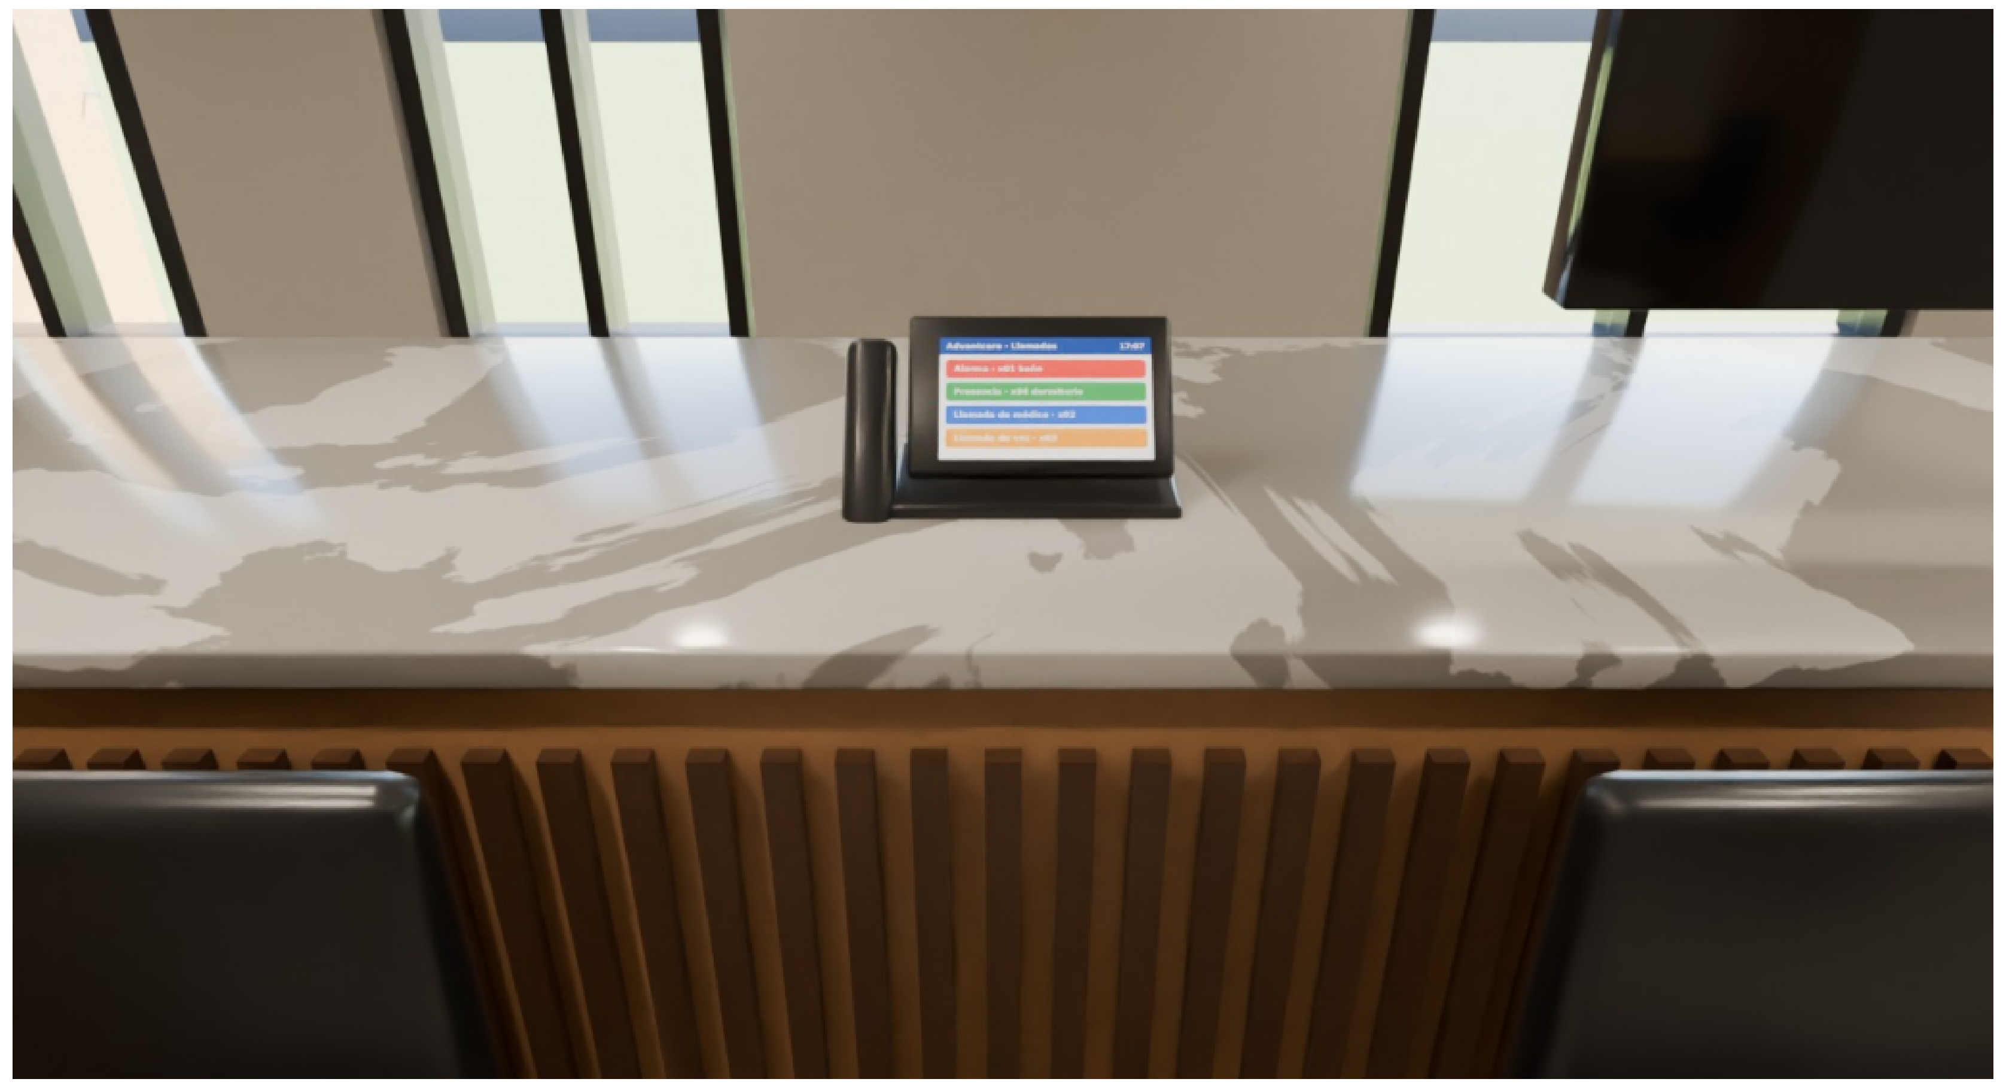
Grandstream ןופלט – תוחא תדמע · ו

ןגומ רויד · ןוכיתה םי ילדגמ
תוריד 32 · תומוק 8 + עקרק – תוחא תאירק
Telab International :ץוי"ע ןכוה   ACE BG · Advantecnia :תכרעמ

םייטסילאירוטופ םירודניר
Photorealistic renders

SCALE · הדימ הנק	DATE · ךיראת	REV	ןוילג
S/E	**15/10/2026**	**B**	**12**

סיסב: תוניכת האדירכל L5 (זוע דסמ / Triplet) · םירטמב תודימ
טמרופ A1 · הרודהמ B – לע התונכת האמיתית