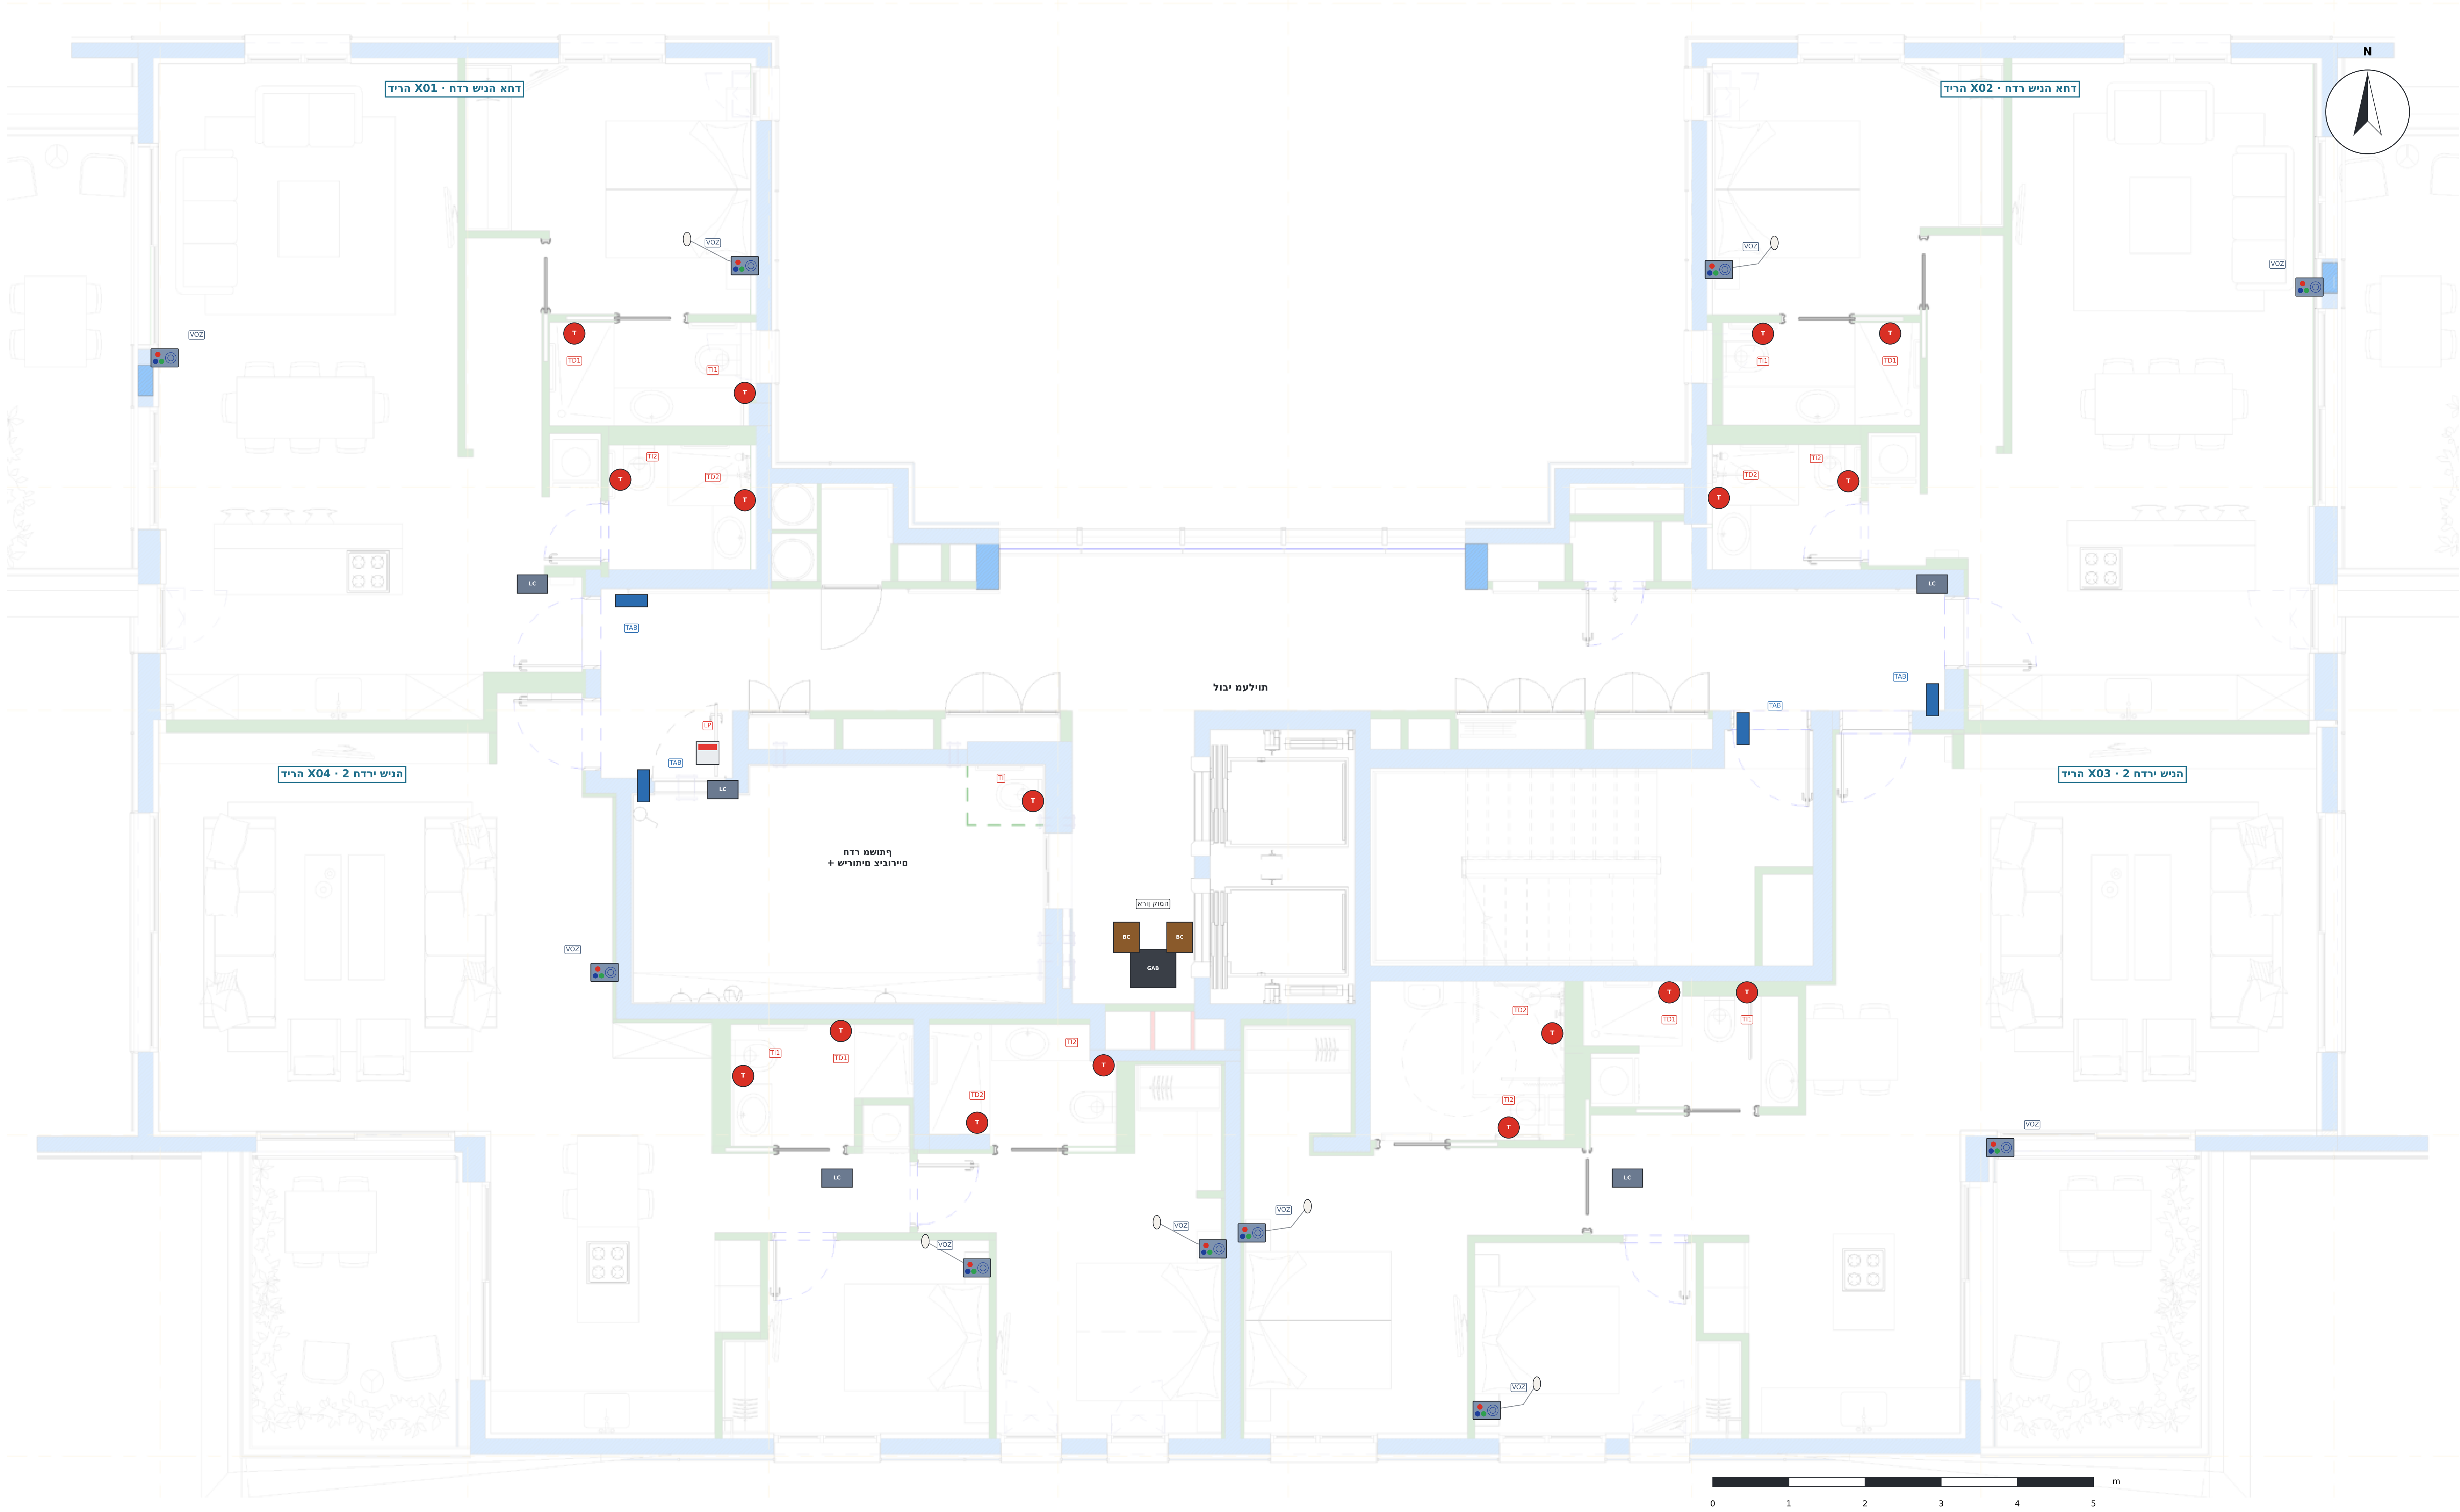

DEVICES · EQUIPOS · ציוד

🟦	TAB · טאבלט בכניסה (iPad / אנדרואיד) – קריאה ודיבור, גובה 1.40 מ' Door tablet – call and voice · קריאה ודיבור – טאבלט בכניסה
▨	VOZ · פנל קולי עם לחצנים ACE82182451 – סלון וחדרי שינה, גובה 1.20–1.30 מ' Voice panel with buttons – living room and bedrooms · סלון וחדרי שינה – פנל קולי עם לחצנים
○	אגס קריאה ליד המיטה (בחדרי השינה) Call pear next to the bed (bedrooms) · אגס קריאה ליד המיטה
T	TI / TD · משיכת חבל ACE40320303W – אסלה ומקלחת, גובה 1.85 מ' Pull-cord – toilet and shower, h 1.85 m · משיכת חבל – אסלה ומקלחת, גובה 1.85 מ'
🟥	LP · מנורת מסדרון ACE41020309 – מעל דלת כל שירותים ציבוריים Corridor light – above each public toilet door · מנורת מסדרון – מעל דלת כל שירותים ציבוריים
LC	LC · LCom ACE71610003 – מרכז הדירה (תקרה) LCom – apartment hub (ceiling) · LCom – מרכז הדירה (תקרה)
BC	BC · BoxCom ACE70810000 – מרכז באס לכמה דירות (תקרה) BoxCom – bus hub for several apartments (ceiling) · BoxCom – מרכז באס לכמה דירות (תקרה)
GAB	ארון קומה: מתג PoE D-Link DES-1210-28P (24 יציאות PoE, 12U) Floor rack: D-Link DES-1210-28P PoE switch · ארון קומה: מתג PoE D-Link DES-1210-28P

כמויות לקומה × 8 קומות

קוד	התקן	לקומה	8 קומות
TAB	טאבלט בכניסה	4	32
VOZ	פנל קולי עם לחצנים	10	80
TI/TD	משיכת חבל (אסלה + מקלחת)	17	136
LP	מנורת מסדרון (שירותים ציבוריים)	1	8
LC	LCom	5	40
BC	BoxCom	2	16
SW	מתג PoE	1	8

NOTES · הערות

1. בסיס: תוכנית אדריכלית L5 (קומה טיפוסית) – 8 קומות זהות: 4 דירות בקומה, 32 בסך הכול.
2. דירות x01 ו-x02: חדר שינה אחד, סלון עם מטבח ו-2 חדרי רחצה. דירות x03 ו-x04: 2 חדרי שינה ו-2 חדרי רחצה.
3. טאבלט בכניסה לכל דירה (iPad / אנדרואיד) לקריאה ודיבור עם האחות.
4. פנל קולי עם לחצנים (ACE82182451) בסלון ובכל חדר שינה; בחדר השינה עם אגס ליד המיטה.
5. משיכת חבל (ACE40320303W) באסלה ובמקלחת בכל חדר רחצה, בגובה 1.85 מ'.
6. שירותים ציבוריים בכל קומה בחדר המשותף: משיכת חבל + מנורת מסדרון מעל הדלת. עם 2 בקרקע – 10 שירותים ציבוריים.
7. ארון קומה ליד המעליות עם מתג PoE D-Link DES-1210-28P; 2 ה-BoxCom בתקרה לידו.
8. מיקומים לפי סימוני הלקוח בתוכנית L2 (nt = פנל קולי, tab = טאבלט): ראו גיליון 03.

גובהי התקנה

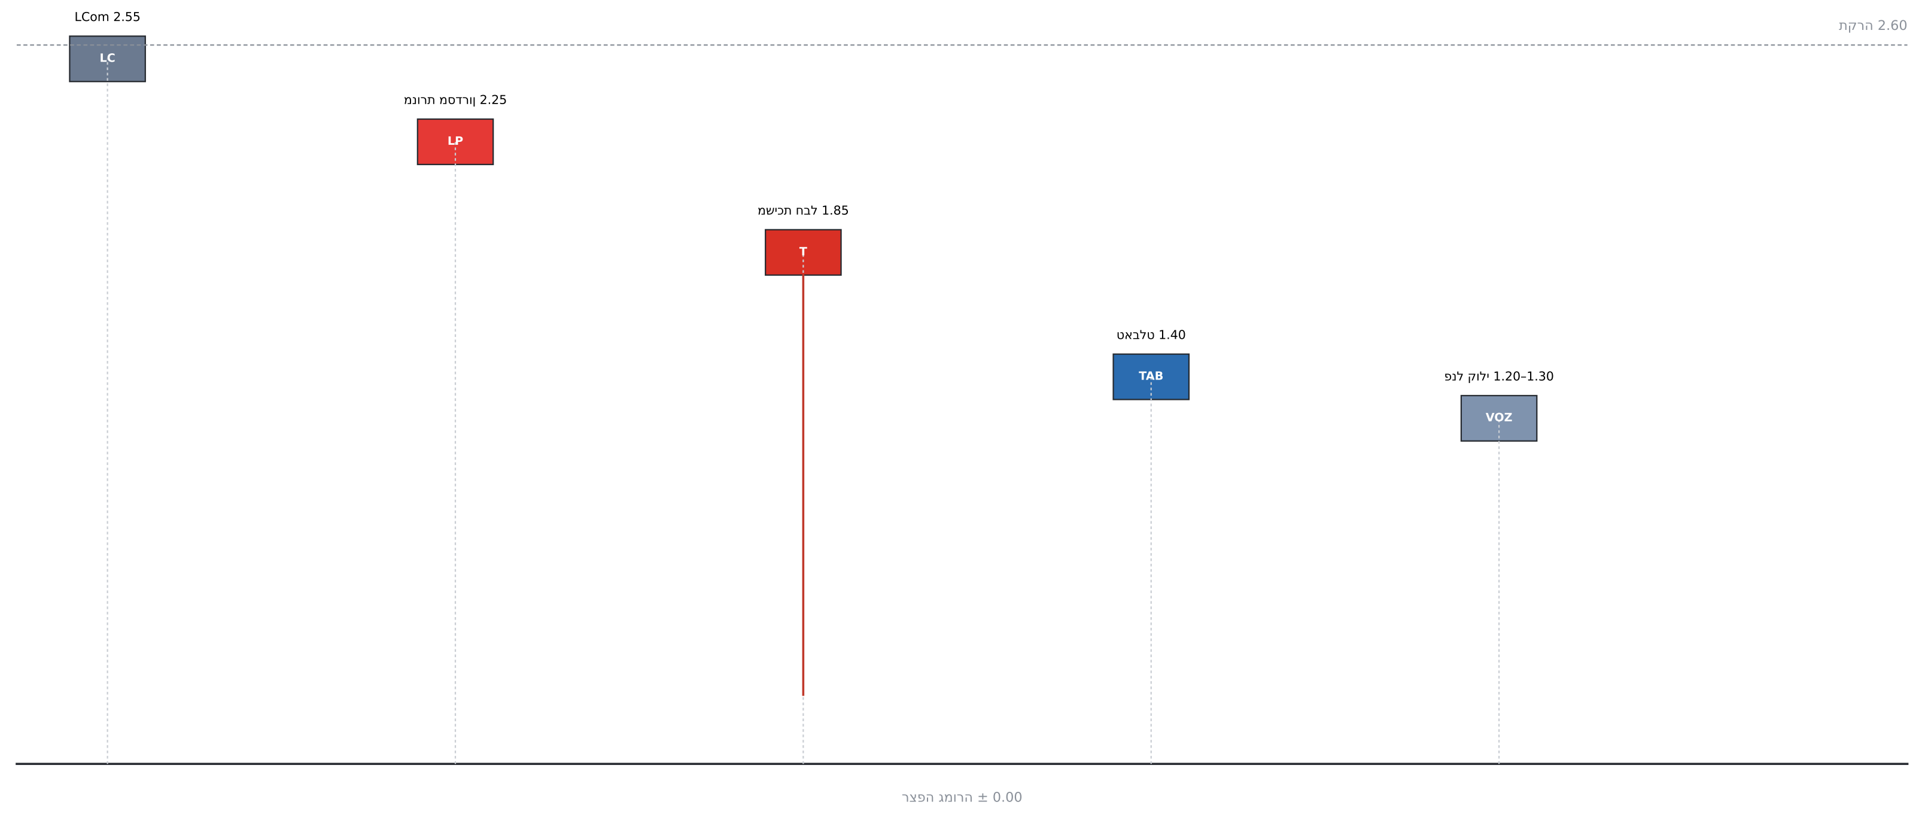

משיכת חבל

טאבלט בכניסה (iPad / אנדרואיד)

מנורת מסדרון

פנל קולי עם לחצנים

מגדלי ים התיכון · דיור מוגן
קריאת אחות – קרקע + 8 קומות · 32 דירות
הוכן ע"י: Telab International   מערכת: ACE BG · Advantecnia

קריאת אחות · קומה טיפוסית 1–8

Typical floor F1–F8 · nurse call

SCALE · קנה מידה	DATE · תאריך	REV	גיליון
1:60	15/10/2026	B	01

בסיס: תוכנית האדריכל L5 (מסד עוז / Triplet) · מידות במטרים
פורמט A1 · מהדורה B – על התוכנית האמיתית

שירותים קריאת אחות

לבח תכישמ

דוק	**ACE40320303W**
םוקימ	םיירוביצה םיתורישה 10-בו הצחר רדח לכב תחלקמו הלסא
הבוג	**1.85 מ'**
תומכ	**138**

1

טבלט אנדרואיד קריאת אחות

הסינכב טלבאט (iPad / דיאורדנא)

דוק	**Advantecnia TV**
םוקימ	הריד לכ תלד דיל ,יבולב
הבוג	**1.40 מ'**
תומכ	**32**

2

מנורה קריאת אחות

ןורדסמ תרונמ

דוק	**ACE41020309**
םוקימ	םיירוביצ םיתוריש לכ תלד לעמ
הבוג	**2.25 מ'**
תומכ	**10**

3

פנל קריאת אחות

םינצחל םע ילוק לנפ

דוק	**ACE82182451**
םוקימ	הניש רדח לכו ןולס (הנישה רדחב םע סגא)
הבוג	**1.20–1.30 מ'**
תומכ	**80**

4

ןופלט הדמעה (דיאורדנא)

דוק	**Grandstream**
םוקימ	עקרקב תוחא תדמע · PoE גתמל תורישי
הבוג	**הדמעה לע**
תומכ	**1**

5

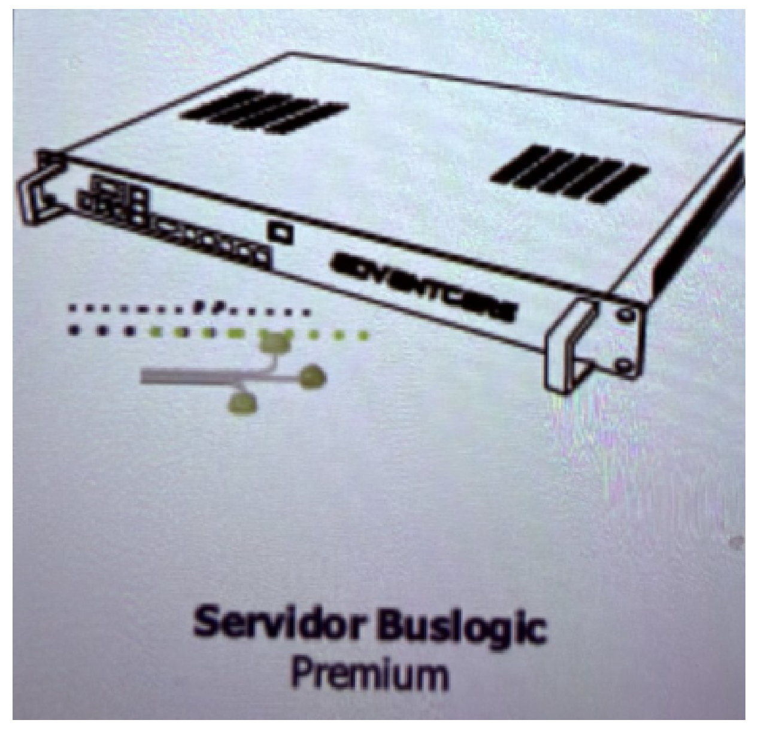

Buslogic Premium תרש

דוק	**Advantcare**
םוקימ	עקרקב ישאר ןורא
הבוג	**ןוראב**
תומכ	**1**

6

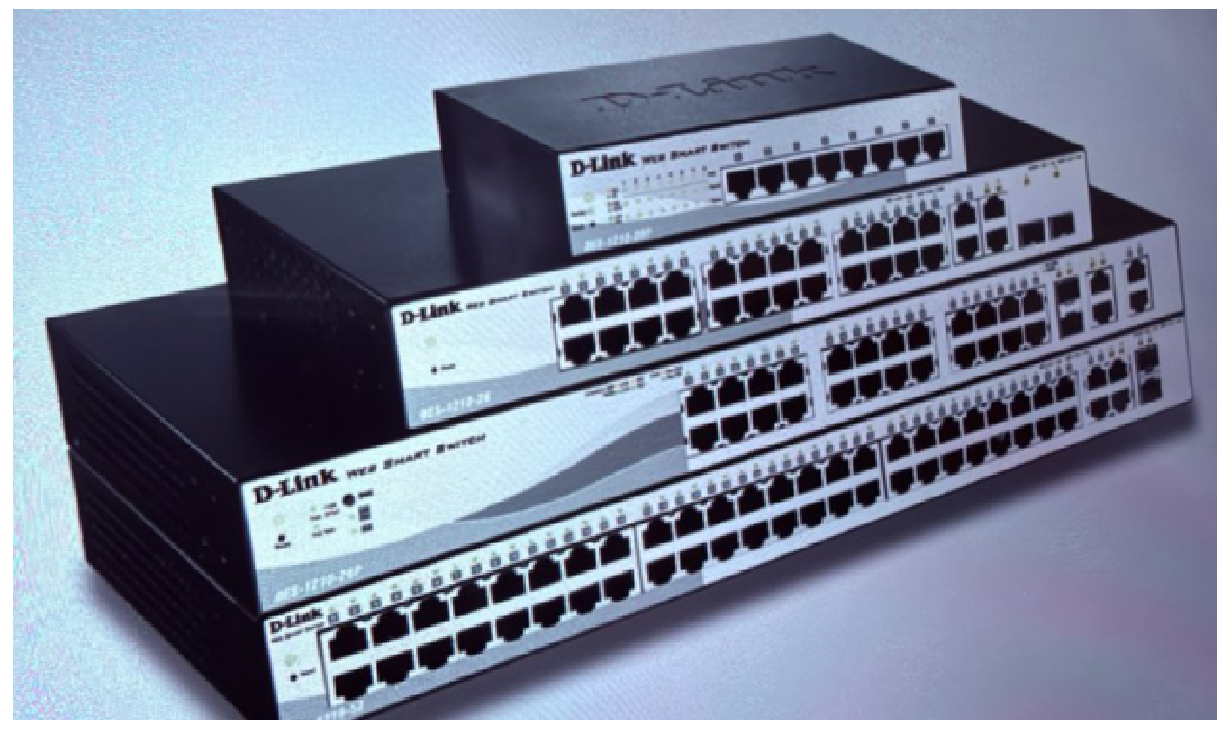

גתמ PoE םע 24 תואיצי

דוק	**D-Link DES-1210-28P**
םוקימ	עקרקבו המוק לכב ןורא
הבוג	**ןוראב**
תומכ	**9**

7

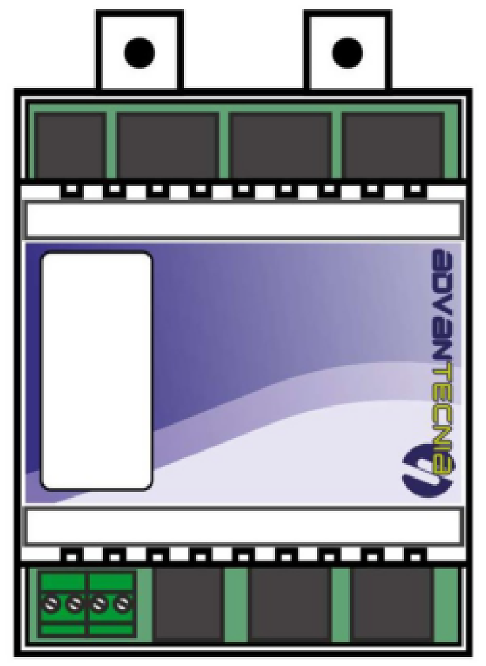

LCom – זכרמ ילאידר

דוק	**ACE71610003**
םוקימ	םיירוביצה םיתורישהו הריד לכ תרקת
הבוג	**2,55 m**
תומכ	**41**

8

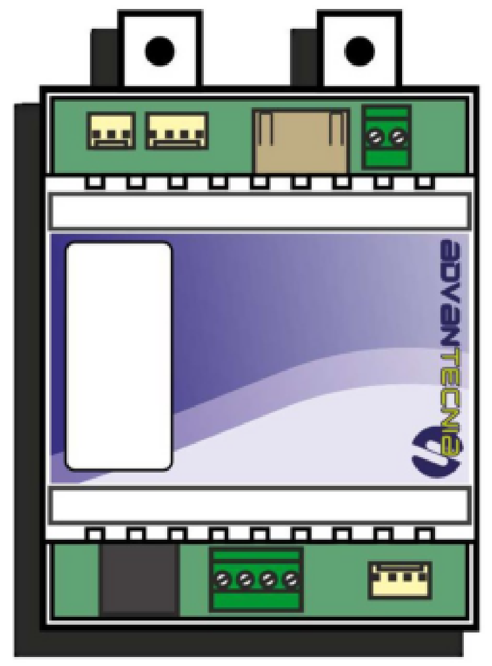

BoxCom – זכרמ סאב

דוק	**ACE70810000**
םוקימ	תוריד המכ רבחמ :ןוראה דיל הרקת
הבוג	**2,55 m**
תומכ	**17**

9

NOTES · תורעה

/ ACE BG 1. לש סוחיי תונומת
Advantecnia, םע תרתוכה ןהלש.

2. לבח תכישמ: לבח םודא םע תידי,
הפצרהמ םג שיגנ.

3. רבדמו ארוק הסינכב טלבאטה
םע תוחאה.

4. םיארוקשכ תקלדנ ןורדסמה תרונמ
םיירוביצה םיתורישהמ.

5. לנפב ןצחל האירק םודא,
ןצחל לוחכ (לאמש) קוריו (ןימי)
רובידל לוקמרו.

6. תרשרש: םינקתה ← LCom (ילאידר) ←
BoxCom (סאב) ← גתמ PoE ← תרש.

7. תורישי רבוחמ הדמעה ןופלט
.PoE-ה גתמל

גצומ עבצ הזיא – הדמעה ןופלט

🟥	(SOS / הכישמ) הקעזה	**םודא**
🟩	תוחכונ: תחא םעפ קורי ןצחל	**קורי**
▨	הקעזה וא האירק לטבמ :בוש קורי ןצחל	**קחמנ**
🟦	(blue call) ןצחל לוחכ: האירק תאפור	**לוחכ**
🟧	תילוק החיש	**םותכ / בוהצ**

ןגומ רויד · ןוכיתה םי ילדגמ

תוריד 32 · תומוק 8 + עקרק – תוחא תאירק

Telab International :הכוןע י"ע   ACE BG · Advantecnia :תכרעמ

תכרעמה דויצ

System devices

SCALE · הדימ הנק	DATE · ךיראת	REV	ןוילג
S/E	**15/10/2026**	**B**	**02**

סיסב: תינכות לכירדאה L5 (זוג דסמ / Triplet) · םירטמב תודימ

טמרופ A1 · הרודהמ B – לע תינכותה תיתימאה

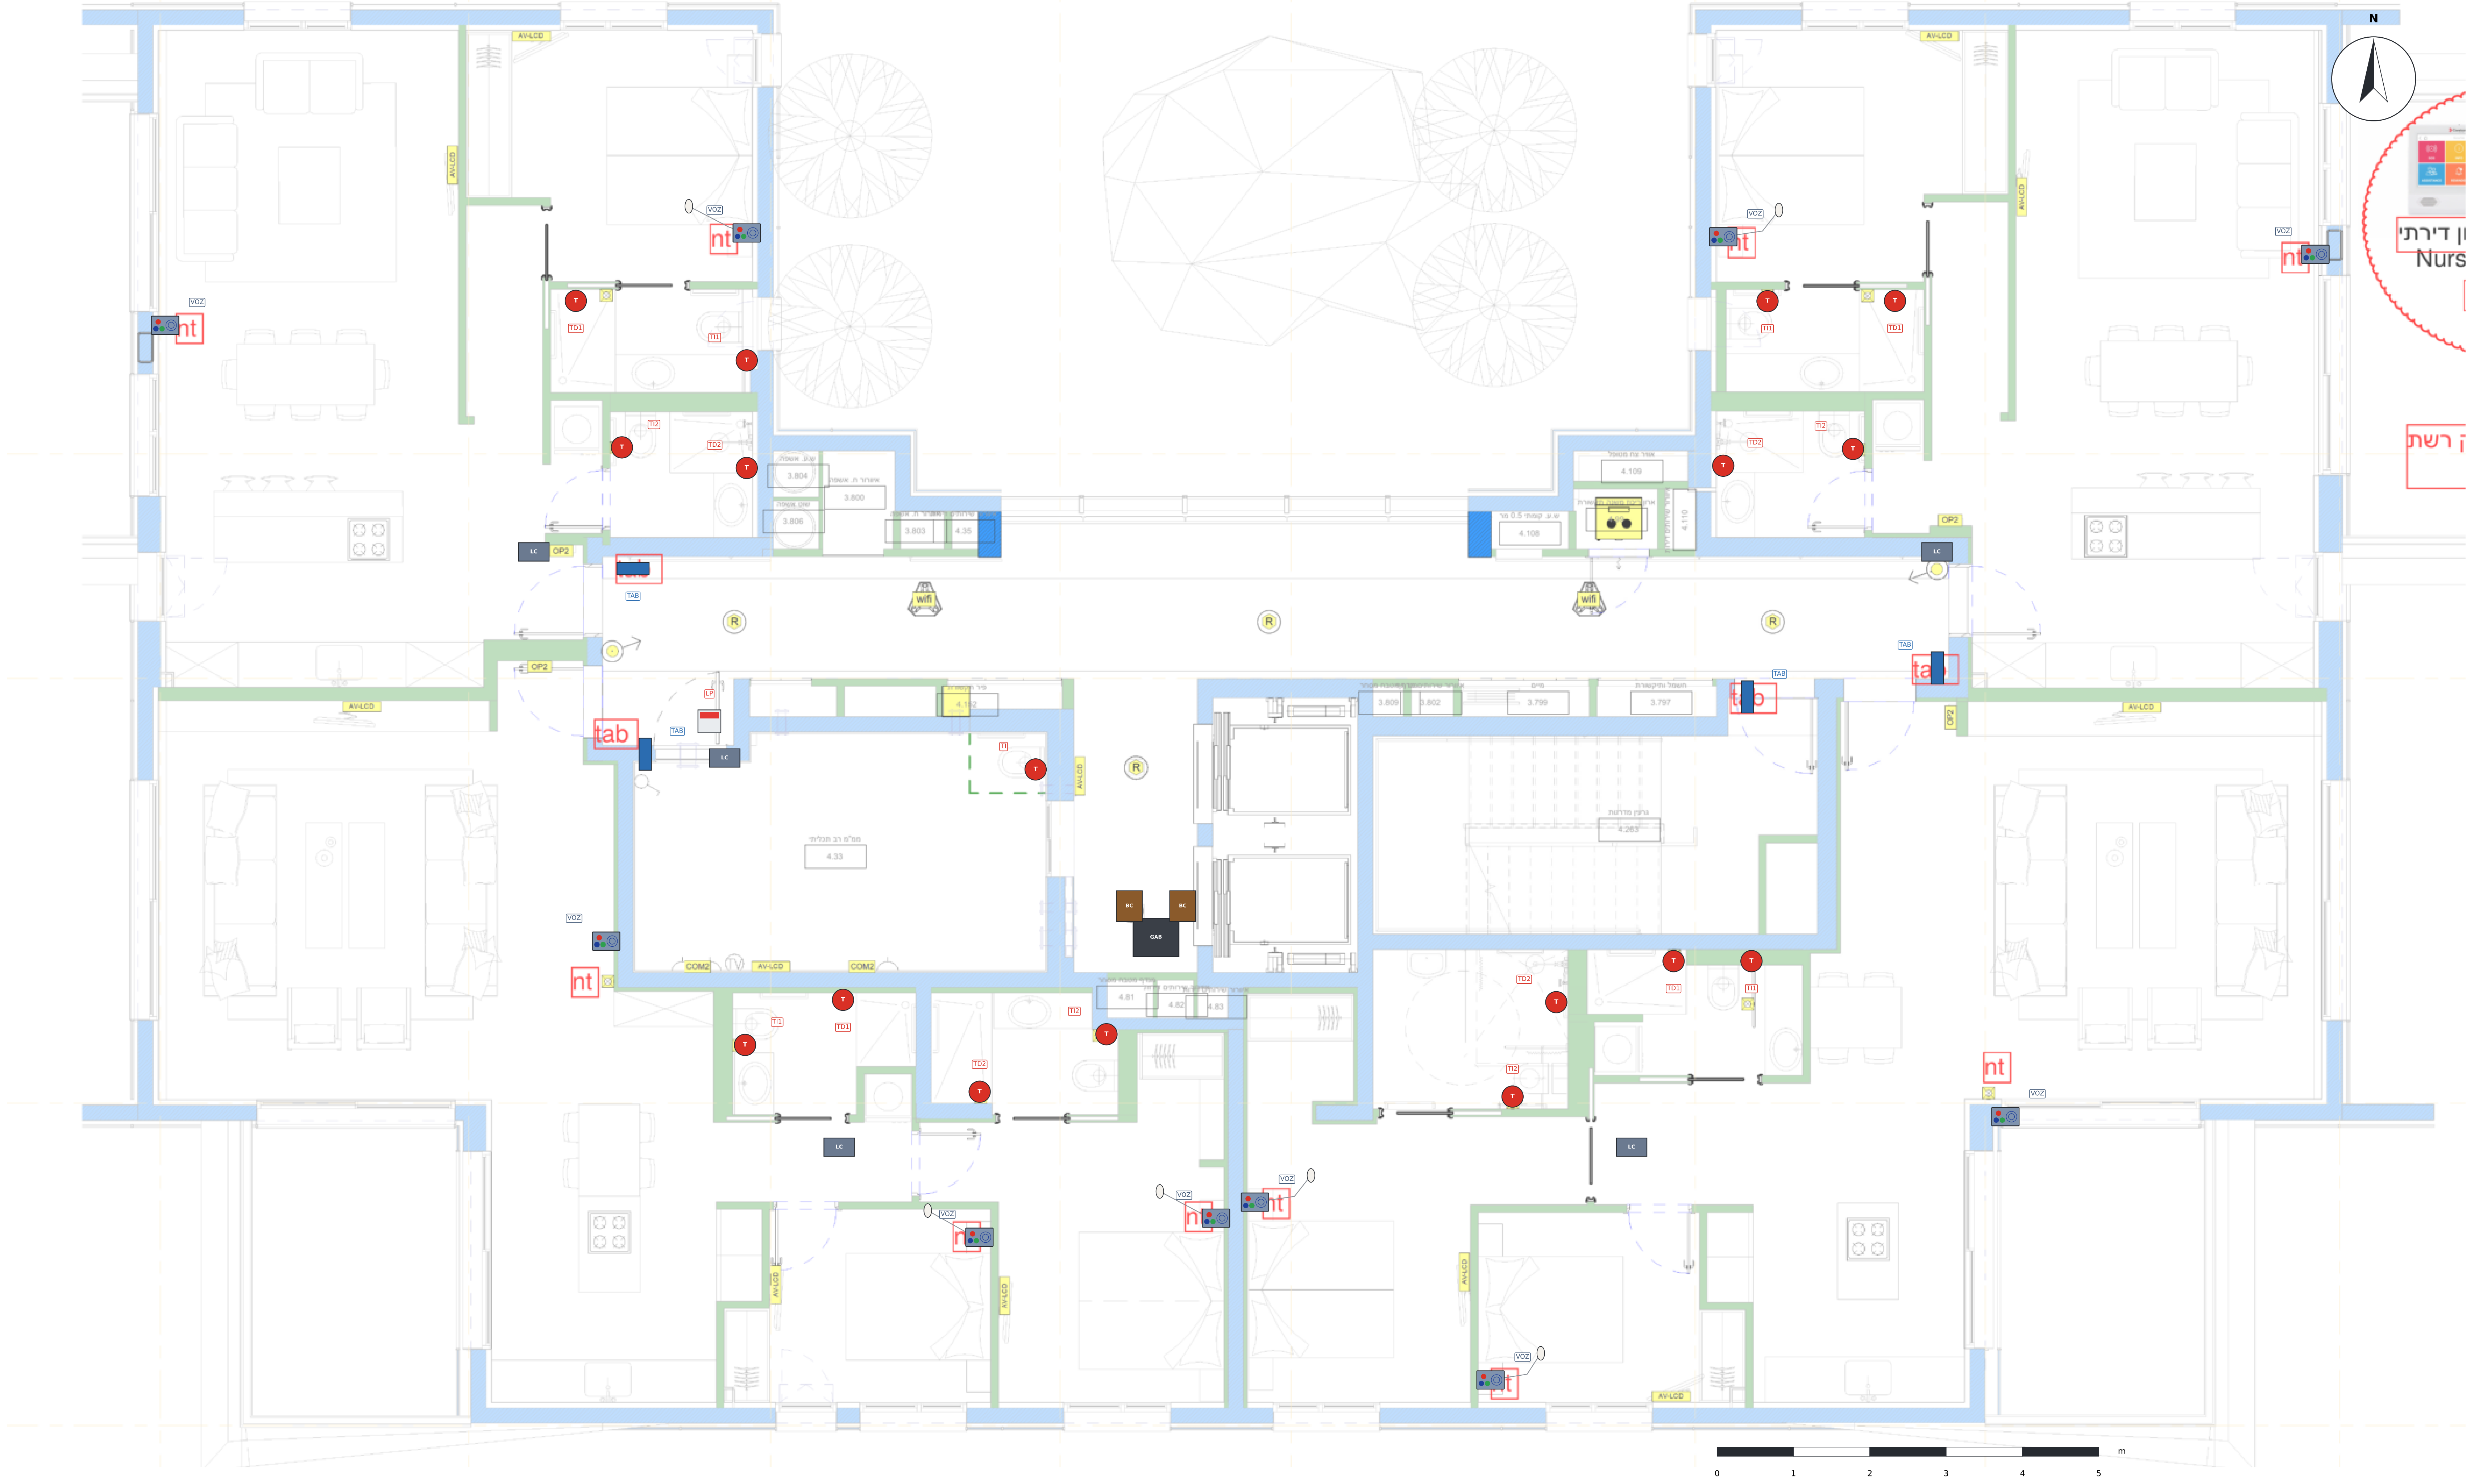

NOTES · תורעה

1. רקע: תינכות IT L2 לש חוקלה םע םינומיסה ולש םודאב:
«nt» = לנפ ילוק ו-«tab» = טלבאט הסינכב.

2. לעמ, עבצב: הצוויד הבהעצה וז.
לכ לנפ וכל טלבאט םיאצמנ םוקמב שהלקוח םיס|.

L2 3. הריבועיםי הצהובים ☒ בחדרי הרחצה תבוכנית
הם השמיכות הבחל (תחלקומו הלסא).

4. 4 הטאבלטים, בלוביי, ליד דלת כל דירה,
ינומיסב ומכ «tab».

5. לתוכניווות L2 ו-L5 (הצהעה סיסב) אותו בבנה;
L5 8 איה הקומה תיספויטה לקומות 1 דע.

DEVICES · EQUIPOS · דויצ

🟦	TAB · טלבאט הסינכב (iPad / דיאורדנא) – קריאה ודיבור, גובה 1.40 מ' Door tablet – call and voice · טלבאט הסינכב – קריאה ודיבור
▨	VOZ · לנפ ילוק םע לחצנים ACE82182451 – סלון וחדרי שינה, גובה 1.20–1.30 מ' Voice panel with buttons – living room and bedrooms · לנפ ילוק םע לחצנים – סלון וחדרי שינה
○	אגס קריאה ליד המיטה (בחדרי השינה) Call pear next to the bed (bedrooms) · אגס קריאה ליד המיטה
T	TI / TD · משיכת חבל ACE40320303W – אסלה ומקלחת, גובה 1.85 מ' Pull-cord – toilet and shower, h 1.85 m · משיכת חבל – אסלה ומקלחת, גובה 1.85 מ'
🟥	LP · מנורת מסדרון ACE41020309 – מעל דלת כל שירותים ציבוריים Corridor light – above each public toilet door · מנורת מסדרון – מעל דלת כל שירותים ציבוריים

שירותים קריאת אחות

לבח תכישמ

טבלט אנדרואיד קריאת אחות

(דיאורדנא / iPad) הסינכב טלבאט

מנורה קריאת אחות

ןורדסמ תרונמ

פנל קריאת אחות

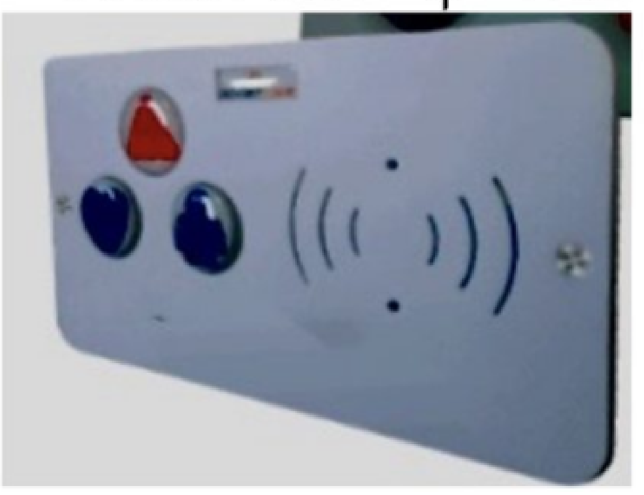

לנפ ילוק םע םינצחל

ןגומ רויד · ןוכיתה םי ילדגמ

תוריד 32 · תומוק 8 + עקרק – תוחא תאירק

Telab International :הכוןע י"ע   ACE BG · Advantecnia :תכרעמ

העצההו (תינכות L2) חוקלה ינומיס

Client marks (plan L2) and proposal

SCALE · הדימ הנק	DATE · ךיראת	REV	ןוילג
1:60	15/10/2026	B	03

בסיס: תינכות לכירדאה L5 (זוג דסמ / Triplet) · םירטמב תודימ

טמרופ A1 · הרודהמ B – לע התוכנית תיתימאה

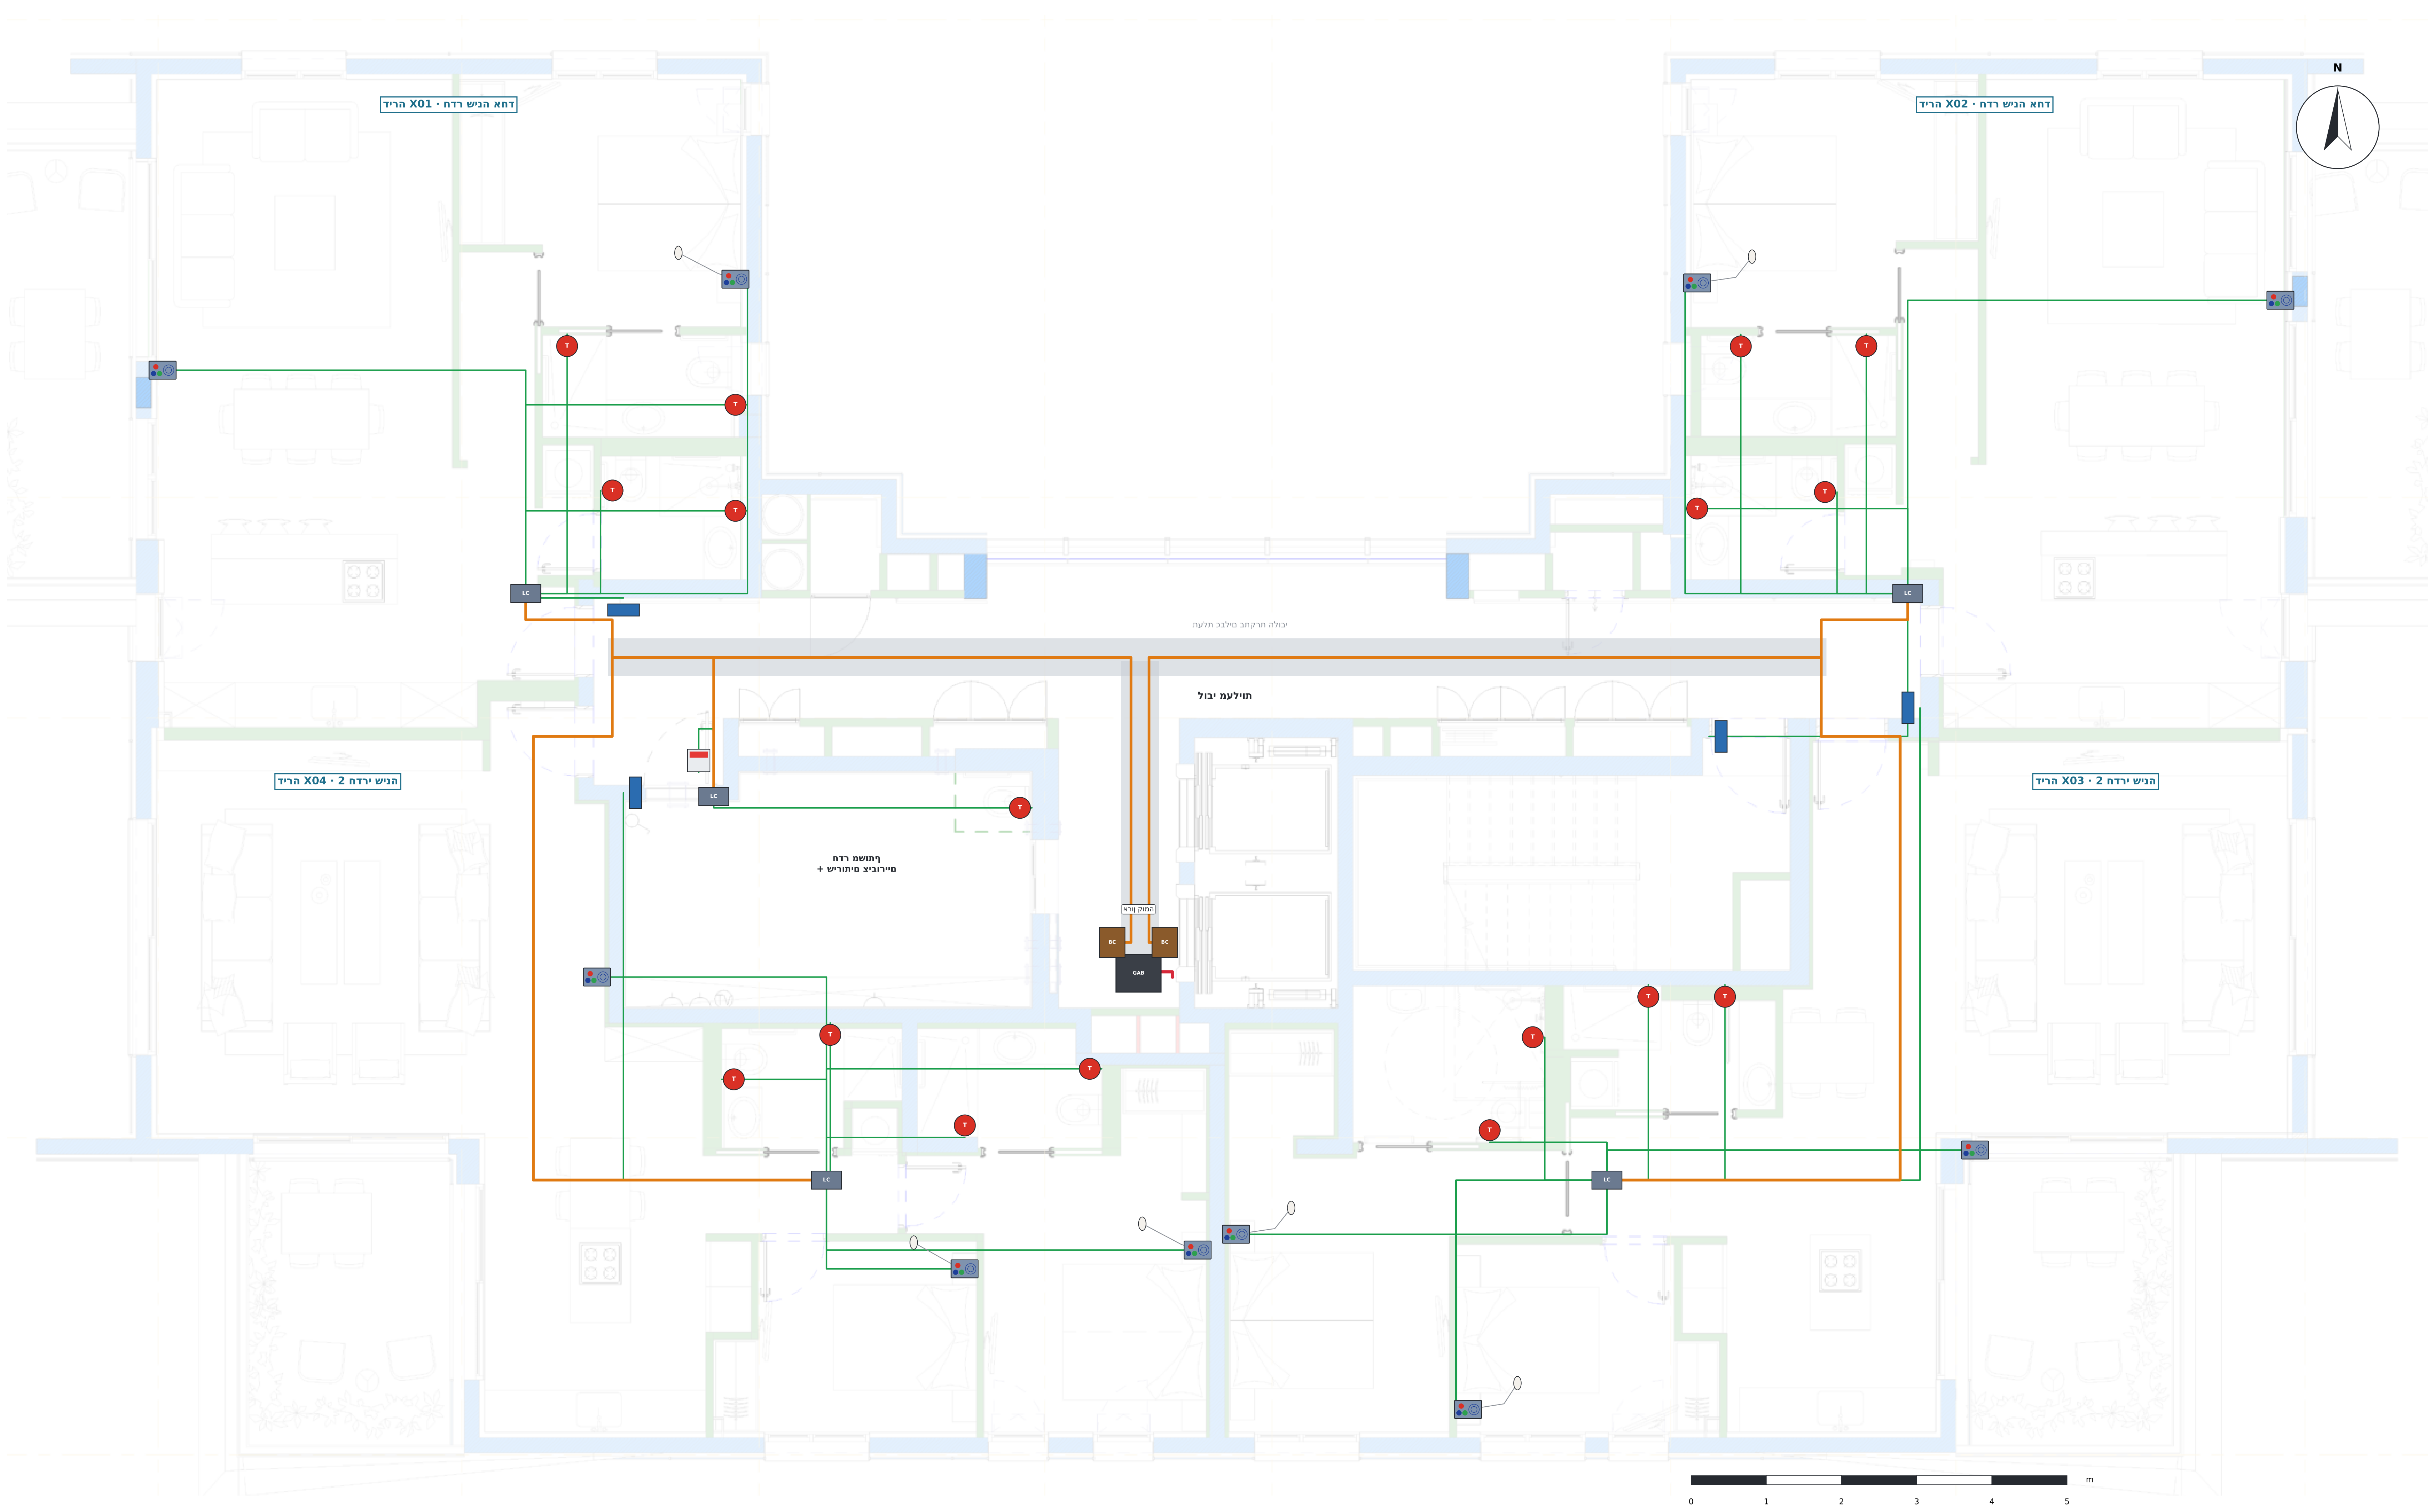

WIRING · CABLEADO · טוויח

🟩 Cat6 ילאידר: לכ ןקתה ← LCom הרידה לש
Cat6 radial: each device → apartment LCom · Cat6 ילאידר: לכ ןקתה ← LCom הרידה לש

🟧 Cat6 / Cat7 תרשרש: LCom ← LCom ← BoxCom הרקתב
Cat6 / Cat7 chain: LCom → LCom → BoxCom · Cat6 / Cat7 תרשרש: LCom ← LCom ← BoxCom

🟥 Cat6A / Cat7 תשר: BoxCom ← גתמ PoE ← דומע ← תרש עקרק
Cat6A / Cat7 network: BoxCom → switch → riser → GF server · Cat6A / Cat7 תשר: BoxCom ← גתמ ← דומע ← תרש

םיכרוא המוקב תיסופיט (אלל הברזר)

🟩	Cat6 ילאידר ךותב הרידה	183 m
🟧	Cat6 / Cat7 תרשרש LCom ← BoxCom	80 m
🟥	Cat6A / Cat7 ןורא דומעו	7 m

NOTES · תורעה

1. לכ ןקתה רבוחמ תילאידר (Cat6) ל-LCom הרידה לש, תרקתב האובמה.
2. ה-LCom םירשורשמ תלעתב הלובי דע ה-BoxCom הרקתב,
.BoxCom 1 · x02 ← x03 ← BoxCom 2 ← רדח ףתושמ ← x01 ← x04 :דיל וראה
3. ה-BoxCom םידרוי גתמל ה-PoE ןוראב; גתמה הלוע
דומעב Cat6A / Cat7 דע תרשה עקרקב.
4. לוכה PoE: ןיא ךרוצ ב-230V ינקתהל הרידה.

NOTES · תורעה

1. סיסב: תוניכת תילכירדא L5 (המוק תיסופיט) – 8 תומוקה תוהז: 4 תוריד המוקב, 32 ךסב לוכה.
2. תוריד x01 ו-x02: רדח הניש דחא, ןולס םע חבטמ ו-2 ירדח הצחר. תוריד x03 ו-x04: 2 ירדח הניש ו-2 ירדח הצחר.
3. טלבאט הסינכב לכל הריד (iPad / דיאורדנא) האירקל ולדיבור םע תוחאה.
4. לנפ ילוק םע םינצחל (ACE82182451) ןולסב ובכל רדח הניש; רדחב הנישה םע אגס דיל הטימה.
5. תוכישמ לבח (ACE40320303W) הלסאב תחלקמבו לכב ירדח הצחרה, הבוגב 1.85 מ'.
6. םיתוריש םיירוביצ לכב המוק רדחב ףתושמה: תכישמ לבח + תרונמ תורדסמ לעמ הלדה. םע 2 עקרקב – 10 םיתוריש םיירוביצ.
7. ןורא המוק דיל תוילעמה םע גתמ PoE D-Link DES-1210-28P; 2 ה-BoxCom הרקתב ודיל.
8. םימוקימ יפל ינומיס הלקוח תונכותב L2 (nt = לנפ ילוק, tab = טלבאט): ואר ןויליג 03.

ןגומ רויד · ןוכיתה םי ילדגמ
תאירק תוחא – עקרק + 8 תומוק · 32 תוריד
Telab International :ןכוה י"ע ACE BG · Advantecnia :תכרעמ

טוויח · 1–8 תיסופיט המוק

Typical floor F1–F8 · wiring

SCALE · הדימ הנק	DATE · ךיראת	REV	ןוילג
1:60	15/10/2026	B	04

סיסב: תוניכת האדריכל L5 (זוע דסמ / Triplet) · םידות במטרים
טמרופ A1 · הרודהמ B – לע התונכות תיתימאה

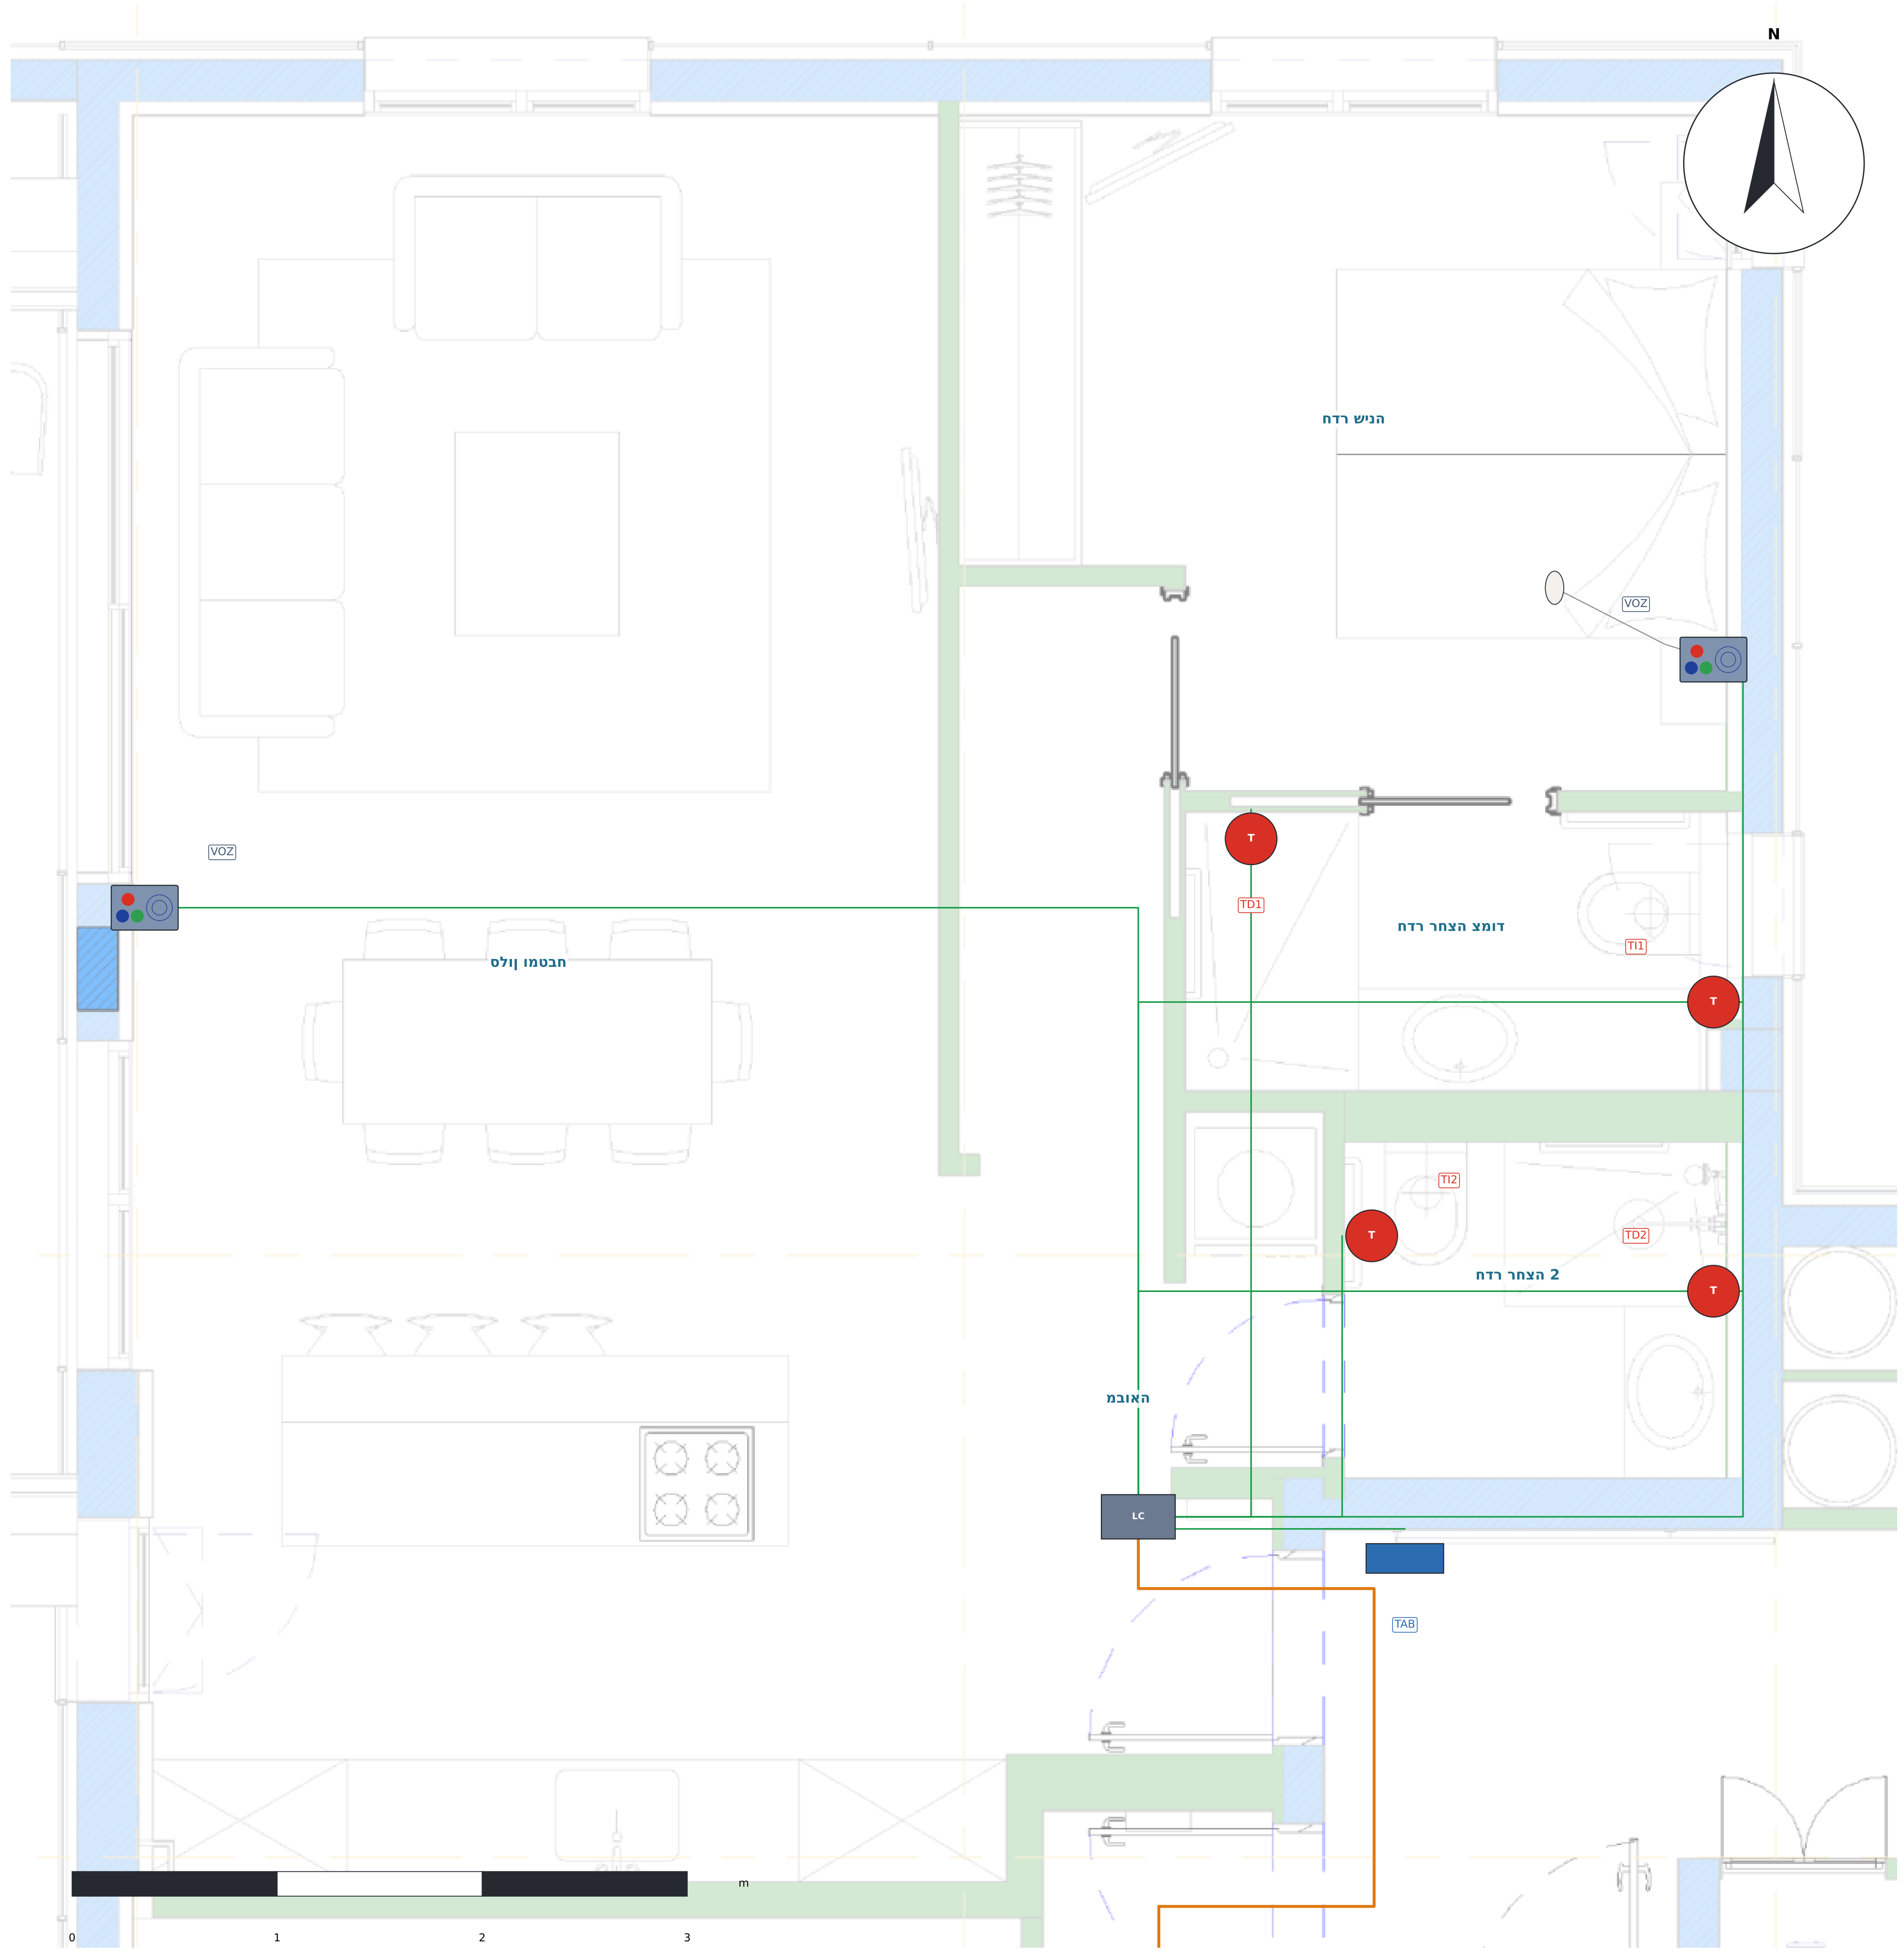

הרידה דויצ

ID	ןקתה	רדח	הבוג
TAB	הסינכב טלבאט	האובמ	1.40 מ'
VOZ-S	סינצחל םע ילוק לנפ	חבטמו ןולס	1,30 m
VOZ-D	סגא + סינצחל םע ילוק לנפ	הניש רדח	1,20 m
TI1	לבח תכישמ	דומצ הצחר רדח	1.85 מ'
TD1	לבח תכישמ	דומצ הצחר רדח	1.85 מ'
TI2	לבח תכישמ	2 הצחר רדח	1.85 מ'
TD2	לבח תכישמ	2 הצחר רדח	1.85 מ'
LCOM	LCom ACE71610003	האובמ	2,55 m

SYMBOLS · SÍMBOLOS · םילמס

- TAB · הסינכב טלבאט (iPad / דיאורדנא) – רובידו האירק ,הבוג 1.40 מ'
  Door tablet – call and voice · רובידו האירק – הסינכב טלבאט
- VOZ · סינצחל םע ילוק לנפ ACE82182451 – ןולס ירדחו הניש ,הבוג 1.20–1.30 מ'
  Voice panel with buttons – living room and bedrooms · סינצחל םע ילוק לנפ – ןולס ירדחו הניש
- סגא האירק דיל הטימה (הנישה ירדחב)
  Call pear next to the bed (bedrooms) · סגא האירק דיל הטימה
- TI / TD · לבח תכישמ ACE40320303W – הלסא תחלקמו, הבוג 1.85 מ'
  Pull-cord – toilet and shower, h 1.85 m · לבח תכישמ – הלסא תחלקמו, הבוג 1.85 מ'
- LP · ןורדסמ תרונמ ACE41020309 – םעל תלד לכ שירותים ציבוריים
  Corridor light – above each public toilet door · ןורדסמ תרונמ – םעל תלד לכ שירותים ציבוריים
- LC · LCom ACE71610003 – הרידה זכרמ (הרקת)
  LCom – apartment hub (ceiling) · LCom – הרידה זכרמ (הרקת)
- BC · BoxCom ACE70810000 – זכרמ סאב המכל תוריד (הרקת)
  BoxCom – bus hub for several apartments (ceiling) · BoxCom – זכרמ סאב המכל תוריד (הרקת)

NOTES · תורעה

1. הריד x02 איה תנומת יאר לש x01 (דויצ ותוא).
2. טלבאט יבולב, דיל תלד הסינכה (ןומיס «tab» לש חוקלה).
3. לנפ ילוק ןולסב רדחבו הנישה (םע סגא דיל הטימה).
4. 2 ירדח הצחר: תכישמ לבח הלסאב תחלקמבו דחא לכב (4 תוכישמ לבח).
5. לוכה רבוחמ תילאידר ב-Cat6 ל-LCom האובמב.

פנל קריאת אחות

סינצחל םע ילוק לנפ

מנורה קריאת אחות

ןורדסמ תרונמ

טבלט אנדרואיד קריאת אחות

הסינכב טלבאט (iPad / דיאורדנא)

שירותים קריאת אחות

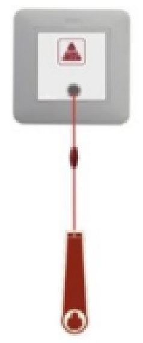

לבח תכישמ

ןגומ רויד · ןוכיתה םי ילדגמ
תוריד 32 · תומוק 8 + עקרק – תוחא תאירק
Telab International :ןכוה ע"י   ACE BG · Advantecnia :תכרעמ

דחא הניש רדח תריד (x01 / x02)

1-bedroom apartment (x01 / x02)

SCALE · הדימ הנק	DATE · ךיראת	REV	ןוילג
1:30	**15/10/2026**	**B**	**05**

סיסב: תוכנית לכירדאה L5 (םדס זוע / Triplet) · םירטמב תודימ
טמרופ A1 · הרודהמ B – לע תוכנותה תיתימאה

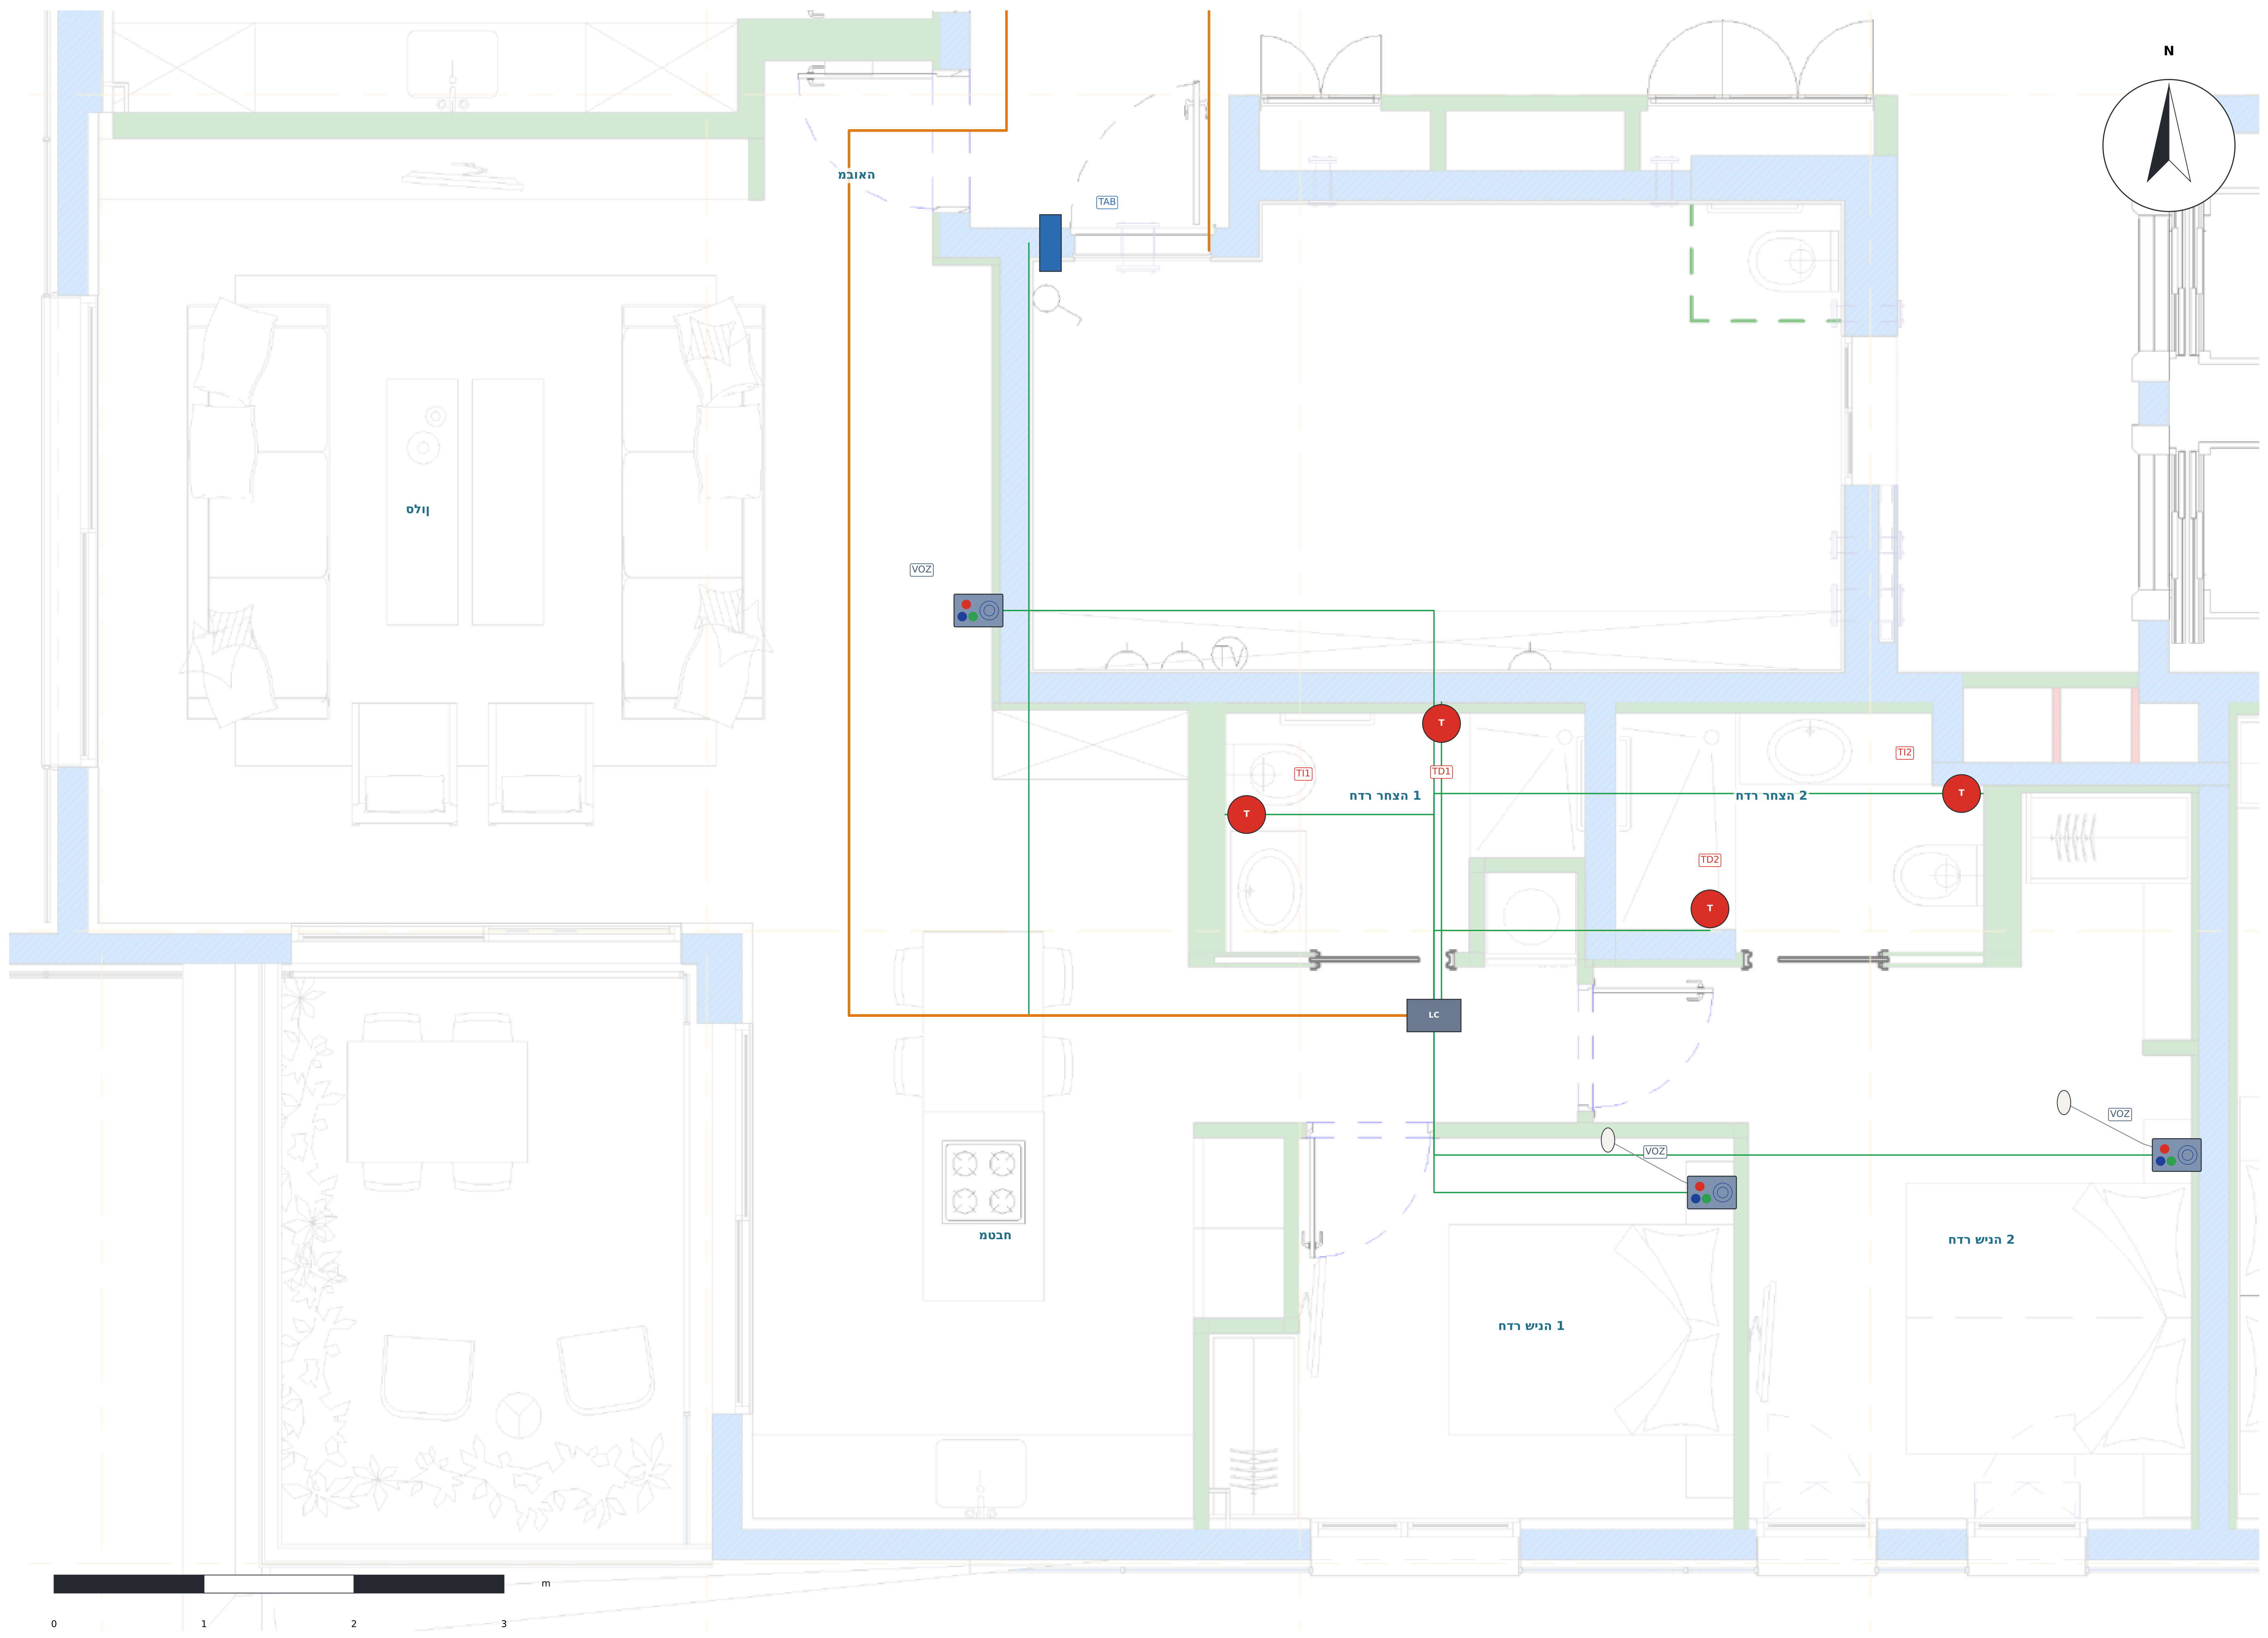

הרידה דויצ

ID	ןקתה	רדח	הבוג
TAB	הסינכב טלבאט	האובמ	1.40 מ'
VOZ-S	סינצחל םע ילוק לנפ	ןולס	1,30 m
VOZ-D1	סגא + סינצחל םע ילוק לנפ	הניש רדח 1	1,20 m
VOZ-D2	סגא + סינצחל םע ילוק לנפ	הניש רדח 2	1,20 m
TI1	לבח תכישמ	הצחר רדח 1	1.85 מ'
TD1	לבח תכישמ	הצחר רדח 1	1.85 מ'
TI2	לבח תכישמ	הצחר רדח 2	1.85 מ'
TD2	לבח תכישמ	הצחר רדח 2	1.85 מ'
LCOM	LCom ACE71610003	האובמ	2,55 m

SYMBOLS · SÍMBOLOS · םילמס

🟦	TAB · הסינכב טלבאט (iPad / דיאורדנא) – רובידו האירק ,הבוג 1.40 מ' Door tablet – call and voice · הסינכב טלבאט – רובידו האירק
VOZ	VOZ · לנפ ילוק םע סינצחל ACE82182451 – ןולס ירדחו הניש ,הבוג 1.20–1.30 מ' Voice panel with buttons – living room and bedrooms · לנפ ילוק םע סינצחל – ןולס ירדחו הניש
○	סגא האירק דיל הטימה (ירדחב הנישה) Call pear next to the bed (bedrooms) · סגא האירק דיל הטימה
T	TI / TD · תכישמ לבח ACE40320303W – הלסא תחלקמו, הבוג 1.85 מ' Pull-cord – toilet and shower, h 1.85 m · תכישמ לבח – הלסא תחלקמו, הבוג 1.85 מ'
🟥	LP · תרונמ ןורדסמ ACE41020309 – לעמ לדת לכ םיתוריש םייבוביצ Corridor light – above each public toilet door · תרונמ ןורדסמ – לעמ לדת לכ םיתוריש םייבוביצ
LC	LC · LCom ACE71610003 – זכרמ הרידה (הרקת) LCom – apartment hub (ceiling) · LCom – זכרמ הרידה (הרקת)
BC	BC · BoxCom ACE70810000 – זכרמ סאב לכמה תוריד (הרקת) BoxCom – bus hub for several apartments (ceiling) · BoxCom – זכרמ סאב לכמה תוריד (הרקת)

NOTES · תורעה

1. הרידב x03 ותוא דויצ (ירדח הצחרה הסירפב הנוש).
2. טלבאט יבולב, דיל תלד הסינכה (ןומיס «tab» לש הלקוח).
3. לנפ ילוק ןולסב ינשבו ירדח הנישה (םע סגא דיל הטימה).
4. 2 ירדח הצחר: תכישמ לבח הלסאב תחלקמבו דחא לכב (4 תוכישמ לבח).
5. לוכה רבוחמ תילאידר ב-Cat6 ל-LCom ןורדסמב ירדח הנישה.

פנל קריאת אחות

סינצחל םע ילוק לנפ

מנורה קריאת אחות

ןורדסמ תרונמ

טבלט אנדרואיד קריאת אחות

הסינכב טלבאט (iPad / דיאורדנא)

שירותים קריאת אחות

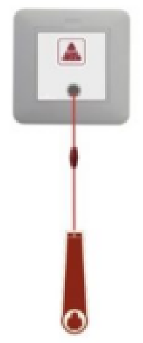

לבח תכישמ

ןגומ רויד · ןוכיתה םי ילדגמ

תוריד 32 · תומוק 8 + עקרק – תוחא תאירק

Telab International :הוכןע י"ע ACE BG · Advantecnia :תכרעמ

(x04 / x03) הניש ירדח ינש תריד

2-bedroom apartment (x04 / x03)

SCALE · הדימ הנק	DATE · ךיראת	REV	ןוילג
1:35	15/10/2026	B	06

סיסב: תוינכת לכירדאה L5 (זוע דסמ / Triplet) · םירטמב תודימ

טמרופ A1 · הרודהמ B – לע תוינכותה תיתימאה

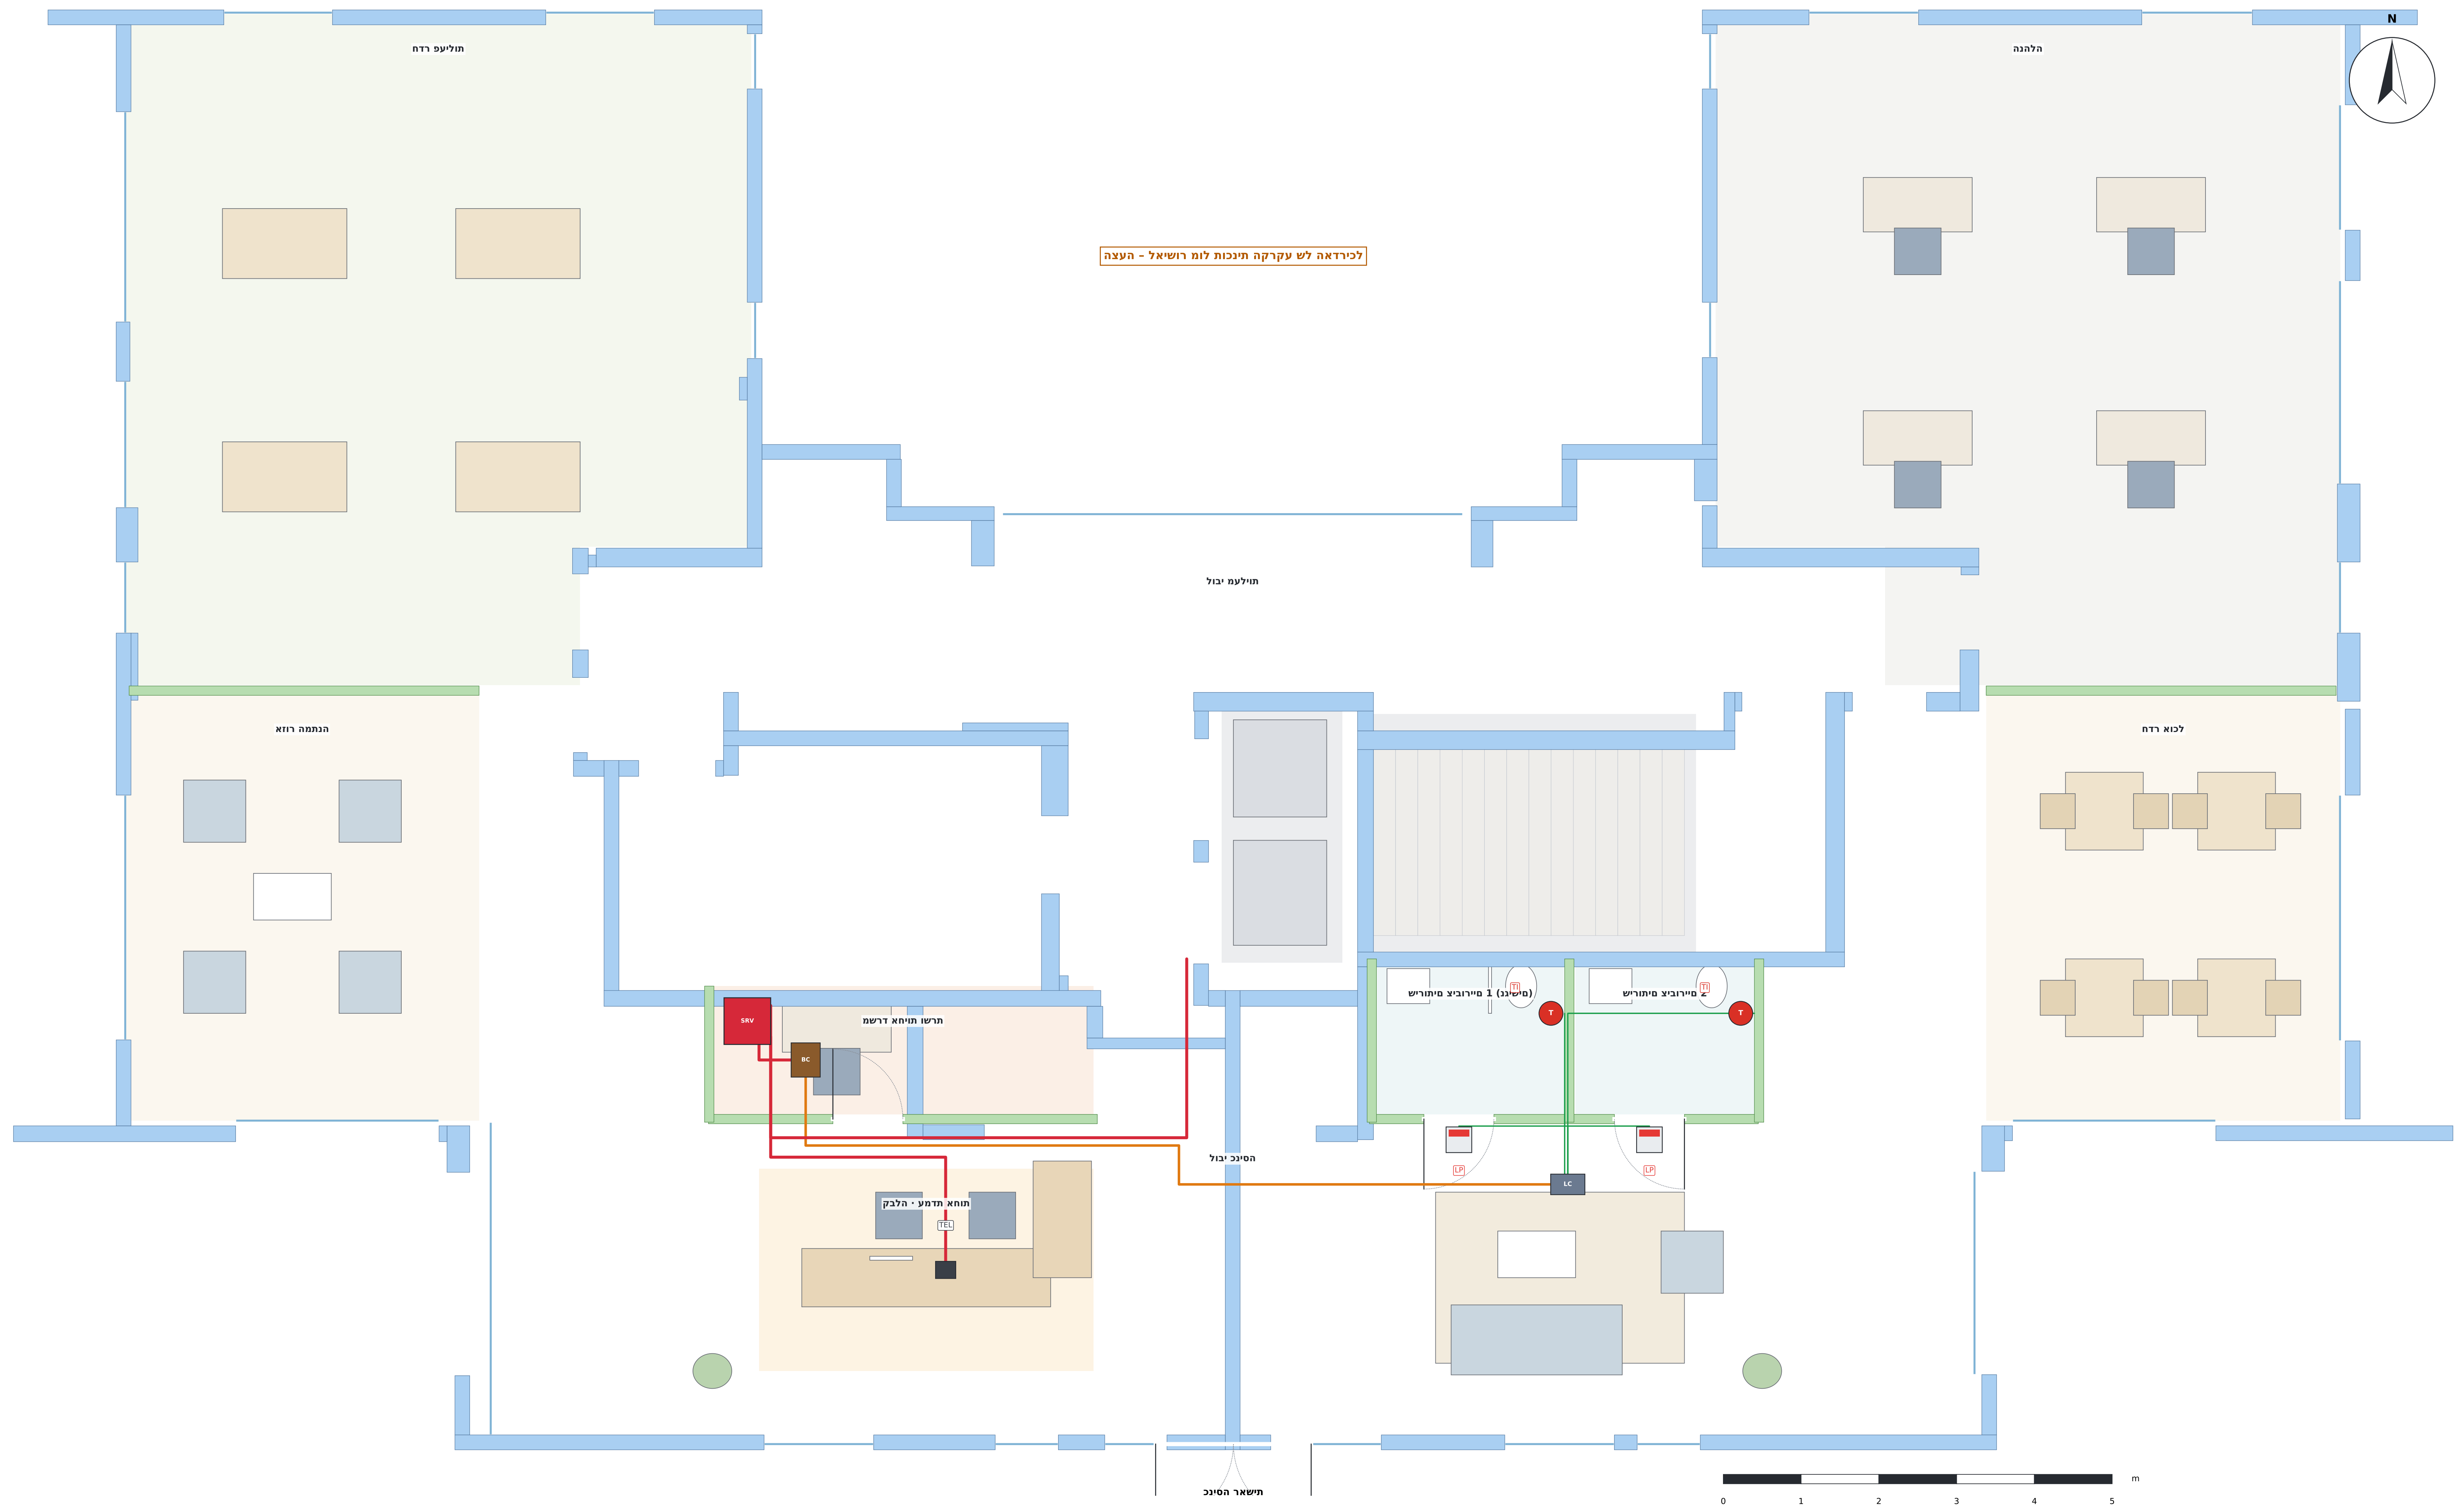

פרט · קבלה ועמדת אחות (1:40)

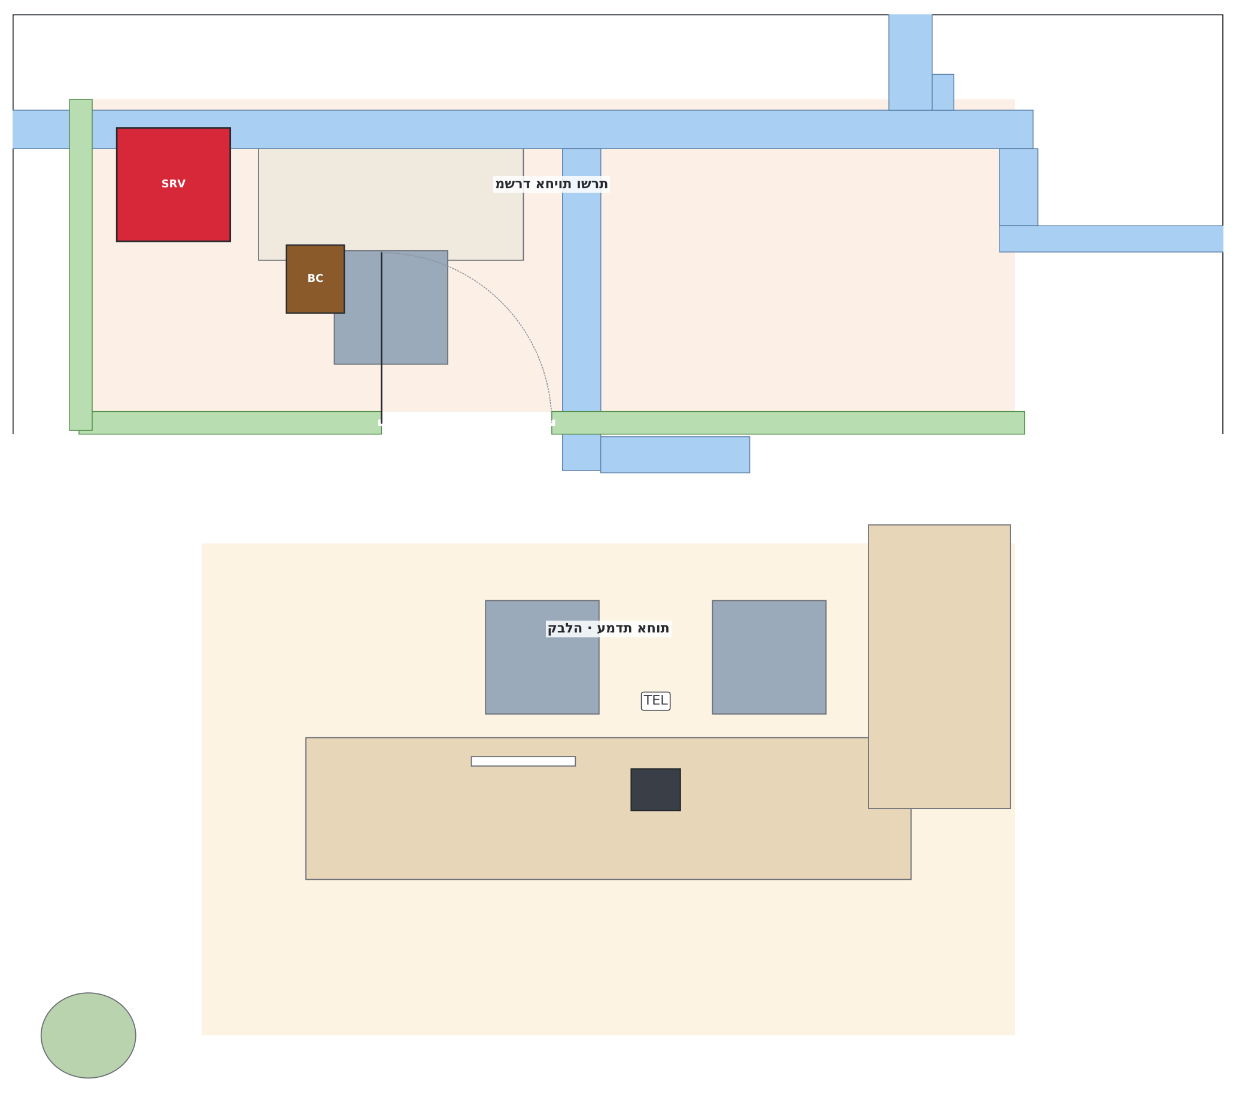

NOTES · תורעה

1. תוחאה תדמע הלבקב, לומ הסינכה תוילעמהו.
2. לע הדמעה: ןופלט Grandstream דיאורדנא, רבוחמ ה-PoE גתמל תורישי. לכ האירק תגצומ עבצב הלש.
3. ירוחאמ הדמעה: דרשמ םע ןוראה ישארה: תרש Buslogic Premium גתמו PoE D-Link. BoxCom לש עקרקה הרקתב.
4. 2 םיתוריש םייריבוצ עקרקב: תכישמ לבח דיל הלסאה תרונמו ןודרסמ לעמ לכ תלד.
5. דומעה מ-8 תומוקה דרוי ןיערגב דע ןוראה ישארה.
6. תעצומ עקרק תסירפ: ןכדועת עיגתשכ תינכותה לש לכירדאה.

SYMBOLS · SÍMBOLOS · םילמס

T	TI / TD · לבח תכישמ ACE40320303W – הלסא תחלקמו, הבוג 1.85 מ' Pull-cord – toilet and shower, h 1.85 m · לבח תכישמ – הלסא תחלקמו, הבוג 1.85 מ'
LC	LC · LCom ACE71610003 – זכרמ הרידה (הרקת) LCom – apartment hub (ceiling) · LCom – זכרמ הרידה (הרקת)
SRV	SRV · ןורא עקרק: תרש Buslogic Premium + גתמ PoE D-Link GF rack: Buslogic Premium server + D-Link PoE switch · ןורא עקרק: תרש Buslogic Premium + גתמ PoE D-Link
🟥	LP · תרונמ ןודרסמ ACE41020309 – לעמ תלד לכ םיתוריש םייריבוצ Corridor light – above each public toilet door · תרונמ ןודרסמ – לעמ תלד לכ םיתוריש םייריבוצ
TEL	TEL · ןופלט Grandstream דיאורדנא – PoE תורישי גתמל Grandstream Android phone – PoE straight to the switch · ןופלט Grandstream דיאורדנא – PoE תורישי גתמל
BC	BC · BoxCom ACE70810000 – זכרמ סאב המכל תוריד (הרקת) BoxCom – bus hub for several apartments (ceiling) · BoxCom – זכרמ סאב המכל תוריד (הרקת)

גצומ עבצ הזיא – הדמעה ןופלט

🟥	(SOS / הכישמ) הקעזא	םודא
🟩	תוחכונ: תחא םעפ קורי ןצחל	קורי
⬜	הקעזא וא האירק לטבמ: בוש קורי ןצחל	קחמנ
🟦	(blue call) אפור תאירק: לוחכ ןצחל	לוחכ
🟧	תילוק החיש	םותכ / בוהצ

ןגומ רויד · ןוכיתה םי ילדגמ
תוריד 32 · תומוק 8 + עקרק – תוחא תאירק
Telab International :ןכוה י"ע ACE BG · Advantecnia :תכרעמ

תוחא תדמעו יבול · עקרק תמוק

Ground floor · lobby and nurse desk

SCALE · הדימ הנק	DATE · ךיראת	REV	ןוילג
1:60	15/10/2026	B	07

בסיס: תינכות לכירדאה L5 (זוע דסמ / Triplet) · םירטמב תודימ
טמרופ A1 · הרודהמ B – לע תינכותה תיתימאה

א · בניין קרקע + 8 קומות

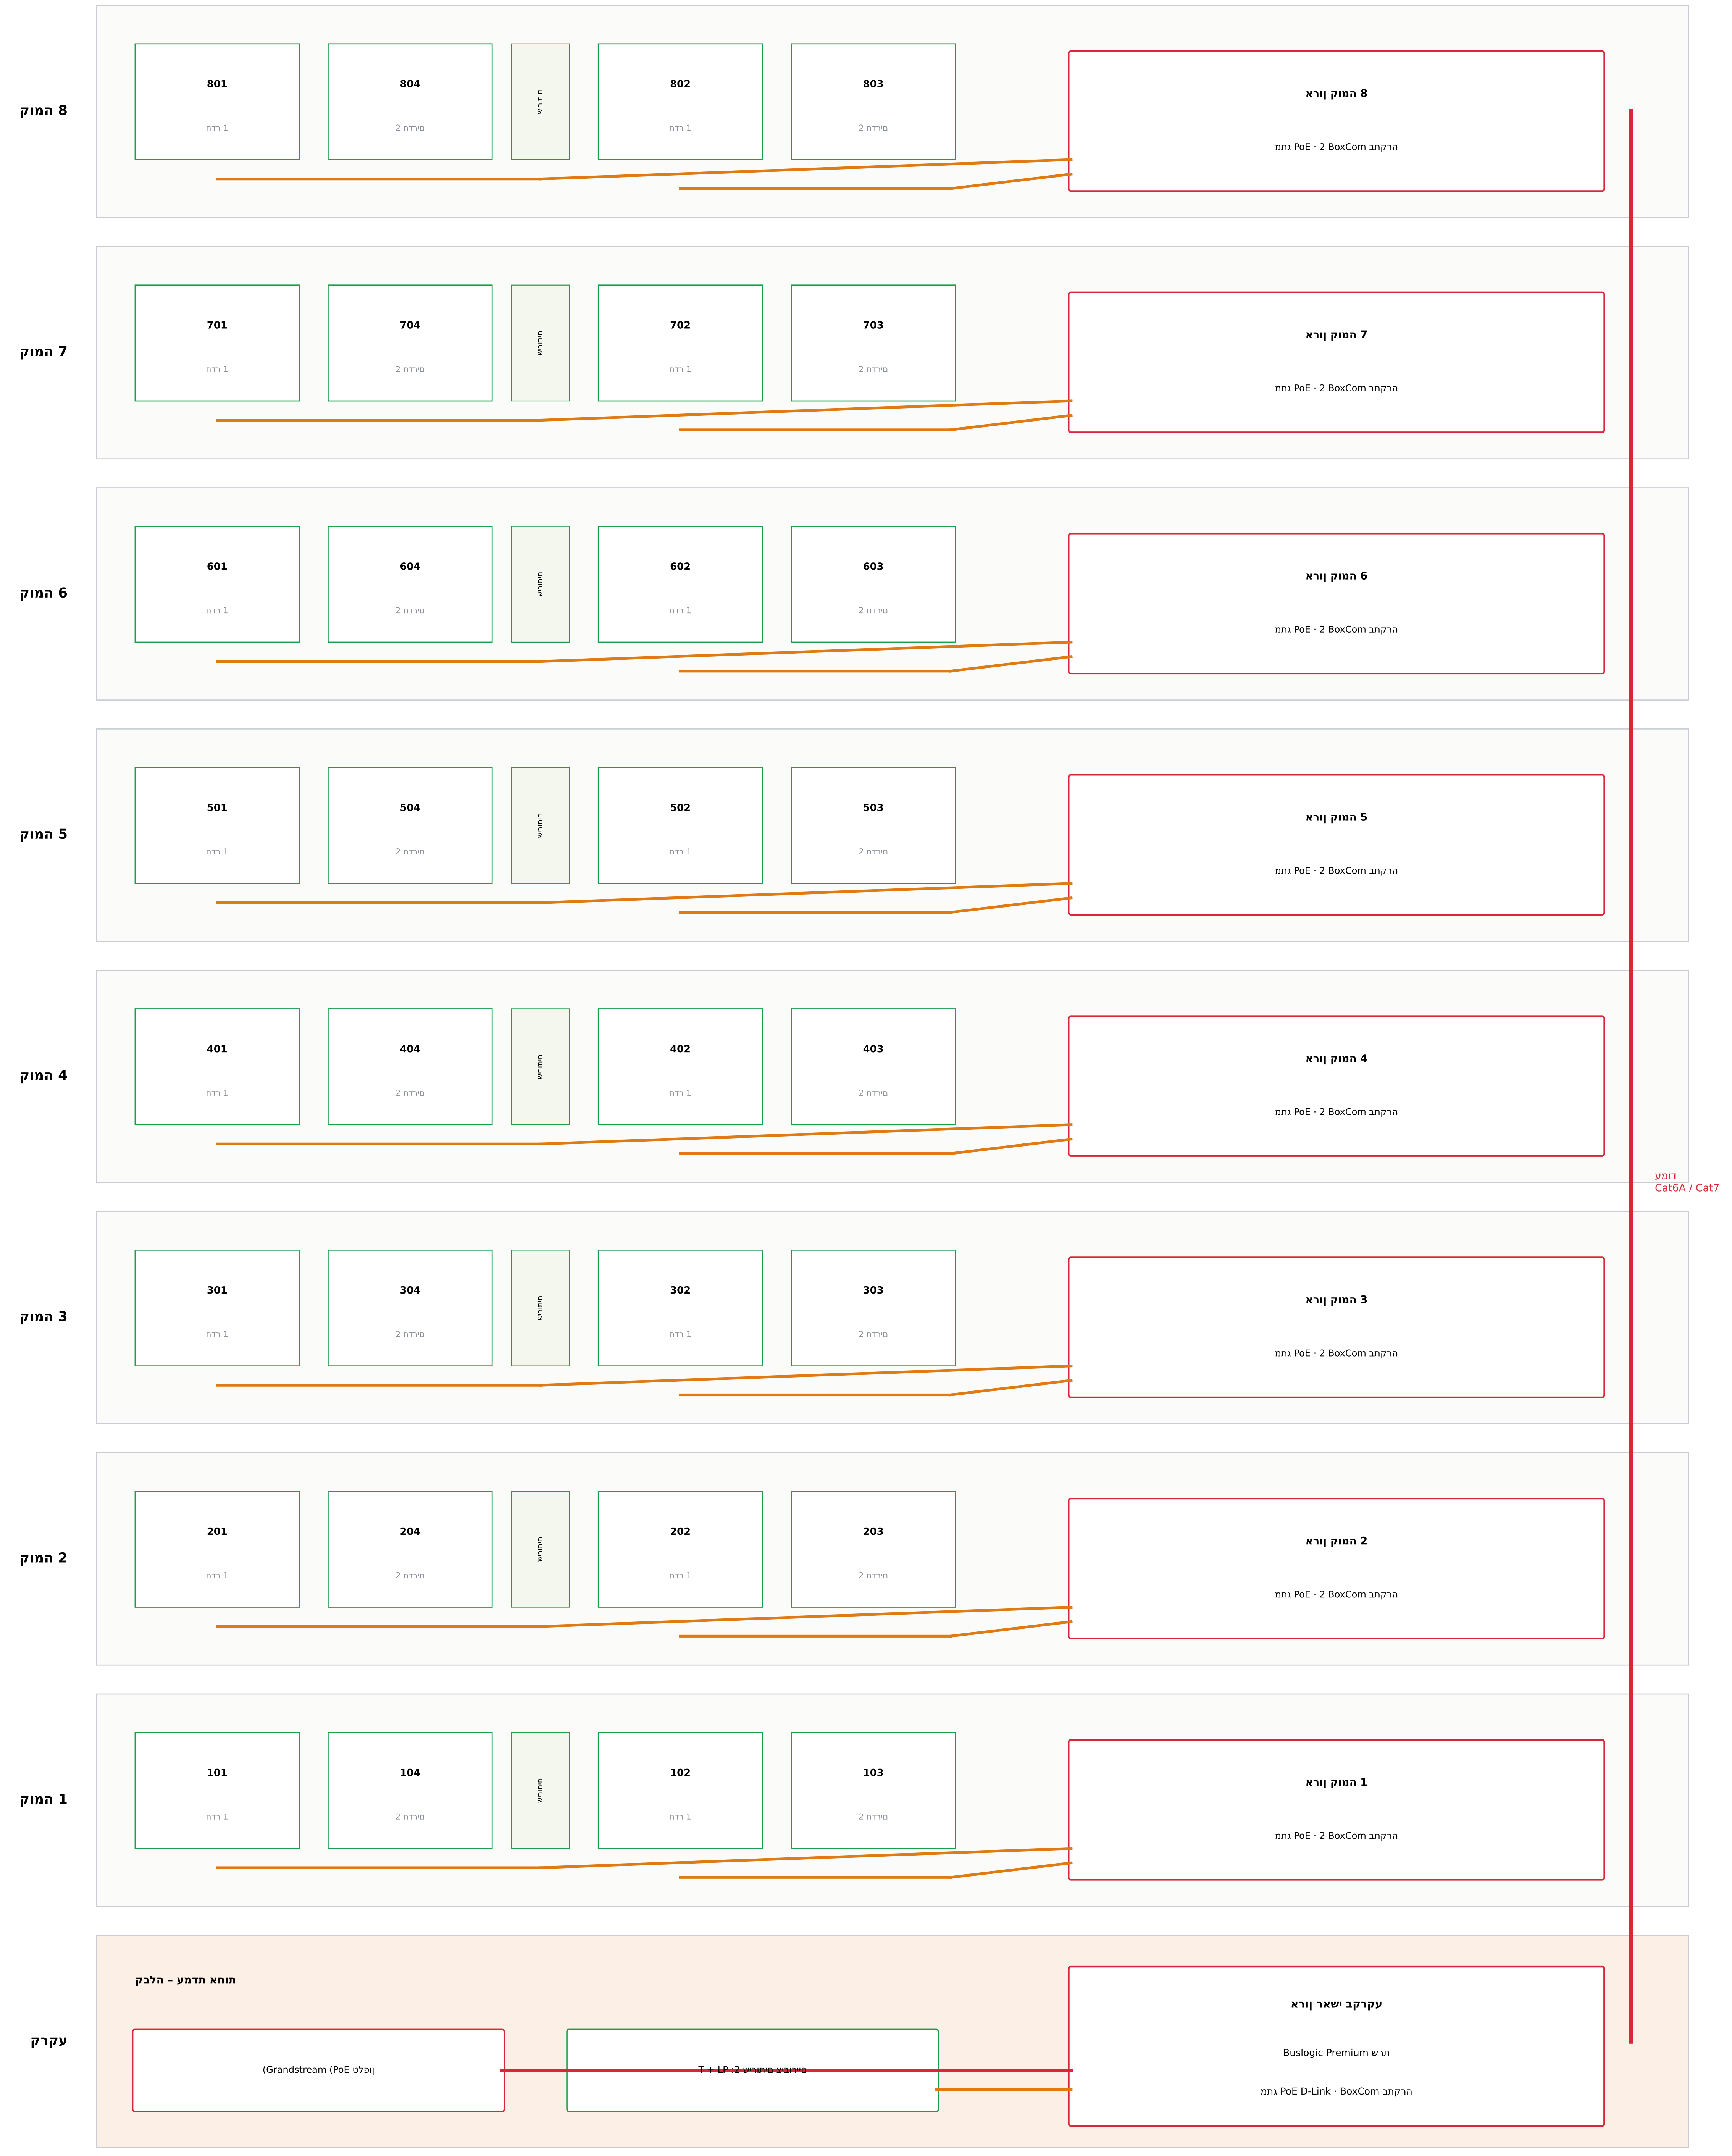

ב · טופולוגיה של דירה

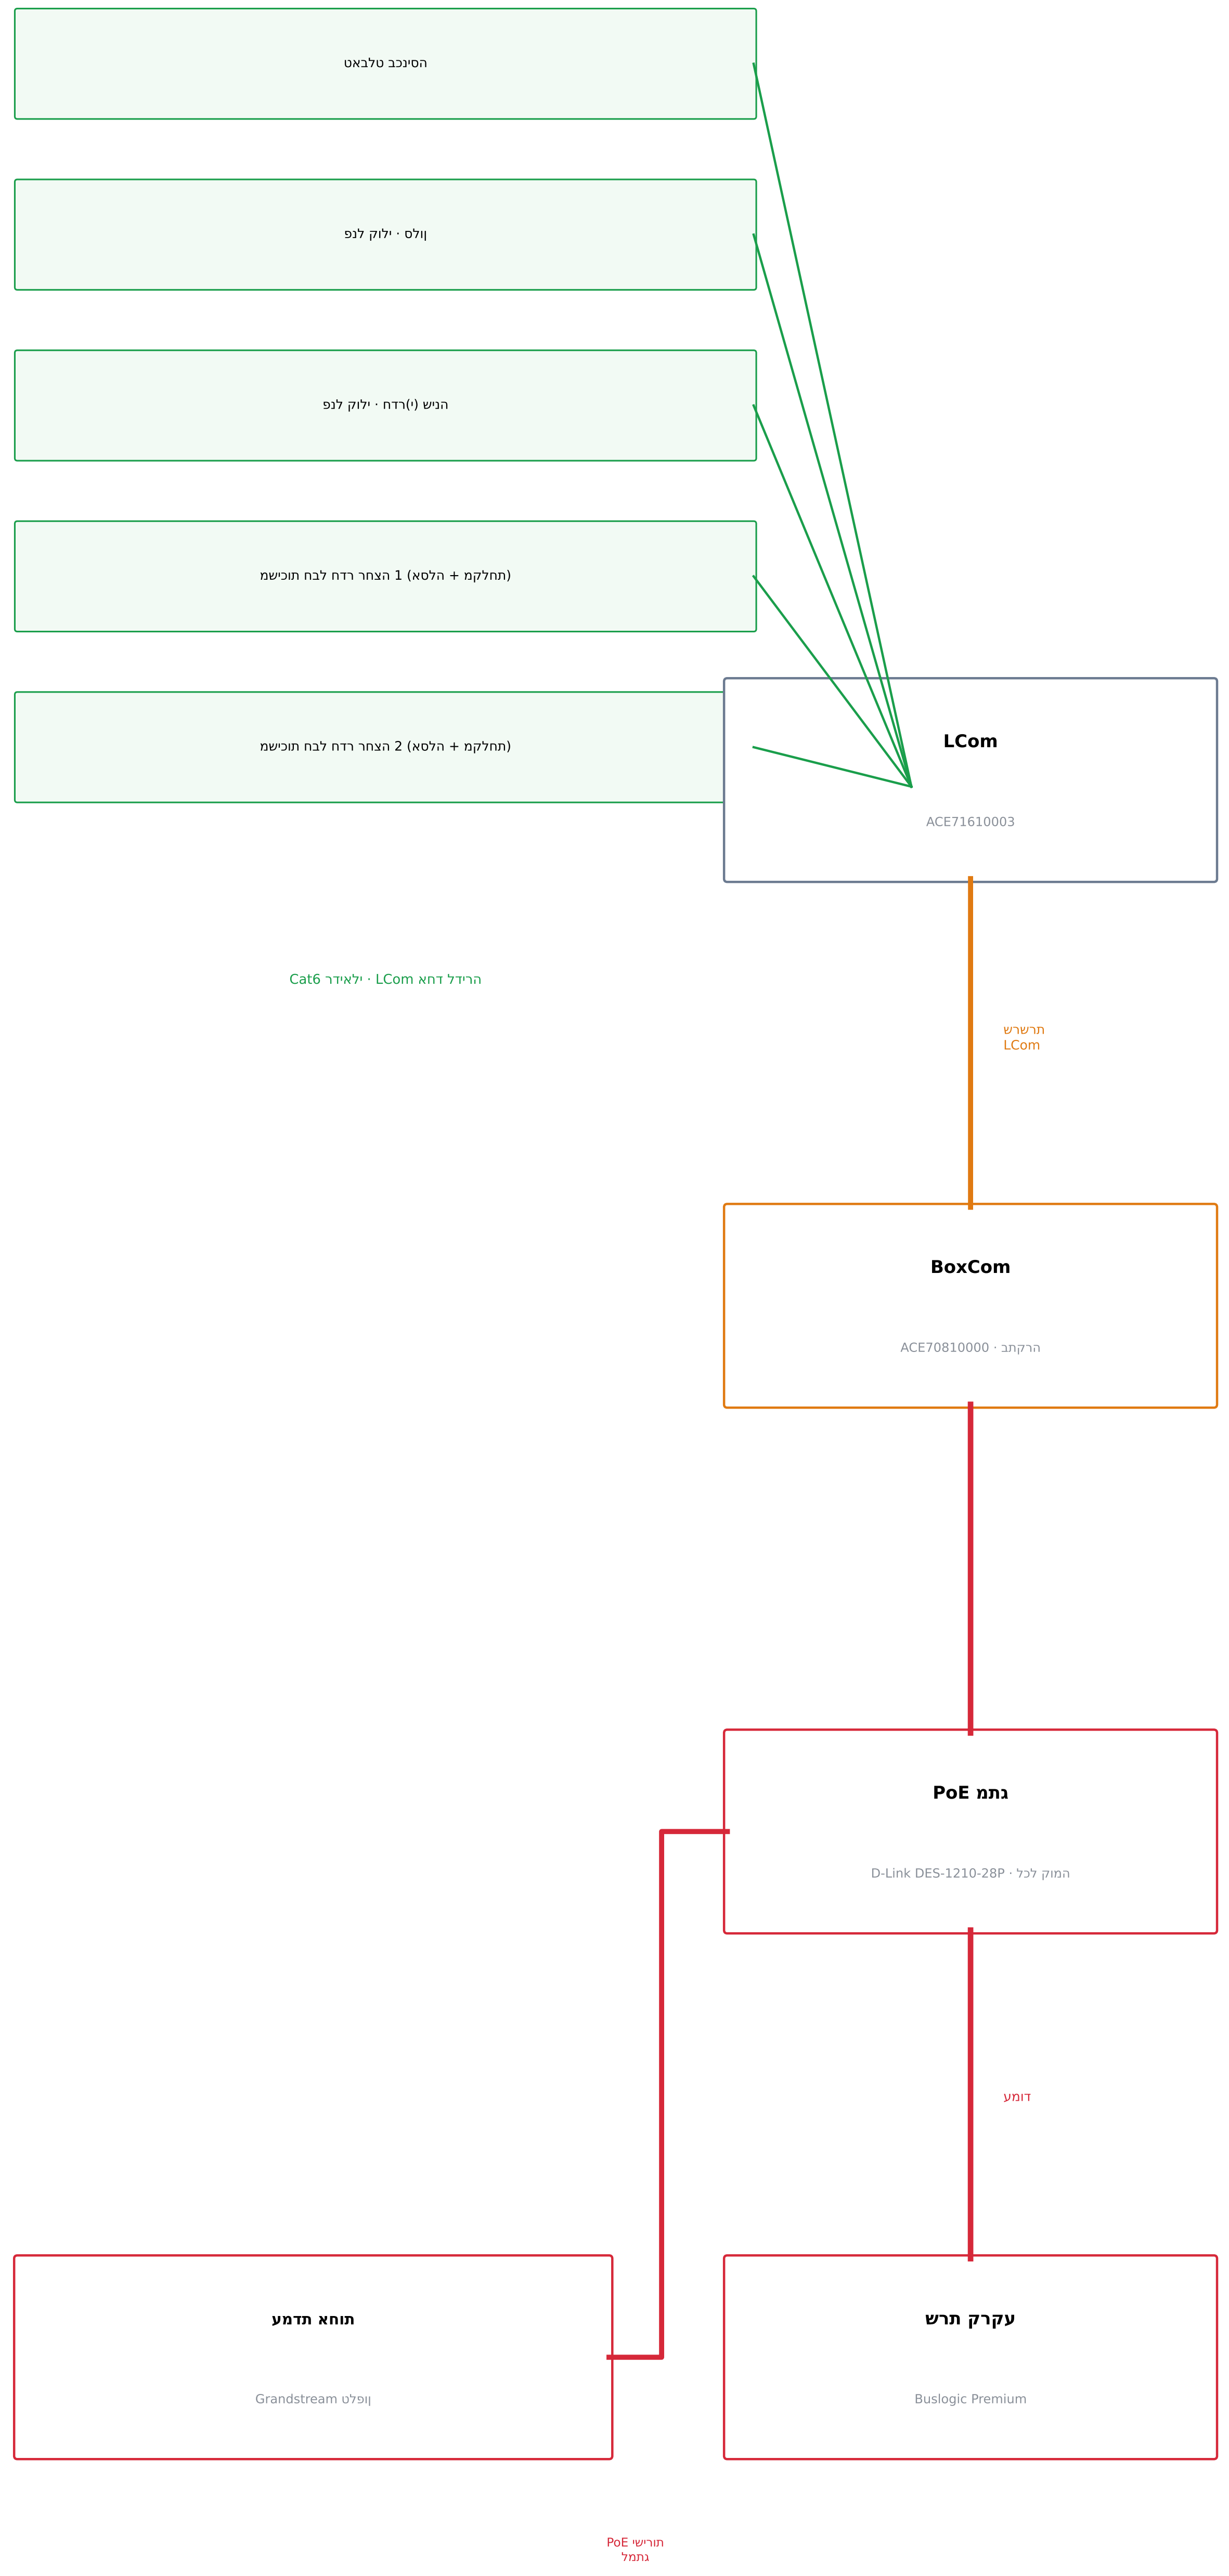

NOTES · הערות

1. 8 קומות זהות עם 4 דירות (2 דירות חדר שינה אחד ו-2 דירות שני חדרי שינה).
2. בכל קומה: BoxCom 2 בתקרה וארון עם מתג ה-PoE.
3. שרשרת x01 ← x04 :1 ← שירותים ציבוריים. שרשרת 2: x03 ← x02.
4. המתקנים מחוברים דרך העמוד עד הארון הראשי בקרקע.
5. טלפון ה-Grandstream בעמדה מחובר ישירות למתג ה-PoE ומציג כל קריאה בצבע שלה.
6. כל המערכת PoE.
7. כמויות ראשוניות: לאמת מול Advantecnia באתר.

מגדלי ים התיכון · דיור מוגן

קריאת אחות – קרקע + 8 קומות · 32 דירות

הוכן ע"י: Telab International   מערכת: ACE BG · Advantecnia

תרשים אנכי וטופולוגיה

Riser diagram and topology

SCALE · קנה מידה	DATE · תאריך	REV	גיליון
S/E	15/10/2026	B	08

בסיס: תוכניות האדריכל L5 (מסד זוג / Triplet) · מידות במטרים

פורמט A1 · מהדורה B – על התכנית האמיתית

תמישר סירמוח – כל הבניין (קרקע + 8 תומוק · 32 תוריד · 10 סיתוריש סיירוביצ)

דוק	רואית	תומכ	הרעה
בתוריד (32)			
TAB	הסינכב טלבאט (iPad / דיאורדנא) – רובידו האירק	**32**	1 הריד לכל
VOZ	ACE82182451 – סינצחל םע ילוק האירק לנפ	**80**	הניש רדח לכ + וולס
TI/TD	לבח תכישמ – ACE40320303W (תחלקמו הלסא)	**128**	4 הריד לכל
LC	LCom – ACE71610003	**32**	1 הריד לכל
סיתוריש סיירוביצ (10)			
T	ACE40320303W – לבח תכישמ	**10**	8 תומוק + 2 עקרקב
LP	ACE41020309 – וורדסמ תרונמ	**10**	תלד לכ לעמ
LC	LCom – ACE71610003	**9**	1 לכל המוק + 1 עקרקב
תונורא ומרכזייה			
BC	BoxCom – ACE70810000 (הרקתב)	**17**	2 המוקל + 1 עקרקב
SW	D-Link DES-1210-28P – תואיצי PoE 24 גתמ	**9**	1 לכל המוק + עקרק
GAB	וורא ריק 12U םע ץאפ' לנאפ (גתמל)	**8**	1 לכל המוק
GAB-PB	UPS וורא ישאר דמוע םע	**1**	עקרק
SRV	תרש Buslogic Premium (Advantcare) םע הנכות	**1**	עקרק
TEL	וופלט Grandstream דיאורדנא (PoE, עבצ יפל גוס האירק)	**1**	תוחא תדמע
סילבכ (+ 15% הברזר)			
—	Cat6 רדאילי רותב תורידה (קורי)	**1700 m**	183 מ' המוקל
—	Cat6 / Cat7 תרשרש LCom ← BoxCom (םותכ)	**750 m**	80 מ' המוקל
—	Cat6A / Cat7 תונורא דומעו (םודא)	**130 m**	דומע ללוכ

NOTES · תורעה

1. כמויות מחושבות מהמודל (תיסופיט המוק × 8 + עקרק).
2. לע ודדמנ לבכ יכרוא הטרושמה יאוותה, + 15%.
3. מחירים: יפל ןוריחמ Advantecnia ינכדעה.
4. השיכר ינפל רתאב תמאל.

וגומ רויד · ווכיתה םי ילדגמ

קרקע תואירק – עקרק + 8 תומוק · 32 תוריד

Telab International :הוכון ע"י ACE BG · Advantecnia :תכרעמ

סירמוח תמישר

Bill of materials

SCALE · הדימ הנק	DATE · ךיראת	REV	ווילג
S/E	**15/10/2026**	**B**	**09**

בסיס: תינכות לכירדאה L5 (זוע דסמ / Triplet) · םירטמב תודימ

טמרופ A1 · הרודהמ B – לע התינכות תיתימאה

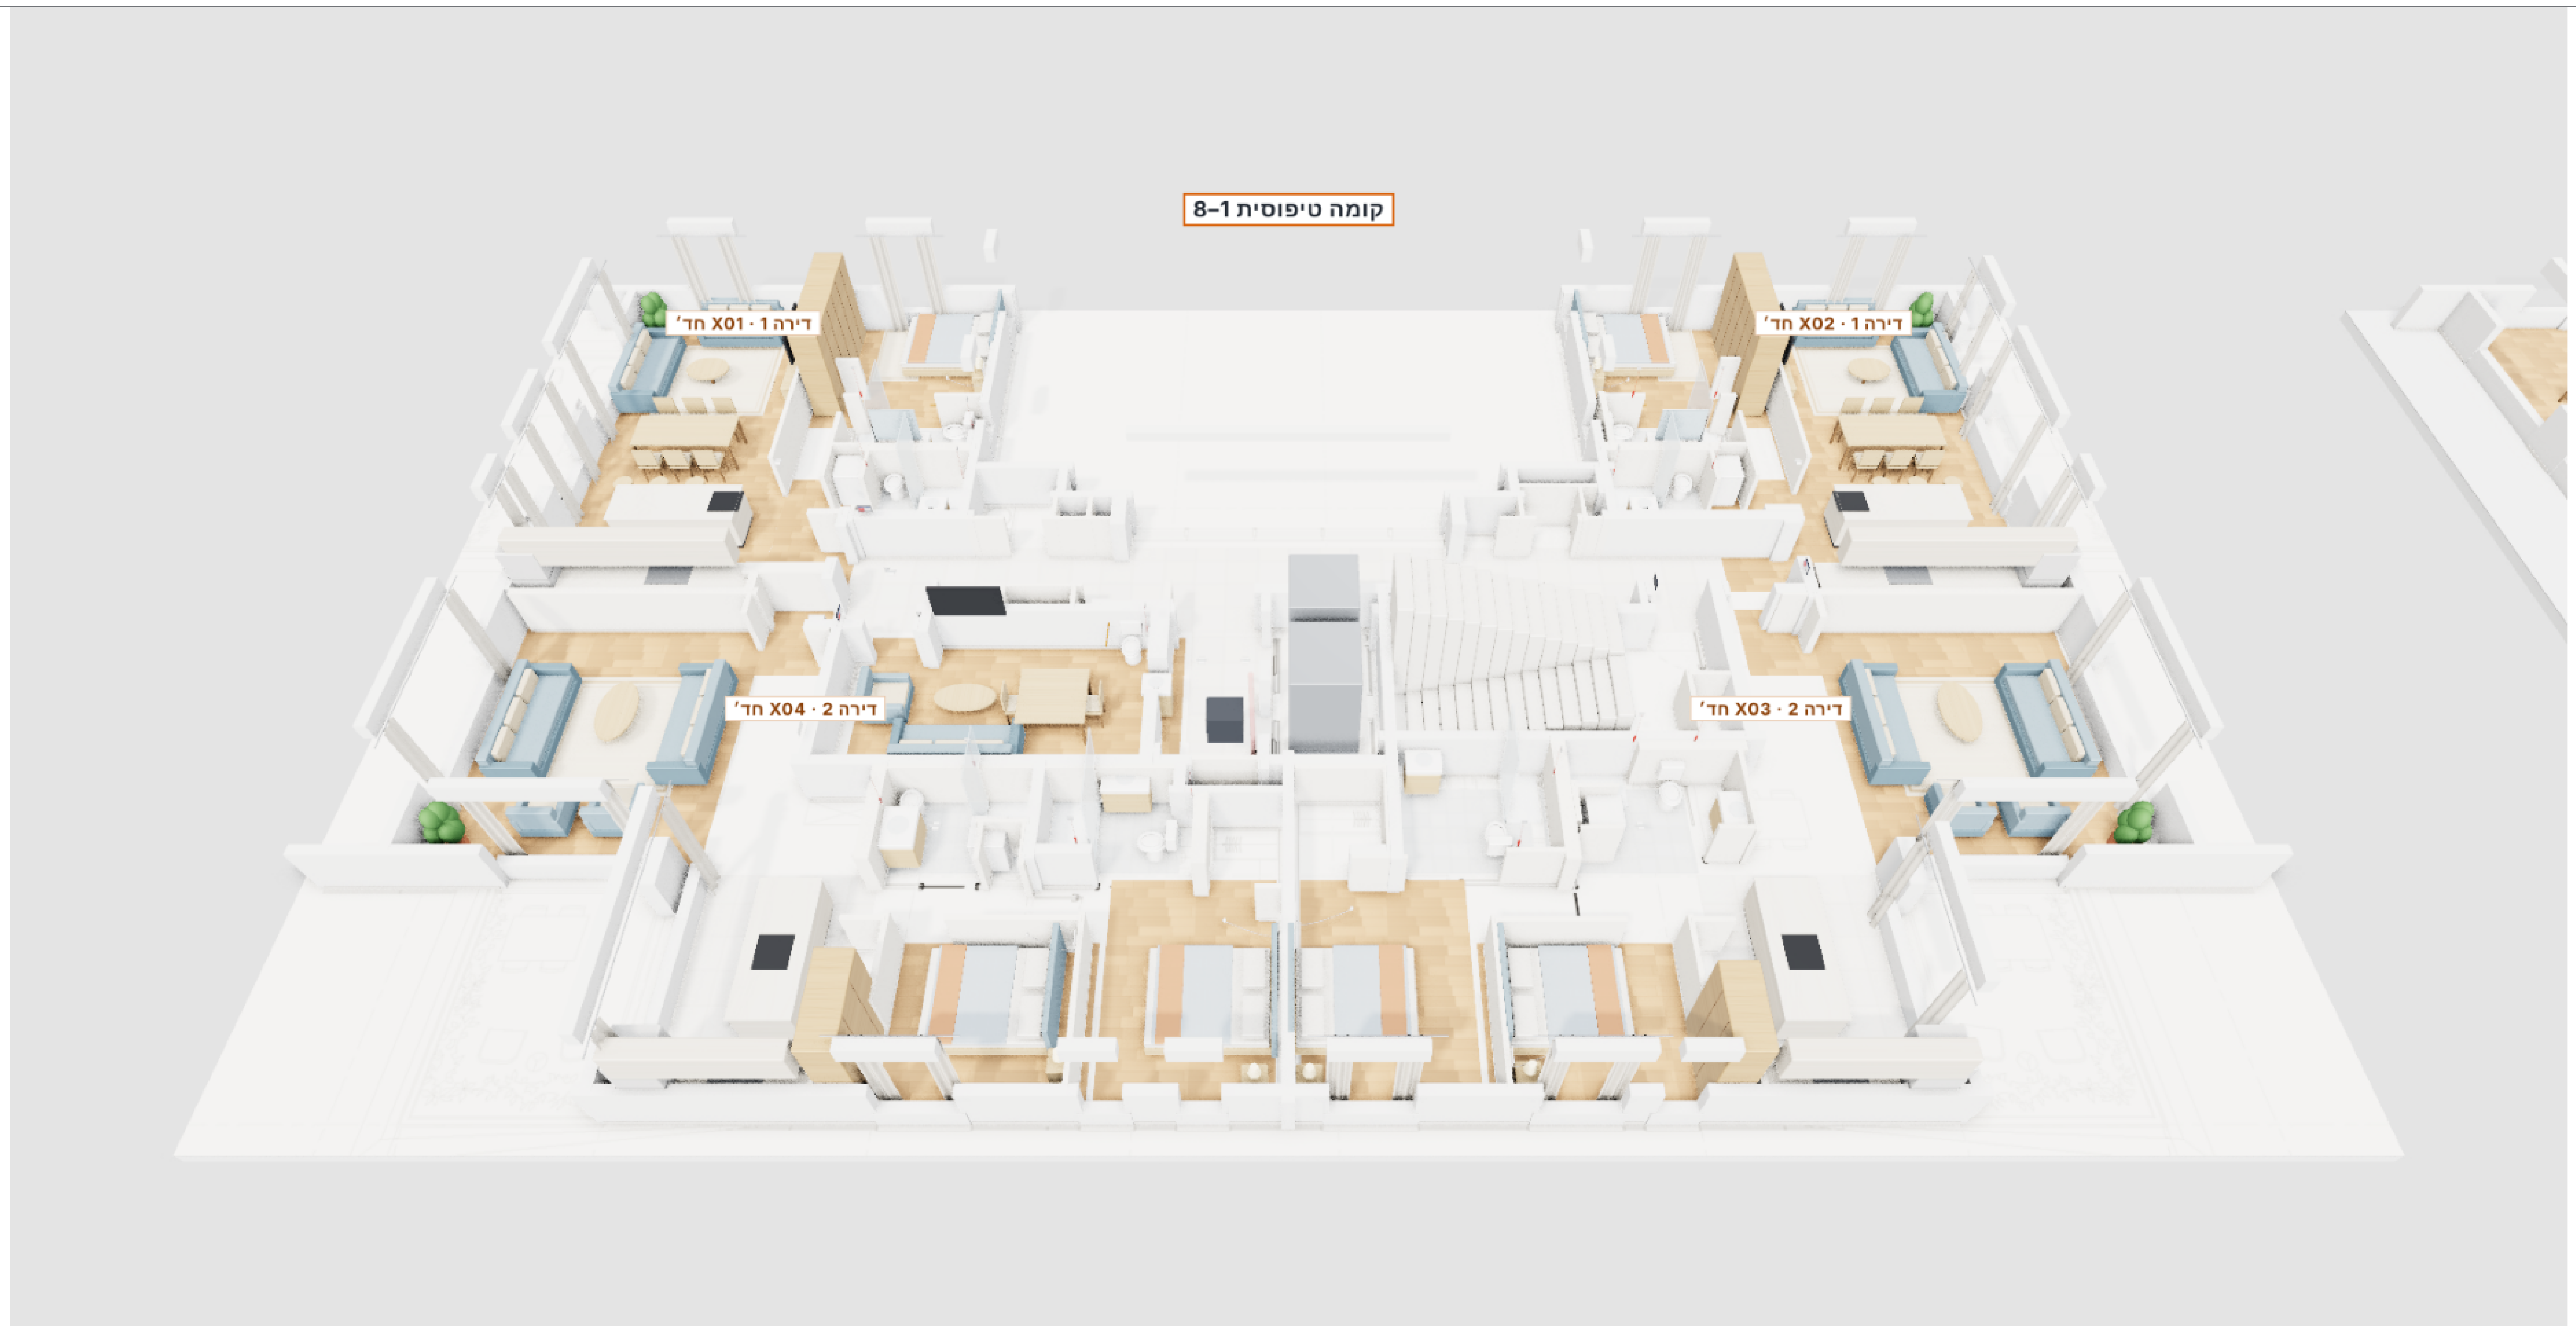

תוריד 4 – תיספיט המוק · א

הסינכב טלבאט · ב

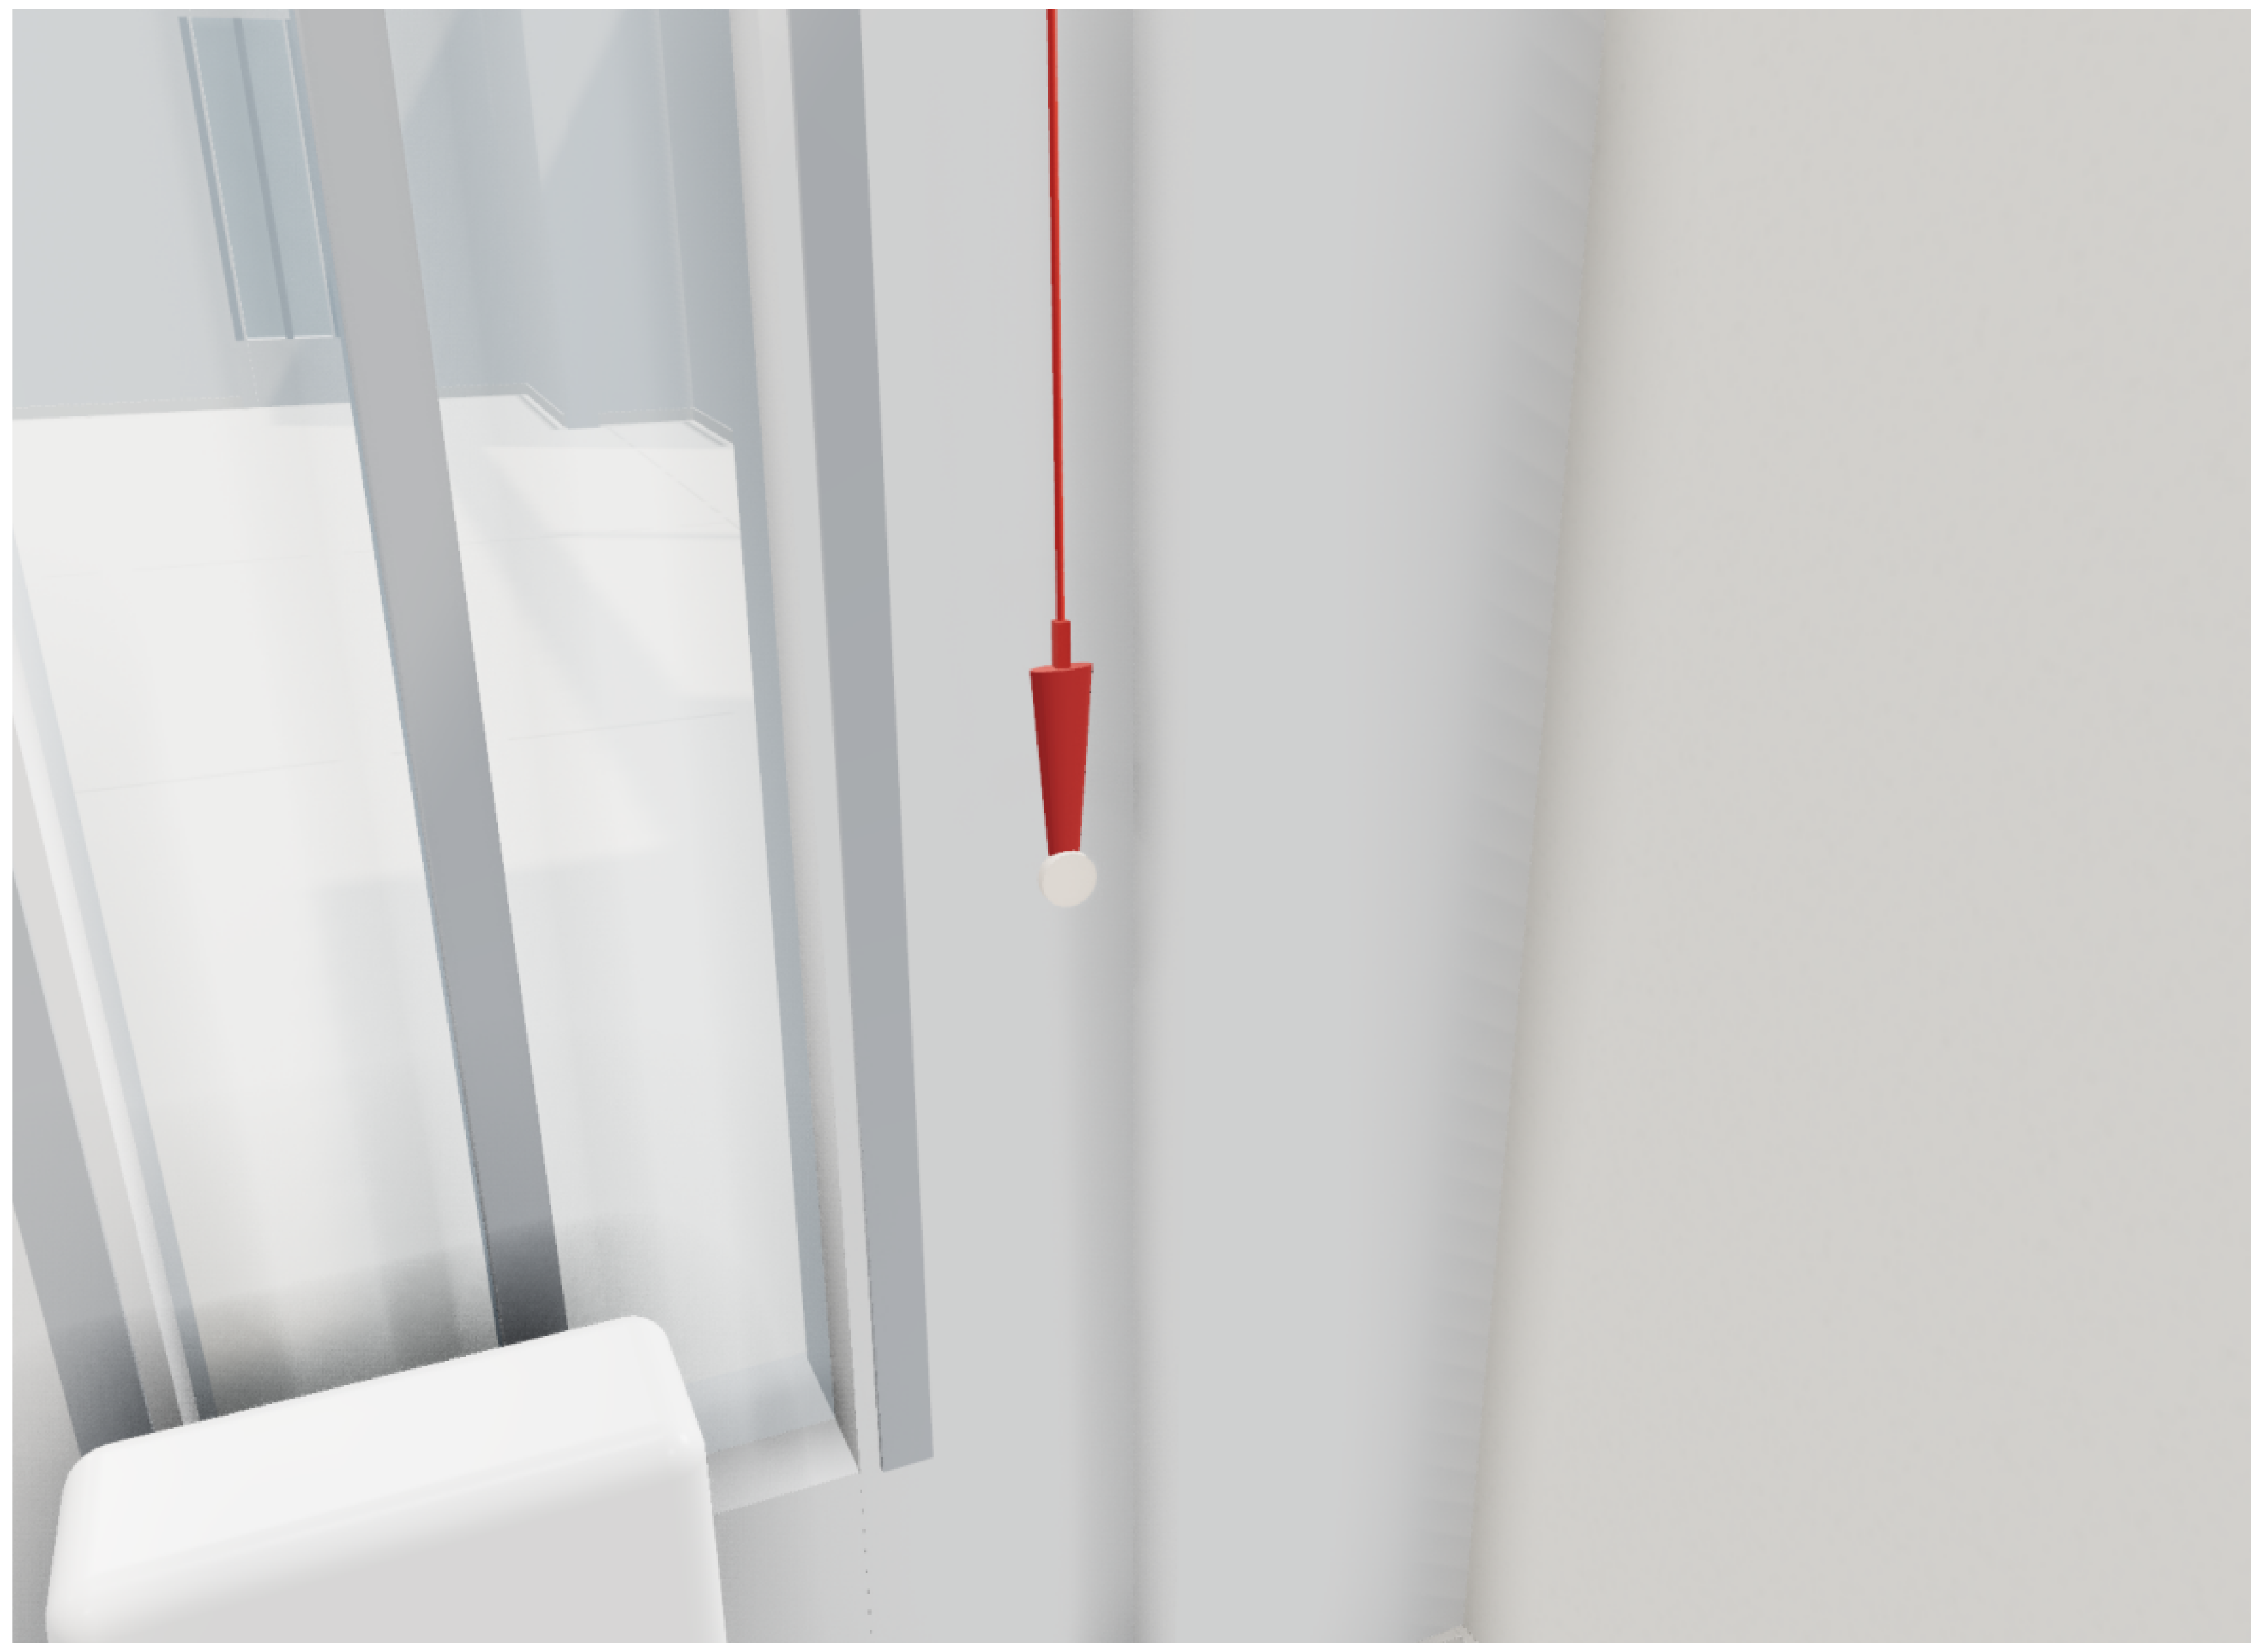

תחלקמבו הלסאב לבח תוכישמ – הצחר רדח · ד

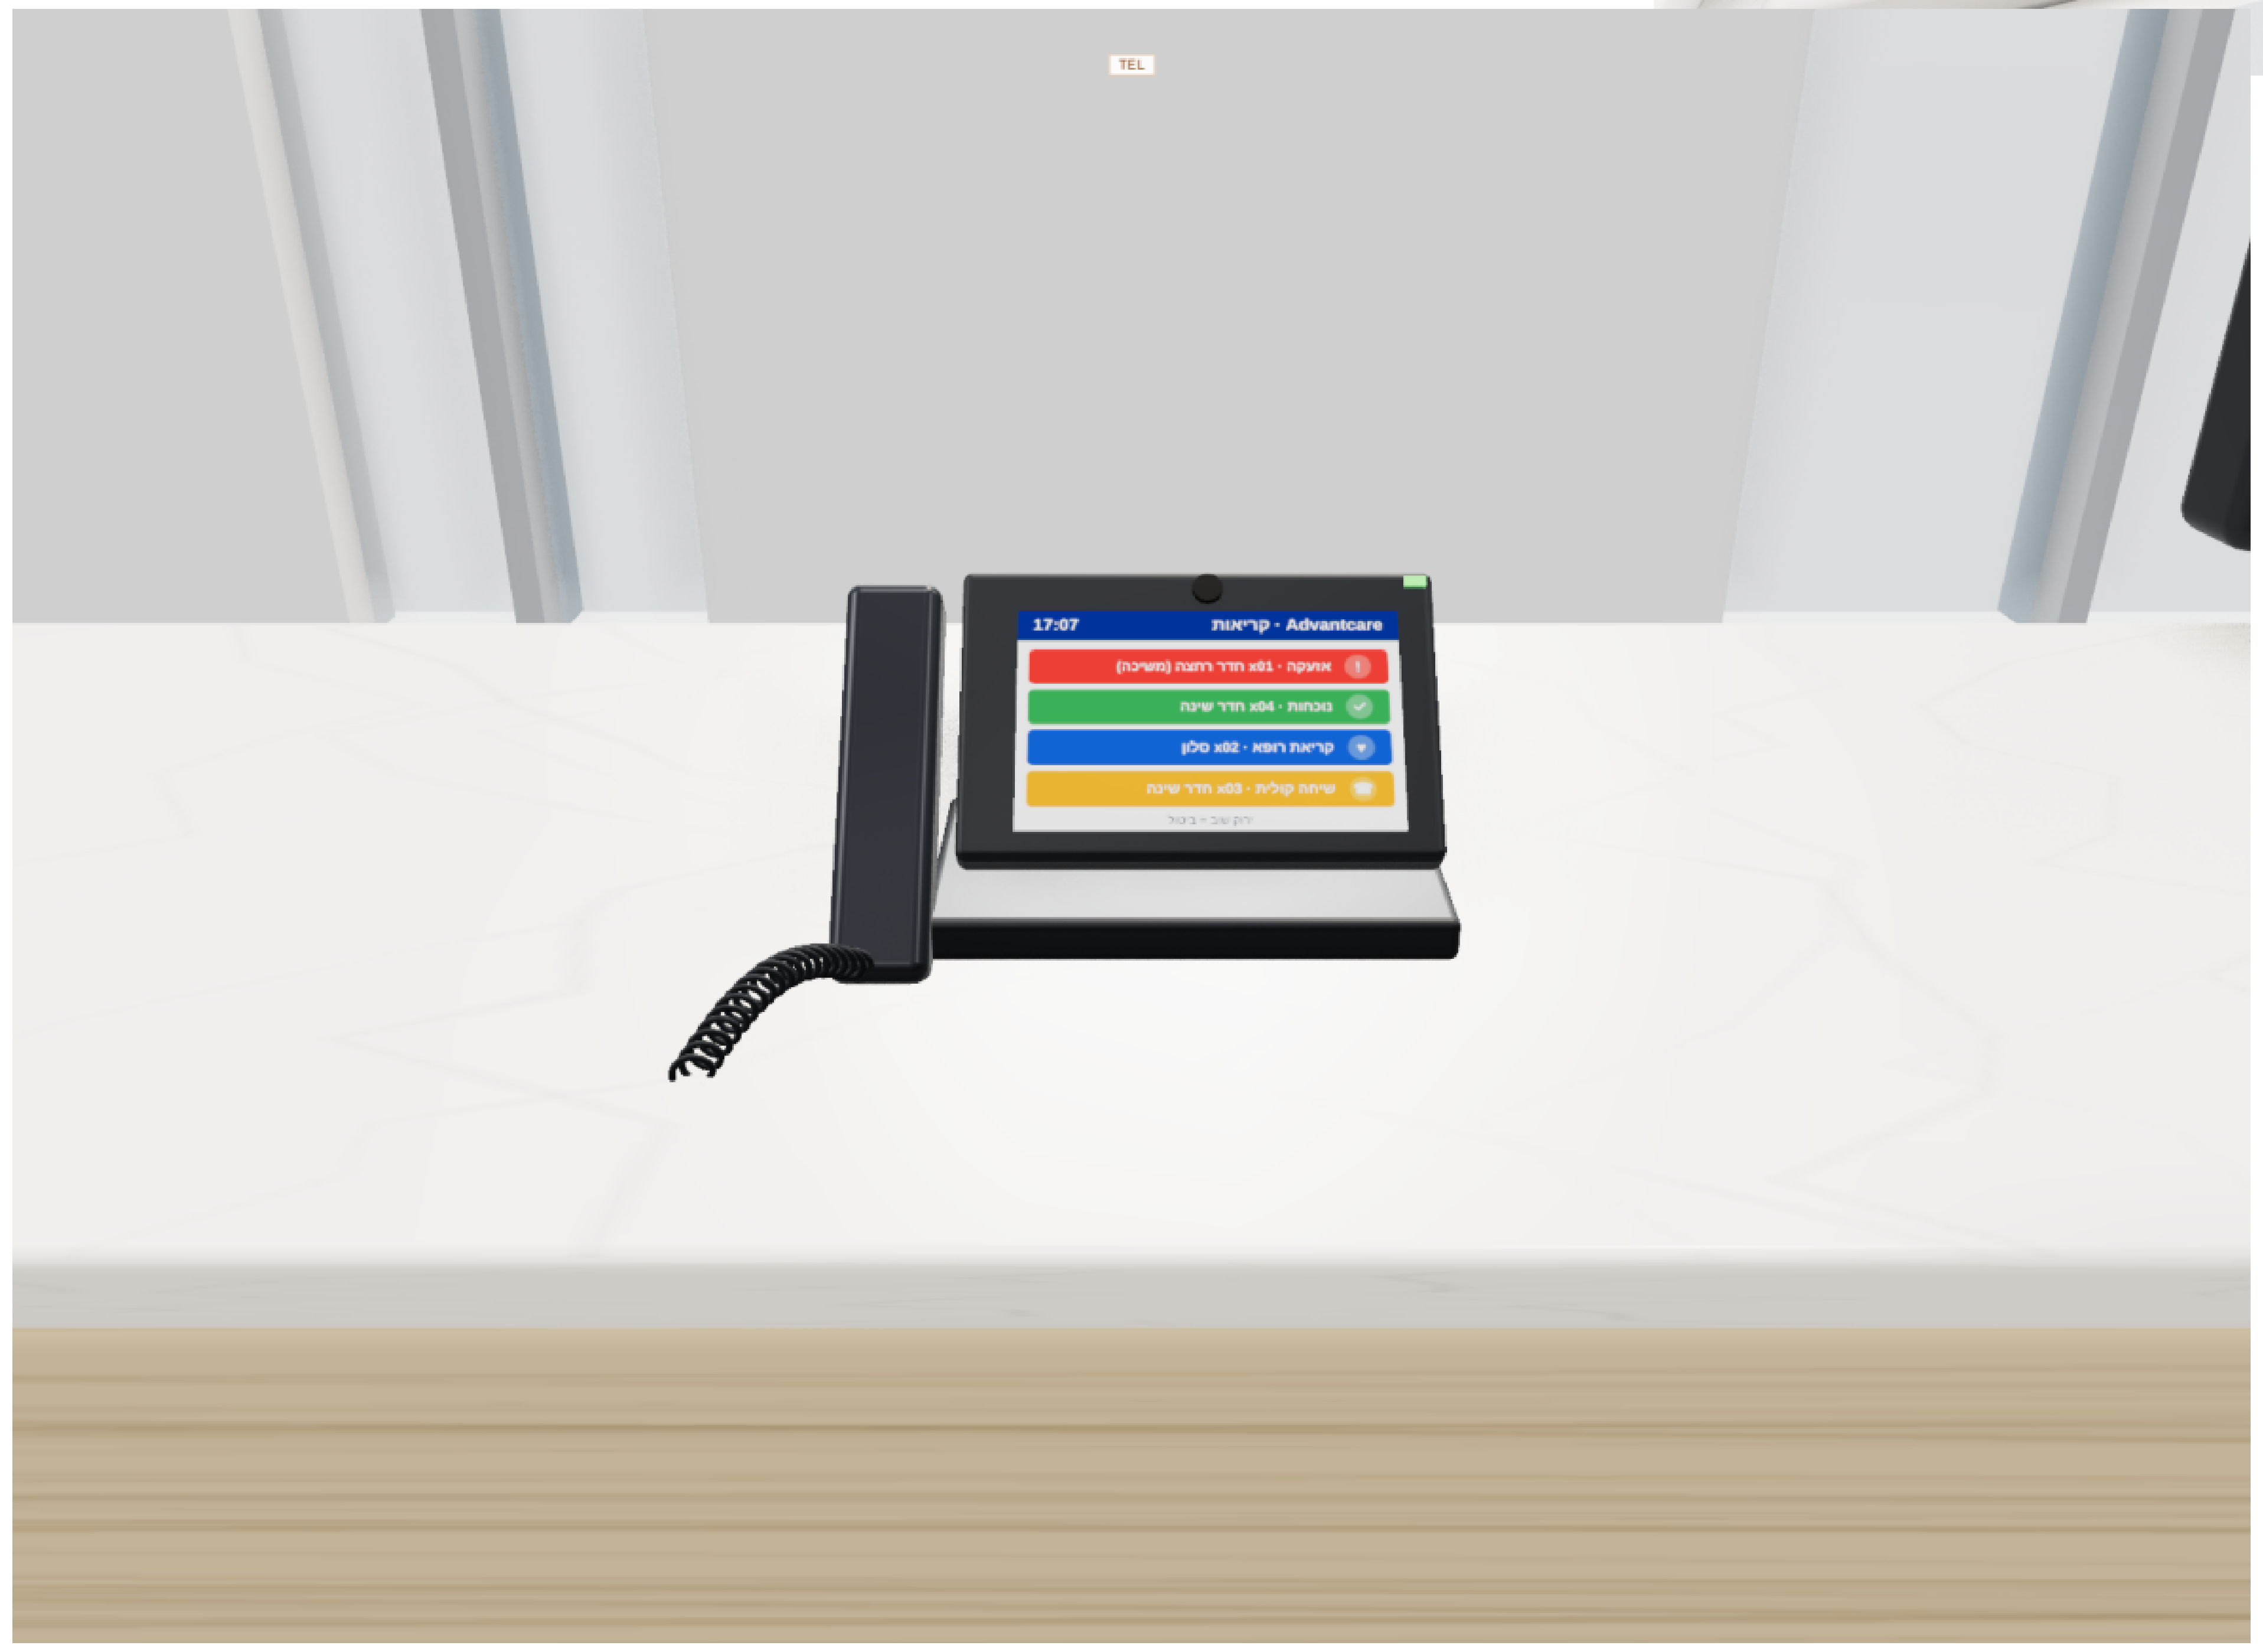

17:07 קריאות · Advantcare
אזעקה · x01 חדר רחצה (משיכה)
נוכחות · x04 חדר שינה
קריאת רופא · x02 סלון
שיחה קולית · x03 חדר שינה

תוחא תדמע – עקרק · ה

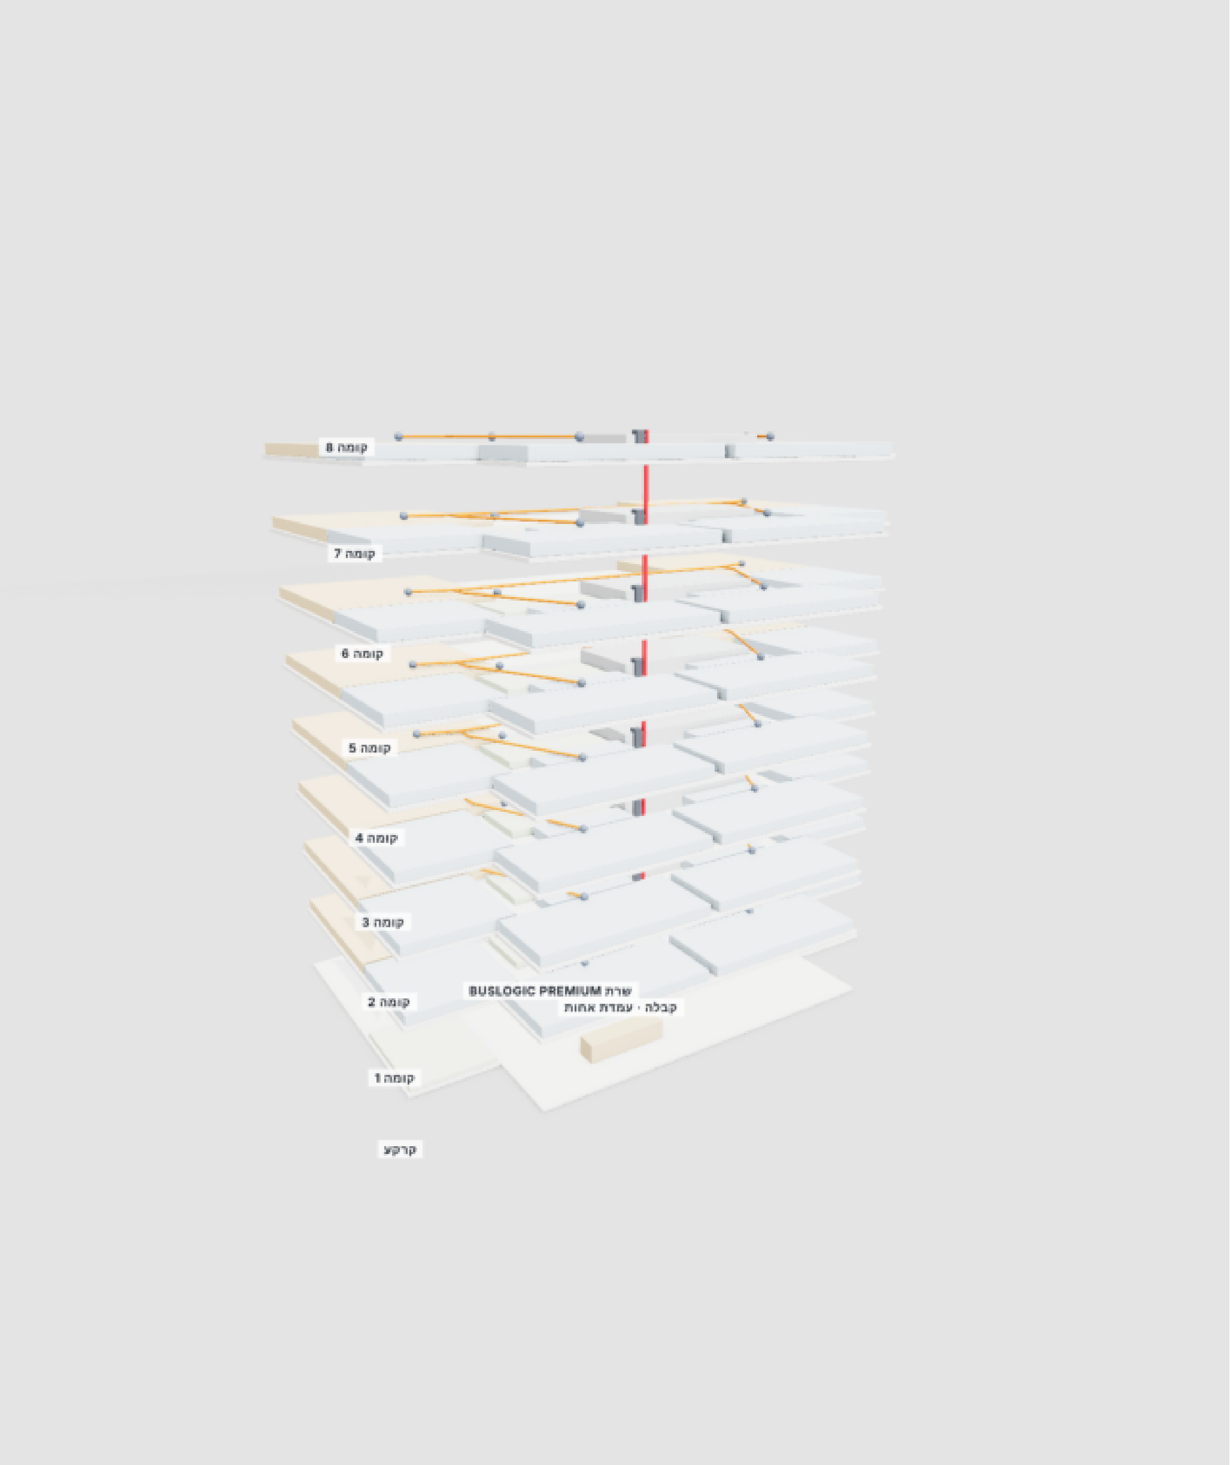

תומוק 8 + עקרק ןיינב · ו

ןגומ רויד · ןוכיתה םי ילדגמ

תוריד 32 · תומוק 8 + עקרק – תוחא תאירק

Telab International :יי"ע ןכוה ACE BG · Advantecnia :תכרעמ

סיידממ-תלת םיטבמ

3D views

SCALE · הדימ הנק
S/E

DATE · ךיראת
15/10/2026

REV
B

ןוילג
10

סיסב: לכירדאה תינכות L5 (זוע דסמ / Triplet) · םירטמב תודימ

טמרופ A1 · הרודהמ B – לע תינכותה תיתימאה

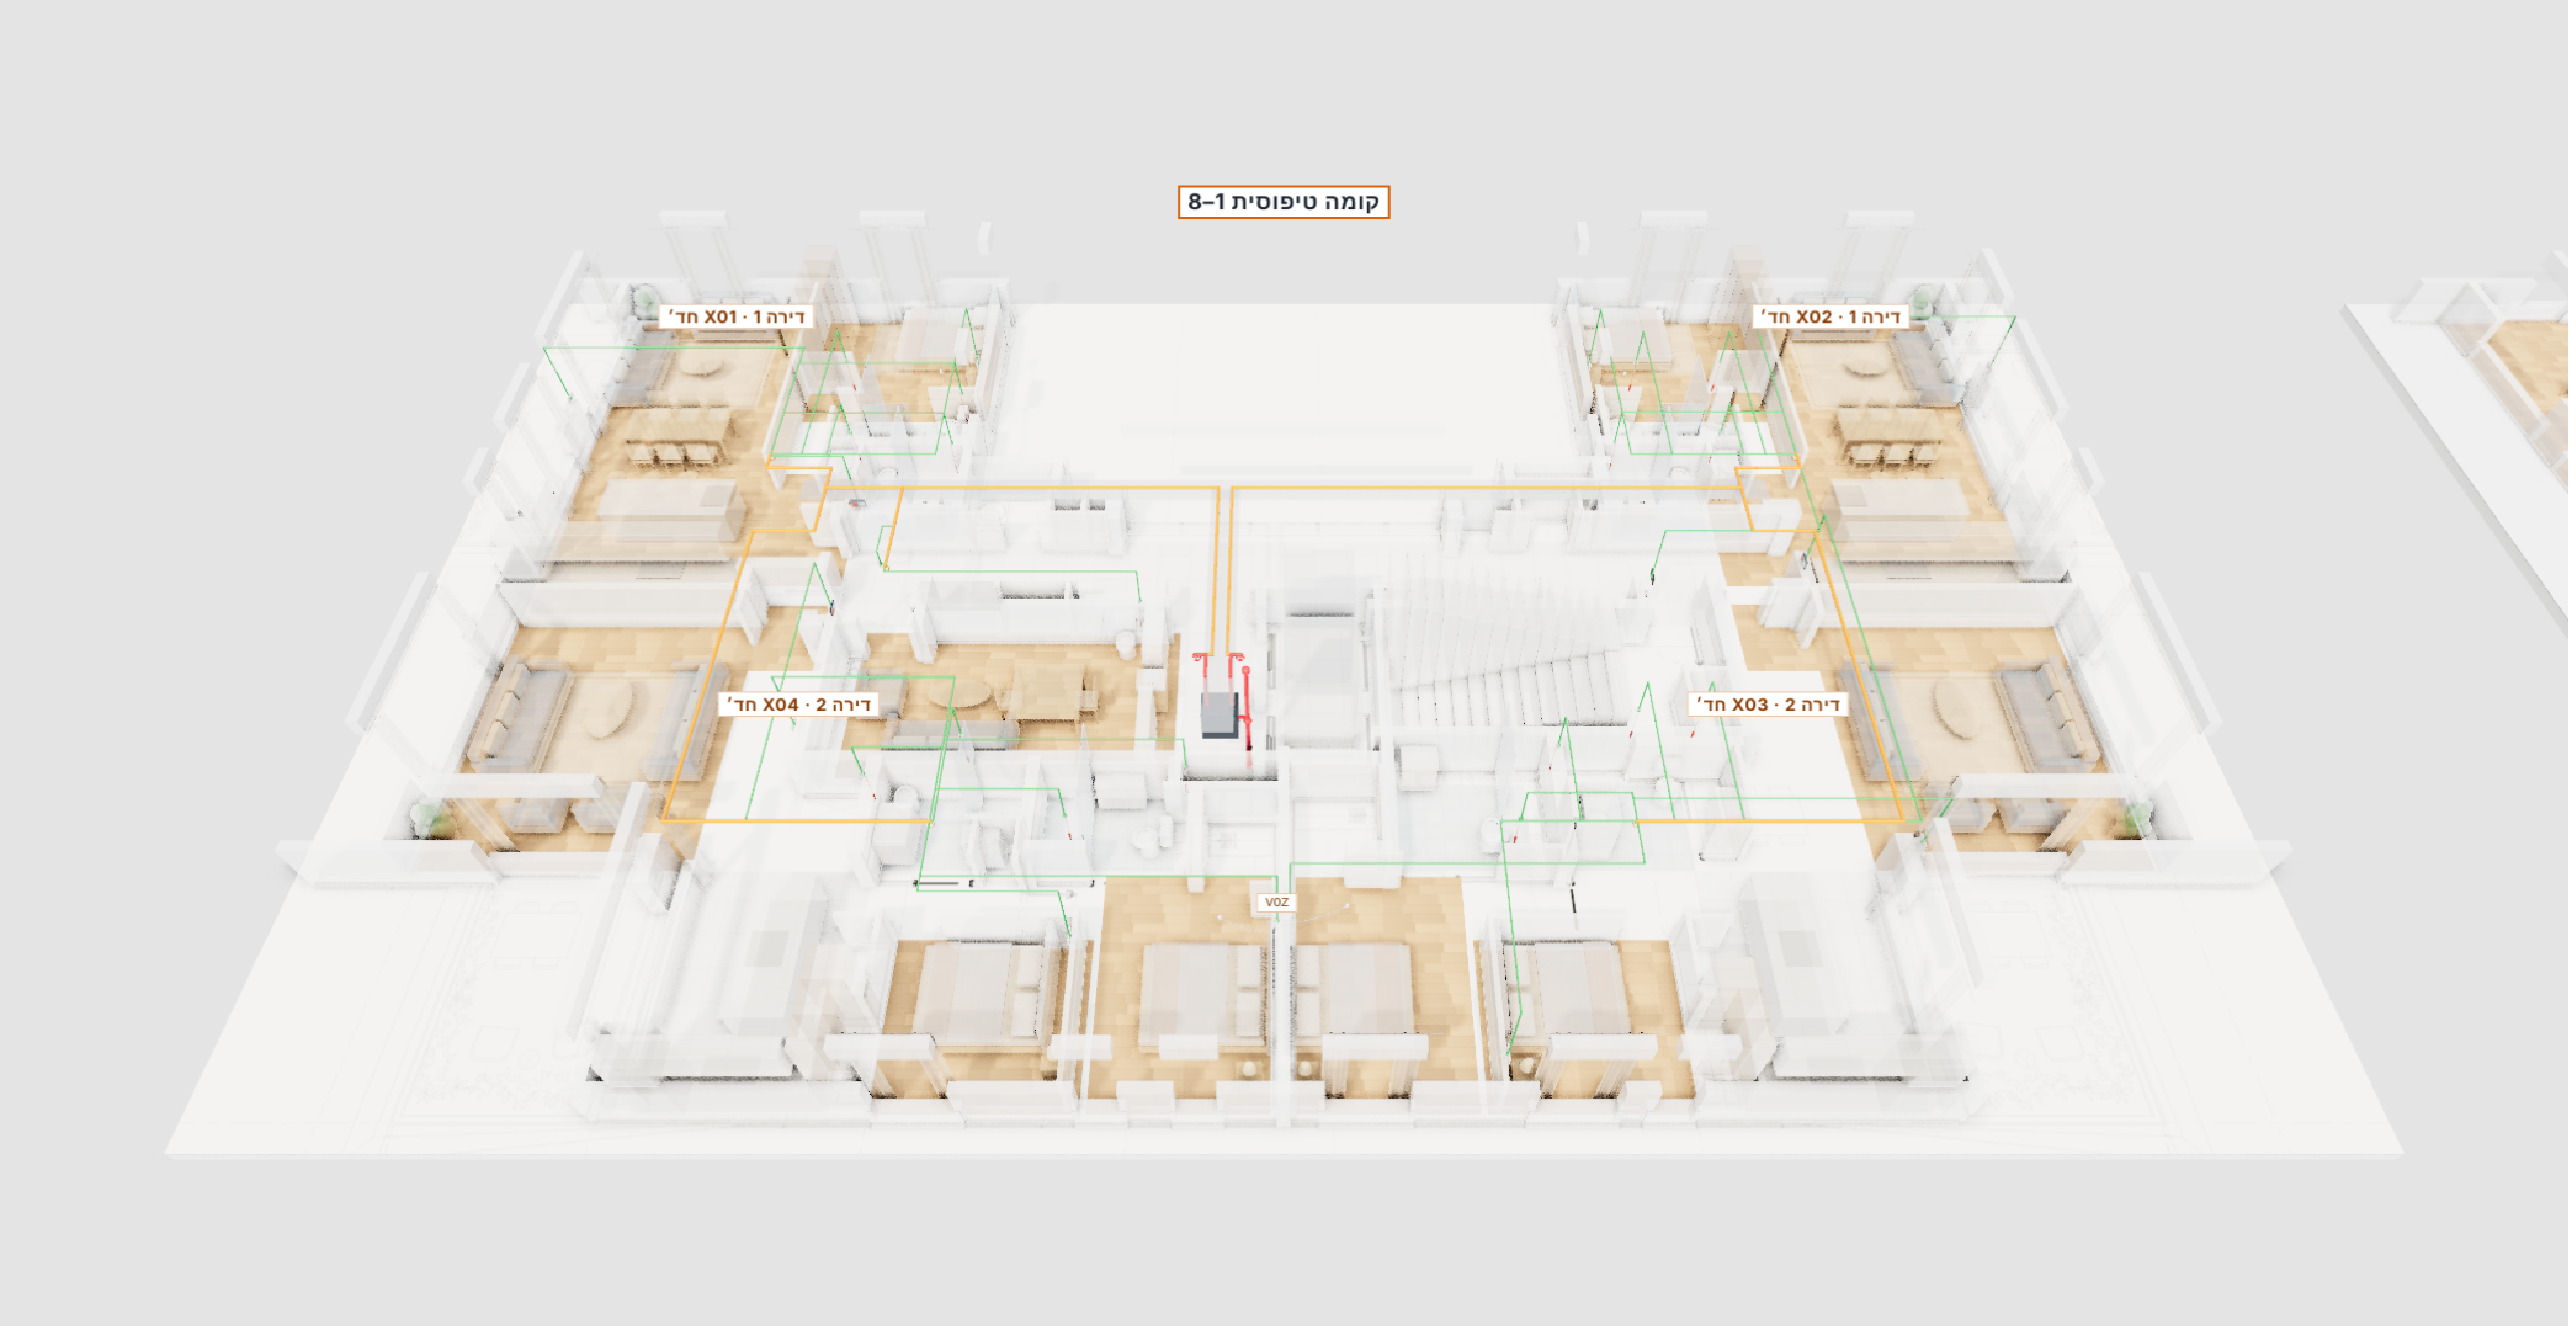

א · המוק תיסופיט – טוויח (ירוק רדיאלי · כתום שרשרת LCom · אדום רשת)

הלבקו יבול – עקרק תמוק · ב

םינצחל םע ילוק לנפ – ןולס · ג

COLOURS · COLORES · םיעבצ

🟩 Cat6 ילאידר: לכ ןקתה ← LCom לש הרידה
Cat6 radial: each device → apartment LCom · Cat6 ילאידר: לכ ןקתה ← LCom לש הרידה

🟧 Cat6 / Cat7 תרשרש: LCom ← LCom ← BoxCom הרקתב
Cat6 / Cat7 chain: LCom → LCom → BoxCom · Cat6 / Cat7 תרשרש: LCom ← LCom ← BoxCom

🟥 Cat6A / Cat7 תשר: BoxCom ← גתמ PoE ← דומע ← תרש עקרק
Cat6A / Cat7 network: BoxCom → switch → riser → GF server · Cat6A / Cat7 תשר: BoxCom ← גתמ ← דומע ← תרש

ןגומ רויד · ןוכיתה םי ילדגמ
תוריד 32 · תומוק 8 + עקרק – תוחא תאירק
Telab International :ןכוה ע"י   ACE BG · Advantecnia :תכרעמ

טוויח – םיידממ-תלת םיטבמ

3D views – wiring

SCALE · הדימ הנק	DATE · ךיראת	REV	ןוילג
S/E	15/10/2026	B	11

סיסב: תונכות תוירדאה לכ L5 (םסד גוז / Triplet) · םירטמב תודימ
טמרופ A1 · הרודהמ B – לע תונכותה תויתימאה

ילוק האירק לנפ – ןולס · א

סגאו ילוק לנפ – הניש רדח · ב

תכישמ – הצחר רדח · ג SOS

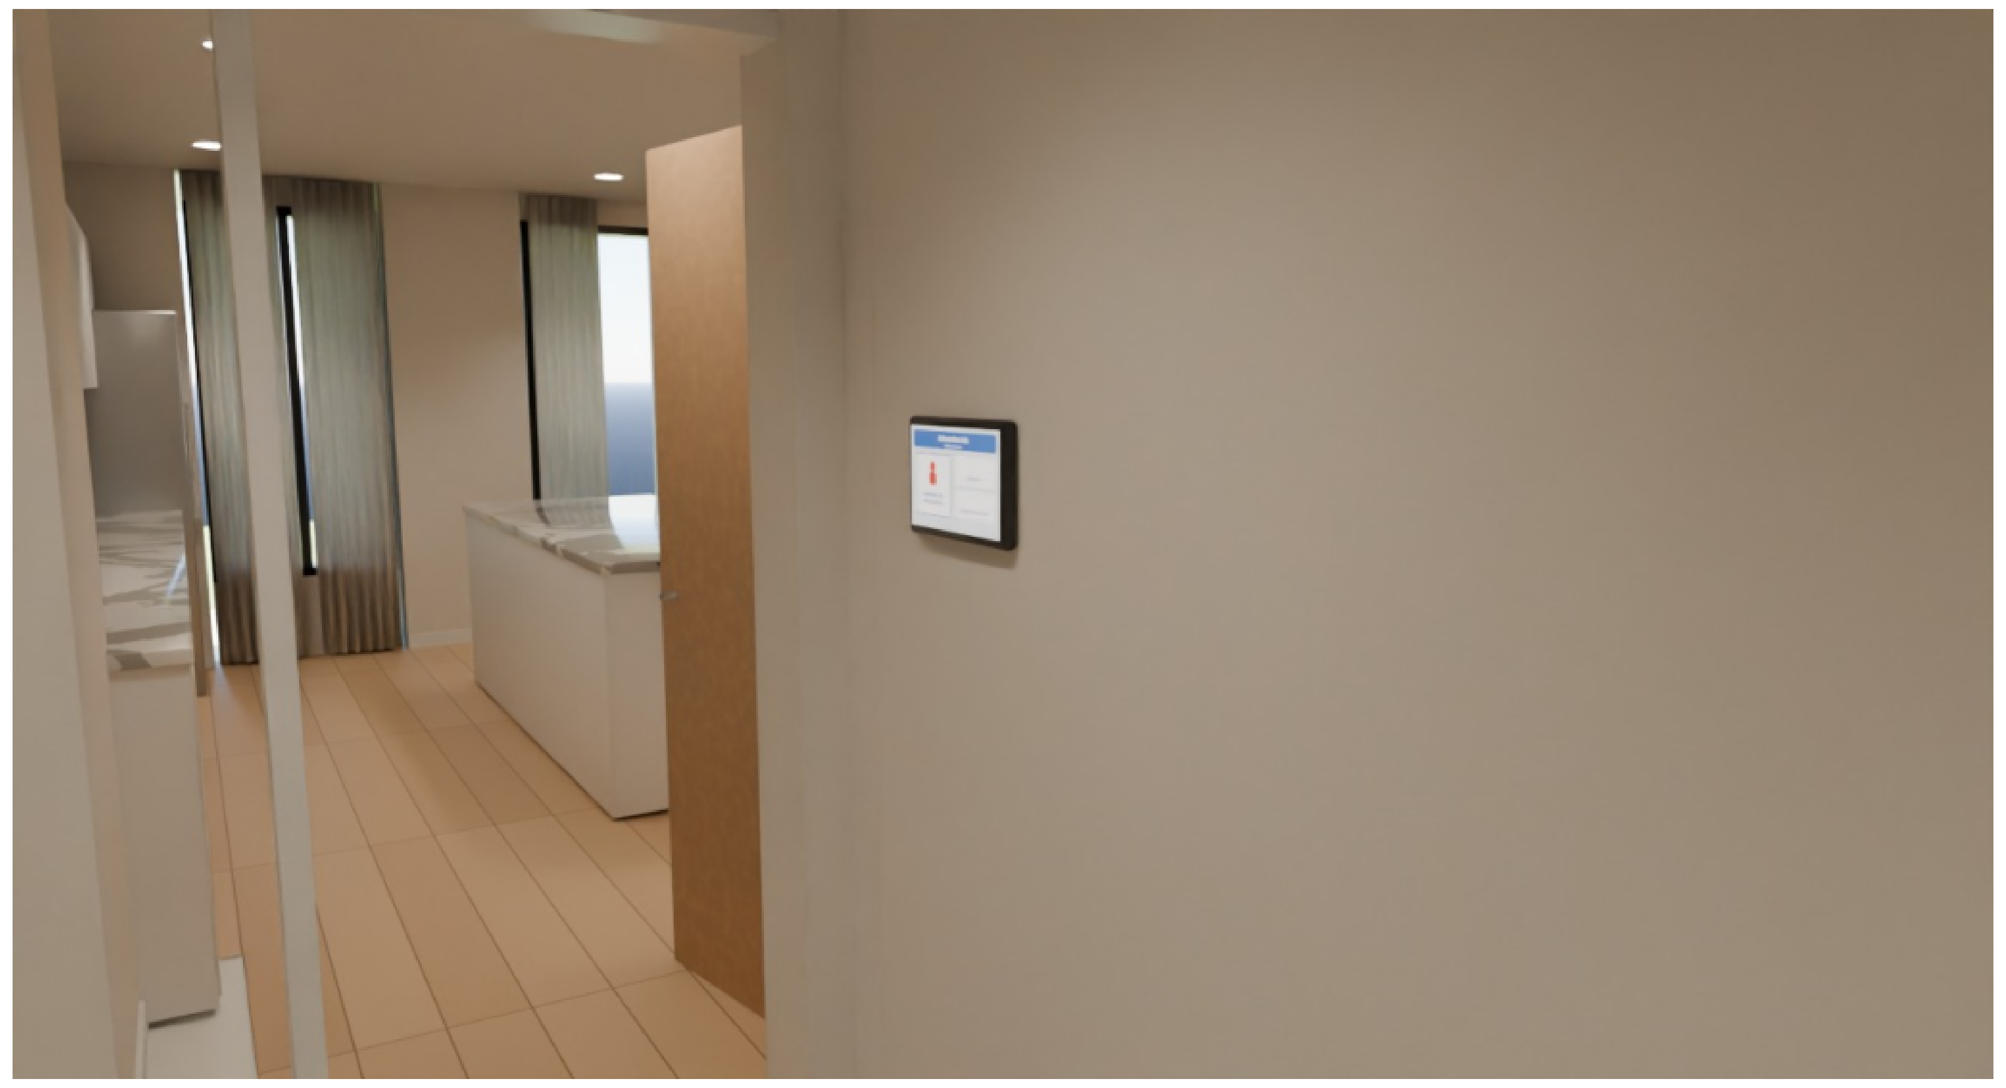

תלדב טלבאט – הסינכ · ד

םיירוביצ םיתוריש – ךתושמ רדח · ה

Grandstream ןופלט – תוחא תדמע · ו

ןגומ רויד · ןוכיתה םי ילדגמ

תוריד 32 · תומוק 8 + עקרק – תוחא תאירק

Telab International :י"ע ןכוה   ACE BG · Advantecnia :תכרעמ

םייטסילאירוטופ םירודניר

Photorealistic renders

SCALE · הדימ הנק	DATE · ךיראת	REV	ןוילג
S/E	**15/10/2026**	**B**	**12**

סיסב: תינכות לכירדאה L5 (גוז םגד / Triplet) · םירטמב תודימ

טמרופ A1 · הרודהמ B – לע תינכותה תיתימאה