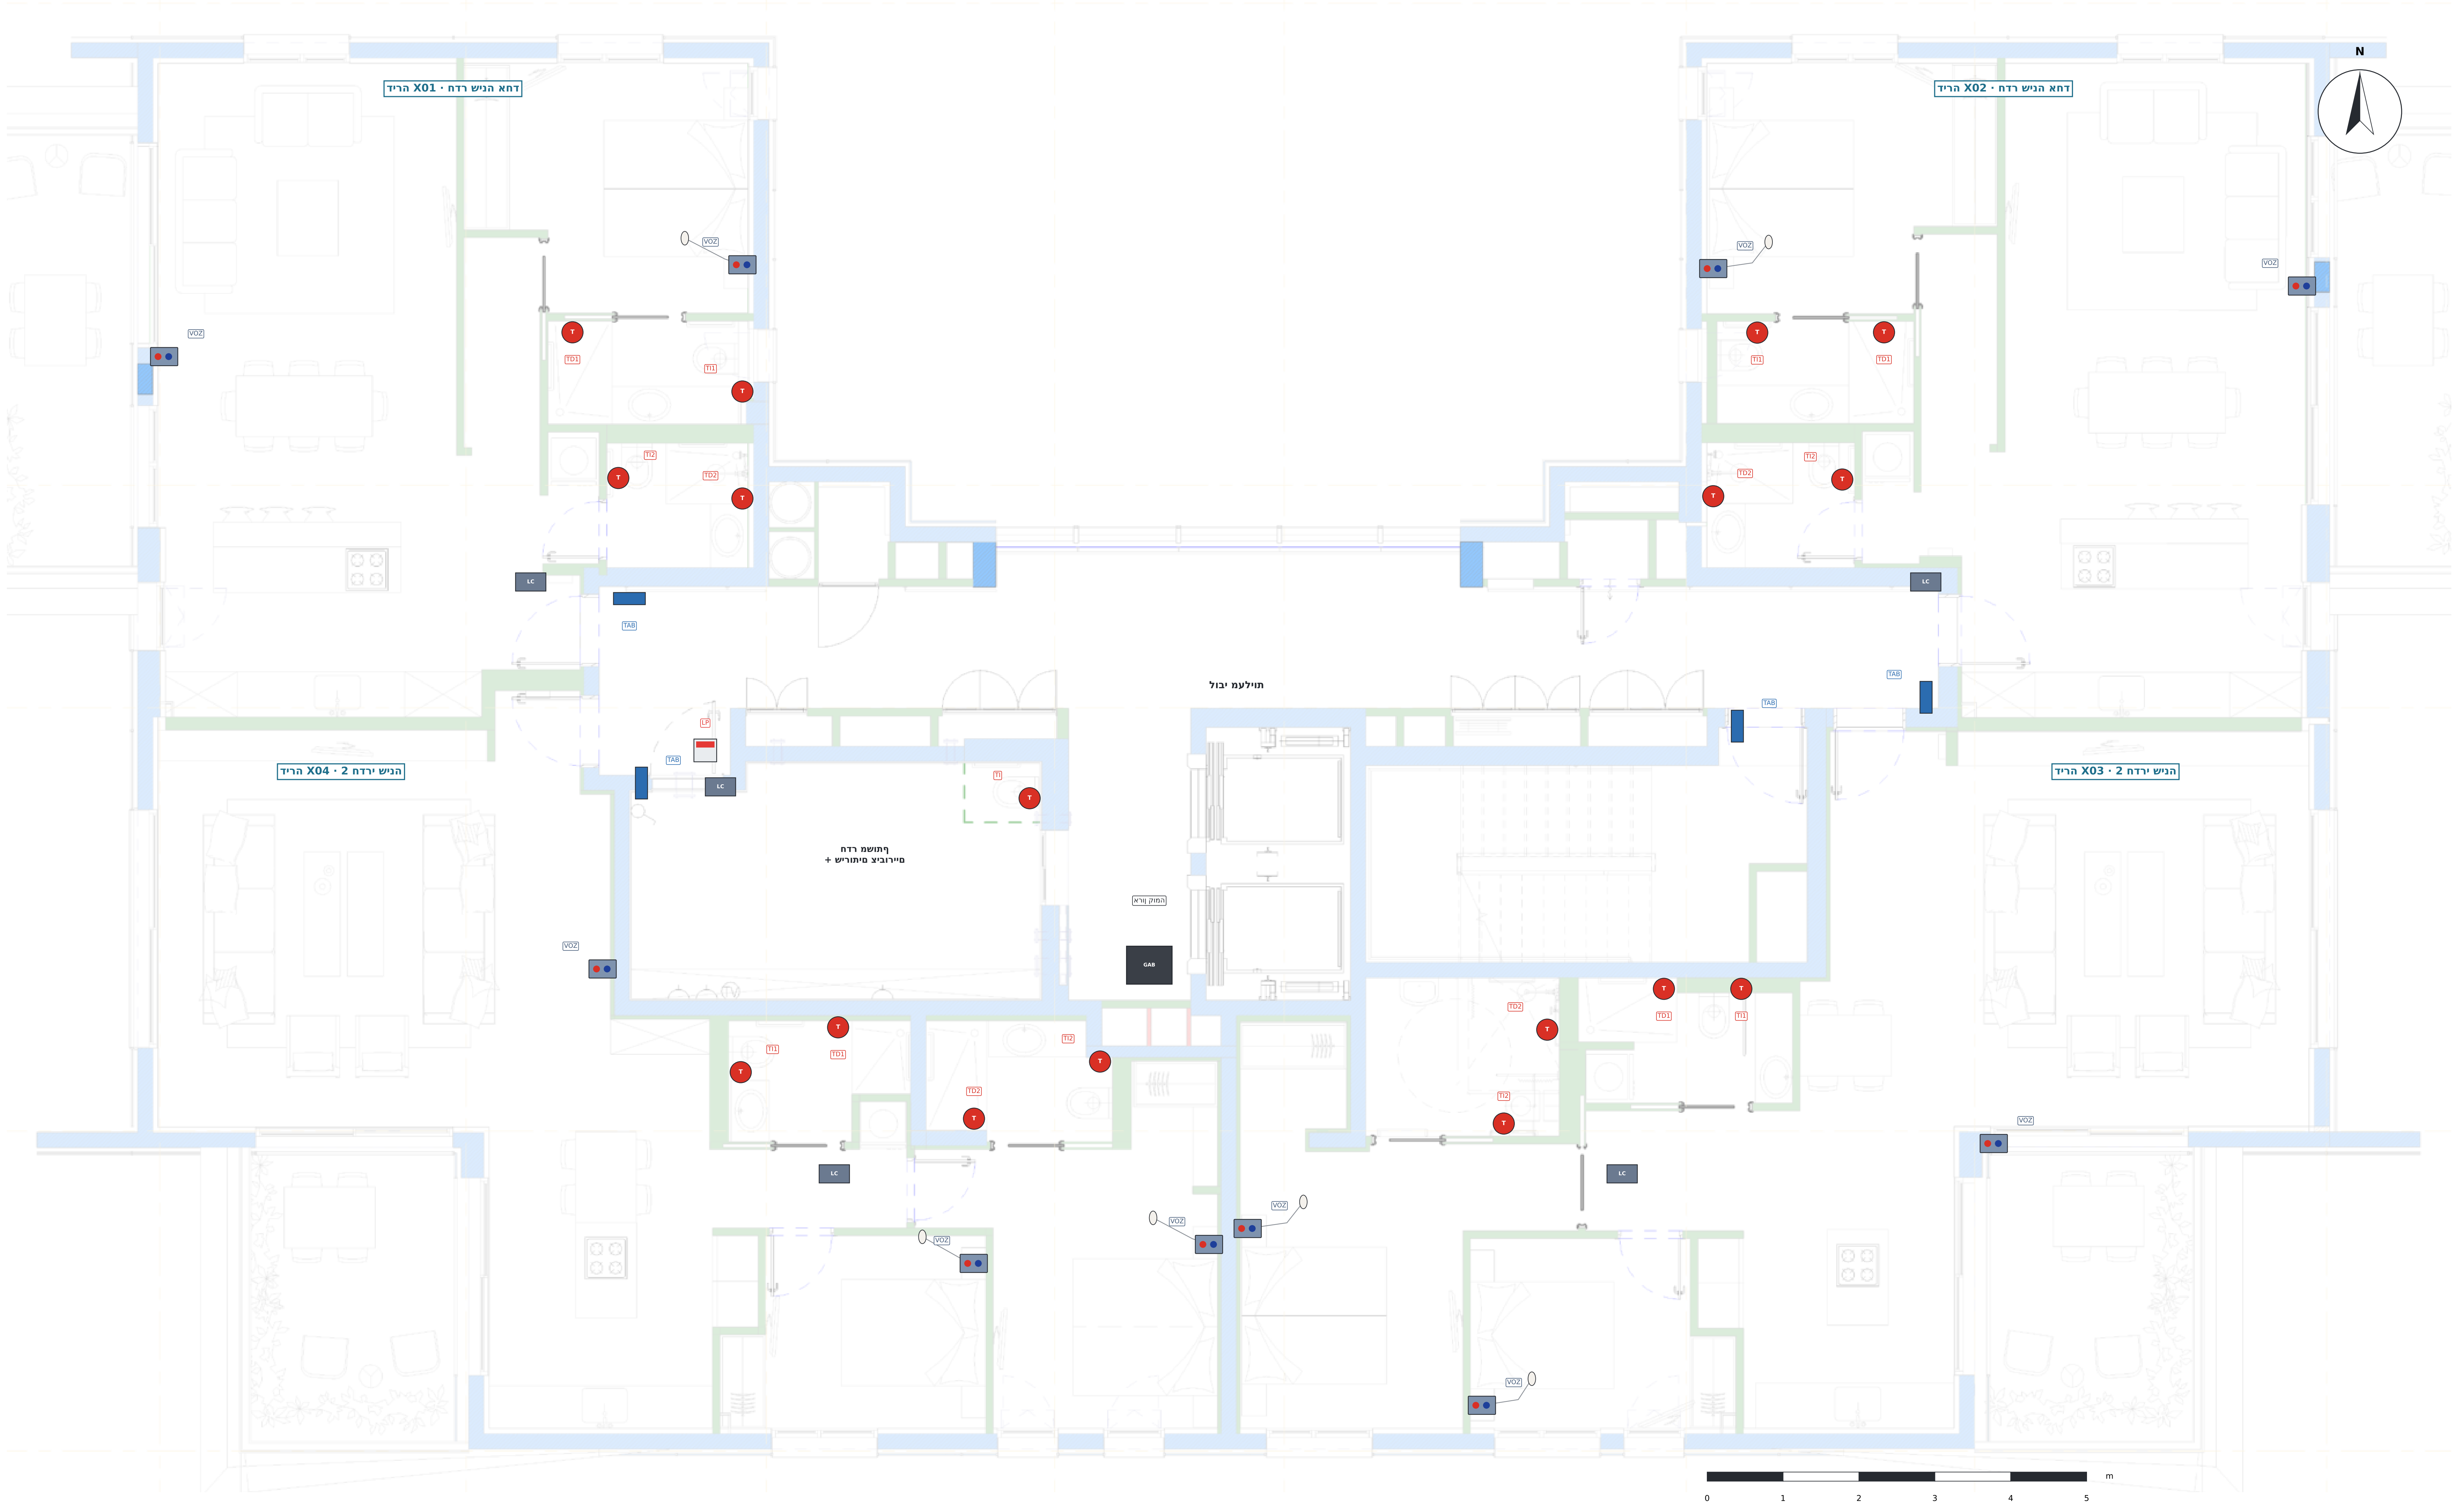
הריד X01 · הניש רדח דחא
הריד X02 · הניש רדח דחא
הריד X03 · 2 ירדח הניש
הריד X04 · 2 ירדח הניש
תוילעמ יבול
ףתושמ רדח
+ םיתוריש םירוביצ
ןורא המוק
GAB
N
VOZ
TAB
LC
LP
T
TI1
TD1
TI2
TD2
TI
0
1
2
3
4
5
m

DEVICES · EQUIPOS · דויצ

- ▬ TAB · הסינכב טלבאט (iPad / דיאורדנא) – האירק רובידו, הבוג 1.40 מ'
  Door tablet – call and voice · הסינכב טלבאט – האירק רובידו
- ●● VOZ · פנל ילוק עם לחצנים ACE82182451 – סלון וחדרי שינה, הבוג 1.20–1.30 מ'
  Voice panel with buttons – living room and bedrooms · לנפ ילוק עם םינצחל – ןולס ודחרי הניש
- ○ אגס האירק דיל הטימה (ירדחב הנישה)
  Call pear next to the bed (bedrooms) · אגס האירק דיל הטימה
- T TI / TD · משיכת חבל ACE40320303W – הלסא תחלקמו, הבוג 1.85 מ'
  Pull-cord – toilet and shower, h 1.85 m · לבח תכישמ – הלסא תחלקמו, הבוג 1.85 מ'
- 🟥 LP · תרונמ ןורדסמ ACE41020309 – מעל דלת כל שירותים ציבוריים
  Corridor light – above each public toilet door · תרונמ ןורדסמ – לעמ תלד לכ םיתוריש םיירוביצ
- LC LC · LCom ACE71610003 – זכרת הרידה (הרקת)
  LCom – apartment hub (ceiling) · LCom – זכרמ הרידה (הרקת)
- GAB PoE ACEUCM6302 12 + גתמU: 2 Buscomm ACE70810000 ןורא המוק
  Floor rack: 2 Buscomm + PoE switch · 2 :ןורא המוק Buscomm + גתמ PoE

תומוק 8 × המוקל תויומכ

דוק	ןקתה	המוקל	תומוק 8
TAB	הסינכב טלבאט	4	32
VOZ	םינצחל םע ילוק לנפ	10	80
TI/TD	משיכת חבל (הלסא + תחלקמ)	17	136
LP	תרונמ ןורדסמ (םיתוריש םיירוביצ)	1	8
LC	LCom	5	40
BC	Buscomm	2	16
SW	PoE גתמ	1	8

NOTES · תורעה

1. סיסב: תוינכות תילכירדא L5 (המוק תיסופיט) – 8 תומוקה תוהז: 4 תוריד המוקב, 32 ךסב לוכה.
2. תוריד x01 ו-x02: רדח הניש דחא, ןולס םע חבטמ ו-2 ירדח הצחר. תוריד x03 ו-x04: 2 ירדח הניש ו-2 ירדח הצחר.
3. טלבאט הסינכב לכל הריד (iPad / דיאורדנא) לקריאה רובידלו םע תוחאה.
4. לנפ ילוק םע םינצחל (ACE82182451) ןולסב ובכל רדח הניש; רדחב הנישה םע אגס דיל הטימה.
5. תוכישמ לבח (ACE40320303W) בלסאה ובמקלחת בכל רדח הצחרה, הבוגב 1.85 מ'.
6. םיתוריש םיירוביצ לכב המוק רדחב המשותף: משיכת לבח + תרונמ ןורדסמ לעמ הלדת. םע 2 בקרקע – 10 םיתוריש םיירוביצ.
7. ןורא המוק ןורדסמב השירות דיל תוילעמה (Tripp Lite 12U, ה תוכנותב ומכ-IT).
8. םימוקימ יפל םינומיס הלוקח תוכנותב L2 (nt = לנפ ילוק, tab = טלבאט): וארו ןויליג 03.

הנקתה יהבוג

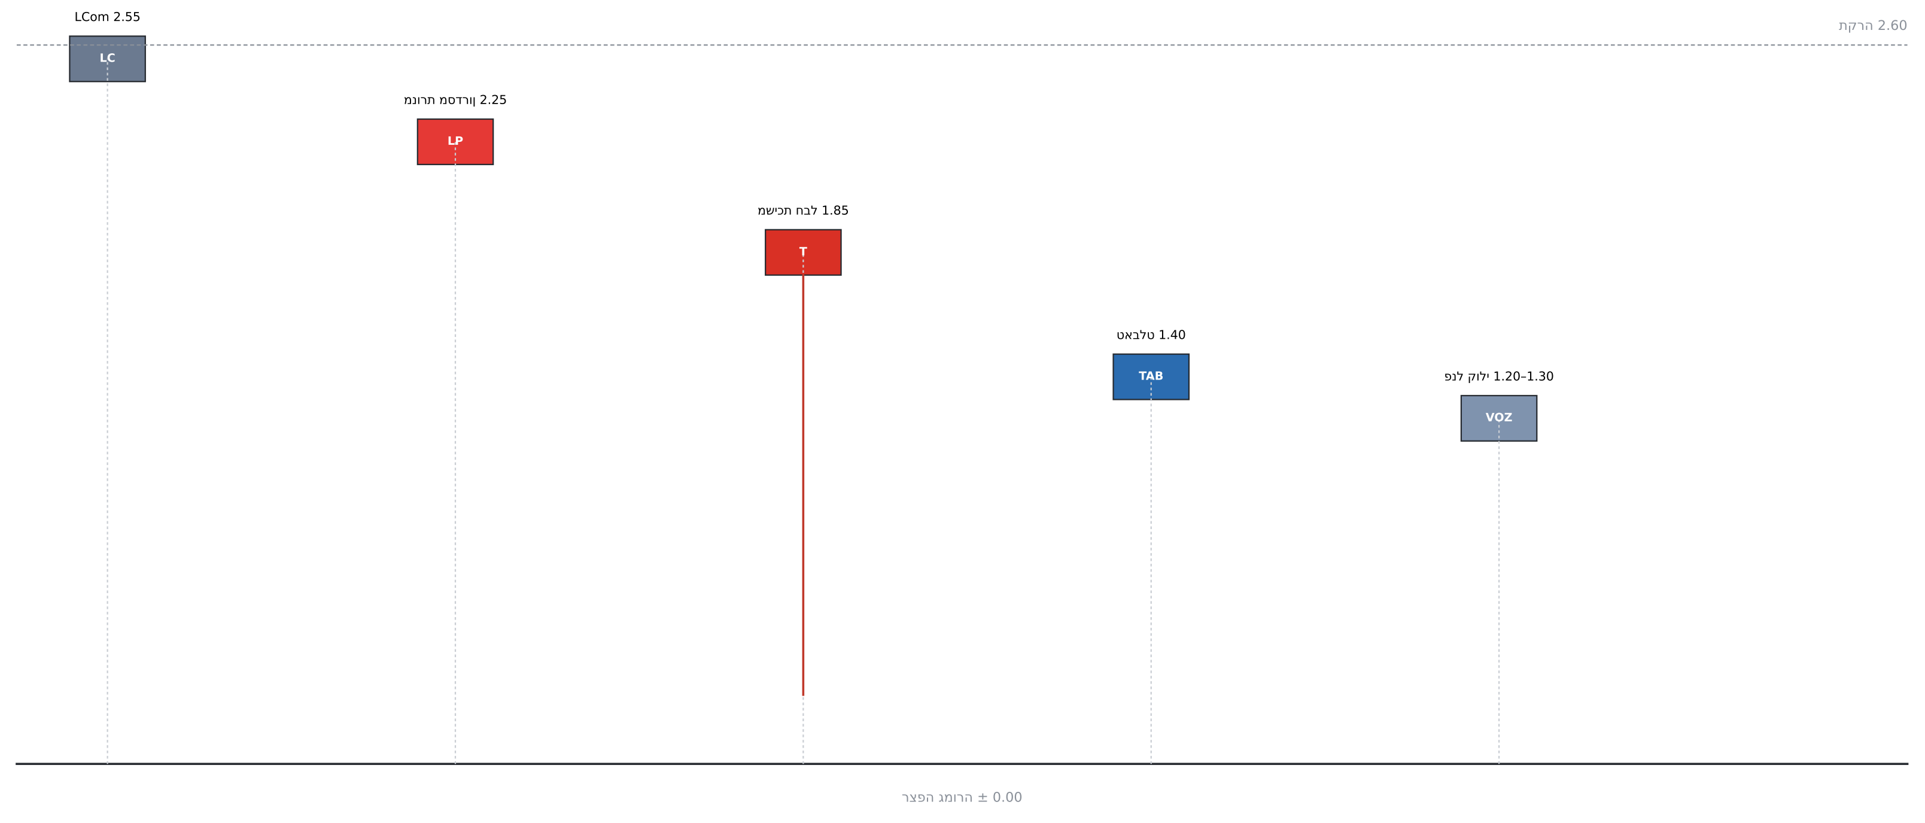
LCom 2.55
LC
הרקת 2.60
ןורדסמ תרונמ 2.25
LP
לבח תכישמ 1.85
T
טלבאט 1.40
TAB
לפנ ילוק 1.20–1.30
VOZ
הפצר הרומג ± 0.00

שירותים קריאת אחות
לבח תכישמ

טבלט אנדרואיד קריאת אחות
Advantecnia
Llamada de enfermera
הסינכב טלבאט (iPad / דיאורדנא)

מנורה קריאת אחות
ןורדסמ תרונמ

פנל קריאת אחות
םינצחל םע ילוק לנפ

ןגומ רויד · ןוכיתה םי ילדגמ
ןקריא תוחא – עקרק + 8 תומוק · 32 תוריד
Telab International :ןכוה ע"י   ACE BG · Advantecnia :תכרעמ

תוחא תאירק · 1–8 תיסופיט המוק

Typical floor F1–F8 · nurse call

SCALE · הדימ הנק	DATE · ךיראת	REV	ןוילג
1:60	15/10/2026	B	01

סיסב: תוינכות תילכירדא L5 (זוע דסמ / Triplet) · םירטמב תודימ
טמרופ A1 · הרודהמ B – לע תוינכותה תויתימאה

שירותים קריאת אחות

לבח תכישמ

דוק	**ACE40320303W**
מוקים	סיירוביצה םיתורישה 10-בו הצחר רדח לכב תחלקמו הלסא
הבוג	**1.85 מ'**
תומכ	**138**

1

טבלט אנדרואיד קריאת אחות

Advantecnia
04:56 a. m.
Llamada de enfermera
Hospital
Salud y bienestar

טאבלט בכנסיה (iPad / דיאורדנא)

דוק	**Advantecnia TV**
מוקים	בולבי, דיל תלד לכ הריד
הבוג	**1.40 מ'**
תומכ	**32**

2

מנורה קריאת אחות

ןורדסמ תרונמ

דוק	**ACE41020309**
מוקים	סיירוביצ םיתוריש לכ תלד לעמ
הבוג	**2.25 מ'**
תומכ	**10**

3

פנל קריאת אחות

םינצחל םע ילוק לנפ

דוק	**ACE82182451**
מוקים	ןולס וכל רדח הניש (בחר הנישה רדחב םע אגס)
הבוג	**1.20–1.30 מ'**
תומכ	**80**

4

NOTES · תורעה

/ ACE BG 1. לש סוחיי תונומת Advantecnia, םע תרתוכה ןהלש.

2. משיכת לבח: לבח אדוס םע תידי, הפצרהמ םג שיגנ.

3. רבדמו ארוק הסינכב טלבאטה םע תוחאה.

4. םיארוקשכ תקלדנ ןורדסמה תרונמ םיירוביצה םיתורישהמ.

5. האירק ןצחל שי לנפב, לוקמרו לוטיב ינצחל רובידל.

LCom :6. הריד לכב ףסונב ACE71610003 הרקתב.

7. בקרקע: ןופלט ינחלוש דיאורדנא ACE52190200 תוחאה תדמעב.

ןגומ רויד · ןוכיתה םי ילדגמ

תוריד 32 · תומוק 8 + עקרק – תוחא תאירק

תכרעמ: ACE BG · Advantecnia   Telab International :ןכוה ע"י

תכרעמה דויצ

System devices

SCALE · הדימ הנק	DATE · ךיראת	REV	ןוילג
S/E	**15/10/2026**	**B**	**02**

סיסב: תינכות לכירדאה L5 (זוג דסמ / Triplet) · םירטמב תודימ

טמרופ A1 · הרודהמ B – לע התינכותה תיתימאה

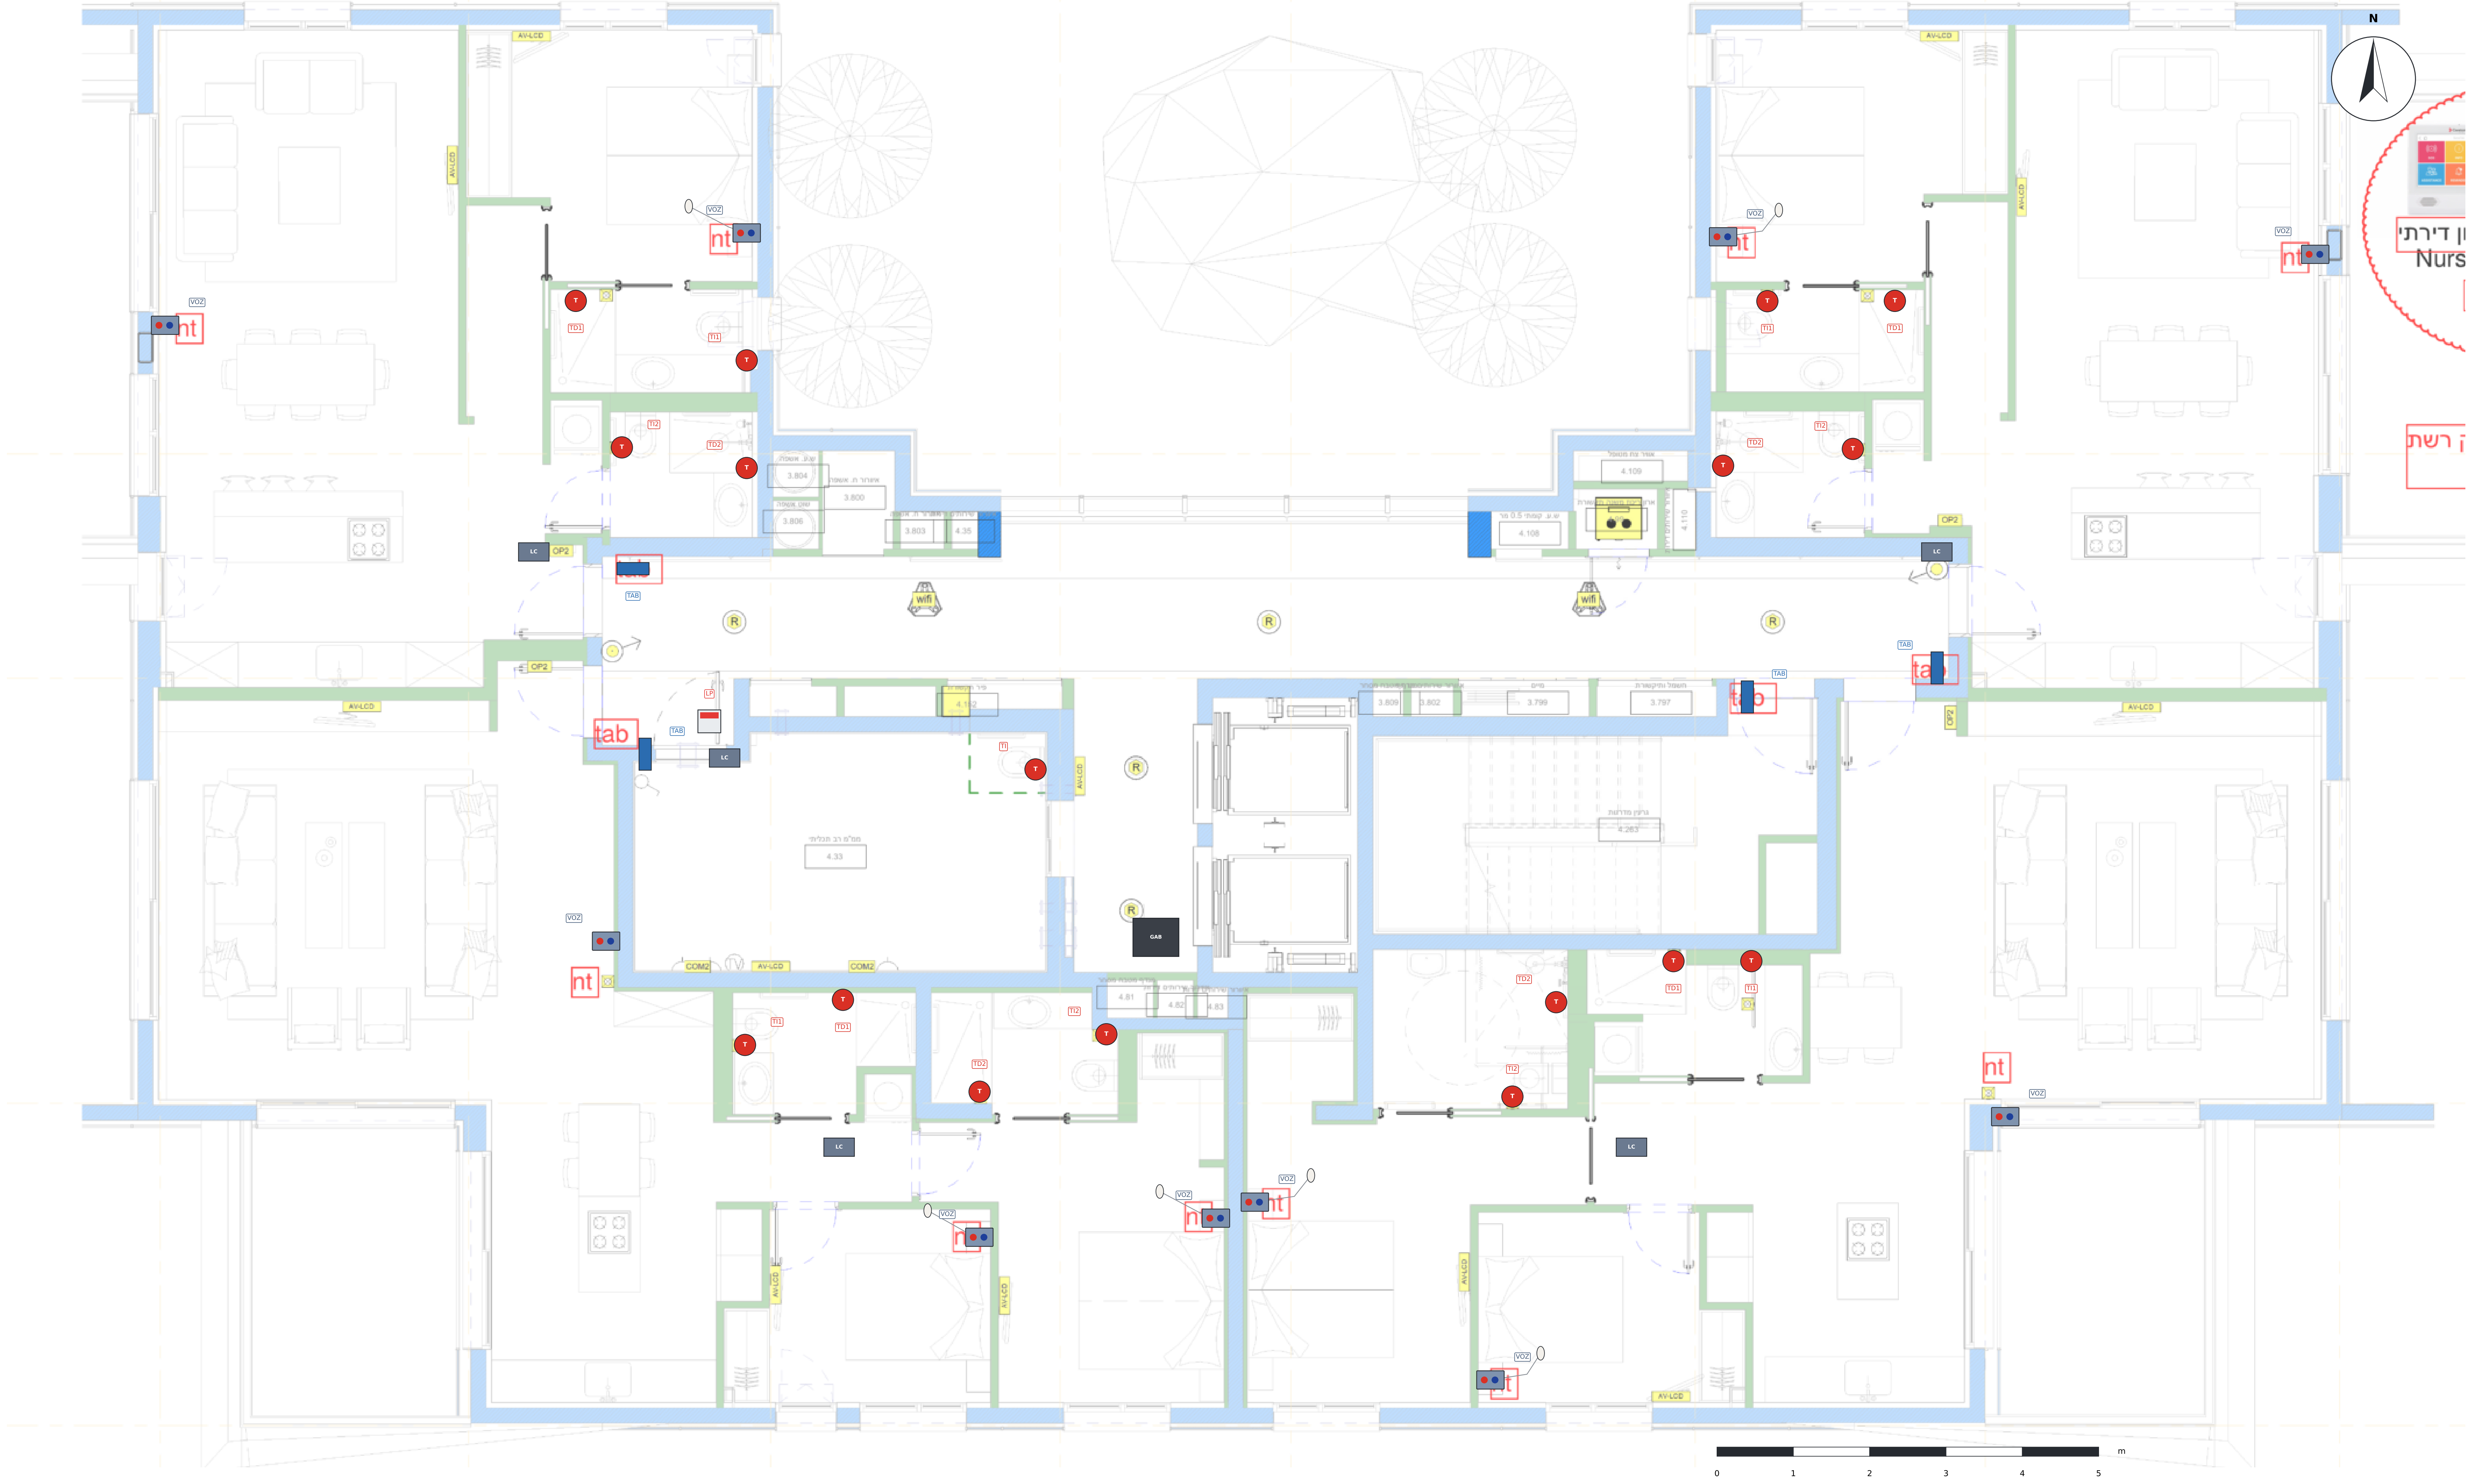

NOTES · תורעה

1. רקע: תינכות IT L2 לש חוקלה םע םינומיסה ולש םודאב:
«nt» = לנפ ילוק ו-«tab» = טלבאט הסינכב.

2. לעמ, עבצב: הציוד בהעצה וז.
לכ לנפ לכו טלבאט נמצאים במקום שהלקוח סימן.

L2 3. תינכותב הצחרה ירדחב ☒ םיבוהצה םיעוביר
הם משיכות החבל (אסלה ומקלחת).

4. 4 הטלבאטים, בולבי, ליד דלת לכ דירה,
.«tab» כמו סימוני

5. תוינכותל L2 ו-L5 (סיסב העצהה) אותו במבנה;
L5 8 היא הקומה הטיפוסית לקומות 1 עד.

DEVICES · EQUIPOS · דויצ

🟦	TAB · טלבאט הסינכב (iPad / אנדרואיד) – קריאה ודיבור, גובה 1.40 מ' Door tablet – call and voice · טלבאט הסינכב – קריאה ודיבור
▨	VOZ · פנל קולי עם לחצנים ACE82182451 – סלון וחדרי שינה, גובה 1.20–1.30 מ' Voice panel with buttons – living room and bedrooms · פנל קולי עם לחצנים – סלון וחדרי שינה
○	אגס קריאה ליד המיטה (חדרי שינה) Call pear next to the bed (bedrooms) · אגס קריאה ליד המיטה
T	TI / TD · משיכת חבל ACE40320303W – אסלה ומקלחת, גובה 1.85 מ' Pull-cord – toilet and shower, h 1.85 m · משיכת חבל – אסלה ומקלחת, גובה 1.85 מ'
🟥	LP · מנורת מסדרון ACE41020309 – מעל דלת כל שירותים ציבוריים Corridor light – above each public toilet door · מנורת מסדרון – מעל דלת כל שירותים ציבוריים

שירותים קריאת אחות

לבח תכישמ

טבלט אנדרואיד קריאת אחות

Advantecnia
Llamada de enfermera
Hospital
Salud y bienestar

הסינכב טלבאט (iPad / דיאורדנא)

מנורה קריאת אחות

ןורדסמ תרונמ

פנל קריאת אחות

סינצחל םע ילוק לנפ

ןגומ רויד · ןוכיתה םי ילדגמ

קריאה אחות – קרקע + 8 תומוק · 32 תוריד

Telab International :ןכוה ע"י   ACE BG · Advantecnia :תכרעמ

העצההו (תינכות L2) חוקלה ינומיס

Client marks (plan L2) and proposal

SCALE · הדימ הנק	DATE · ךיראת	REV	ןוילג
1:60	15/10/2026	B	03

בסיס: תינכות האדרילכ L5 (דגם זוג / Triplet) · םירטמב תודימ

טמרופ A1 · ההדורה B – לע התינכות תיתימאה

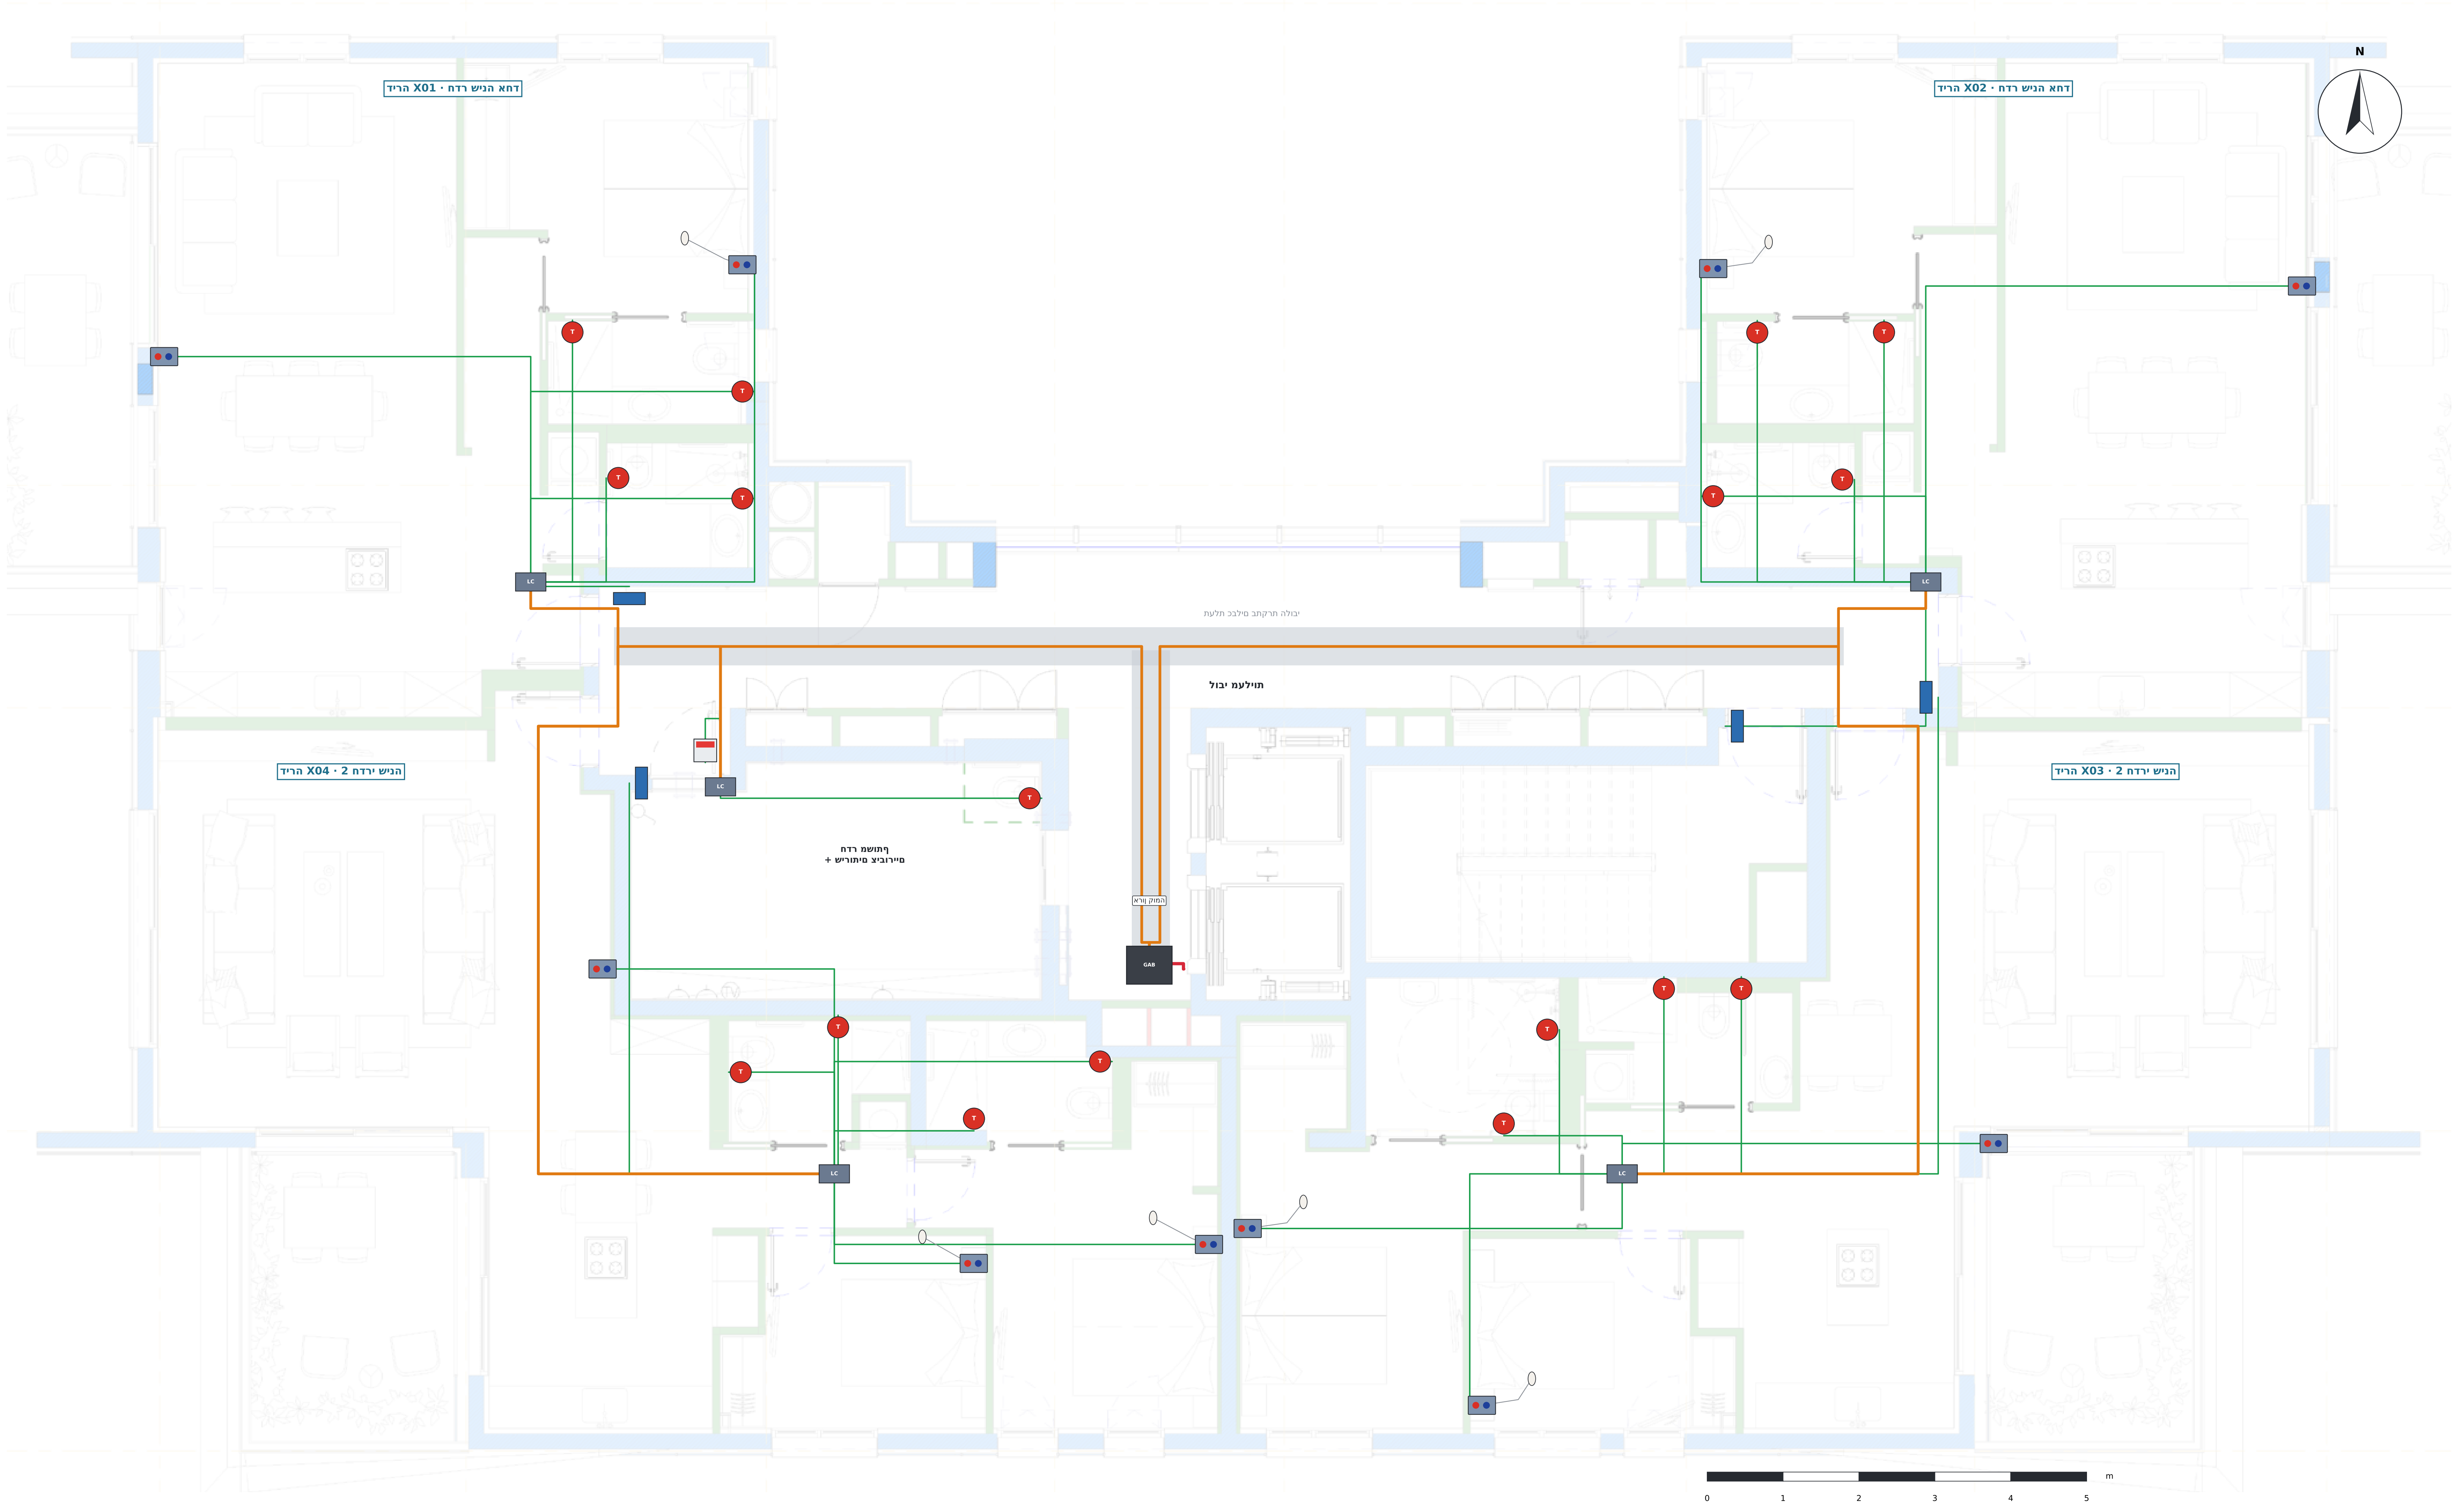

WIRING · CABLEADO · טוויח

🟩 Cat6 ילאידר: לכ ןקתה ← LCom הרידה לש
Cat6 radial: each device → apartment LCom · Cat6 ילאידר: לכ ןקתה ← LCom הרידה לש

🟧 Cat6 / Cat7 תרשרש: LCom ← LCom ← Buscomm ןוראב
Cat6 / Cat7 chain: LCom → LCom → Buscomm · Cat6 / Cat7 תרשרש: LCom ← LCom ← Buscomm

🟥 Cat6A / Cat7 תשר: Buscomm ← גתמ ← דומע ← תרש עקרק
Cat6A / Cat7 network: Buscomm → switch → riser → GF server · Cat6A / Cat7 תשר: Buscomm ← גתמ ← דומע ← תרש

םיכרוא תיסופיט המוקב (הברזר אלל)

🟩	Cat6 ילאידר ךותב תורידה	183 m
🟧	Cat6 / Cat7 תרשרש LCom ← Buscomm	82 m
🟥	Cat6A / Cat7 ןורא ועמוד	4 m

NOTES · תורעה

1. לכ ןקתה רבוחמ ילאידרית (Cat6) ל-LCom הרידה לש, תרקתב האובמה.
2. ה-LCom תודיחי םירשורשמ ךרואל תלעת היבולה דע ןורא המוקה:
x01 ← x04 ← רדח ךתושמ ← Buscomm 1 · x02 ← x03 ← Buscomm 2.
3. גתמ ה-PoE לש המוקה רבוחמ ךרד דומע Cat6A / Cat7 דע
תרשה תמוקב עקרקה.
4. לוכה PoE: ןיא ךרוצ ב-230V ינקתהל תורידה.

NOTES · תורעה

1. סיסב: תינכות תילכירדא L5 (המוק תיסופיט) – 8 תומוקה תוהז: 4 תוריד המוקב, 32 ךסב לוכה.
2. תוריד x01 ו-x02: רדח הניש דחא, ןולס םע חבטמ ו-2 ירדח הצחר. תוריד x03 ו-x04: 2 ירדח הניש ו-2 ירדח הצחר.
3. טלבאט בכנסיה לכל הריד (iPad / דיאורדנא) לקריאה ולדיבור םע האחות.
4. לנפ ילוק םע םינצחל (ACE82182451) בסלון ובכל רדח הניש; בחדר השינה םע אגס דיל הטימה.
5. תוכישמ לבח (ACE40320303W) בסאלה ובמקלחת בכל ירדח הרחצה, הבוגב 1.85 מ'.
6. םיתוריש םיירוביצ בכל המוק בחדר ךתושמה: תכישמ לבח + רונמ תרוסדמ ןועמל הדלת. םע 2 בקרקע – 10 םיתוריש םיירוביצ.
.(IT-ומכ תובנית ה ,Tripp Lite 12U) 7. ןורא המוק בסמדרון השירות דיל המעליות
8. םימוקימ יפל ינומיס הלוקח תובנית L2 (nt = לנפ ילוק, tab = טלבאט): וארו ןוילג 03.

ןגומ רויד · ןוכיתה םי ילדגמ

תוריד 32 · תומוק 8 + עקרק – תוחא תאירק

Telab International :ןכוה ע"י ACE BG · Advantecnia :תכרעמ

טוויח · 1–8 תיסופיט המוק

Typical floor F1–F8 · wiring

SCALE · הדימ הנק	DATE · ךיראת	REV	ןוילג
1:60	15/10/2026	B	04

בסיס: תינכות לכירדאה L5 (זוג דסמ / Triplet) · תודימ םירטמב

טמרופ A1 · הרודהמ B – לע תינכותה תיתימאה

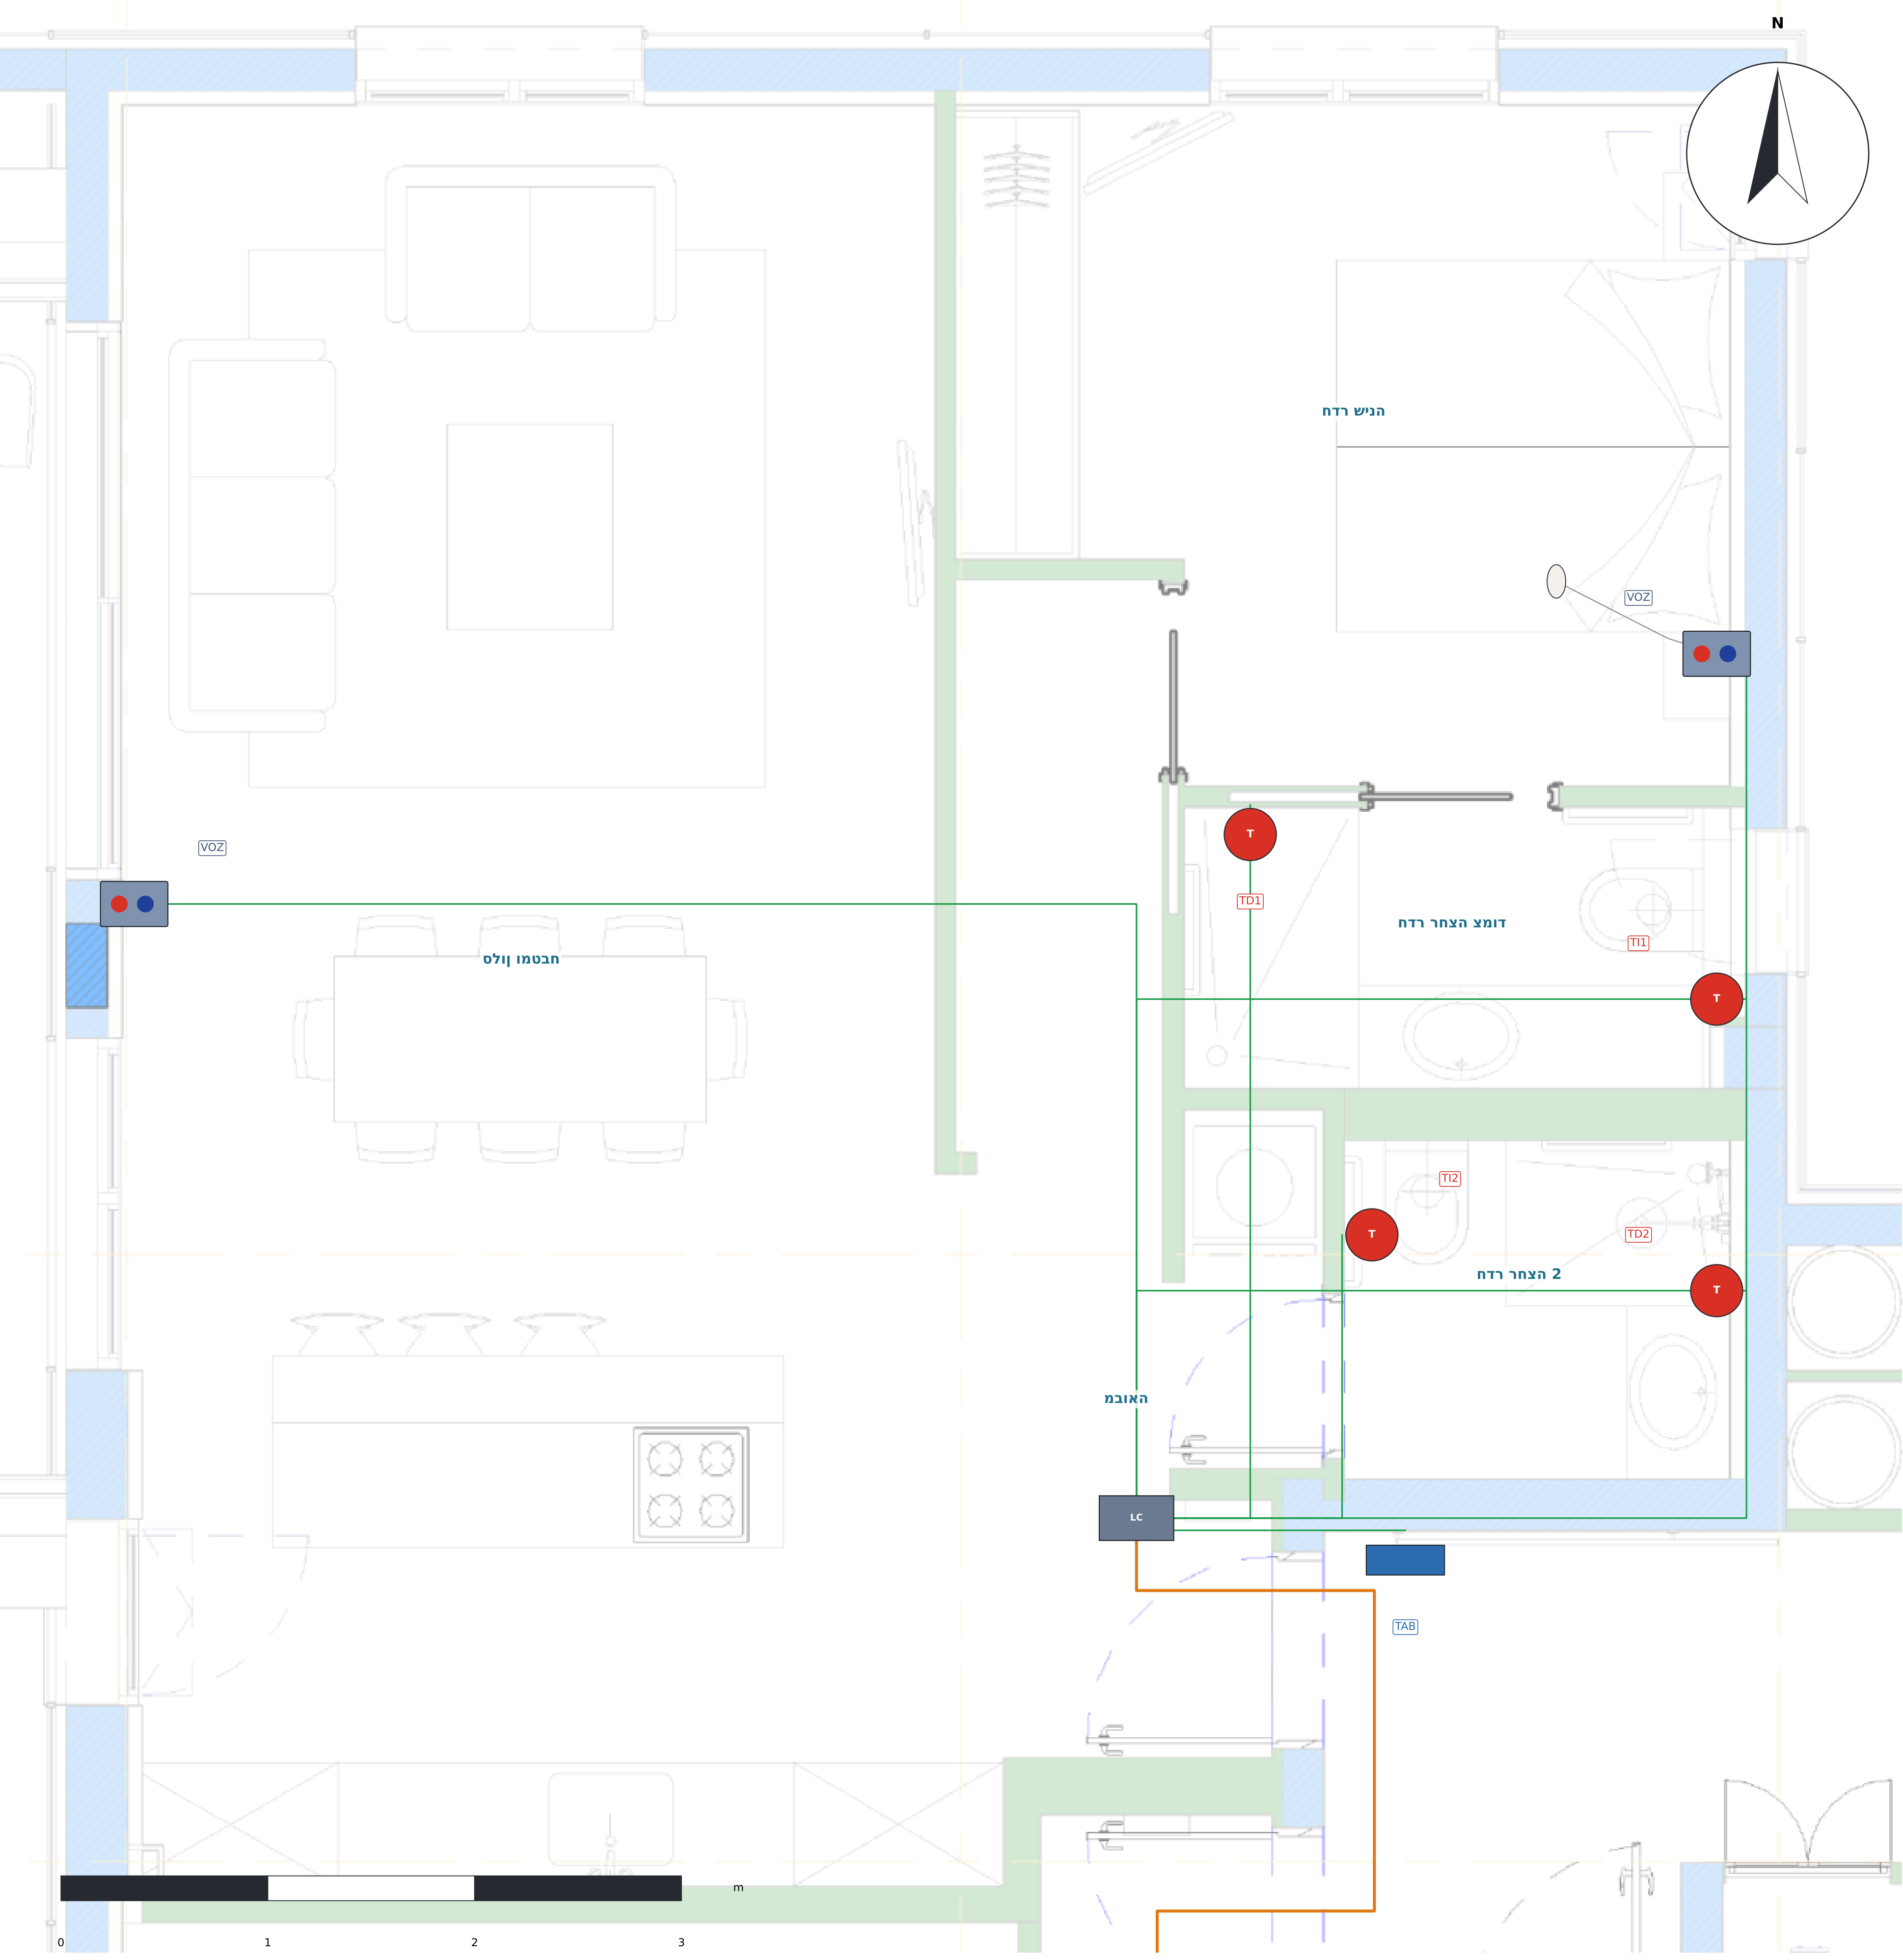
N
הניש רדח
VOZ
דומצ הצחר רדח
TD1
TI1
T
חבטמו ןולס
VOZ
TI2
TD2
2 הצחר רדח
האובמ
LC
TAB
0
1
2
3
m

הרידה דויצ

ID	ןקתה	רדח	הבוג
TAB	הסינכב טלבאט	האובמ	1.40 מ'
VOZ-S	םינצחל םע ילוק לנפ	חבטמו ןולס	1,30 m
VOZ-D	םינצחל םע ילוק לנפ + סגא	הניש רדח	1,20 m
TI1	לבח תכישמ	דומצ הצחר רדח	1.85 מ'
TD1	לבח תכישמ	דומצ הצחר רדח	1.85 מ'
TI2	לבח תכישמ	2 הצחר רדח	1.85 מ'
TD2	לבח תכישמ	2 הצחר רדח	1.85 מ'
LCOM	LCom ACE71610003	האובמ	2,55 m

SYMBOLS · SÍMBOLOS · םילמס

- 🟦 TAB · הסינכב טלבאט (iPad / דיאורדנא) – רוביד האירק, הבוג 1.40 מ'
  Door tablet – call and voice · הסינכב טלבאט – רוביד האירק
- ●● VOZ · םינצחל םע ילוק לנפ ACE82182451 – ןולס ירדחו הניש, הבוג 1.20–1.30 מ'
  Voice panel with buttons – living room and bedrooms · םינצחל םע ילוק לנפ – ןולס ירדחו הניש
- ○ הטימה דיל האירק סגא (הנישה ירדחב)
  Call pear next to the bed (bedrooms) · הטימה דיל האירק סגא
- 🔴 TI / TD · לבח תכישמ ACE40320303W – הלסא תחלקמו, הבוג 1.85 מ'
  Pull-cord – toilet and shower, h 1.85 m · לבח תכישמ – הלסא תחלקמו, הבוג 1.85 מ'
- 🟥 LP · ןורדסמ תרונמ ACE41020309 – םיירוביצ םיתורש לכ תלד לעמ
  Corridor light – above each public toilet door · ןורדסמ תרונמ – םיירוביצ םיתורש לכ תלד לעמ
- LC · LCom ACE71610003 – הרידה זכרמ (הרקת)
  LCom – apartment hub (ceiling) · LCom – הרידה זכרמ (הרקת)

NOTES · תורעה

1. הריד x02 איה תנומת יאר לש x01 (דויצ ותוא).
2. טלבאט יבולב, דיל תלד הסינכה (ןומיס «tab» לש חוקלה).
3. לנפ ילוק ןולסב ובחדר הנישה (םע סגא דיל הטימה).
4. 2 ירדח הצחר: תכישמ לבח הלסאב תחלקמבו לכב דחא (4 תוכישמ לבח).
5. לוכה רבוחמ תילאידר ב-Cat6 ל-LCom האובמב.

שירותים קריאת אחות

לבח תכישמ

טבלט אנדרואיד קריאת אחות
Advantecnia
Llamada de enfermera
Hospital
Salud y bienestar

הסינכב טלבאט (iPad / דיאורדנא)

מנורה קריאת אחות

ןורדסמ תרונמ

פנל קריאת אחות

םינצחל םע ילוק לנפ

ןגומ רויד · ןוכיתה םי ילדגמ
תוריד 32 · תומוק 8 + עקרק – תוחא תאירק
Telab International :ןכוה ע"י   ACE BG · Advantecnia :תכרעמ

(x01 / x02) דחא הניש רדח תריד
1-bedroom apartment (x01 / x02)

SCALE · הדימ הנק	DATE · ךיראת	REV	ןוילג
1:30	**15/10/2026**	**B**	**05**

סיסב: לכירדאה תינכות L5 (זוע דסמ / Triplet) · םירטמב תודימ
טמרופ A1 · הרודהמ B – לע התינכות תיתימאה

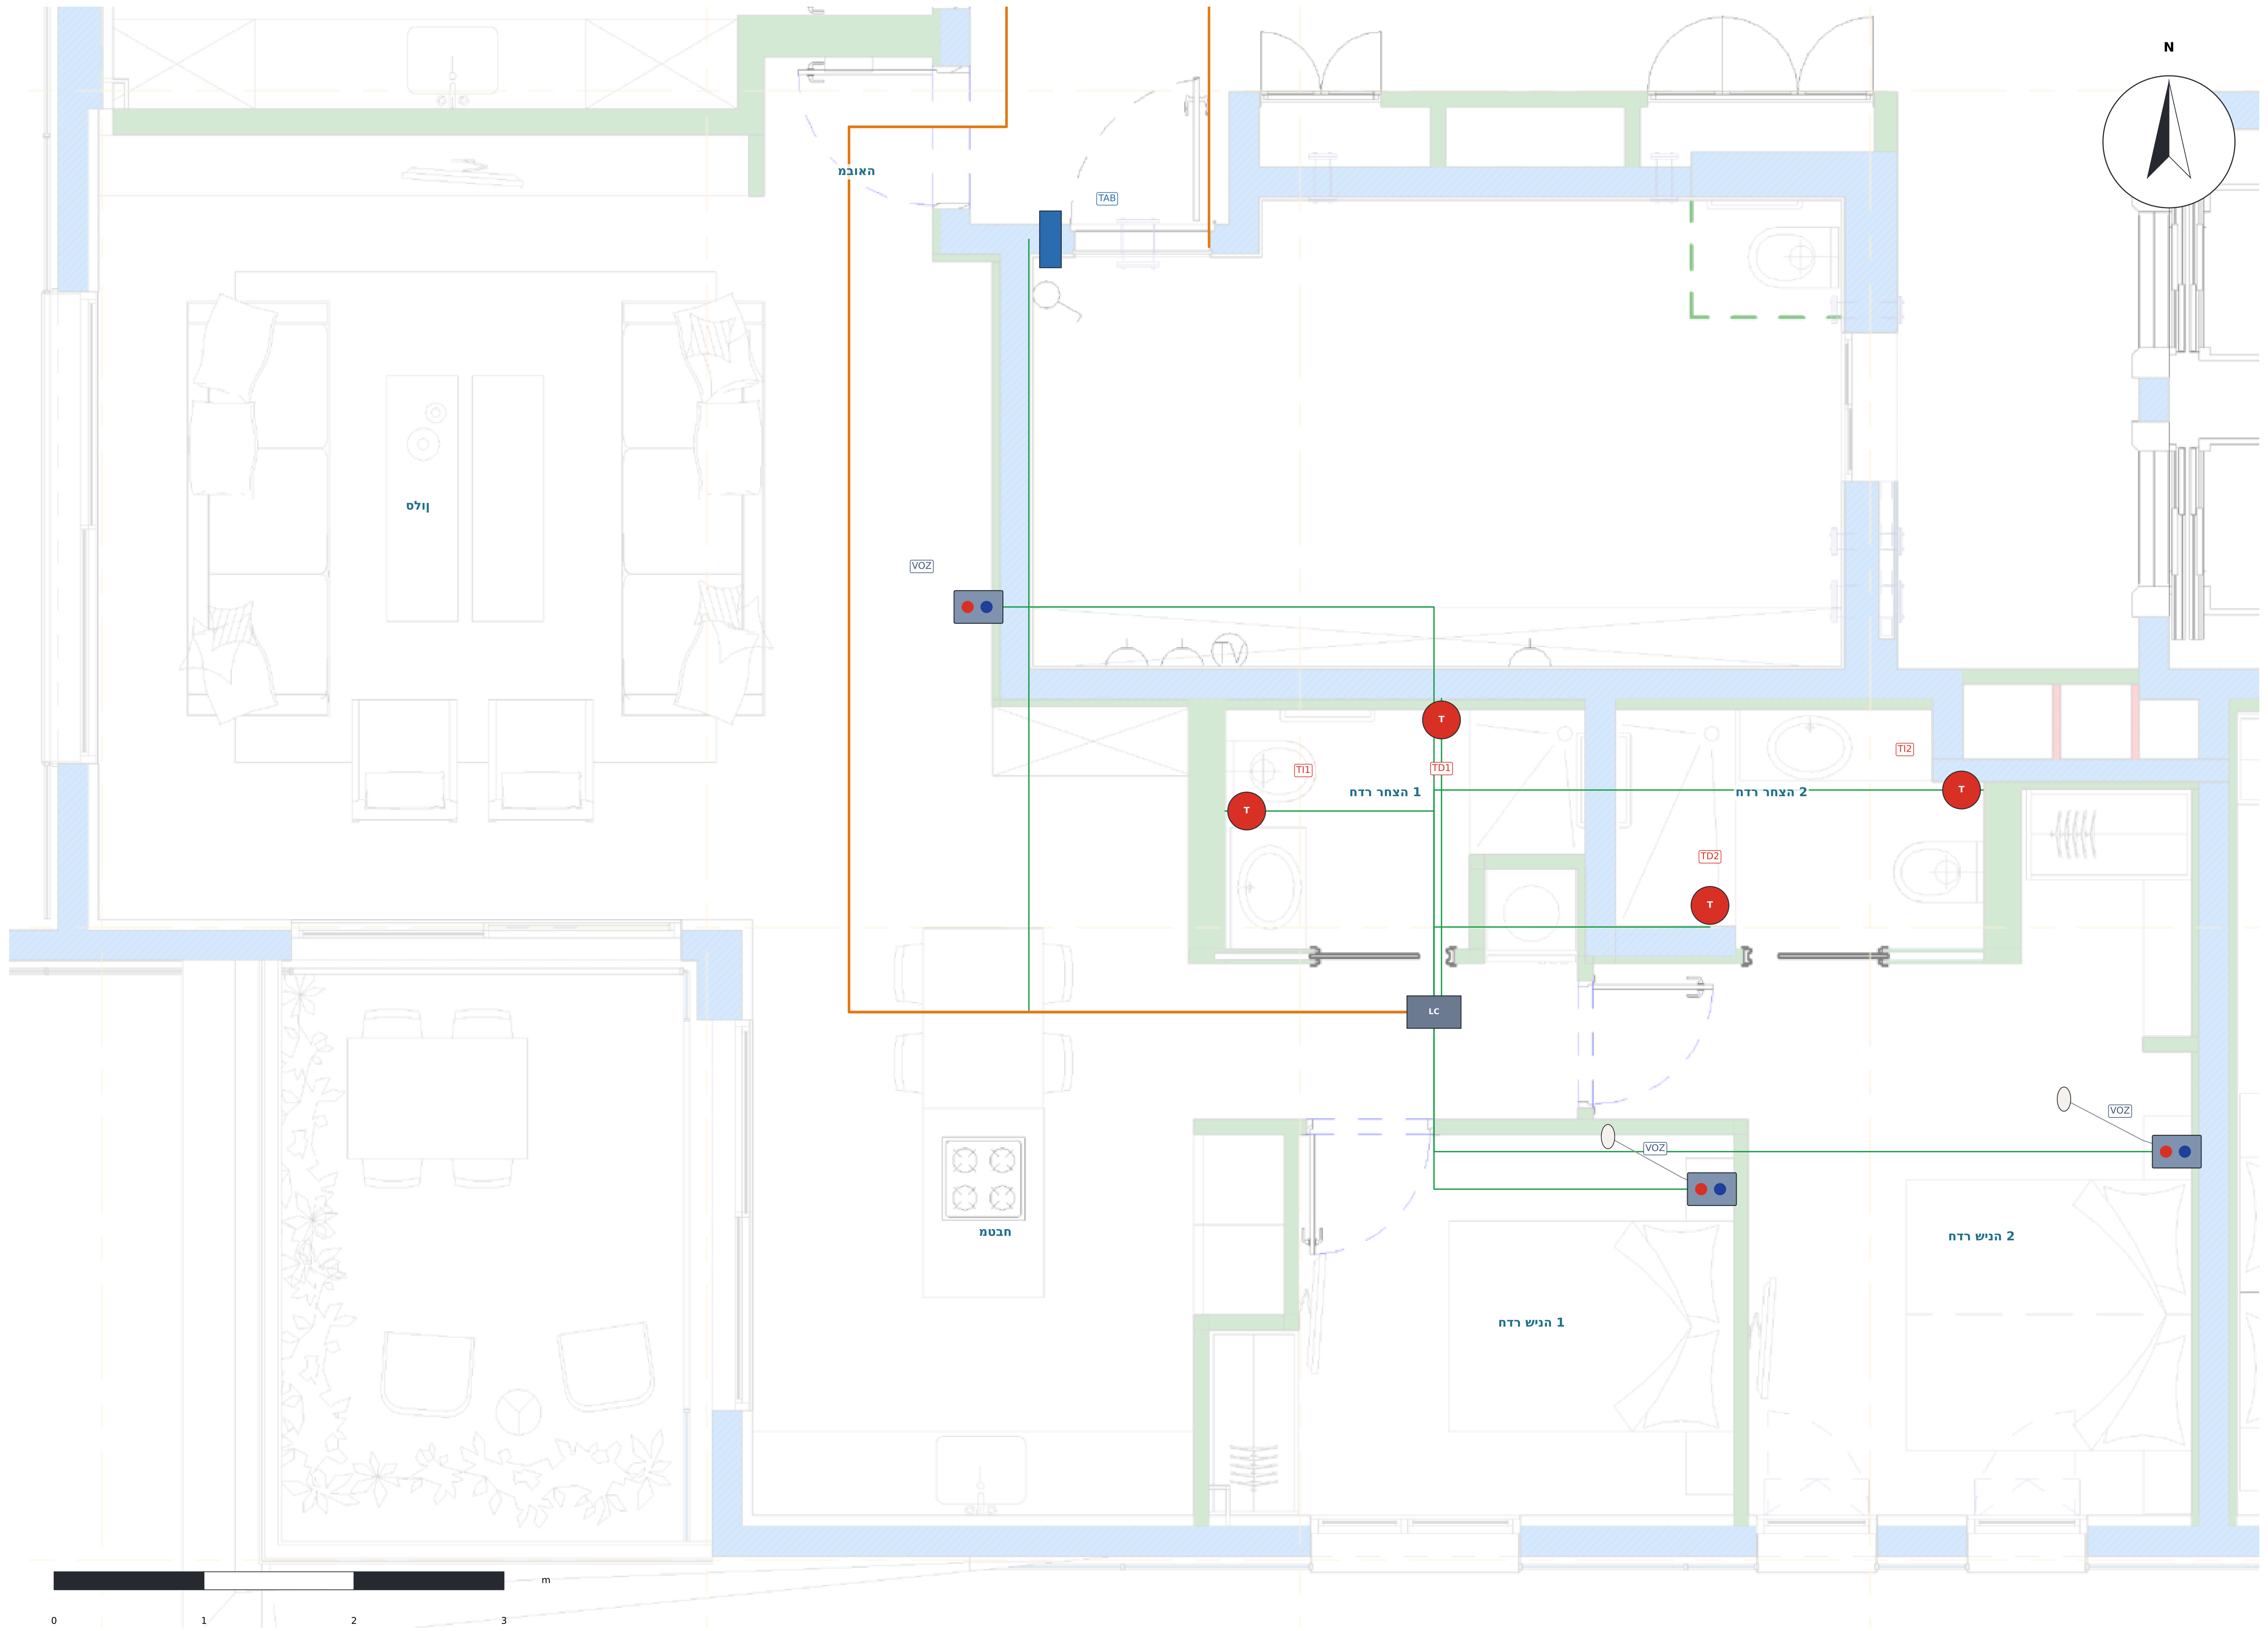
N
מבואה
TAB
VOZ
סלון
TV
T
TI1
TD1
TI2
TD2
חדר רחצה 1
חדר רחצה 2
LC
מטבח
VOZ
VOZ
חדר שינה 1
חדר שינה 2
m
0
1
2
3

ציוד הדירה

ID	התקן	חדר	גובה
TAB	טאבלט בכניסה	מבואה	1.40 מ'
VOZ-S	פנל קולי עם לחצנים	סלון	1,30 m
VOZ-D1	פנל קולי עם לחצנים + אגס	חדר שינה 1	1,20 m
VOZ-D2	פנל קולי עם לחצנים + אגס	חדר שינה 2	1,20 m
TI1	משיכת חבל	חדר רחצה 1	1.85 מ'
TD1	משיכת חבל	חדר רחצה 1	1.85 מ'
TI2	משיכת חבל	חדר רחצה 2	1.85 מ'
TD2	משיכת חבל	חדר רחצה 2	1.85 מ'
LCOM	LCom ACE71610003	מבואה	2,55 m

SYMBOLS · SÍMBOLOS · סמלים

🟦	TAB · טאבלט בכניסה (iPad / אנדרואיד) – קריאה ודיבור, גובה 1.40 מ' Door tablet – call and voice · טאבלט בכניסה – קריאה ודיבור
● ●	VOZ · פנל קולי עם לחצנים ACE82182451 – סלון וחדרי שינה, גובה 1.20–1.30 מ' Voice panel with buttons – living room and bedrooms · פנל קולי עם לחצנים – סלון וחדרי שינה
○	אגס קריאה ליד המיטה (בחדרי שינה) Call pear next to the bed (bedrooms) · אגס קריאה ליד המיטה
T	TI / TD · משיכת חבל ACE40320303W – אסלה ומקלחת, גובה 1.85 מ' Pull-cord – toilet and shower, h 1.85 m · משיכת חבל – אסלה ומקלחת, גובה 1.85 מ'
🟥	LP · מנורת מסדרון ACE41020309 – מעל דלת כל שירותים ציבוריים Corridor light – above each public toilet door · מנורת מסדרון – מעל דלת כל שירותים ציבוריים
LC	LC · LCom ACE71610003 – מרכז הדירה (תקרה) LCom – apartment hub (ceiling) · LCom – מרכז הדירה (תקרה)

NOTES · הערות

1. אותו ציוד בדירה x03 (חדרי הרחצה בפריסה שונה).
2. טאבלט בלובי, ליד דלת הכניסה (סימון «tab» של הלקוח).
3. פנל קולי בסלון ובשני חדרי השינה (עם אגס ליד המיטה).
4. 2 חדרי רחצה: משיכת חבל באסלה ובמקלחת בכל אחד (4 משיכות חבל).
5. הכול מחובר רדיאלית ב-Cat6 ל-LCom במסדרון חדרי השינה.

שירותים קריאת אחות

משיכת חבל

טבלט אנדרואיד קריאת אחות
Advantecnia
Llamada de enfermera
Hospital

טאבלט בכניסה (iPad / אנדרואיד)

מנורה קריאת אחות

מנורת מסדרון

פנל קריאת אחות

פנל קולי עם לחצנים

מגדלי הים התיכון · דיור מוגן
קריאת אחות – קרקע + 8 קומות · 32 דירות
מערכת: ACE BG · Advantecnia   הוכן ע"י: Telab International

דירת שני חדרי שינה (x04 / x03)
2-bedroom apartment (x04 / x03)

SCALE · קנה מידה	DATE · תאריך	REV	גיליון
1:35	**15/10/2026**	**B**	**06**

בסיס: תכניות האדריכל L5 (מסד זוג / Triplet) · מידות במטרים
פורמט A1 · מהדורה B – על התוכנית האמיתית

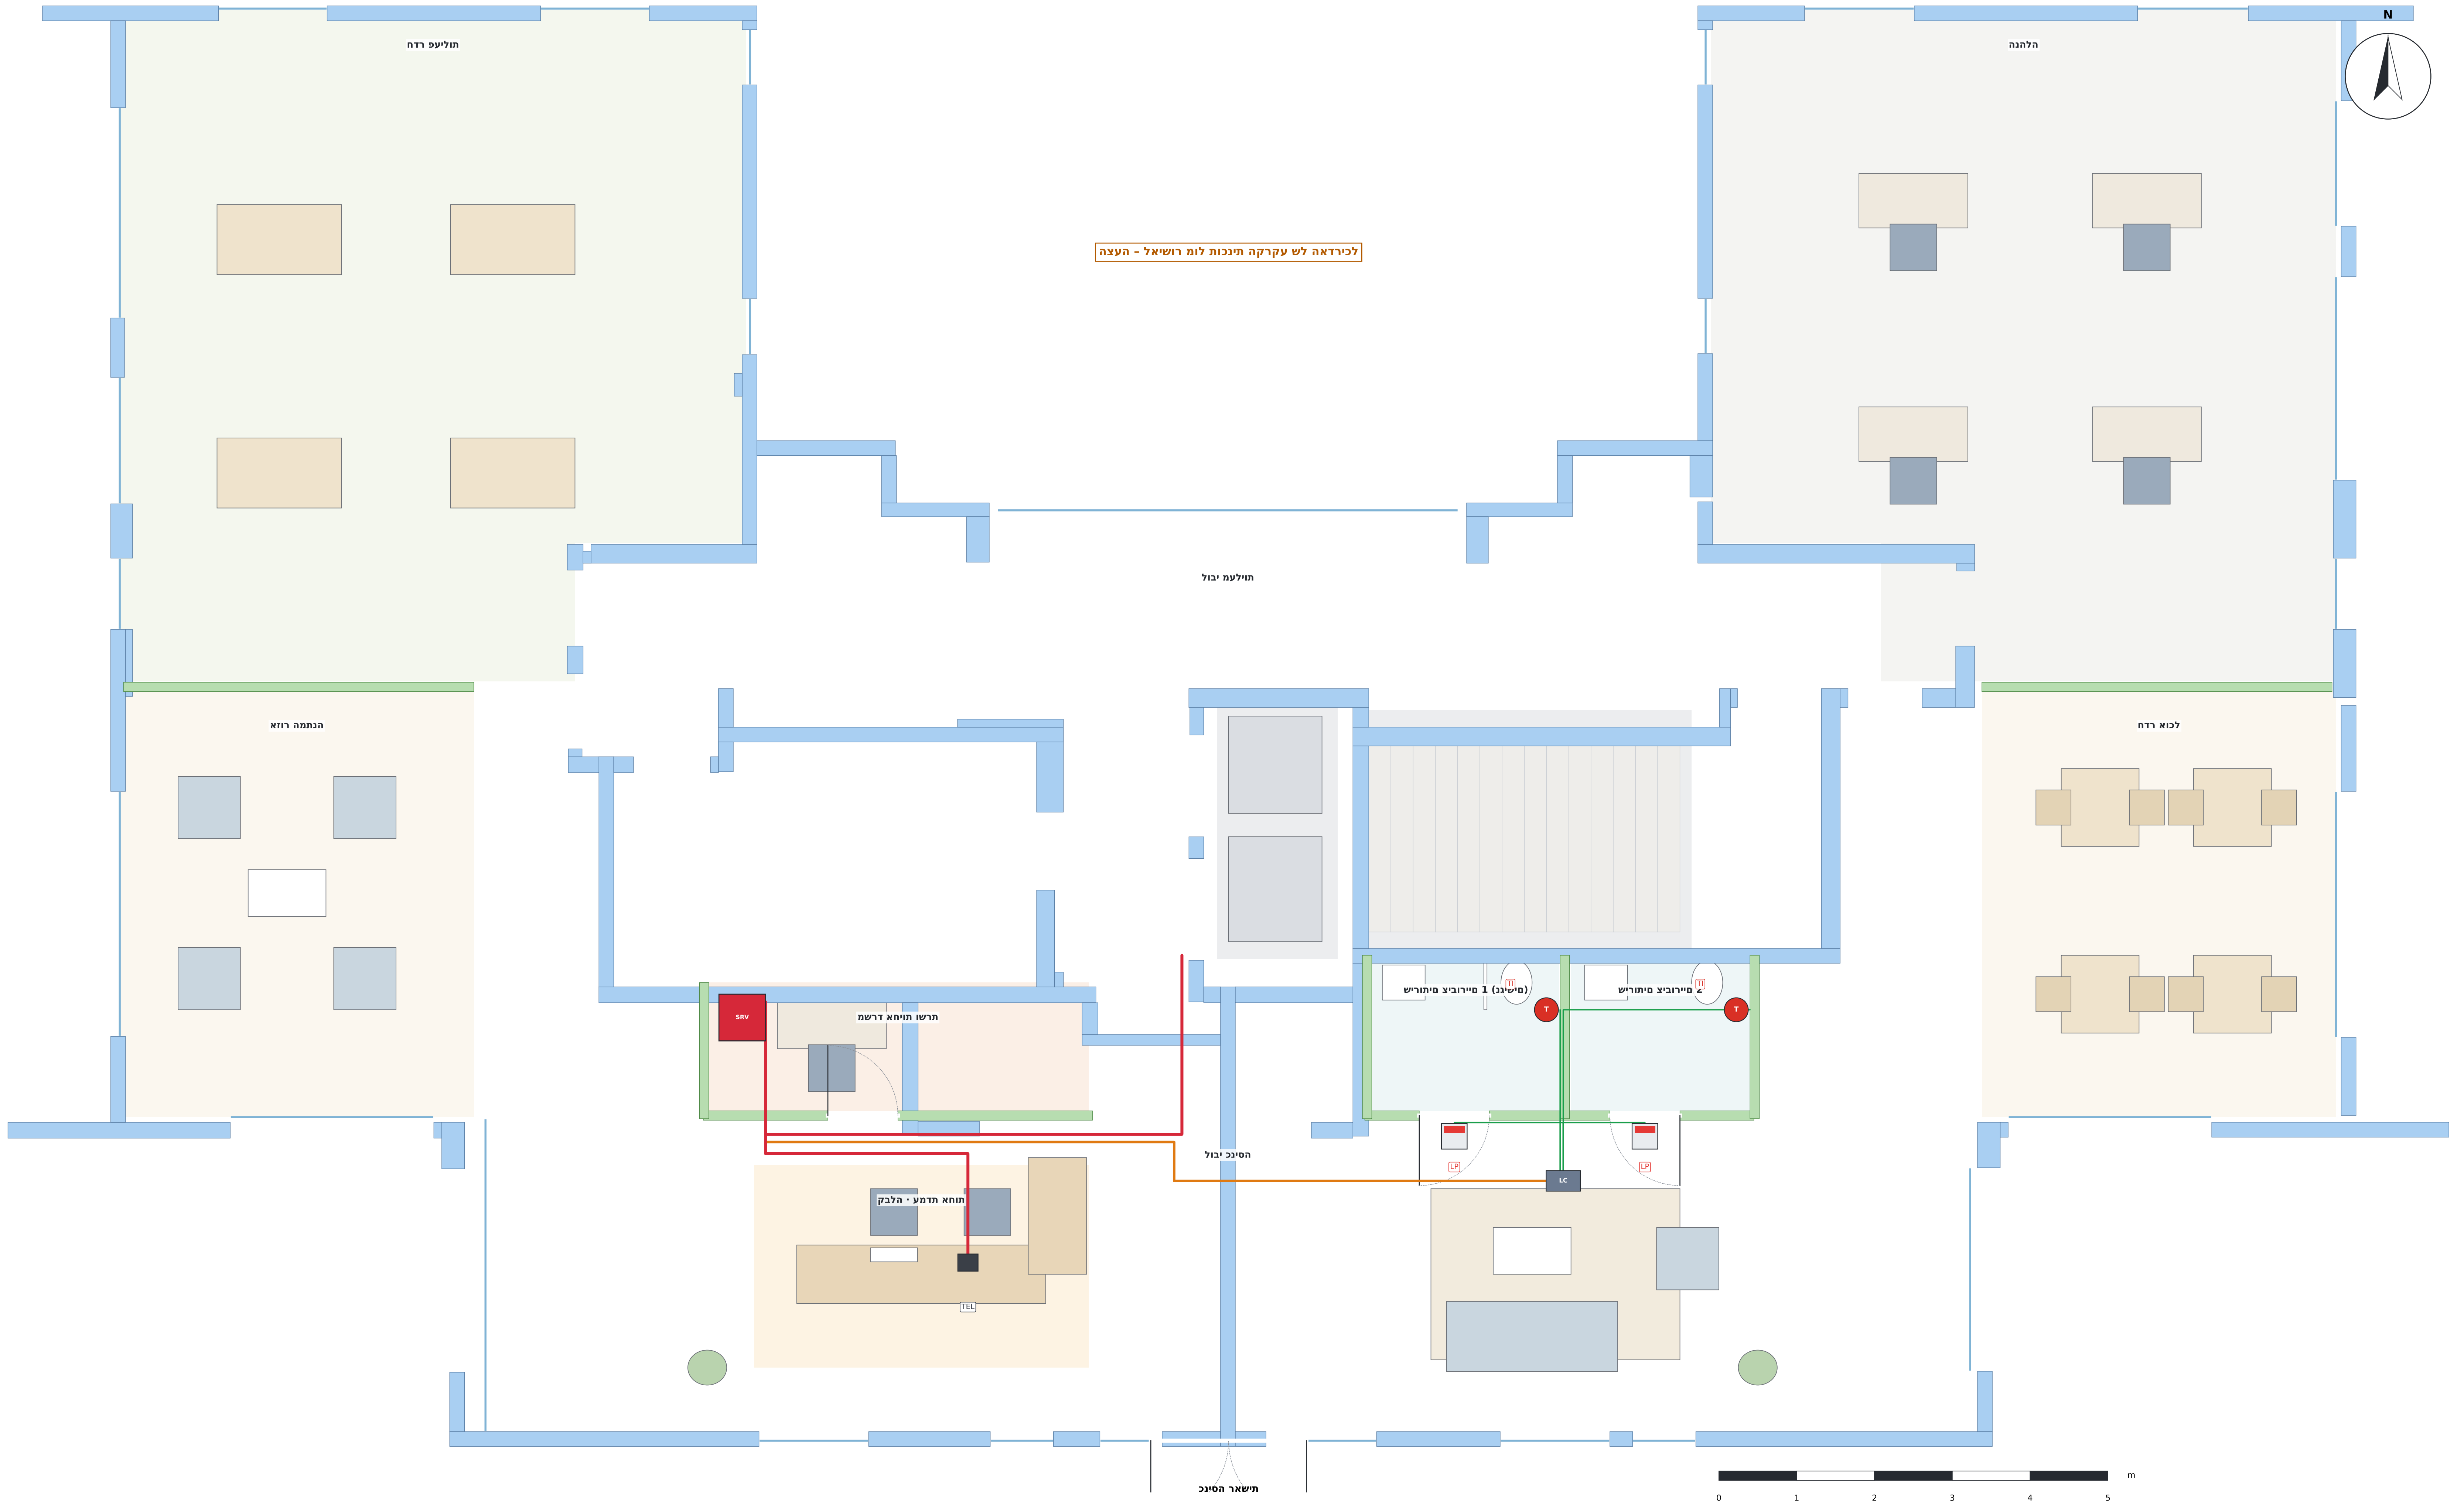
N
חדר פעילות
הצעה – לאישור מול תוכנית הקרקע של האדריכל
הנהלה
לובי מעליות
אזור המתנה
חדר אוכל
משרד אחיות ושרת
SRV
שירותים ציבוריים 1 (נגישים)
שירותים ציבוריים 2
TI
T
LP
LC
לובי כניסה
קבלה · עמדת אחות
TEL
כניסה ראשית
0
1
2
3
4
5
m

פרט · קבלה ועמדת אחות (1:40)

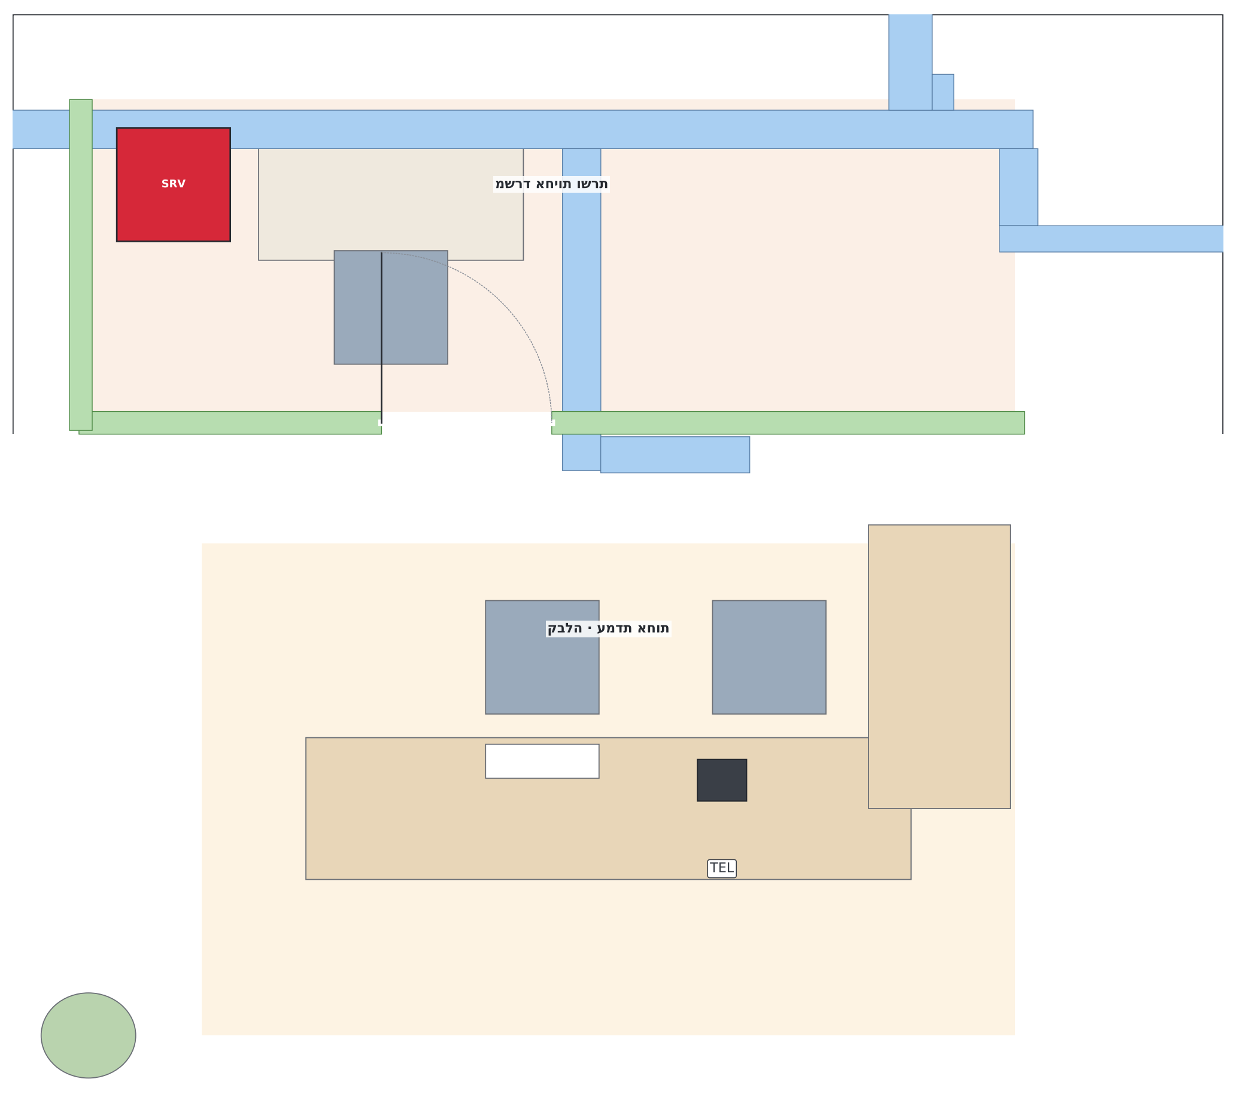
SRV
משרד אחיות ושרת
קבלה · עמדת אחות
TEL

NOTES · הערות

1. עמדת האחות בקבלה, מול הכניסה והמעליות.

ACE52190200 2. על העמדה: טלפון שולחני אנדרואיד
(מקבל קריאות ודיבור).

3. מאחורי העמדה: משרד האחיות עם הארון הראשי:
שרת ACE51010103, מתג PoE ACEUCM6302 ו-Buscomm של הקרקע.

4. 2 שירותים ציבוריים בקרקע: משיכת חבל ליד האסלה ומנורת מסדרון
מעל כל דלת.

5. העמוד מ-8 הקומות יורד בגרעין עד הארון הראשי.

6. פריסת קרקע מוצעת: תעודכן כשתגיע
התוכנית של האדריכל.

SYMBOLS · SÍMBOLOS · סמלים

T — TI / TD · משיכת חבל ACE40320303W – אסלה ומקלחת, גובה 1.85 מ'
Pull-cord – toilet and shower, h 1.85 m · משיכת חבל – אסלה ומקלחת, גובה 1.85 מ'

LP · מנורת מסדרון ACE41020309 – מעל דלת כל שירותים ציבוריים
Corridor light – above each public toilet door · מנורת מסדרון – מעל דלת כל שירותים ציבוריים

LC — LC · LCom ACE71610003 – רכזת דירה (תקרה)
LCom – apartment hub (ceiling) · LCom – רכזת דירה (תקרה)

TEL — TEL · טלפון שולחני אנדרואיד ACE52190200
Android desk phone · טלפון שולחני אנדרואיד

SRV — SRV · ארון קרקע: שרת ACE51010103 + מתג + Buscomm
GF rack: server + switch + Buscomm · ארון קרקע: שרת + מתג + Buscomm

מגדלי ים התיכון · דיור מוגן
32 דירות · 8 קומות + קרקע – קריאת אחות
הוכן ע"י: Telab International   מערכת: ACE BG · Advantecnia

קומת קרקע · לובי ועמדת אחות

Ground floor · lobby and nurse desk

SCALE · קנה מידה	DATE · תאריך	REV	גיליון
1:60	15/10/2026	B	07

בסיס: תוכנית האדריכל L5 (מסד זוג / Triplet) · מידות במטרים
פורמט A1 · מהדורה B – על התוכנית האמיתית

א · בניין קרקע + 8 קומות

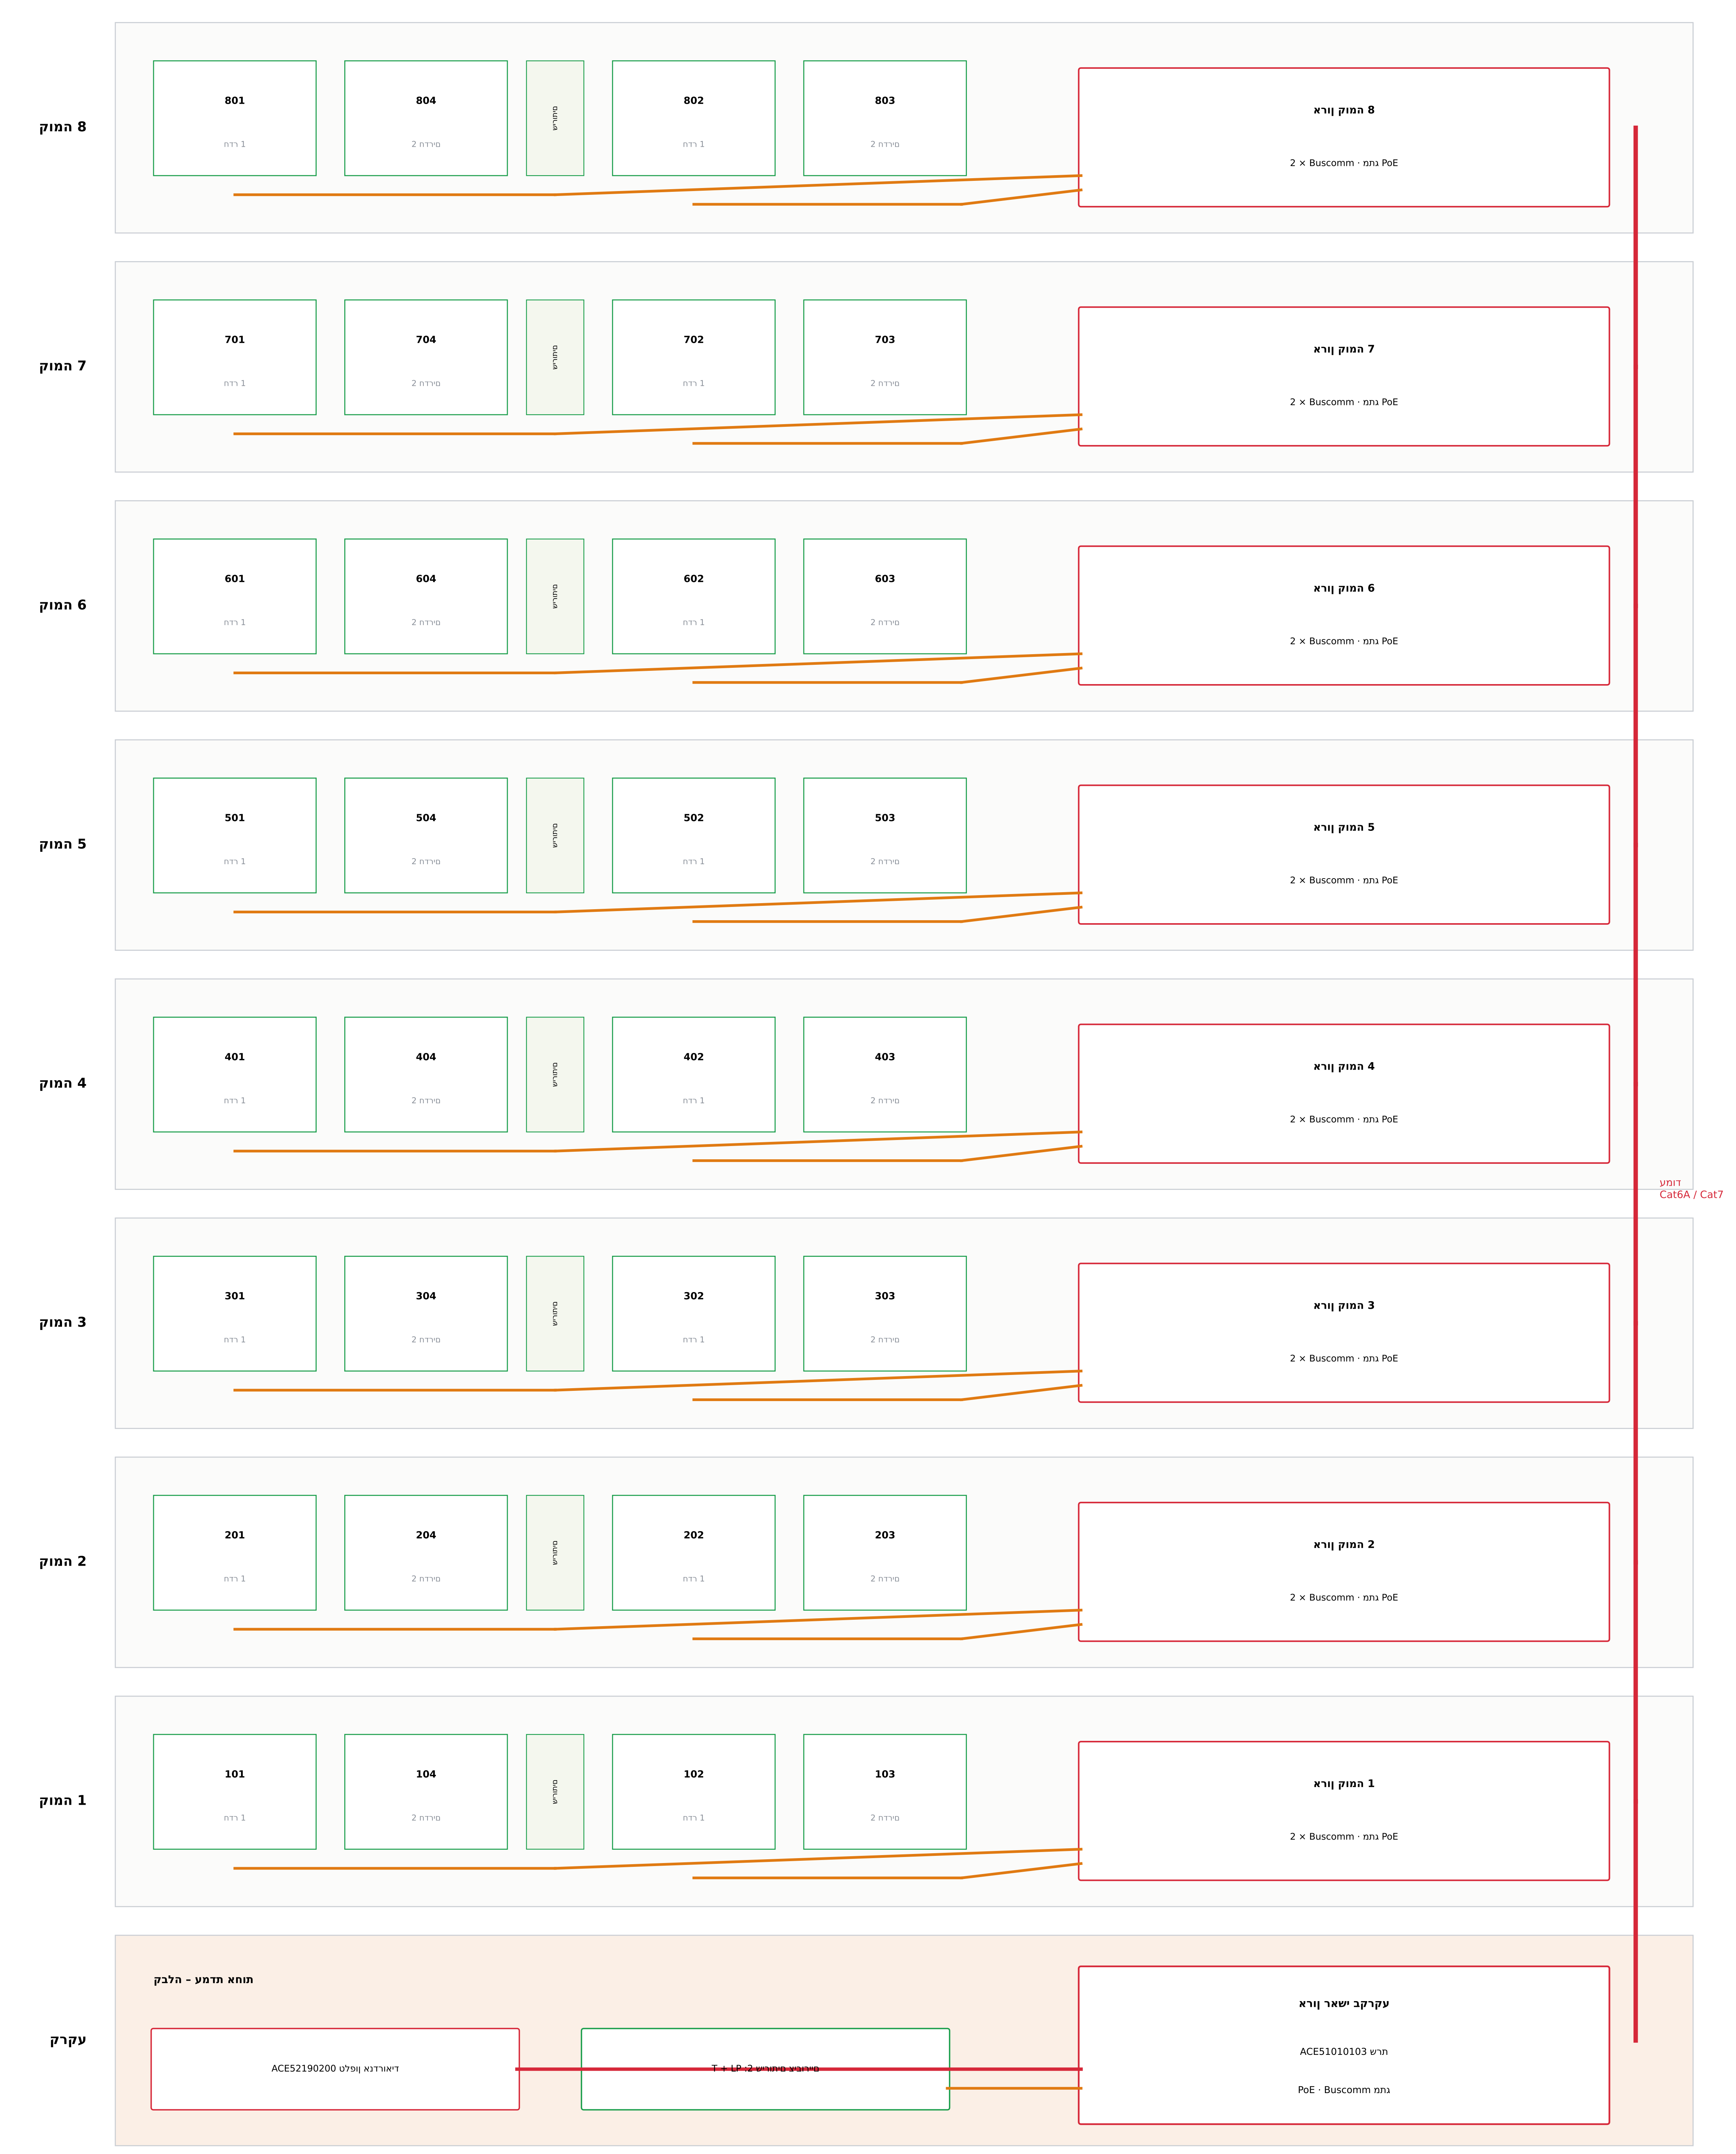
קומה 8
801 חדר 1
804 2 חדרים
שירותים
802 חדר 1
803 2 חדרים
ארון קומה 8
2 × Buscomm · מתג PoE
קומה 7
701 חדר 1
704 2 חדרים
שירותים
702 חדר 1
703 2 חדרים
ארון קומה 7
2 × Buscomm · מתג PoE
קומה 6
601 חדר 1
604 2 חדרים
שירותים
602 חדר 1
603 2 חדרים
ארון קומה 6
2 × Buscomm · מתג PoE
קומה 5
501 חדר 1
504 2 חדרים
שירותים
502 חדר 1
503 2 חדרים
ארון קומה 5
2 × Buscomm · מתג PoE
קומה 4
401 חדר 1
404 2 חדרים
שירותים
402 חדר 1
403 2 חדרים
ארון קומה 4
2 × Buscomm · מתג PoE
קומה 3
301 חדר 1
304 2 חדרים
שירותים
302 חדר 1
303 2 חדרים
ארון קומה 3
2 × Buscomm · מתג PoE
קומה 2
201 חדר 1
204 2 חדרים
שירותים
202 חדר 1
203 2 חדרים
ארון קומה 2
2 × Buscomm · מתג PoE
קומה 1
101 חדר 1
104 2 חדרים
שירותים
102 חדר 1
103 2 חדרים
ארון קומה 1
2 × Buscomm · מתג PoE
עמוד
Cat6A / Cat7
קרקע
קבלה – עמדת אחות
טלפון אנדרואיד ACE52190200
שירותים ציבוריים: 2 T + LP
ארון ראשי בקרקע
שרת ACE51010103
מתג Buscomm · PoE

ב · טופולוגיה של דירה

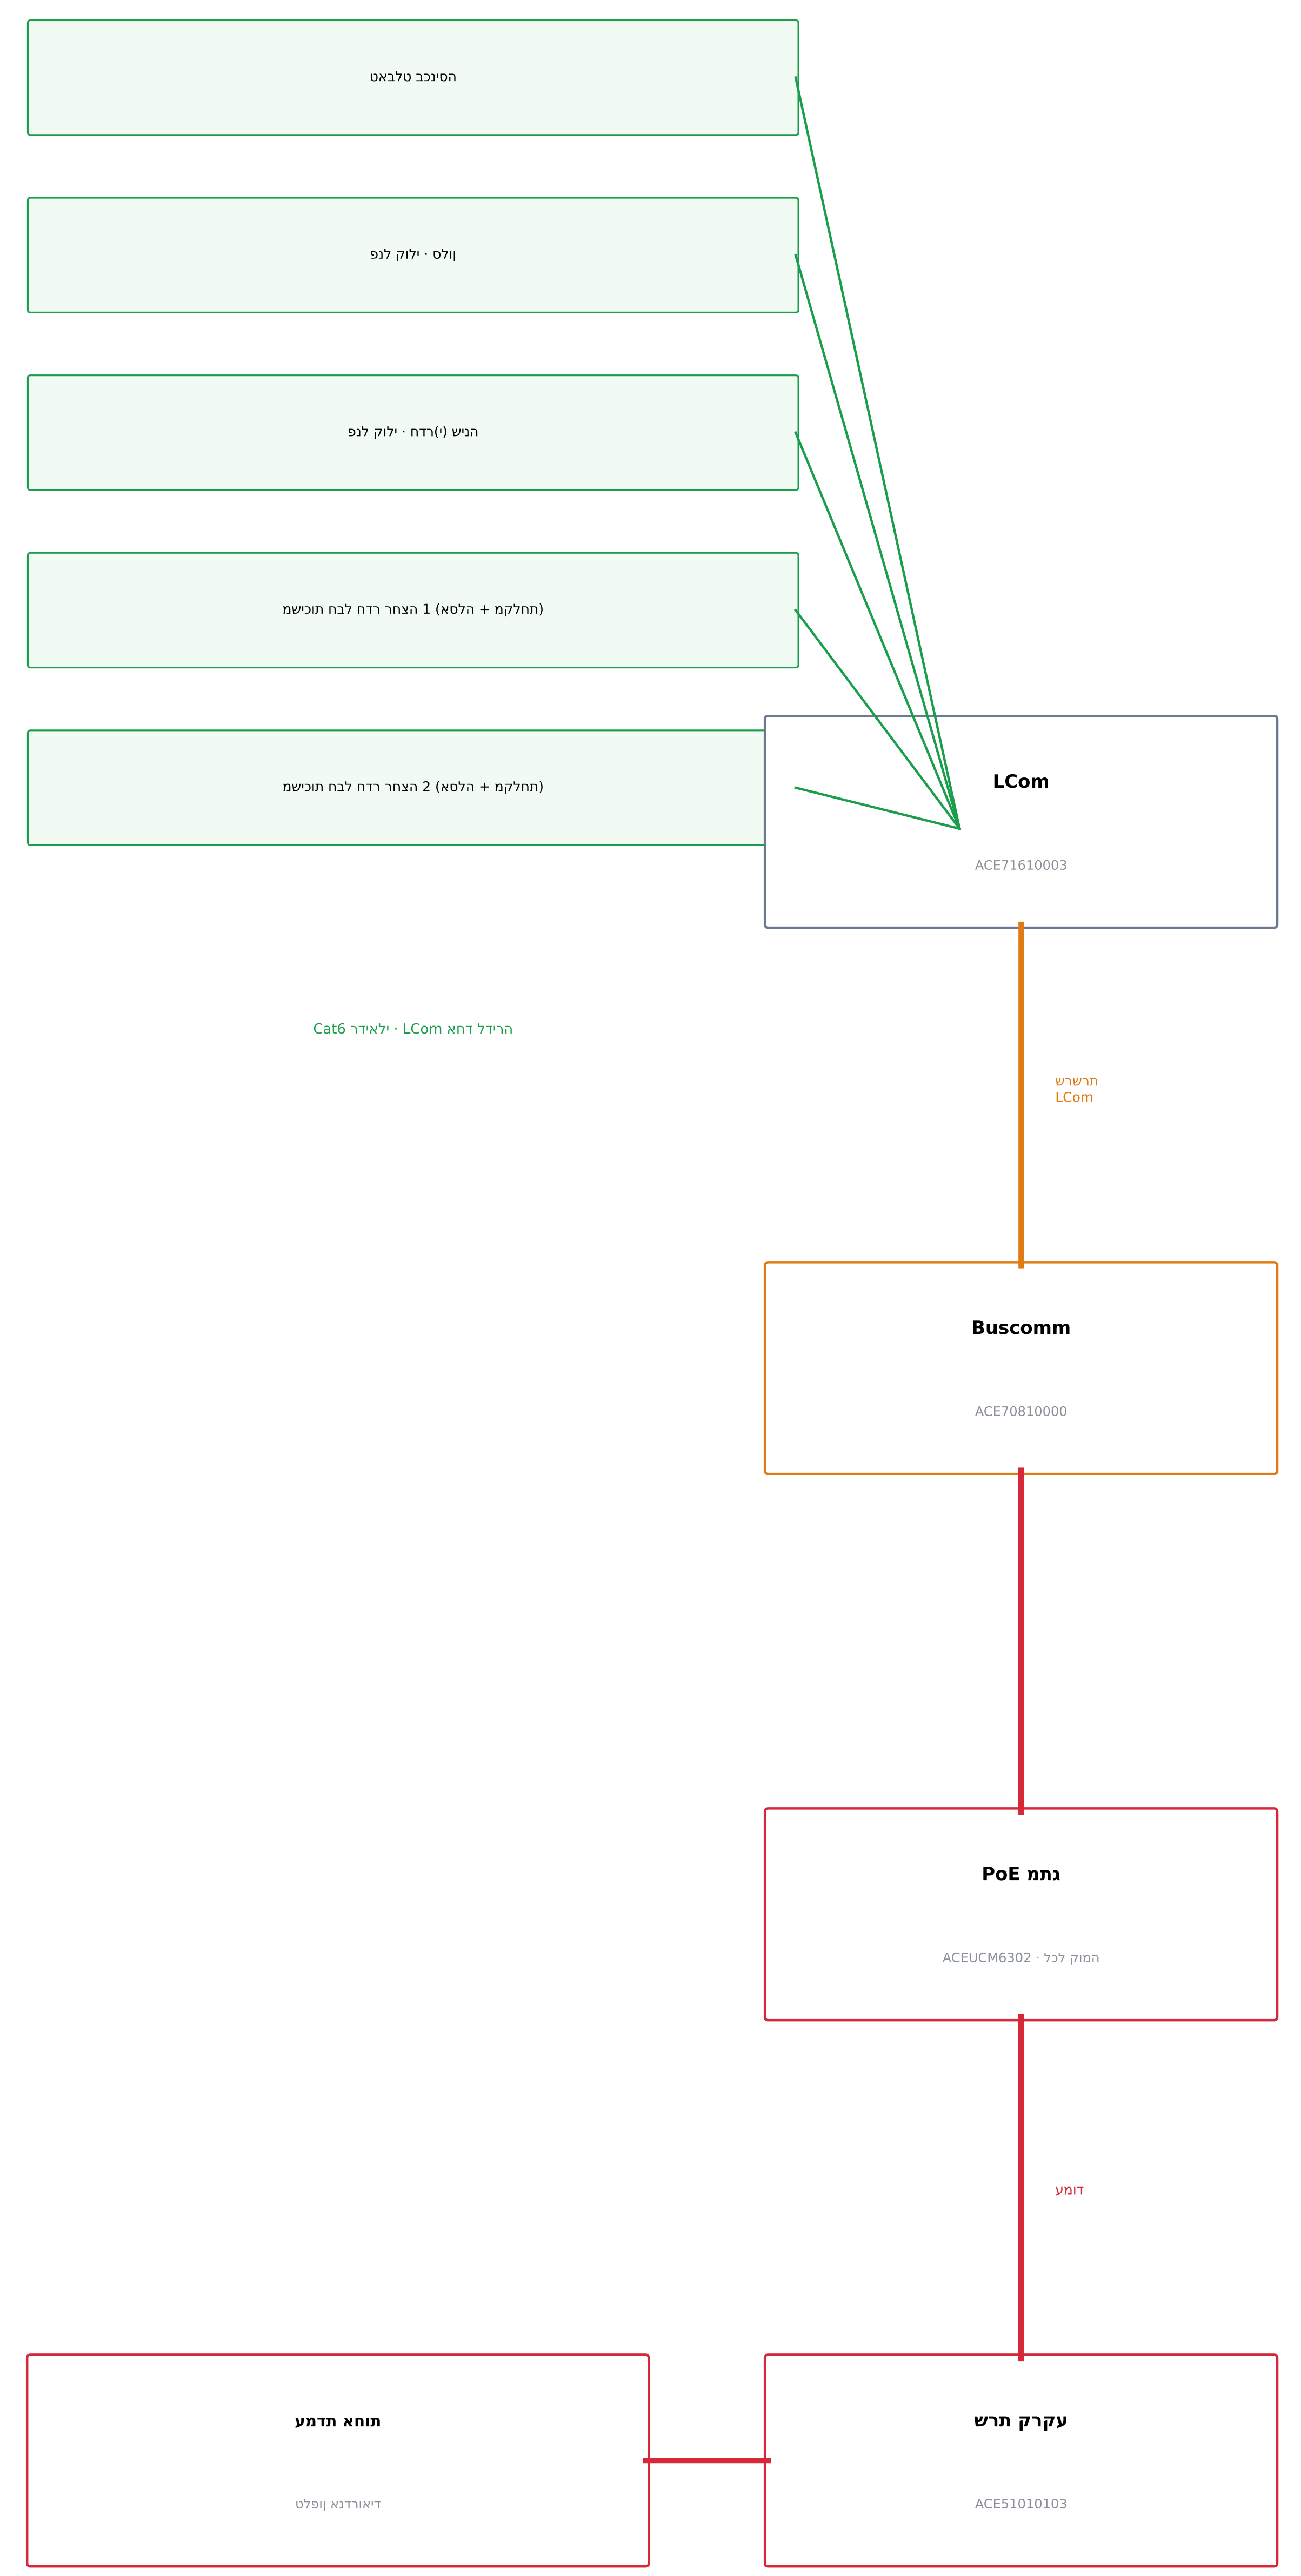
טאבלט בכניסה
סלון · פנל קולי
חדר(י) שינה · פנל קולי
משיכות חבל חדר רחצה 1 (אסלה + מקלחת)
משיכות חבל חדר רחצה 2 (אסלה + מקלחת)
LCom
ACE71610003
LCom אחד לדירה · ידיאלי Cat6
שרשרת
LCom
Buscomm
ACE70810000
מתג PoE
ACEUCM6302 · לכל קומה
עמוד
עמדת אחות
טלפון אנדרואיד
שרת קרקע
ACE51010103

NOTES · הערות

1. 8 קומות זהות עם 4 דירות
(2 דירות חדר שינה אחד ו-2 דירות שני חדרי שינה).

2. בכל קומה: ארון עם 2 Buscomm
ומתג PoE.

3. שרשרת 1: x01 ← x04 ← שירותים ציבוריים.
שרשרת 2: x02 ← x03.

4. המתגים מחוברים דרך העמוד
עד הארון הראשי בקרקע.

5. הקריאות מגיעות בדיבור לטלפון
האנדרואיד בעמדת האחות.

6. כל המערכת PoE.

7. כמויות ראשוניות: לאמת
מול Advantecnia ובאתר.

מגדלי ים התיכון · דיור מוגן
קריאת אחות – קרקע + 8 קומות · 32 דירות
מערכת: ACE BG · Advantecnia   הוכן ע"י: Telab International

תרשים אנכי וטופולוגיה

Riser diagram and topology

SCALE · קנה מידה	DATE · תאריך	REV	גיליון
S/E	15/10/2026	B	08

בסיס: תוכניות האדריכל L5 (מסד זוג / Triplet) · מידות במטרים
פורמט A1 · מהדורה B – על התכנית האמיתית

רשימת חומרים – כל הבניין (קרקע + 8 קומות · 32 דירות · 10 שירותים ציבוריים)

קוד	**תיאור**	**כמות**	**הערה**
דירות (32)			
TAB	טאבלט בכניסה (iPad / אנדרואיד) – קריאה ודיבור	**32**	1 לכל דירה
VOZ	ACE82182451 – פנל קריאה קולי עם לחצנים	**80**	סלון + כל חדר שינה
TI/TD	משיכת חבל – ACE40320303W (אסלה ומקלחת)	**128**	4 לכל דירה
LC	LCom – ACE71610003	**32**	1 לכל דירה
שירותים ציבוריים (10)			
T	ACE40320303W – משיכת חבל	**10**	8 קומות + 2 בקרקע
LP	ACE41020309 – מנורת מסדרון	**10**	מעל כל דלת
LC	LCom – ACE71610003	**9**	1 לכל קומה + 1 בקרקע
ארונות ומרכזייה			
BC	Buscomm – ACE70810000	**17**	2 לכל קומה + 1 בקרקע
SW	מתג PoE – ACEUCM6302	**9**	1 לכל קומה + קרקע
GAB	ארון קיר 12U (Tripp Lite SRW12US) עם פאץ' פאנל	**8**	1 לכל קומה
GAB-PB	ארון ראשי עומד עם UPS	**1**	קרקע
SRV	Advantecnia – ACE51010103 שרת + תוכנת	**1**	קרקע
TEL	ACE52190200 – טלפון שולחני אנדרואיד	**1**	עמדת אחות
כבלים (+ 15% רזרבה)			
—	Cat6 רדיאלי בתוך הדירות (ירוק)	**1700 m**	183 מ' לקומה
—	Cat6 / Cat7 שרשרת LCom ← Buscomm (כתום)	**780 m**	82 מ' לקומה
—	Cat6A / Cat7 ארונות ועמוד (אדום)	**100 m**	כולל עמוד

NOTES · הערות

1. כמויות מחושבות מהמודל (קומה טיפוסית × 8 + קרקע).
2. אורכי כבל נמדדו על התוואי המשורטט, + 15%.
3. מחירים: לפי מחירון Advantecnia העדכני.
4. לאמת באתר לפני רכישה.

מגדלי ים התיכון · דיור מוגן

קריאת אחות – קרקע + 8 קומות · 32 דירות

הוכן ע"י: Telab International   מערכת: ACE BG · Advantecnia

רשימת חומרים

Bill of materials

SCALE · קנה מידה	DATE · תאריך	REV	גיליון
S/E	**15/10/2026**	**B**	**09**

בסיס: תוכנית האדריכל L5 (זוג מסד / Triplet) · מידות במטרים

פורמט A1 · מהדורה B – על התוכנית האמיתית

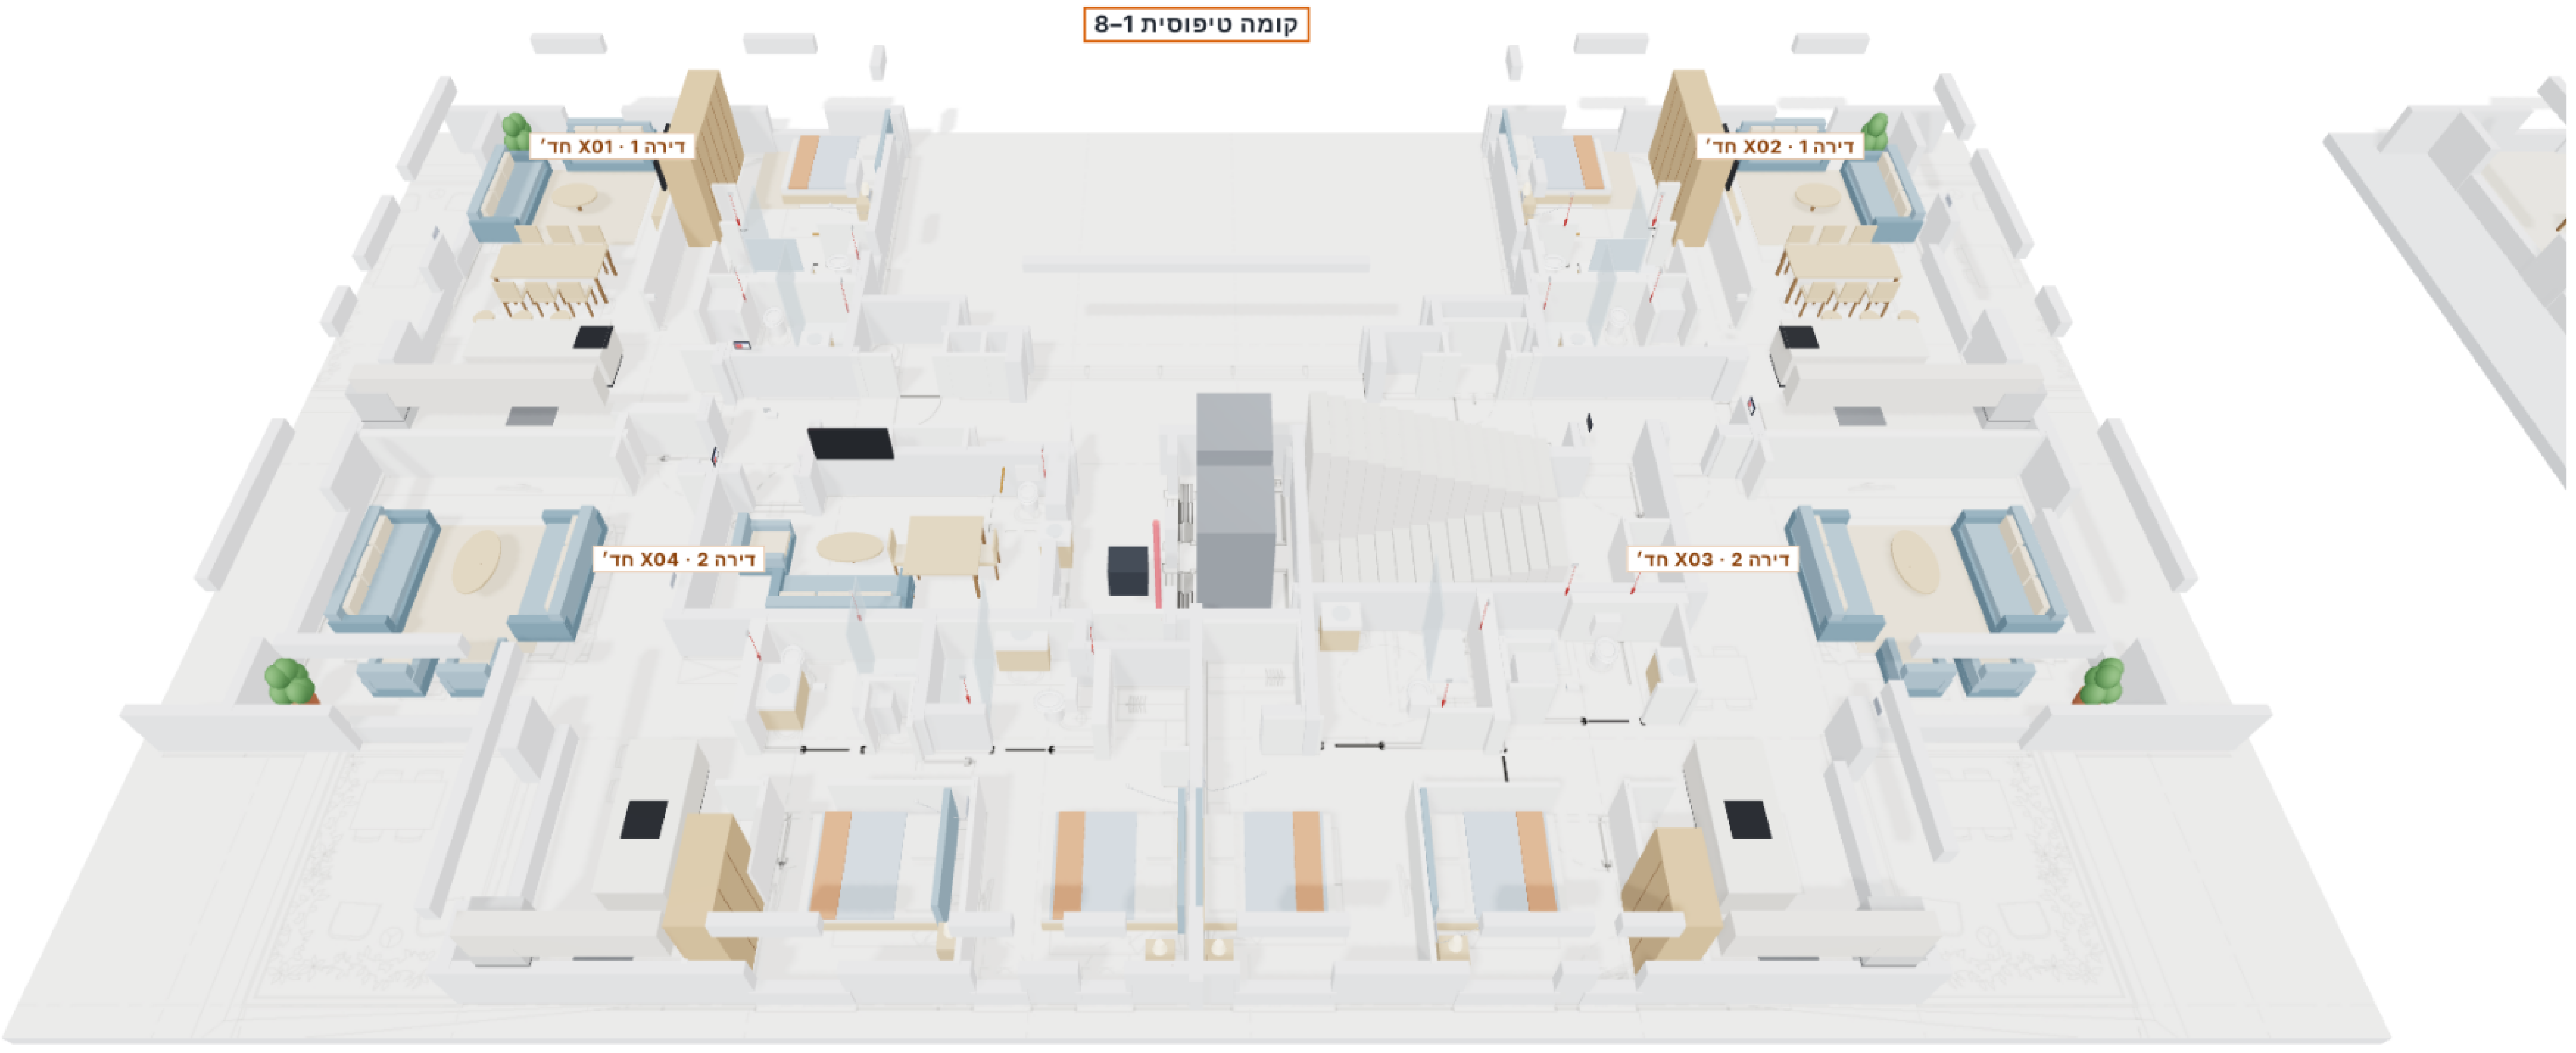
קומה טיפוסית 1–8
דירה 1 · X01 חד'
דירה 1 · X02 חד'
דירה 2 · X04 חד'
דירה 2 · X03 חד'

א · קומה טיפוסית – 4 דירות

ב · טאבלט בכניסה

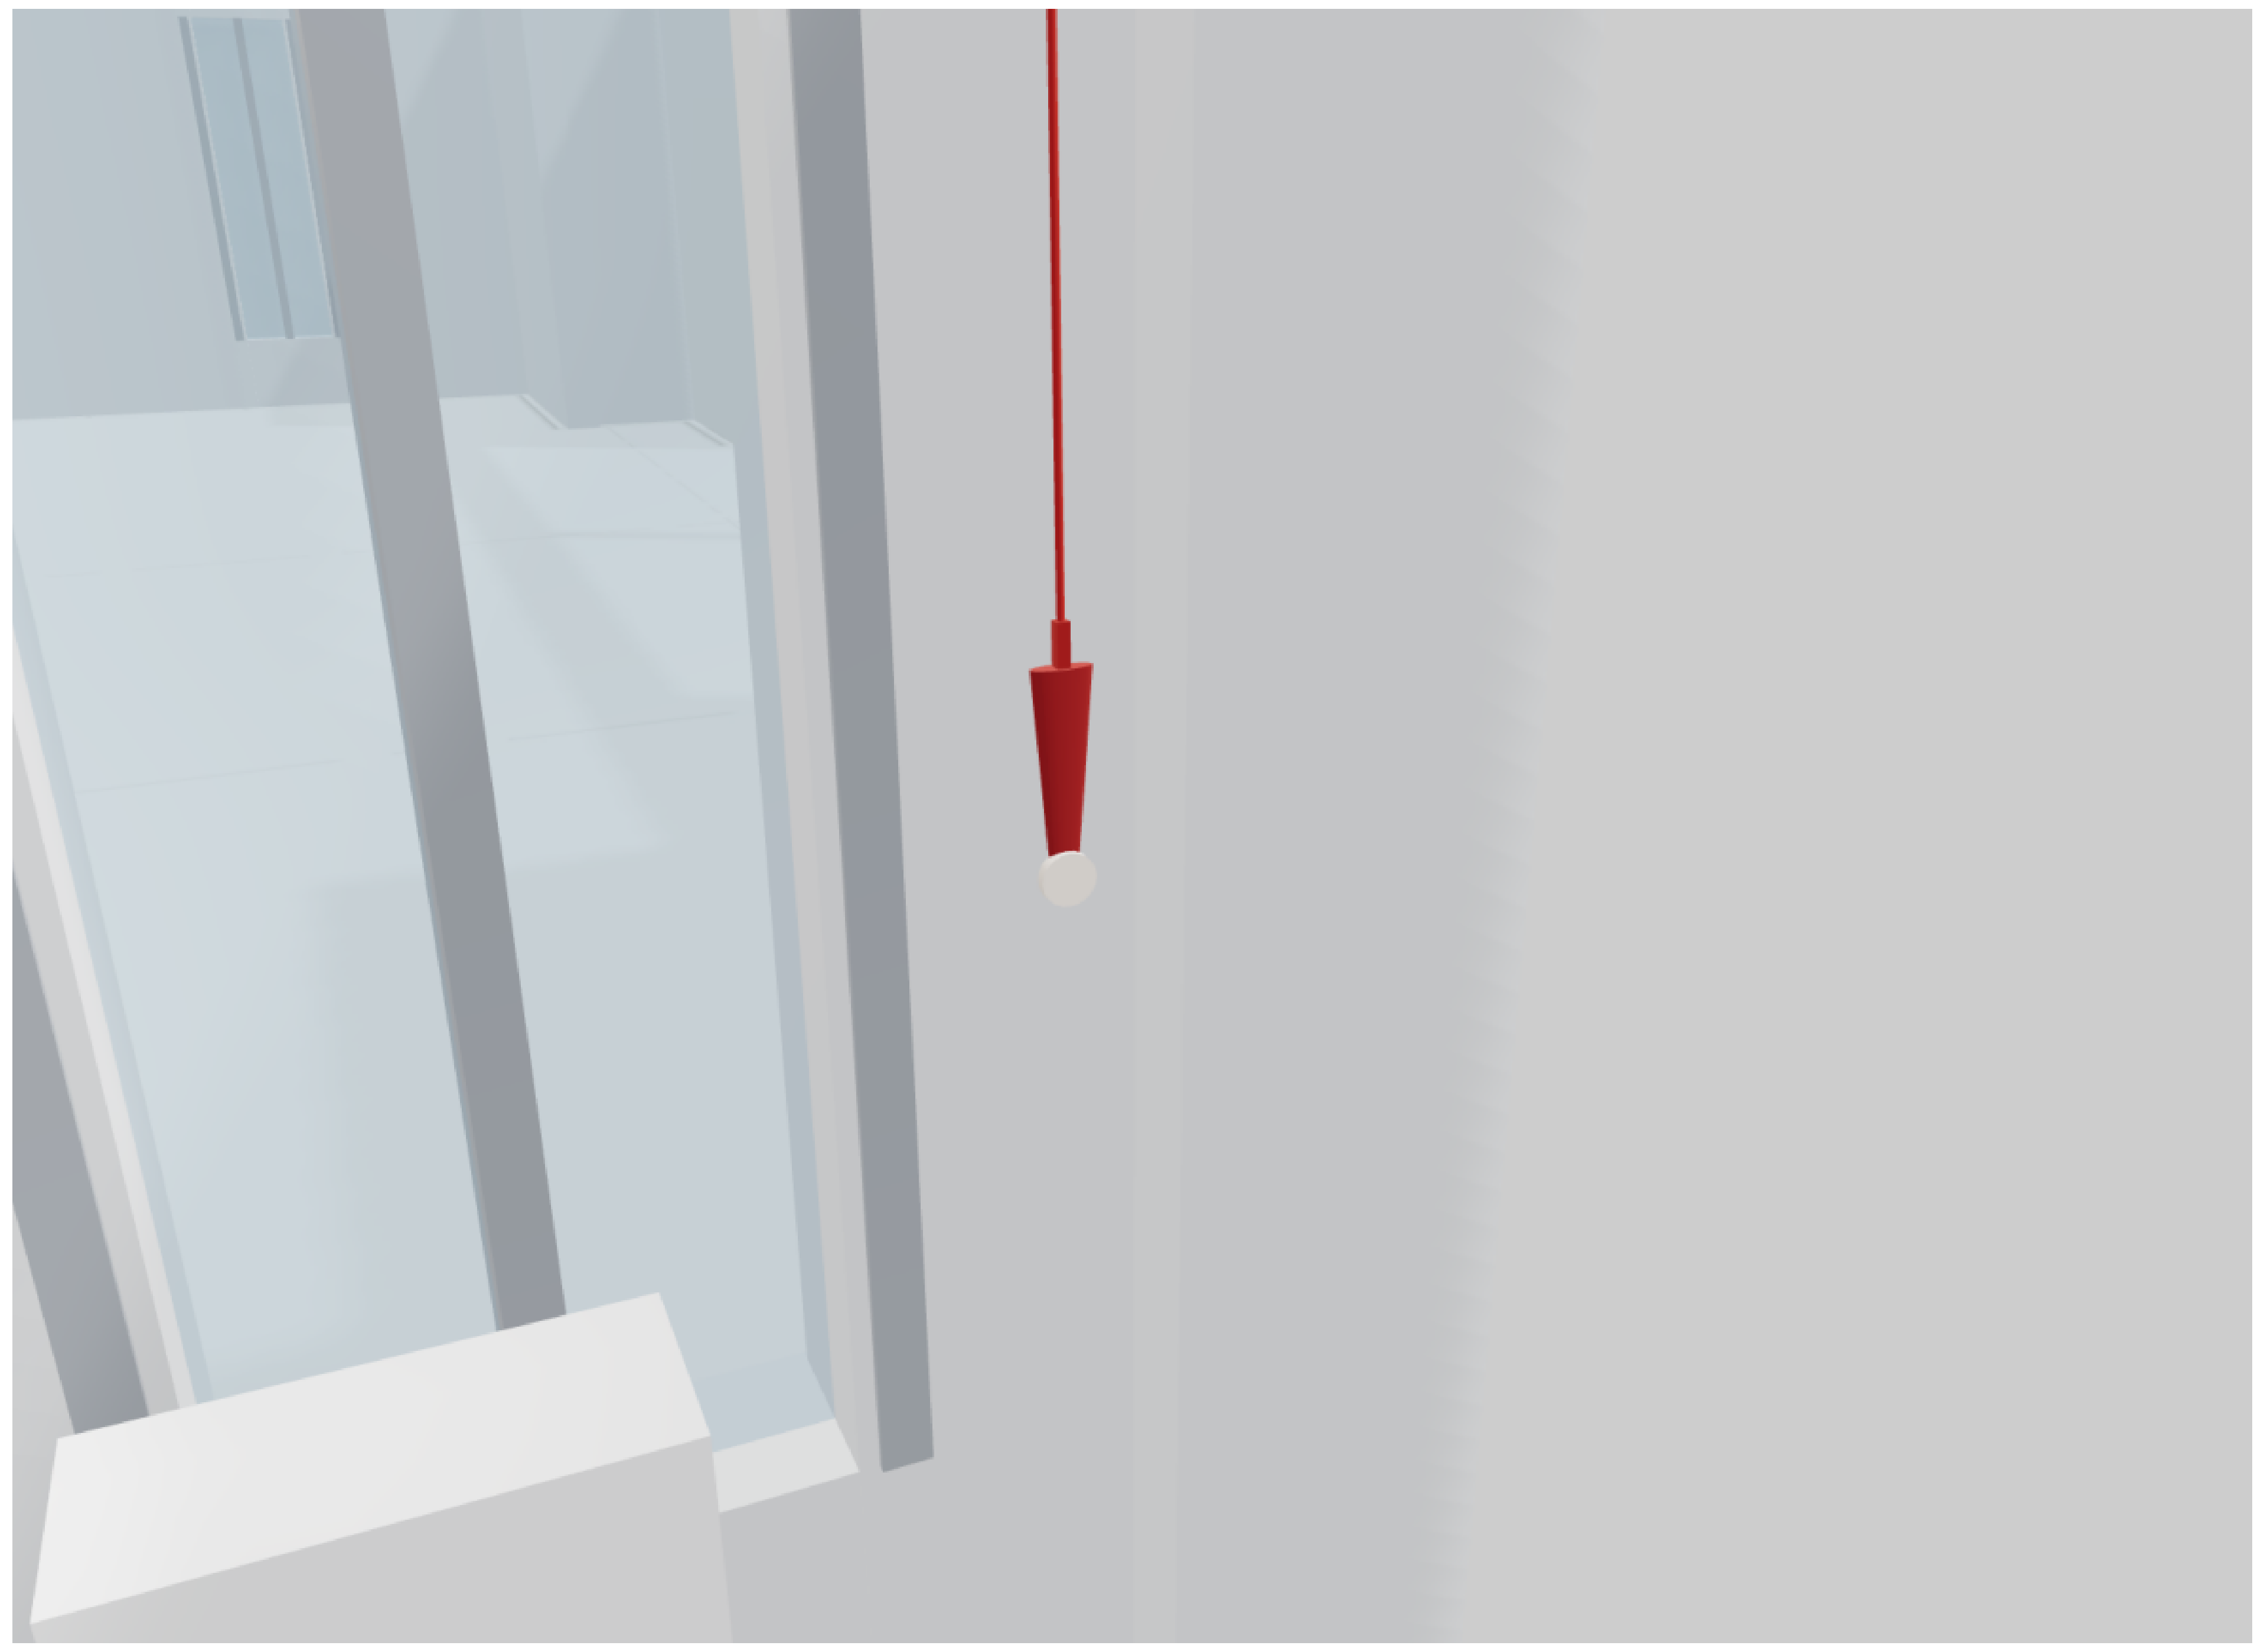

ד · חדר רחצה – משיכות חבל באסלה ובמקלחת

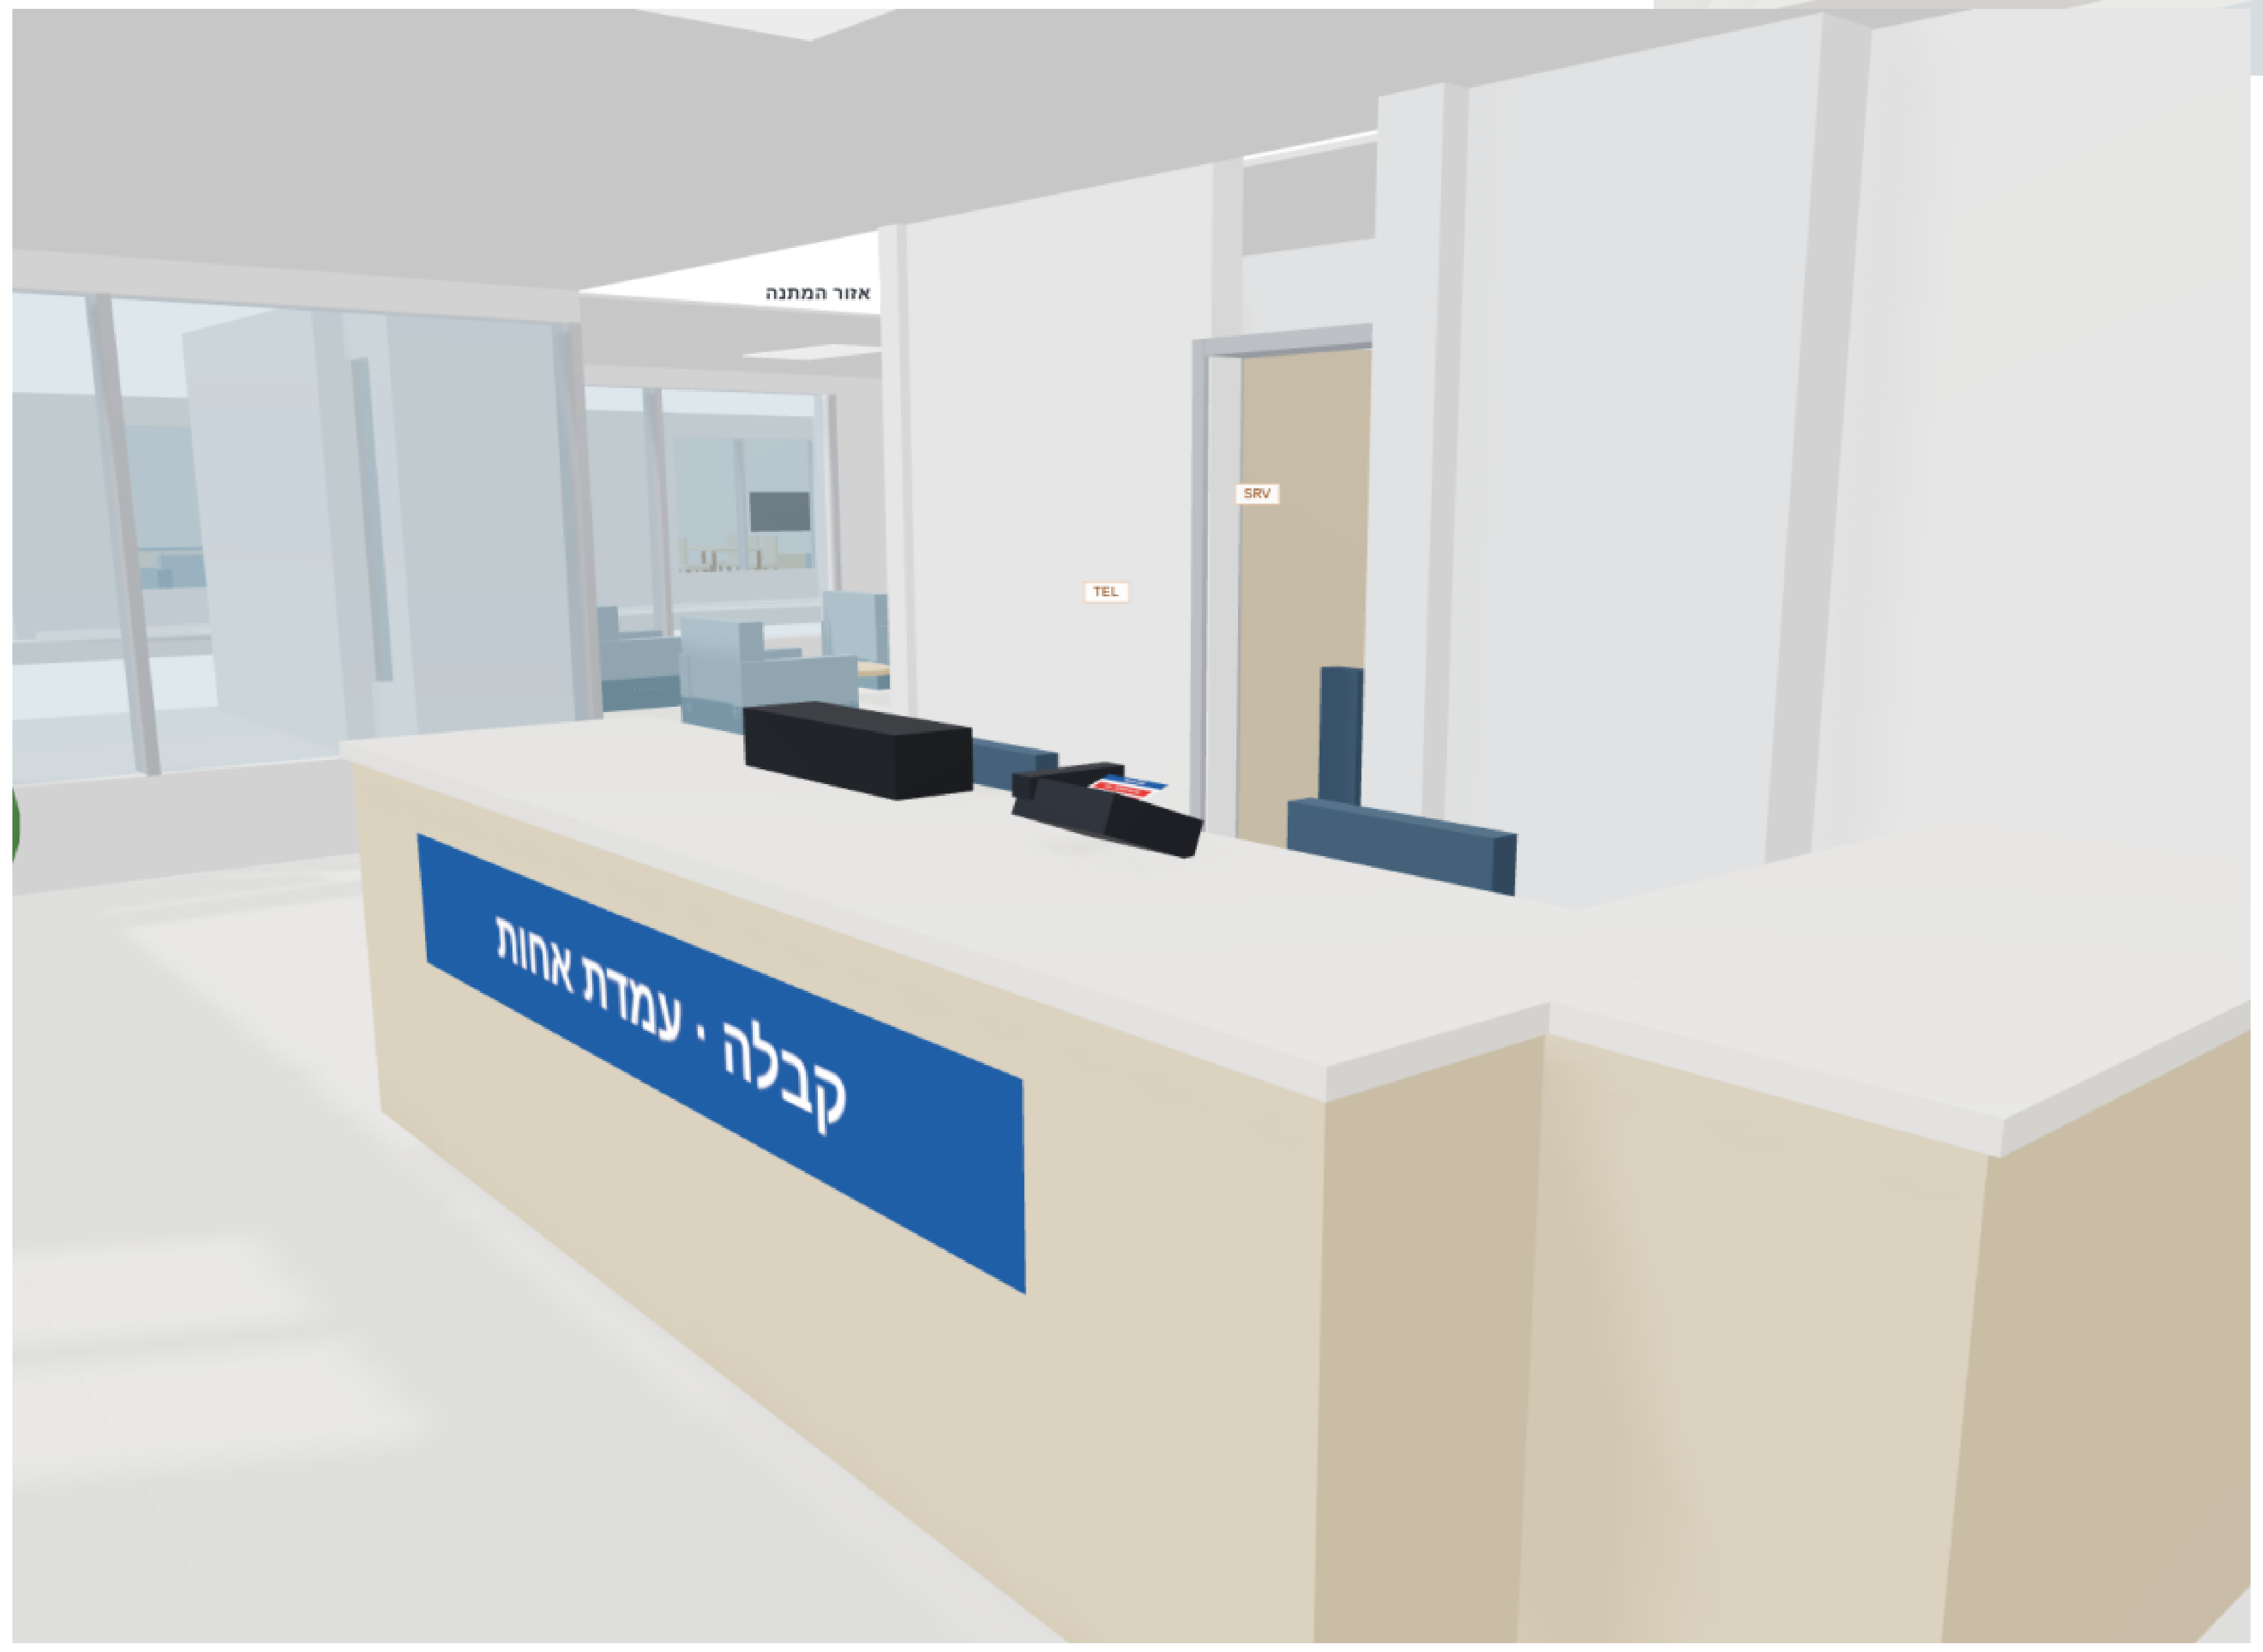
אזור המתנה
SRV
TEL
קבלה · עמדת אחות

ה · קרקע – עמדת אחות

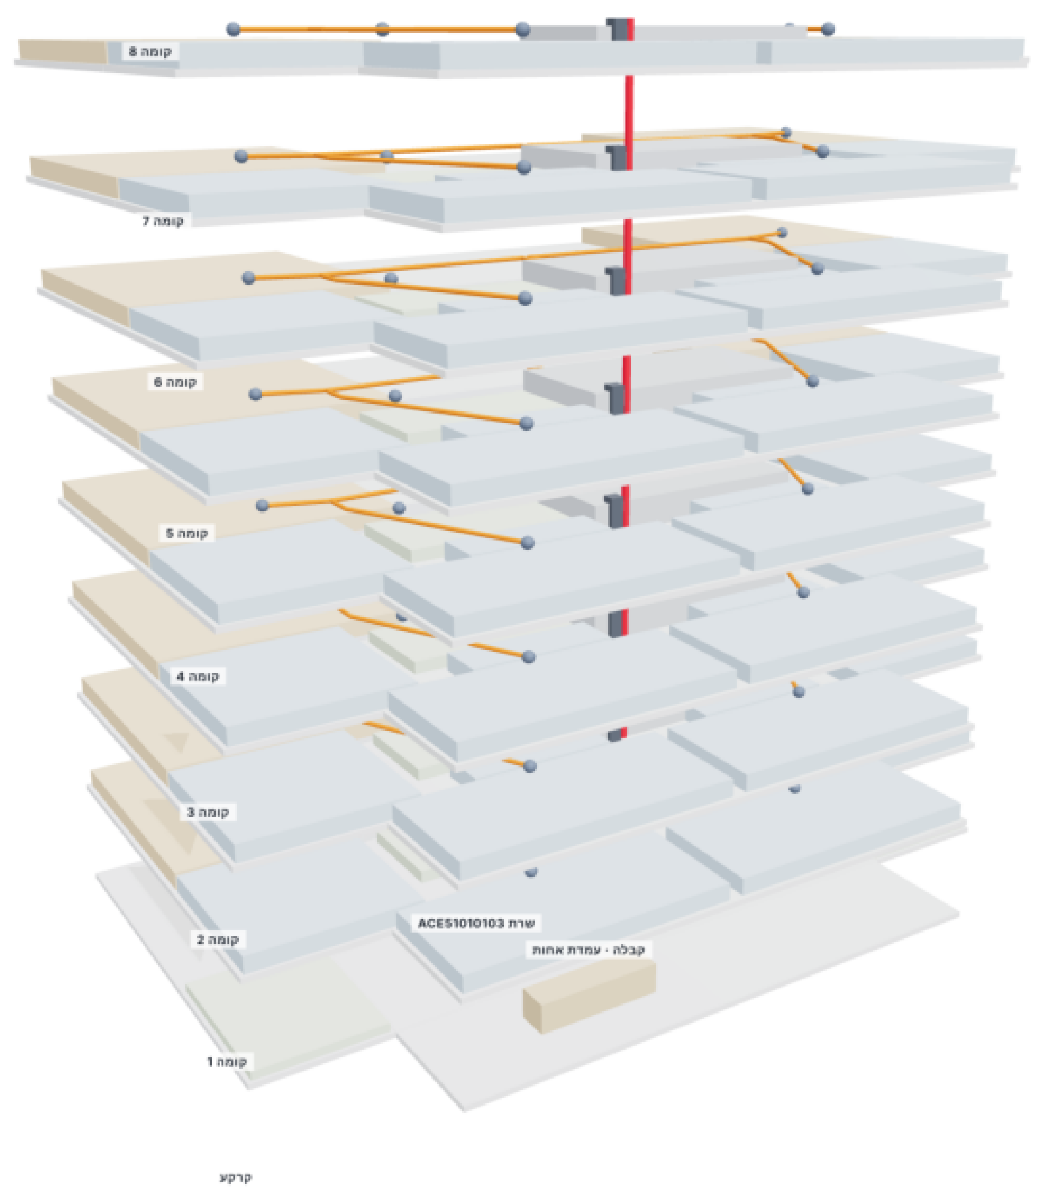
קומה 8
קומה 7
קומה 6
קומה 5
קומה 4
קומה 3
קומה 2
קומה 1
שרת ACES1010103
קבלה · עמדת אחות
קרקע

ו · בניין קרקע + 8 קומות

מגדלי ים התיכון · דיור מוגן

קריאת אחות – קרקע + 8 קומות · 32 דירות

מערכת: ACE BG · Advantecnia   הוכן ע"י: Telab International

מבטים תלת-ממדיים

3D views

SCALE · קנה מידה	DATE · תאריך	REV	גיליון
S/E	15/10/2026	B	10

בסיס: תוכנית האדריכל L5 (מסד עוז / Triplet) · מידות במטרים

פורמט A1 · מהדורה B – על התוכנית האמיתית

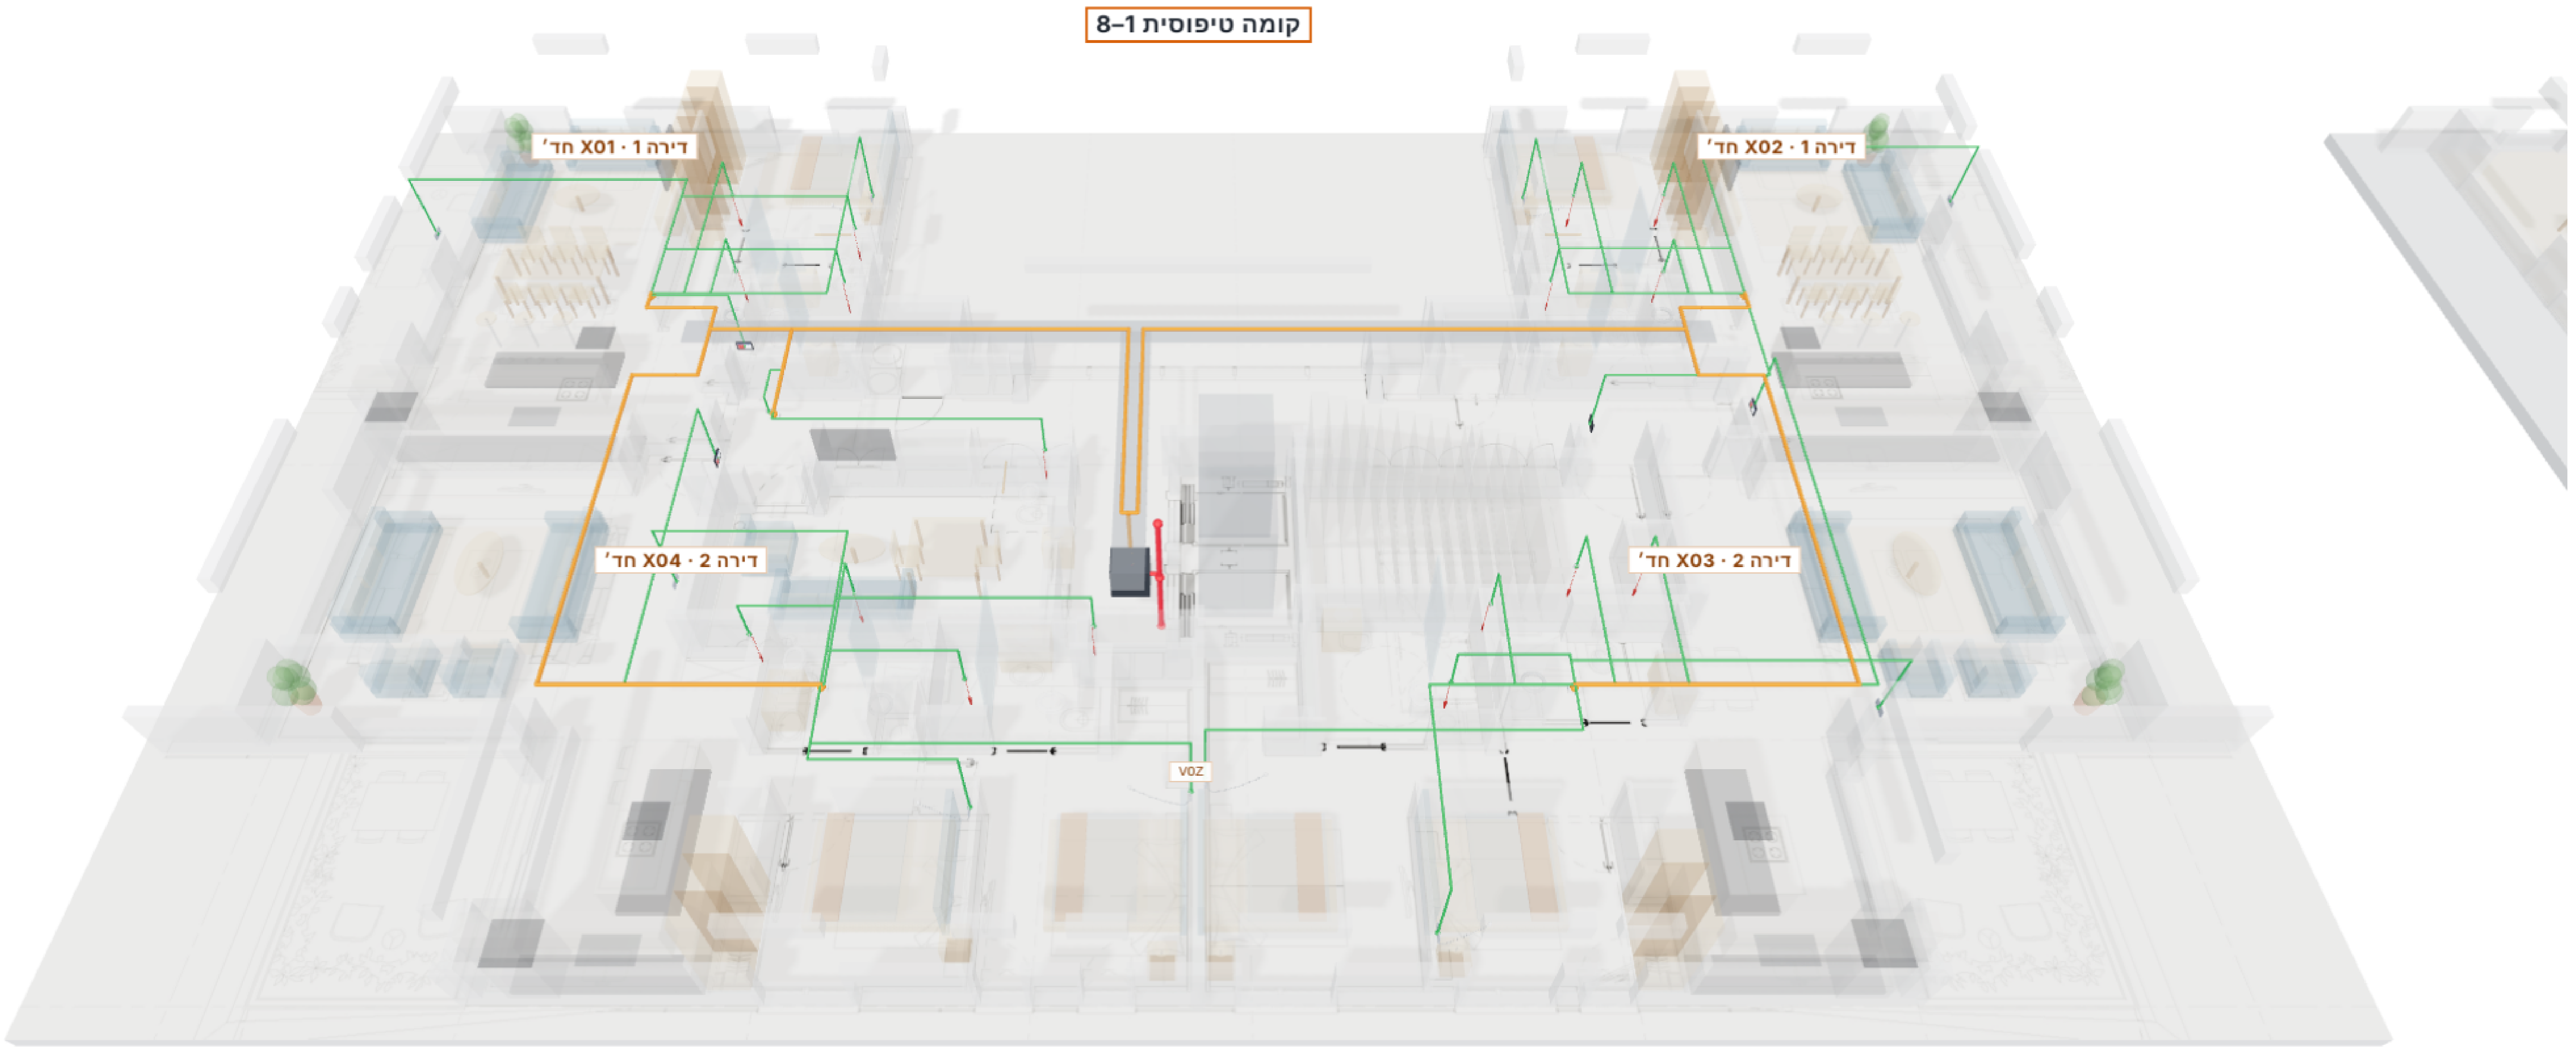

(תשר םודא · LCom תרשרש םותכ · ילאידר קורי) טוויח – תיסופיט המוק · א

הלבקו יבול – עקרק תמוק · ב

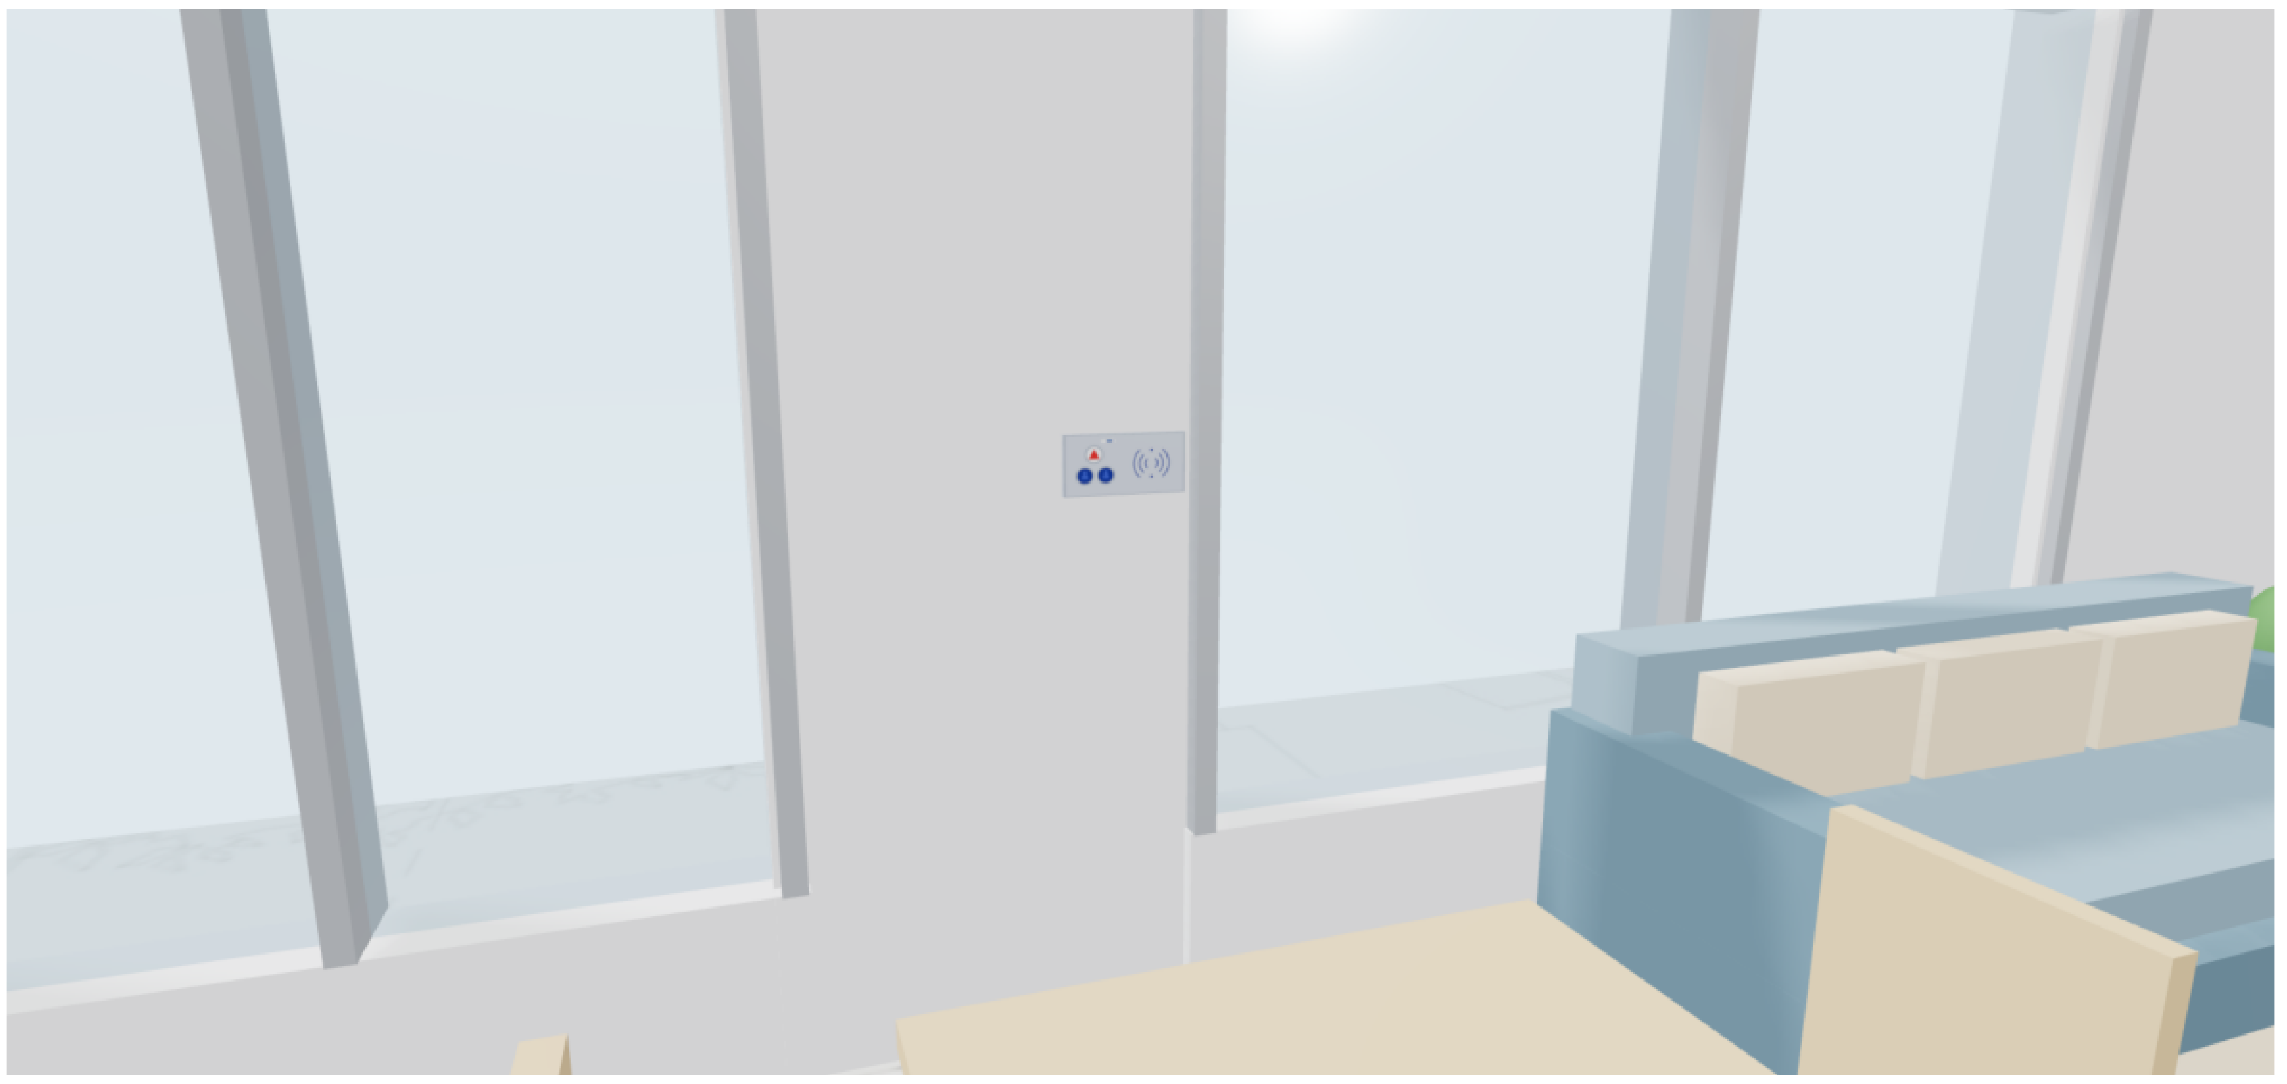

םינצחל םע ילוק לנפ – ןולס · ג

COLOURS · COLORES · םיעבצ

🟩 Cat6 ידאילי: לכ ןקתה ← LCom לש הרידה
Cat6 radial: each device → apartment LCom · Cat6 ידאילי: לכ ןקתה ← LCom לש הרידה

🟧 Cat6 / Cat7 תרשרש: LCom ← LCom ← Buscomm ןוראב
Cat6 / Cat7 chain: LCom → LCom → Buscomm · Cat6 / Cat7 תרשרש: LCom ← LCom ← Buscomm

🟥 Cat6A / Cat7 תשר: Buscomm ← גתמ ← דומע ← תרש עקרק
Cat6A / Cat7 network: Buscomm → switch → riser → GF server · Cat6A / Cat7 תשר: Buscomm ← גתמ ← דומע ← תרש

ןגומ רויד · ןוכיתה םי ילדגמ
קריאת תוחא – עקרק + 8 תומוק · 32 תוריד
Telab International :הכוןי"ע   ACE BG · Advantecnia :תכרעמ

טוויח – םיידממ-תלת םיטבמ
3D views – wiring

SCALE · הדימ הנק
S/E

DATE · ךיראת
15/10/2026

REV
B

ןויליג
11

סיסב: תונכית האדירכל L5 (םסד זוע / Triplet) · םידות במטריס
טמרופ A1 · ההמדורה B – לע תונכותה תיתימאה