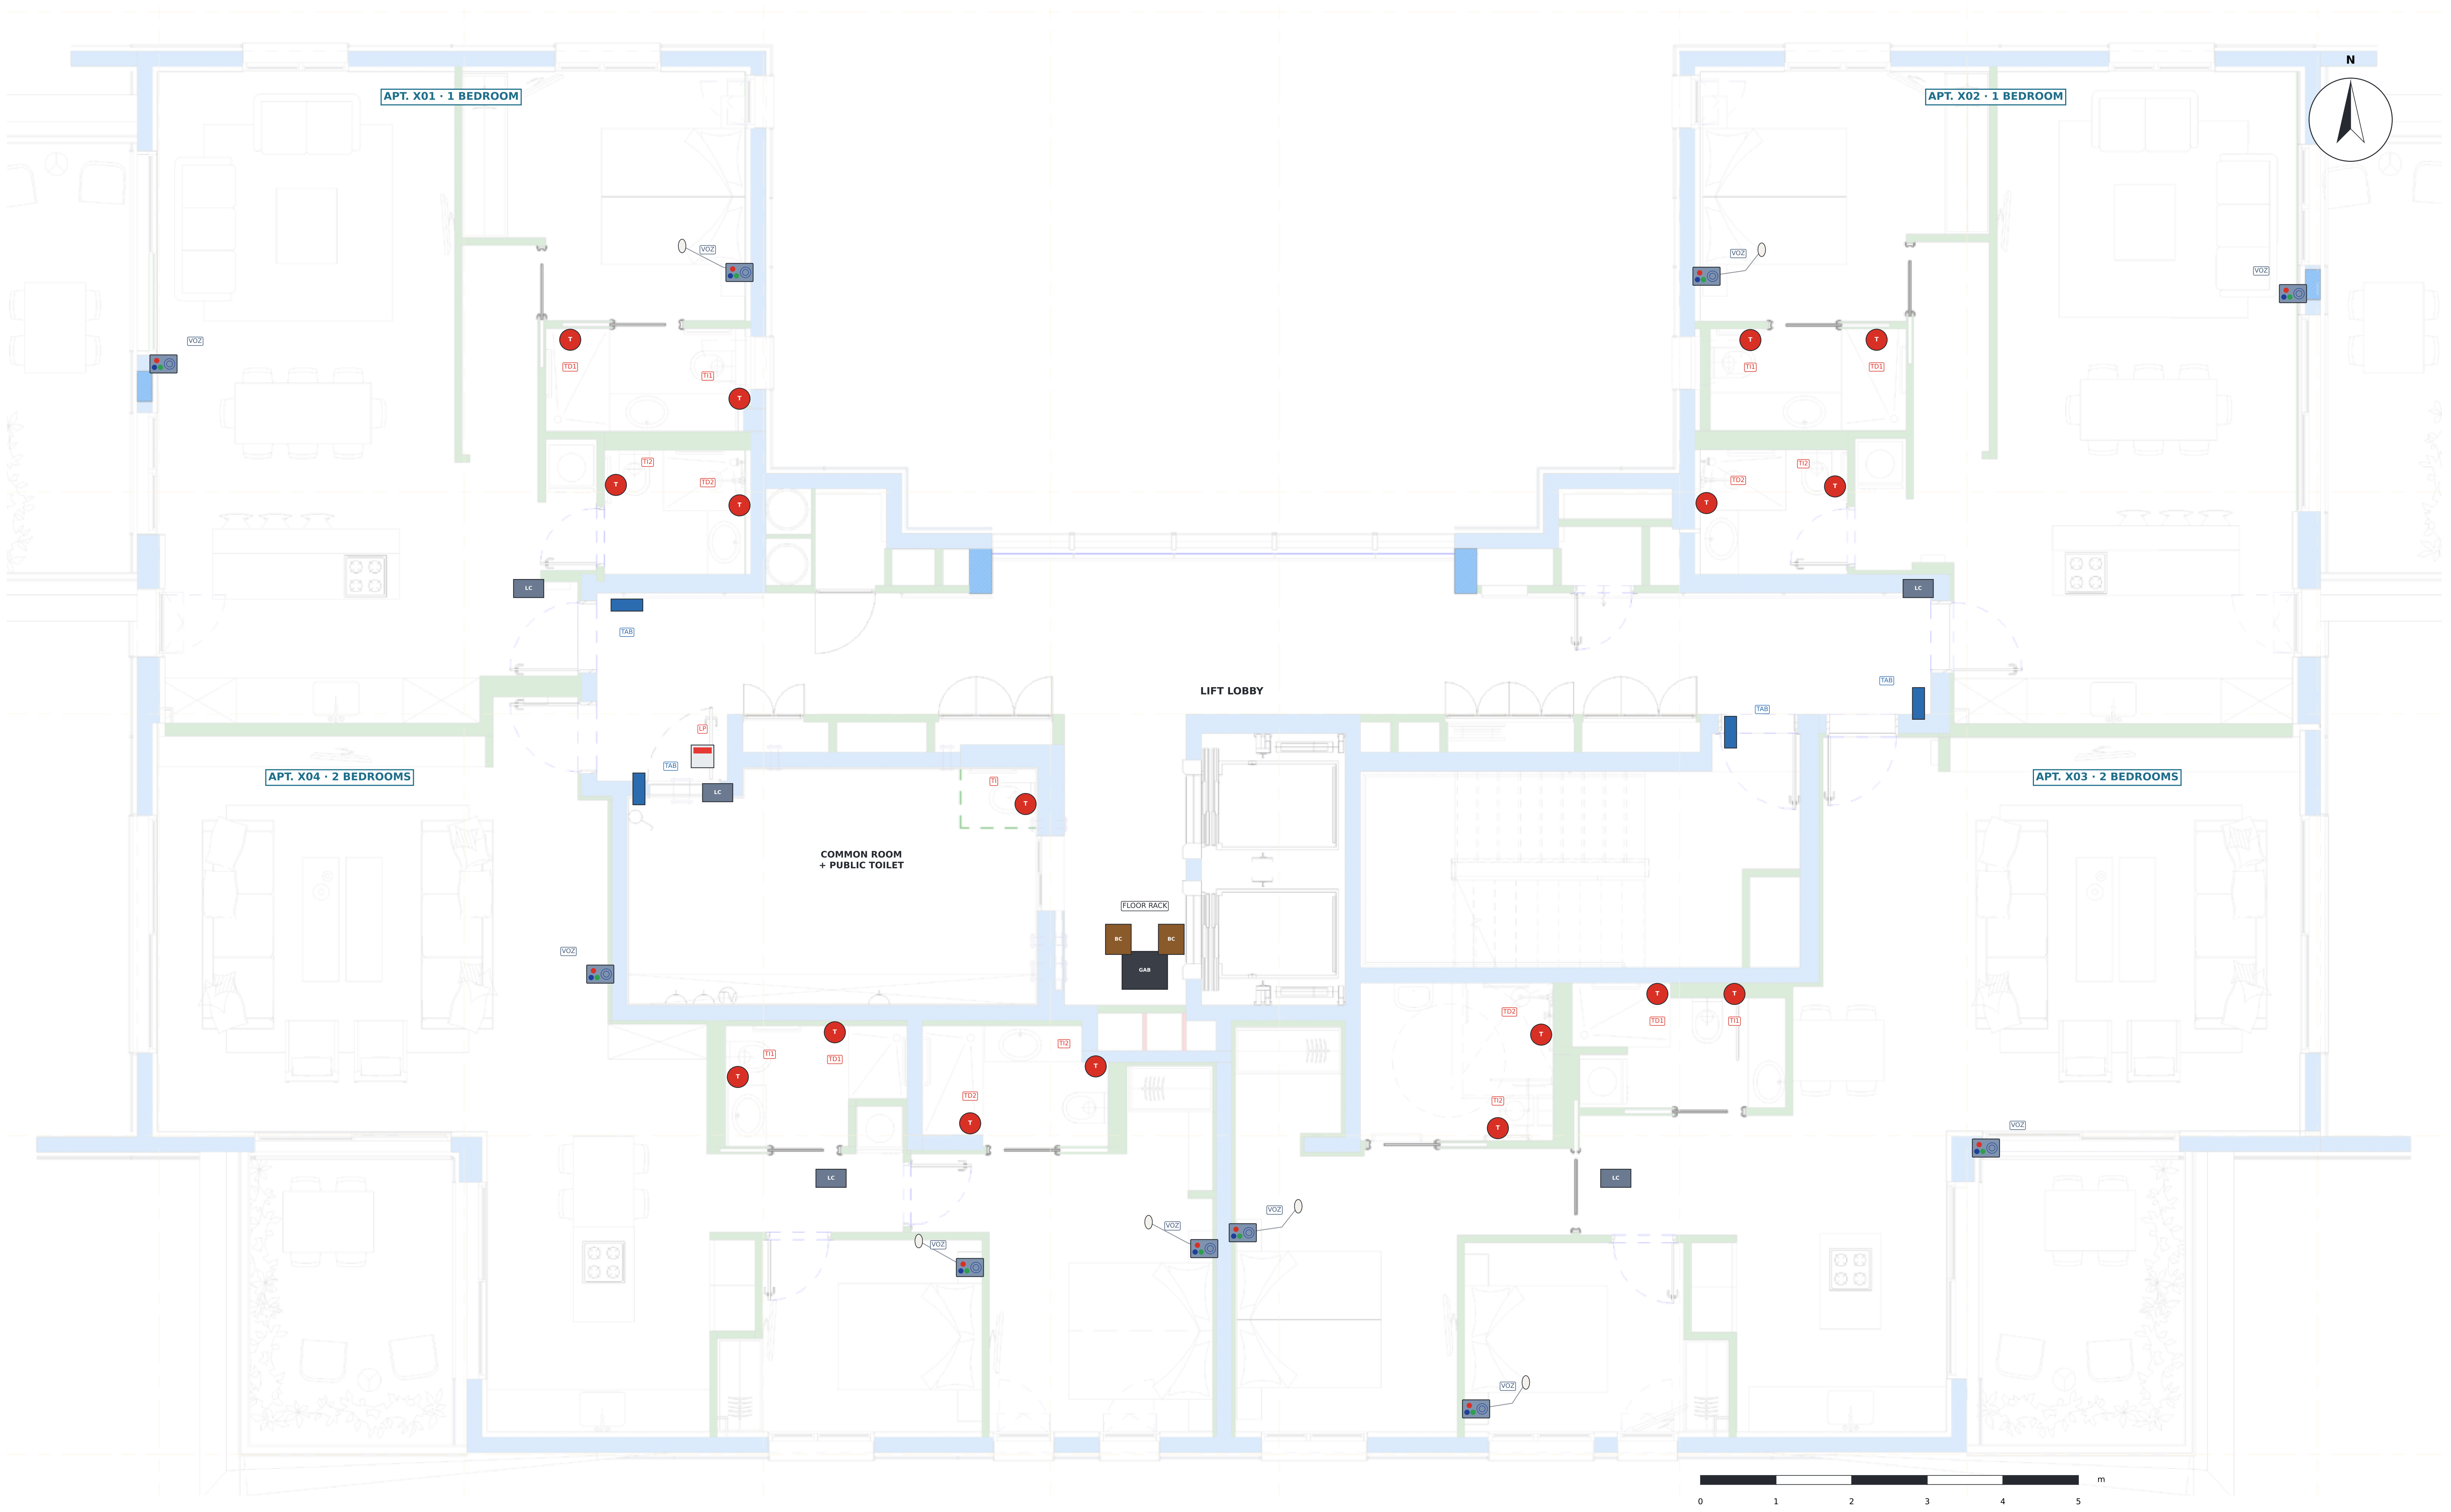

DEVICES · EQUIPOS · ציוד

- TAB · Door tablet (iPad / Android) – call and voice, h 1.40 m
  Door tablet – call and voice · טאבלט כניסה – קריאה ודיבור
- VOZ · Voice panel with buttons ACE82182451 – living room and bedrooms, h 1.20–1.30 m
  Voice panel with buttons – living room and bedrooms · פנל קולי עם לחצנים – סלון וחדרי שינה
- Call pear next to the bed (bedrooms)
  Call pear next to the bed (bedrooms) · אגס קריאה ליד המיטה
- T · TI / TD · Pull-cord ACE40320303W – toilet and shower, h 1.85 m
  Pull-cord – toilet and shower, h 1.85 m · משיכת חבל – אסלה ומקלחת, גובה 1.85 מ'
- LP · Corridor light ACE41020309 – above each public toilet door
  Corridor light – above each public toilet door · מנורת מסדרון – מעל דלת כל שירותים ציבוריים
- LC · LC · LCom ACE71610003 – apartment hub (ceiling)
  LCom – apartment hub (ceiling) · LCom – מרכז דירה (תקרה)
- BC · BC · BoxCom ACE70810000 – bus hub for several apartments (ceiling)
  BoxCom – bus hub for several apartments (ceiling) · BoxCom – מרכז באס לכמה דירות (תקרה)
- GAB · 12U floor rack: D-Link DES-1210-28P PoE switch (24 PoE ports)
  Floor rack: D-Link DES-1210-28P PoE switch · ארון קומה: מתג PoE D-Link DES-1210-28P

QUANTITIES PER FLOOR × 8 FLOORS

Code	Device	Per floor	8 floors
TAB	Door tablet	4	32
VOZ	Voice panel with buttons	10	80
TI/TD	Pull-cord (toilet + shower)	17	136
LP	Corridor light (public toilet)	1	8
LC	LCom	5	40
BC	BoxCom	2	16
SW	PoE switch	1	8

NOTES · NOTAS

1. Base: architectural plan L5 (typical floor) – all 8 floors are identical: 4 apartments per floor, 32 in total.
2. Apartments x01 and x02: 1 bedroom, living room with kitchen and 2 bathrooms. Apartments x03 and x04: 2 bedrooms and 2 bathrooms.
3. Tablet at the door of each apartment (iPad / Android) to call and talk to the nurse.
4. Voice panel with buttons (ACE82182451) in the living room and in each bedroom; in bedrooms, with a pear next to the bed.
5. Pull-cords (ACE40320303W) at the toilet and shower of every bathroom, at 1.85 m.
6. One public toilet per floor in the common room: pull-cord + corridor light above the door. With the 2 on GF, 10 public toilets in total.
7. Floor rack next to the lifts with the D-Link DES-1210-28P PoE switch; the 2 BoxComs go on the ceiling next to it.
8. Locations per the client's marks on plan L2 (nt = voice panel, tab = tablet): see sheet 03.

שירותים קריאת אחות

Pull-cord

טבלט אנדרואיד קריאת אחות
Advantecnia
Llamada de enfermera

Door tablet (iPad / Android)

מנורה קריאת אחות

Corridor light

פנל קריאת אחות

Voice panel with buttons

MOUNTING HEIGHTS

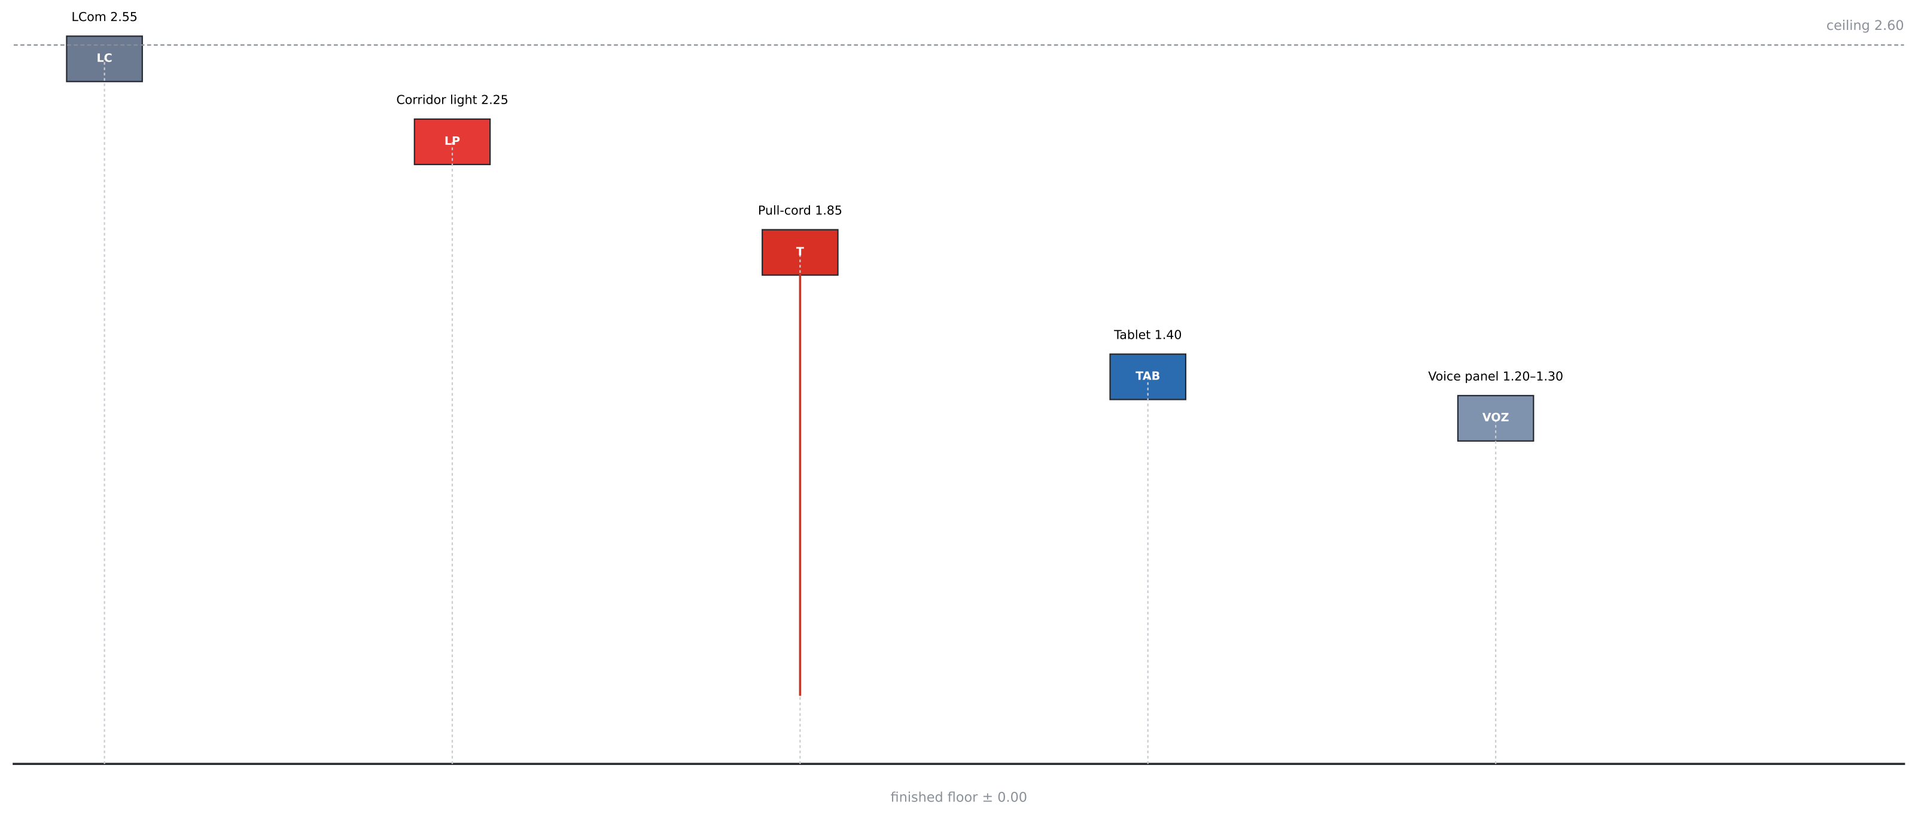

MIGDALEI YAM A TIJON · ASSISTED LIVING
Nurse call – GF + 8 floors · 32 apartments
System: ACE BG · Advantecnia Prepared by: Telab International

TYPICAL FLOOR F1–F8 · NURSE CALL

SCALE · ESCALA	DATE · FECHA	REV	SHEET
1:60	15/10/2026	B	01

Base: architect's plan L5 (Massad Oz / Triplet) · dimensions in m
A1 format · Rev. B – on the real plan

שירותים קריאת אחות

Pull-cord

Code	**ACE40320303W**
Location	Toilet and shower of every bathroom and the 10 public toilets
Height	**1.85 m**
Quantity	**138**

1

טבלט אנדרואיד קריאת אחות

TV
Advantecnia
Llamada de enfermera
Hospital
Salud y bienestar

Door tablet (iPad / Android)

Code	**Advantecnia TV**
Location	In the lobby, next to each apartment door
Height	**1.40 m**
Quantity	**32**

2

מנורה קריאת אחות

Corridor light

Code	**ACE41020309**
Location	Above each public toilet door
Height	**2.25 m**
Quantity	**10**

3

פנל קריאת אחות

Voice panel with buttons

Code	**ACE82182451**
Location	Living room and each bedroom (with pear in bedrooms)
Height	**1.20–1.30 m**
Quantity	**80**

4

GRANDSTREAM
HD

Desk phone (Android)

Code	**Grandstream**
Location	Nurse desk on GF · PoE straight to the switch
Height	**on the desk**
Quantity	**1**

5

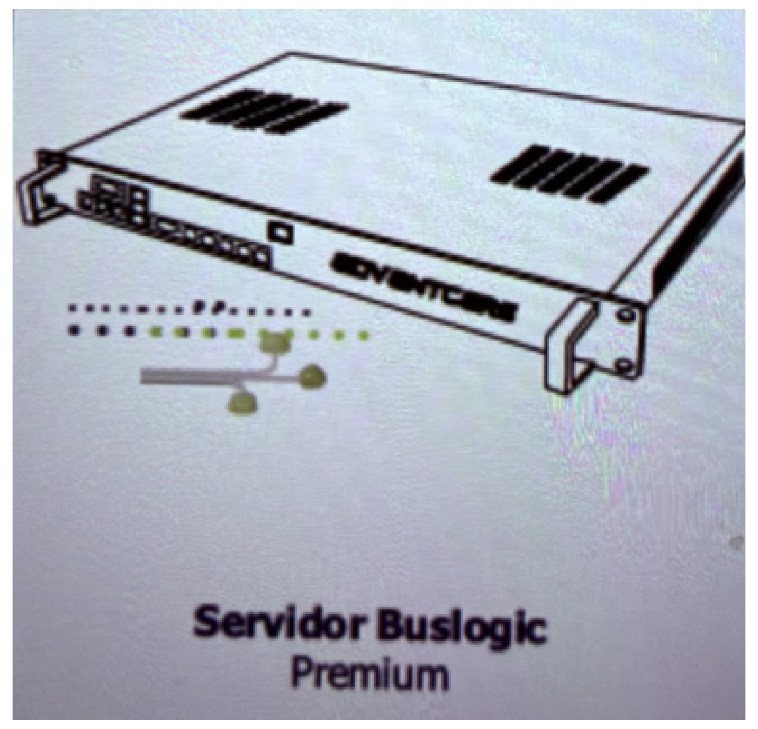

Buslogic Premium server

Code	**Advantcare**
Location	Main GF rack
Height	**in rack**
Quantity	**1**

6

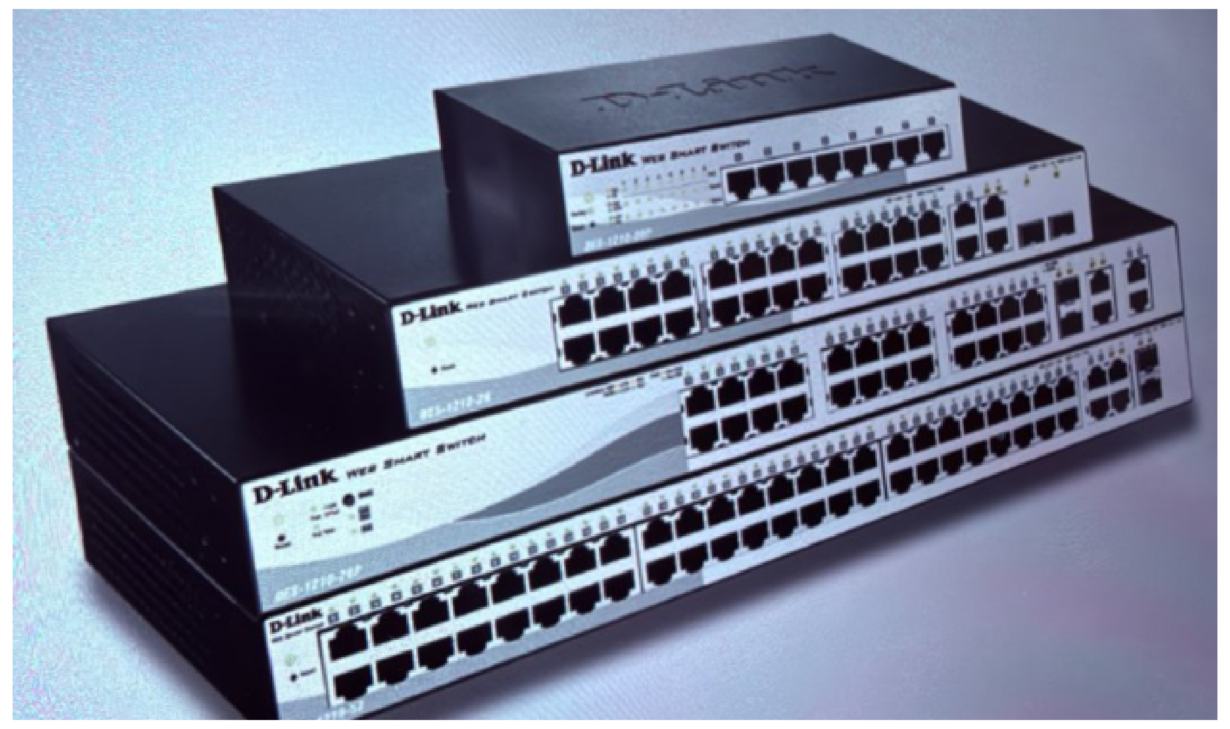

24-port PoE switch

Code	**D-Link DES-1210-28P**
Location	Rack on each floor and GF
Height	**in rack**
Quantity	**9**

7

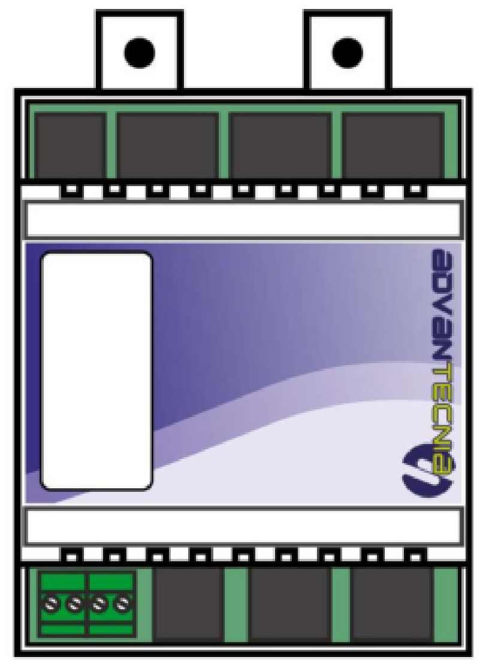

LCom – radial hub

Code	**ACE71610003**
Location	Ceiling of each apartment and public toilets
Height	**2,55 m**
Quantity	**41**

8

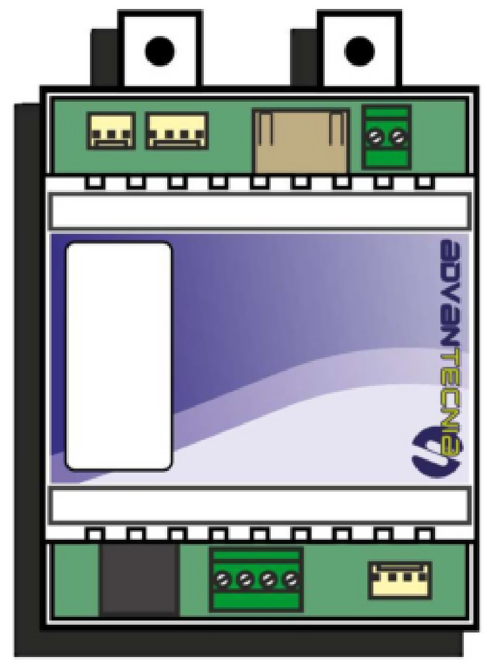

BoxCom – bus hub

Code	**ACE70810000**
Location	Ceiling next to the rack: joins several apartments
Height	**2,55 m**
Quantity	**17**

9

NOTES · NOTAS

1. Reference photos from ACE BG / Advantecnia, with their title.
2. Pull-cord: red cord with handle, reachable from the floor.
3. The door tablet calls and talks to the nurse.
4. The corridor light turns on when someone calls from the public toilet.
5. The panel has a red call button, a blue (left) and a green (right) button and a speaker to talk.
6. Chain: devices → LCom (radial) → BoxCom (bus) → PoE switch → server.
7. The desk phone goes straight to the PoE switch.

DESK PHONE – WHICH COLOUR SHOWS

🟥	Alarm (pull-cord / SOS)	**Red**
🟩	Green button once: presence	**Green**
▨	Green button again: cancels call or alarm	**Cleared**
🟦	Blue button: doctor call (blue call)	**Blue**
🟧	Voice call	**Yellow / orange**

MIGDALEI YAM A TIJON · ASSISTED LIVING

Nurse call – GF + 8 floors · 32 apartments

System: ACE BG · Advantecnia Prepared by: Telab International

SYSTEM DEVICES

SCALE · ESCALA	DATE · FECHA	REV	SHEET
S/E	**15/10/2026**	**B**	**02**

Base: architect's plan L5 (Massad Oz / Triplet) · dimensions in m

A1 format · Rev. B – on the real plan

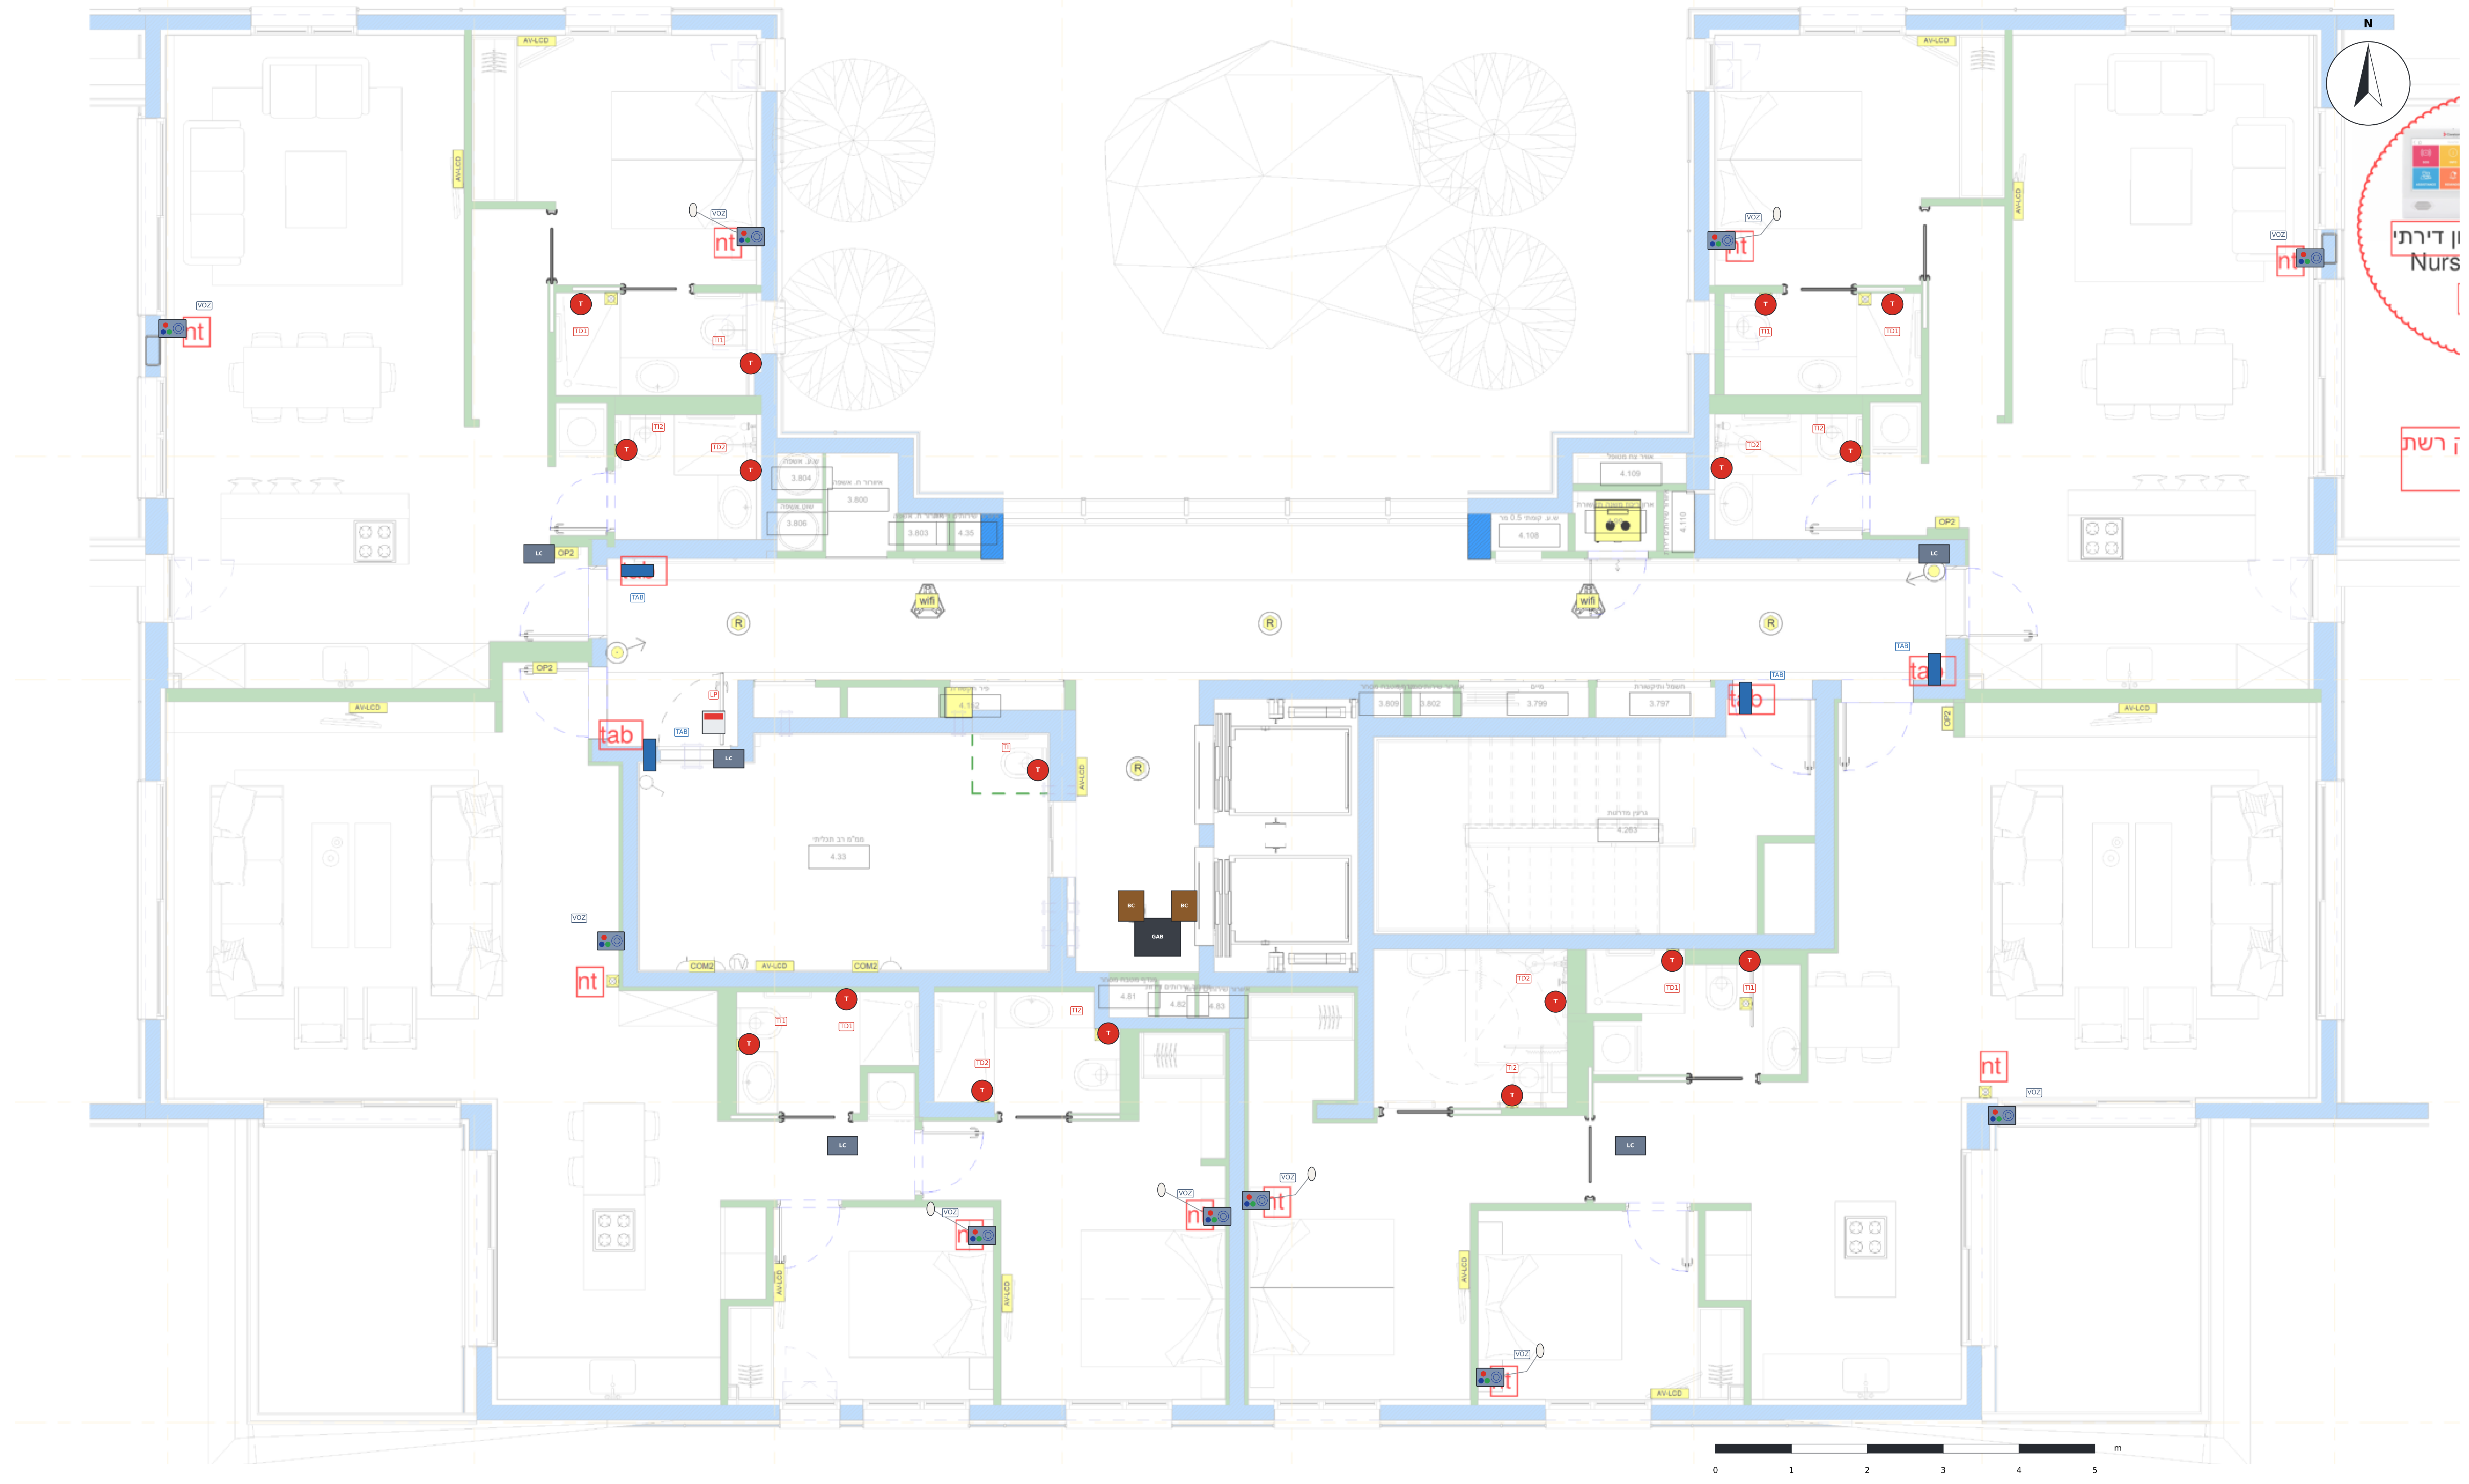

NOTES · NOTAS

1. Background: the client's IT plan L2 with their red marks: «nt» = voice panel and «tab» = door tablet.

2. On top, in colour: the devices of this proposal. Each panel and tablet is where the client marked it.

3. The yellow ⊠ squares in the L2 bathrooms are the pull-cords (toilet and shower).

4. The 4 tablets are in the lobby, next to each apartment door, as in the «tab» marks.

5. Plans L2 and L5 (base of this proposal) share the same structure; L5 is the typical floor for floors 1 to 8.

DEVICES · EQUIPOS · דויצ

🟦	TAB · Door tablet (iPad / Android) – call and voice, h 1.40 m Door tablet – call and voice · טלבאט בכניסה – קריאה ודיבור
▨	VOZ · Voice panel with buttons ACE82182451 – living room and bedrooms, h 1.20–1.30 m Voice panel with buttons – living room and bedrooms · פנל קולי עם לחצנים – סלון וחדרי שינה
○	Call pear next to the bed (bedrooms) Call pear next to the bed (bedrooms) · אגס קריאה ליד המיטה
T	TI / TD · Pull-cord ACE40320303W – toilet and shower, h 1.85 m Pull-cord – toilet and shower, h 1.85 m · משיכת חבל – אסלה ומקלחת, גובה 1.85 מ'
🟥	LP · Corridor light ACE41020309 – above each public toilet door Corridor light – above each public toilet door · מנורת מסדרון – מעל דלת כל שירותים ציבוריים

שירותים קריאת אחות

Pull-cord

טבלט אנדרואיד קריאת אחות

Advantecnia
Llamada de enfermera

Door tablet (iPad / Android)

מנורה קריאת אחות

Corridor light

פנל קריאת אחות

Voice panel with buttons

MIGDALEI YAM A TIJON · ASSISTED LIVING

Nurse call – GF + 8 floors · 32 apartments

System: ACE BG · Advantecnia   Prepared by: Telab International

CLIENT MARKS (PLAN L2) AND PROPOSAL

SCALE · ESCALA	DATE · FECHA	REV	SHEET
1:60	15/10/2026	B	03

Base: architect's plan L5 (Massad Oz / Triplet) · dimensions in m

A1 format · Rev. B – on the real plan

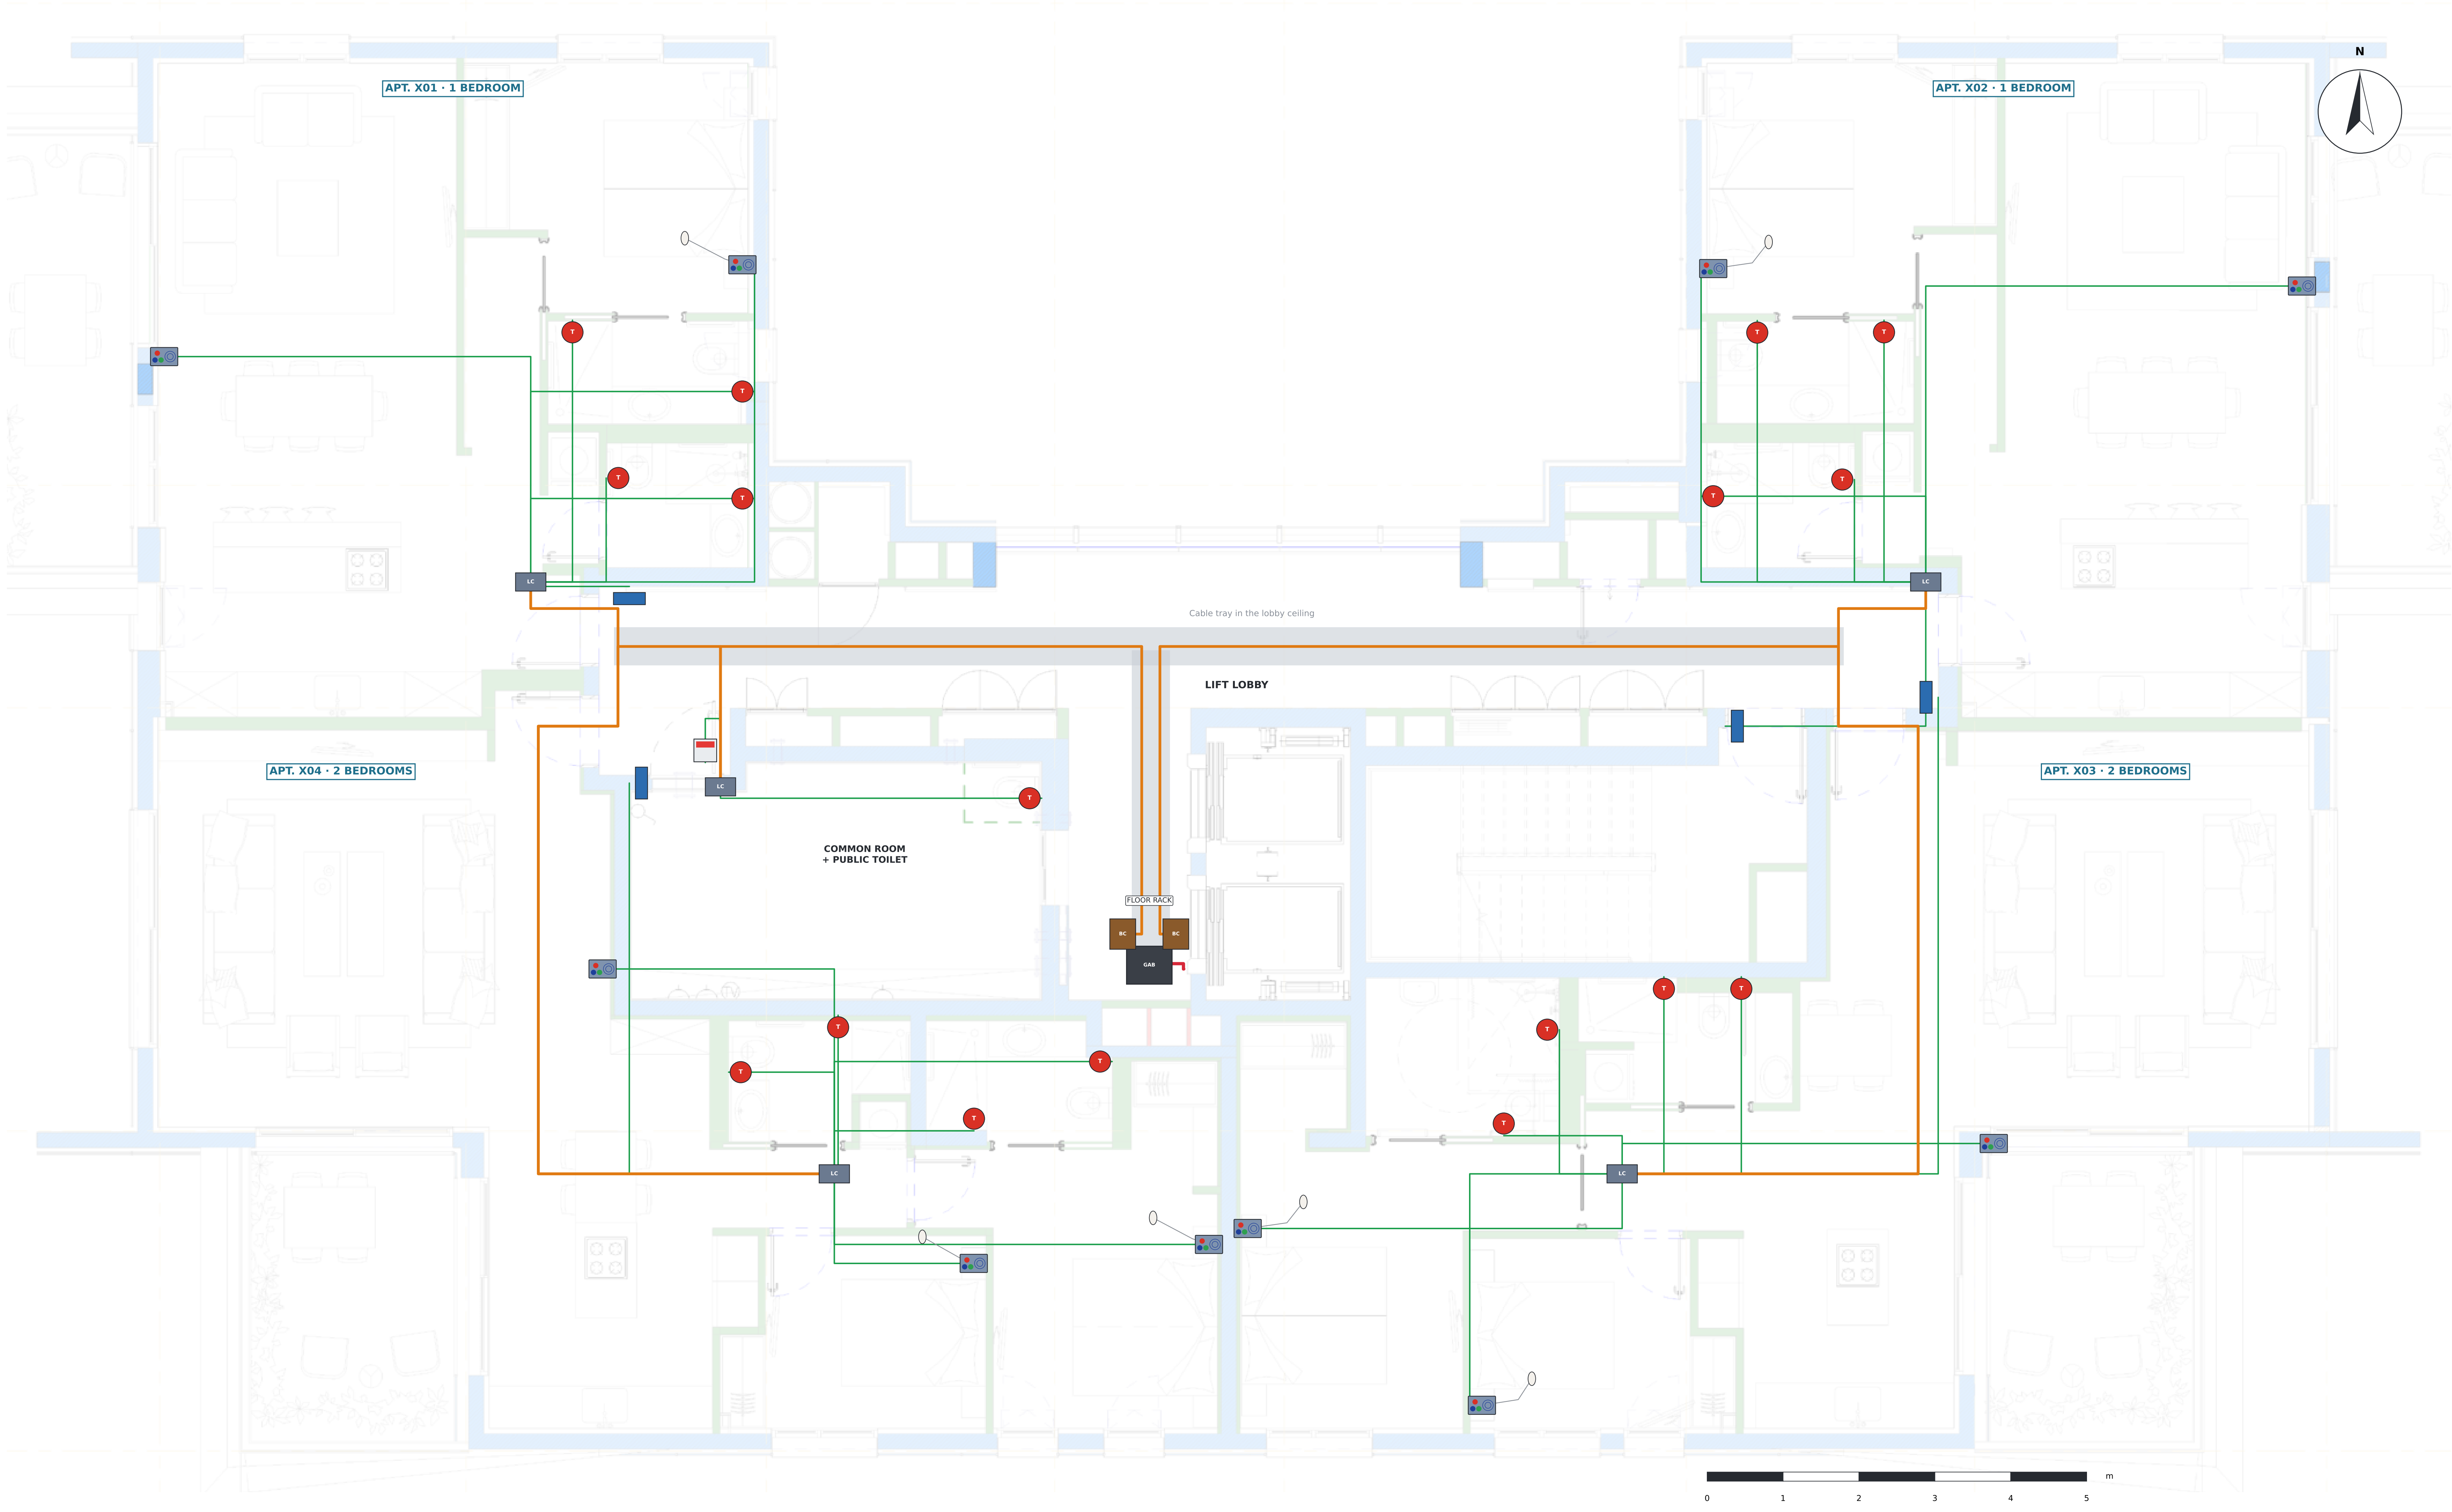

WIRING · CABLEADO · תיווט

🟩	Cat6 radial: each device → its apartment LCom Cat6 radial: each device → apartment LCom · Cat6 רדיאלי: כל התקן ← LCom של הדירה
🟧	Cat6 / Cat7 chain: LCom → LCom → ceiling BoxCom Cat6 / Cat7 chain: LCom → LCom → BoxCom · Cat6 / Cat7 שרשרת: LCom ← LCom ← BoxCom
🟥	Cat6A / Cat7 network: BoxCom → PoE switch → riser → GF server Cat6A / Cat7 network: BoxCom → switch → riser → GF server · Cat6A / Cat7 רשת: BoxCom ← מתג ← עמוד ← שרת

TYPICAL FLOOR LENGTHS (no spare)

🟩	Cat6 radial inside the apartments	**183 m**
🟧	Cat6 / Cat7 chain LCom → BoxCom	**80 m**
🟥	Cat6A / Cat7 rack and riser	**7 m**

NOTES · NOTAS

1. Each device runs radially (Cat6) to its apartment LCom, in the hall ceiling.
2. The LComs are chained along the lobby tray to the ceiling BoxComs next to the rack: x01 → x04 → common room → BoxCom 1 · x02 → x03 → BoxCom 2.
3. The BoxComs drop to the PoE switch in the rack; the switch runs up the Cat6A / Cat7 riser to the GF server.
4. Everything is PoE: no 230 V needed for the apartment devices.

NOTES · NOTAS

1. Base: architectural plan L5 (typical floor) – all 8 floors are identical: 4 apartments per floor, 32 in total.
2. Apartments x01 and x02: 1 bedroom, living room with kitchen and 2 bathrooms. Apartments x03 and x04: 2 bedrooms and 2 bathrooms.
3. Tablet at the door of each apartment (iPad / Android) to call and talk to the nurse.
4. Voice panel with buttons (ACE82182451) in the living room and in each bedroom; in bedrooms, with a pear next to the bed.
5. Pull-cords (ACE40320303W) at the toilet and shower of every bathroom, at 1.85 m.
6. One public toilet per floor in the common room: pull-cord + corridor light above the door. With the 2 on GF, 10 public toilets in total.
7. Floor rack next to the lifts with the D-Link DES-1210-28P PoE switch; the 2 BoxComs go on the ceiling next to it.
8. Locations per the client's marks on plan L2 (nt = voice panel, tab = tablet): see sheet 03.

MIGDALEI YAM A TIJON · ASSISTED LIVING
Nurse call – GF + 8 floors · 32 apartments
System: ACE BG · Advantecnia   Prepared by: Telab International

TYPICAL FLOOR F1–F8 · WIRING

SCALE · ESCALA	DATE · FECHA	REV	SHEET
1:60	**15/10/2026**	**B**	**04**

Base: architect's plan L5 (Massad Oz / Triplet) · dimensions in m
A1 format · Rev. B – on the real plan

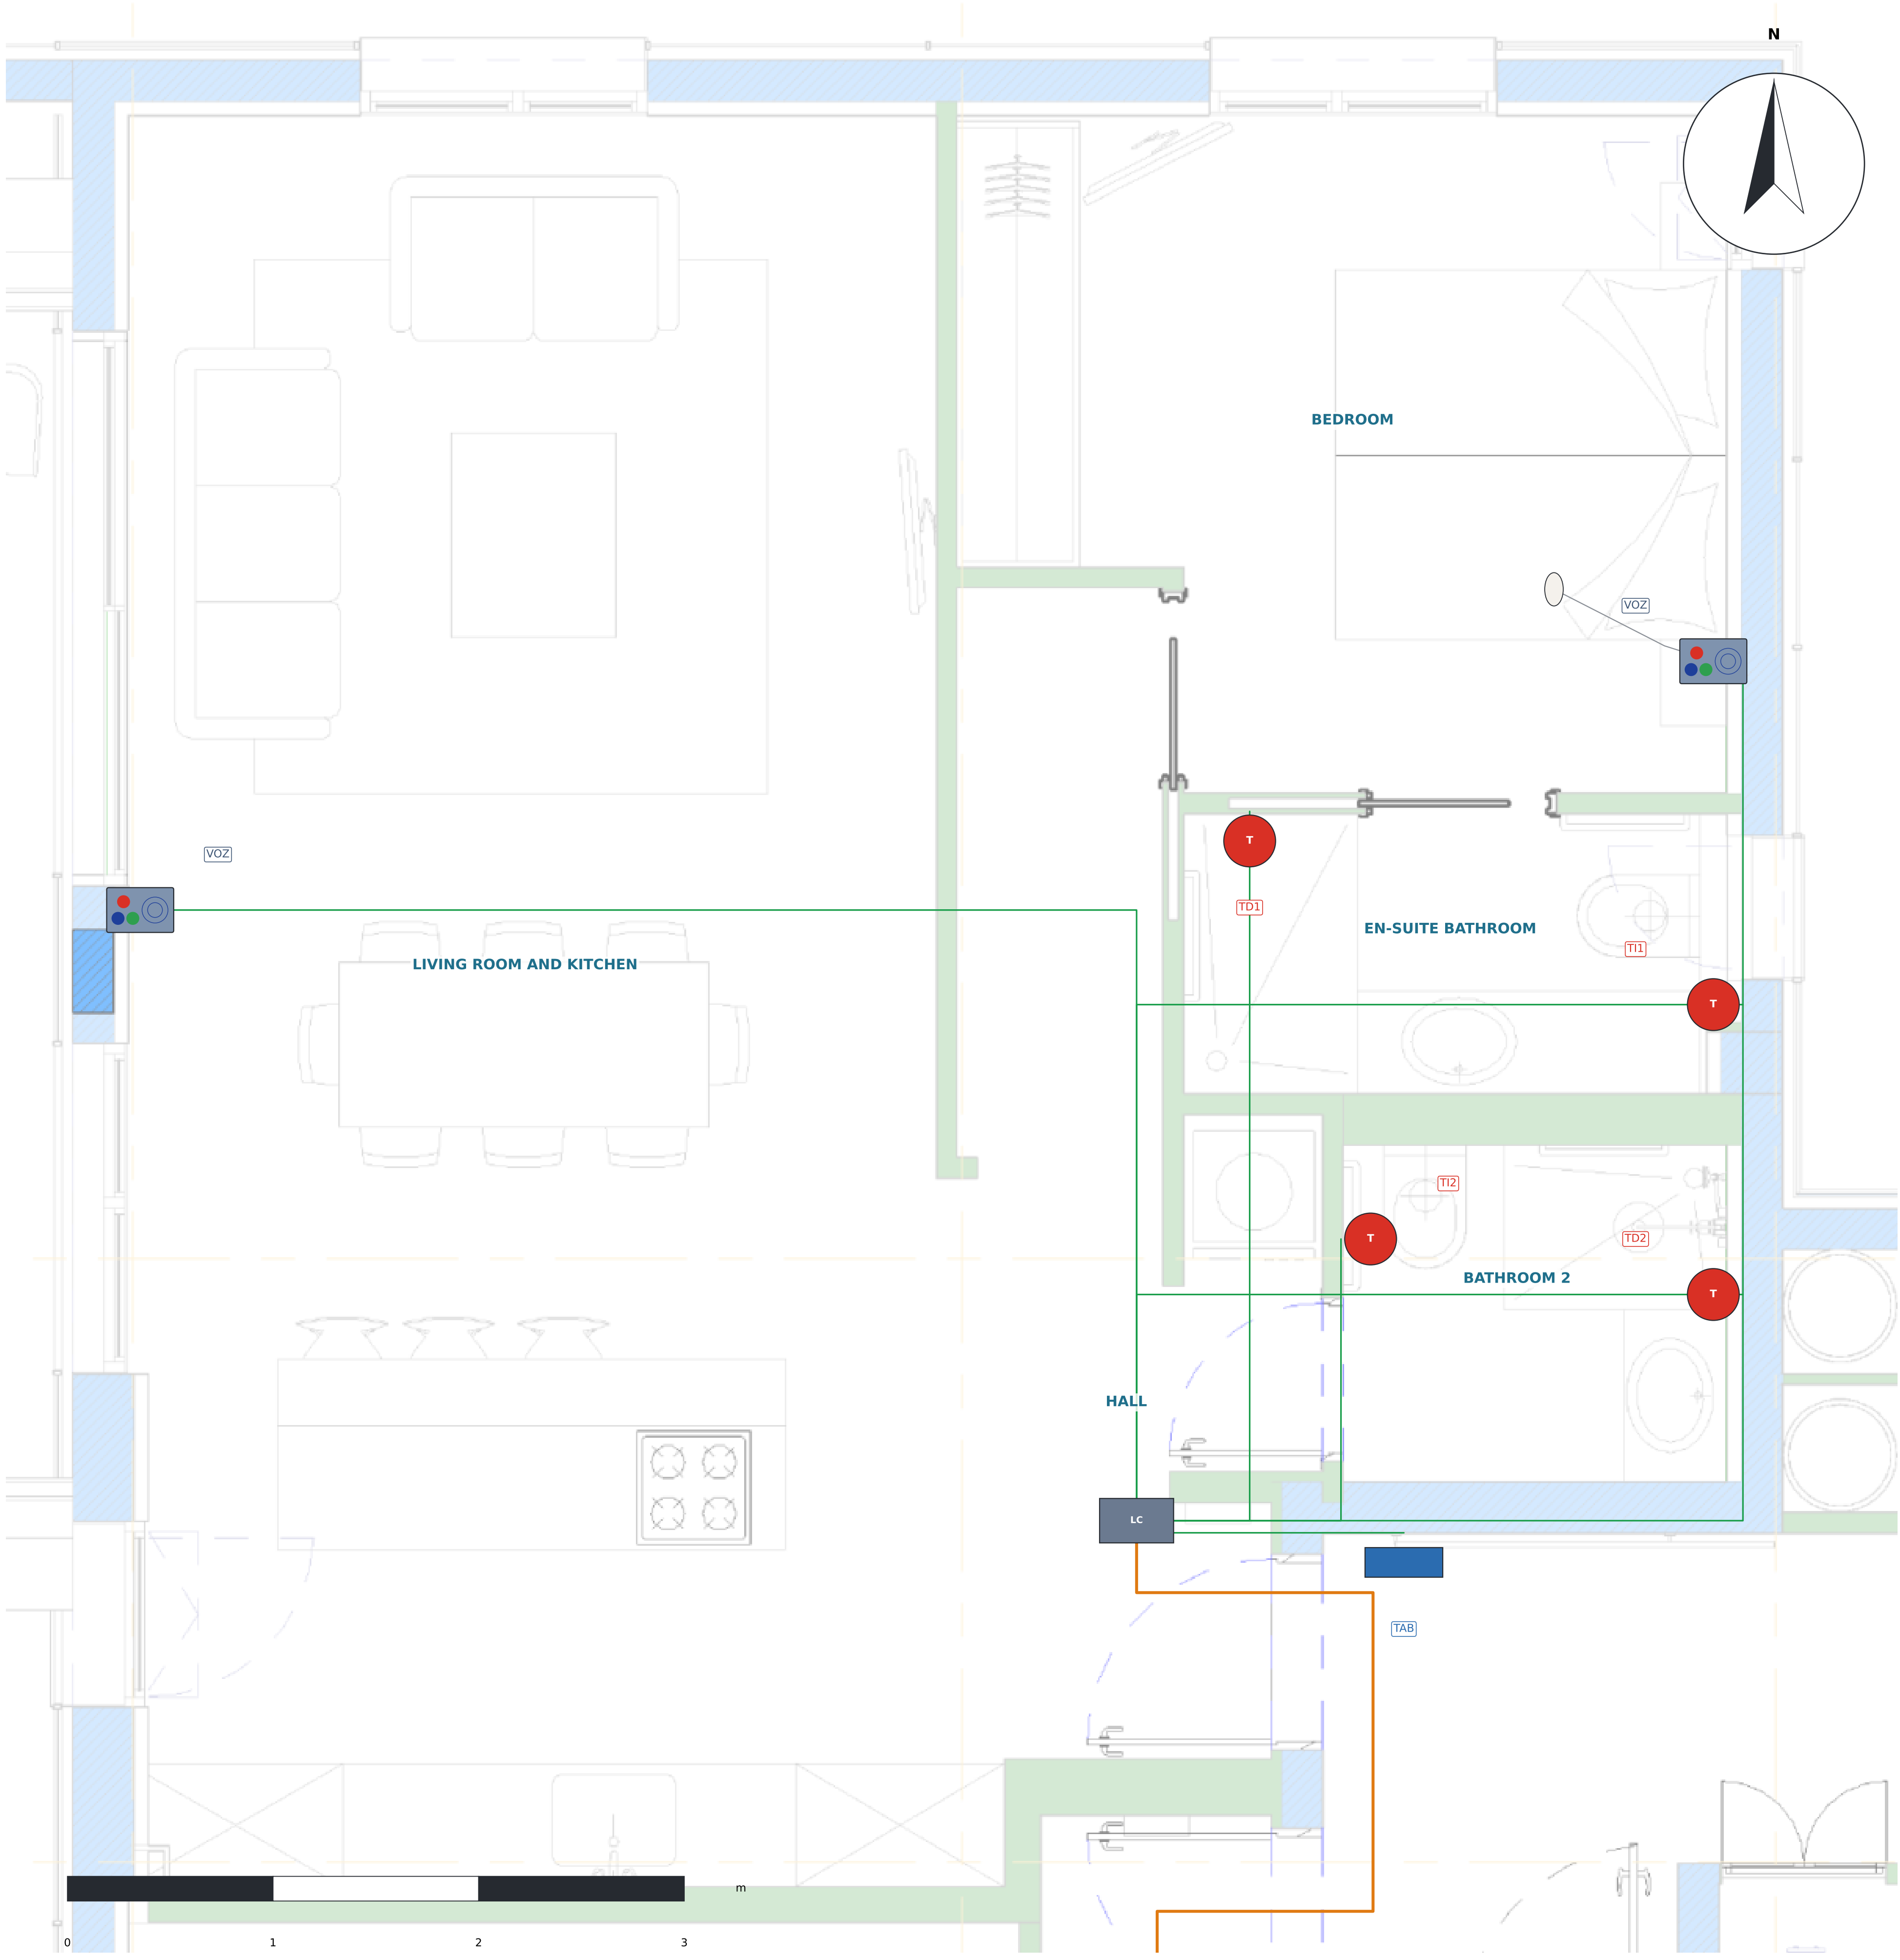

APARTMENT DEVICES

ID	Device	Room	Height
TAB	Door tablet	Hall	1.40 m
VOZ-S	Voice panel with buttons	Living room and kitchen	1,30 m
VOZ-D	Voice panel with buttons + pear	Bedroom	1,20 m
TI1	Pull-cord	En-suite bathroom	1.85 m
TD1	Pull-cord	En-suite bathroom	1.85 m
TI2	Pull-cord	Bathroom 2	1.85 m
TD2	Pull-cord	Bathroom 2	1.85 m
LCOM	LCom ACE71610003	Hall	2,55 m

SYMBOLS · SÍMBOLOS · סמלים

🟦	TAB · Door tablet (iPad / Android) – call and voice, h 1.40 m Door tablet – call and voice · טאבלט בכניסה – קריאה ודיבור
VOZ	VOZ · Voice panel with buttons ACE82182451 – living room and bedrooms, h 1.20–1.30 m Voice panel with buttons – living room and bedrooms · פנל קולי עם לחצנים – סלון וחדרי שינה
⬯	Call pear next to the bed (bedrooms) Call pear next to the bed (bedrooms) · אגס קריאה ליד המיטה
T	TI / TD · Pull-cord ACE40320303W – toilet and shower, h 1.85 m Pull-cord – toilet and shower, h 1.85 m · משיכת חבל – אסלה ומקלחת, גובה 1.85 מ'
🟥	LP · Corridor light ACE41020309 – above each public toilet door Corridor light – above each public toilet door · מנורת מסדרון – מעל דלת כל שירותים ציבוריים
LC	LC · LCom ACE71610003 – apartment hub (ceiling) LCom – apartment hub (ceiling) · LCom – מרכז הדירה (תקרה)
BC	BC · BoxCom ACE70810000 – bus hub for several apartments (ceiling) BoxCom – bus hub for several apartments (ceiling) · BoxCom – מרכז באס לכמה דירות (תקרה)

NOTES · NOTAS

1. Apartment x02 mirrors x01 (same devices).
2. Tablet in the lobby, next to the front door (client's «tab» mark).
3. Voice panel in the living room and in the bedroom (with pear next to the bed).
4. 2 bathrooms: pull-cord at the toilet and at the shower of each (4 pull-cords).
5. Everything runs radially in Cat6 to the hall LCom.

שירותים קריאת אחות

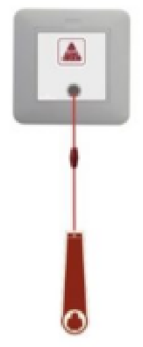

Pull-cord

טבלט אנדרואיד קריאת אחות

Advantecnia
Llamada de enfermera

Door tablet (iPad / Android)

מנורה קריאת אחות

Corridor light

פנל קריאת אחות

Voice panel with buttons

MIGDALEI YAM A TIJON · ASSISTED LIVING

Nurse call – GF + 8 floors · 32 apartments

System: ACE BG · Advantecnia Prepared by: Telab International

1-BEDROOM APT. (x01 / x02)

SCALE · ESCALA	DATE · FECHA	REV	SHEET
1:30	**15/10/2026**	**B**	**05**

Base: architect's plan L5 (Massad Oz / Triplet) · dimensions in m

A1 format · Rev. B – on the real plan

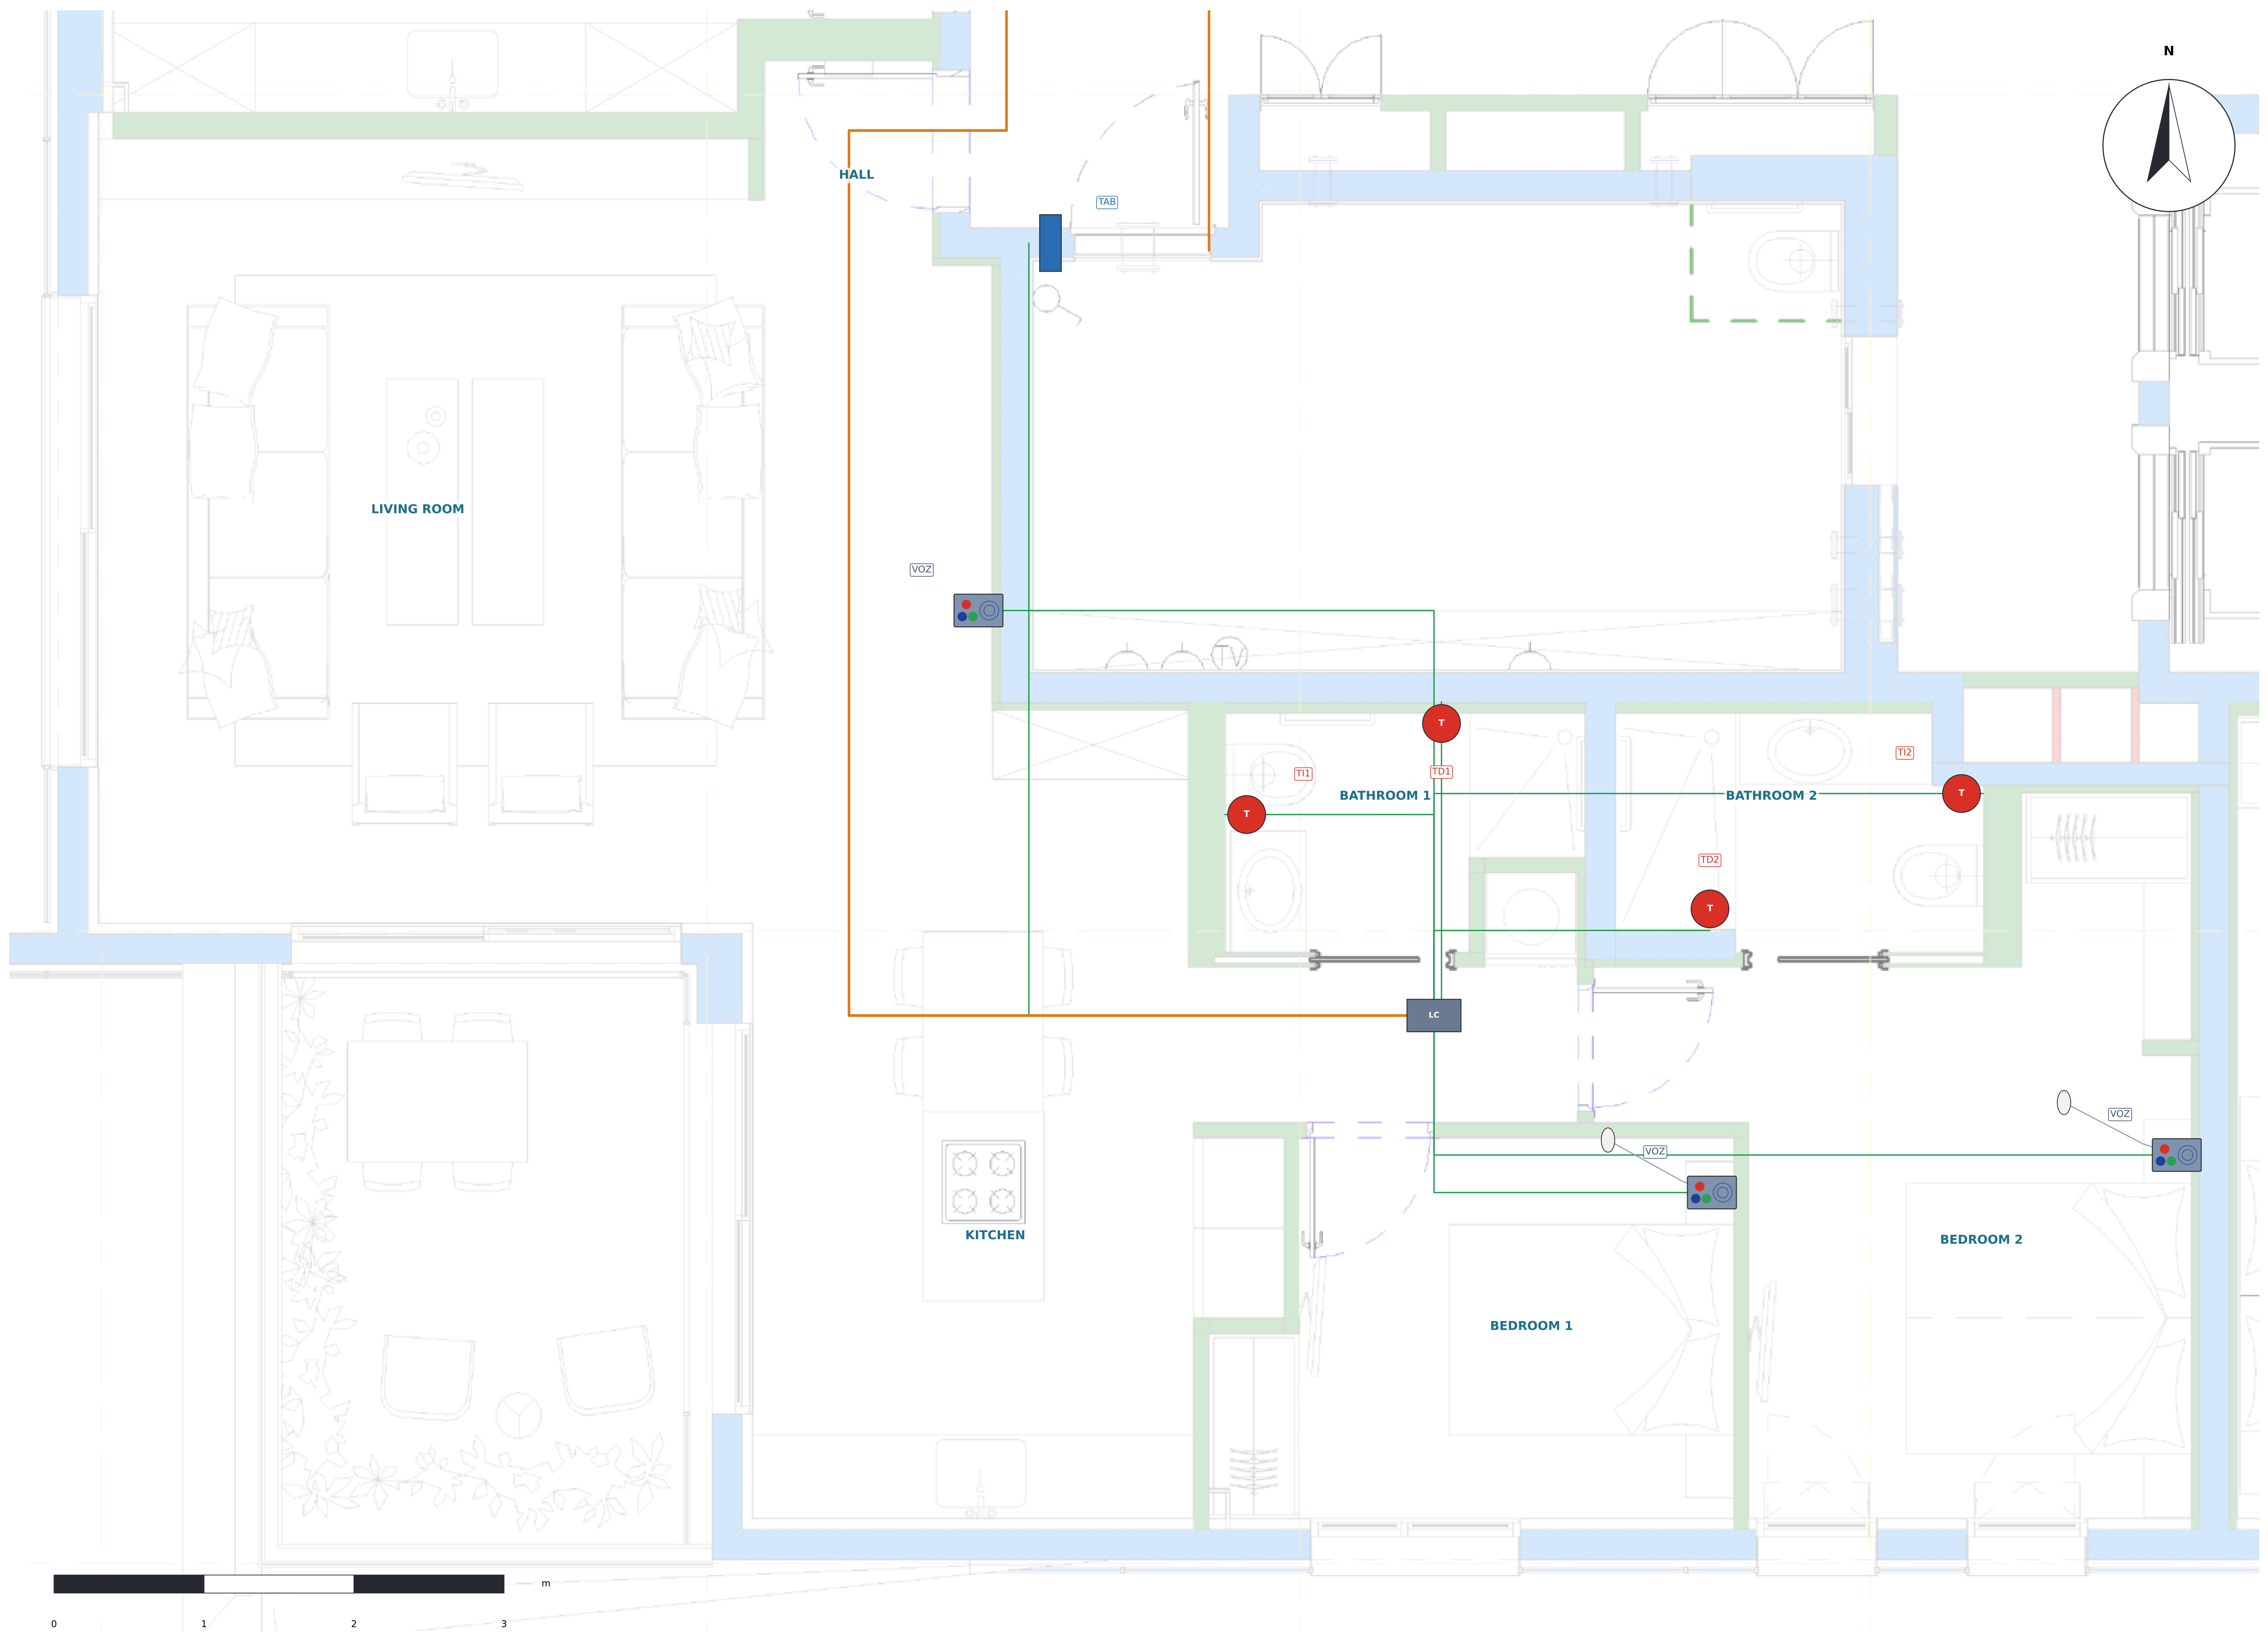

APARTMENT DEVICES

ID	Device	Room	Height
TAB	Door tablet	Hall	1.40 m
VOZ-S	Voice panel with buttons	Living room	1,30 m
VOZ-D1	Voice panel with buttons + pear	Bedroom 1	1,20 m
VOZ-D2	Voice panel with buttons + pear	Bedroom 2	1,20 m
TI1	Pull-cord	Bathroom 1	1.85 m
TD1	Pull-cord	Bathroom 1	1.85 m
TI2	Pull-cord	Bathroom 2	1.85 m
TD2	Pull-cord	Bathroom 2	1.85 m
LCOM	LCom ACE71610003	Hall	2,55 m

SYMBOLS · SÍMBOLOS · םילמס

🟦	TAB · Door tablet (iPad / Android) – call and voice, h 1.40 m Door tablet – call and voice · רובידו האירק – הסינכב טלבאט
▨	VOZ · Voice panel with buttons ACE82182451 – living room and bedrooms, h 1.20–1.30 m Voice panel with buttons – living room and bedrooms · הניש ירדחו ןולס – םינצחל םע ילוק לנפ
○	Call pear next to the bed (bedrooms) Call pear next to the bed (bedrooms) · הטימה דיל האירק סגא
T	TI / TD · Pull-cord ACE40320303W – toilet and shower, h 1.85 m Pull-cord – toilet and shower, h 1.85 m · 'מ 1.85 הבוג ,תחלקמו הלסא – לבח תכישמ
🟥	LP · Corridor light ACE41020309 – above each public toilet door Corridor light – above each public toilet door · םיירוביצ םיתוריש לכ תלד לעמ – ןורדסמ תרונמ
LC	LC · LCom ACE71610003 – apartment hub (ceiling) LCom – apartment hub (ceiling) · LCom – הרידה זכרמ (הרקת)
BC	BC · BoxCom ACE70810000 – bus hub for several apartments (ceiling) BoxCom – bus hub for several apartments (ceiling) · BoxCom – תוריד המכל סאב זכרמ (הרקת)

NOTES · NOTAS

1. Apartment x03 has the same devices (bathrooms laid out differently).
2. Tablet in the lobby, next to the front door (client's «tab» mark).
3. Voice panel in the living room and in both bedrooms (with pear next to the bed).
4. 2 bathrooms: pull-cord at the toilet and at the shower of each (4 pull-cords).
5. Everything runs radially in Cat6 to the LCom in the bedroom corridor.

שירותים קריאת אחות

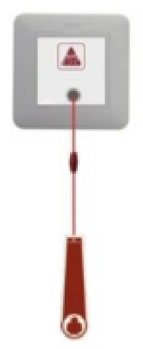

Pull-cord

טבלט אנדרואיד קריאת אחות

Advantecnia
Llamada de enfermera

Door tablet (iPad / Android)

מנורה קריאת אחות

Corridor light

פנל קריאת אחות

Voice panel with buttons

MIGDALEI YAM A TIJON · ASSISTED LIVING

Nurse call – GF + 8 floors · 32 apartments

System: ACE BG · Advantecnia   Prepared by: Telab International

2-BEDROOM APT. (x04 / x03)

SCALE · ESCALA	DATE · FECHA	REV	SHEET
1:35	15/10/2026	B	06

Base: architect's plan L5 (Massad Oz / Triplet) · dimensions in m

A1 format · Rev. B – on the real plan

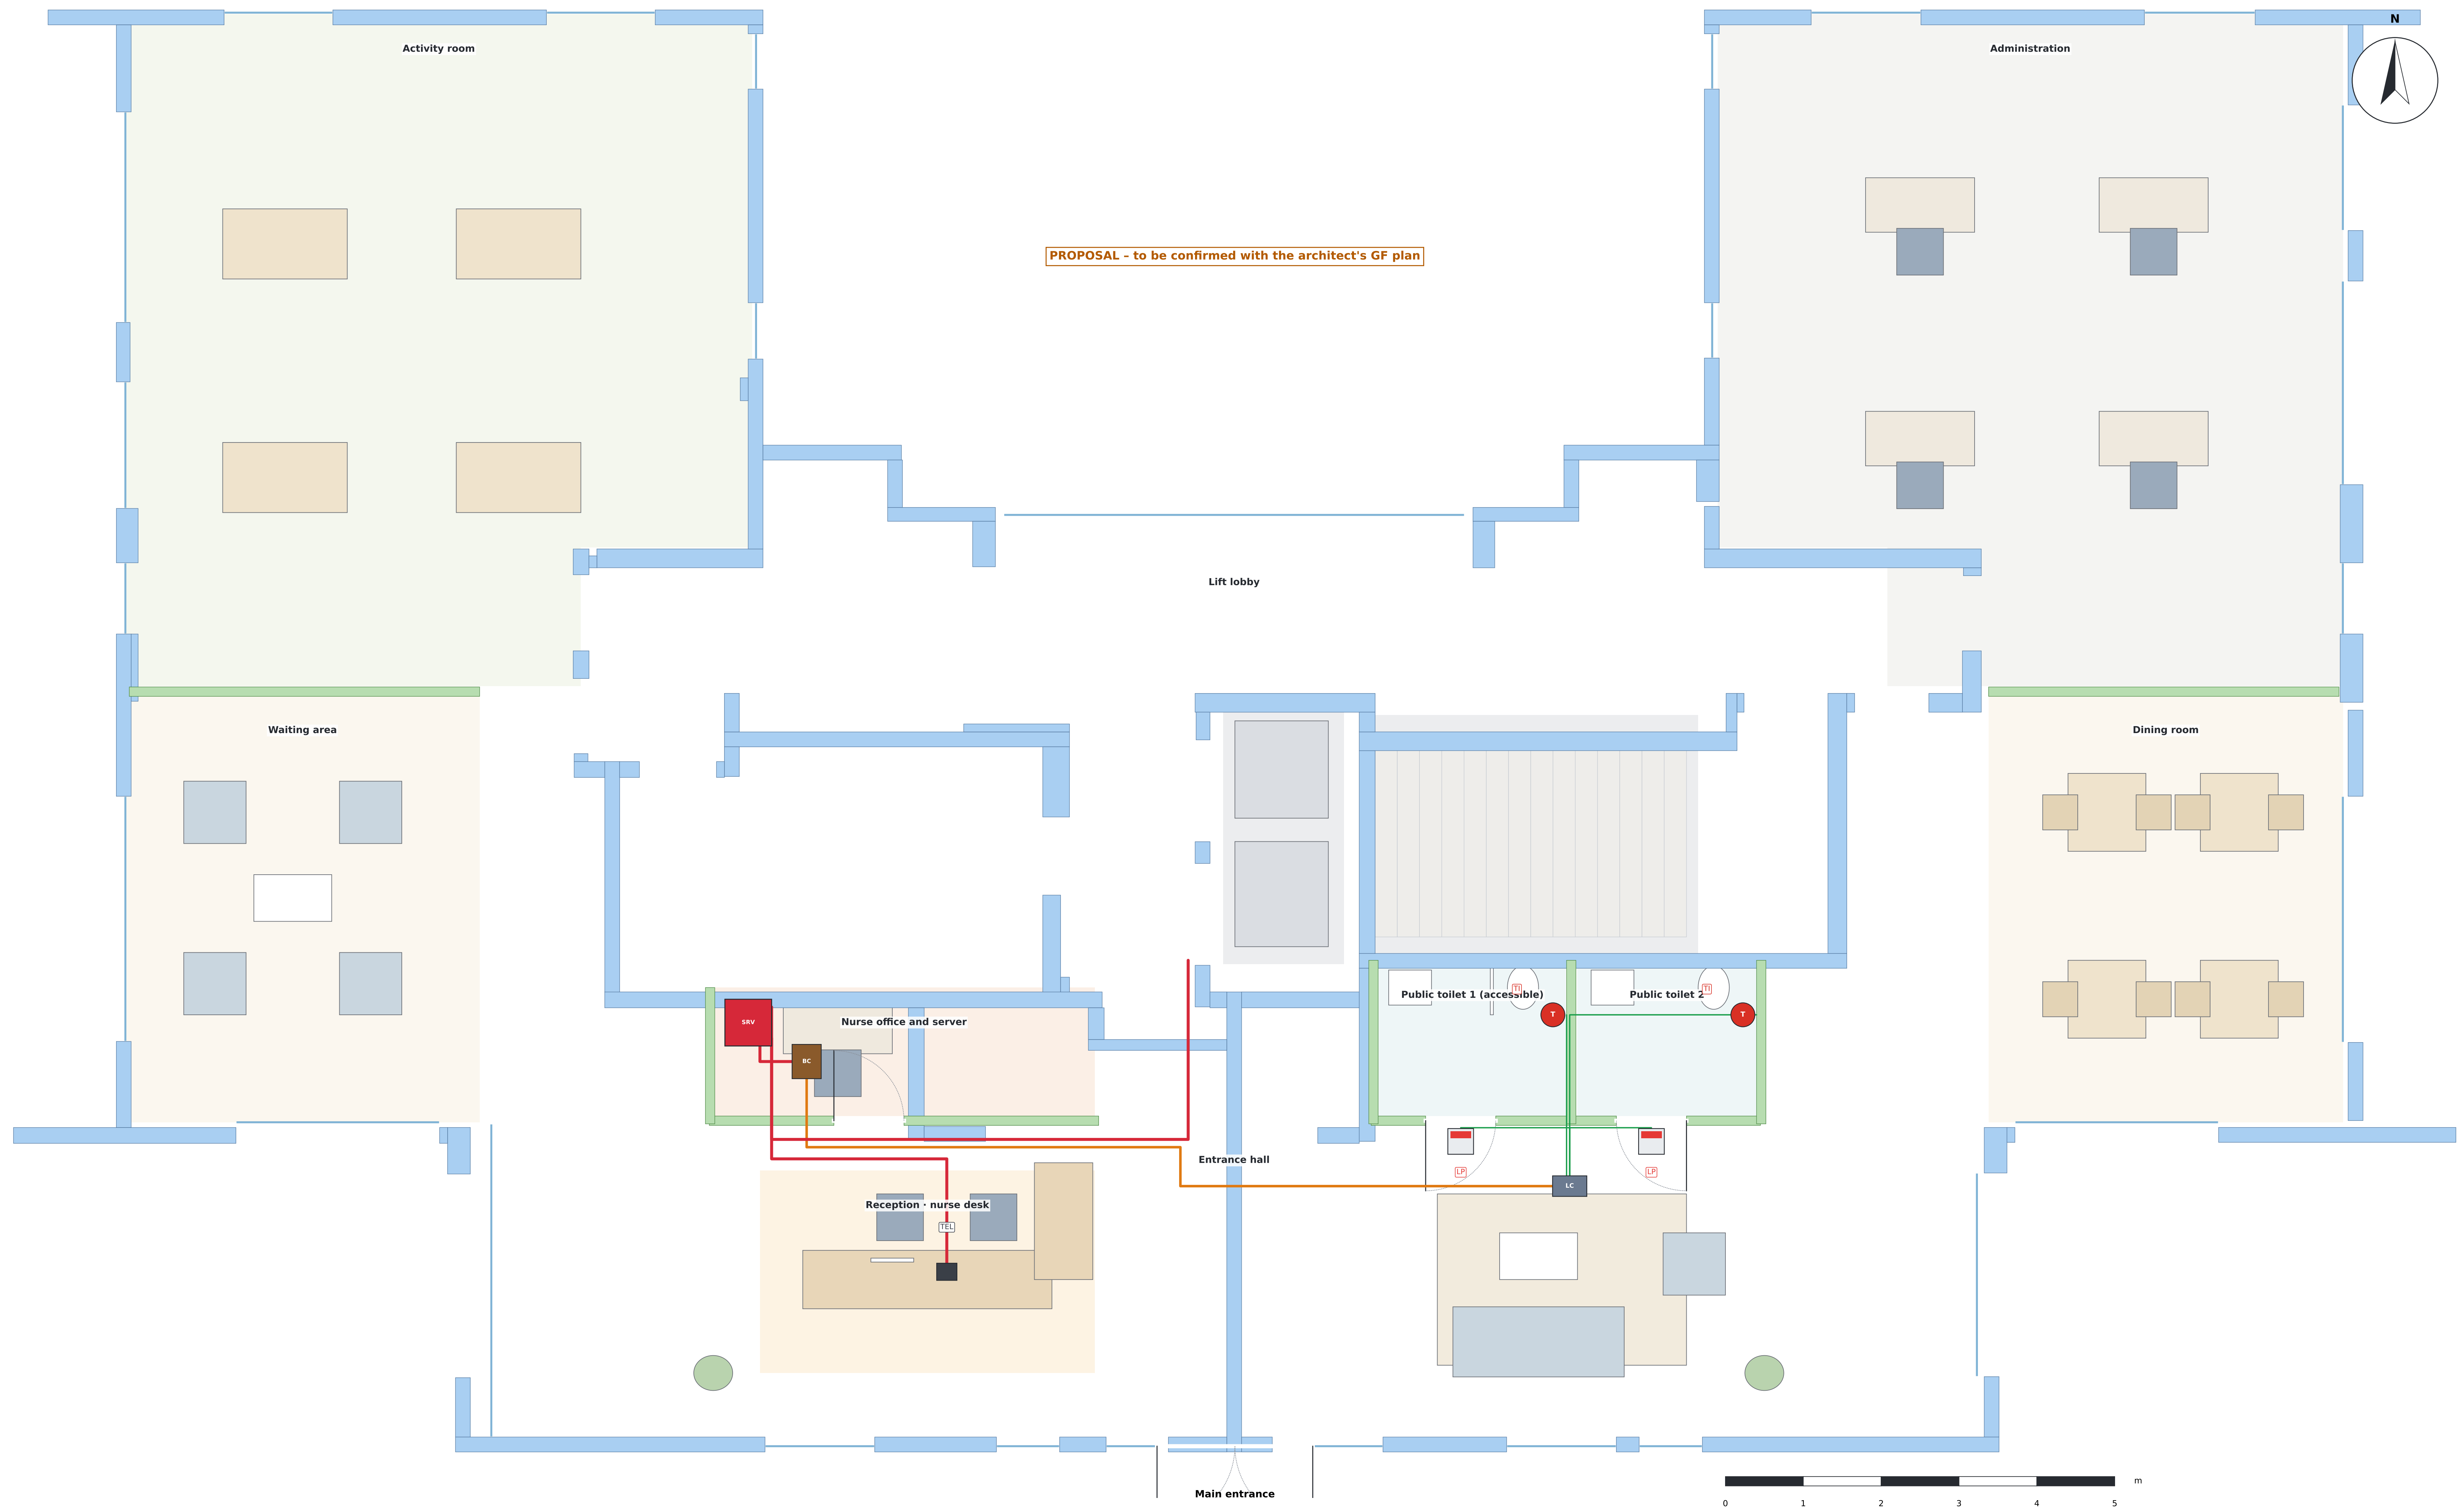
N
Activity room
Administration
PROPOSAL – to be confirmed with the architect's GF plan
Lift lobby
Waiting area
Dining room
SRV
BC
Nurse office and server
Public toilet 1 (accessible)
Public toilet 2
T
LP
LC
Entrance hall
Reception · nurse desk
TEL
Main entrance
0
1
2
3
4
5
m

DETAIL · RECEPTION AND NURSE DESK (1:40)

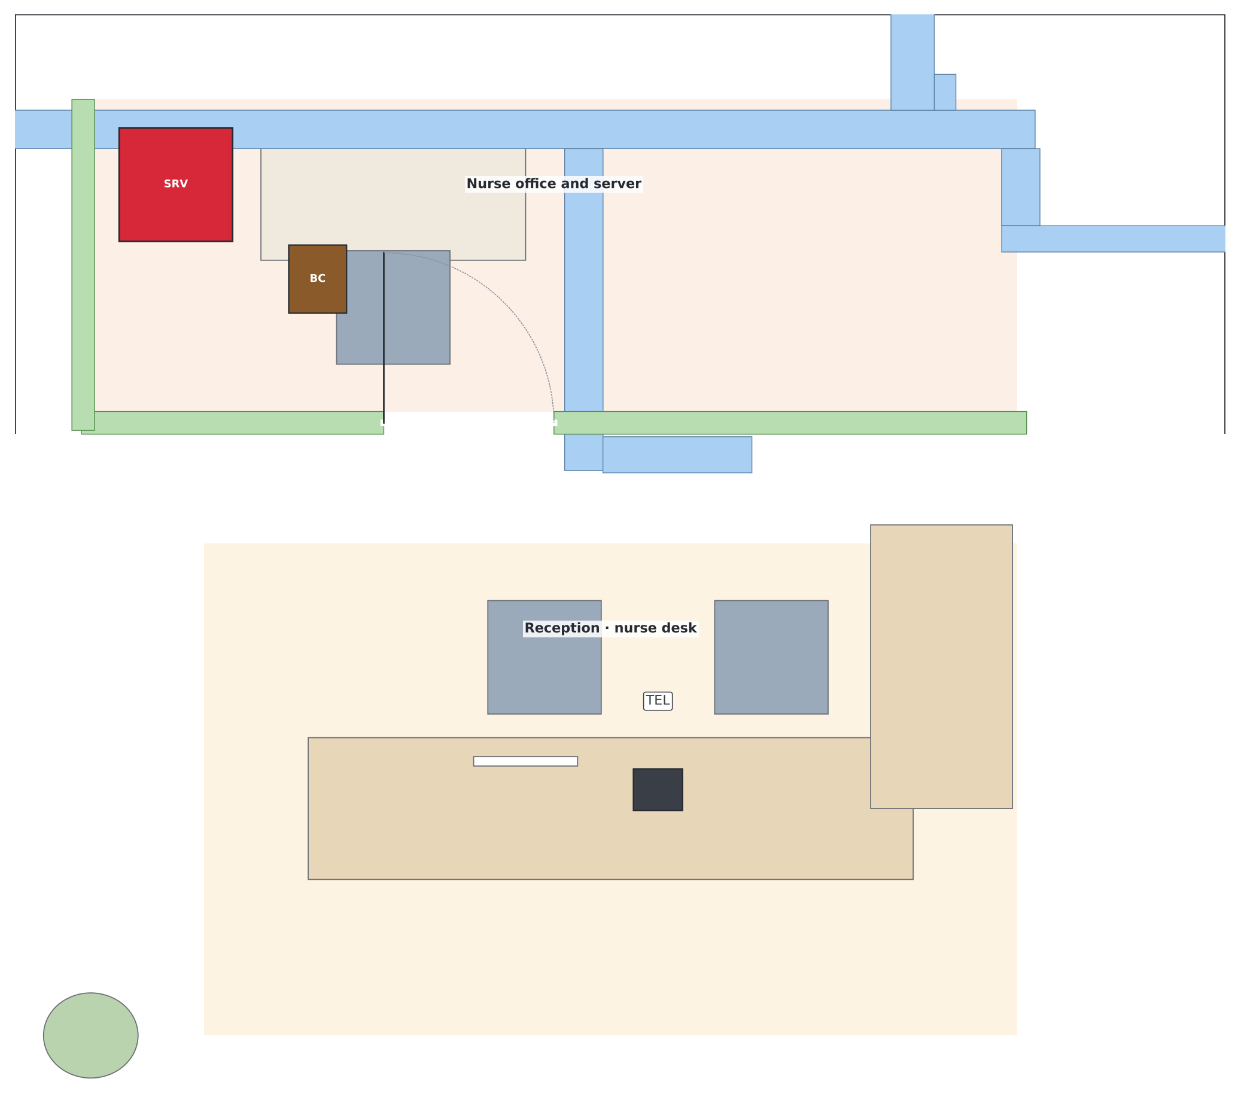
SRV
BC
Nurse office and server
Reception · nurse desk
TEL

NOTES · NOTAS

1. Nurse desk at reception, facing the entrance and the lifts.
2. On the desk: Grandstream Android phone, connected straight to the PoE switch. Each call shows in its colour.
3. Behind the desk: office with the main rack: Buslogic Premium server and D-Link PoE switch. GF BoxCom on the ceiling.
4. 2 public toilets on GF: pull-cord next to the toilet and corridor light above each door.
5. The riser from the 8 floors runs down the core to the main rack.
6. Proposed GF layout: to be adjusted when the architect's plan arrives.

SYMBOLS · SÍMBOLOS · סמלים

T	TI / TD · Pull-cord ACE40320303W – toilet and shower, h 1.85 m Pull-cord – toilet and shower, h 1.85 m · משיכת חבל – אסלה ומקלחת, גובה 1.85 מ'
LC	LC · LCom ACE71610003 – apartment hub (ceiling) LCom – apartment hub (ceiling) · LCom – רכזת דירה (תקרה)
SRV	SRV · GF rack: Buslogic Premium server + D-Link PoE switch GF rack: Buslogic Premium server + D-Link PoE switch · ארון תקשורת: שרת Buslogic Premium + מתג PoE D-Link
🟥	LP · Corridor light ACE41020309 – above each public toilet door Corridor light – above each public toilet door · נורת מסדרון – מעל כל דלת שירותים ציבוריים
TEL	TEL · Grandstream Android phone – PoE straight to the switch Grandstream Android phone – PoE straight to the switch · טלפון Grandstream אנדרואיד – PoE ישירות למתג
BC	BC · BoxCom ACE70810000 – bus hub for several apartments (ceiling) BoxCom – bus hub for several apartments (ceiling) · BoxCom – רכזת באס לכמה דירות (תקרה)

DESK PHONE – WHICH COLOUR SHOWS

🟥	Alarm (pull-cord / SOS)	Red
🟩	Green button once: presence	Green
▨	Green button again: cancels call or alarm	Cleared
🟦	Blue button: doctor call (blue call)	Blue
🟧	Voice call	Yellow / orange

MIGDALEI YAM A TIJON · ASSISTED LIVING
Nurse call – GF + 8 floors · 32 apartments
System: ACE BG · Advantecnia Prepared by: Telab International

GROUND FLOOR · LOBBY AND NURSE DESK

SCALE · ESCALA	DATE · FECHA	REV	SHEET
1:60	15/10/2026	B	07

Base: architect's plan L5 (Massad Oz / Triplet) · dimensions in m
A1 format · Rev. B – on the real plan

A · BUILDING GF + 8 FLOORS

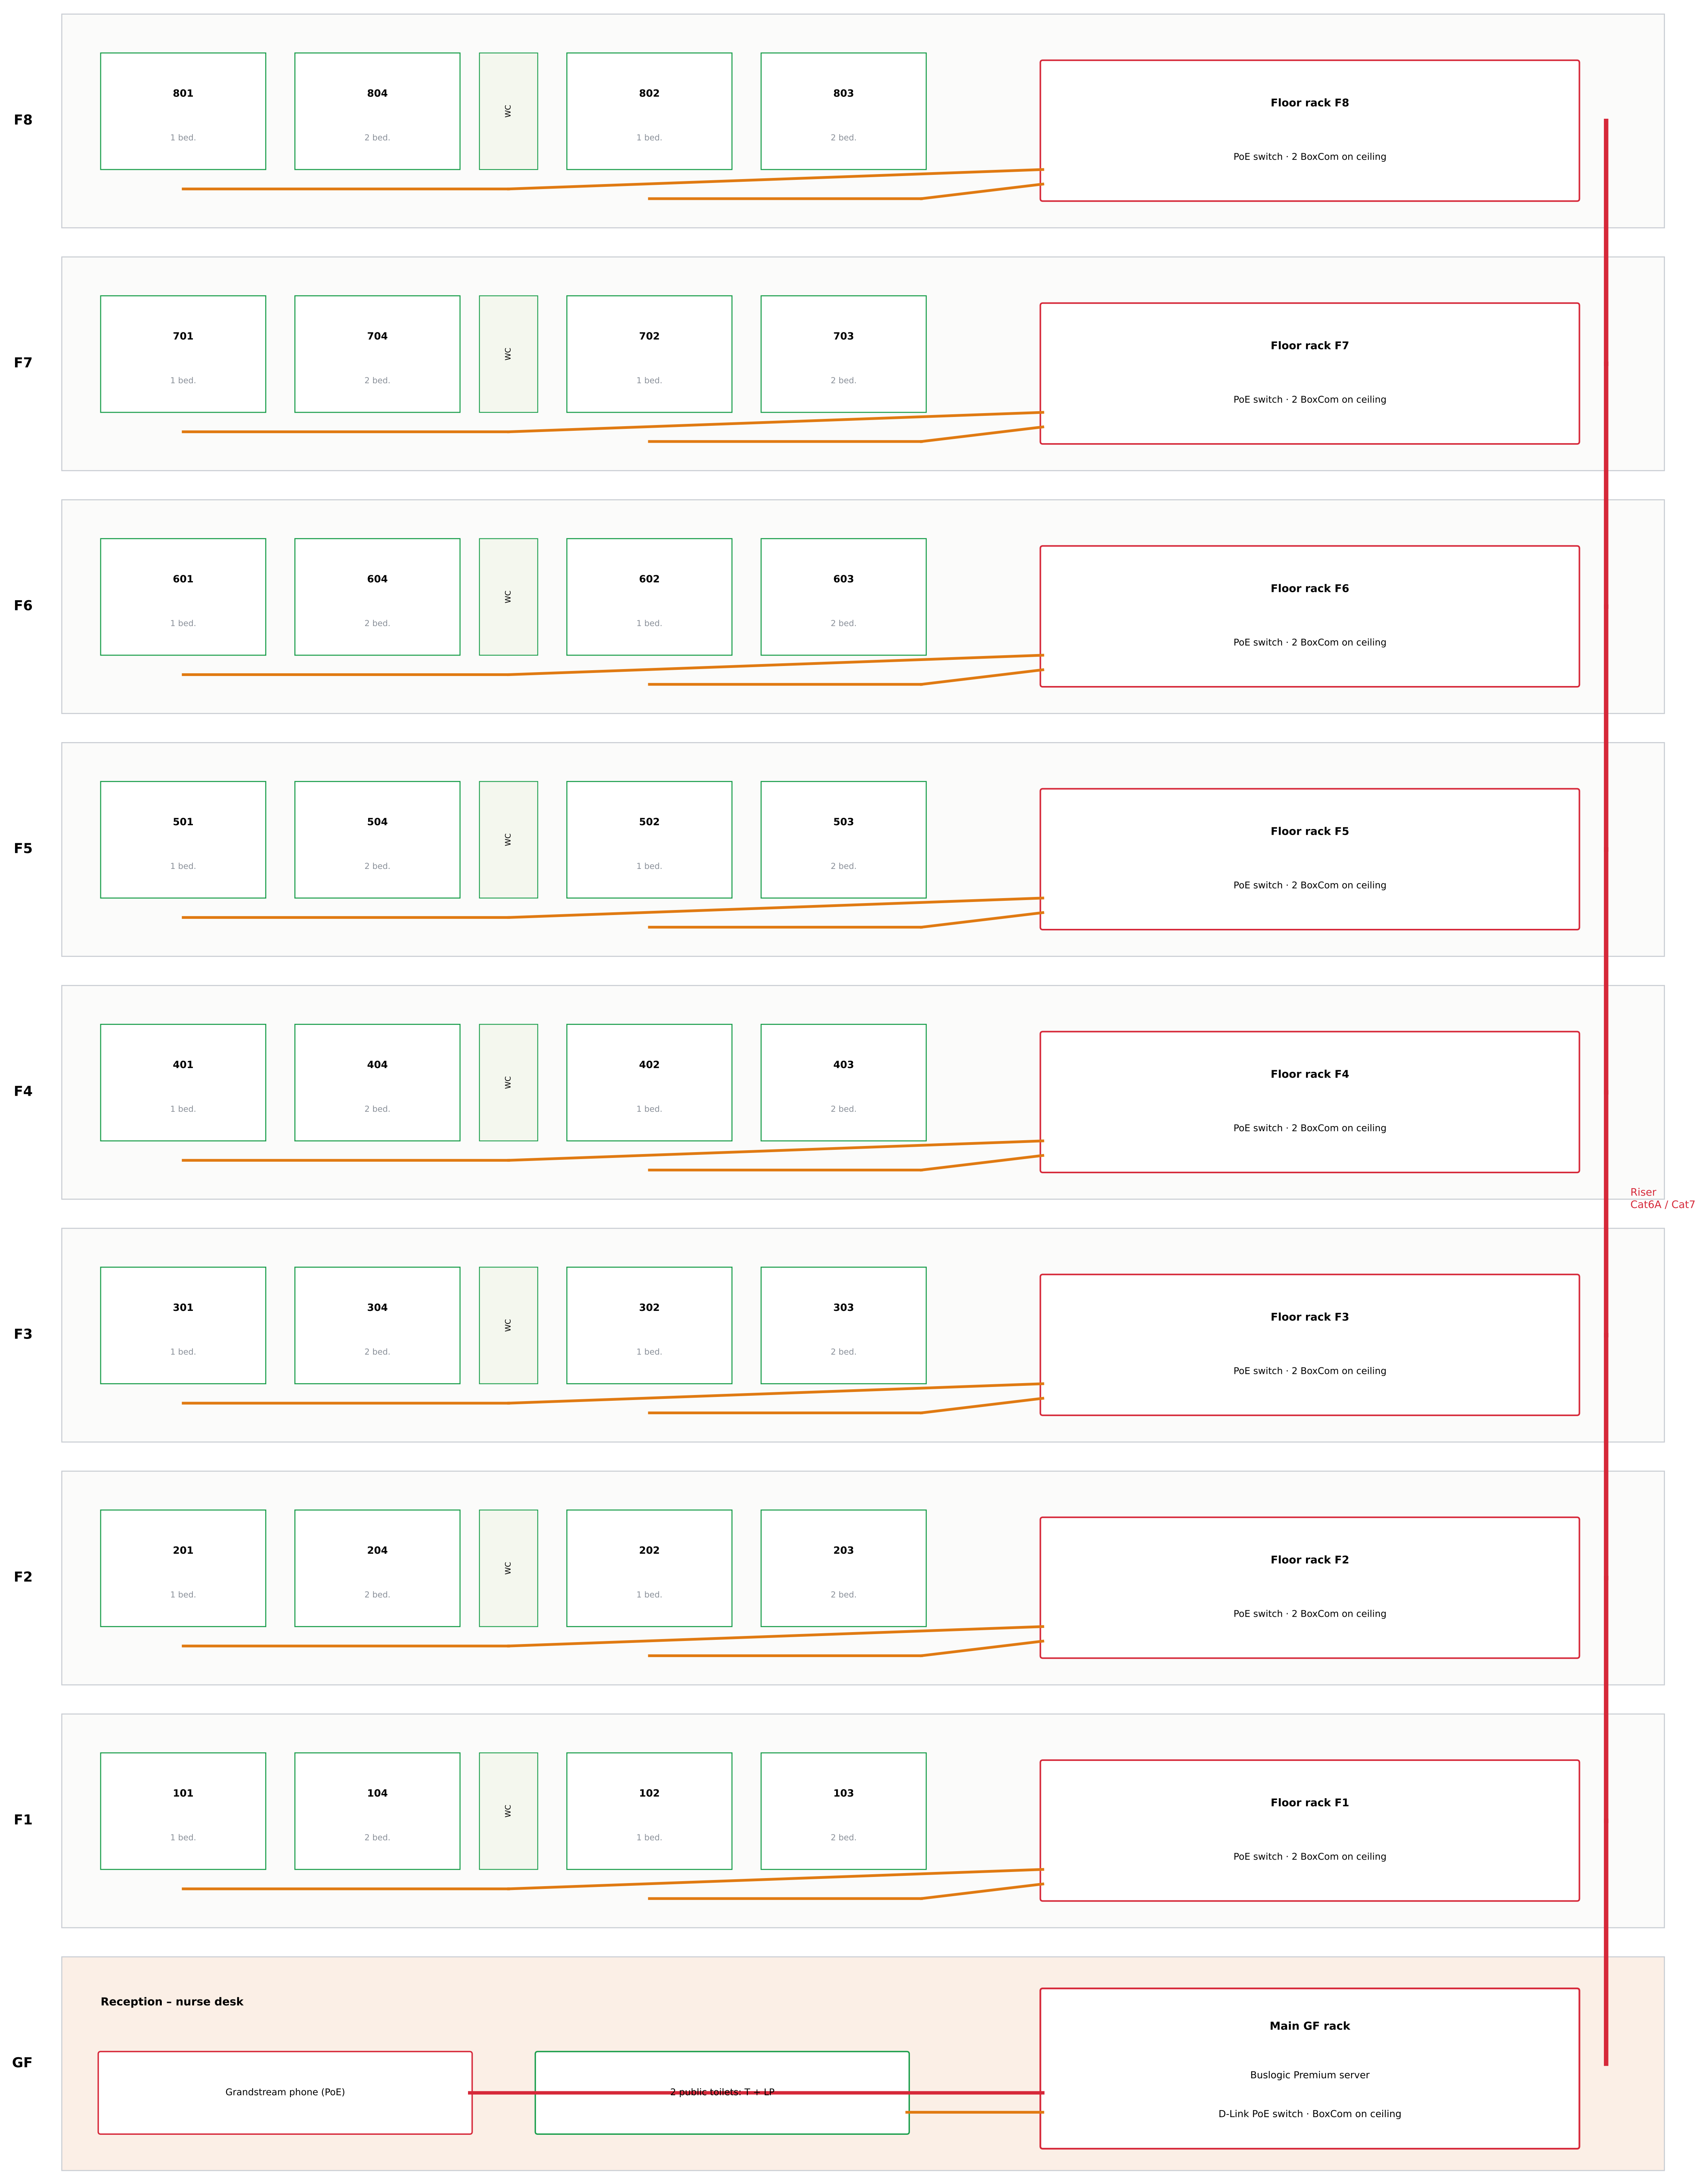
F8
801
1 bed.
804
2 bed.
WC
802
1 bed.
803
2 bed.
Floor rack F8
PoE switch · 2 BoxCom on ceiling
F7
701
1 bed.
704
2 bed.
WC
702
1 bed.
703
2 bed.
Floor rack F7
PoE switch · 2 BoxCom on ceiling
F6
601
1 bed.
604
2 bed.
WC
602
1 bed.
603
2 bed.
Floor rack F6
PoE switch · 2 BoxCom on ceiling
F5
501
1 bed.
504
2 bed.
WC
502
1 bed.
503
2 bed.
Floor rack F5
PoE switch · 2 BoxCom on ceiling
F4
401
1 bed.
404
2 bed.
WC
402
1 bed.
403
2 bed.
Floor rack F4
PoE switch · 2 BoxCom on ceiling
Riser
Cat6A / Cat7
F3
301
1 bed.
304
2 bed.
WC
302
1 bed.
303
2 bed.
Floor rack F3
PoE switch · 2 BoxCom on ceiling
F2
201
1 bed.
204
2 bed.
WC
202
1 bed.
203
2 bed.
Floor rack F2
PoE switch · 2 BoxCom on ceiling
F1
101
1 bed.
104
2 bed.
WC
102
1 bed.
103
2 bed.
Floor rack F1
PoE switch · 2 BoxCom on ceiling
GF
Reception – nurse desk
Grandstream phone (PoE)
2 public toilets: T + LP
Main GF rack
Buslogic Premium server
D-Link PoE switch · BoxCom on ceiling

B · TOPOLOGY OF ONE APARTMENT

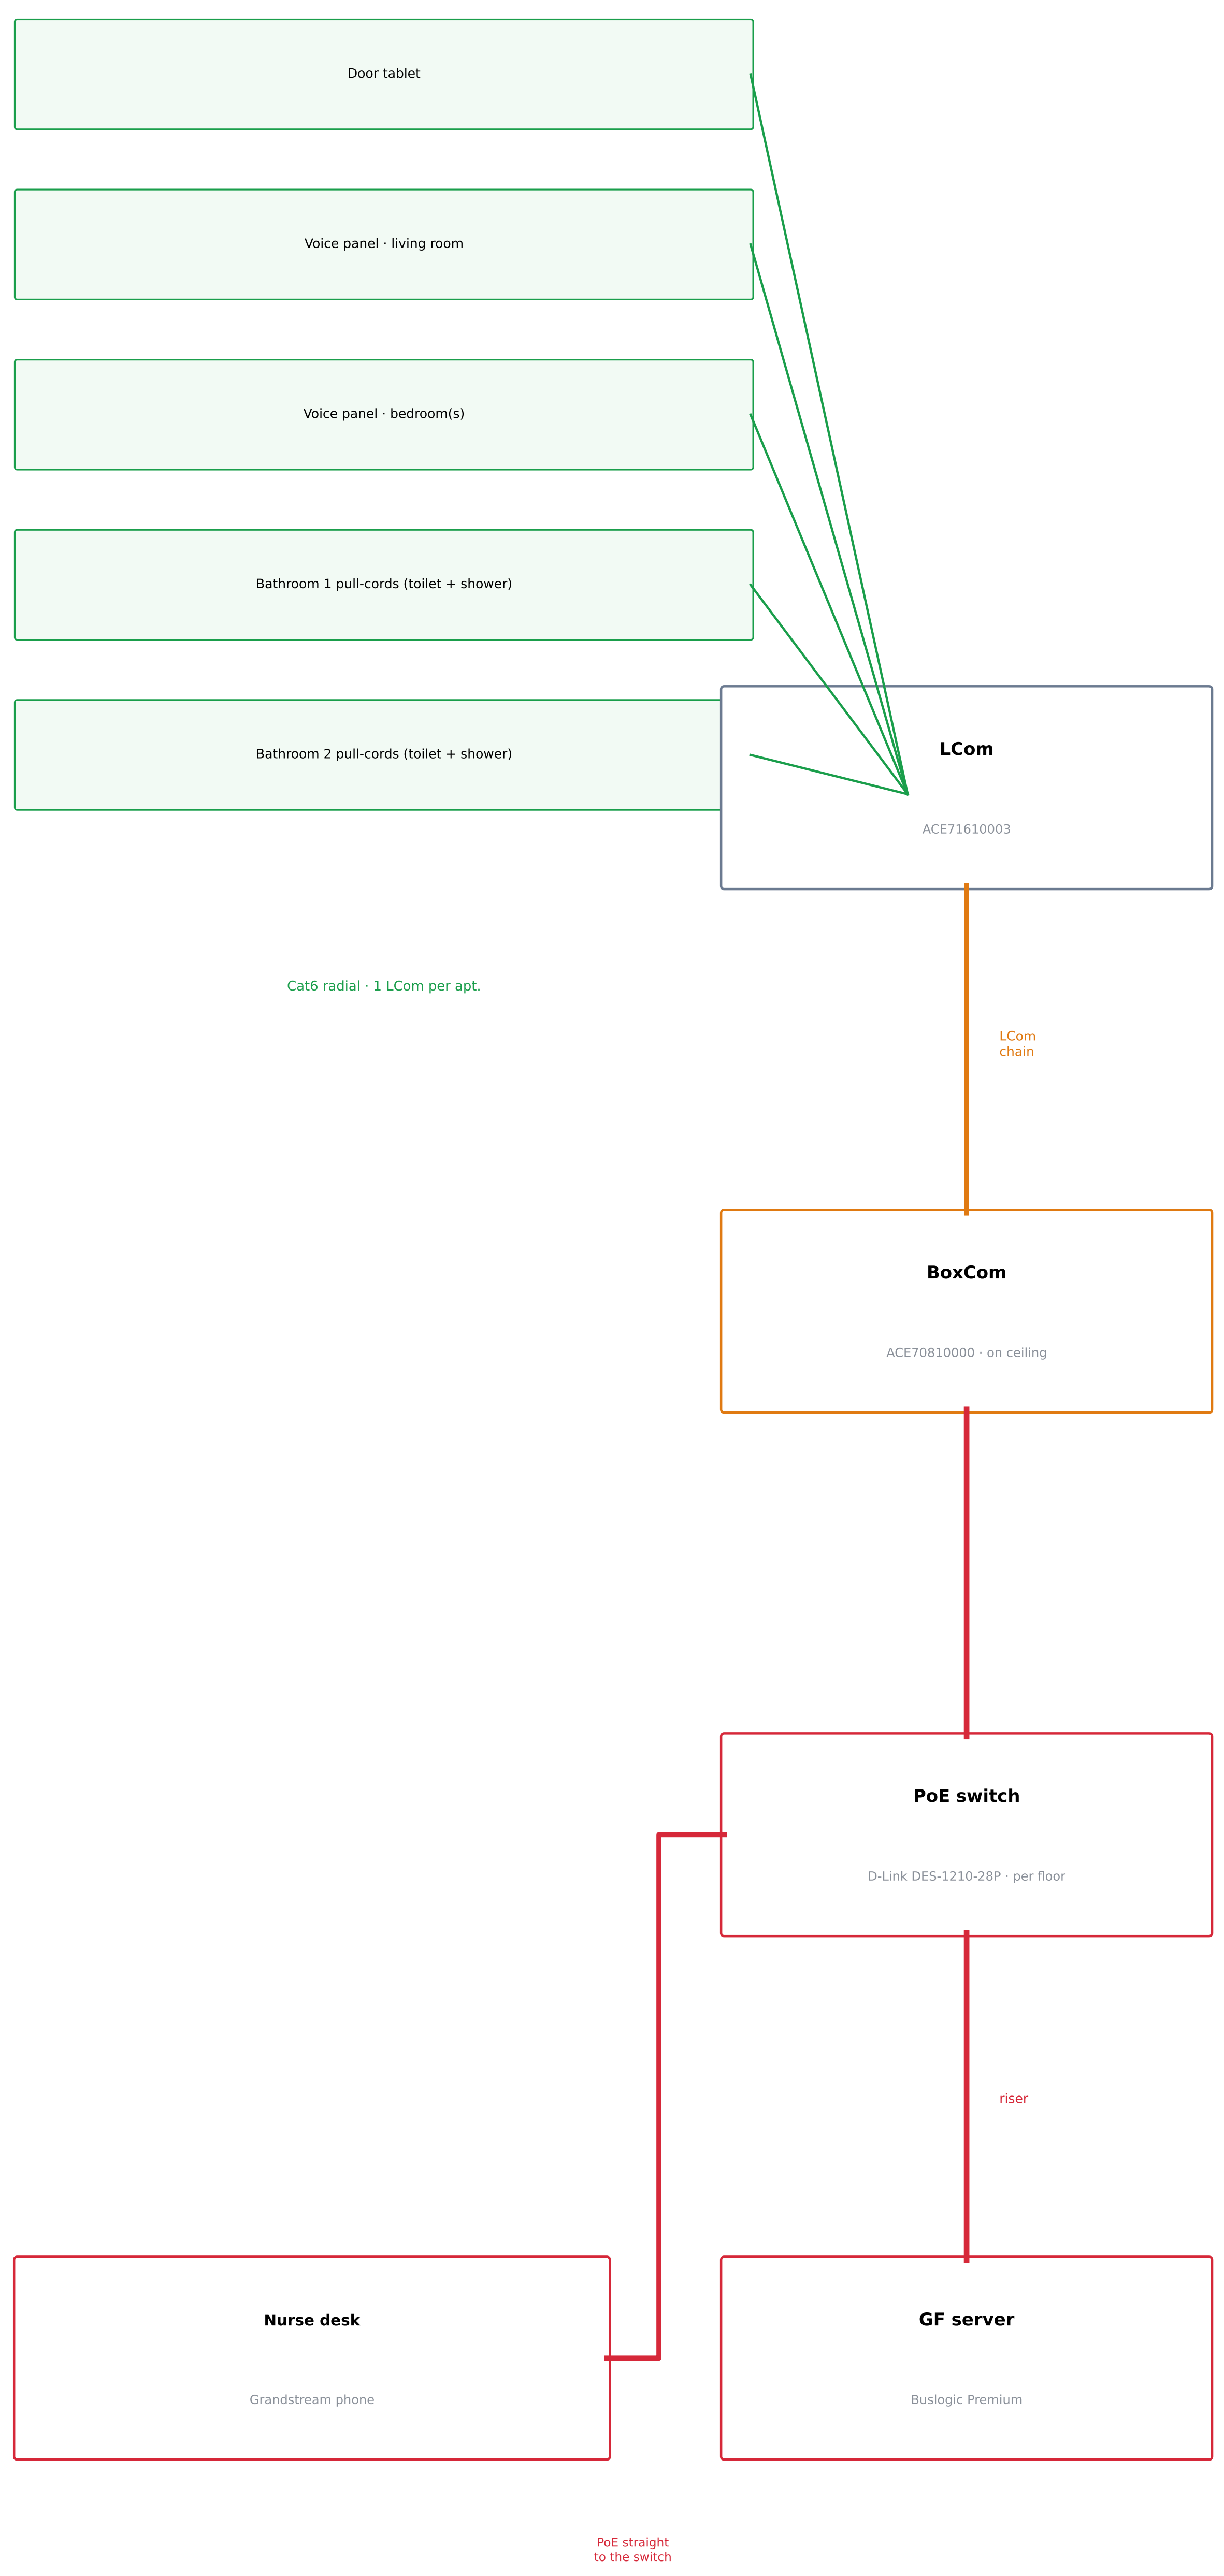
Door tablet
Voice panel · living room
Voice panel · bedroom(s)
Bathroom 1 pull-cords (toilet + shower)
Bathroom 2 pull-cords (toilet + shower)
LCom
ACE71610003
Cat6 radial · 1 LCom per apt.
LCom
chain
BoxCom
ACE70810000 · on ceiling
PoE switch
D-Link DES-1210-28P · per floor
riser
Nurse desk
Grandstream phone
GF server
Buslogic Premium
PoE straight
to the switch

NOTES · NOTAS

1. 8 identical floors with 4 apartments (2 one-bedroom and 2 two-bedroom).

2. On each floor: 2 BoxComs on the ceiling and a rack with the PoE switch.

3. Chain 1: x01 → x04 → public toilet.
Chain 2: x02 → x03.

4. The switches run up the riser to the main GF rack.

5. The Grandstream desk phone goes straight to the PoE switch and shows each call in its colour.

6. The whole system is PoE.

7. Preliminary quantities: validate with Advantecnia and on site.

MIGDALEI YAM A TIJON · ASSISTED LIVING

Nurse call – GF + 8 floors · 32 apartments

System: ACE BG · Advantecnia   Prepared by: Telab International

RISER DIAGRAM AND TOPOLOGY

SCALE · ESCALA	DATE · FECHA	REV	SHEET
S/E	**15/10/2026**	**B**	**08**

Base: architect's plan L5 (Massad Oz / Triplet) · dimensions in m

A1 format · Rev. B – on the real plan

BILL OF MATERIALS – WHOLE BUILDING (GF + 8 floors · 32 apartments · 10 public toilets)

Code	Description	Qty.	Remark
IN THE APARTMENTS (32)			
TAB	Door tablet (iPad / Android) – call and voice	**32**	1 per apartment
VOZ	Voice call panel with buttons – ACE82182451	**80**	living room + each bedroom
TI/TD	Pull-cord – ACE40320303W (toilet and shower)	**128**	4 per apartment
LC	LCom – ACE71610003	**32**	1 per apartment
PUBLIC TOILETS (10)			
T	Pull-cord – ACE40320303W	**10**	8 floors + 2 on GF
LP	Corridor light – ACE41020309	**10**	above each door
LC	LCom – ACE71610003	**9**	1 per floor + 1 on GF
RACKS AND HEAD-END			
BC	BoxCom – ACE70810000 (on the ceiling)	**17**	2 per floor + 1 on GF
SW	24-port PoE switch – D-Link DES-1210-28P	**9**	1 per floor + GF
GAB	12U wall rack with patch panel (for the switch)	**8**	1 per floor
GAB-PB	Main floor-standing rack with UPS	**1**	GF
SRV	Buslogic Premium server (Advantcare) with software	**1**	GF
TEL	Grandstream Android phone (PoE, colours by call type)	**1**	nurse desk
CABLES (+ 15 % spare)			
—	Cat6 radial inside the apartments (green)	**1700 m**	183 m per floor
—	Cat6 / Cat7 chain LCom → BoxCom (orange)	**750 m**	80 m per floor
—	Cat6A / Cat7 racks and riser (red)	**130 m**	includes riser

NOTES · NOTAS

1. Quantities calculated from the model (typical floor × 8 + GF).
2. Cable lengths measured on the drawn route, + 15 %.
3. Prices: per current Advantecnia price list.
4. Validate on site before purchasing.

MIGDALEI YAM A TIJON · ASSISTED LIVING
Nurse call – GF + 8 floors · 32 apartments
System: ACE BG · Advantecnia   Prepared by: Telab International

BILL OF MATERIALS

SCALE · ESCALA	DATE · FECHA	REV	SHEET
S/E	**15/10/2026**	**B**	**09**

Base: architect's plan L5 (Massad Oz / Triplet) · dimensions in m
A1 format · Rev. B – on the real plan

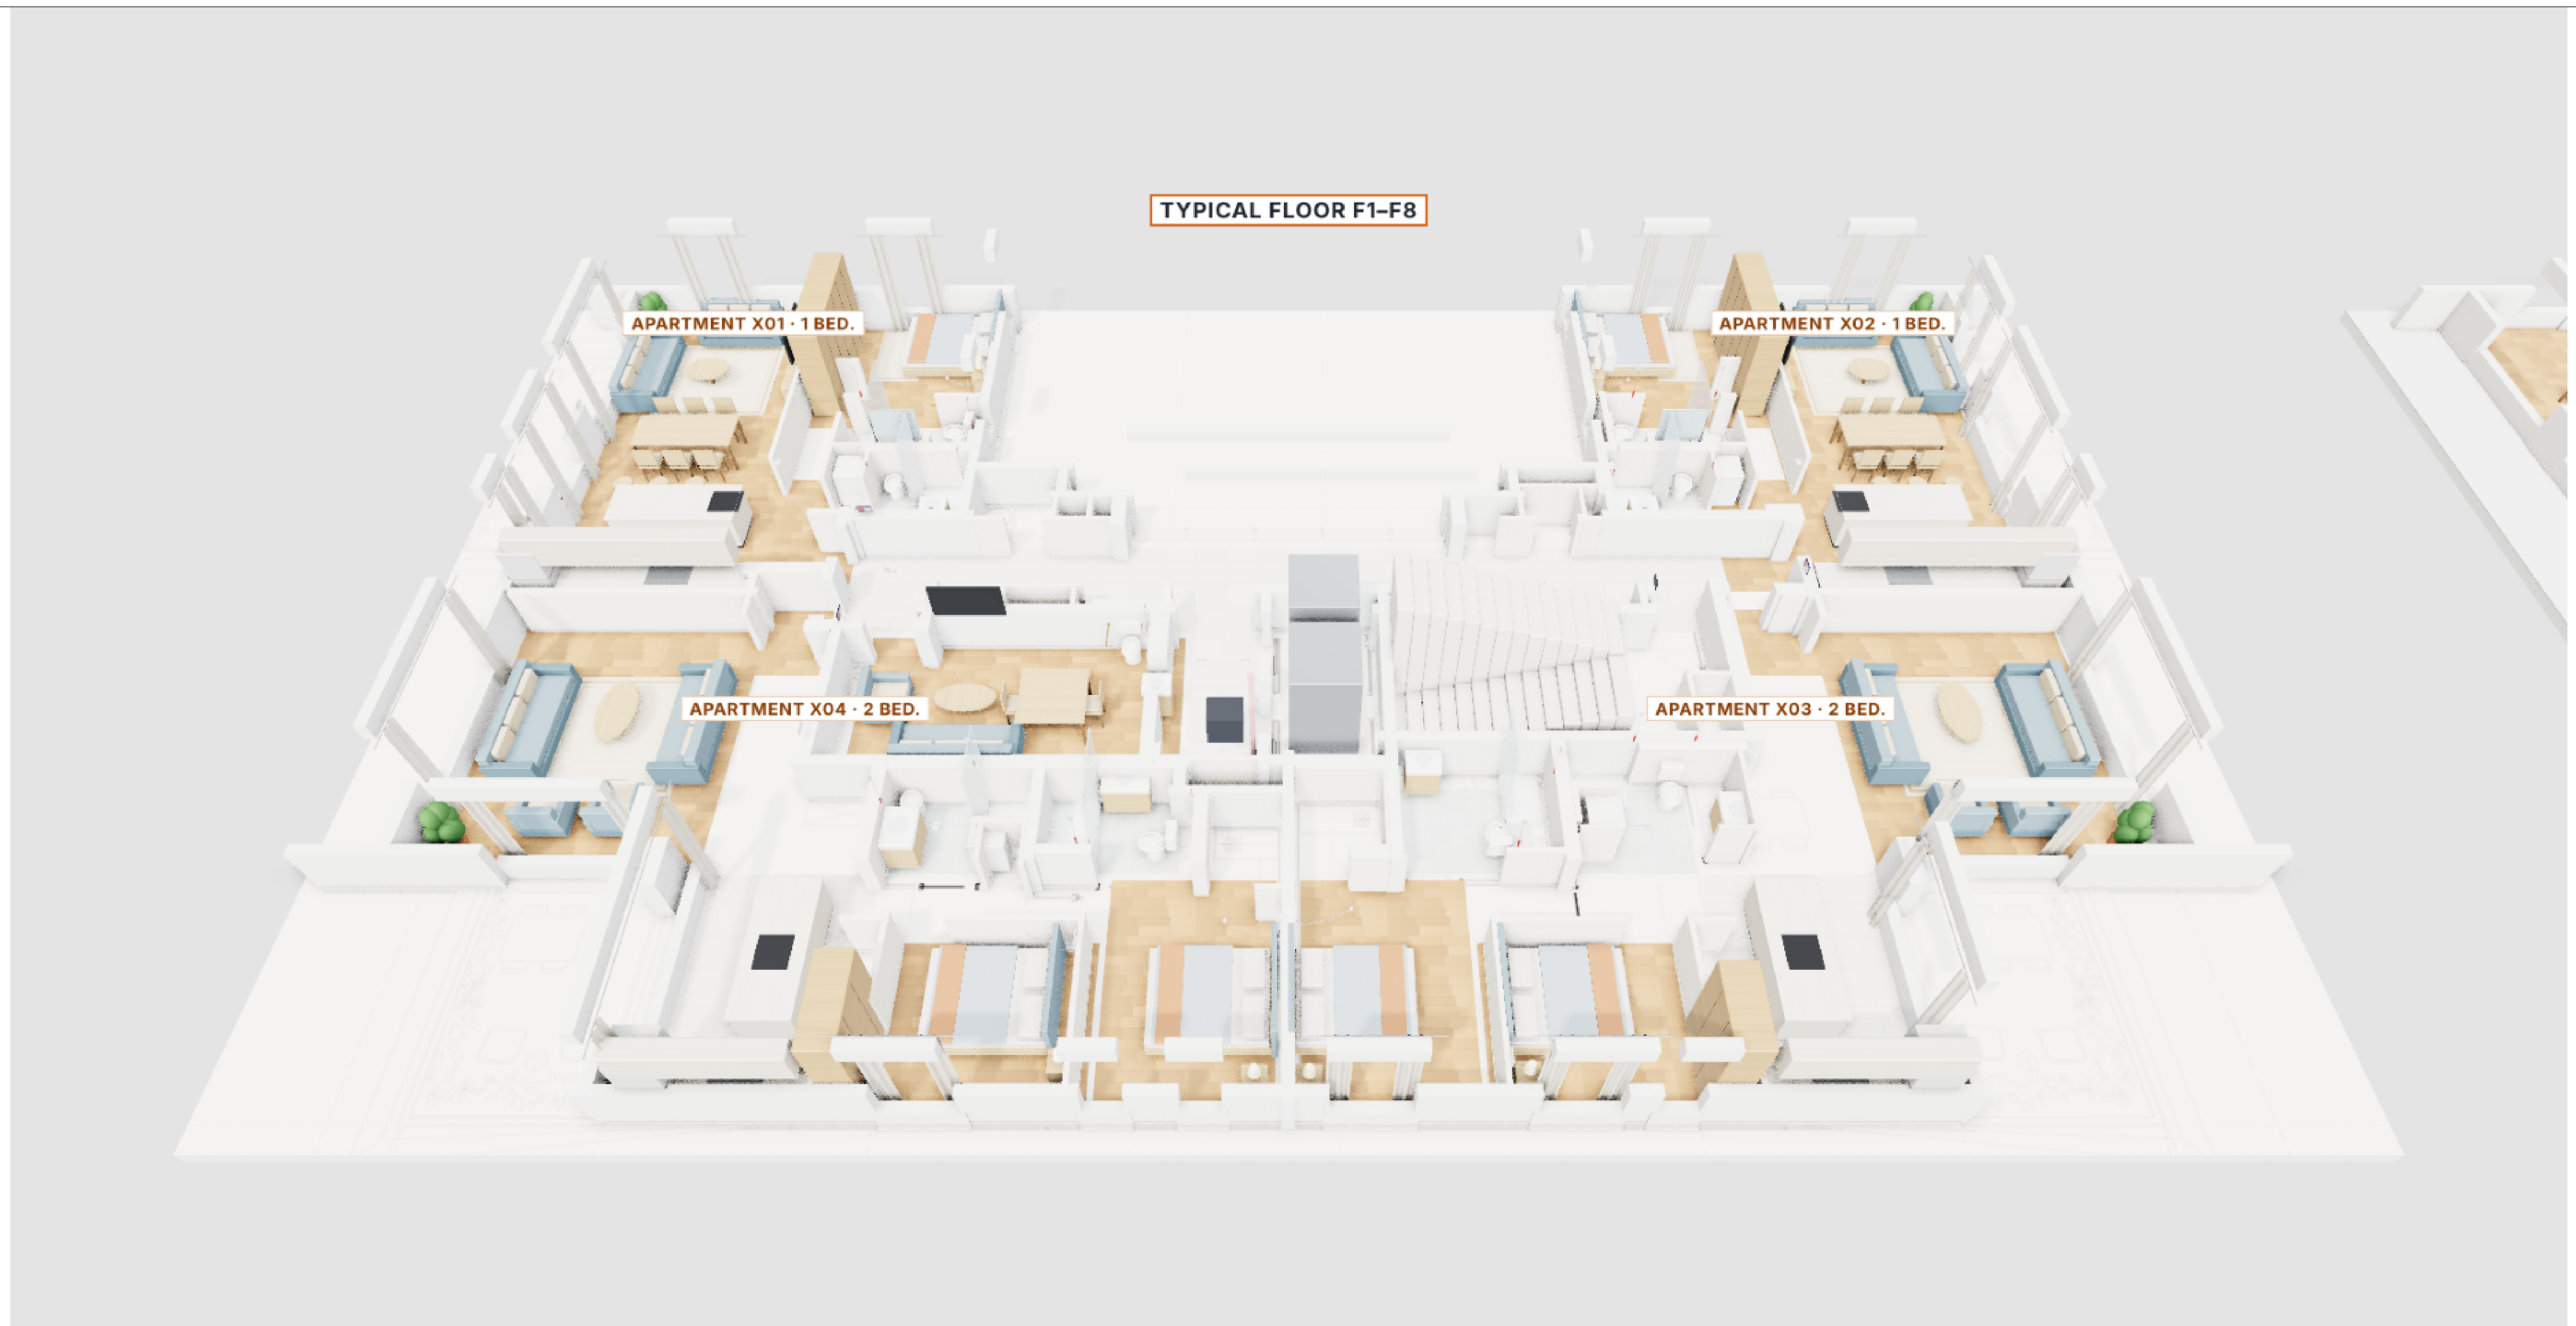
TYPICAL FLOOR F1–F8
APARTMENT X01 · 1 BED.
APARTMENT X02 · 1 BED.
APARTMENT X04 · 2 BED.
APARTMENT X03 · 2 BED.

A · Typical floor – 4 apartments

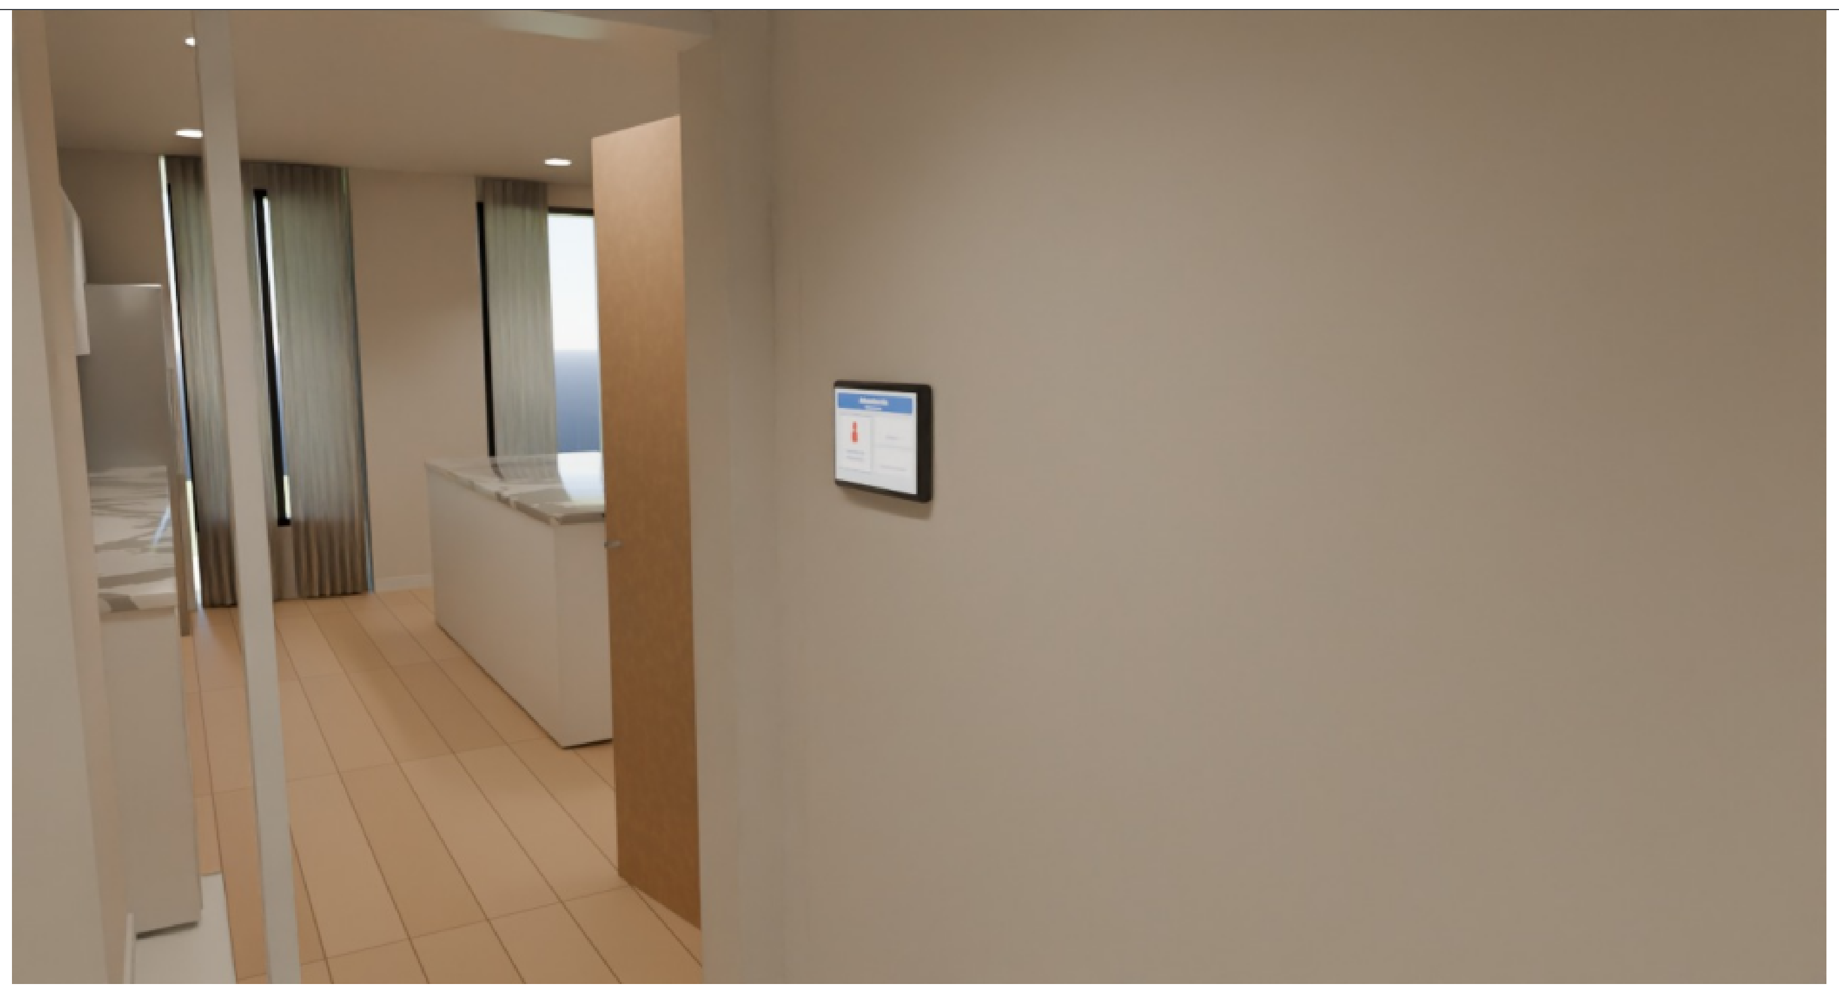

B · Door tablet

C · Bedroom – voice panel and pear

D · Bathroom – pull-cords at toilet and shower

E · GF – nurse desk

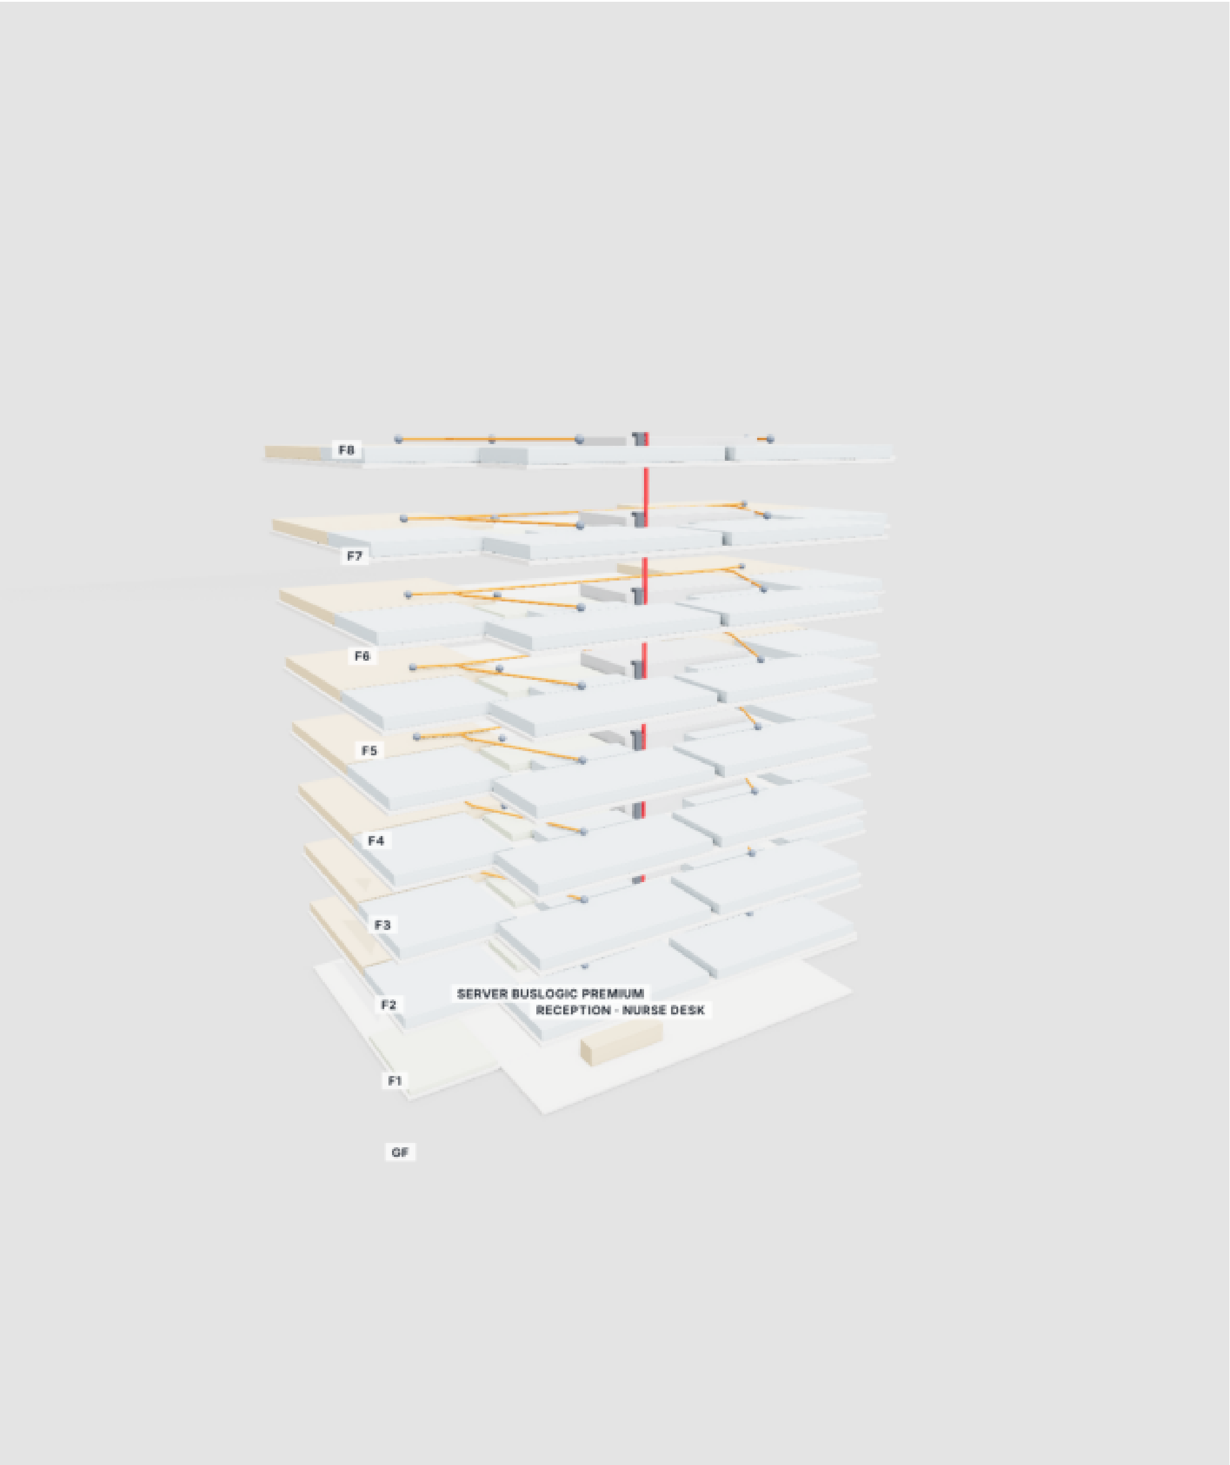
F8
F7
F6
F5
F4
F3
F2
F1
GF
SERVER BUSLOGIC PREMIUM
RECEPTION · NURSE DESK

F · Building GF + 8 floors

MIGDALEI YAM A TIJON · ASSISTED LIVING

Nurse call – GF + 8 floors · 32 apartments

System: ACE BG · Advantecnia   Prepared by: Telab International

3D VIEWS

SCALE · ESCALA	DATE · FECHA	REV	SHEET
S/E	**15/10/2026**	**B**	**10**

Base: architect's plan L5 (Massad Oz / Triplet) · dimensions in m

A1 format · Rev. B – on the real plan

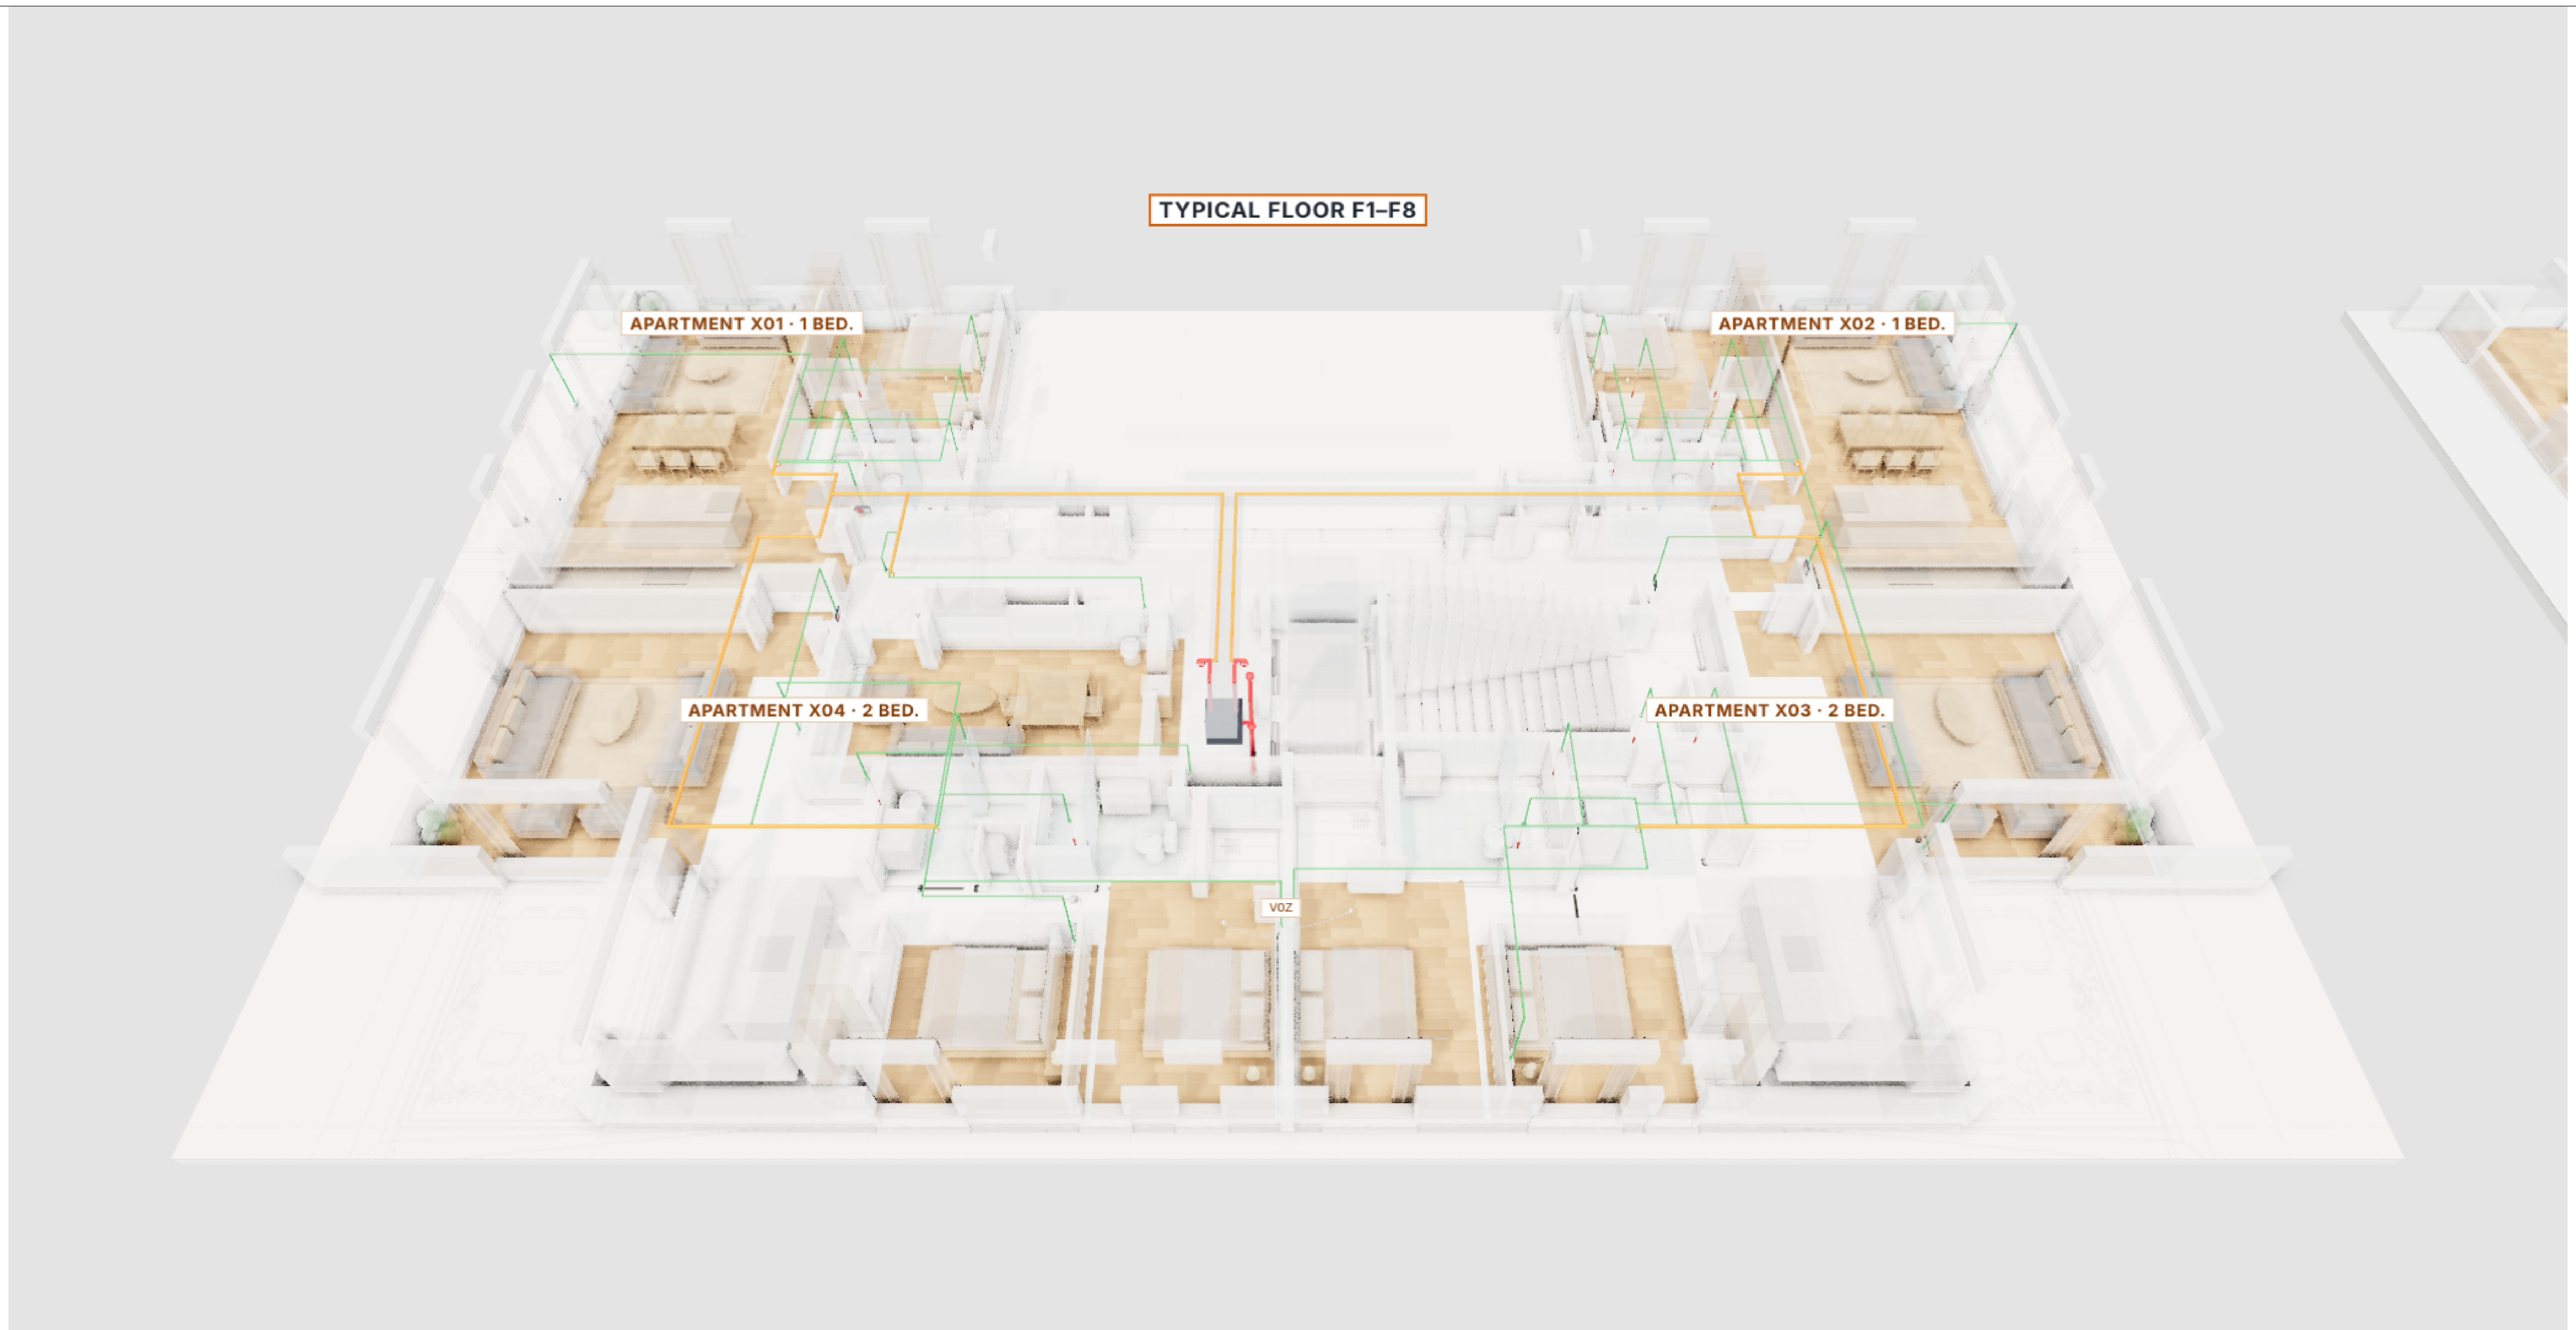
TYPICAL FLOOR F1–F8
APARTMENT X01 · 1 BED.
APARTMENT X02 · 1 BED.
APARTMENT X04 · 2 BED.
APARTMENT X03 · 2 BED.
VOZ

A · Typical floor – wiring (green radial · orange LCom chain · red network)

B · Ground floor – lobby and reception

C · Living room – voice panel with buttons

COLOURS · COLORES · צבעים

🟩 Cat6 radial: each device → its apartment LCom
Cat6 radial: each device → apartment LCom · Cat6 רדיאלי: כל התקן ← LCom של הדירה

🟧 Cat6 / Cat7 chain: LCom → LCom → ceiling BoxCom
Cat6 / Cat7 chain: LCom → LCom → BoxCom · Cat6 / Cat7 שרשרת: LCom ← LCom ← BoxCom

🟥 Cat6A / Cat7 network: BoxCom → PoE switch → riser → GF server
Cat6A / Cat7 network: BoxCom → switch → riser → GF server · Cat6A / Cat7 רשת: BoxCom ← מתג ← עמוד ← שרת

MIGDALEI YAM A TIJON · ASSISTED LIVING
Nurse call – GF + 8 floors · 32 apartments
System: ACE BG · Advantecnia   Prepared by: Telab International

3D VIEWS – WIRING

SCALE · ESCALA	DATE · FECHA	REV	SHEET
S/E	15/10/2026	B	11

Base: architect's plan L5 (Massad Oz / Triplet) · dimensions in m
A1 format · Rev. B – on the real plan

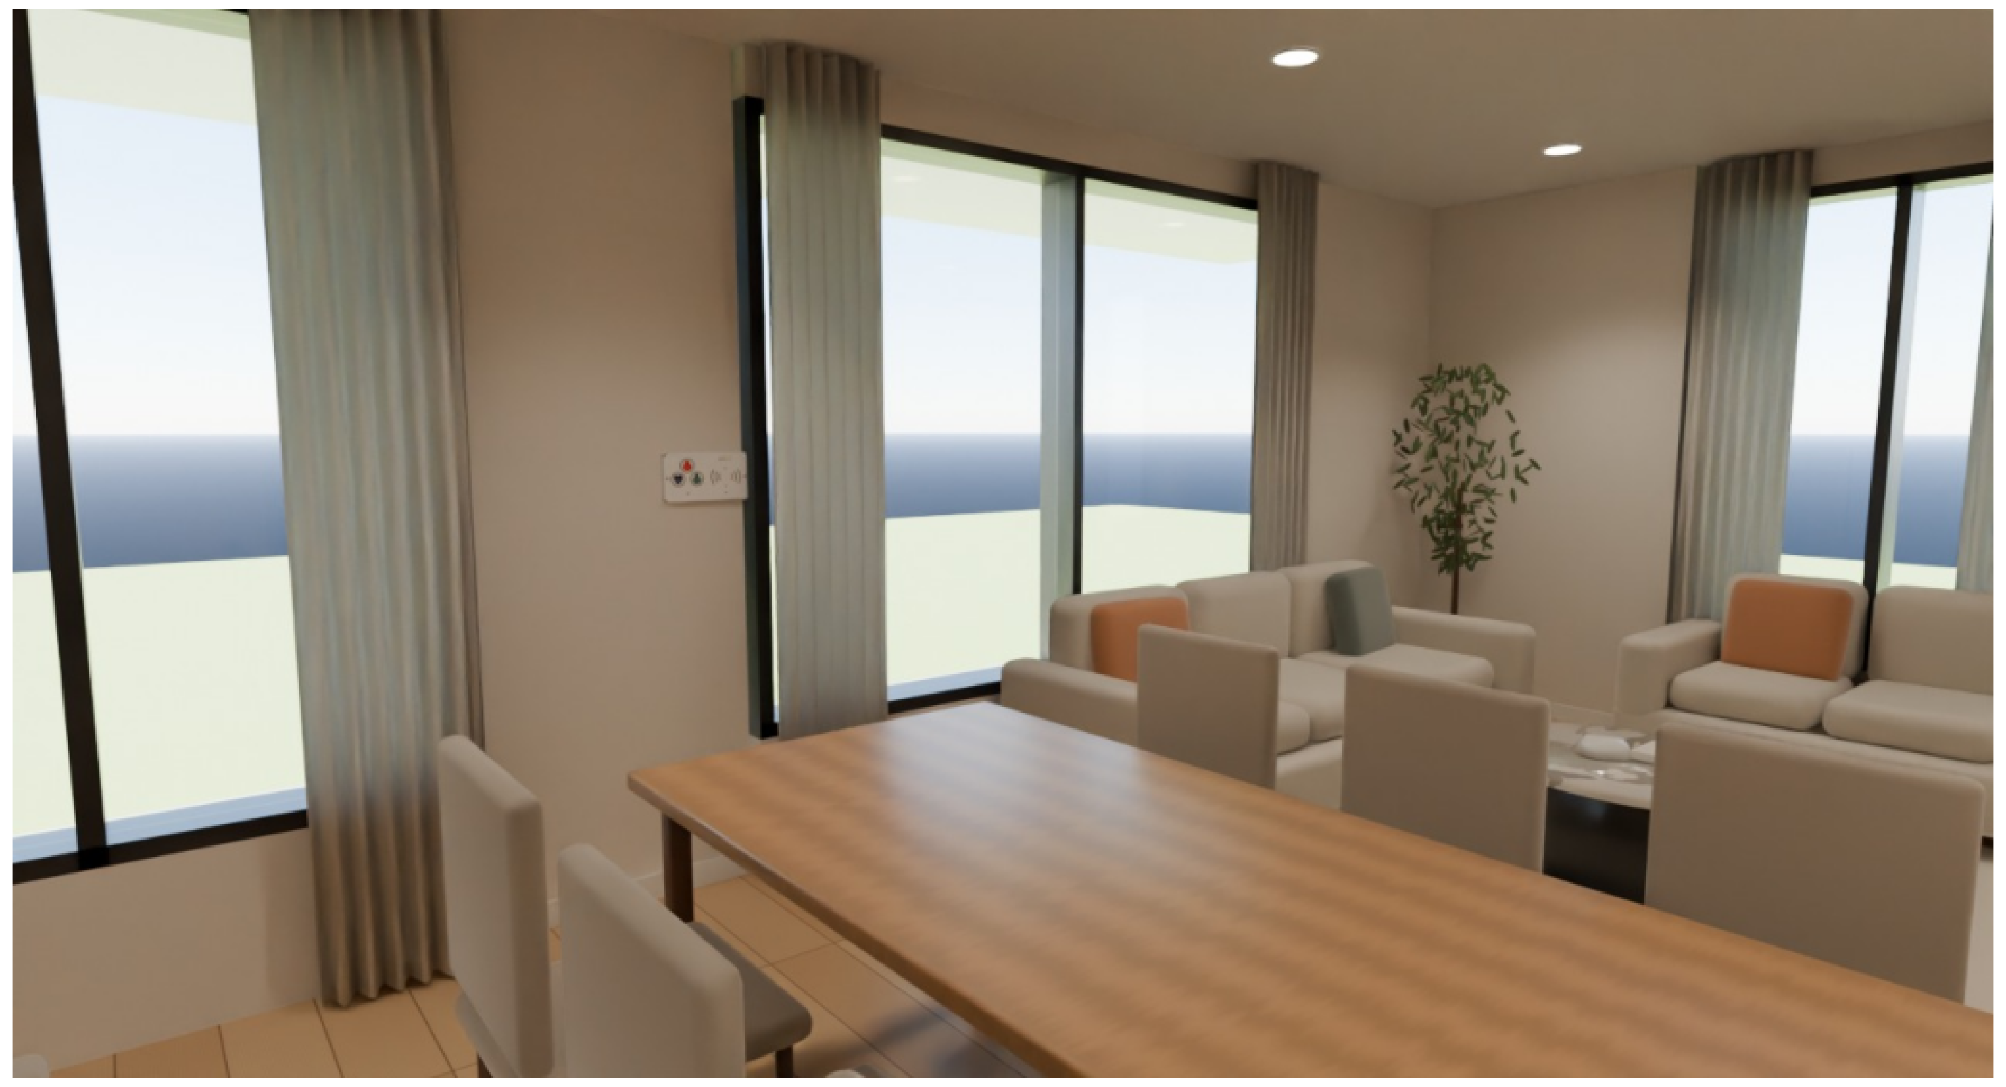
A · Living room – voice call panel

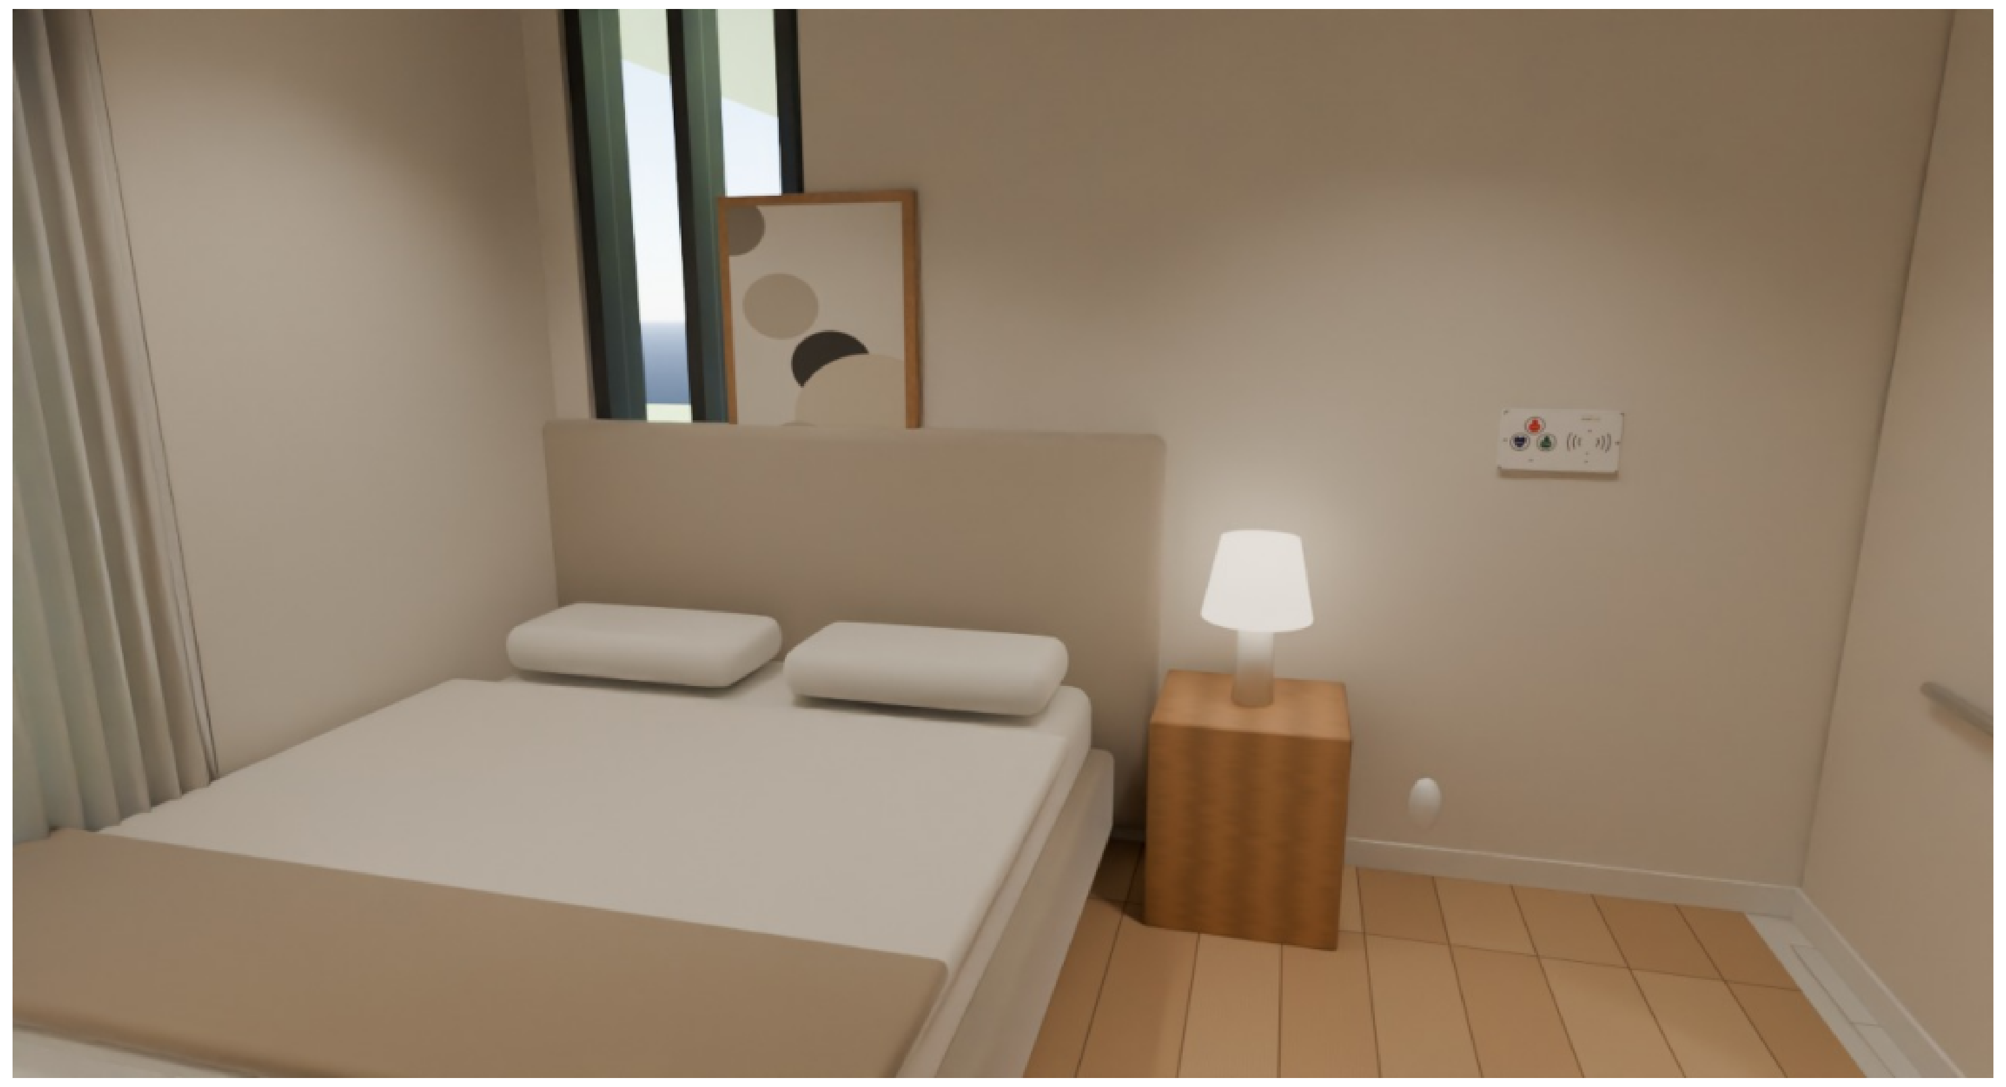
B · Bedroom – voice panel and call pear

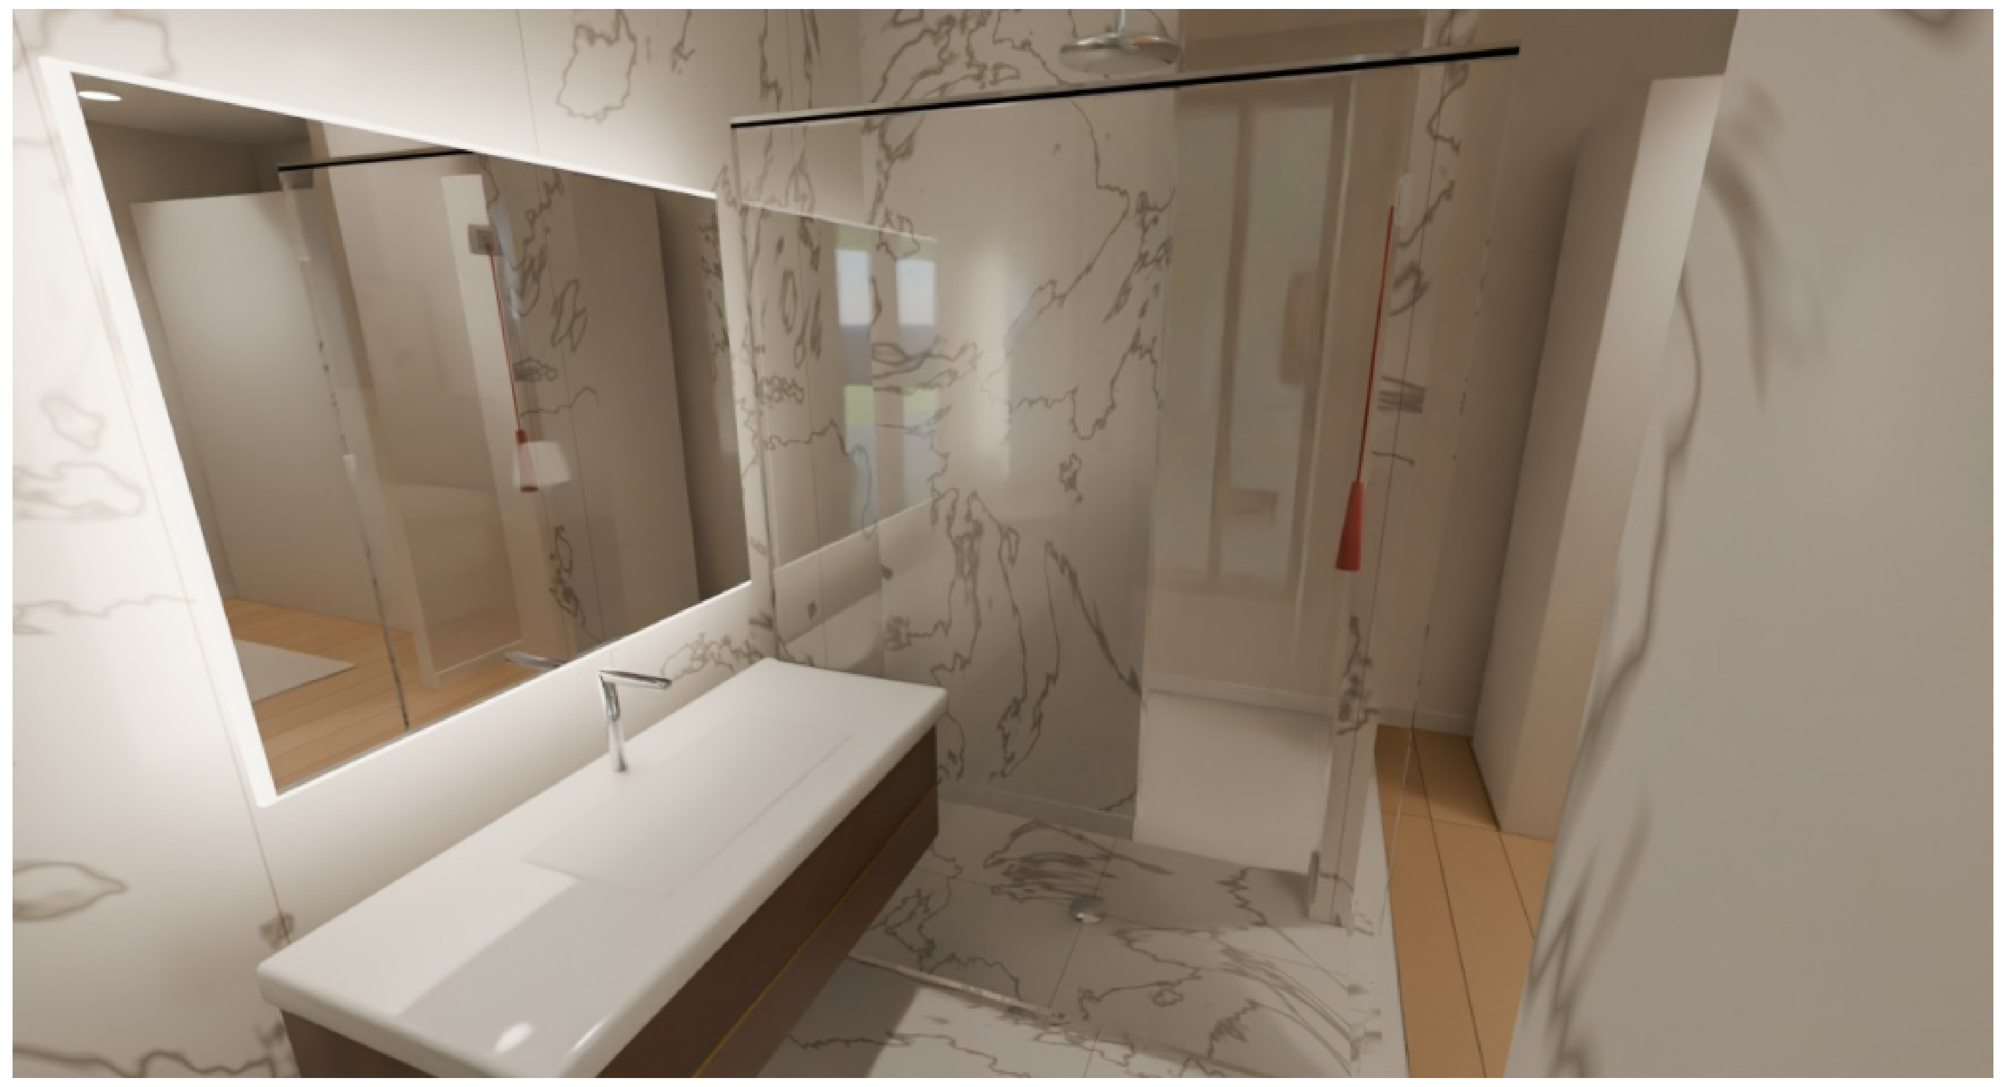
C · Bathroom – SOS pull-cord

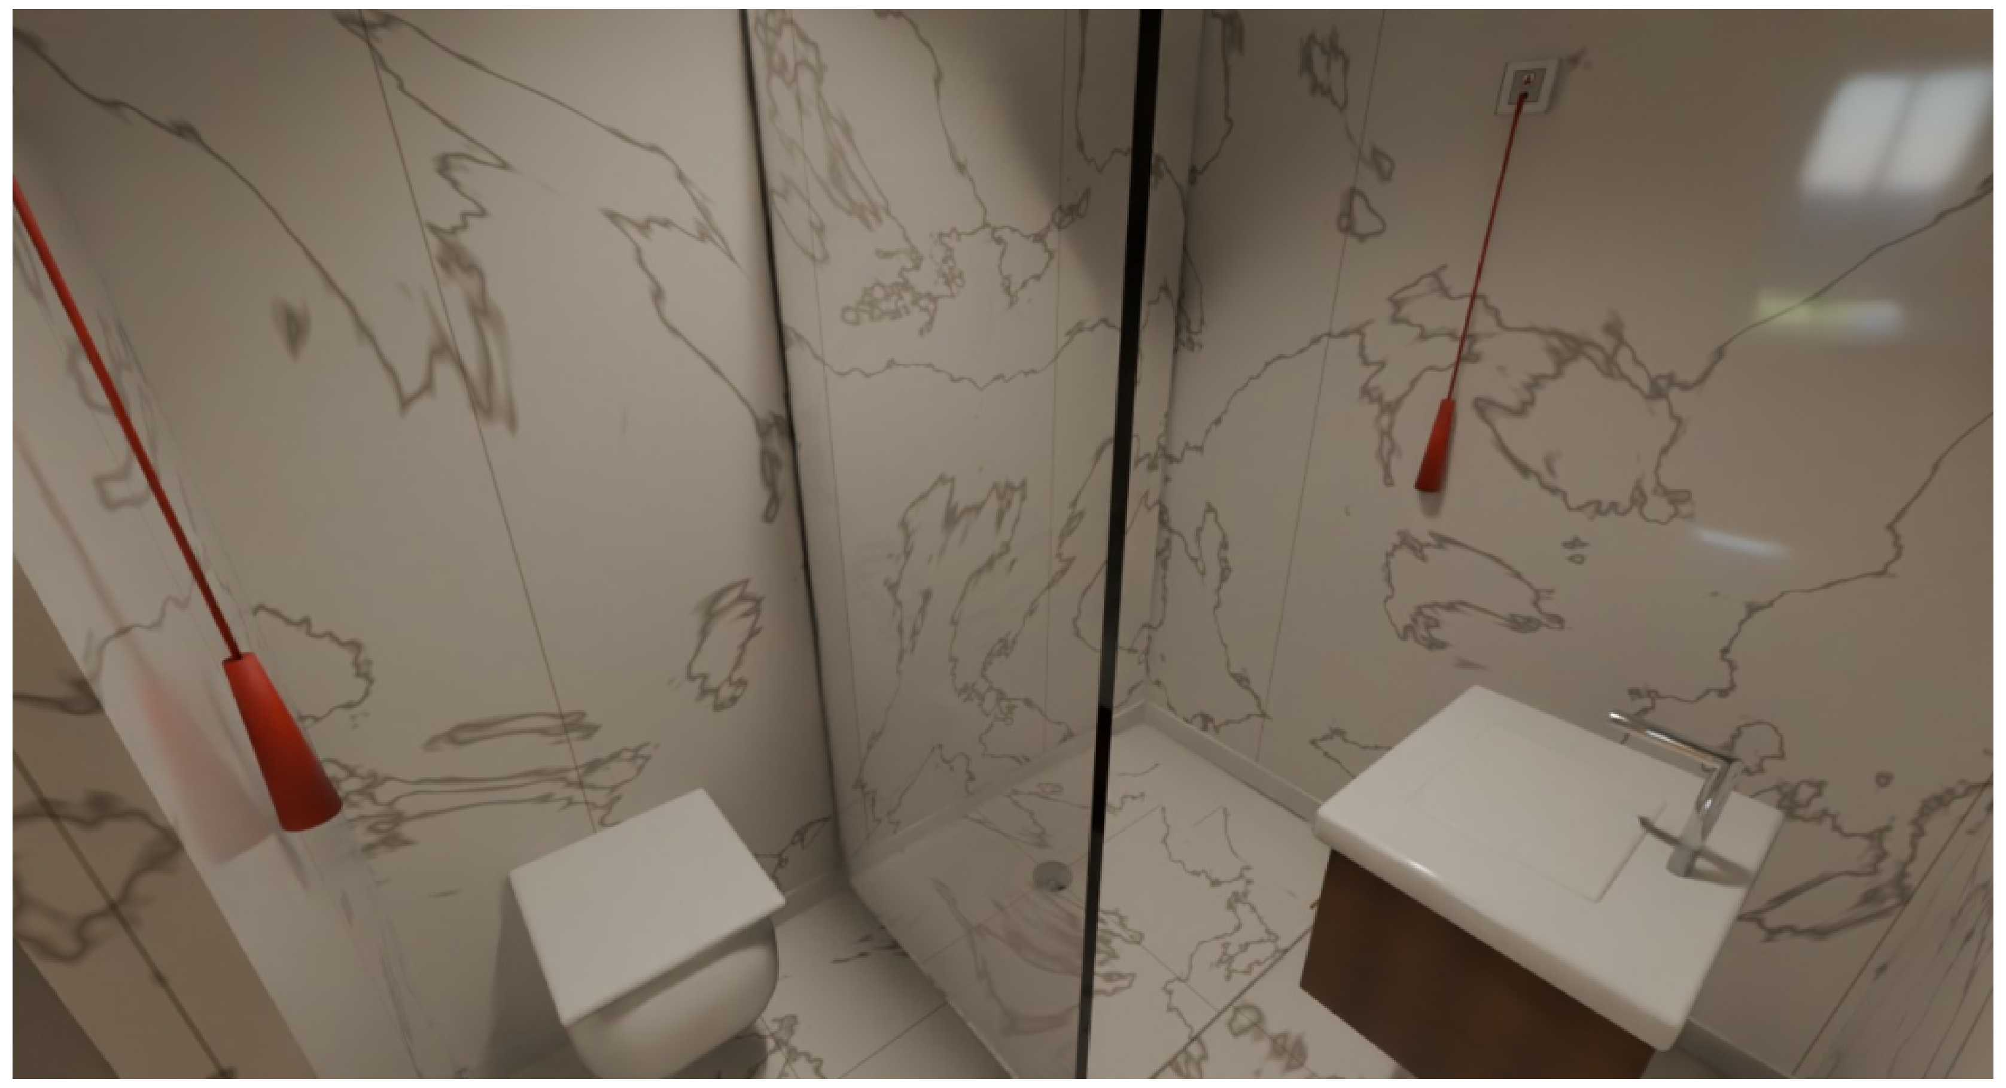
D · Bathroom 2 – pull-cord at toilet and shower

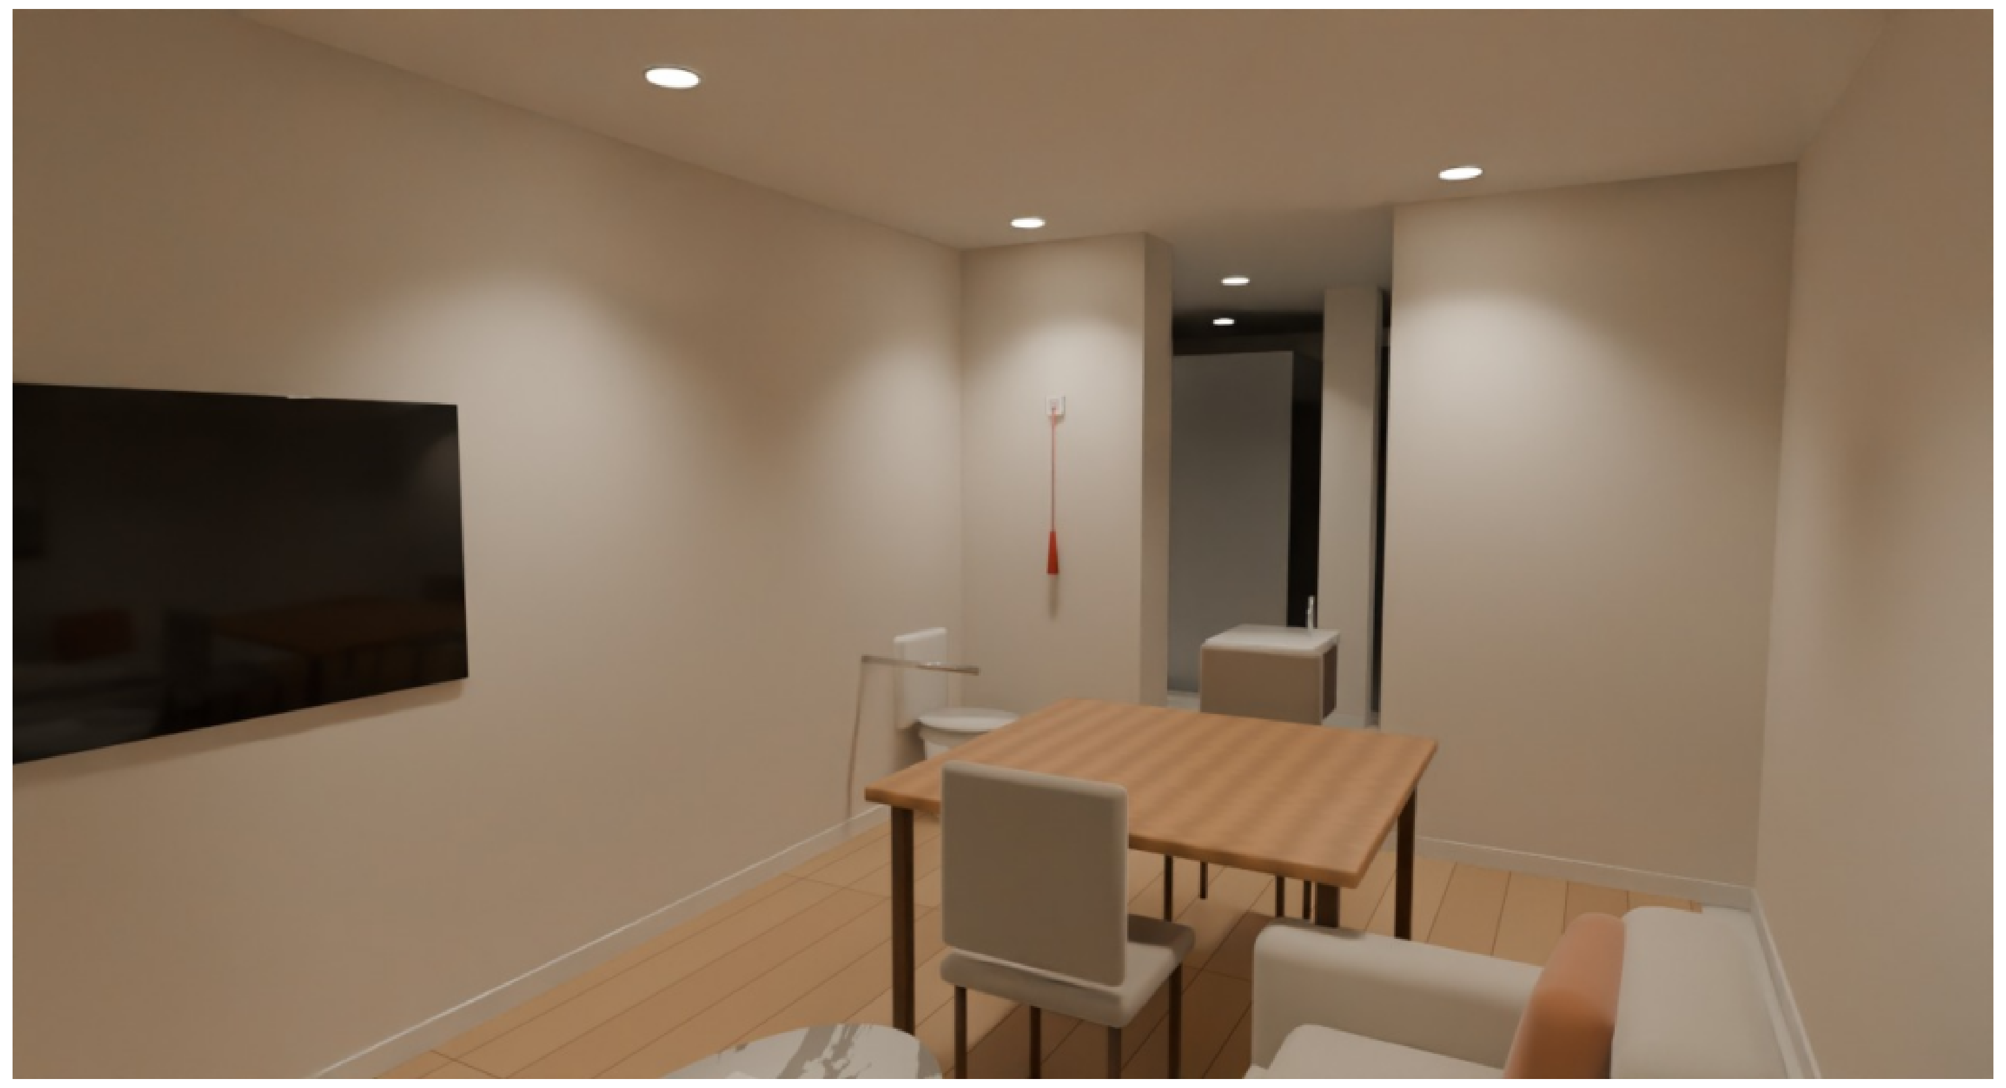
E · Common room – public toilet

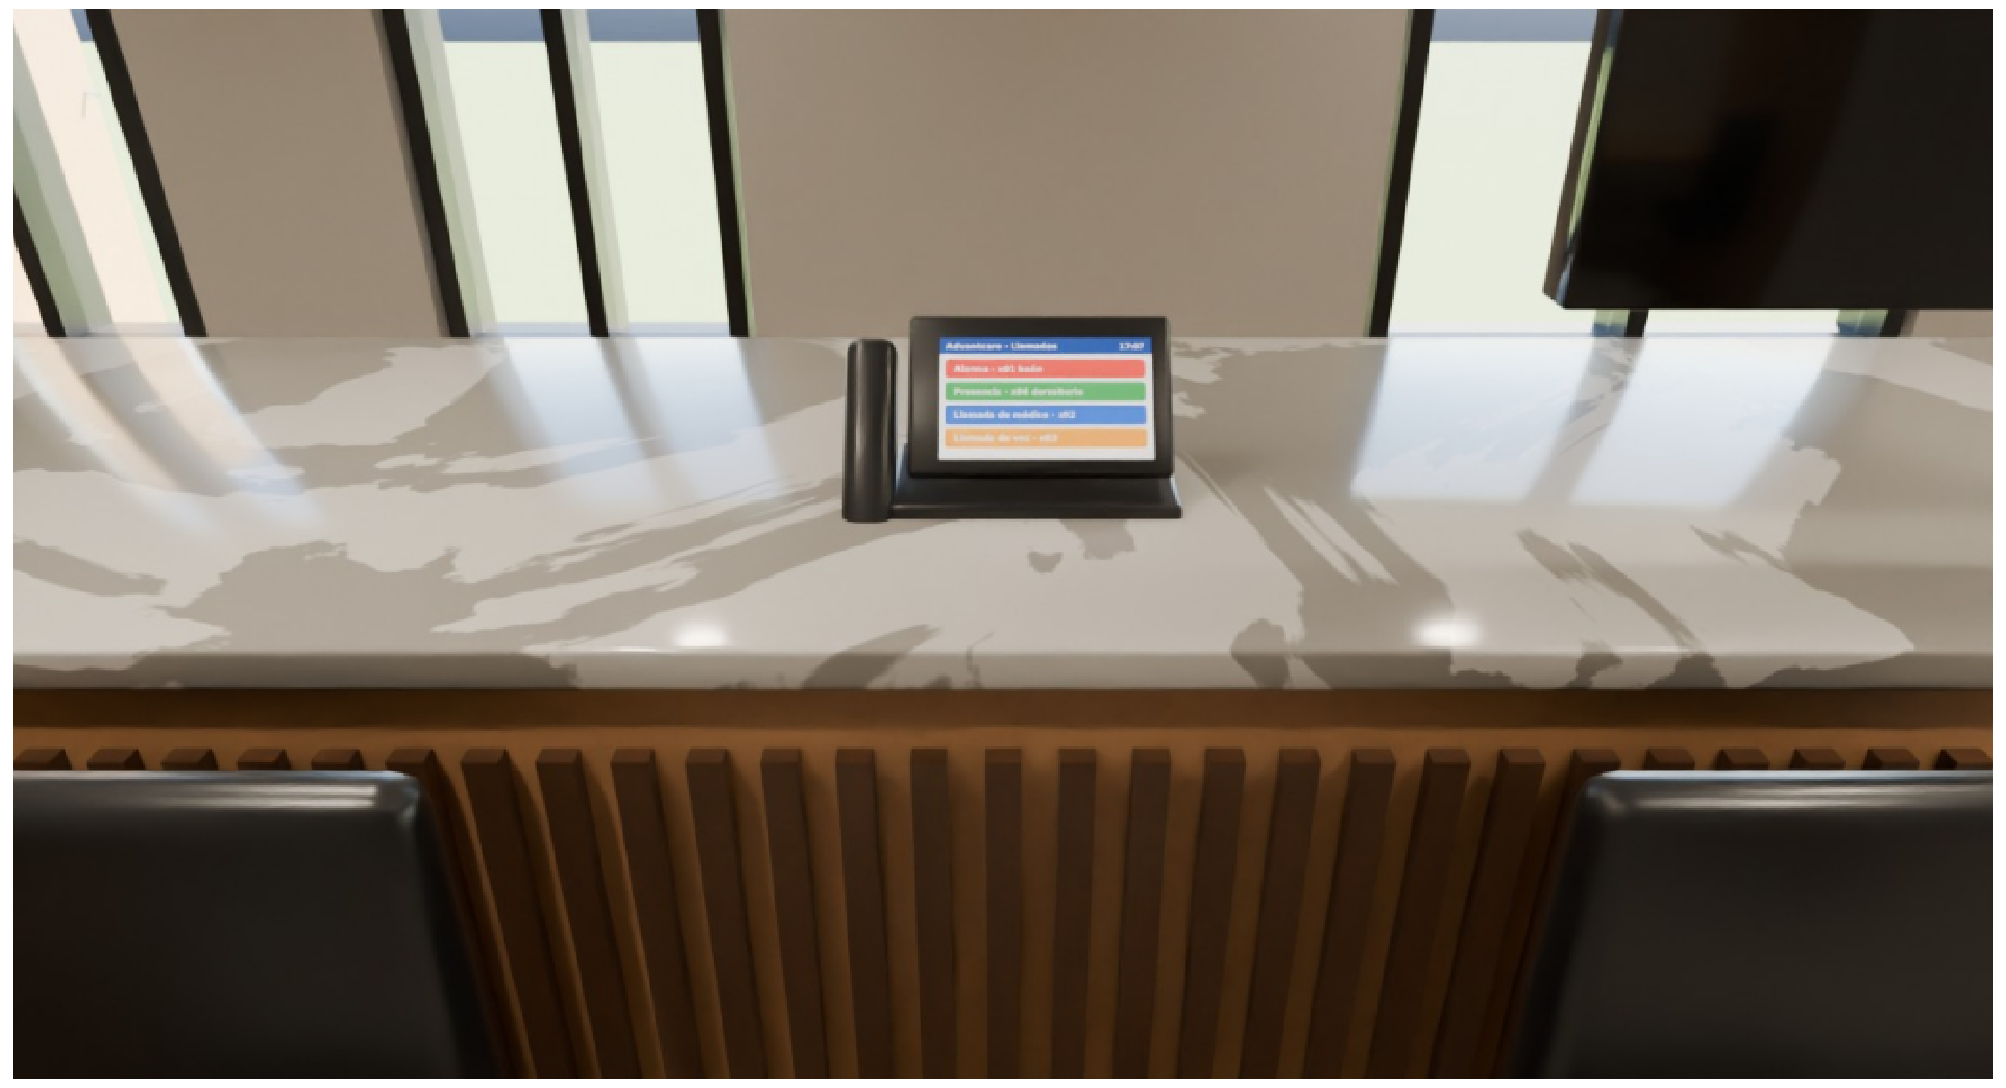
F · Nurse desk – Grandstream phone

MIGDALEI YAM A TIJON · ASSISTED LIVING

Nurse call – GF + 8 floors · 32 apartments

System: ACE BG · Advantecnia   Prepared by: Telab International

PHOTOREALISTIC RENDERS

SCALE · ESCALA	DATE · FECHA	REV	SHEET
S/E	15/10/2026	B	12

Base: architect's plan L5 (Massad Oz / Triplet) · dimensions in m

A1 format · Rev. B – on the real plan