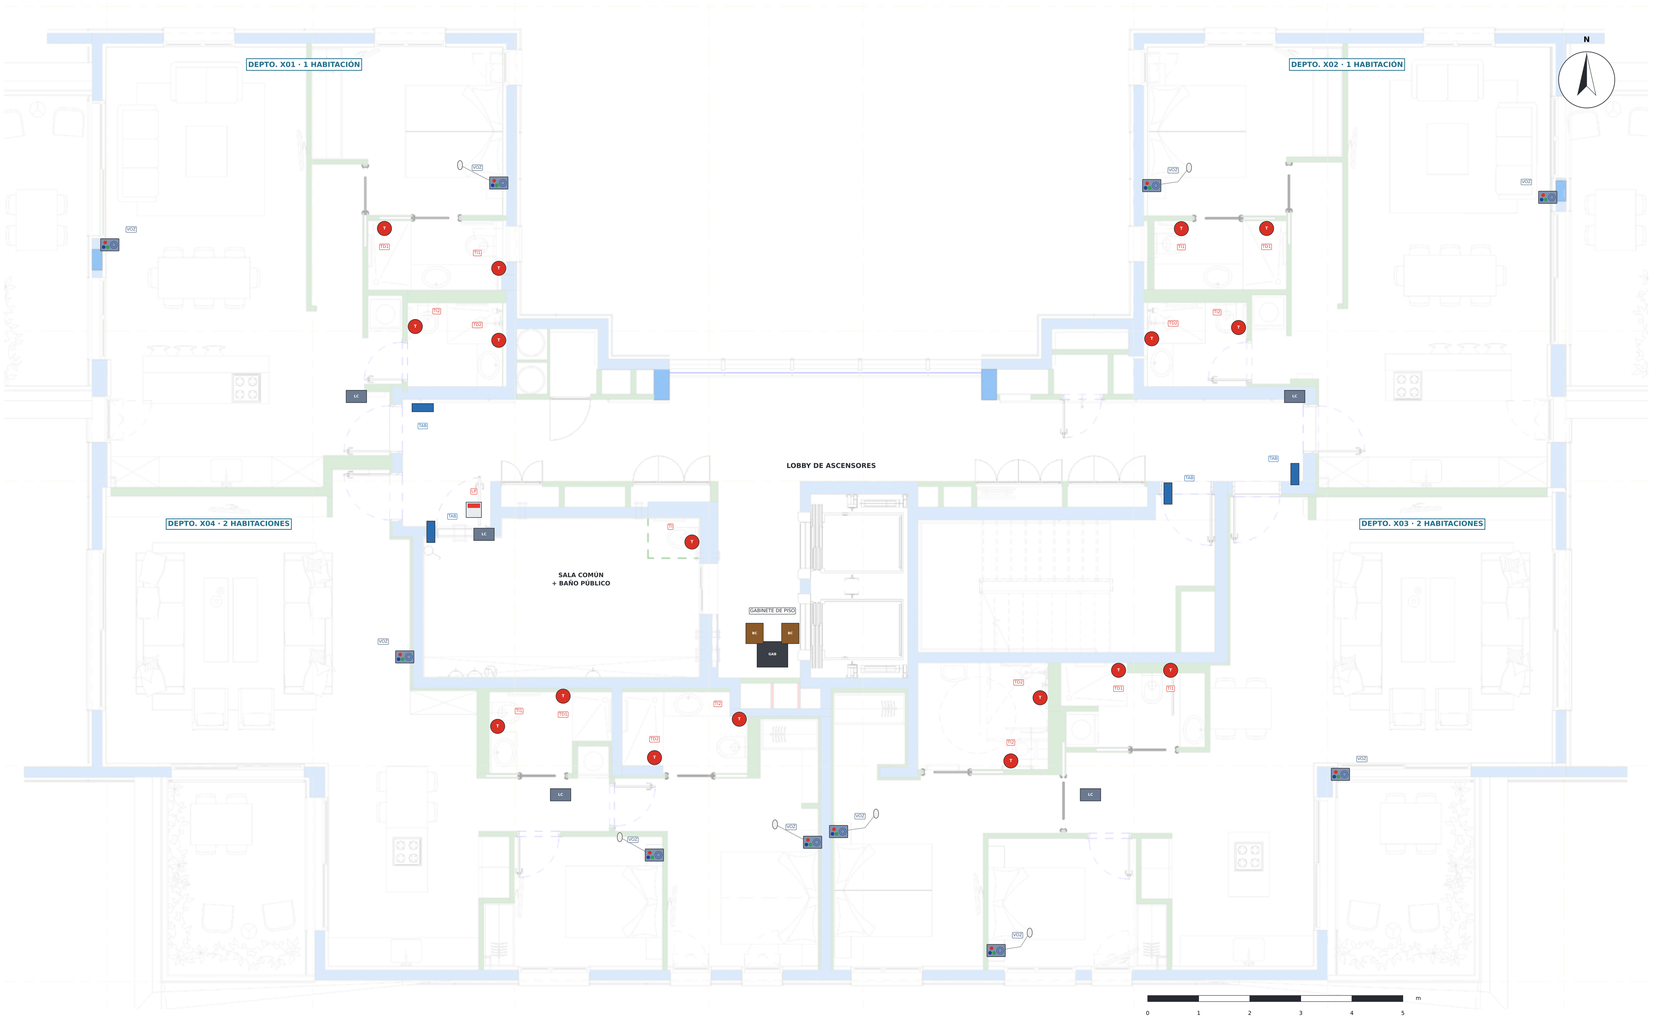


EQUIPOS · DEVICES · ציוד

- **TAB** · Tablet de la puerta (iPad / Android) – llamada y voz, h 1,40 m
  Door tablet – call and voice · טאבלט בדלת – שיחה וקול · גובה 1.40 מ׳
- **VOZ** · Panel con voz y botones ACE82182451 – salón y dormitorios, h 1,20–1,30 m
  Voice panel with buttons – living room and bedrooms · פאנל קולי עם כפתורים – סלון וחדרי שינה · גובה 1.20–1.30 מ׳
- Pera de llamada junto a la cama (en los dormitorios)
  Call pear next to the bed (bedrooms) · כפתור חיבור ליד המיטה (בחדרי השינה)
- **TI / TD** · Tirador de baño ACE40320303W – inodoro y ducha, h 1,85 m
  Pull-cord – toilet and shower, h 1.85 m · חבל משיכה מאולתר לשירותים ולמקלחת · גובה 1.85 מ׳
- **LP** · Luz de pasillo ACE41020309 – sobre la puerta de cada baño público
  Corridor light – above each public toilet door · מנורת מסדרון מעל דלת כל שירותים ציבוריים
- **LC** · LCom ACE71610003 – concentrador del departamento (cielorraso)
  LCom – apartment hub (ceiling) · LCom – מרכזת הדירה (בתקרה)
- **BC** · BoxCom ACE70810000 – concentrador en bus de varios deptos. (techo)
  BoxCom – bus hub for several apartments (ceiling) · BoxCom – מרכזת אוטובוס עבור מספר דירות (בתקרה)
- **GAB** · Gabinete de piso 12U: switch PoE D-Link DES-1210-28P (24 puertos PoE)
  Floor rack: D-Link DES-1210-28P PoE switch · ארון רצפה: מתג PoE D-Link DES-1210-28P


CANTIDADES POR PISO × 8 PISOS

Código	Equipo	Por piso	8 pisos
TAB	Tablet de la puerta	4	32
VOZ	Panel con voz y botones	10	80
TI/TD	Tirador de baño (inodoro + ducha)	17	136
LP	Luz de pasillo (baño público)	1	8
LC	LCom	5	40
BC	BoxCom	2	16
SW	Switch PoE	1	8

NOTAS · NOTES

1. Base: plano de arquitectura L5 (piso tipo) – los 8 pisos son iguales: 4 departamentos por piso, 32 en total.
2. Departamentos x01 y x02: 1 habitación, salón con cocina y 2 baños. Departamentos x03 y x04: 2 habitaciones y 2 baños.
3. Tablet en la puerta de cada departamento (iPad / Android) para llamar y hablar con enfermería.
4. Panel con voz y botones (ACE82182451) en el salón y en cada dormitorio; en el dormitorio, con pera junto a la cama.
5. Tiradores de baño (ACE40320303W) en el inodoro y en la ducha de todos los baños, a 1,85 m.
6. Baño público por piso en la sala común: tirador + luz de pasillo sobre la puerta. Con los 2 de PB suman 10 baños públicos.
7. Gabinete de piso junto a los ascensores con el switch PoE D-Link DES-1210-28P; los 2 BoxCom van en el techo, al lado.
8. Ubicaciones según las marcas del cliente en el plano L2 (nt = panel con voz, tab = tablet): ver lámina 03.

ALTURAS DE MONTAJE

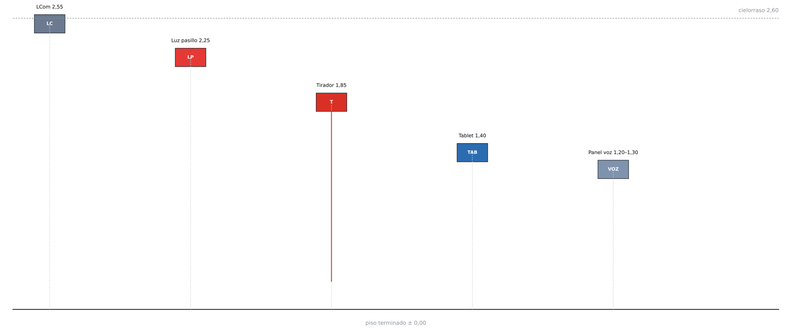

שירותים קריאת אחות



Tirador de baño

טבלט אנדרואיד קריאת אחות



Tablet en la puerta (iPad / Android)

מנורה קריאת אחות



Luz de pasillo

פנל קריאת אחות



Panel con voz y botones

MIGDALEI YAM A TIJON · VIVIENDA TUTELADA

Llamada de enfermería – PB + 8 pisos · 32 departamentos

Sistema: ACE BG · Advantecnia Elaboró: Telab International

PISO TIPO P1–P8 · LLAMADA DE ENFERMERÍA

Typical floor F1–F8 · nurse call

ESCALA · SCALE	FECHA · DATE	REV	LÁMINA
1:60	15/10/2026	B	01

Base: plano del arquitecto L5 (Massad Oz / Triplet) · cotas en metros

Formato A1 · Rev. B – sobre plano real

שירותים קריאת אחות



Tirador de baño

Código	**ACE40320303W**
Ubicación	Inodoro y ducha de cada baño y de los 10 baños públicos
Altura	**1,85 m**
Cantidad	**138**

1

טבלט אנדרואיד קריאת אחות



Tablet en la puerta (iPad / Android)

Código	**Advantecnia TV**
Ubicación	En el lobby, junto a la puerta de cada departamento
Altura	**1,40 m**
Cantidad	**32**

2

מנורה קריאת אחות



Luz de pasillo

Código	**ACE41020309**
Ubicación	Sobre la puerta de cada baño público
Altura	**2,25 m**
Cantidad	**10**

3

NOTAS · NOTES

1. Fotos de referencia de ACE BG / Advantecnia, con su título.

2. Tirador: cordón rojo con empuñadura, alcanzable desde el piso.

3. La tablet de la puerta llama y habla con enfermería.

4. La luz de pasillo se enciende cuando llaman desde el baño público.

5. El panel tiene botón rojo de llamada, botón azul (izq.) y verde (der.) y altavoz para hablar.

6. Cadena: equipos → LCom (radial) → BoxCom (bus) → switch PoE → servidor.

7. El teléfono del desk va directo al switch PoE.

פנל קריאת אחות



Panel con voz y botones

Código	**ACE82182451**
Ubicación	Salón y cada dormitorio (en el dormitorio, con pera)
Altura	**1,20–1,30 m**
Cantidad	**80**


4



Teléfono del desk (Android)

Código	**Grandstream**
Ubicación	Desk de enfermería en PB · PoE directo al switch
Altura	**sobre el desk**
Cantidad	**1**


5

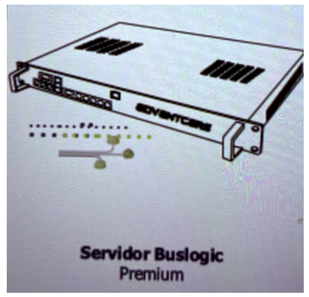

Servidor Buslogic Premium

Código	**Advantcare**
Ubicación	Gabinete principal de PB
Altura	**en gabinete**
Cantidad	**1**


6

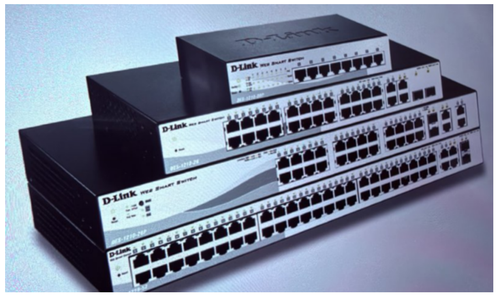

Switch PoE de 24 puertos

Código	**D-Link DES-1210-28P**
Ubicación	Gabinete de cada piso y de PB
Altura	**en gabinete**
Cantidad	**9**


7

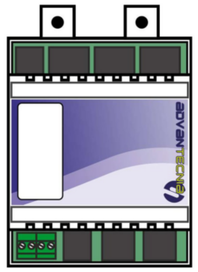

LCom – concentrador radial

Código	**ACE71610003**
Ubicación	Techo de cada departamento y baños públicos
Altura	**2,55 m**
Cantidad	**41**

8

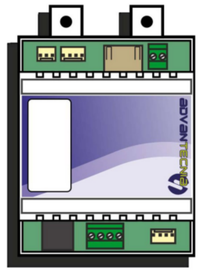

BoxCom – concentrador en bus

Código	**ACE70810000**
Ubicación	Techo junto al gabinete: une varios deptos.
Altura	**2,55 m**
Cantidad	**17**

9

TELÉFONO DEL DESK – QUÉ COLOR SE VE

Alarma (tirador / SOS)	**Rojo**
Botón verde 1 vez: presencia	**Verde**
Botón verde otra vez: cancela llamada o alarma	Se borra
Botón azul: llamada de médico (blue call)	**Azul**
Llamada de voz	**Amarillo / naranja**

MIGDALEI YAM A TIJON · VIVIENDA TUTELADA

Llamada de enfermería – PB + 8 pisos · 32 departamentos

Sistema: ACE BG · Advantecnia Elaboró: Telab International


EQUIPOS DEL SISTEMA

System devices

ESCALA · SCALE	FECHA · DATE	REV	LÁMINA
S/E	15/10/2026	B	02

Base: plano del arquitecto L5 (Massad Oz / Triplet) · cotas en metros

Formato A1 · Rev. B – sobre plano real

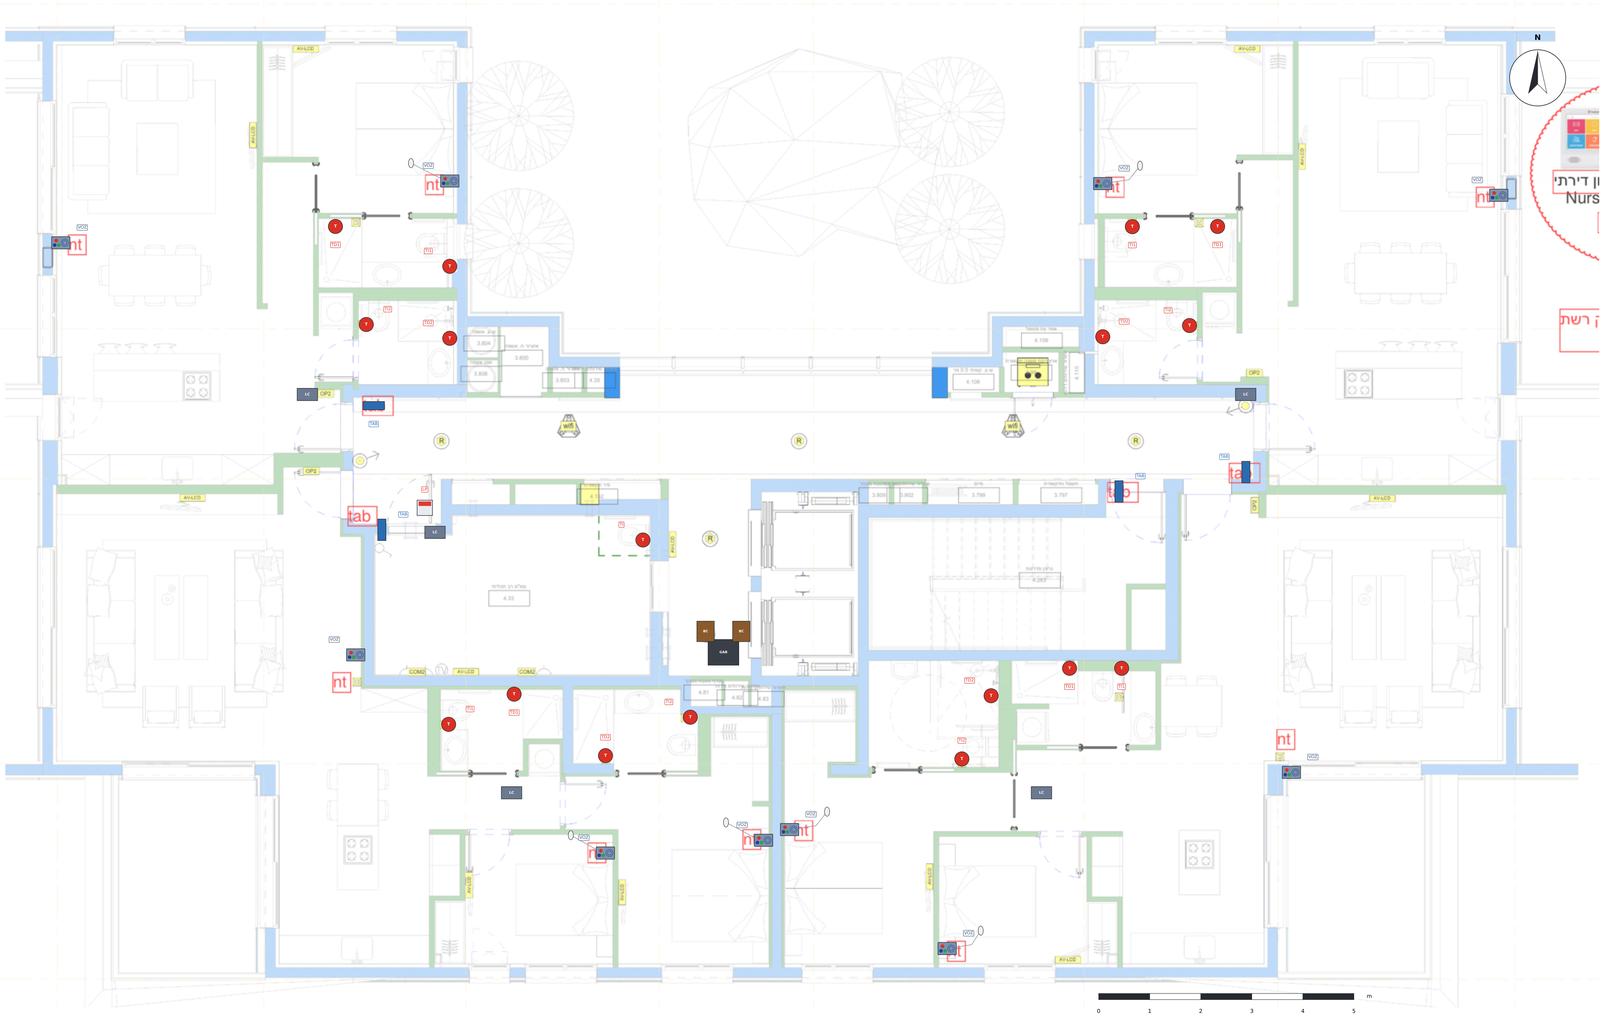

NOTAS · NOTES

1. Fondo: plano IT L2 del cliente con sus marcas en rojo: «nt» = panel con voz y «tab» = tablet de la puerta.

2. Encima, en color: los equipos de esta propuesta. Cada panel y cada tablet está donde el cliente lo marcó.

3. Los cuadrados amarillos ⊠ de los baños del plano L2 son los tiradores (inodoro y ducha).

4. Las 4 tablets quedan en el lobby, junto a la puerta de cada departamento, como en las marcas «tab».

5. El plano L2 y el L5 (base de esta propuesta) tienen la misma estructura; L5 es el piso tipo de los pisos 1 a 8.

EQUIPOS · DEVICES · דגם

- **TAB** · Tablet de la puerta (iPad / Android) – llamada y voz, h 1,40 m
  Door tablet – call and voice · הברה ושיחה – טאבלט ליד הדלת
- **VOZ** · Panel con voz y botones ACE82182451 – salón y dormitorios, h 1,20–1,30 m
  Voice panel with buttons – living room and bedrooms · לוח קולי עם כפתורים – סלון וחדרי שינה
- Pera de llamada junto a la cama (en los dormitorios)
  Call pear next to the bed (bedrooms) · כפתור זימון ליד המיטה – בחדרי השינה
- **TI / TD** · Tirador de baño ACE40320303W – inodoro y ducha, h 1,85 m
  Pull-cord – toilet and shower, h 1.85 m · חבל משיכה בשירותים וליד המקלחת – לגובה 1.85 מ'
- **LP** · Luz de pasillo ACE41020309 – sobre la puerta de cada baño público
  Corridor light – above each public toilet door · גוף תאורה במסדרון – מעל דלת כל שירותים ציבוריים

שירותים קריאת אחות



Tirador de baño

טבלט אנדרואיד קריאת אחות



Tablet en la puerta (iPad / Android)

מנורה קריאת אחות



Luz de pasillo

פנל קריאת אחות



Panel con voz y botones

MIGDALEI YAM A TIJON · VIVIENDA TUTELADA

Llamada de enfermería – PB + 8 pisos · 32 departamentos

Sistema: ACE BG · Advantecnia Elaboró: Telab International


MARCAS DEL CLIENTE (PLANO L2) Y PROPUESTA

Client marks (plan L2) and proposal

ESCALA · SCALE	FECHA · DATE	REV	LÁMINA
1:60	15/10/2026	B	03

Base: plano del arquitecto L5 (Massad Oz / Triplet) · cotas en metros

Formato A1 · Rev. B – sobre plano real

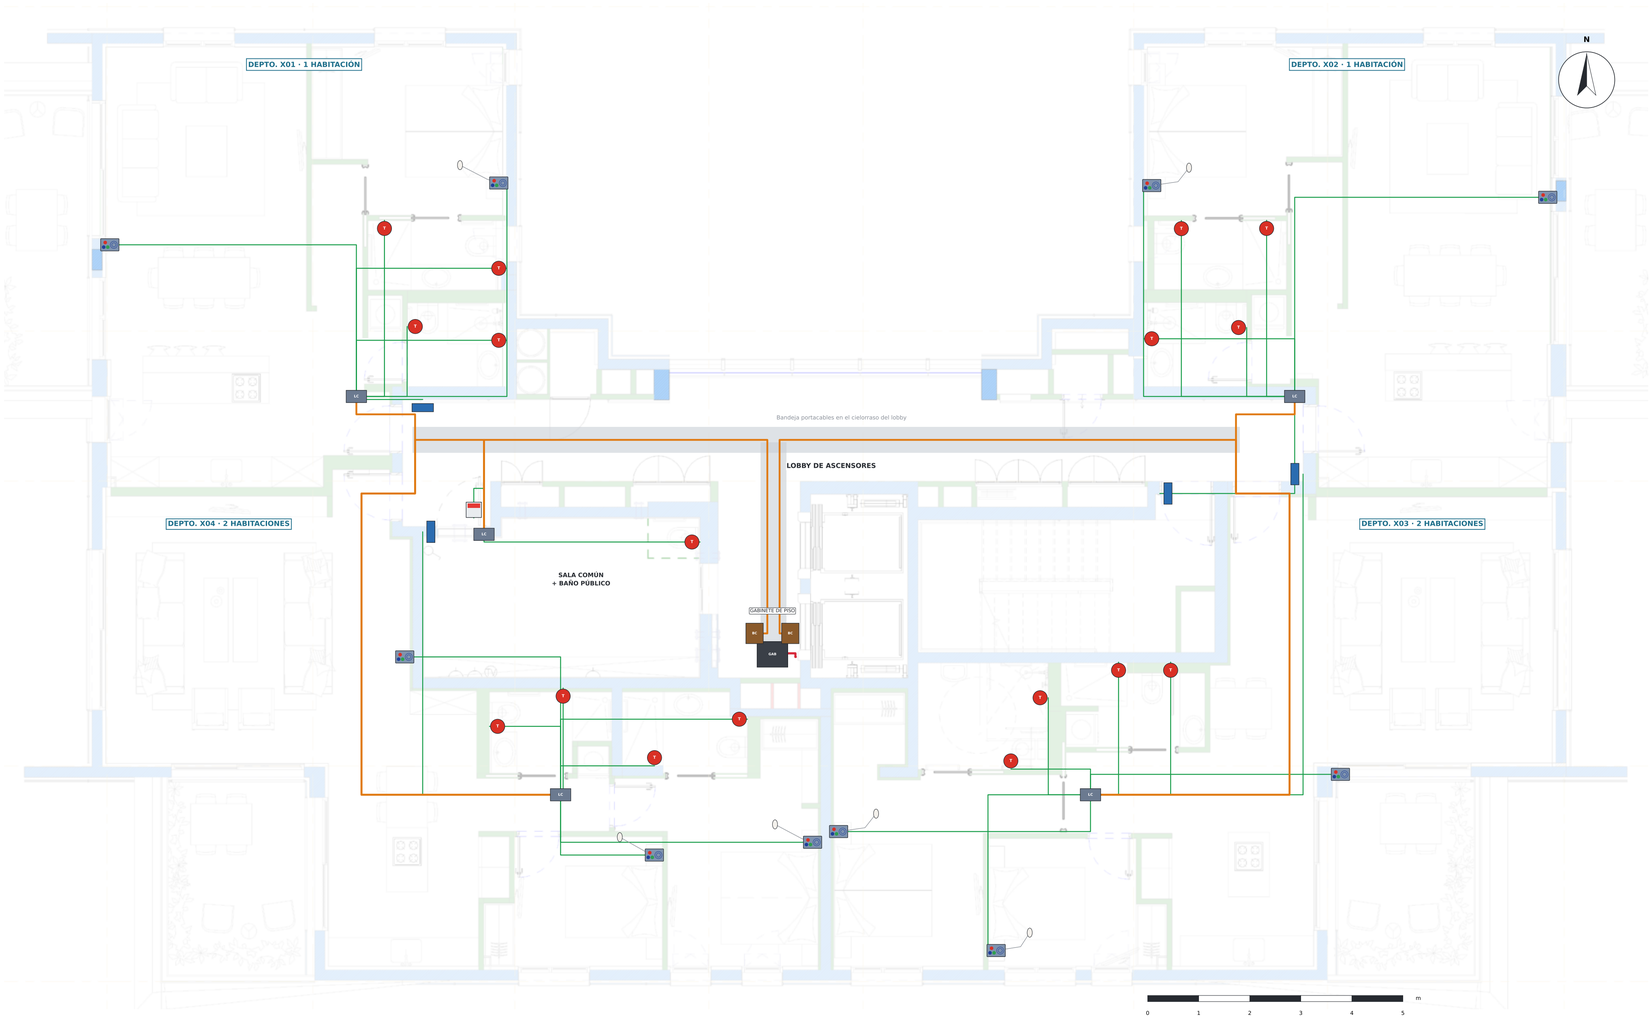

CABLEADO · WIRING · סוגיות

Cat6 radial: cada equipo → LCom de su departamento
Cat6 radial: each device → apartment LCom · Cat6 רדיאלי: כל התקן ← LCom של הדירה

Cat6 / Cat7 cadena: LCom → LCom → BoxCom del techo
Cat6 / Cat7 chain: LCom → LCom → BoxCom · Cat6 / Cat7 שרשרת: LCom ← LCom ← BoxCom

Cat6A / Cat7 red: BoxCom → switch PoE → montante → servidor PB
Cat6A / Cat7 network: BoxCom → switch → riser → GF server · Cat6A / Cat7 רשת: BoxCom ← מתג ← עמוד ← שרת

LONGITUDES DEL PISO TIPO (sin reserva)

Cat6 radial dentro de los departamentos	**183 m**
Cat6 / Cat7 cadena LCom → BoxCom	**80 m**
Cat6A / Cat7 gabinete y montante	**7 m**

NOTAS · NOTES

1. Cada equipo va radial (Cat6) al LCom de su departamento, en el cielorraso del hall.
2. Los LCom se encadenan por la bandeja del lobby hasta los BoxCom del techo, junto al gabinete: x01 → x04 → sala común → BoxCom 1 · x02 → x03 → BoxCom 2.
3. Los BoxCom bajan al switch PoE del gabinete; el switch sube por el montante Cat6A / Cat7 hasta el servidor de PB.
4. Todo es PoE: no hace falta 230 V en los equipos de los departamentos.

NOTAS · NOTES

1. Base: plano de arquitectura L5 (piso tipo) – los 8 pisos son iguales: 4 departamentos por piso, 32 en total.
2. Departamentos x01 y x02: 1 habitación, salón con cocina y 2 baños. Departamentos x03 y x04: 2 habitaciones y 2 baños.
3. Tablet en la puerta de cada departamento (iPad / Android) para llamar y hablar con enfermería.
4. Panel con voz y botones (ACE82182451) en el salón y en cada dormitorio; en el dormitorio, con pera junto a la cama.
5. Tiradores de baño (ACE40320303W) en el inodoro y en la ducha de todos los baños, a 1,85 m.
6. Baño público por piso en la sala común: tirador + luz de pasillo sobre la puerta. Con los 2 de PB suman 10 baños públicos.
7. Gabinete de piso junto a los ascensores con el switch PoE D-Link DES-1210-28P; los 2 BoxCom van en el techo, al lado.
8. Ubicaciones según las marcas del cliente en el plano L2 (nt = panel con voz, tab = tablet): ver lámina 03.

MIGDALEI YAM A TIJON · VIVIENDA TUTELADA

Llamada de enfermería – PB + 8 pisos · 32 departamentos

Sistema: ACE BG · Advantecnia Elaboró: Telab International


PISO TIPO P1–P8 · CABLEADO

Typical floor F1–F8 · wiring

ESCALA · SCALE	FECHA · DATE	REV	LÁMINA
1:60	**15/10/2026**	**B**	**04**

Base: plano del arquitecto L5 (Massad Oz / Triplet) · cotas en metros

Formato A1 · Rev. B – sobre plano real

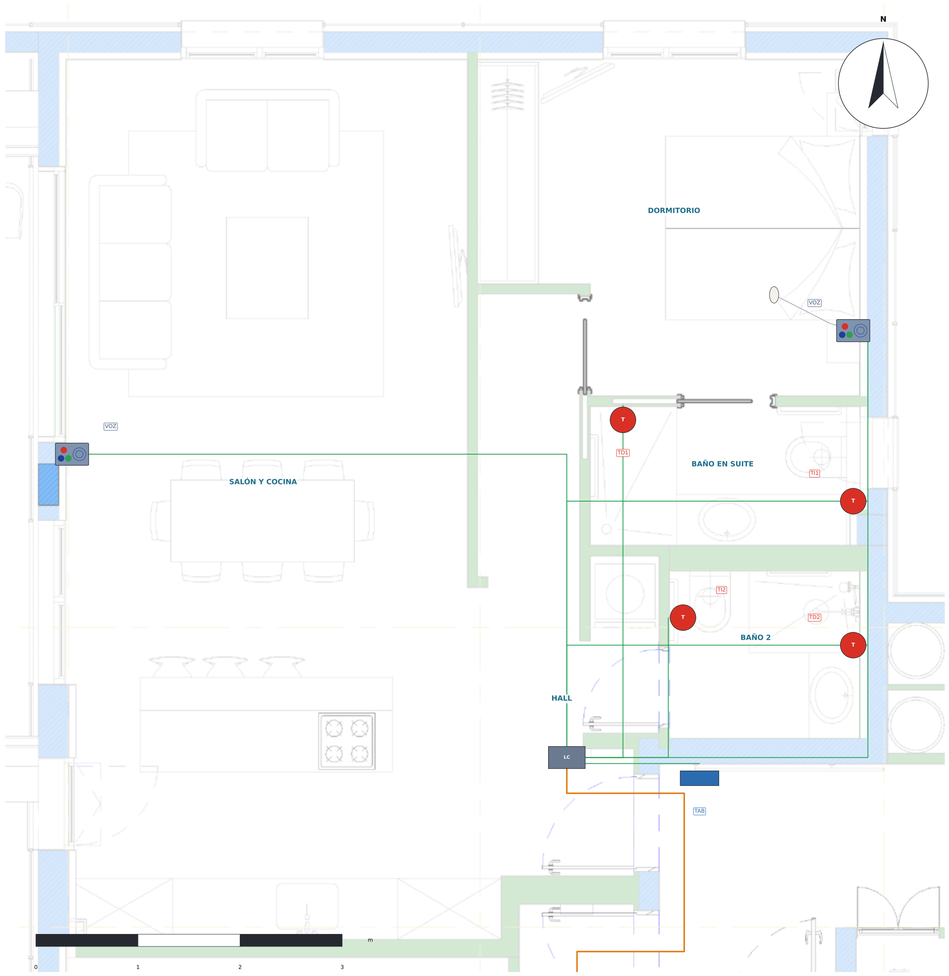

EQUIPOS DEL DEPARTAMENTO

ID	Equipo	Local	Altura
TAB	Tablet de la puerta	Hall	1,40 m
VOZ-S	Panel voz y botones	Salón y cocina	1,30 m
VOZ-D	Panel voz y botones + pera	Dormitorio	1,20 m
TI1	Tirador de baño	Baño en suite	1,85 m
TD1	Tirador de baño	Baño en suite	1,85 m
TI2	Tirador de baño	Baño 2	1,85 m
TD2	Tirador de baño	Baño 2	1,85 m
LCOM	LCom ACE71610003	Hall	2,55 m

SÍMBOLOS · SYMBOLS · סימנים

TAB · Tablet de la puerta (iPad / Android) – llamada y voz, h 1,40 m
Door tablet – call and voice · · הצגת האריח – התקשר וקלאנט

VOZ · Panel con voz y botones ACE82182451 – salón y dormitorios, h 1,20–1,30 m
Voice panel with buttons – living room and bedrooms · · הגיש ירדוח עלם – קיצוחל כץ ילקן לעד

Pera de llamada junto a la cama (en los dormitorios)
Call pear next to the bed (bedrooms) · · המתנה ליד האריח סמוא

TI / TD · Tirador de baño ACE40320303W – inodoro y ducha, h 1,85 m
Pull-cord – toilet and shower, h 1.85 m · · ח' 1.85 ,הבוא ,מחלקצ החלוא – לקח תוישא

LP · Luz de pasillo ACE41020309 – sobre la puerta de cada baño público
Corridor light – above each public toilet door · · סיורבמ סחיטיש לק תלד לעמ – נורדטמ תיחפה

LC · LCom ACE71610003 – concentrador del departamento (cielorraso)
LCom – apartment hub (ceiling) · · LCom – (טרקעל) בויחה בוכמ

BC · BoxCom ACE70810000 – concentrador en bus de varios deptos. (techo)
BoxCom – bus hub for several apartments (ceiling) · · BoxCom – (טרקעל) תורי המכלל טשנ ובוכמ

NOTAS · NOTES

1. El departamento x02 es el espejo del x01 (misma dotación).
2. Tablet en el lobby, junto a la puerta de entrada (marca «tab» del cliente).
3. Panel con voz en el salón y en el dormitorio (con pera junto a la cama).
4. 2 baños: tirador en el inodoro y en la ducha de cada uno (4 tiradores).
5. Todo va radial en Cat6 al LCom del hall.

פנל קריאת אחות



Panel con voz y botones

מנורה קריאת אחות



Luz de pasillo

טבלט אנדרואיד קריאת אחות



Tablet en la puerta (iPad / Android)

שירותים קריאת אחות



Tirador de baño

MIGDALEI YAM A TIJON · VIVIENDA TUTELADA

Llamada de enfermería – PB + 8 pisos · 32 departamentos

Sistema: ACE BG · Advantecnia Elaboró: Telab International

DEPTO. 1 HABITACIÓN (x01 / x02)

1-bedroom apartment (x01 / x02)

ESCALA · SCALE	FECHA · DATE	REV	LÁMINA
1:30	15/10/2026	B	05

Base: plano del arquitecto L5 (Massad Oz / Triplet) · cotas en metros

Formato A1 · Rev. B – sobre plano real



EQUIPOS DEL DEPARTAMENTO

ID	Equipo	Local	Altura
TAB	Tablet de la puerta	Hall	1,40 m
VOZ-S	Panel voz y botones	Salón	1,30 m
VOZ-D1	Panel voz y botones + pera	Dormitorio 1	1,20 m
VOZ-D2	Panel voz y botones + pera	Dormitorio 2	1,20 m
TI1	Tirador de baño	Baño 1	1,85 m
TD1	Tirador de baño	Baño 1	1,85 m
TI2	Tirador de baño	Baño 2	1,85 m
TD2	Tirador de baño	Baño 2	1,85 m
LCOM	LCom ACE71610003	Hall	2,55 m

SÍMBOLOS · SYMBOLS · סימנים

TAB · Tablet de la puerta (iPad / Android) – llamada y voz, h 1,40 m
Door tablet – call and voice · טאבלט בפתח – שיחה וקול · גובה 1.40 מ׳

VOZ · Panel con voz y botones ACE82182451 – salón y dormitorios, h 1,20–1,30 m
Voice panel with buttons – living room and bedrooms · לוח קול וכפתורים – סלון וחדרי שינה · גובה 1.20–1.30 מ׳

Pera de llamada junto a la cama (en los dormitorios)
Call pear next to the bed (bedrooms) · כפתור חיבור ליד מיטה · בחדרי שינה

TI / TD · Tirador de baño ACE40320303W – inodoro y ducha, h 1,85 m
Pull-cord – toilet and shower, h 1.85 m · חבל משיכה – שירותים ומקלחת · גובה 1.85 מ׳

LP · Luz de pasillo ACE41020309 – sobre la puerta de cada baño público
Corridor light – above each public toilet door · מנורת מסדרון – מעל דלת כל שירותים ציבוריים

LC · LCom ACE71610003 – concentrador del departamento (cielorraso)
LCom – apartment hub (ceiling) · LCom – מרכז דירתי (בתקרה) · LCom – מרכז דירתי (בתקרה)

BC · BoxCom ACE70810000 – concentrador en bus de varios deptos. (techo)
BoxCom – bus hub for several apartments (ceiling) · BoxCom – מרכז אזורי למספר דירות (בתקרה) · BoxCom – מרכז אזורי למספר דירות (בתקרה)

NOTAS · NOTES

1. El departamento x03 tiene la misma dotación (baños con otra distribución).
2. Tablet en el lobby, junto a la puerta de entrada (marca «tab» del cliente).
3. Panel con voz en el salón y en los 2 dormitorios (con pera junto a la cama).
4. 2 baños: tirador en el inodoro y en la ducha de cada uno (4 tiradores).
5. Todo va radial en Cat6 al LCom del pasillo de los dormitorios.

שירותים קריאת אחות



Tirador de baño

טבלט אנדרואיד קריאת אחות



Tablet en la puerta (iPad / Android)

מנורה קריאת אחות



Luz de pasillo

פנל קריאת אחות



Panel con voz y botones

MIGDALEI YAM A TIJON · VIVIENDA TUTELADA

Llamada de enfermería – PB + 8 pisos · 32 departamentos

Sistema: ACE BG · Advantecnia Elaboró: Telab International

DEPTO. 2 HABITACIONES (x04 / x03)

2-bedroom apartment (x04 / x03)


ESCALA · SCALE	FECHA · DATE	REV	LÁMINA
1:35	15/10/2026	B	06

Base: plano del arquitecto L5 (Massad Oz / Triplet) · cotas en metros

Formato A1 · Rev. B – sobre plano real



DETALLE · RECEPCIÓN Y DESK DE ENFERMERÍA (1:40)

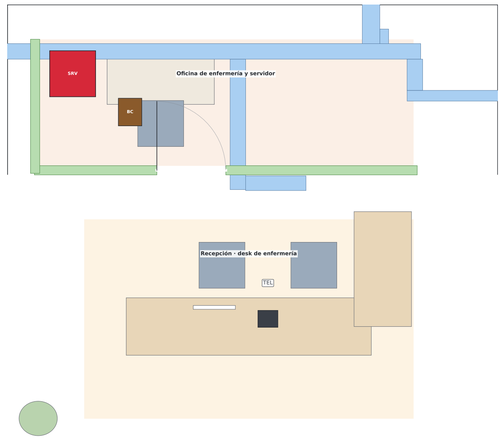

NOTAS · NOTES

1. Desk de enfermería en la recepción, frente a la entrada y a los ascensores.
2. Sobre el desk: teléfono Grandstream Android, conectado directo al switch PoE. Cada llamada se ve con su color.
3. Detrás del desk: oficina con el gabinete principal: servidor Buslogic Premium y switch PoE D-Link. BoxCom de PB en el techo.
4. 2 baños públicos en PB: tirador junto al inodoro y luz de pasillo sobre cada puerta.
5. El montante de los 8 pisos baja por el núcleo hasta el gabinete principal.
6. Distribución de PB propuesta: se ajusta cuando llegue el plano del arquitecto.

SÍMBOLOS · SYMBOLS · סימלים

- **T** — TI / TD · Tirador de baño ACE40320303W – inodoro y ducha, h 1,85 m
  Pull-cord – toilet and shower, h 1.85 m · חבל הפעלה: שירותים ומקלחת, גובה 1.85 מ'
- **LP** — LP · Luz de pasillo ACE41020309 – sobre la puerta de cada baño público
  Corridor light – above each public toilet door · מיקרוגל מיקרוגל מיקרוגל מיקרוגל – מעל כל דלת של שירותים ציבוריים
- **LC** — LC · LCom ACE71610003 – concentrador del departamento (cielorraso)
  LCom – apartment hub (ceiling) · LCom – רכזת דירה (תקרה)
- **TEL** — TEL · Teléfono Grandstream Android – PoE directo al switch
  Grandstream Android phone – PoE straight to the switch · טלפון Grandstream אנדרואיד – ישירות מהשקע PoE
- **SRV** — SRV · Gabinete PB: servidor Buslogic Premium + switch PoE D-Link
  GF rack: Buslogic Premium server + D-Link PoE switch · ארון קומת קרקע: שרת Buslogic Premium + מתג PoE D-Link
- **BC** — BC · BoxCom ACE70810000 – concentrador en bus de varios deptos. (techo)
  BoxCom – bus hub for several apartments (ceiling) · BoxCom – רכזת אוטובוס עבור מספר דירות (תקרה)

TELÉFONO DEL DESK – QUÉ COLOR SE VE

Alarma (tirador / SOS)	**Rojo**
Botón verde 1 vez: presencia	**Verde**
Botón verde otra vez: cancela llamada o alarma	Se borra
Botón azul: llamada de médico (blue call)	**Azul**
Llamada de voz	**Amarillo / naranja**

MIGDALEI YAM A TIJON · VIVIENDA TUTELADA

Llamada de enfermería – PB + 8 pisos · 32 departamentos

Sistema: ACE BG · Advantecnia Elaboró: Telab International

PLANTA BAJA · LOBBY Y DESK DE ENFERMERÍA

Ground floor · lobby and nurse desk

ESCALA · SCALE	FECHA · DATE	REV	LÁMINA
1:60	15/10/2026	B	07


Base: plano del arquitecto L5 (Massad Oz / Triplet) · cotas en metros

Formato A1 · Rev. B – sobre plano real

A · EDIFICIO PB + 8 PISOS



B · TOPOLOGÍA DE UN DEPARTAMENTO

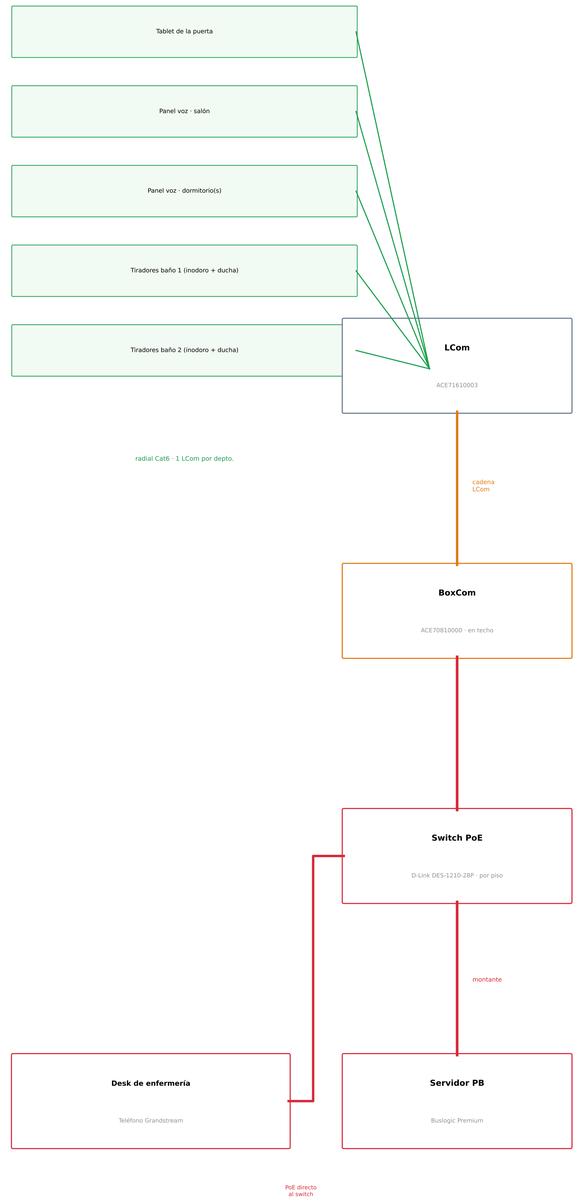

NOTAS · NOTES

1. 8 pisos iguales con 4 departamentos (2 de 1 habitación y 2 de 2).
2. En cada piso: 2 BoxCom en el techo y un gabinete con el switch PoE.
3. Cadena 1: x01 → x04 → baño público. Cadena 2: x02 → x03.
4. Los switches suben por el montante hasta el gabinete principal de PB.
5. El teléfono Grandstream del desk va directo al switch PoE y muestra cada llamada con su color.
6. Todo el sistema es PoE.
7. Cantidades de anteproyecto: validar con Advantecnia y en obra.

MIGDALEI YAM A TIJON · VIVIENDA TUTELADA

Llamada de enfermería – PB + 8 pisos · 32 departamentos

Sistema: ACE BG · Advantecnia Elaboró: Telab International

ESQUEMA VERTICAL Y TOPOLOGÍA

Riser diagram and topology

ESCALA · SCALE	FECHA · DATE	REV	LÁMINA
S/E	15/10/2026	B	08

Base: plano del arquitecto L5 (Massad Oz / Triplet) · cotas en metros

Formato A1 · Rev. B – sobre plano real

LISTA DE MATERIALES – EDIFICIO COMPLETO (PB + 8 pisos · 32 departamentos · 10 baños públicos)

Código	Descripción	Cant.	Observación
EN LOS DEPARTAMENTOS (32)			
TAB	Tablet de la puerta (iPad / Android) – llamada y voz	**32**	1 por departamento
VOZ	Panel de llamada con voz y botones – ACE82182451	**80**	salón + cada dormitorio
TI/TD	Tirador de baño – ACE40320303W (inodoro y ducha)	**128**	4 por departamento
LC	LCom – ACE71610003	**32**	1 por departamento
BAÑOS PÚBLICOS (10)			
T	Tirador de baño – ACE40320303W	**10**	8 pisos + 2 en PB
LP	Luz de pasillo – ACE41020309	**10**	sobre cada puerta
LC	LCom – ACE71610003	**9**	1 por piso + 1 en PB
GABINETES Y CENTRAL			
BC	BoxCom – ACE70810000 (en el techo)	**17**	2 por piso + 1 en PB
SW	Switch PoE 24 puertos – D-Link DES-1210-28P	**9**	1 por piso + PB
GAB	Gabinete mural 12U con patch panel (para el switch)	**8**	1 por piso
GAB-PB	Gabinete principal de piso con UPS	**1**	PB
SRV	Servidor Buslogic Premium (Advantcare) con software	**1**	PB
TEL	Teléfono Grandstream Android (PoE, colores por tipo de llamada)	**1**	desk de enfermería
CABLES (+ 15 % de reserva)			
—	Cat6 radial dentro de los departamentos (verde)	**1700 m**	183 m por piso
—	Cat6 / Cat7 cadena LCom → BoxCom (naranja)	**750 m**	80 m por piso
—	Cat6A / Cat7 gabinetes y montante (rojo)	**130 m**	incluye montante

NOTAS · NOTES

1. Cantidades calculadas del modelo (piso tipo × 8 + PB).

2. Longitudes de cable medidas sobre el recorrido dibujado, + 15 %.

3. Precios: según lista vigente de Advantecnia.

4. Validar en obra antes de comprar.

MIGDALEI YAM A TIJON · VIVIENDA TUTELADA

Llamada de enfermería – PB + 8 pisos · 32 departamentos

Sistema: ACE BG · Advantecnia Elaboró: Telab International


LISTA DE MATERIALES

Bill of materials


ESCALA · SCALE	FECHA · DATE	REV	LÁMINA
S/E	15/10/2026	B	09

Base: plano del arquitecto L5 (Massad Oz / Triplet) · cotas en metros

Formato A1 · Rev. B – sobre plano real

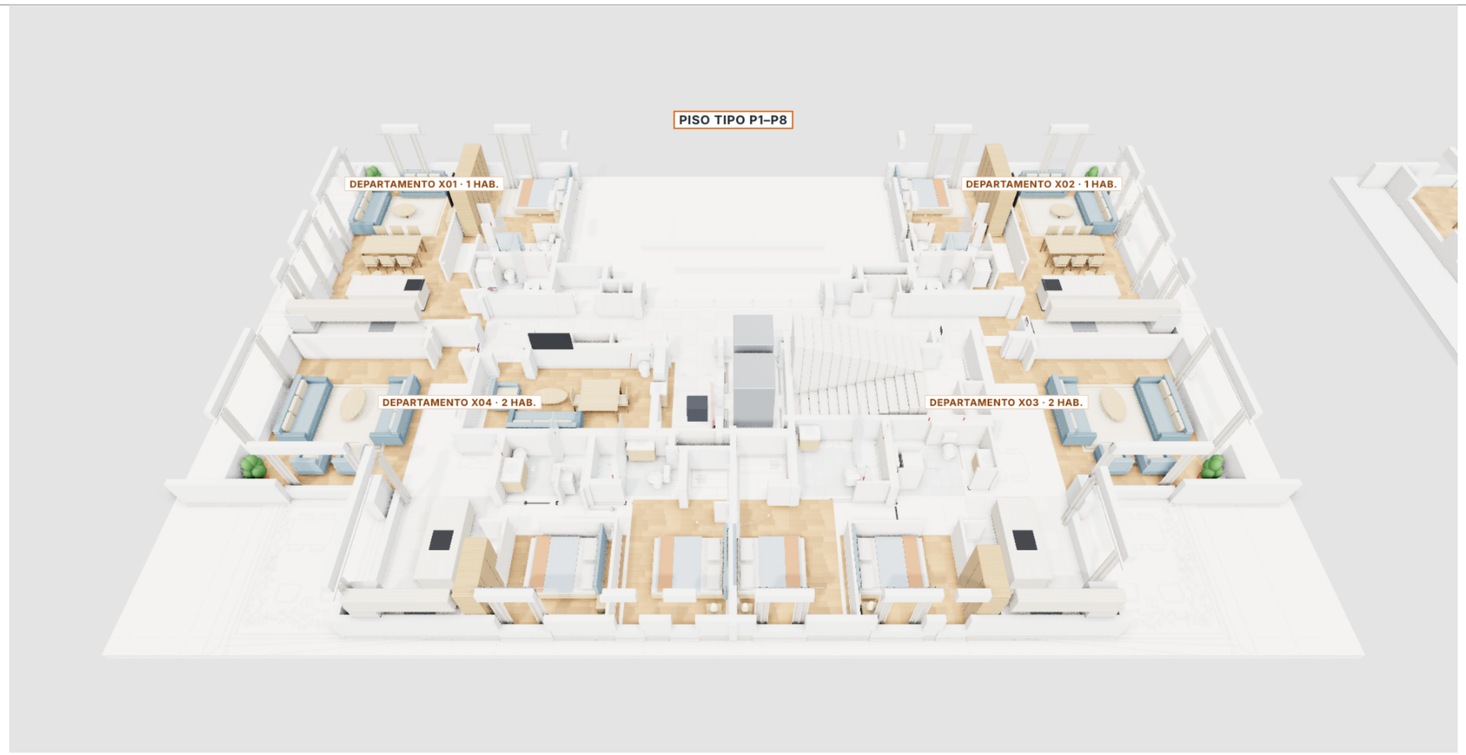

A · Piso tipo – 4 departamentos

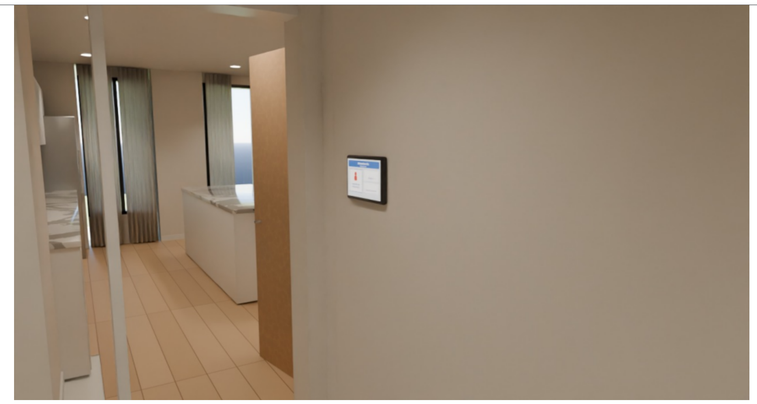

B · Tablet de la puerta




C · Dormitorio – panel con voz y pera



D · Baño – tiradores en inodoro y ducha



E · PB – desk de enfermería

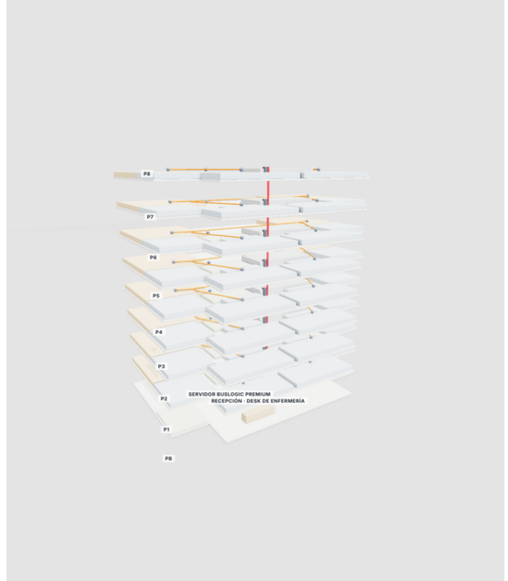

F · Edificio PB + 8 pisos

MIGDALEI YAM A TIJON · VIVIENDA TUTELADA

Llamada de enfermería – PB + 8 pisos · 32 departamentos

Sistema: ACE BG · Advantecnia Elaboró: Telab International


VISTAS 3D

3D views

ESCALA · SCALE	FECHA · DATE	REV	LÁMINA
S/E	15/10/2026	B	10

Base: plano del arquitecto LS (Massad Oz / Triplet) · cotas en metros

Formato A1 · Rev. B – sobre plano real

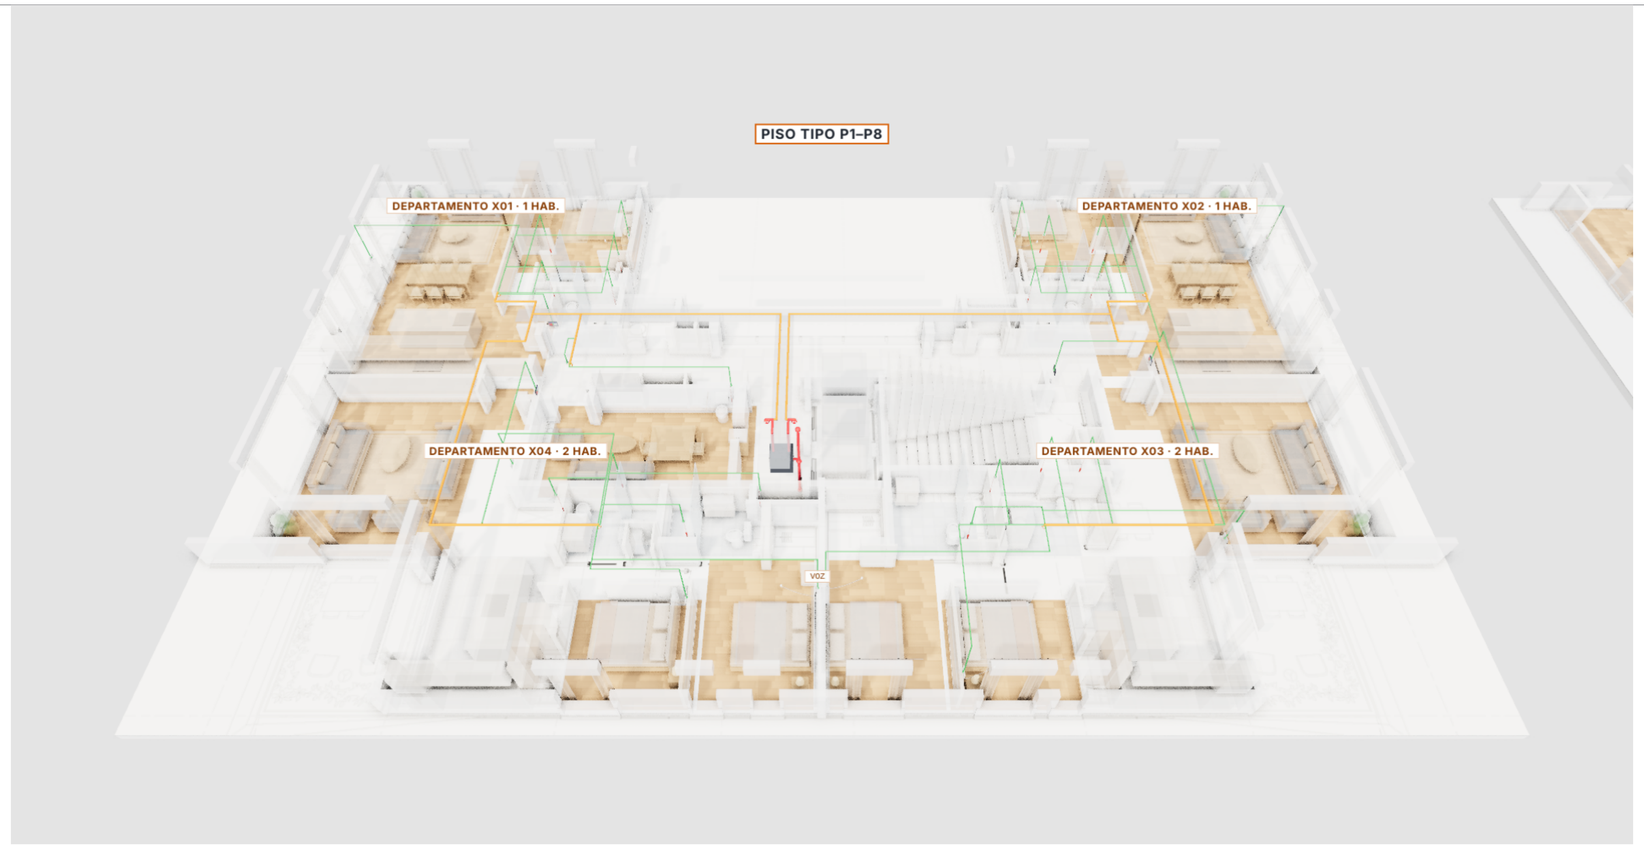

A · Piso tipo – cableado (verde radial · naranja cadena LCom · rojo red)



B · Planta baja – lobby y recepción



C · Salón – panel con voz y botones

COLORES · COLOURS · סיבבצ

Cat6 radial: cada equipo → LCom de su departamento
Cat6 radial: each device → apartment LCom · Cat6 רדיאלי: כל מכשיר → LCom דירה

Cat6 / Cat7 cadena: LCom → LCom → BoxCom del techo
Cat6 / Cat7 chain: LCom → LCom → BoxCom · Cat6 / Cat7 שרשרת: LCom ← LCom ← BoxCom

Cat6A / Cat7 red: BoxCom → switch PoE → rmontante → servidor PB
Cat6A / Cat7 network: BoxCom → switch → riser → GF server · Cat6A / Cat7 רשת: BoxCom ← מתג ← גזרה ← שרת

MIGDALEI YAM A TIJON · VIVIENDA TUTELADA

Llamada de enfermería – PB + 8 pisos · 32 departamentos

Sistema: ACE BG · Advantecnia Elaboró: Telab International

VISTAS 3D – CABLEADO

3D views – wiring

ESCALA · SCALE	FECHA · DATE	REV	LÁMINA
S/E	15/10/2026	B	11

Base: plano del arquitecto LS (Massad Oz / Triplet) · cotas en metros

Formato A1 · Rev. B – sobre plano real



A · Salón – panel de llamada con voz



B · Dormitorio – panel con voz y pera



C · Baño – tirador SOS



D · Baño 2 – tirador en inodoro y ducha



E · Sala común – baño público



F · Desk de enfermería – teléfono Grandstream

MIGDALEI YAM A TIJON · VIVIENDA TUTELADA

Llamada de enfermería – PB + 8 pisos · 32 departamentos

Sistema: ACE BG · Advantecnia Elaboró: Telab International

RENDERS FOTORREALISTAS

Photorealistic renders

ESCALA · SCALE	FECHA · DATE	REV	LÁMINA
S/E	15/10/2026	B	12

Base: plano del arquitecto LS (Massad Oz / Triplet) · cotas en metros

Formato A1 · Rev. B – sobre plano real