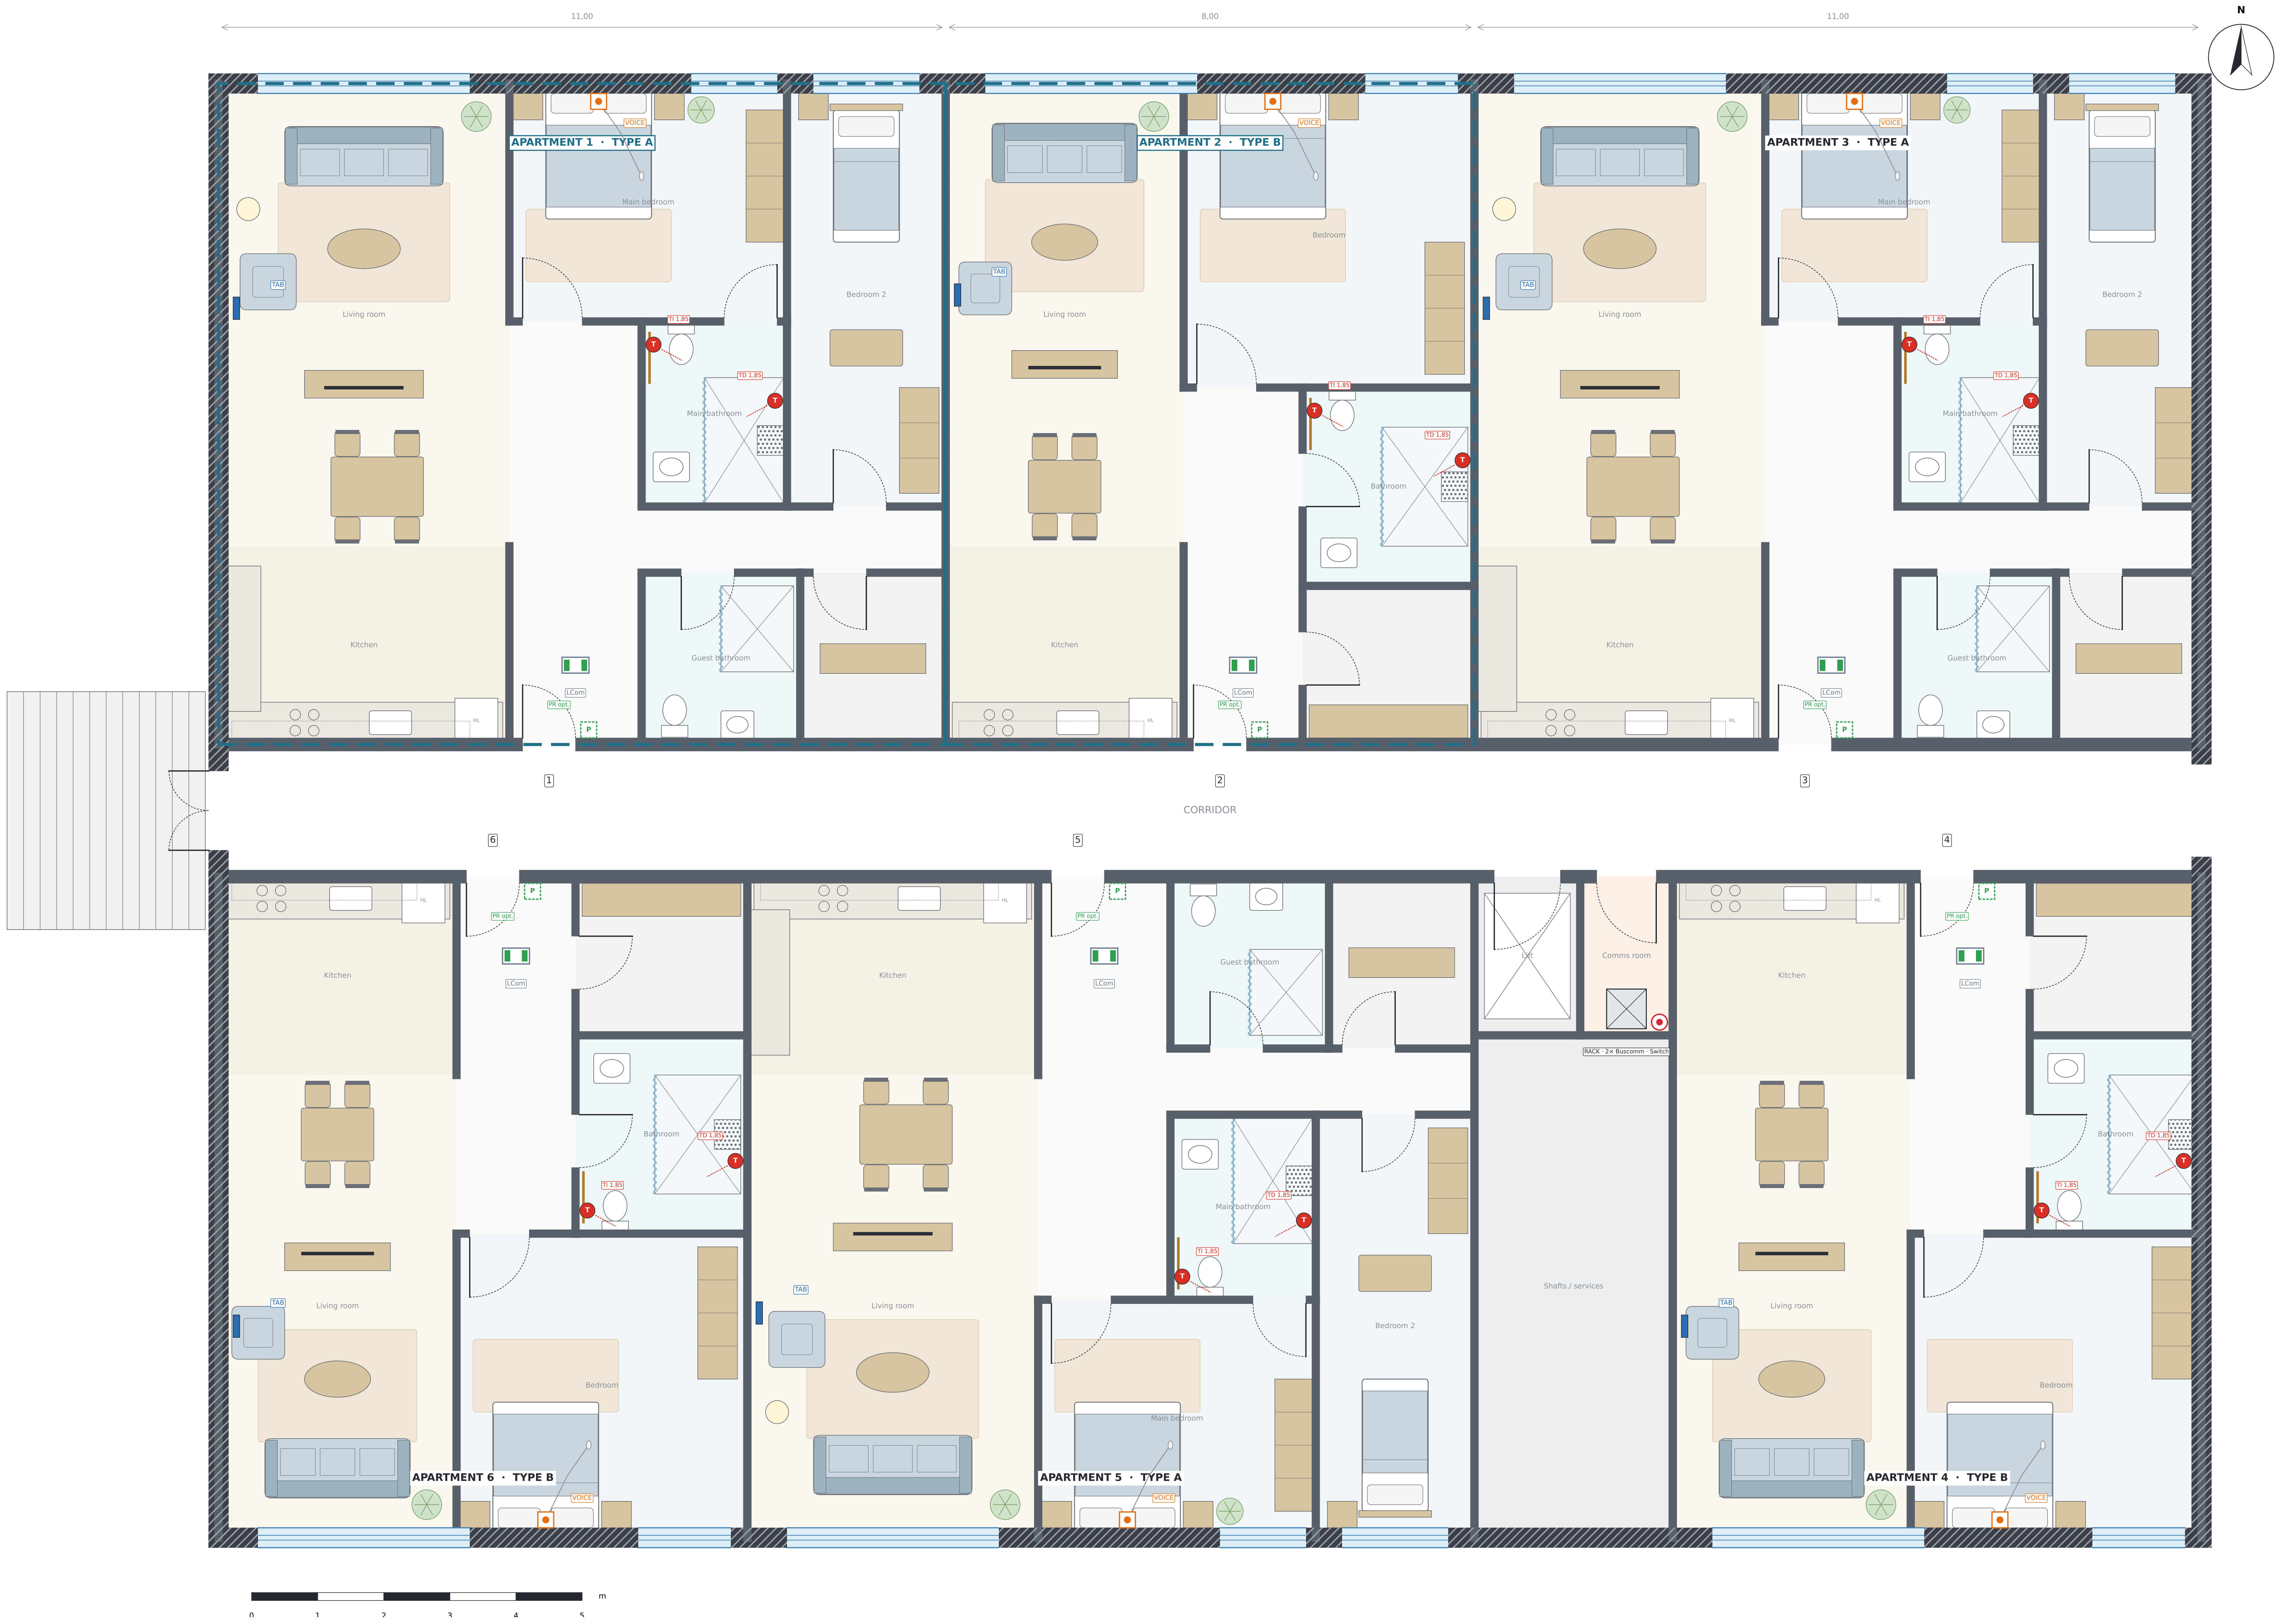

NOTES

1. Floor tipo: 6 departamentos intercalados (A-B-A al norte, B-A-B al sur). Se destacan el 1 (tipo A) y el 2 (tipo B).

2. Type A: living + open kitchen, main bedroom with en-suite (shower + toilet), bedroom 2, guest bathroom with shower, hall and storage.

3. Type B: living + open kitchen, one bedroom and one bathroom with shower.

4. Per apartment: Android tablet in the living room, voice call in the main bedroom and 2 pull-cords (toilet and shower) in the main bathroom.

5. Presence / cancel button next to the entrance door: optional.

6. Floor comms room next to the lift; stairs at the west end.

7. Residential furniture (not hospital).

SYMBOLS

▮	TAB · Android tablet in the living room – call and voice Android tablet in the living room – call and voice · טאבלט אנדרואיד בסלון – קריאה ודיבור
T	TI / TD · Toilet / shower pull-cord ACE40320303W (main bathroom, h 1.85 m) Toilet / shower pull-cord ACE40320303W (main bath, h 1.85 m) · משיכת חבל אסלה / מקלחת ACE40320303W
▮ ▮	LCom ACE71610003 · apartment hub (hall ceiling) LCom ACE71610003 · apartment hub (hall ceiling) · LCom ACE71610003 · מרכז דירה (תקרת המבואה)
●	VOICE · Voice nurse call ACE82182451 (main bedroom) Voice nurse call ACE82182451 (main bedroom) · קריאת אחות קולית ACE82182451 (חדר שינה ראשי)
P	PR · Presence / cancel junto a la puerta – OPCIONAL Presence / cancel next to the door – OPTIONAL · כפתור נוכחות / ביטול ליד הדלת – אופציונלי
RACK	Rack del piso: 2 Buscomm ACE70810000 + switch PoE ACEUCM6302 Floor rack: 2 Buscomm ACE70810000 + PoE switch ACEUCM6302 · ארון קומה: 2 Buscomm + מתג PoE

MIGDALEI YAM A TIJON · ASSISTED LIVING
Nurse call system – GF + 6 floors · 36 apartments
System: ACE BG · Advantecnia Prepared by: Telab International

TYPICAL FLOOR – EQUIPMENT

TYPICAL FLOOR – EQUIPMENT

SCALE	DATE	REV	SHEET
1:60	**12/10/2026**	**A**	**01**

Dimensions in metres
A1 format · Rev. A – Preliminary design

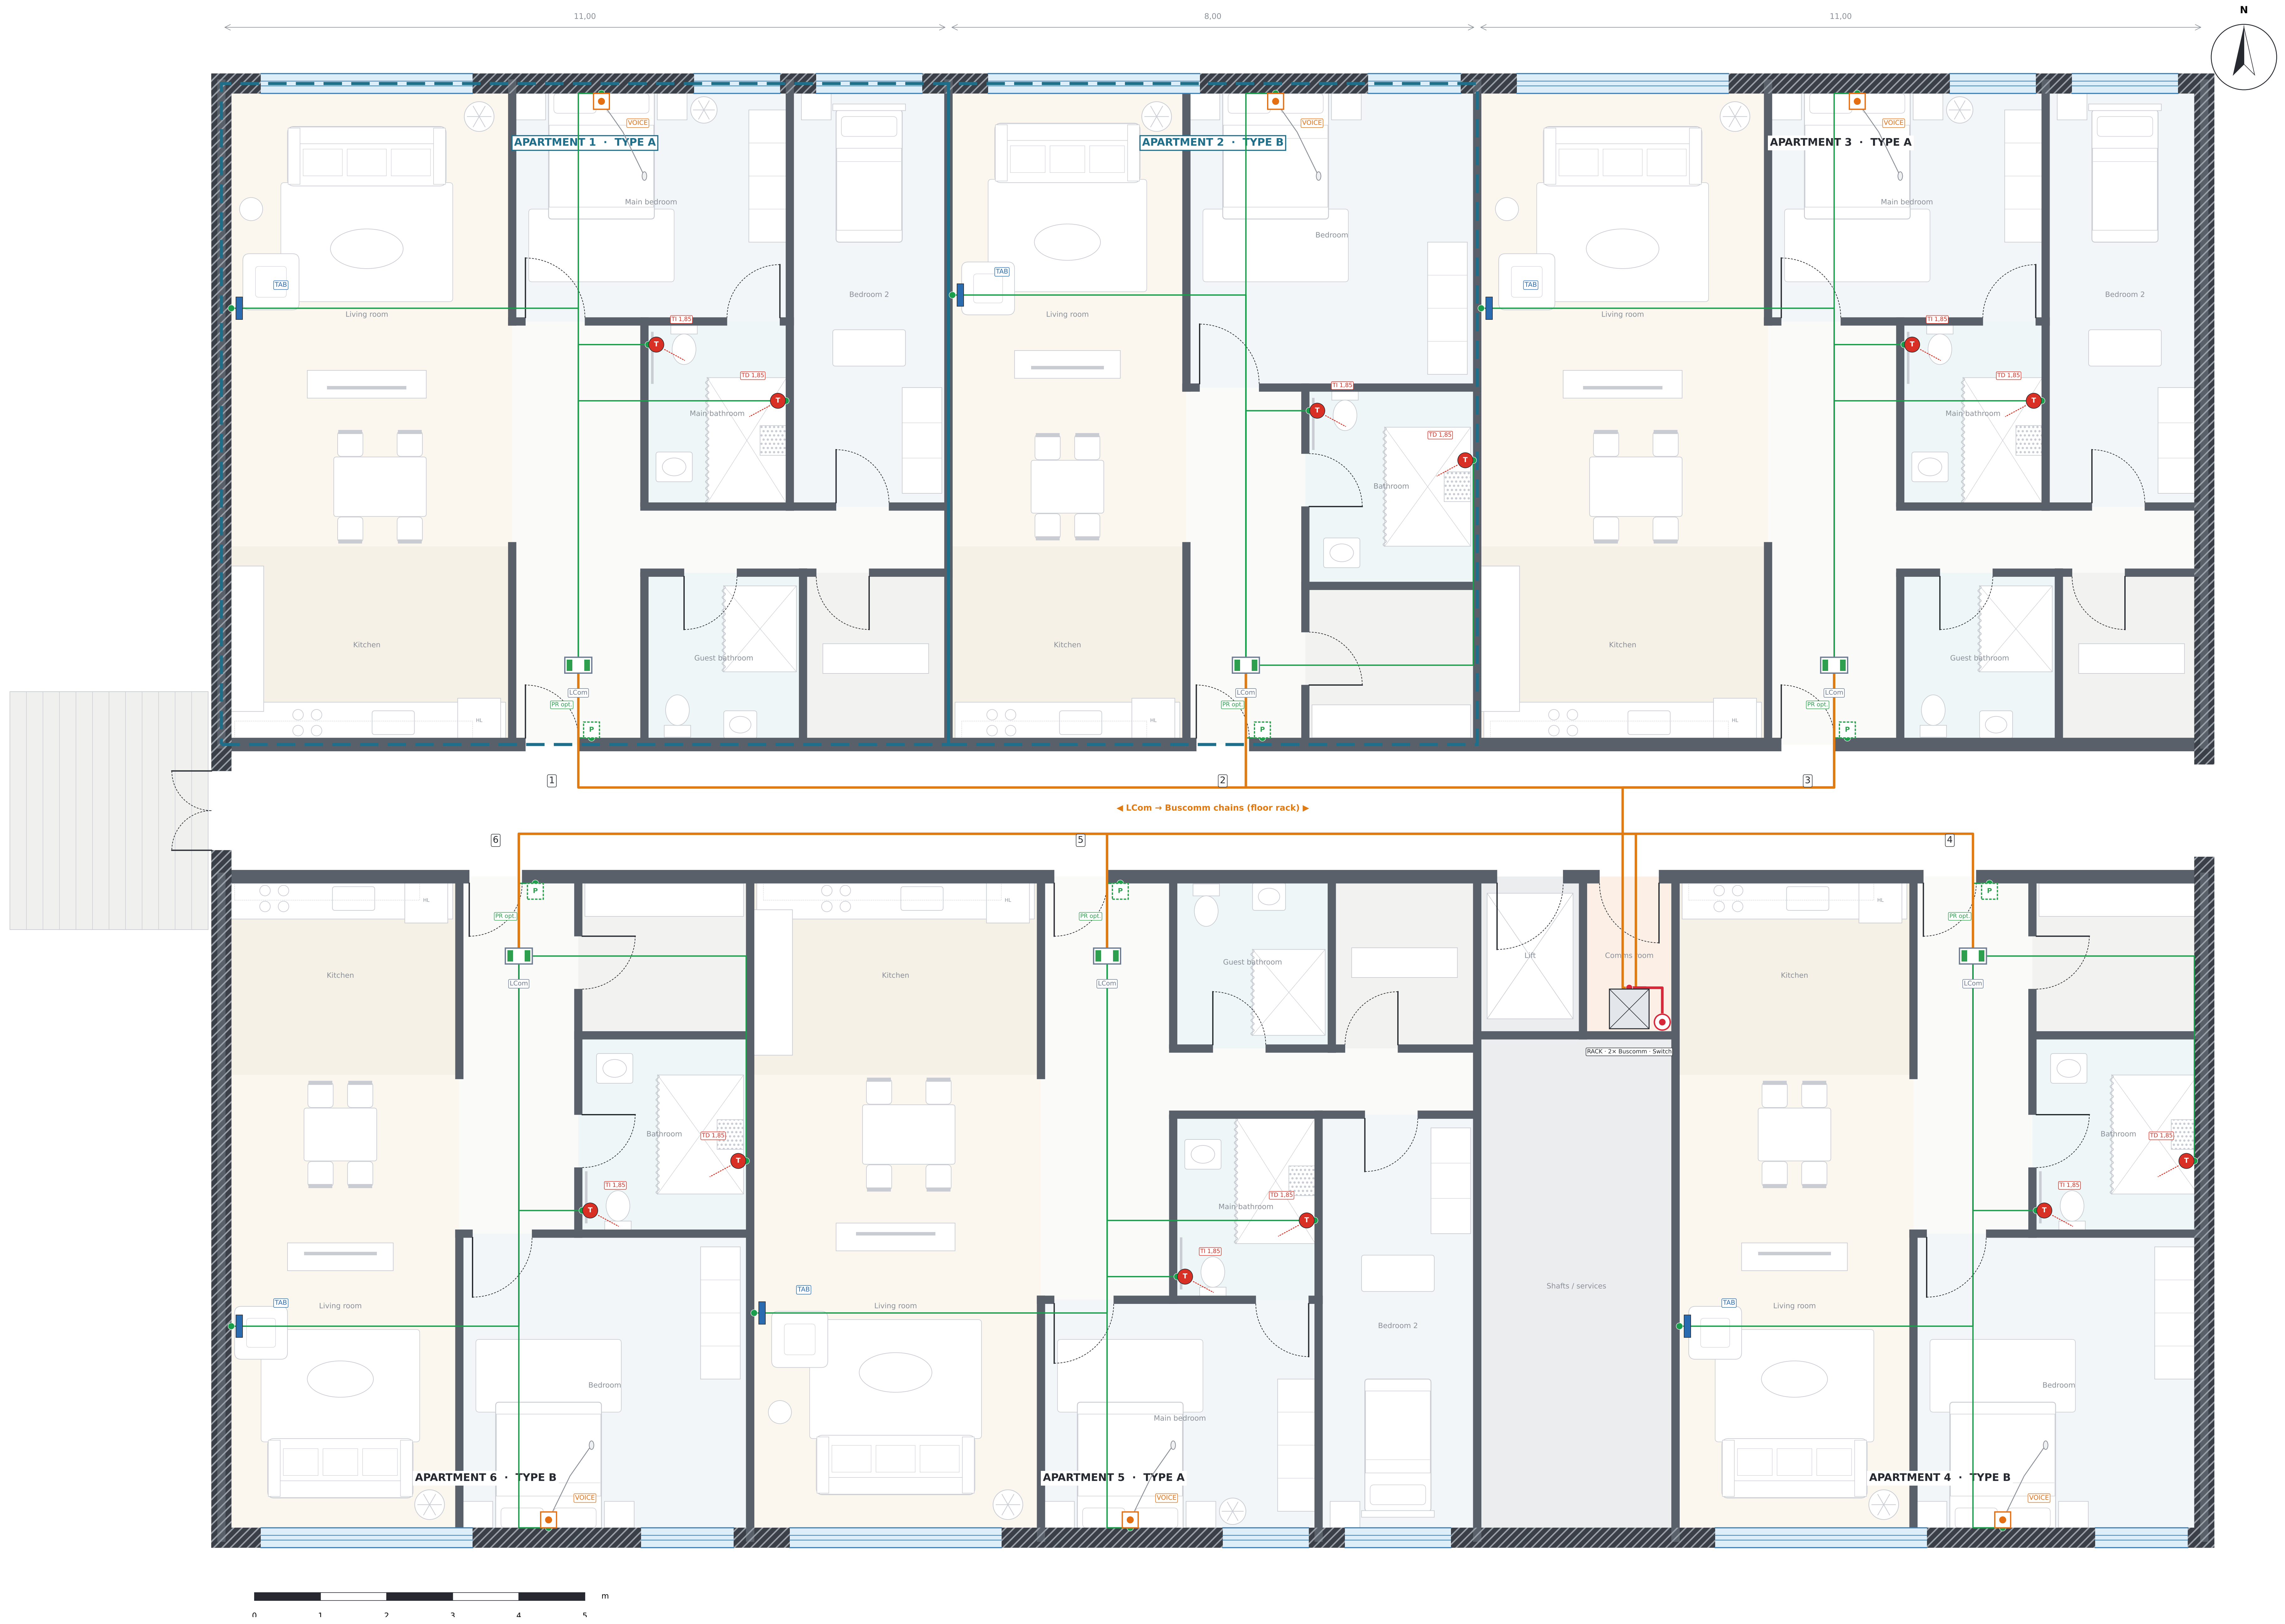

NOTES

1. Floor tipo: 6 departamentos intercalados (3 tipo A + 3 tipo B). Se destacan el 1 (A) y el 2 (B), detallados en las láminas 03 y 04.
2. Each apartment has one LCom in the hall ceiling: all its devices reach it radially with Cat6.
3. LComs are chained in threes to one Buscomm: north 1-2-3 → Buscomm 1, south 4-5-6 → Buscomm 2.
4. The 2 Buscomm and the PoE switch are in the rack of the floor comms room, next to the lift.
5. The switches of the 6 floors are chained up the riser to the ground-floor server. Vertical diagram on sheet 05.
6. The whole system is PoE: no power circuits needed in the apartments.
7. No corridor light. The call reaches the nurse desk at reception (GF) as voice / alarm.

WIRING – ALL Cat6 / Cat7 AND PoE (no mains power for the system)

🟩 Cat6 radial: each apartment device → its LCom
Cat6 radial: each device → its LCom · Cat6 רדיאלי: כל התקן ← LCom

🟥 Cat6A / Cat7 network: Buscomm → floor switch → riser → server (GF)
Cat6A / Cat7 network: Buscomm → floor switch → riser → server · Cat6A / Cat7 רשת: Buscomm ← מתג ← עמוד ← שרת

🟧 Cat6 / Cat7 chain: LCom → LCom → LCom → Buscomm (3 per Buscomm)
Cat6 / Cat7 chain: LCom → LCom → LCom → Buscomm · Cat6 / Cat7 שרשרת: LCom ← LCom ← Buscomm

- - - Cat6 to the optional presence / cancel button
Cat6 to optional presence / cancel button · Cat6 ללחצן נוכחות אופציונלי

SYMBOLS

▮ TAB · Android tablet in the living room – call and voice
Android tablet in the living room – call and voice · טאבלט אנדרואיד בסלון – קריאה ודיבור

T TI / TD · Toilet / shower pull-cord ACE40320303W (main bathroom, h 1.85 m)
Toilet / shower pull-cord ACE40320303W (main bath, h 1.85 m) · משיכת חבל אסלה / מקלחת ACE40320303W

▯ LCom ACE71610003 · apartment hub (hall ceiling)
LCom ACE71610003 · apartment hub (hall ceiling) · LCom ACE71610003 · מרכז דירה (תקרת המבואה)

● VOICE · Voice nurse call ACE82182451 (main bedroom)
Voice nurse call ACE82182451 (main bedroom) · קריאת אחות קולית ACE82182451 (חדר שינה ראשי)

P PR · Presence / cancel junto a la puerta – OPCIONAL
Presence / cancel next to the door – OPTIONAL · נוכחות / ביטול ליד הדלת – אופציונלי

RACK Rack del piso: 2 Buscomm ACE70810000 + switch PoE ACEUCM6302
Floor rack: 2 Buscomm ACE70810000 + PoE switch ACEUCM6302 · ארון קומה: 2 Buscomm + מתג PoE

MIGDALEI YAM A TIJON · ASSISTED LIVING
Nurse call system – GF + 6 floors · 36 apartments
System: ACE BG · Advantecnia   Prepared by: Telab International

TYPICAL FLOOR – WIRING

TYPICAL FLOOR – WIRING

SCALE	DATE	REV	SHEET
1:60	12/10/2026	A	02

Dimensions in metres
A1 format · Rev. A – Preliminary design

A · EQUIPMENT · 1:50

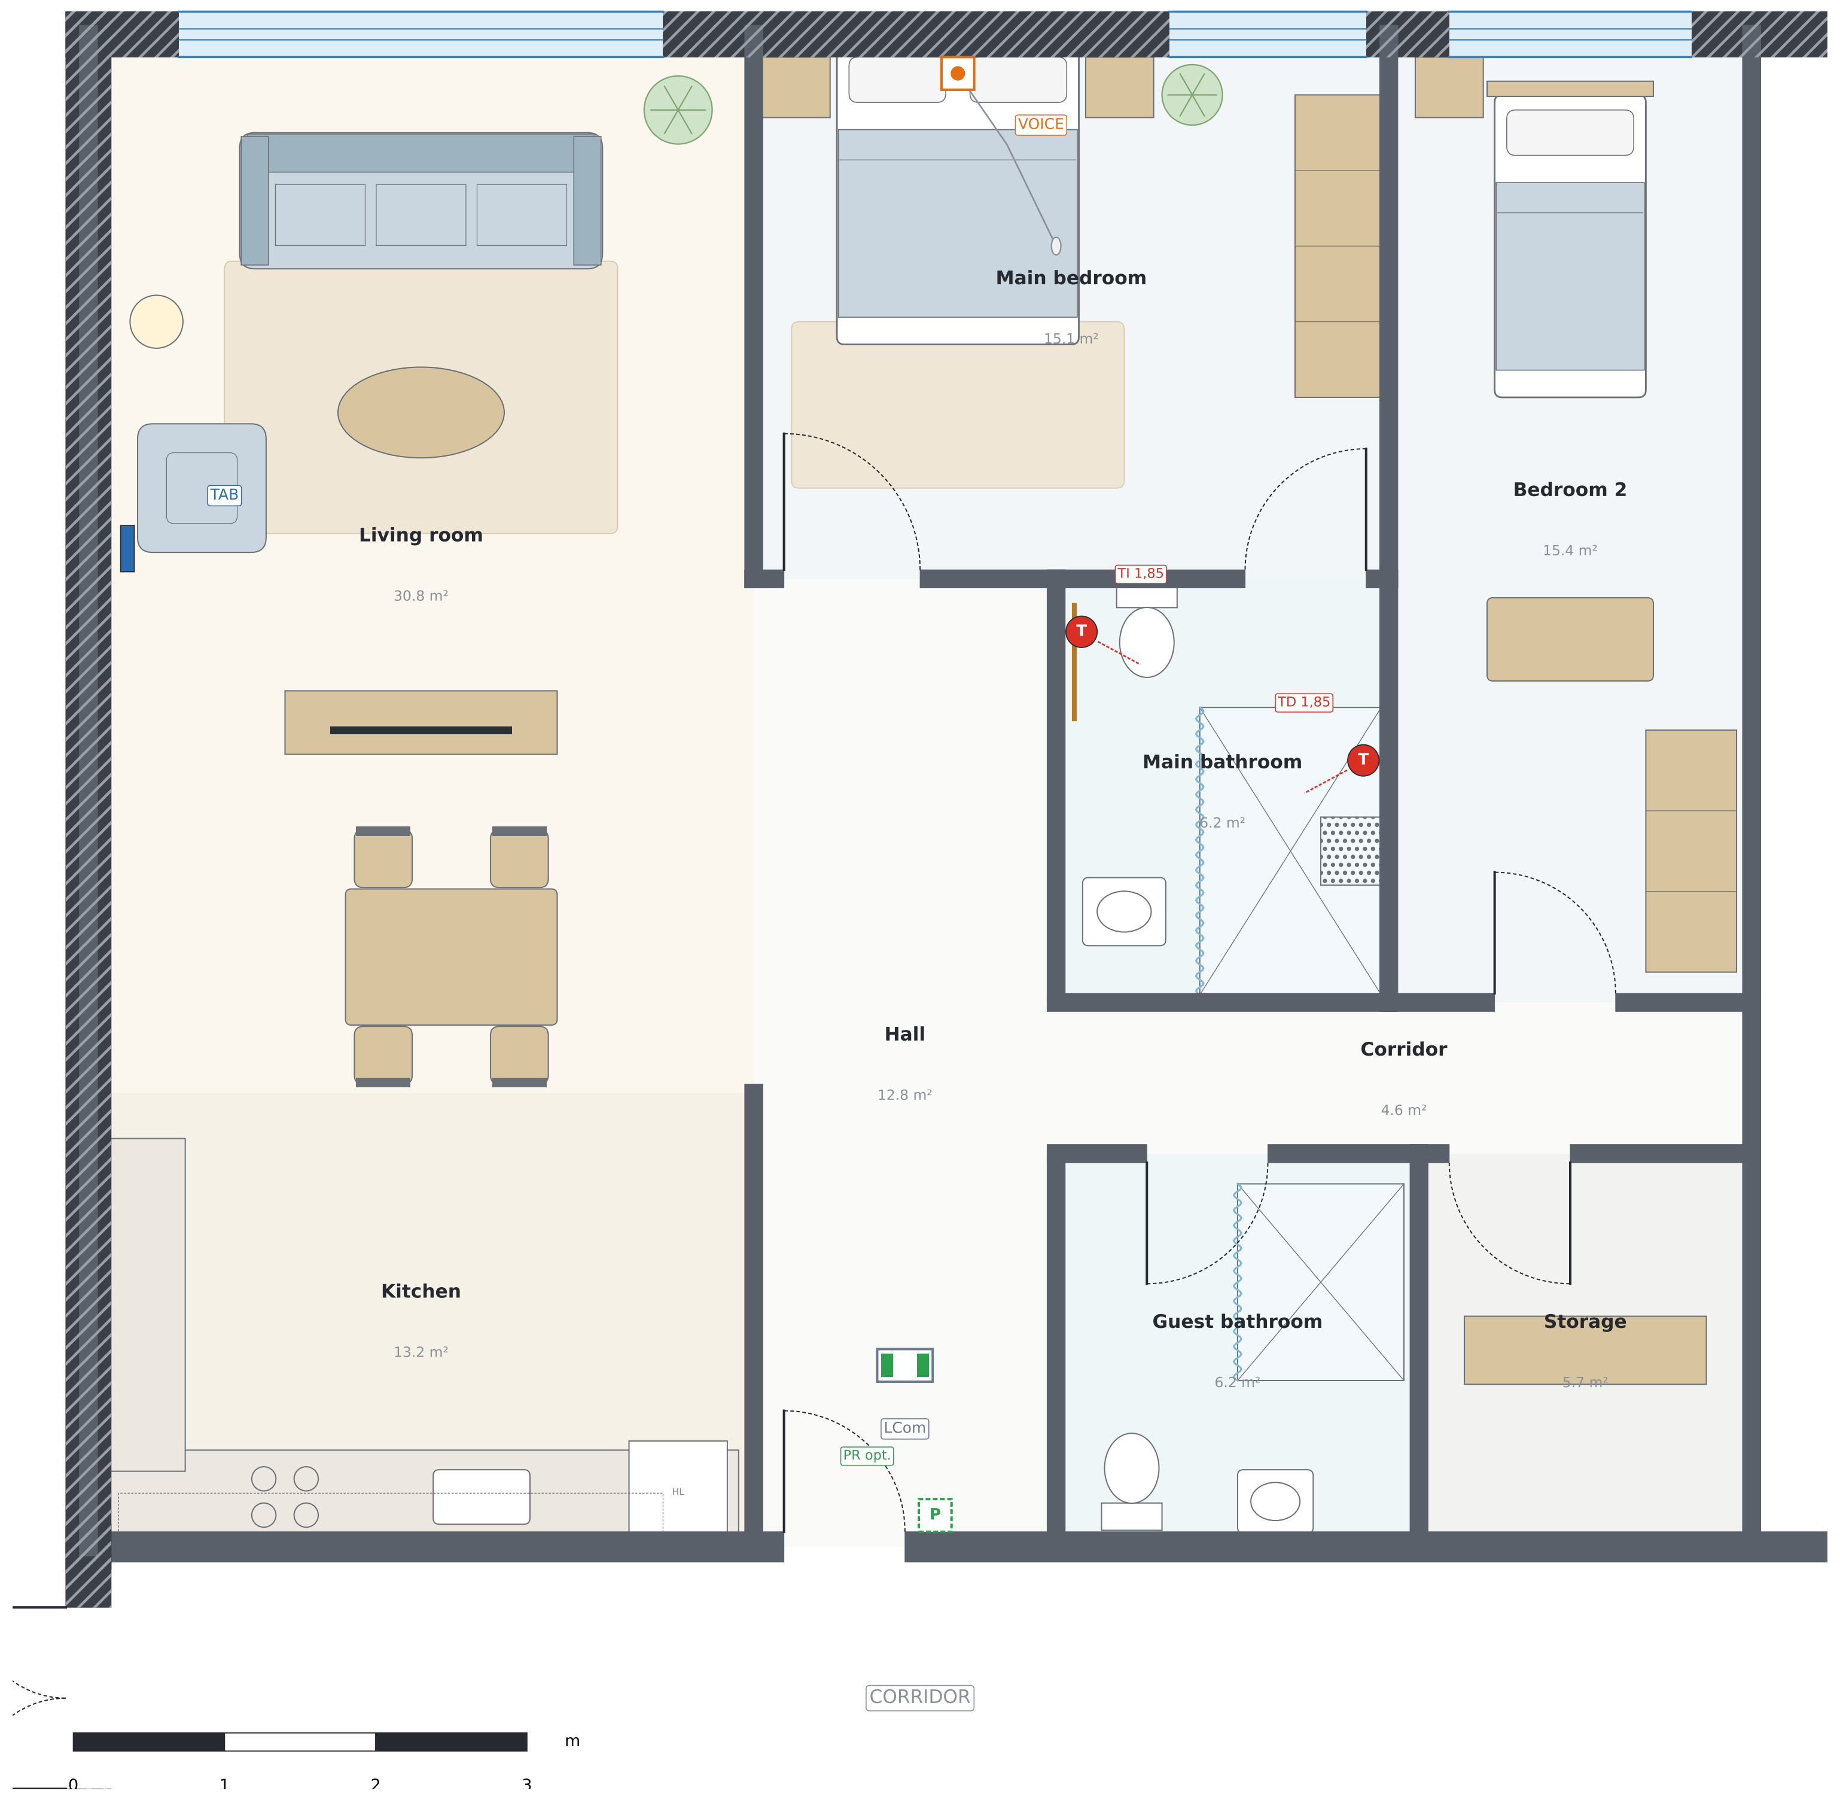

B · WIRING · 1:50

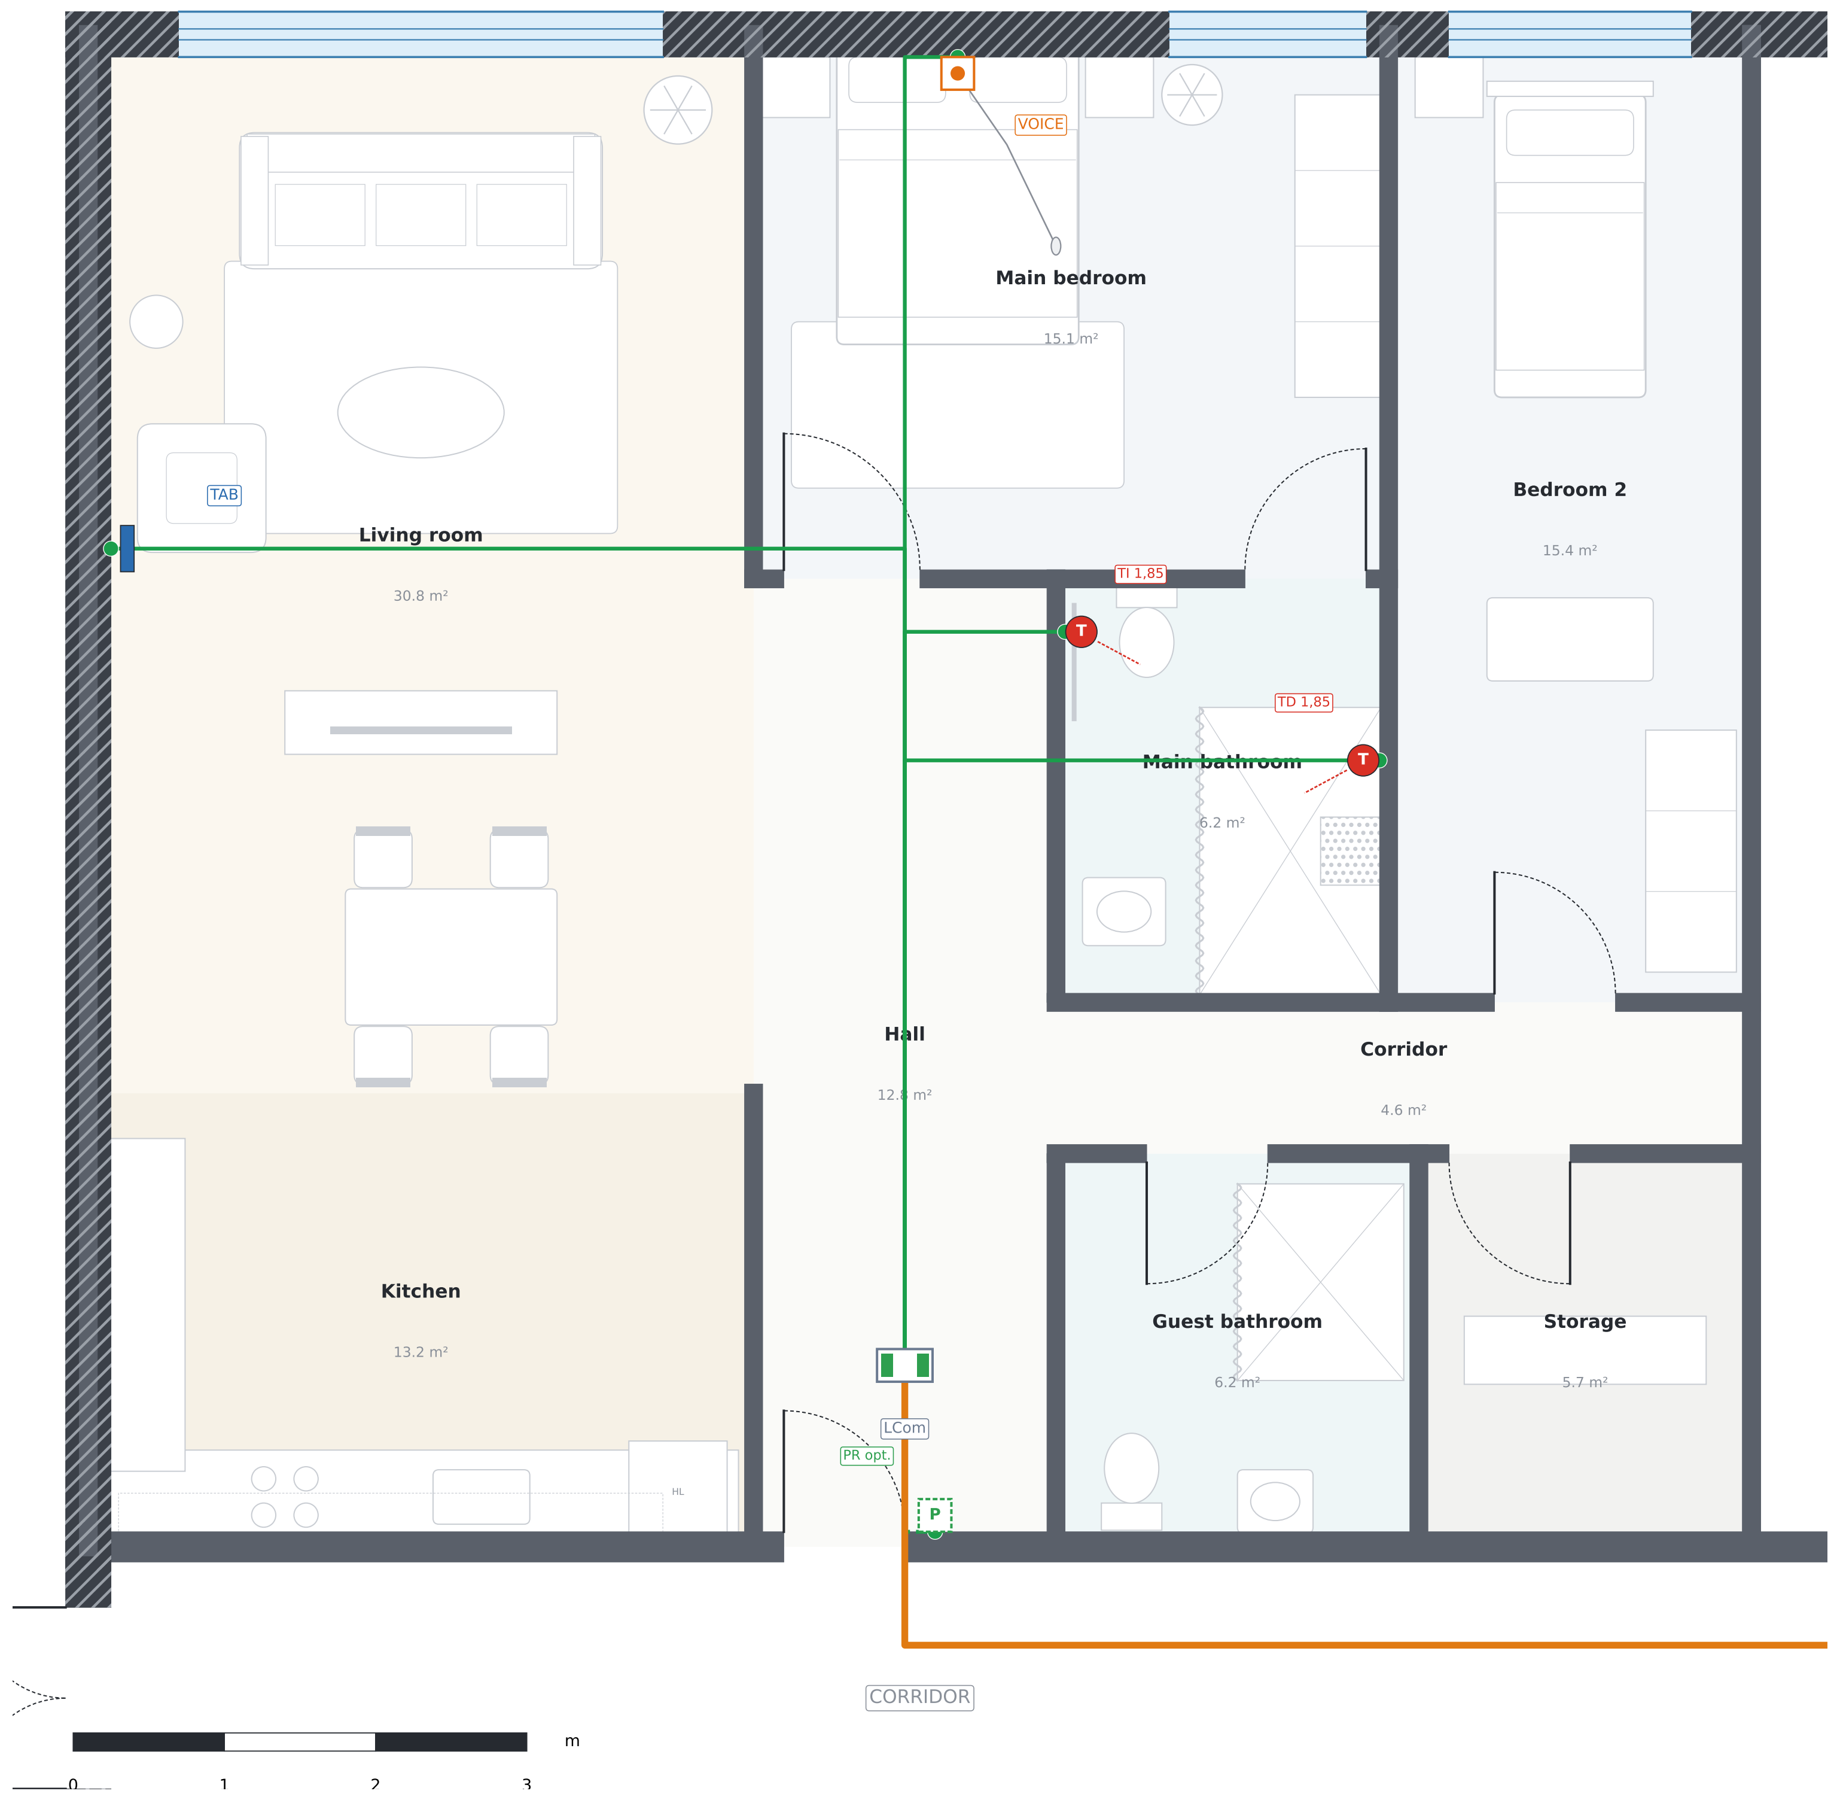

NOTES

1. Apartment 1 – type A, approx. 110 m².
2. Living room with open kitchen; guest bathroom with shower next to the living.
3. Main bedroom with en-suite bathroom (shower + toilet) and bedroom 2.
4. Call: Android tablet in the living room, voice call in the main bedroom, pull-cords at the toilet and shower of the main bathroom.
5. Presence / cancel button next to the door: optional (dashed).
6. All Cat6 radial to the hall LCom; the LCom continues the chain to the floor Buscomm. All PoE.

C · MOUNTING HEIGHTS (schematic elevation)

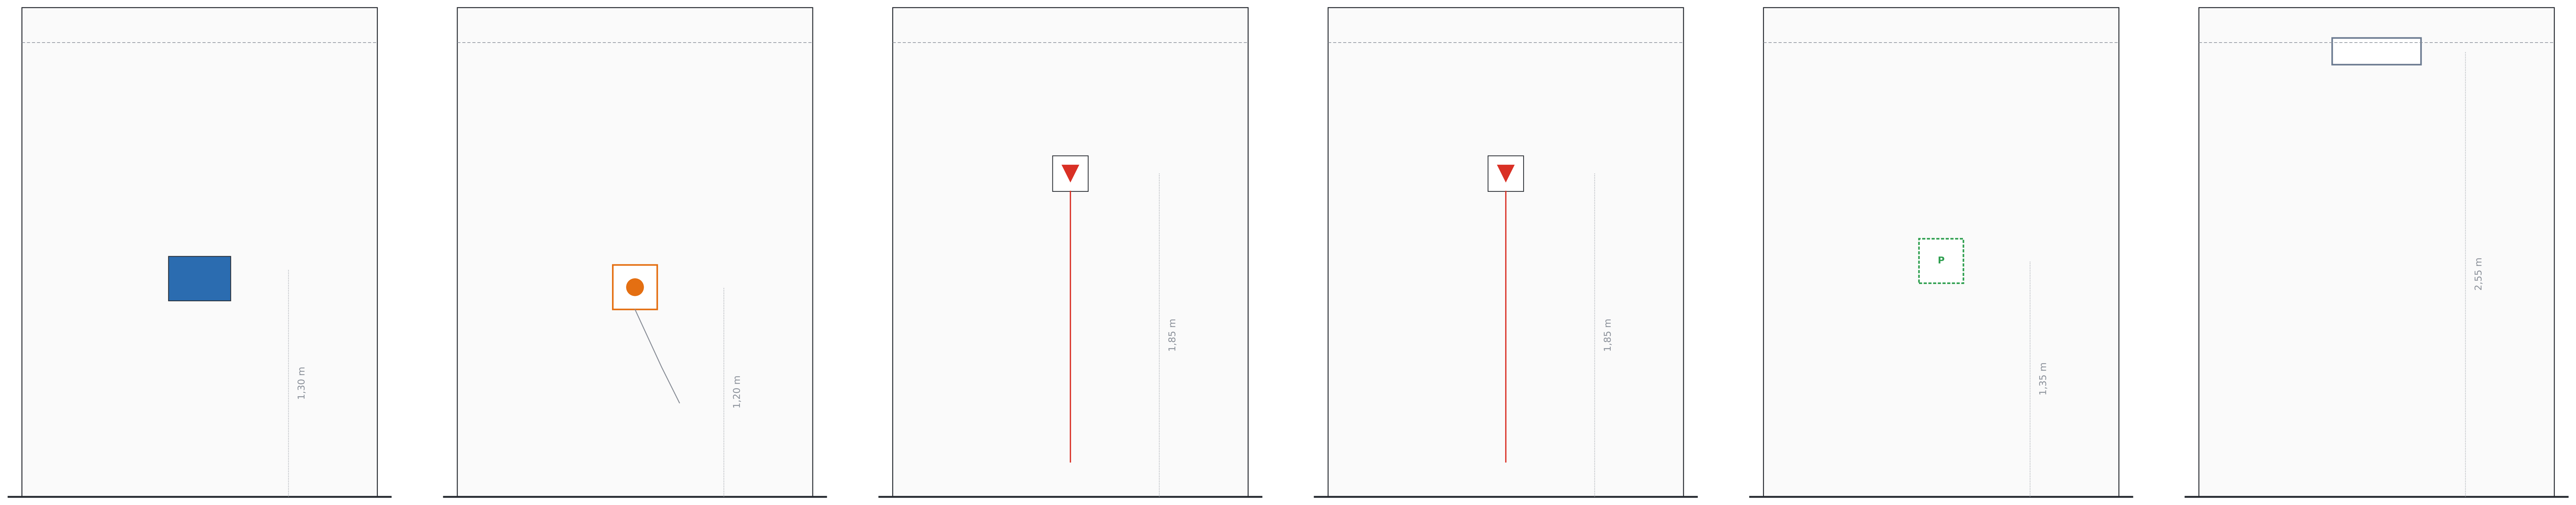

Living room – tablet

Bedroom – voice call

Bathroom – toilet pull-cord

Bathroom – shower pull-cord

Entrance – presence (opt.)

Hall – LCom (ceiling)

SÍMBOLOS Y CABLEADO · SYMBOLS & WIRING

🟦	TAB · Android tablet in the living room – call and voice Android tablet in the living room – call and voice · טאבלט אנדרואיד בסלון – קריאה ודיבור
T	TI / TD · Toilet / shower pull-cord ACE40320303W (main bathroom, h 1.85 m) Toilet / shower pull-cord ACE40320303W (main bath, h 1.85 m) · משיכת חבל אסלה / מקלחת ACE40320303W
▮▮	LCom ACE71610003 · apartment hub (hall ceiling) LCom ACE71610003 · apartment hub (hall ceiling) · LCom ACE71610003 · מרכז דירה (תקרת המבואה)
━	Cat6 / Cat7 chain: LCom → LCom → LCom → Buscomm (3 per Buscomm) Cat6 / Cat7 chain: LCom → LCom → LCom → Buscomm · Cat6 / Cat7 שרשרת: LCom ← LCom ← Buscomm
●	VOICE · Voice nurse call ACE82182451 (main bedroom) Voice nurse call ACE82182451 (main bedroom) · קריאת אחות קולית ACE82182451 (חדר שינה ראשי)
P	PR · Presence / cancel junto a la puerta – OPCIONAL Presence / cancel next to the door – OPTIONAL · נוכחות / ביטול ליד הדלת – אופציונלי
━	Cat6 radial: each apartment device → its LCom Cat6 radial: each device → its LCom · Cat6 רדיאלי: כל התקן ← LCom
- - -	Cat6 to the optional presence / cancel button Cat6 to optional presence / cancel button · Cat6 לחצן נוכחות אופציונלי

MIGDALEI YAM A TIJON · ASSISTED LIVING
Nurse call system – GF + 6 floors · 36 apartments
System: ACE BG · Advantecnia   Prepared by: Telab International

TYPE A APARTMENT – DETAIL
TYPE A APARTMENT – DETAIL

SCALE	DATE	REV	SHEET
1:50	**12/10/2026**	**A**	**03**

Dimensions in metres
A1 format · Rev. A – Preliminary design

A · EQUIPMENT · 1:45

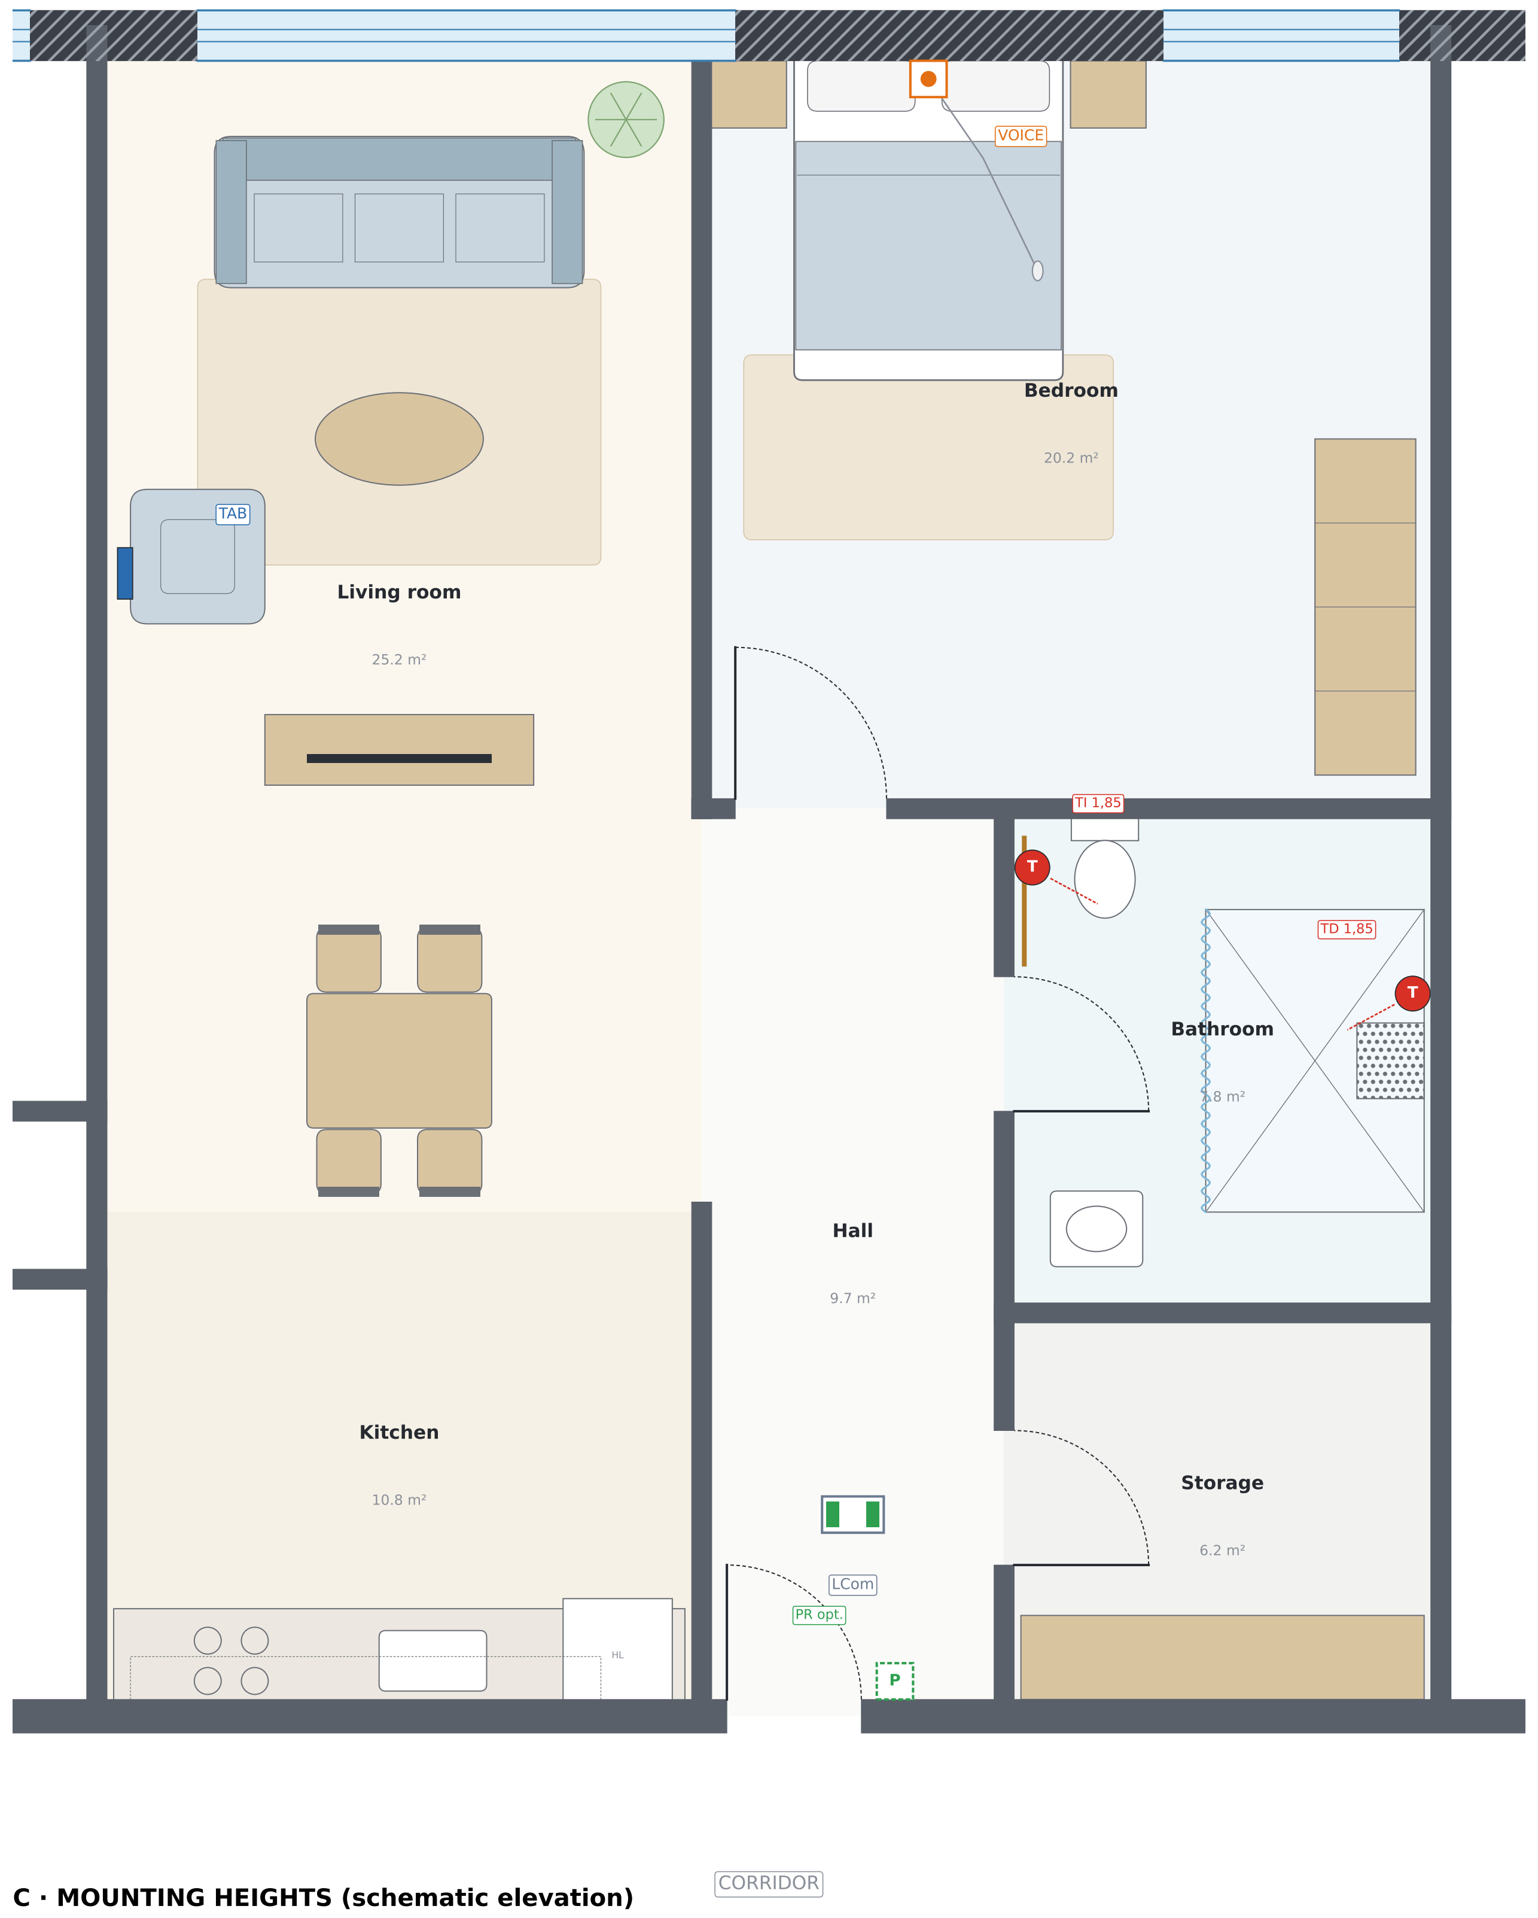

B · WIRING · 1:45

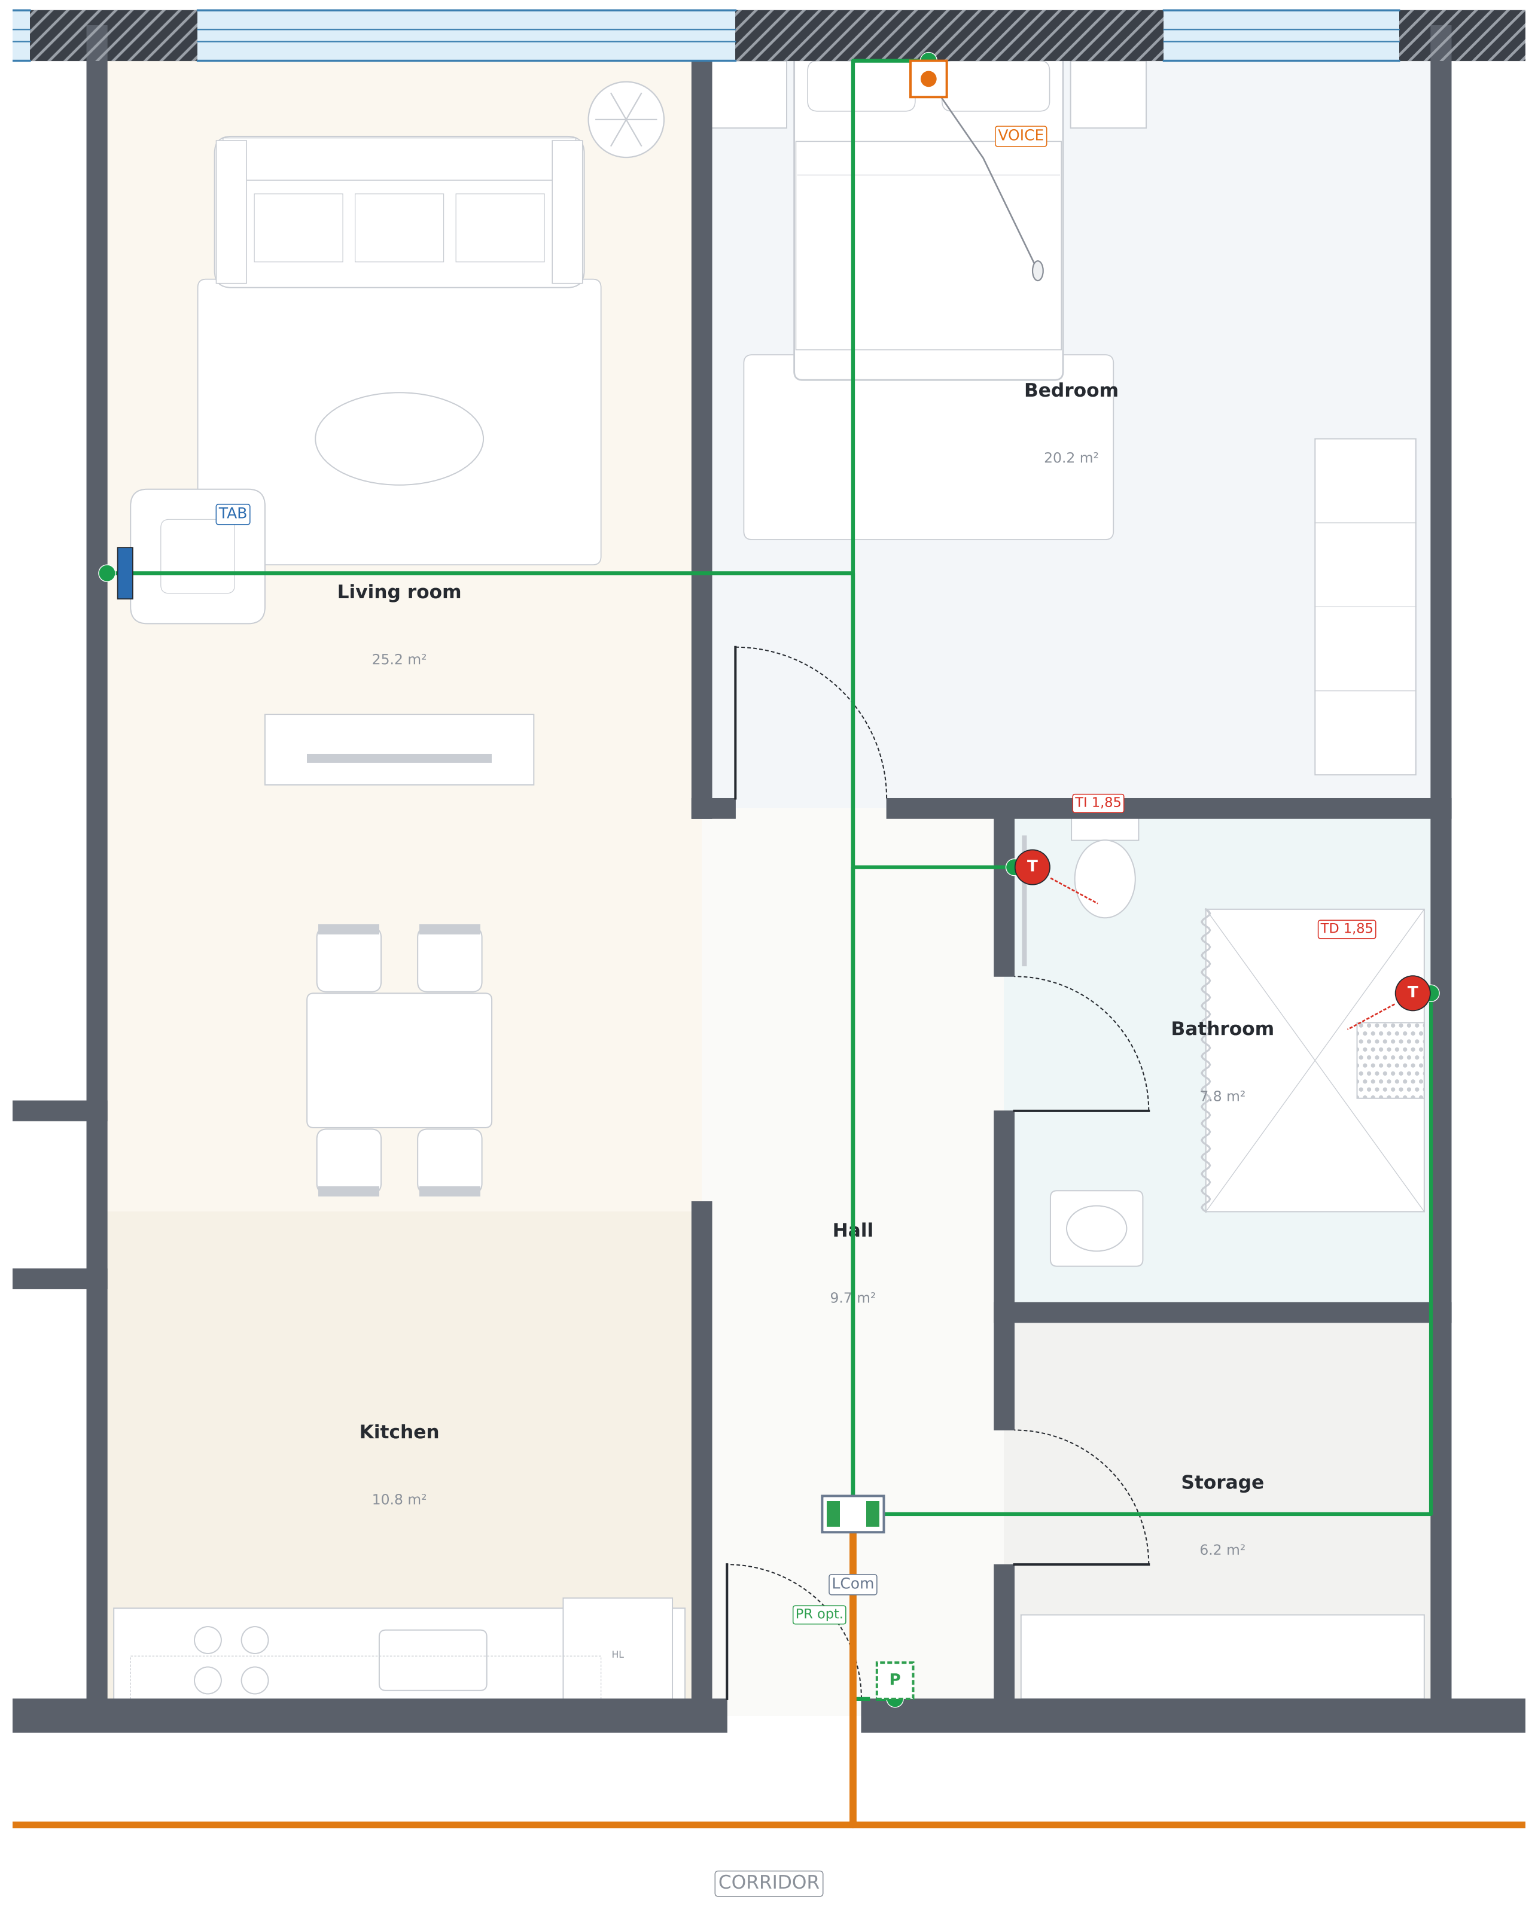

NOTES

1. Apartment 2 – type B, approx. 80 m².
2. Living room with open kitchen, one bedroom and one bathroom with shower.
3. Call: Android tablet in the living room, voice call in the bedroom, pull-cords at toilet and shower.
4. Presence / cancel button next to the door: optional (dashed).
5. All Cat6 radial to the hall LCom; the LCom continues the chain to the floor Buscomm. All PoE.

C · MOUNTING HEIGHTS (schematic elevation)

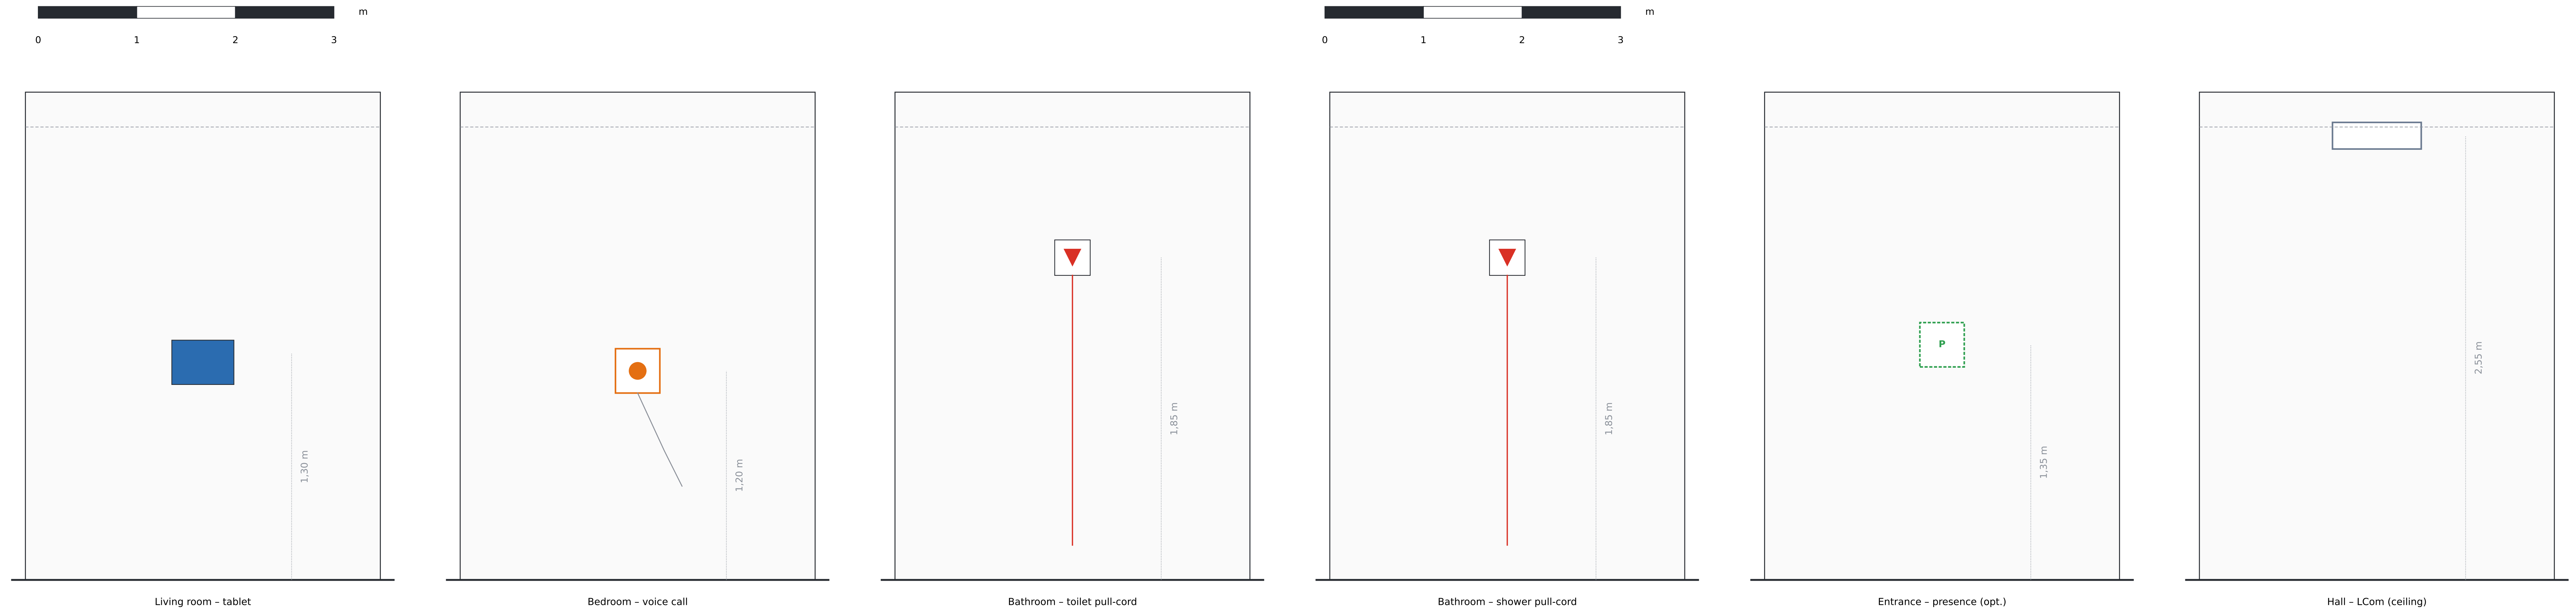

Living room – tablet

Bedroom – voice call

Bathroom – toilet pull-cord

Bathroom – shower pull-cord

Entrance – presence (opt.)

Hall – LCom (ceiling)

SÍMBOLOS Y CABLEADO · SYMBOLS & WIRING

▮	TAB · Android tablet in the living room – call and voice Android tablet in the living room – call and voice · טאבלט אנדרואיד בסלון – קריאה ודיבור
T	TI / TD · Toilet / shower pull-cord ACE40320303W (main bathroom, h 1.85 m) Toilet / shower pull-cord ACE40320303W (main bath, h 1.85 m) · משיכת חבל באסלה / מקלחת ACE40320303W
▯	LCom ACE71610003 · apartment hub (hall ceiling) LCom ACE71610003 · apartment hub (hall ceiling) · LCom ACE71610003 · מרכז דירה (תקרת המבואה)
━	Cat6 / Cat7 chain: LCom → LCom → LCom → Buscomm (3 per Buscomm) Cat6 / Cat7 chain: LCom → LCom → LCom → Buscomm · Cat6 / Cat7 שרשרת: LCom ← LCom ← Buscomm
●	VOICE · Voice nurse call ACE82182451 (main bedroom) Voice nurse call ACE82182451 (main bedroom) · קריאת אחות קולית ACE82182451 (חדר שינה ראשי)
P	PR · Presence / cancel junto a la puerta – OPCIONAL Presence / cancel next to the door – OPTIONAL · נוכחות / ביטול ליד הדלת – אופציונלי
━	Cat6 radial: each apartment device → its LCom Cat6 radial: each device → its LCom · Cat6 רדיאלי: כל התקן ← LCom
╌	Cat6 to the optional presence / cancel button Cat6 to optional presence / cancel button · Cat6 ללחצן נוכחות אופציונלי

MIGDALEI YAM A TIJON · ASSISTED LIVING
Nurse call system – GF + 6 floors · 36 apartments
System: ACE BG · Advantecnia Prepared by: Telab International

TYPE B APARTMENT – DETAIL
TYPE B APARTMENT – DETAIL

SCALE	DATE	REV	SHEET
1:50	12/10/2026	A	04

Dimensions in metres
A1 format · Rev. A – Preliminary design

A · BUILDING VERTICAL DIAGRAM (GF + 6 FLOORS)

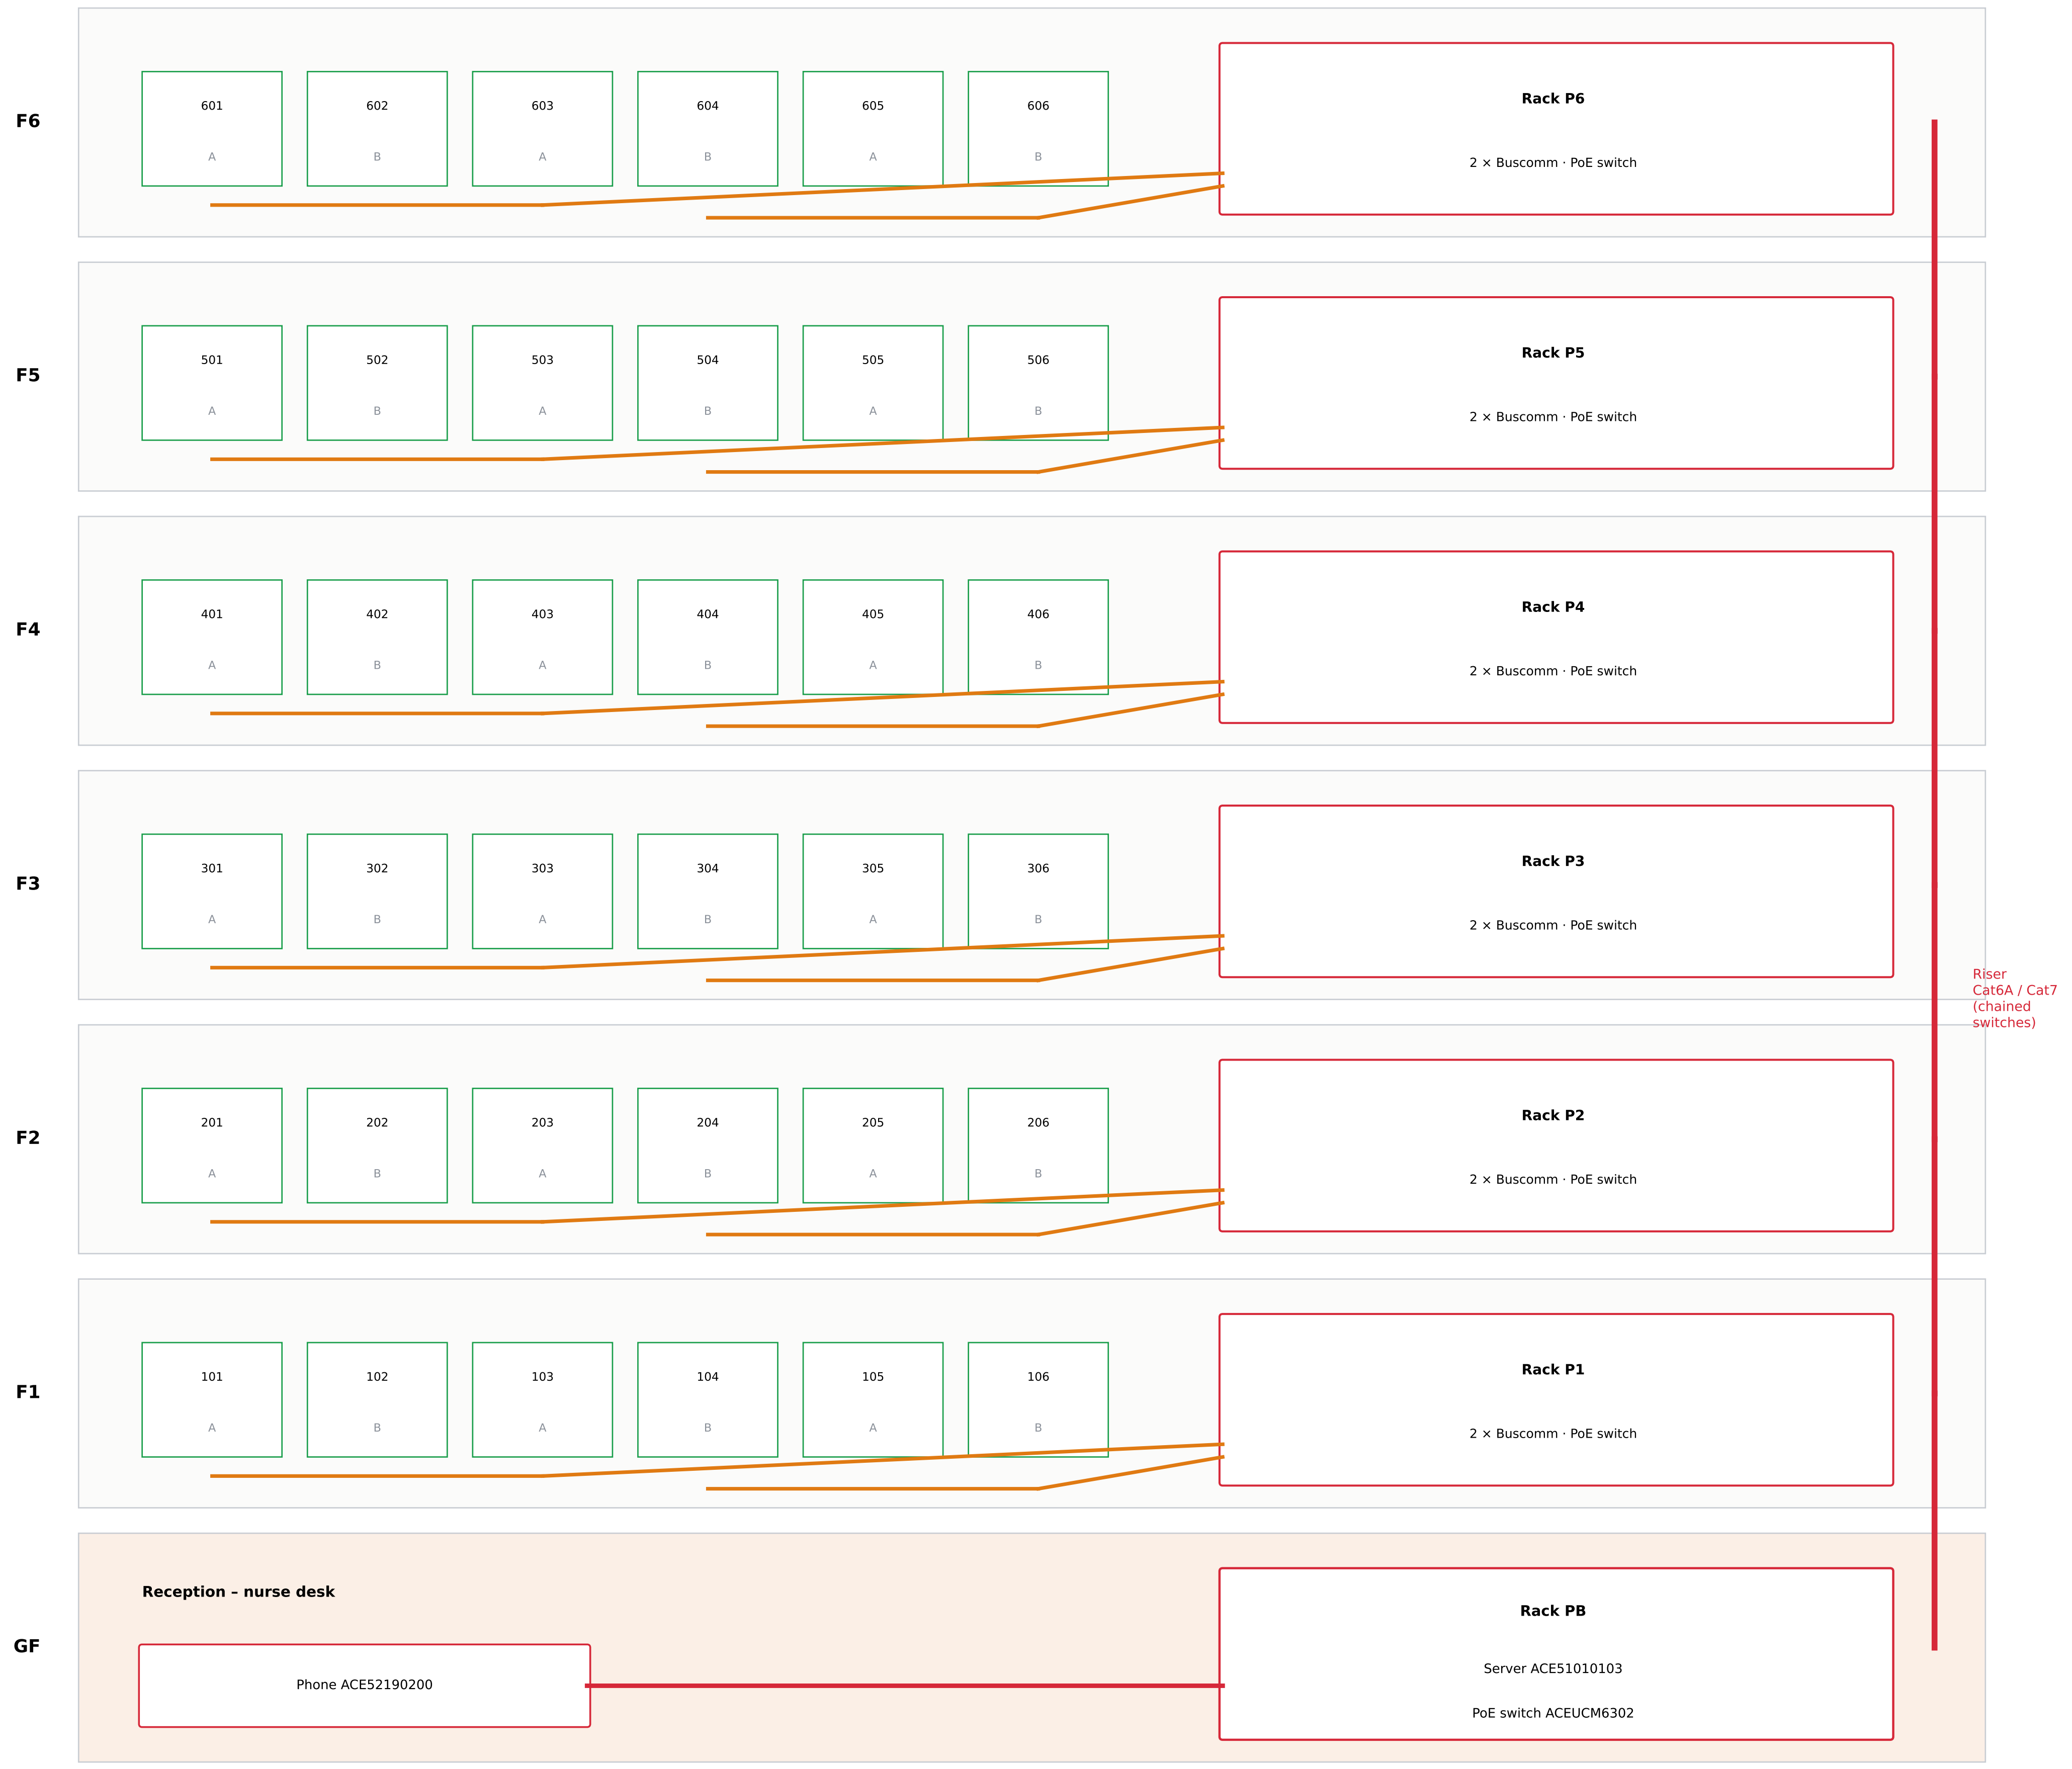

B · TOPOLOGY PER APARTMENT AND PER FLOOR

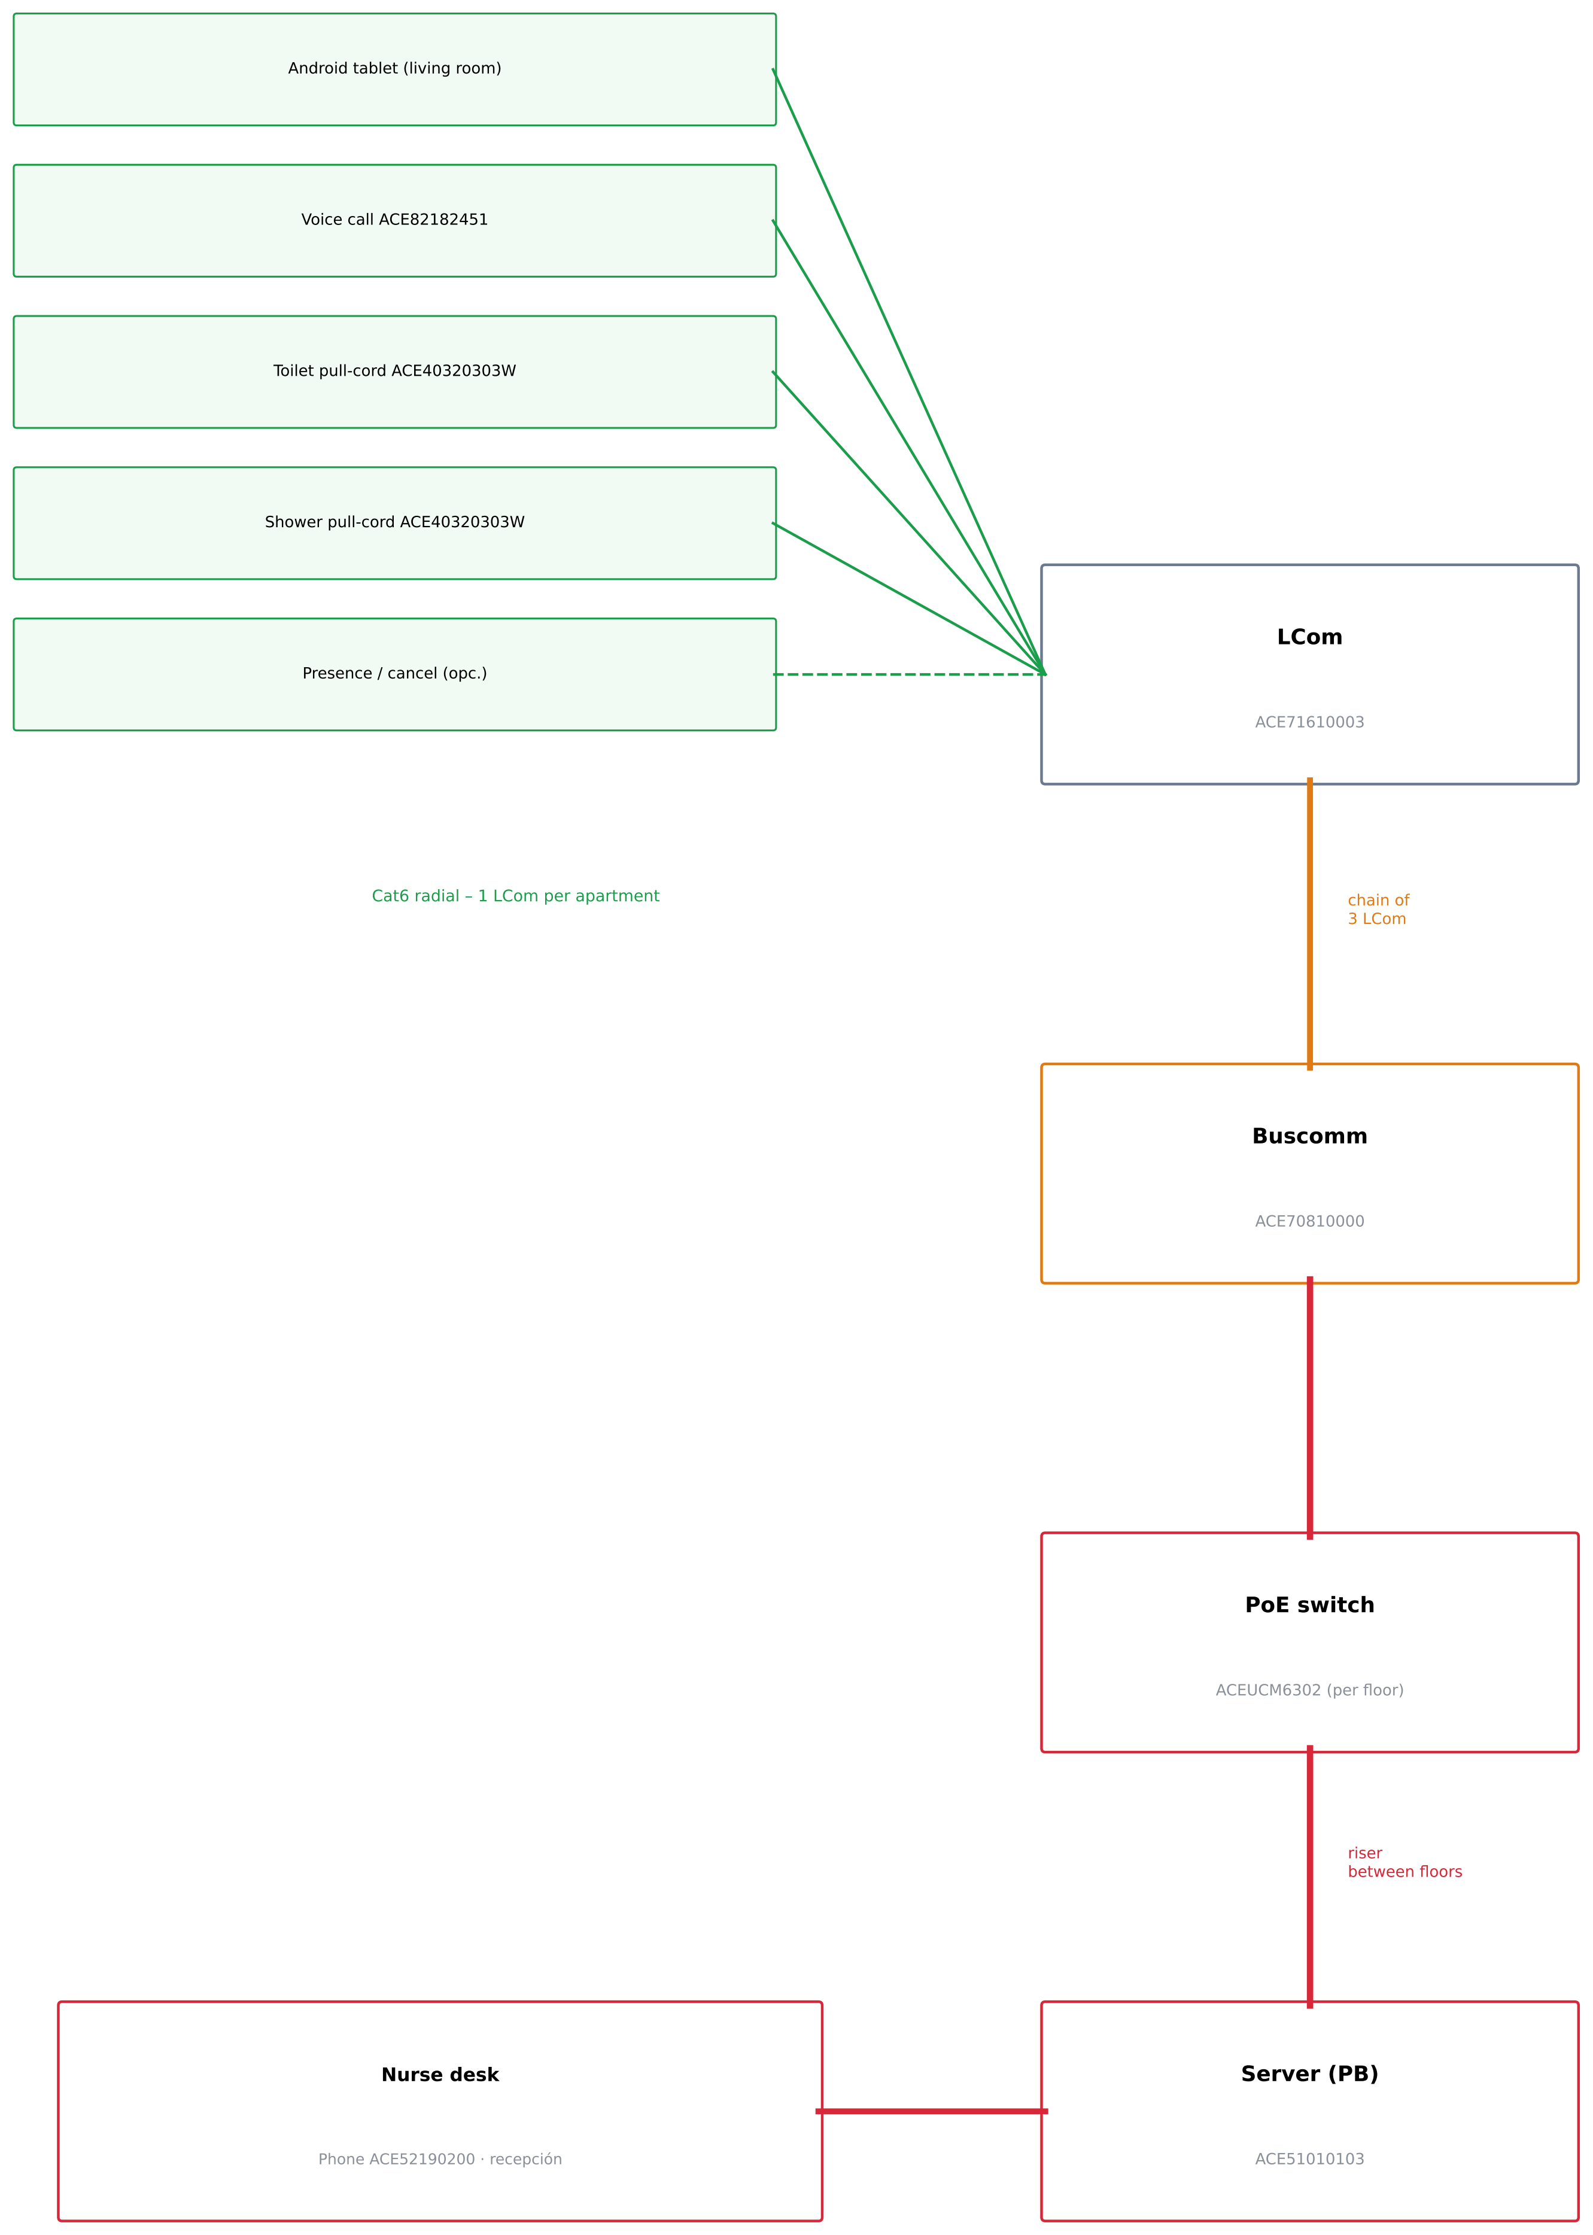

NOTES

1. Ground floor: reception with the nurse desk (phone ACE52190200) and the main rack with the server.
2. Floors 1 a 6: 6 departamentos por piso (3 tipo A y 3 tipo B intercalados).
3. On each floor: 2 Buscomm (3 LCom each) and one PoE switch in the rack.
4. Switches are chained floor to floor up the Cat6A / Cat7 riser to the ground-floor server.
5. The whole system is PoE.
6. Calls reach the nurse desk as voice or as an alarm.
7. Preliminary quantities: validate with Advantecnia and on site.

C · BILL OF MATERIALS – WHOLE BUILDING (36 apartments)

Code	Description	Qty	Remarks
IN EACH APARTMENT (× 36)			
TAB	Wall-mounted Android tablet (living) – call and voice	36	1 per apartment
VOICE	Voice nurse call – ACE82182451	36	main bedroom
TI / TD	Toilet / shower pull-cord – ACE40320303W	72	2 per apartment
PR	Presence / cancel junto a la puerta – OPCIONAL	(36)	optional
LCom	Apartment hub – ACE71610003	36	1 per apartment
PER FLOOR (× 6) AND GROUND FLOOR			
BC	Buscomm – ACE70810000	12	2 per floor (3 LCom each)
SW	PoE switch – ACEUCM6302	7	1 per floor + GF
RACK	Rack de comunicaciones con patch panel y UPS	7	1 per floor + GF
SV	Server + Advantecnia software – ACE51010103	1	GF
TEL	Nurse desk phone – ACE52190200	1	GF reception
CABLES (typical floor × 6, + 15 % spare)			
—	Cat6 radial inside the apartments (green)	1640 m	237 m per floor
—	Cat6 / Cat7 chain LCom → Buscomm (orange)	620 m	89 m per floor
—	Cat6A / Cat7 rack + riser, 7 levels (red)	70 m	includes riser

MIGDALEI YAM A TIJON · ASSISTED LIVING
Nurse call system – GF + 6 floors · 36 apartments
System: ACE BG · Advantecnia Prepared by: Telab International

VERTICAL DIAGRAM, TOPOLOGY AND MATERIALS
VERTICAL DIAGRAM, TOPOLOGY AND MATERIALS

SCALE	DATE	REV	SHEET
NTS	**12/10/2026**	**A**	**05**

Dimensions in metres
A1 format · Rev. A – Preliminary design

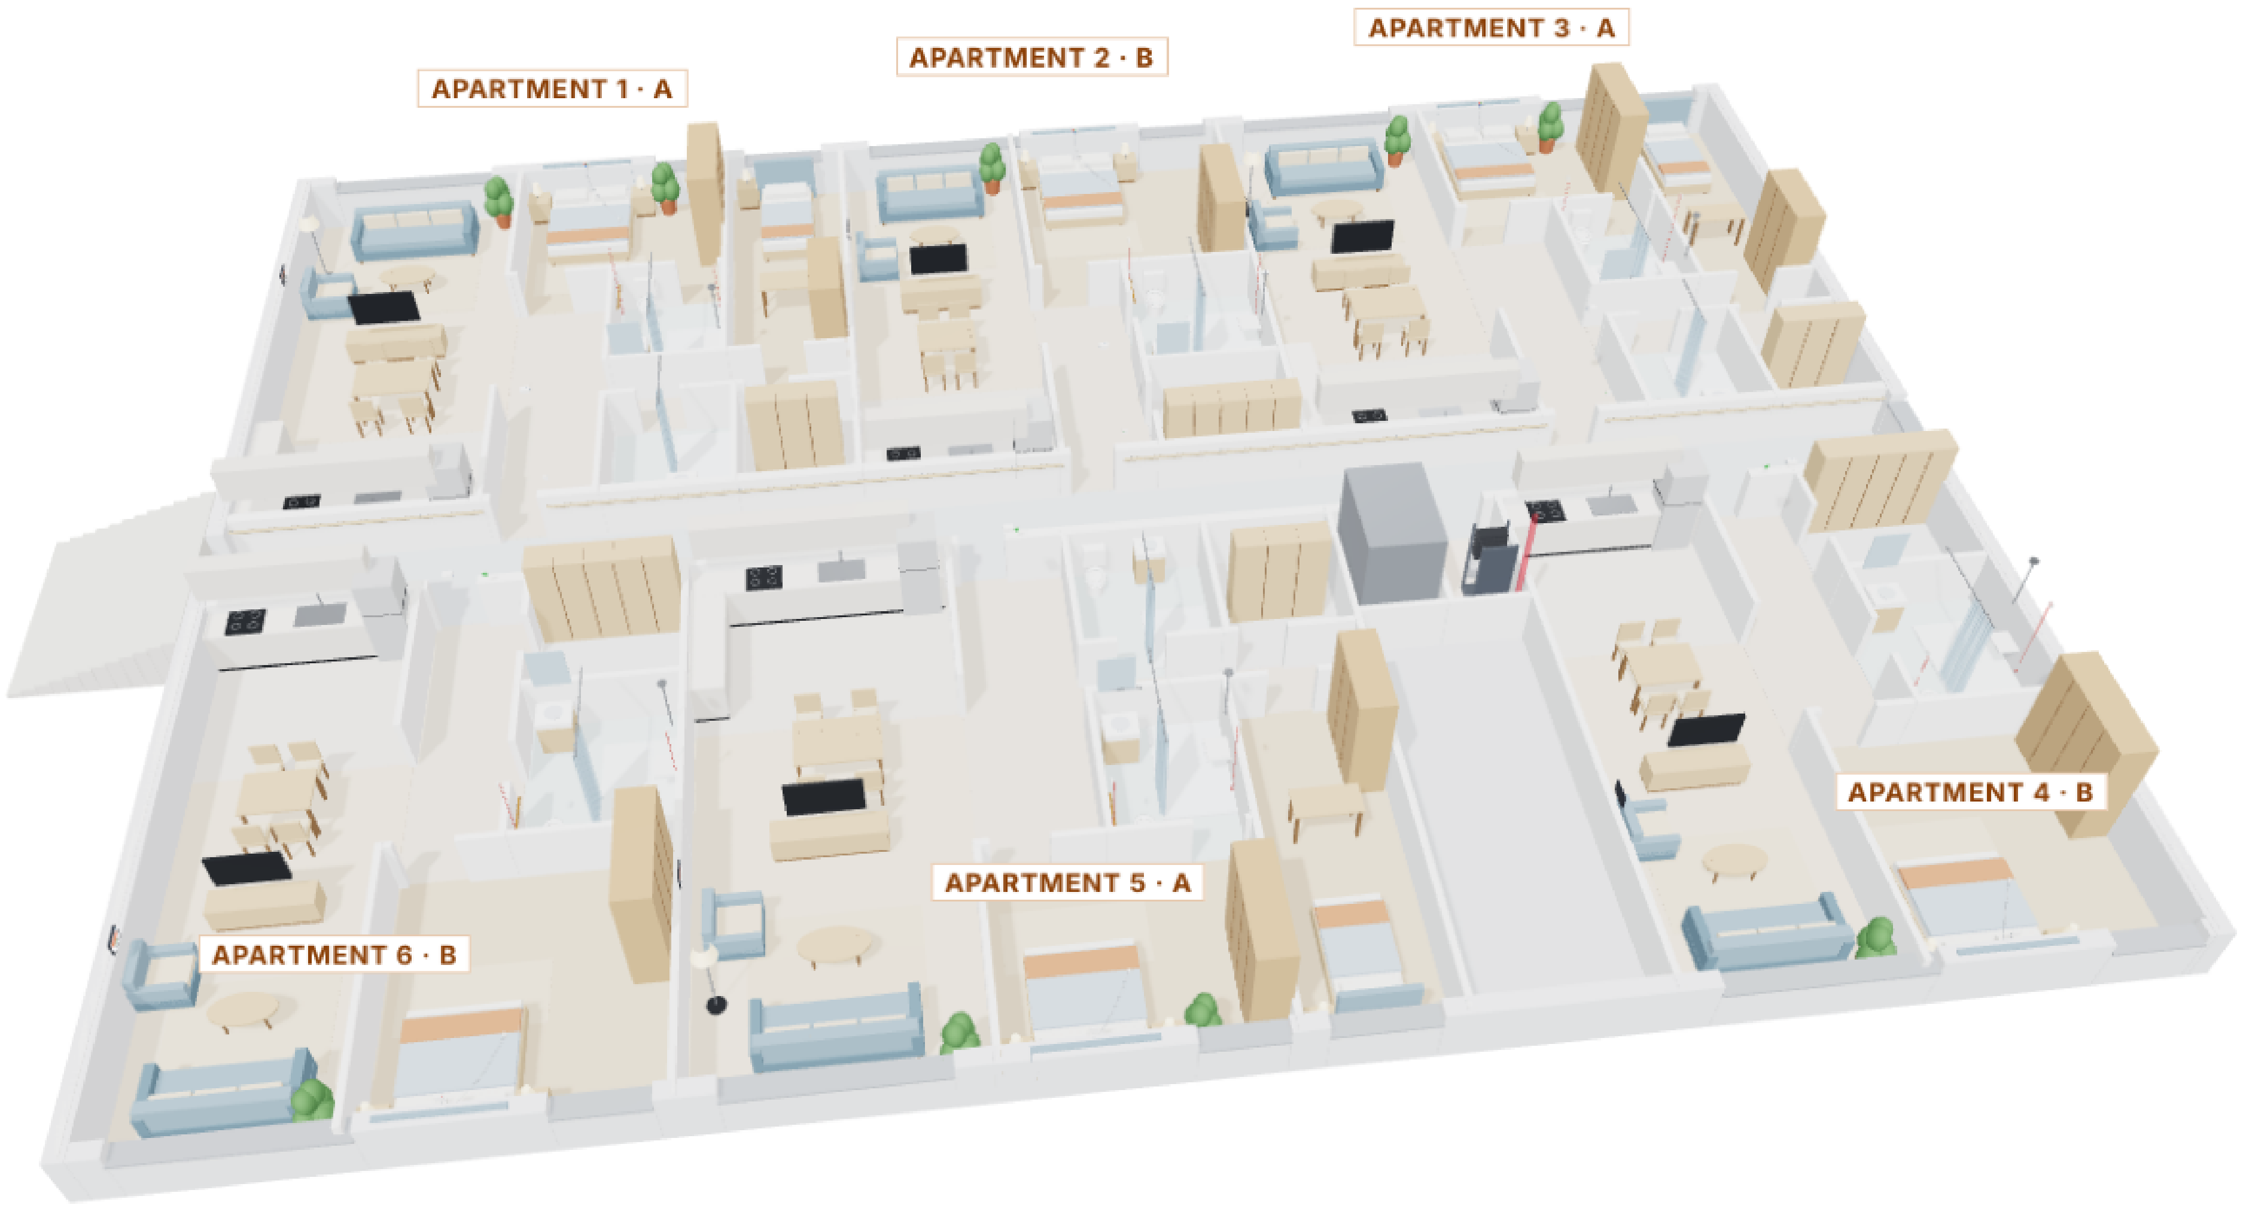

A · Floor tipo – departamentos 1 (tipo A) y 2 (tipo B) destacados

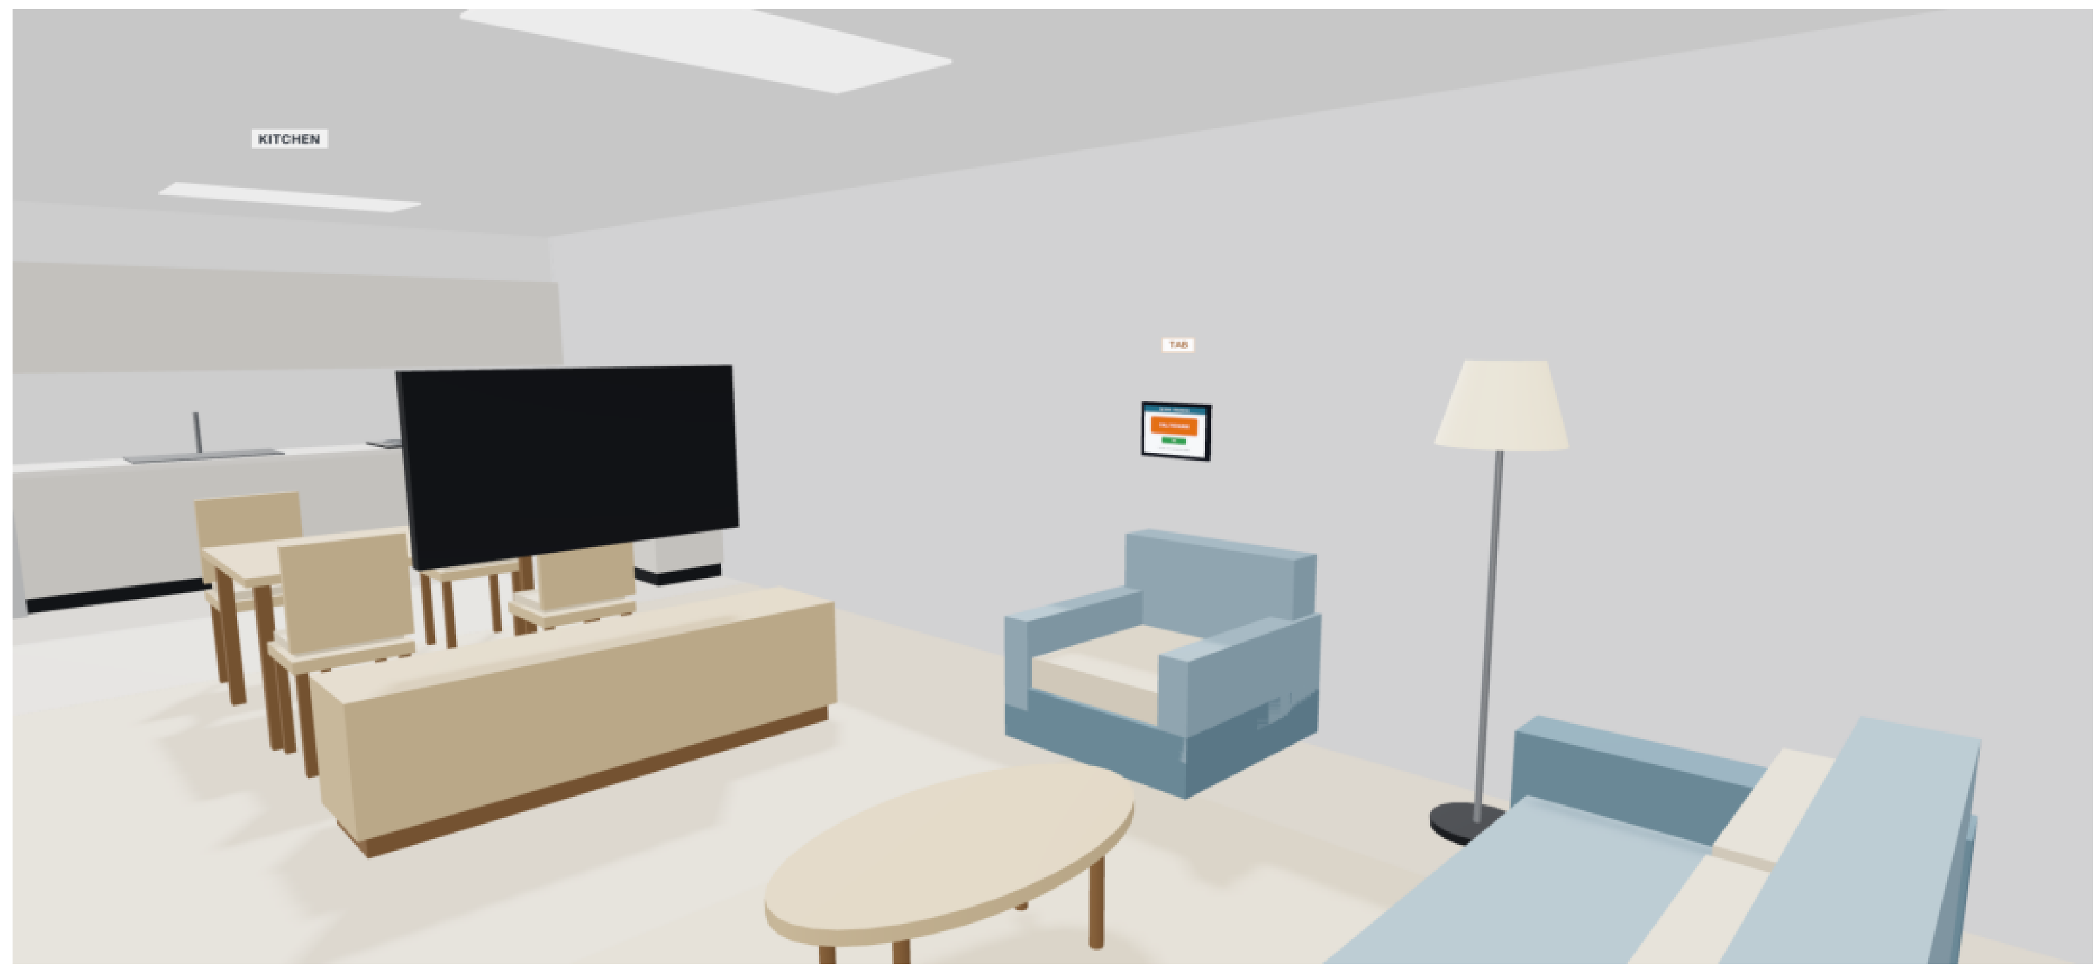

B · Living room with Android tablet

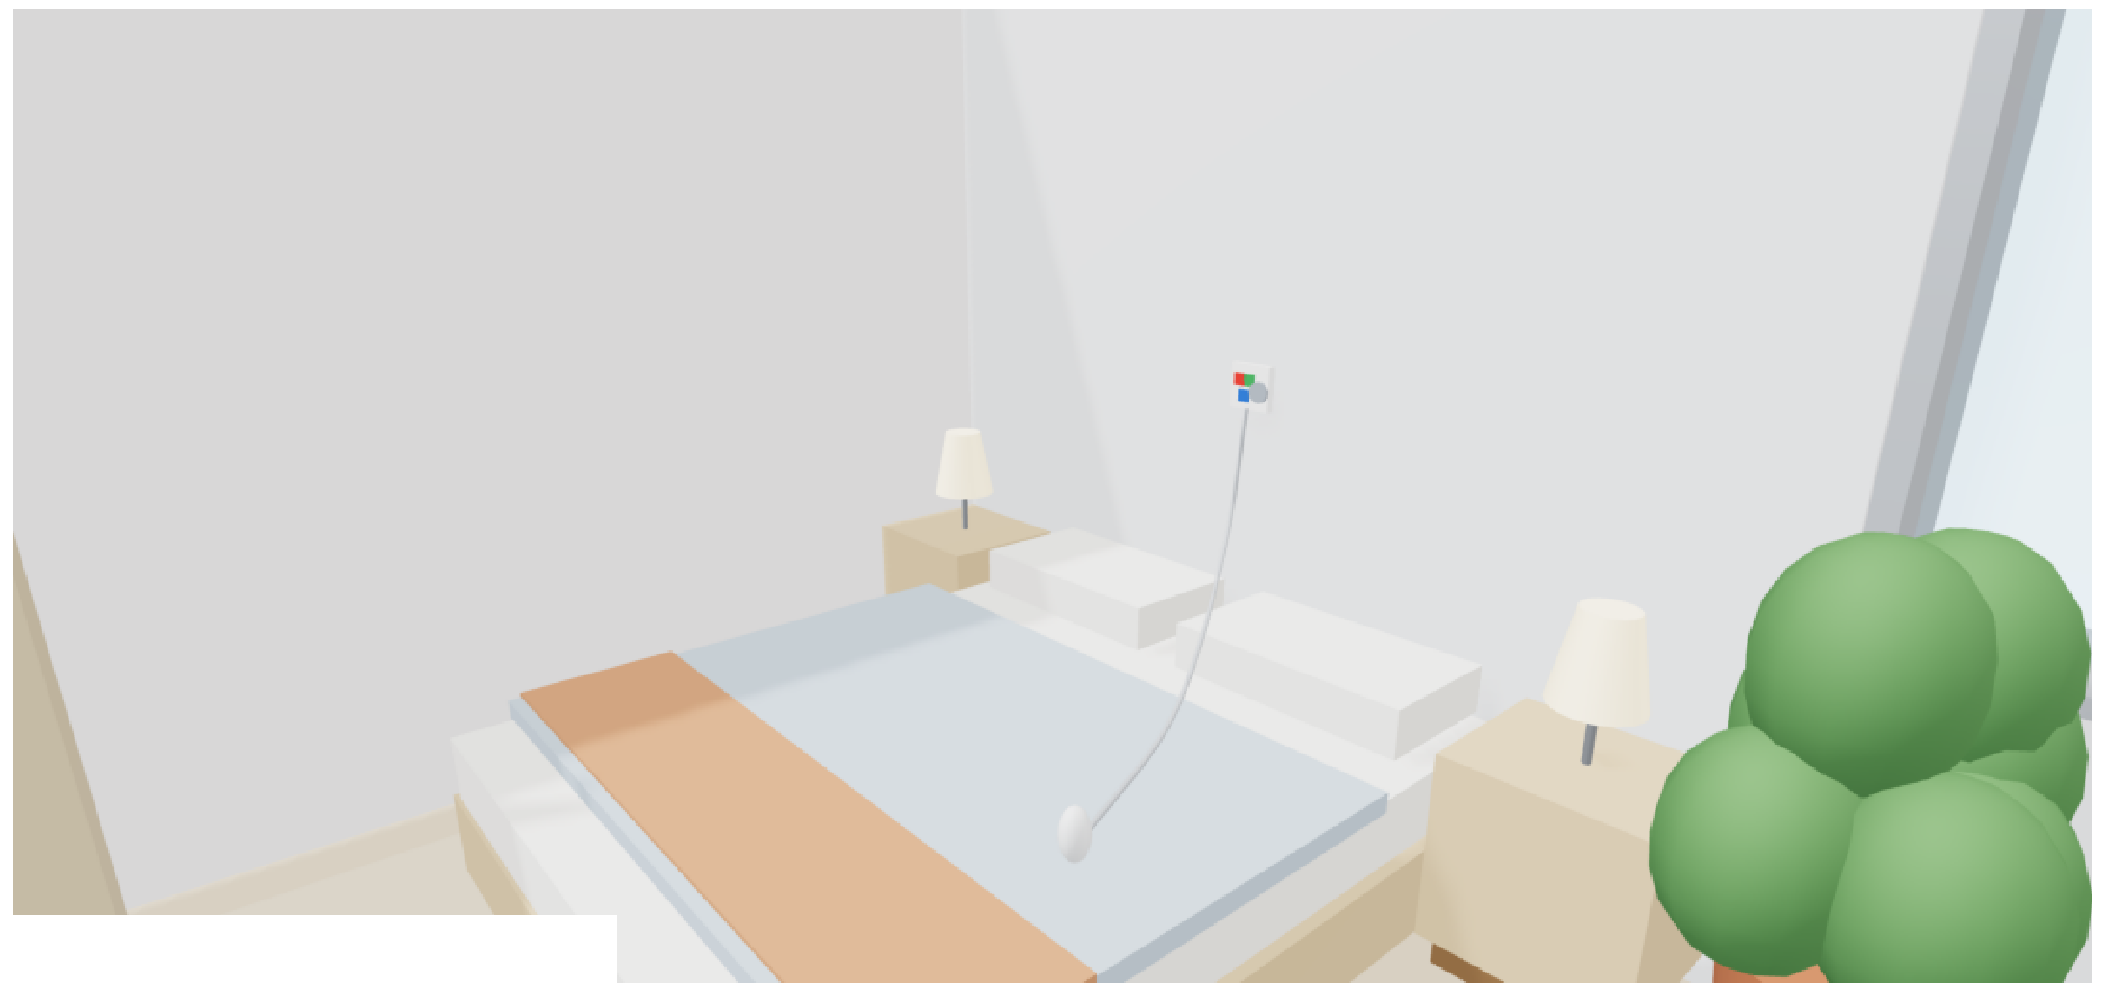

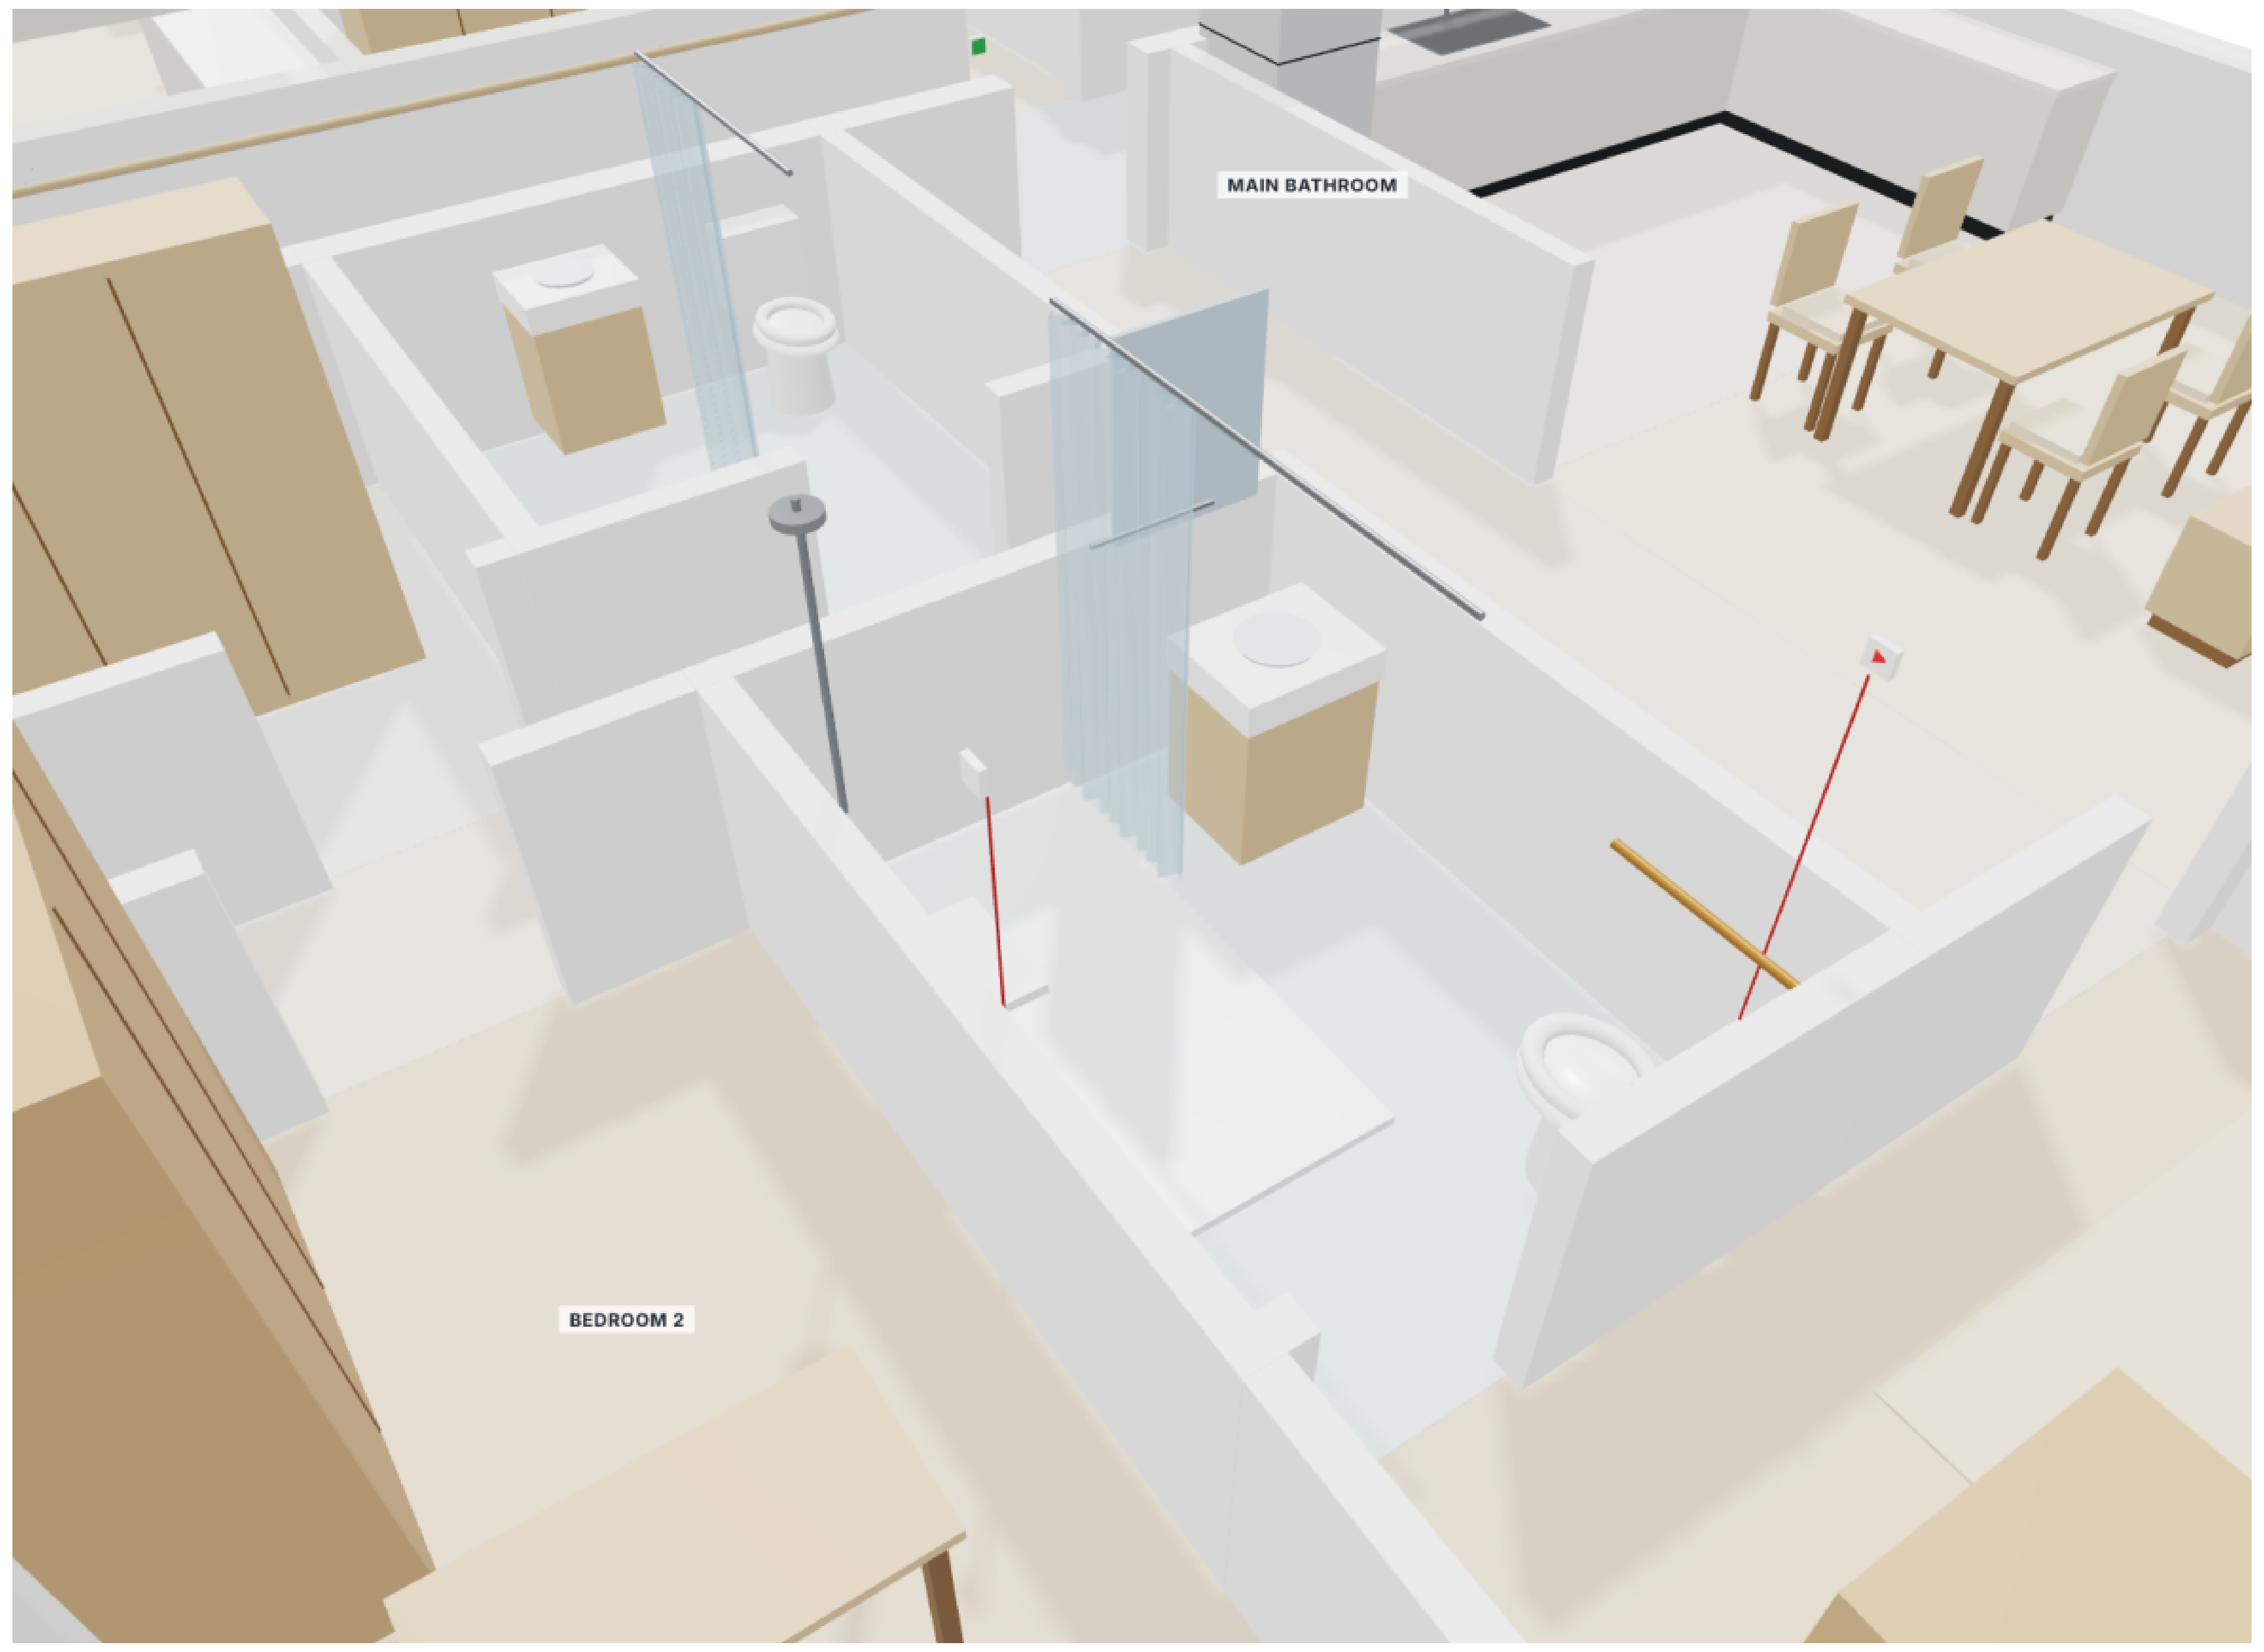

D · Main bathroom – toilet and shower pull-cords

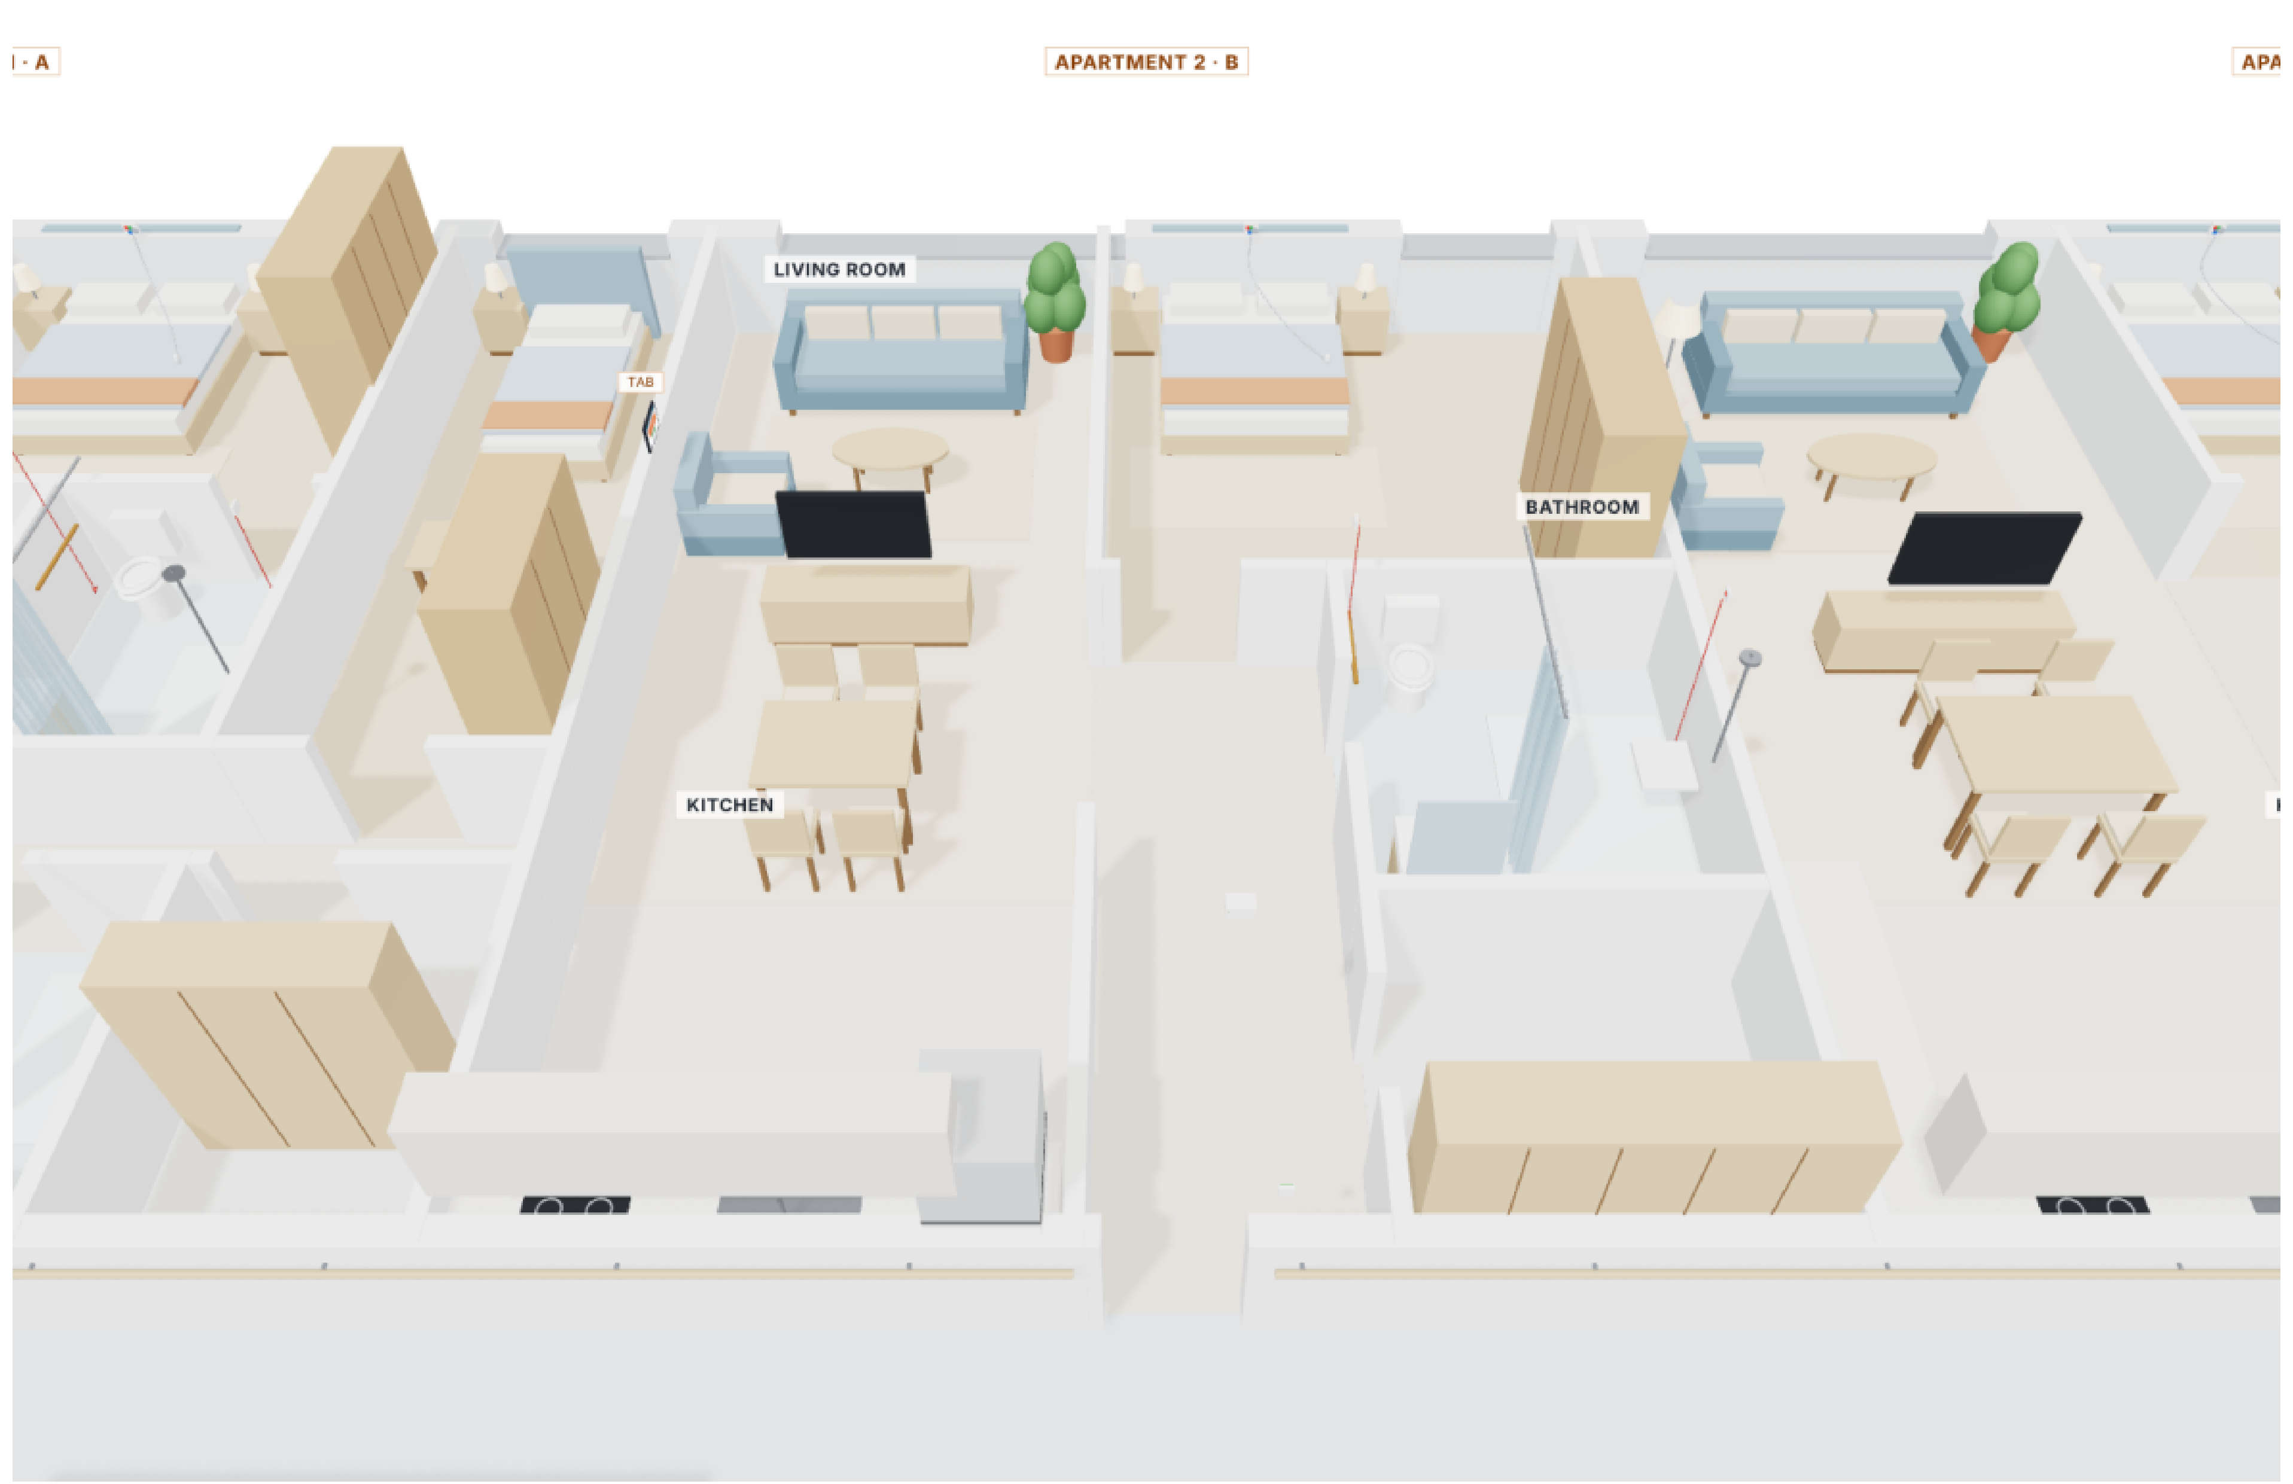

E · Type B apartment

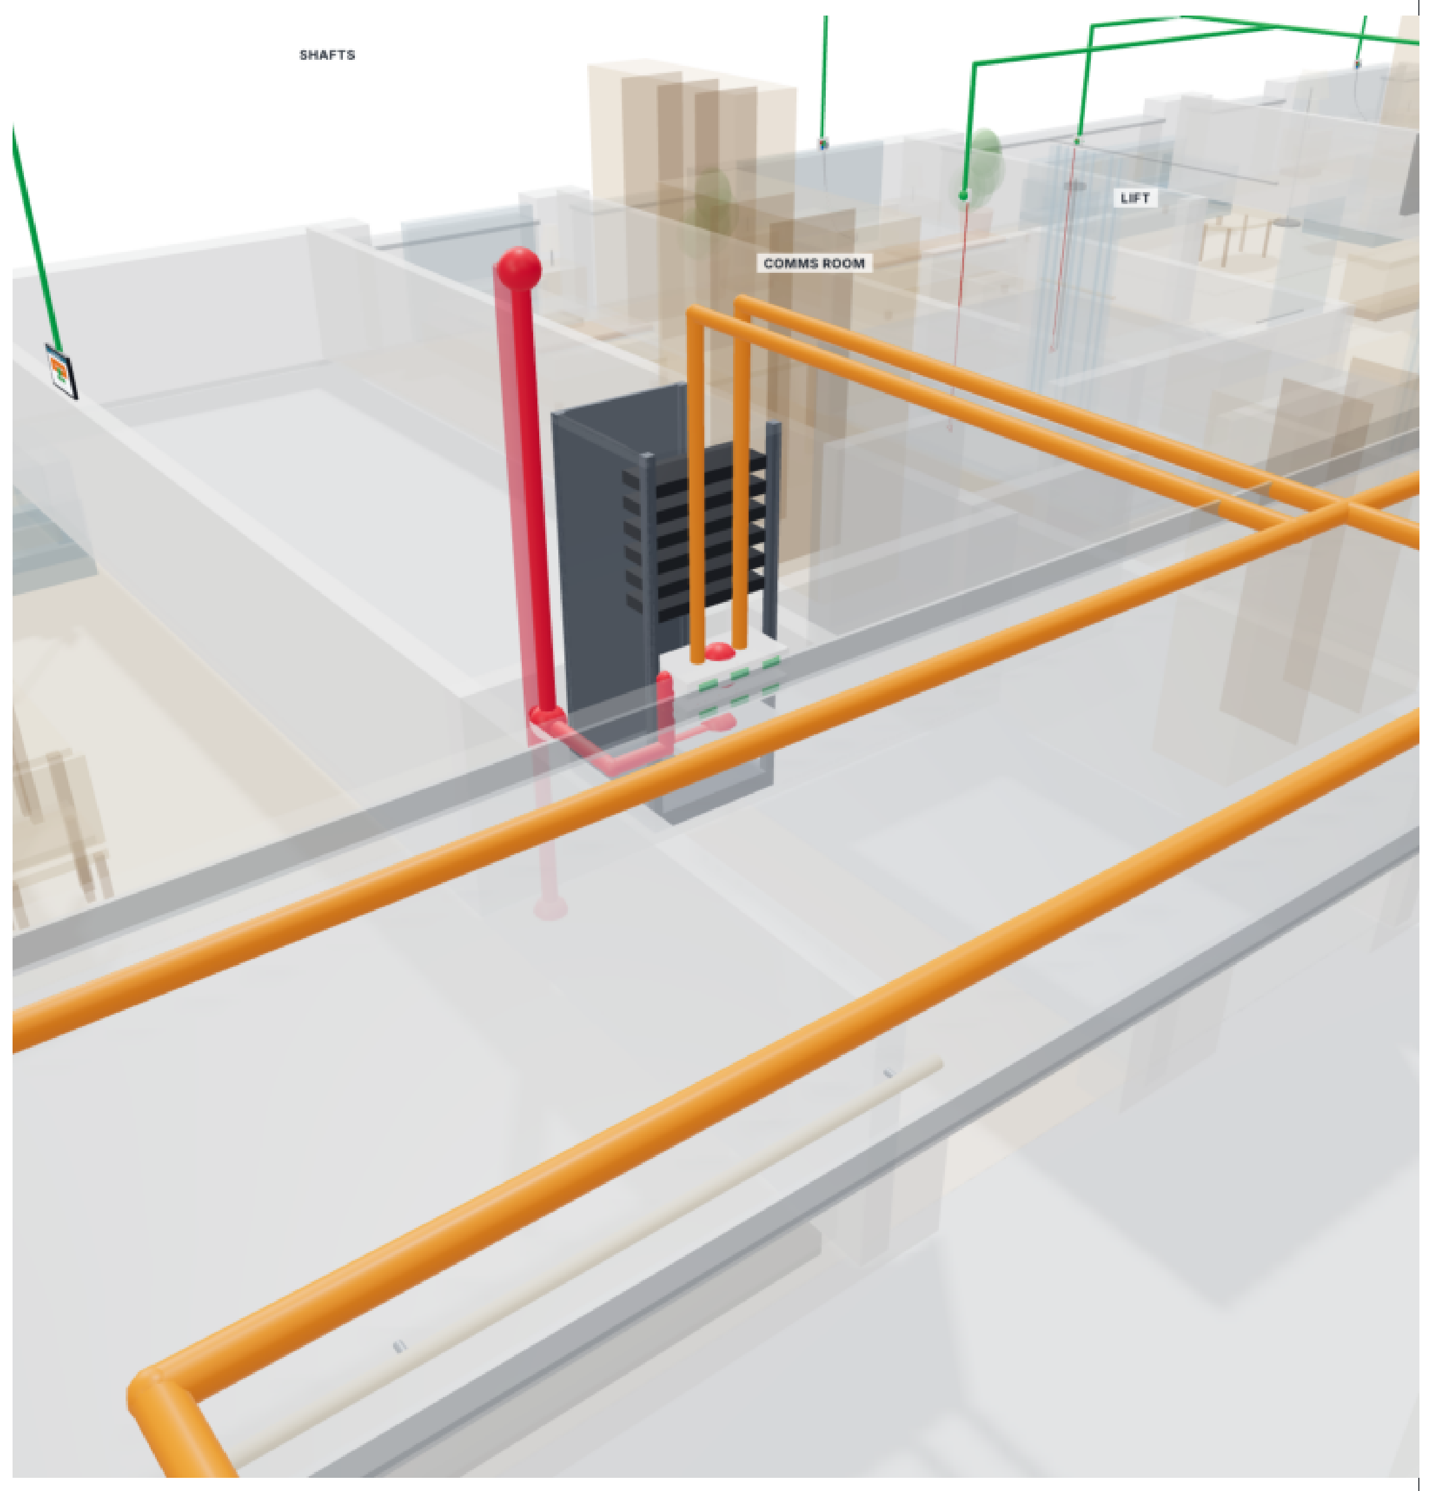

F · Floor comms room

MIGDALEI YAM A TIJON · ASSISTED LIVING
Nurse call system – GF + 6 floors · 36 apartments
System: ACE BG · Advantecnia Prepared by: Telab International

3D VIEWS – EQUIPMENT

3D VIEWS – EQUIPMENT

SCALE	DATE	REV	SHEET
NTS	**12/10/2026**	**A**	**06**

Dimensions in metres
A1 format · Rev. A – Preliminary design

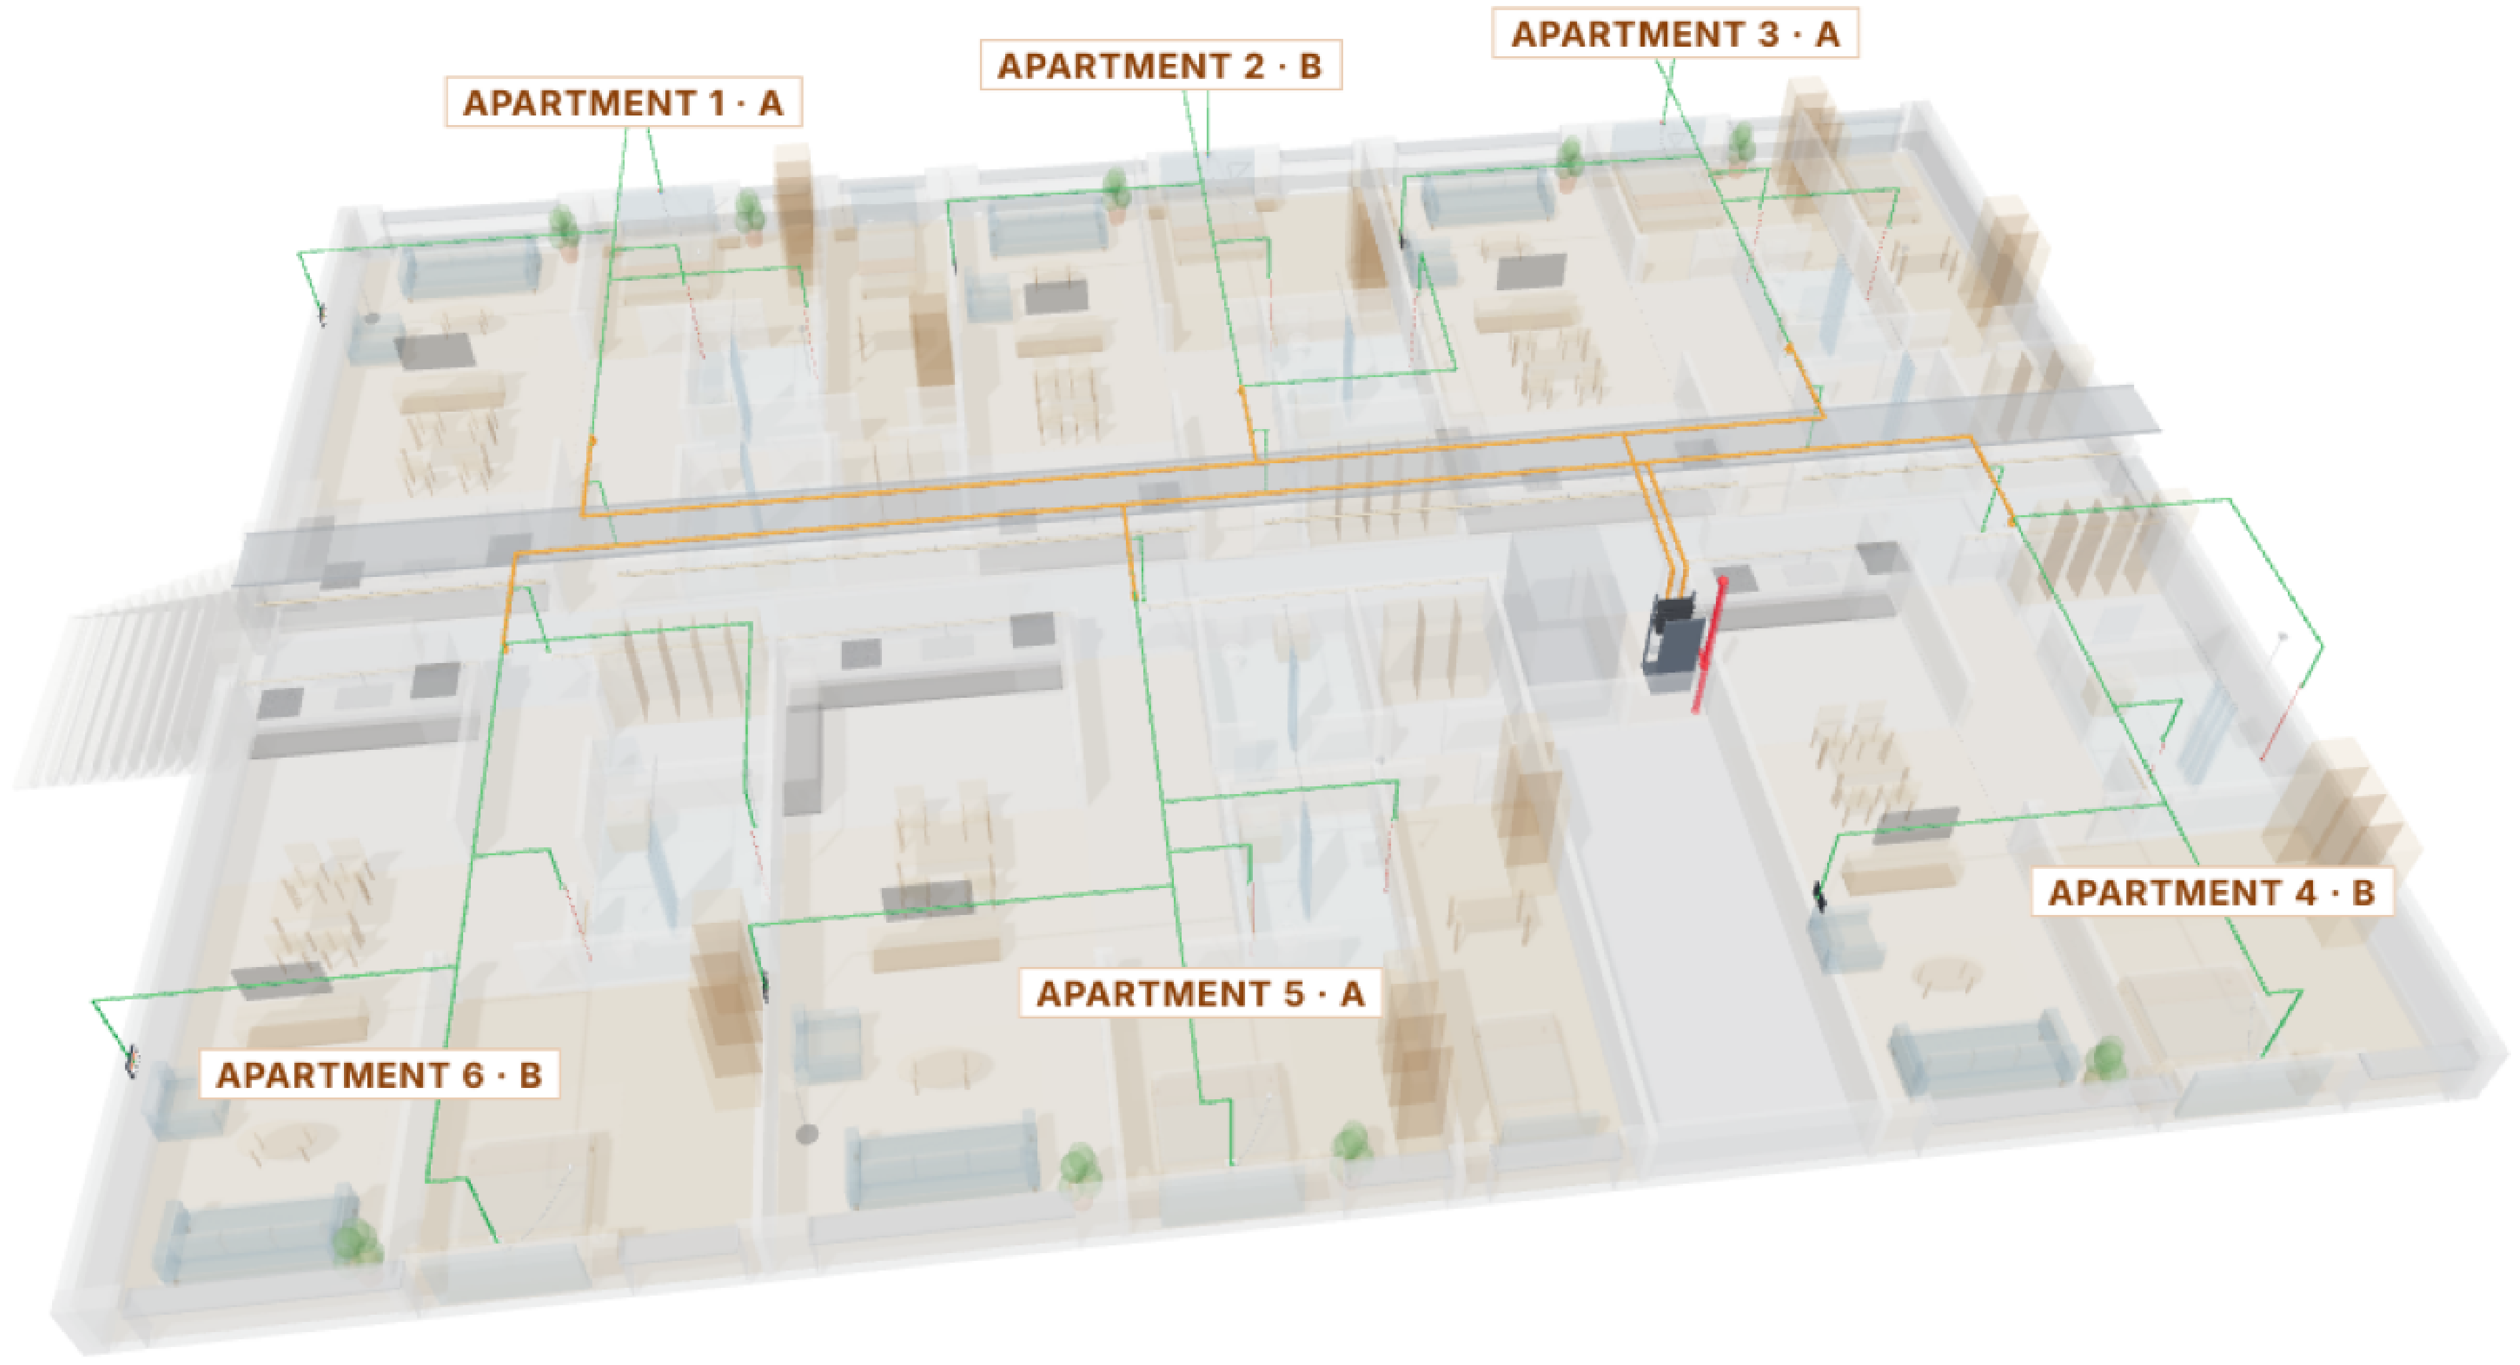

A · Floor tipo – cableado (verde radial · naranja cadena LCom · rojo red)

COLOURS

🟩 Cat6 radial: each apartment device → its LCom
Cat6 radial: each device → its LCom · Cat6 רדיאלי: כל התקן ← LCom

🟧 Cat6 / Cat7 chain: LCom → LCom → LCom → Buscomm (3 per Buscomm)
Cat6 / Cat7 chain: LCom → LCom → LCom → Buscomm · Cat6 / Cat7 שרשרת: LCom ← LCom ← Buscomm

🟥 Cat6A / Cat7 network: Buscomm → floor switch → riser → server (GF)
Cat6A / Cat7 network: Buscomm → floor switch → riser → server · Cat6A / Cat7 רשת: Buscomm ← מתג ← עמוד ← שרת

- - - Cat6 to the optional presence / cancel button
Cat6 to optional presence / cancel button · Cat6 ללחצן נוכחות אופציונלי

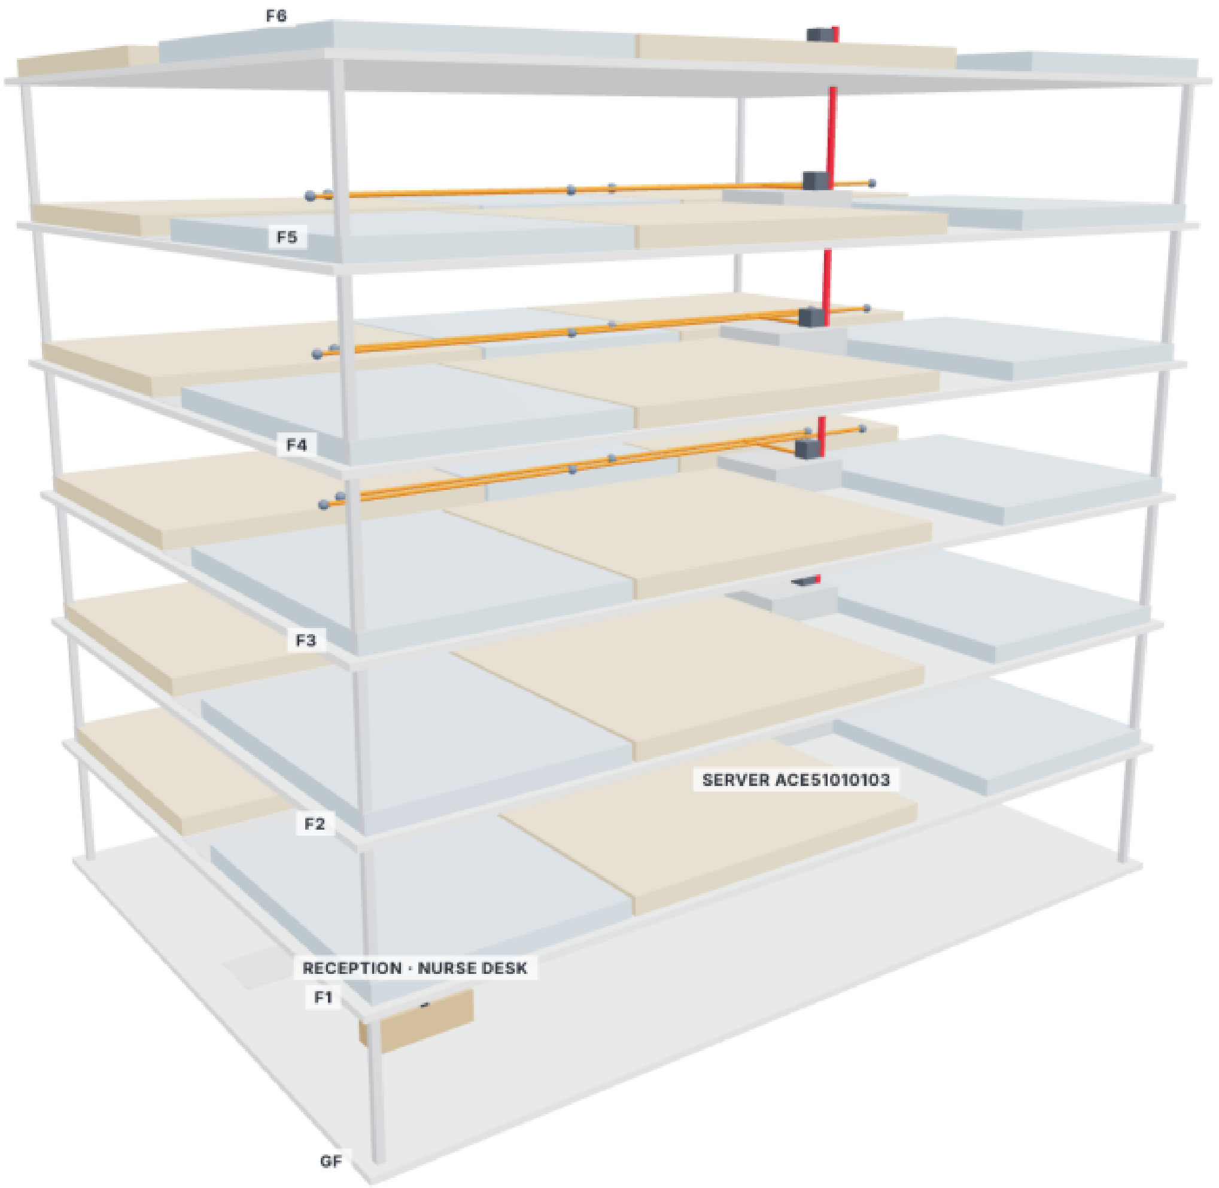

B · Building GF + 6 floors – riser

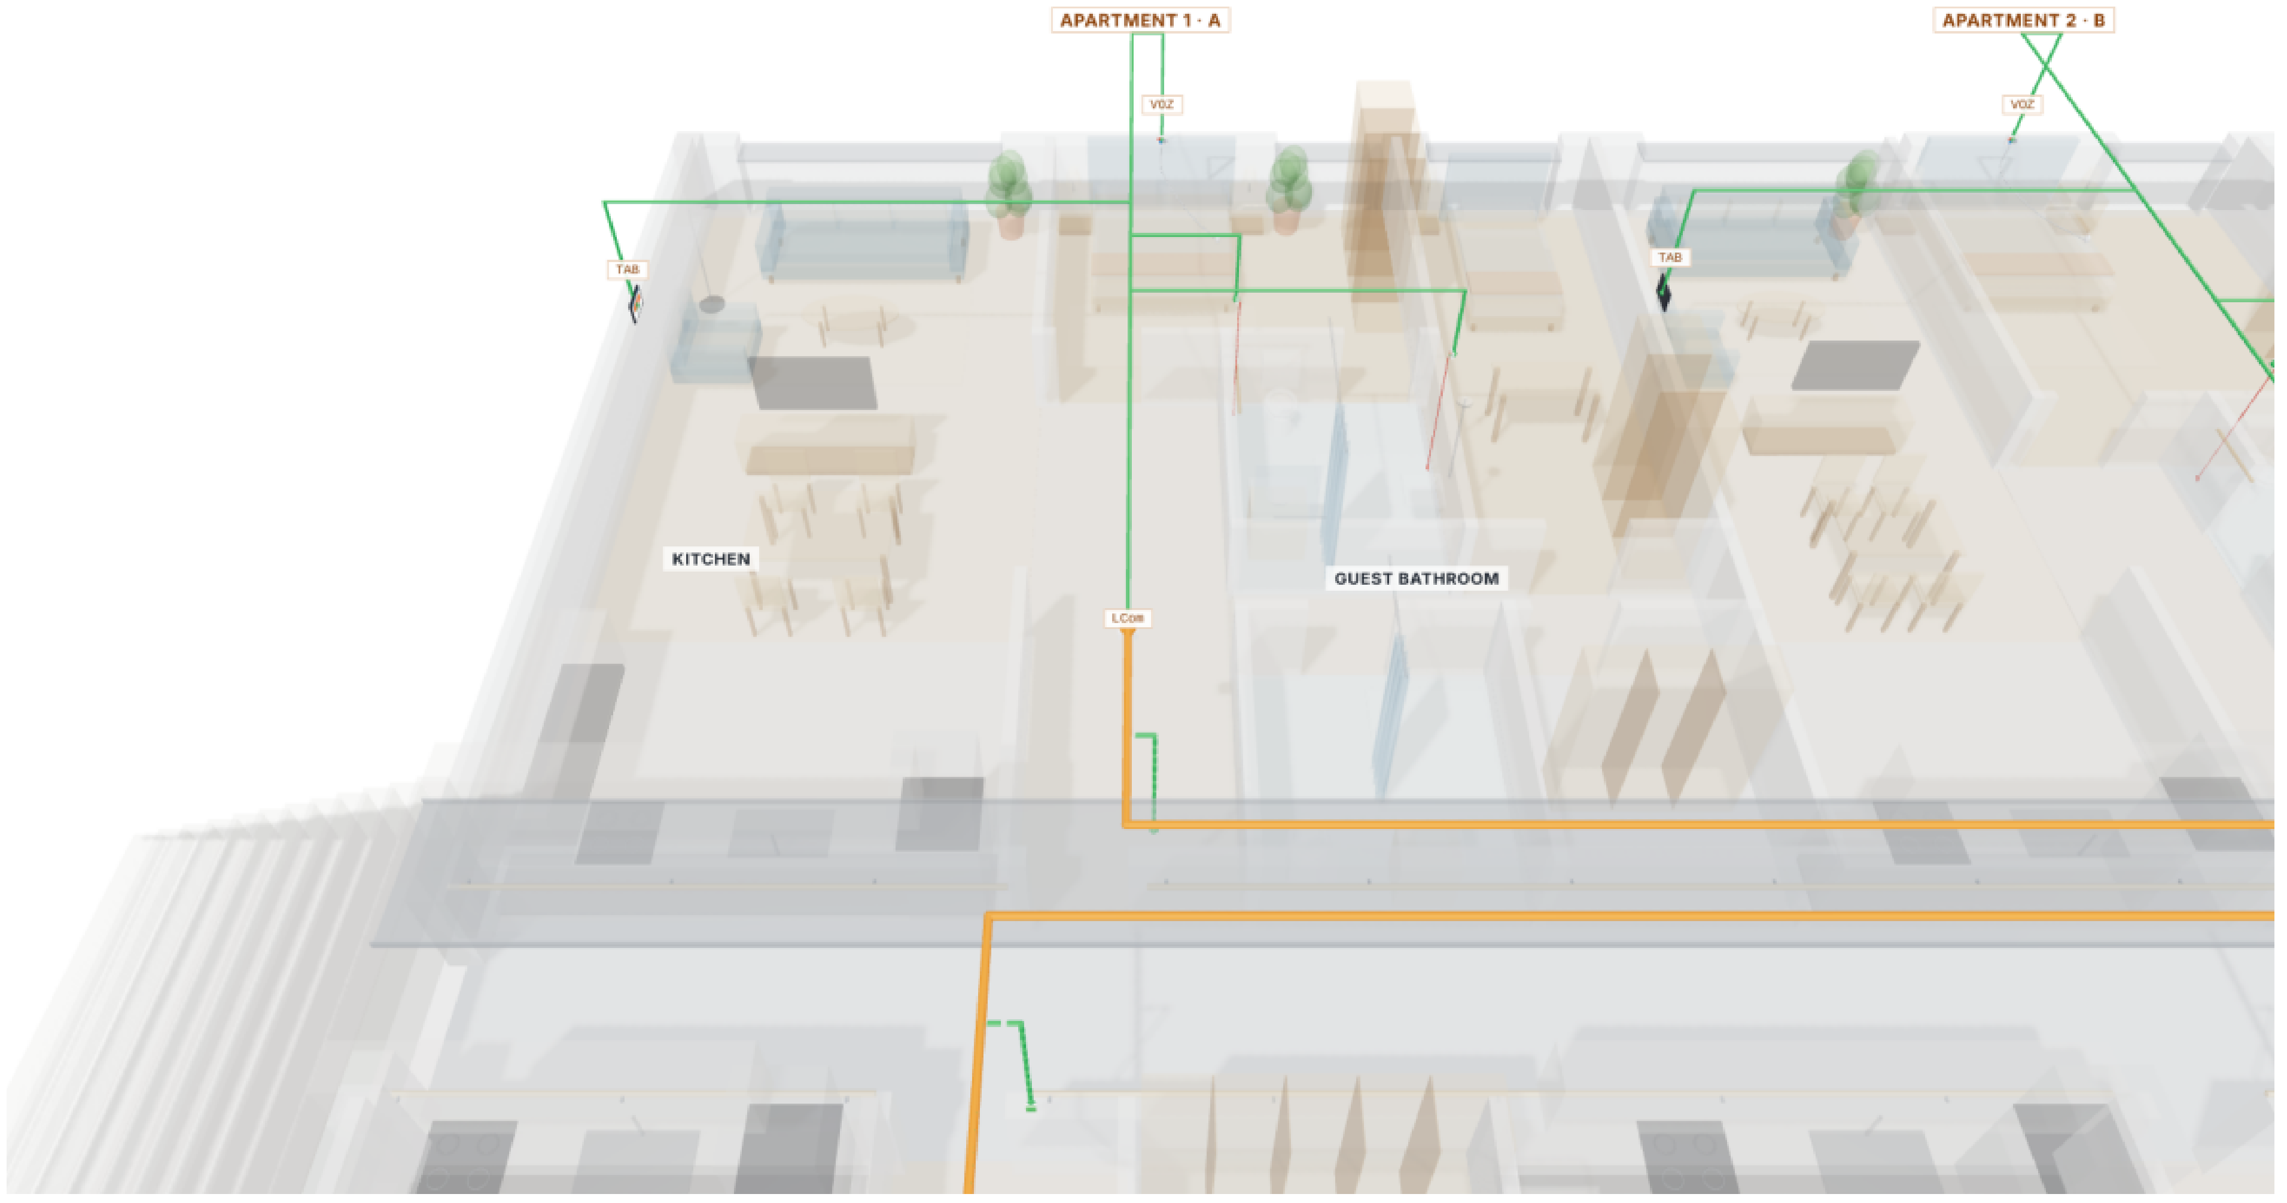

C · Type A apartment – radial to the LCom

MIGDALEI YAM A TIJON · ASSISTED LIVING
Nurse call system – GF + 6 floors · 36 apartments
System: ACE BG · Advantecnia Prepared by: Telab International

3D VIEWS – WIRING AND BUILDING

3D VIEWS – WIRING AND BUILDING

SCALE	DATE	REV	SHEET
NTS	**12/10/2026**	**A**	**07**
Dimensions in metres A1 format · Rev. A – Preliminary design			