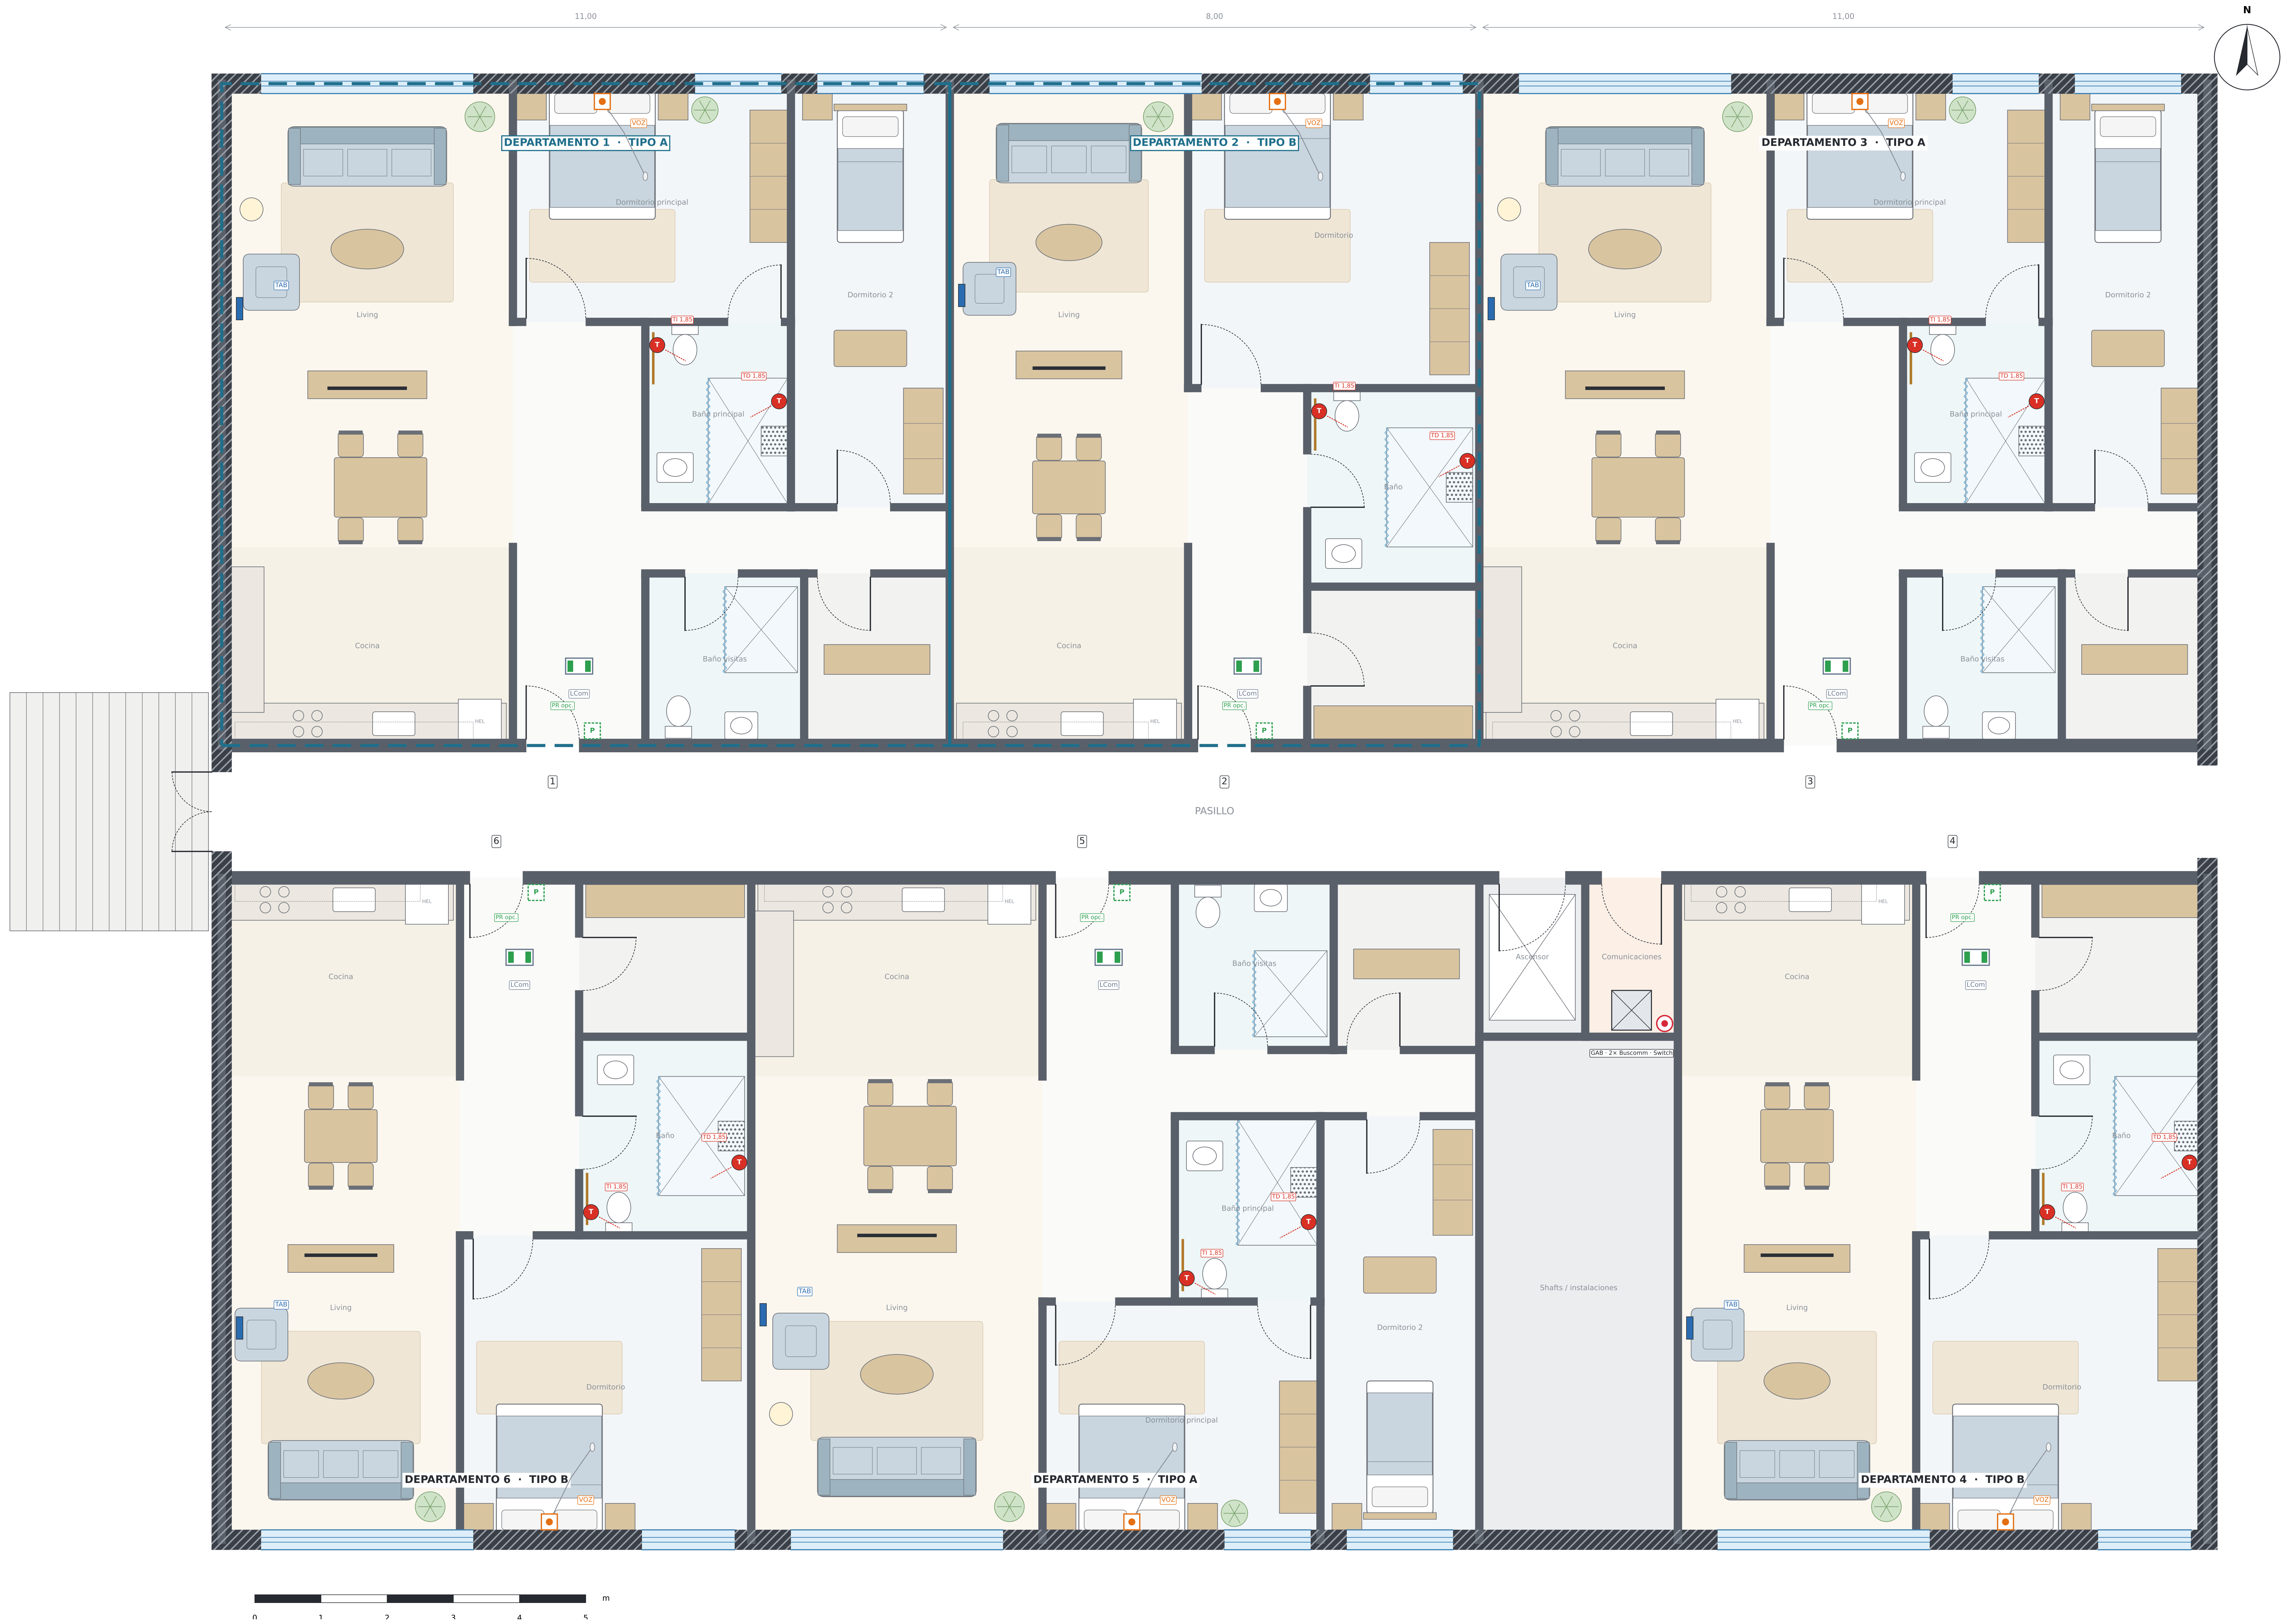

NOTAS · NOTES

1. Piso tipo: 6 departamentos intercalados (A-B-A al norte, B-A-B al sur). Se destacan el 1 (tipo A) y el 2 (tipo B).
2. Tipo A: living + cocina abierta, dormitorio principal con baño en suite (ducha + inodoro), dormitorio 2, baño de visitas con ducha, hall y depósito.
3. Tipo B: living + cocina abierta, un dormitorio y un baño con ducha.
4. Por departamento: tablet Android en el living, llamada con voz en el dormitorio principal y 2 tiradores (inodoro y ducha) en el baño principal.
5. Pulsador de presencia / cancelación junto a la puerta de entrada: opcional.
6. Sala de comunicaciones del piso junto al ascensor; escalera en el extremo oeste.
7. Mobiliario de vivienda (no hospitalario).

SÍMBOLOS · SYMBOLS · סמלים

🟦	TAB · Tablet Android en el living – llamada y voz Android tablet in the living room – call and voice · טאבלט אנדרואיד בסלון – קריאה ודיבור
T	TI / TD · Tirador inodoro / ducha ACE40320303W (baño principal, h 1,85 m) Toilet / shower pull-cord ACE40320303W (main bath, h 1.85 m) · משיכת חבל אסלה / מקלחת ACE40320303W
▮▮	LCom ACE71610003 · concentrador del departamento (cielorraso del hall) LCom ACE71610003 · apartment hub (hall ceiling) · LCom ACE71610003 · מרכז דירה (תקרת המבואה)
●	VOZ · Llamada de enfermería con voz ACE82182451 (dormitorio principal) Voice nurse call ACE82182451 (main bedroom) · קריאת אחות קולית ACE82182451 (חדר שינה ראשי)
P	PR · Presencia / cancelación junto a la puerta – OPCIONAL Presence / cancel next to the door – OPTIONAL · נוכחות / ביטול ליד הדלת – אופציונלי
GAB	Gabinete del piso: 2 Buscomm ACE70810000 + switch PoE ACEUCM6302 Floor rack: 2 Buscomm ACE70810000 + PoE switch ACEUCM6302 · ארון קומה: 2 Buscomm + מתג PoE

MIGDALEI YAM A TIJON · DEPARTAMENTOS TUTELADOS
Sistema de llamada de enfermería – PB + 6 pisos · 36 departamentos
Sistema: ACE BG · Advantecnia Elaboró: Telab International

PISO TIPO – EQUIPAMIENTO

Typical floor – equipment

ESCALA · SCALE	FECHA · DATE	REV	LÁMINA
1:60	**12/10/2026**	**A**	**01**

Cotas en metros · Dimensions in m · מידות במטרים
Formato A1 · Rev. A – Anteproyecto

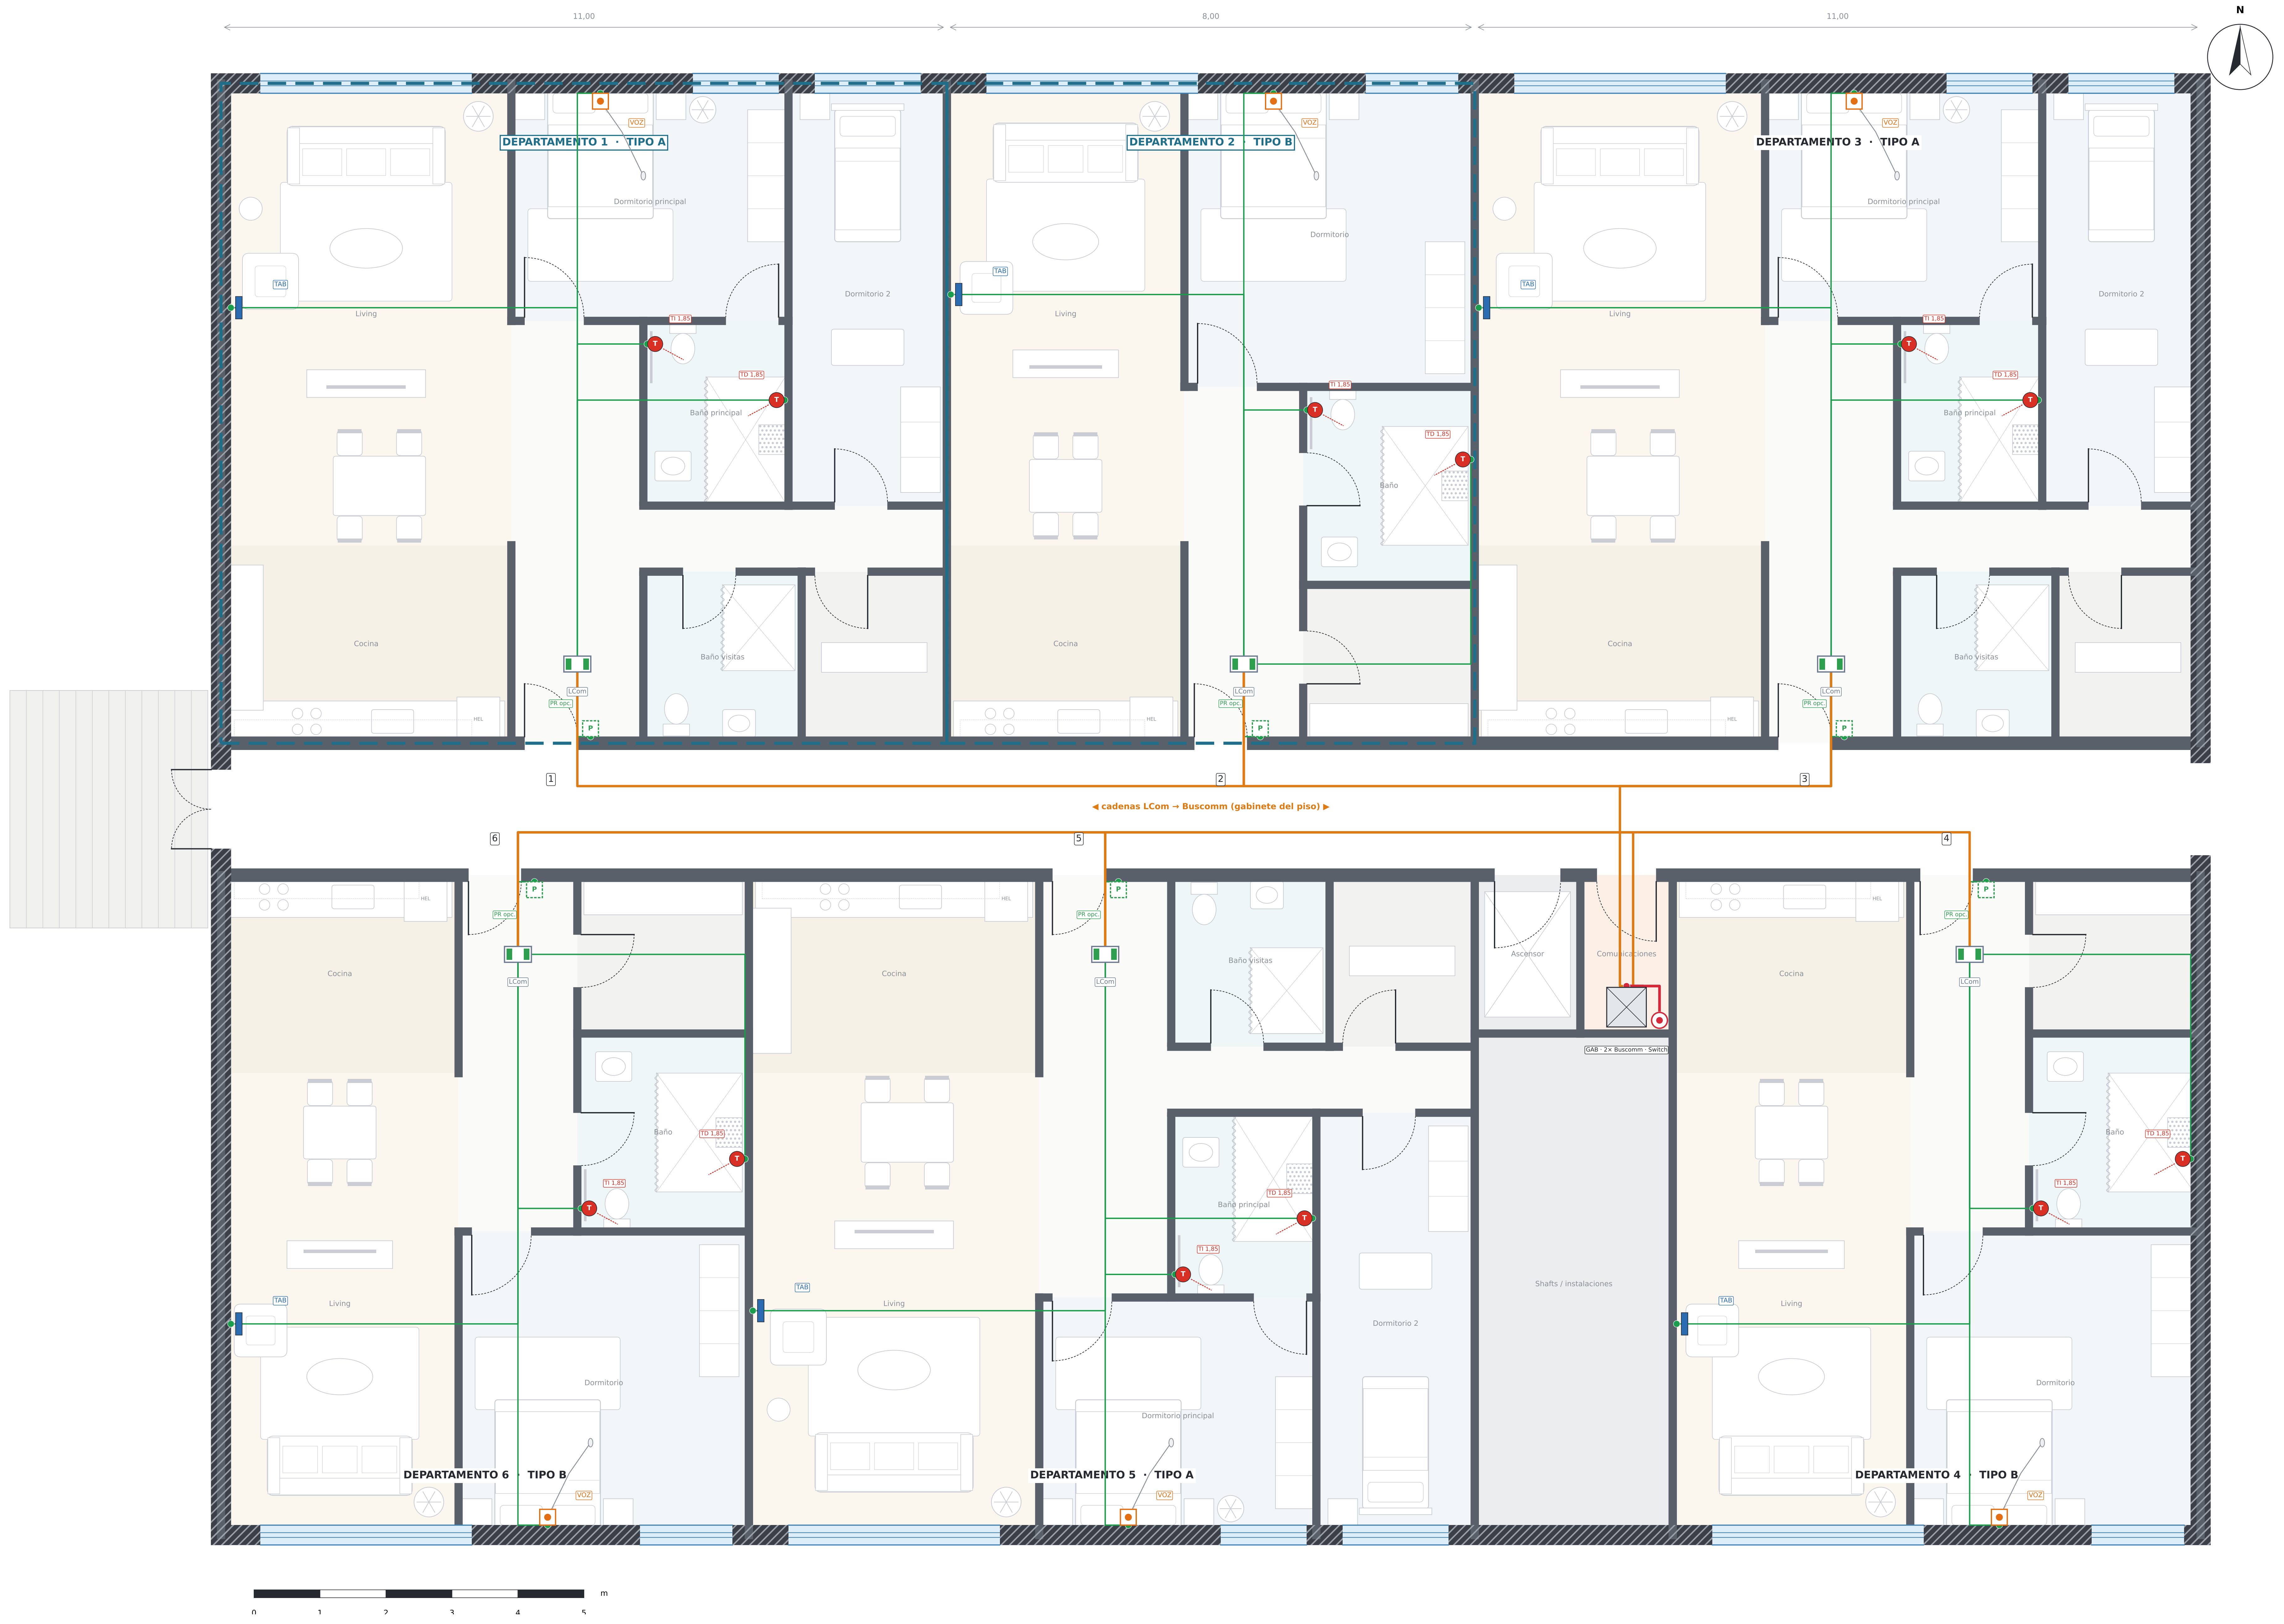

NOTAS · NOTES

1. Piso tipo: 6 departamentos intercalados (3 tipo A + 3 tipo B). Se destacan el 1 (A) y el 2 (B), detallados en las láminas 03 y 04.
2. Cada departamento tiene un LCom en el cielorraso del hall: todos sus elementos llegan en radial con Cat6.
3. Los LCom se encadenan de a 3 hasta una Buscomm: norte 1-2-3 → Buscomm 1, sur 4-5-6 → Buscomm 2.
4. Las 2 Buscomm y el switch PoE están en el gabinete de la sala de comunicaciones del piso, junto al ascensor.
5. Los switches de los 6 pisos se encadenan por el montante hasta el servidor de PB. Esquema vertical en lámina 05.
6. Todo el sistema es PoE: no requiere circuitos eléctricos en los departamentos.
7. Sin luz de pasillo. La llamada llega por voz / alarma al puesto de enfermería de la recepción (PB).

CABLEADO – TODO Cat6 / Cat7 Y PoE (sin electricidad para el sistema)

🟩 Cat6 radial: cada elemento del departamento → su LCom
Cat6 radial: each device → its LCom · Cat6 רדיאלי: כל התקן ← LCom

🟥 Cat6A / Cat7 red: Buscomm → switch del piso → montante → servidor (PB)
Cat6A / Cat7 network: Buscomm → floor switch → riser → server · Cat6A / Cat7 רשת: Buscomm ← מתג ← עמוד ← שרת

🟧 Cat6 / Cat7 en cadena: LCom → LCom → LCom → Buscomm (3 por Buscomm)
Cat6 / Cat7 chain: LCom → LCom → LCom → Buscomm · Cat6 / Cat7 שרשרת: LCom ← LCom ← Buscomm

- - - Cat6 al pulsador opcional de presencia / cancelación
Cat6 to optional presence / cancel button · Cat6 ללחצן נוכחות אופציונלי

SÍMBOLOS · SYMBOLS · סמלים

TAB · Tablet Android en el living – llamada y voz
Android tablet in the living room – call and voice · טאבלט אנדרואיד בסלון – קריאה ודיבור

T TI / TD · Tirador inodoro / ducha ACE40320303W (baño principal, h 1,85 m)
Toilet / shower pull-cord ACE40320303W (main bath, h 1.85 m) · משיכת חבל אסלה / מקלחת ACE40320303W

LCom ACE71610003 · concentrador del departamento (cielorraso del hall)
LCom ACE71610003 · apartment hub (hall ceiling) · LCom ACE71610003 · רכזת דירה (תקרת המבואה)

● VOZ · Llamada de enfermería con voz ACE82182451 (dormitorio principal)
Voice nurse call ACE82182451 (main bedroom) · קריאת אחות קולית ACE82182451 (חדר שינה ראשי)

P PR · Presencia / cancelación junto a la puerta – OPCIONAL
Presence / cancel next to the door – OPTIONAL · נוכחות / ביטול ליד הדלת – אופציונלי

GAB Gabinete del piso: 2 Buscomm ACE70810000 + switch PoE ACEUCM6302
Floor rack: 2 Buscomm ACE70810000 + PoE switch ACEUCM6302 · ארון קומה: 2 Buscomm + מתג PoE

MIGDALEI YAM A TIJON · DEPARTAMENTOS TUTELADOS
Sistema de llamada de enfermería – PB + 6 pisos · 36 departamentos
Sistema: ACE BG · Advantecnia   Elaboró: Telab International

PISO TIPO – CABLEADO

Typical floor – wiring

ESCALA · SCALE	FECHA · DATE	REV	LÁMINA
1:60	12/10/2026	A	02

Cotas en metros · Dimensions in m · מידות במטרים
Formato A1 · Rev. A – Anteproyecto

A · EQUIPAMIENTO · 1:50

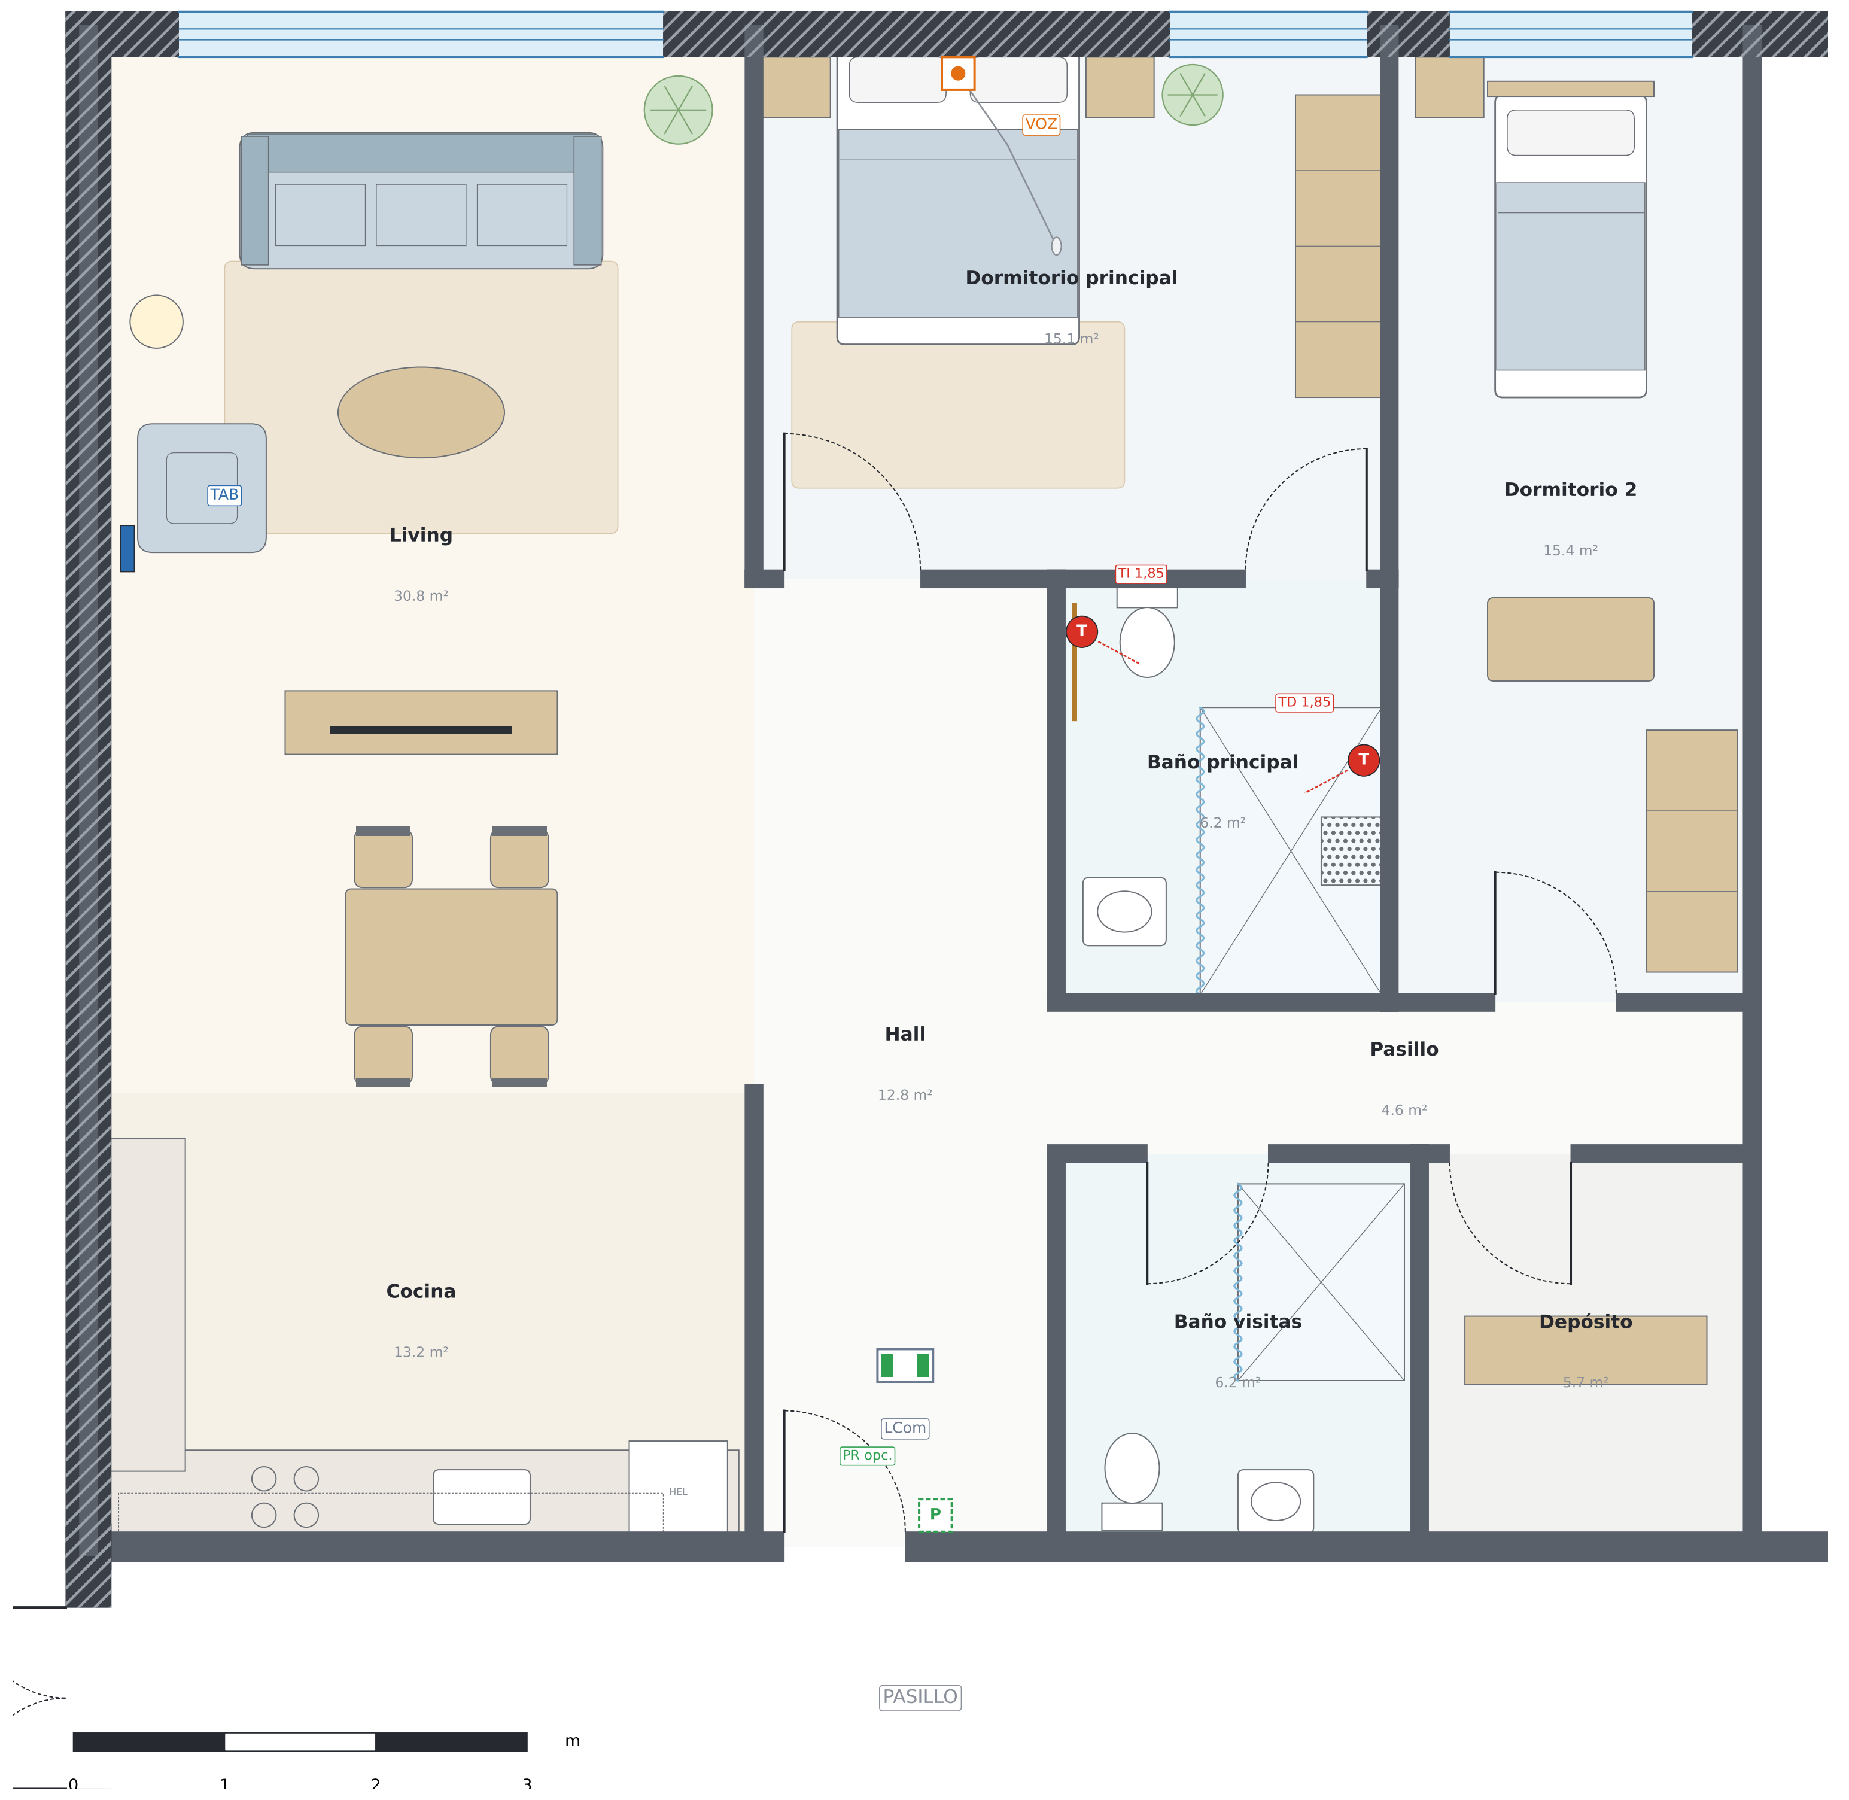

B · CABLEADO · 1:50

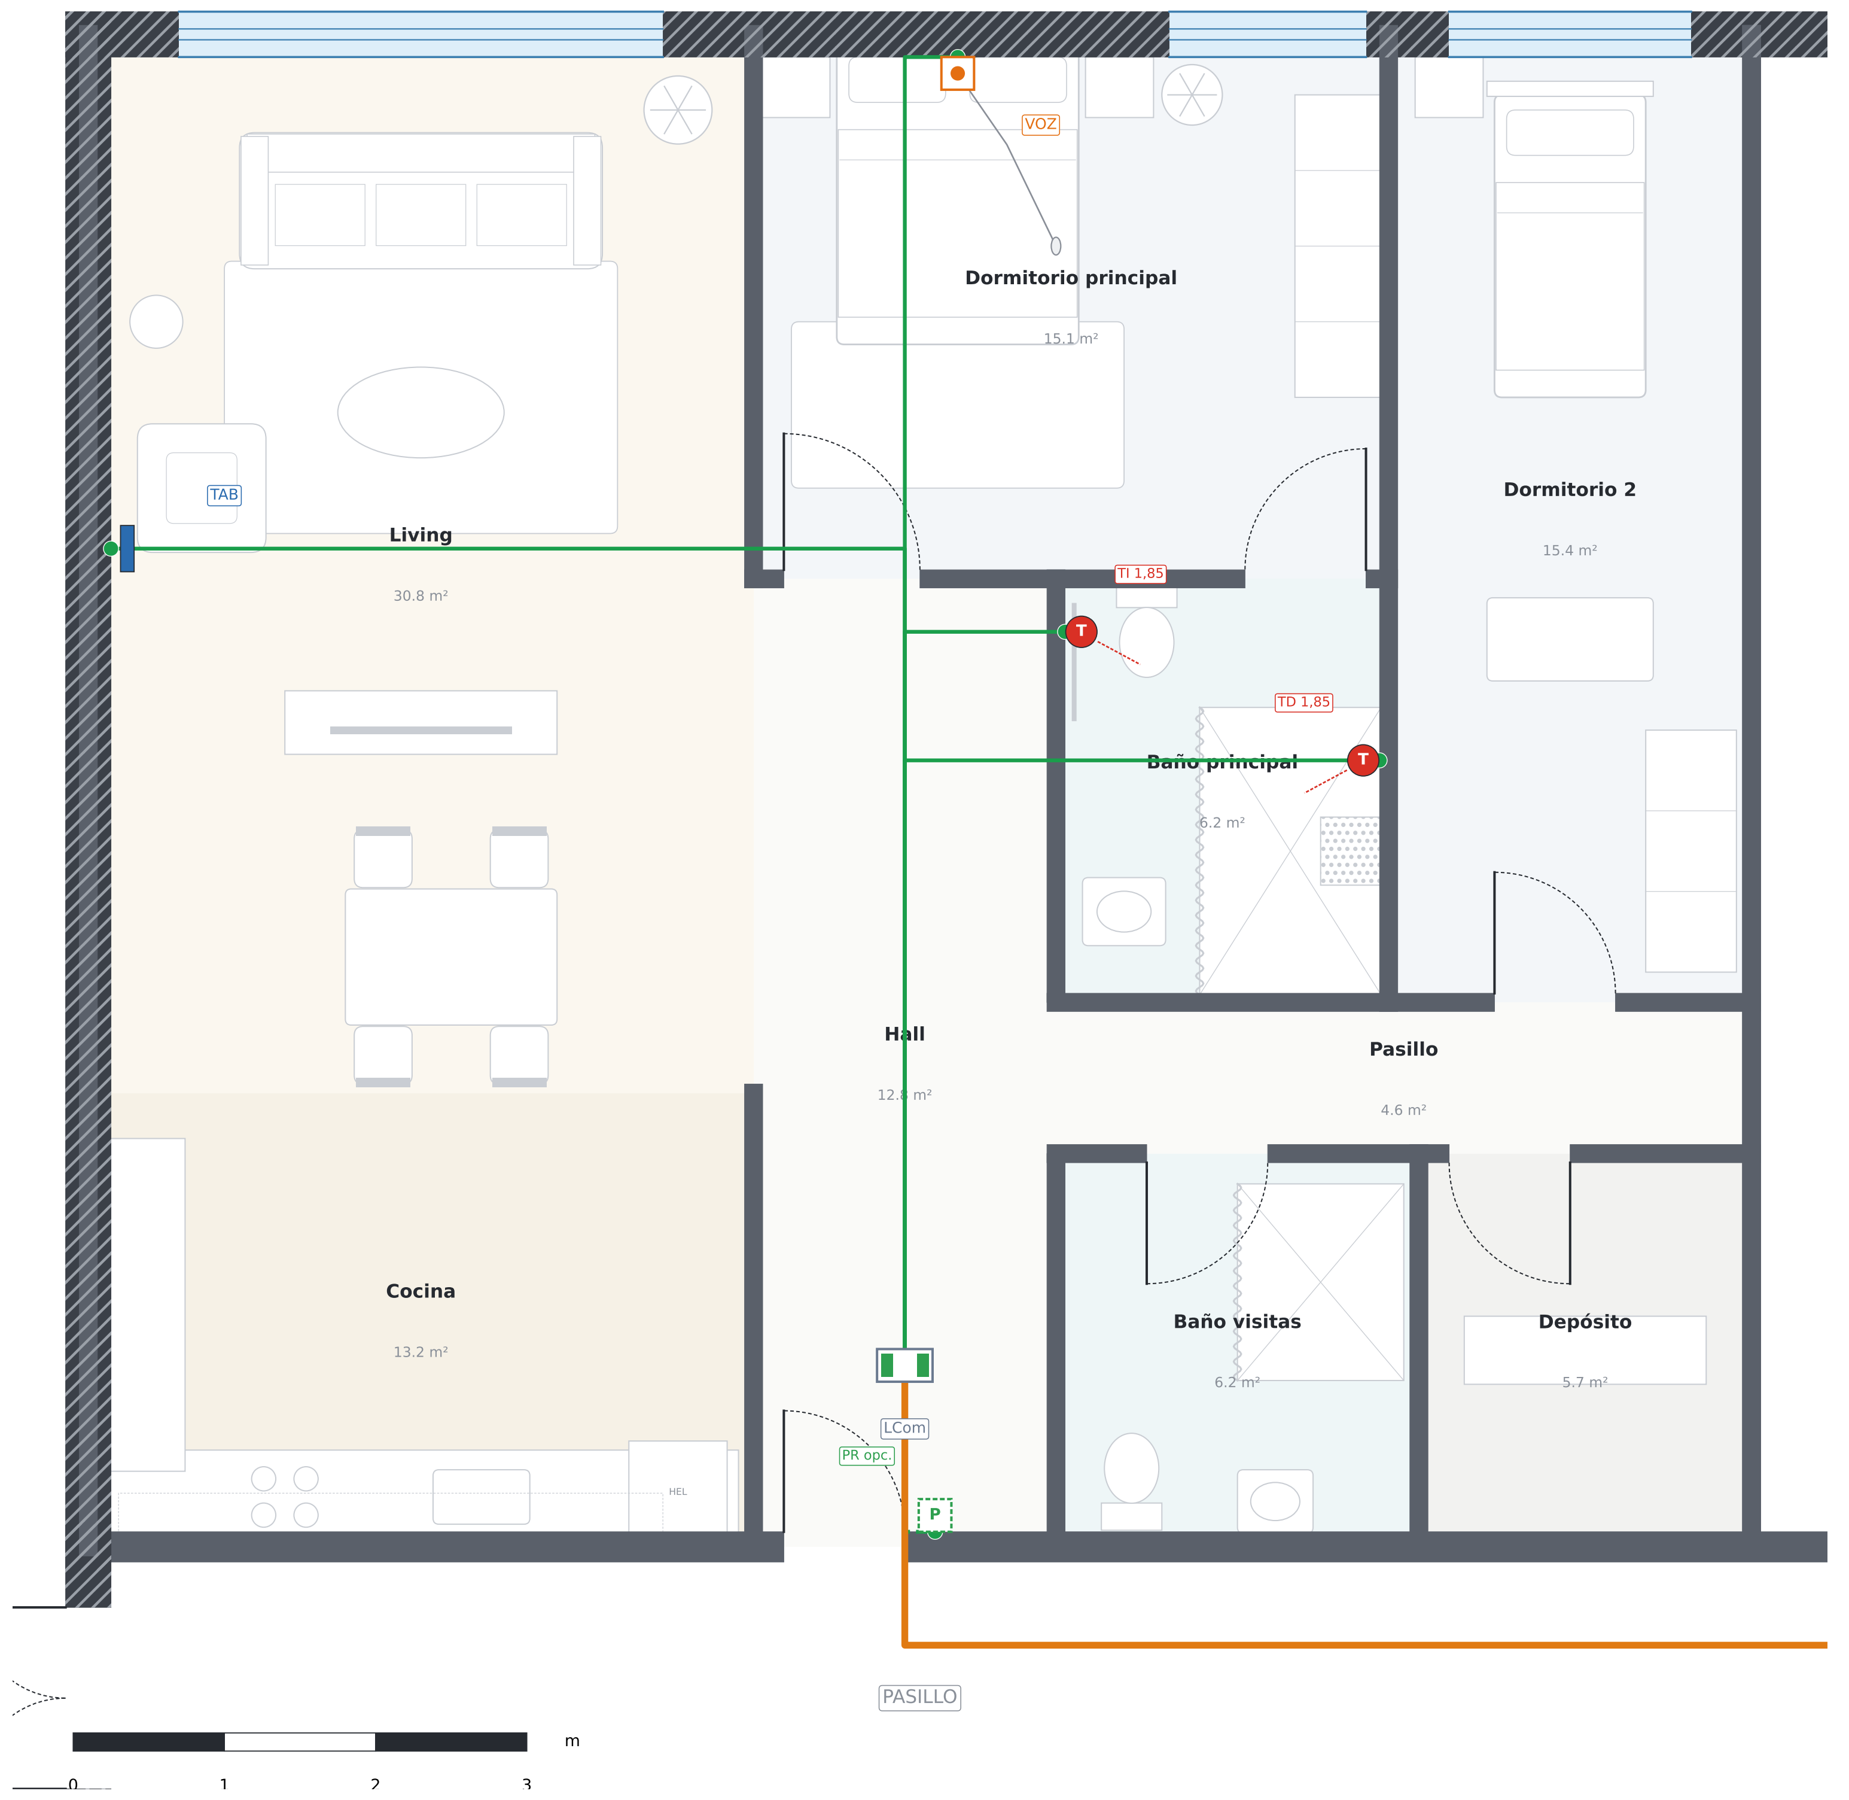

NOTAS · NOTES

1. Departamento 1 – tipo A, aprox. 110 m².
2. Living con cocina integrada; baño de visitas con ducha al lado del living.
3. Dormitorio principal con baño en suite (ducha + inodoro) y dormitorio 2.
4. Llamada: tablet Android en el living, llamada con voz en el dormitorio principal, tiradores en inodoro y ducha del baño principal.
5. Pulsador de presencia / cancelación junto a la puerta: opcional (punteado).
6. Todo en Cat6 radial al LCom del hall; el LCom sigue la cadena hacia la Buscomm del piso. Todo PoE.

C · ALTURAS DE MONTAJE (alzado esquemático)

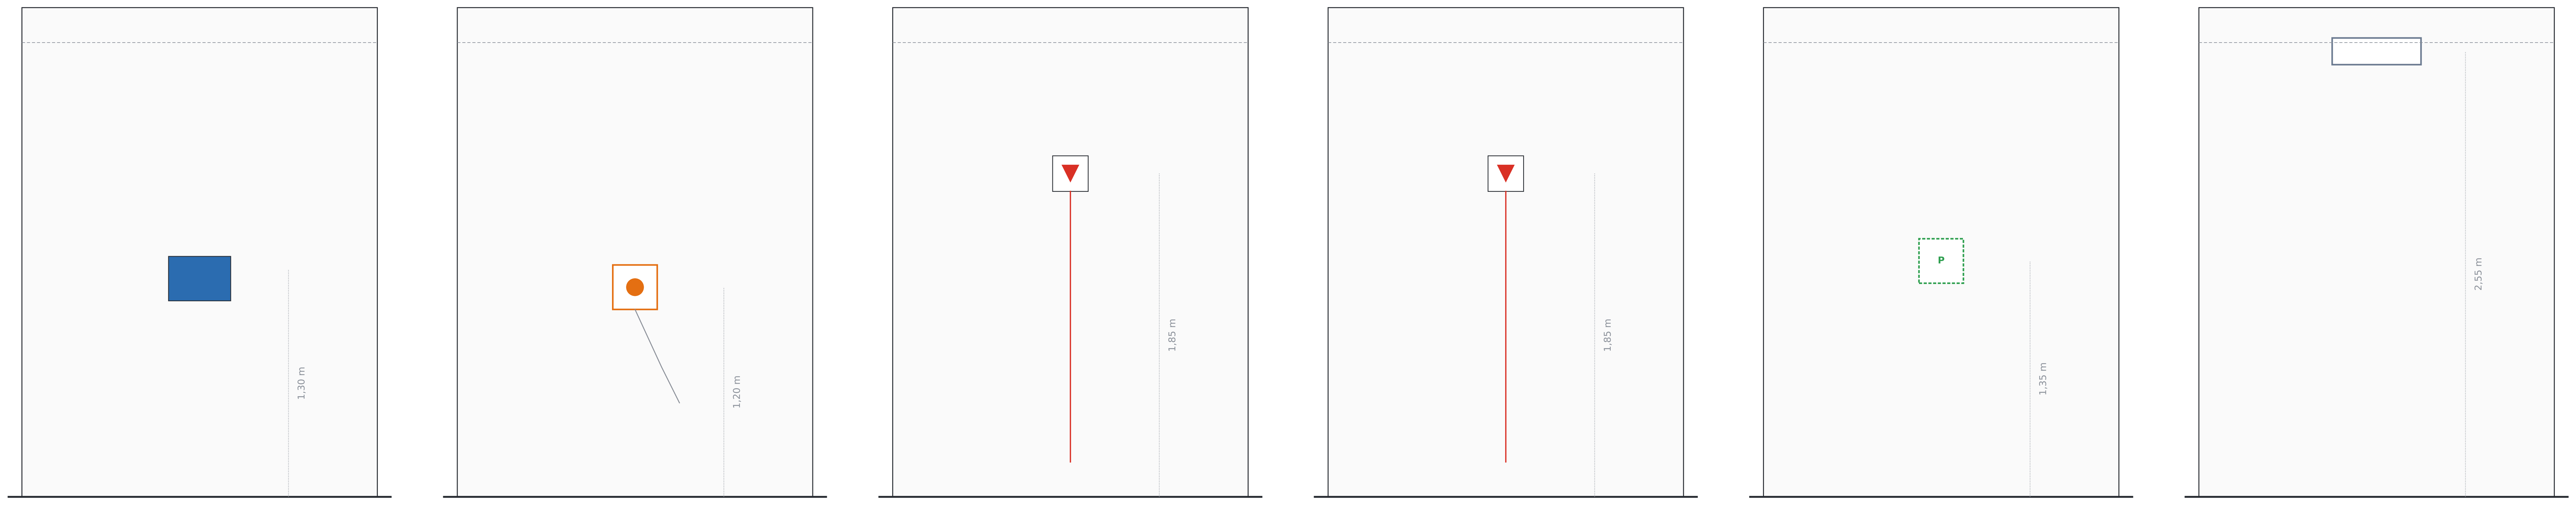

Living – tablet · Dormitorio – llamada con voz · Baño – tirador inodoro · Baño – tirador ducha · Entrada – presencia (opc.) · Hall – LCom (cielorraso)

SÍMBOLOS Y CABLEADO · SYMBOLS & WIRING

- 🟦 TAB · Tablet Android en el living – llamada y voz
  Android tablet in the living room – call and voice · טאבלט אנדרואיד בסלון – קריאה ודיבור
- 🔴 TI / TD · Tirador inodoro / ducha ACE40320303W (baño principal, h 1,85 m)
  Toilet / shower pull-cord ACE40320303W (main bath, h 1.85 m) · משיכת חבל אסלה / מקלחת ACE40320303W
- ▮▮ LCom ACE71610003 · concentrador del departamento (cielorraso del hall)
  LCom ACE71610003 · apartment hub (hall ceiling) · LCom ACE71610003 · מרכז דירה (תקרת המבואה)
- ━ Cat6 / Cat7 en cadena: LCom → LCom → LCom → Buscomm (3 por Buscomm)
  Cat6 / Cat7 chain: LCom → LCom → LCom → Buscomm · Cat6 / Cat7 שרשרת: LCom ← LCom ← Buscomm
- ● VOZ · Llamada de enfermería con voz ACE82182451 (dormitorio principal)
  Voice nurse call ACE82182451 (main bedroom) · קריאת אחות קולית ACE82182451 (חדר שינה ראשי)
- P PR · Presencia / cancelación junto a la puerta – OPCIONAL
  Presence / cancel next to the door – OPTIONAL · נוכחות / ביטול ליד הדלת – אופציונלי
- ━ Cat6 radial: cada elemento del departamento → su LCom
  Cat6 radial: each device → its LCom · Cat6 רדיאלי: כל התקן ← LCom
- ╍ Cat6 al pulsador opcional de presencia / cancelación
  Cat6 to optional presence / cancel button · Cat6 ללחצן נוכחות אופציונלי

MIGDALEI YAM A TIJON · DEPARTAMENTOS TUTELADOS
Sistema de llamada de enfermería – PB + 6 pisos · 36 departamentos
Sistema: ACE BG · Advantecnia Elaboró: Telab International

DEPARTAMENTO TIPO A – DETALLE

Apartment type A – detail

ESCALA · SCALE	FECHA · DATE	REV	LÁMINA
1:50	**12/10/2026**	**A**	**03**

Cotas en metros · Dimensions in m · מידות במטרים
Formato A1 · Rev. A – Anteproyecto

A · EQUIPAMIENTO · 1:45

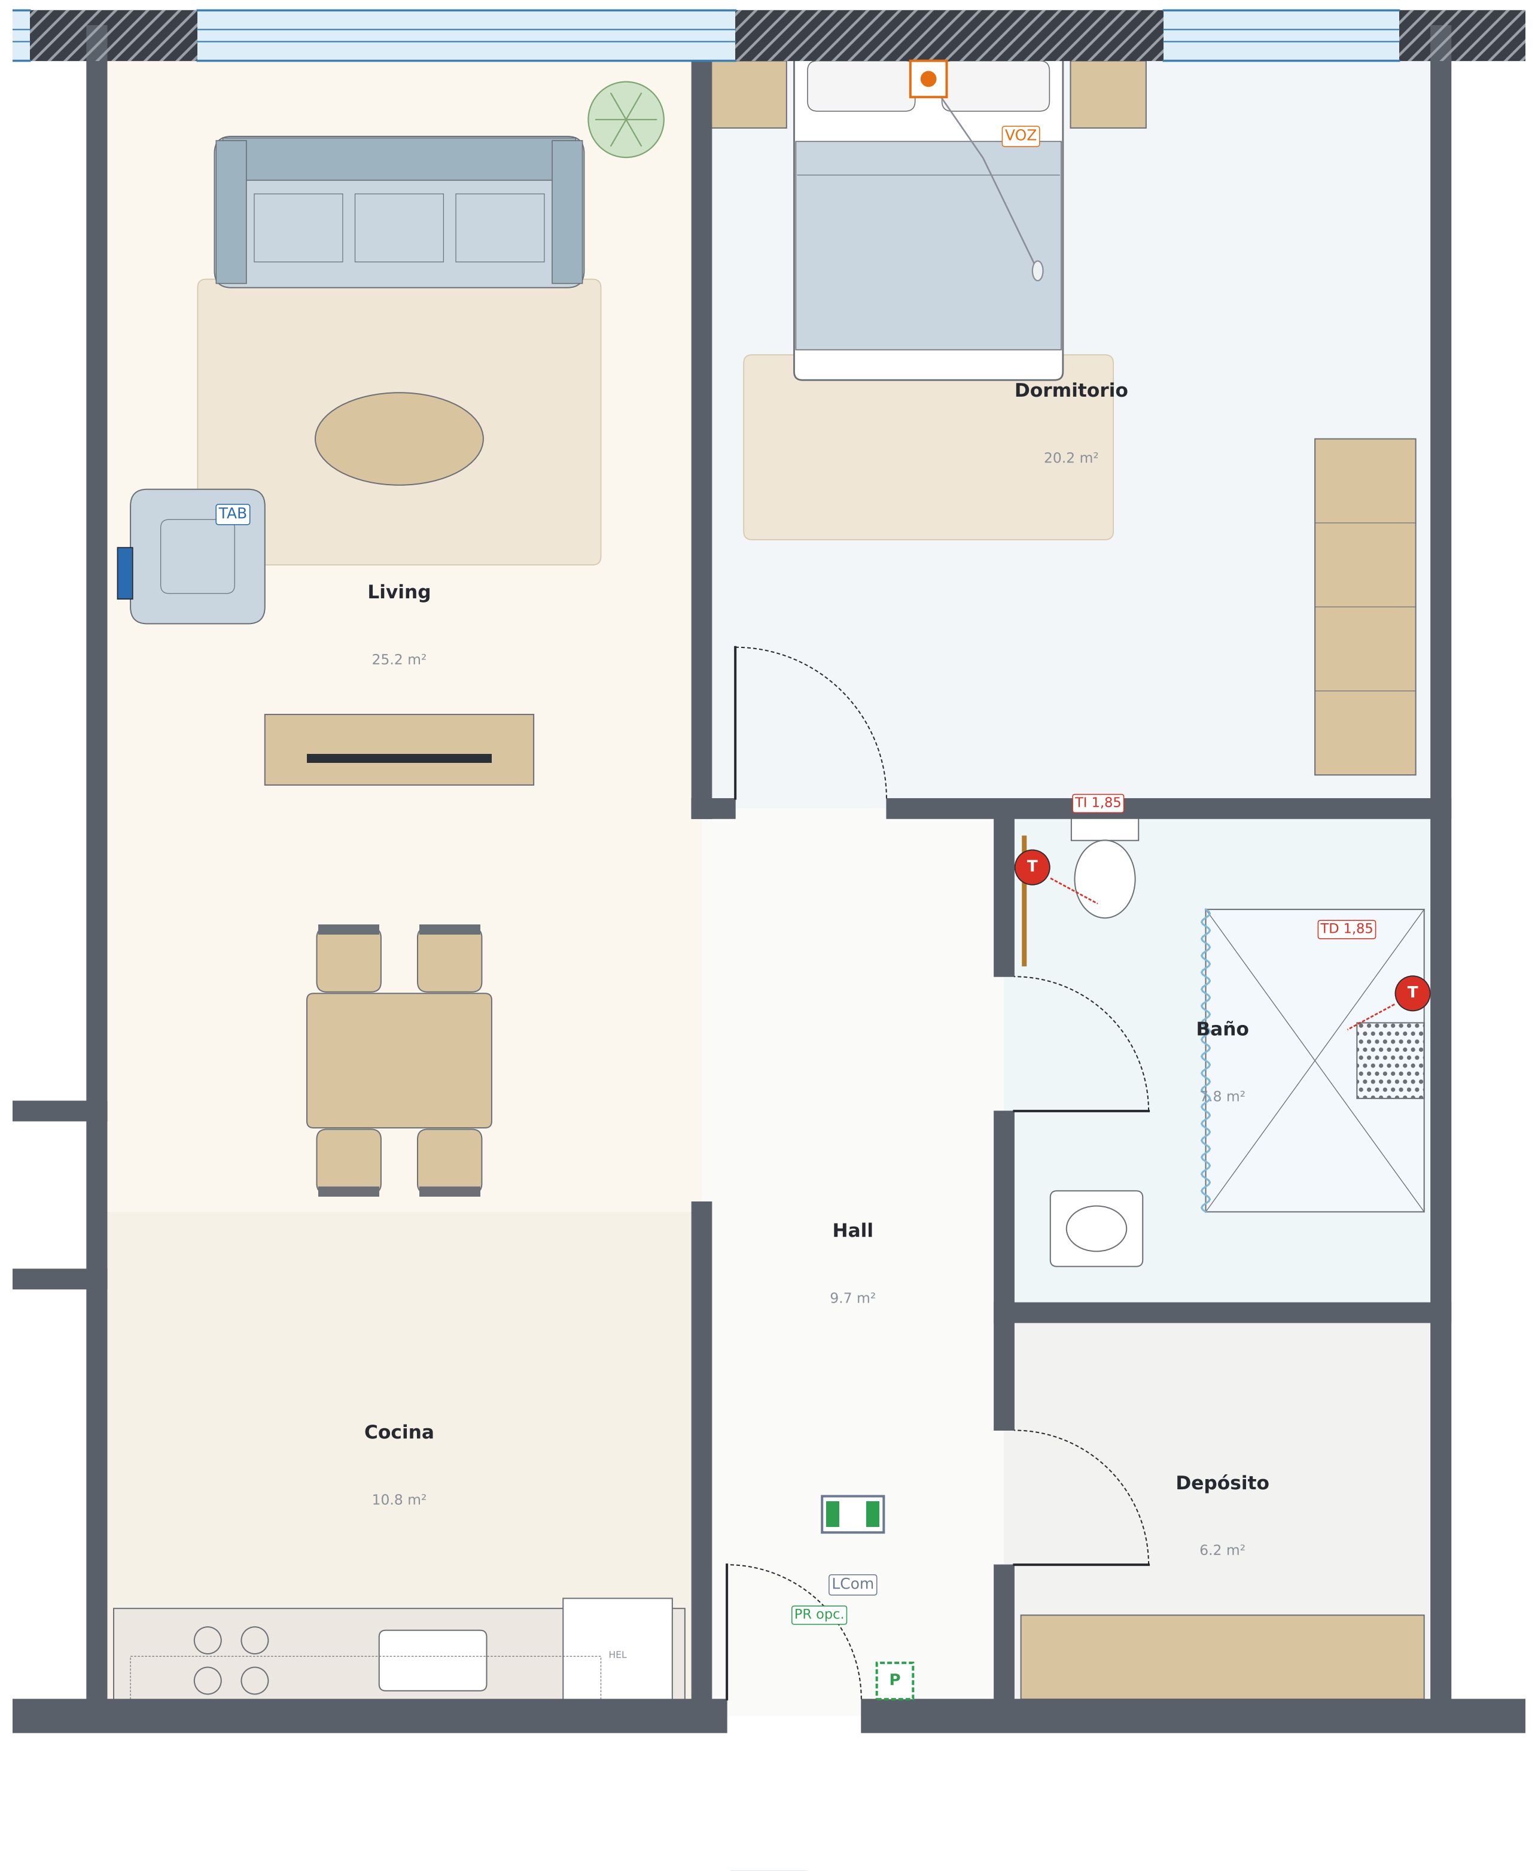

B · CABLEADO · 1:45

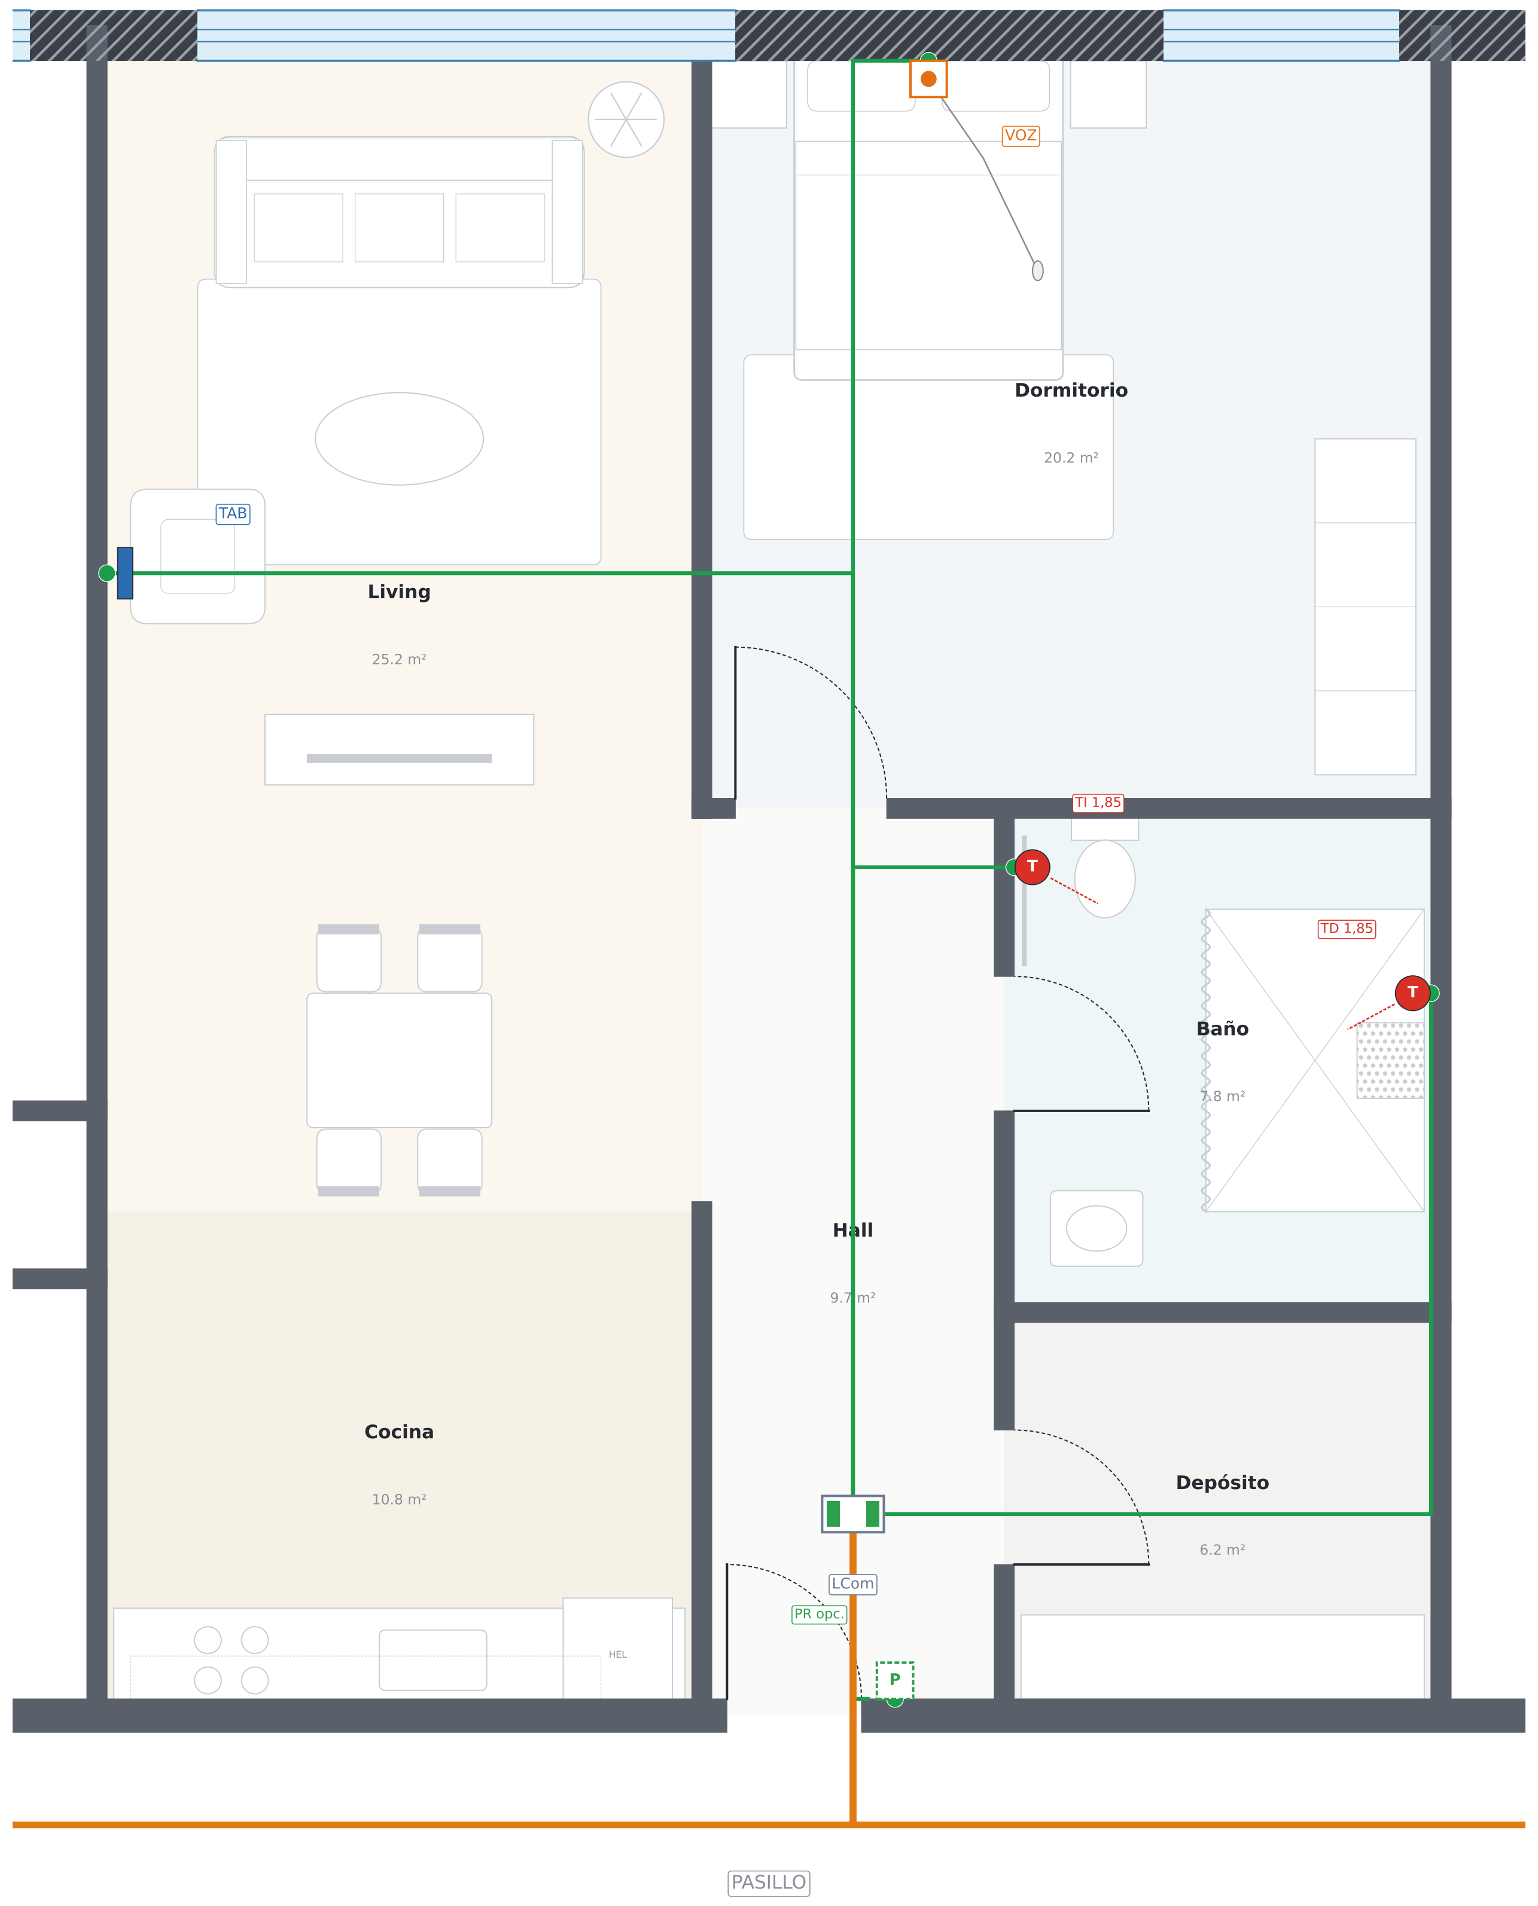

NOTAS · NOTES

1. Departamento 2 – tipo B, aprox. 80 m².
2. Living con cocina integrada, un dormitorio y un baño con ducha.
3. Llamada: tablet Android en el living, llamada con voz en el dormitorio, tiradores en inodoro y ducha.
4. Pulsador de presencia / cancelación junto a la puerta: opcional (punteado).
5. Todo en Cat6 radial al LCom del hall; el LCom sigue la cadena hacia la Buscomm del piso. Todo PoE.

C · ALTURAS DE MONTAJE (alzado esquemático)

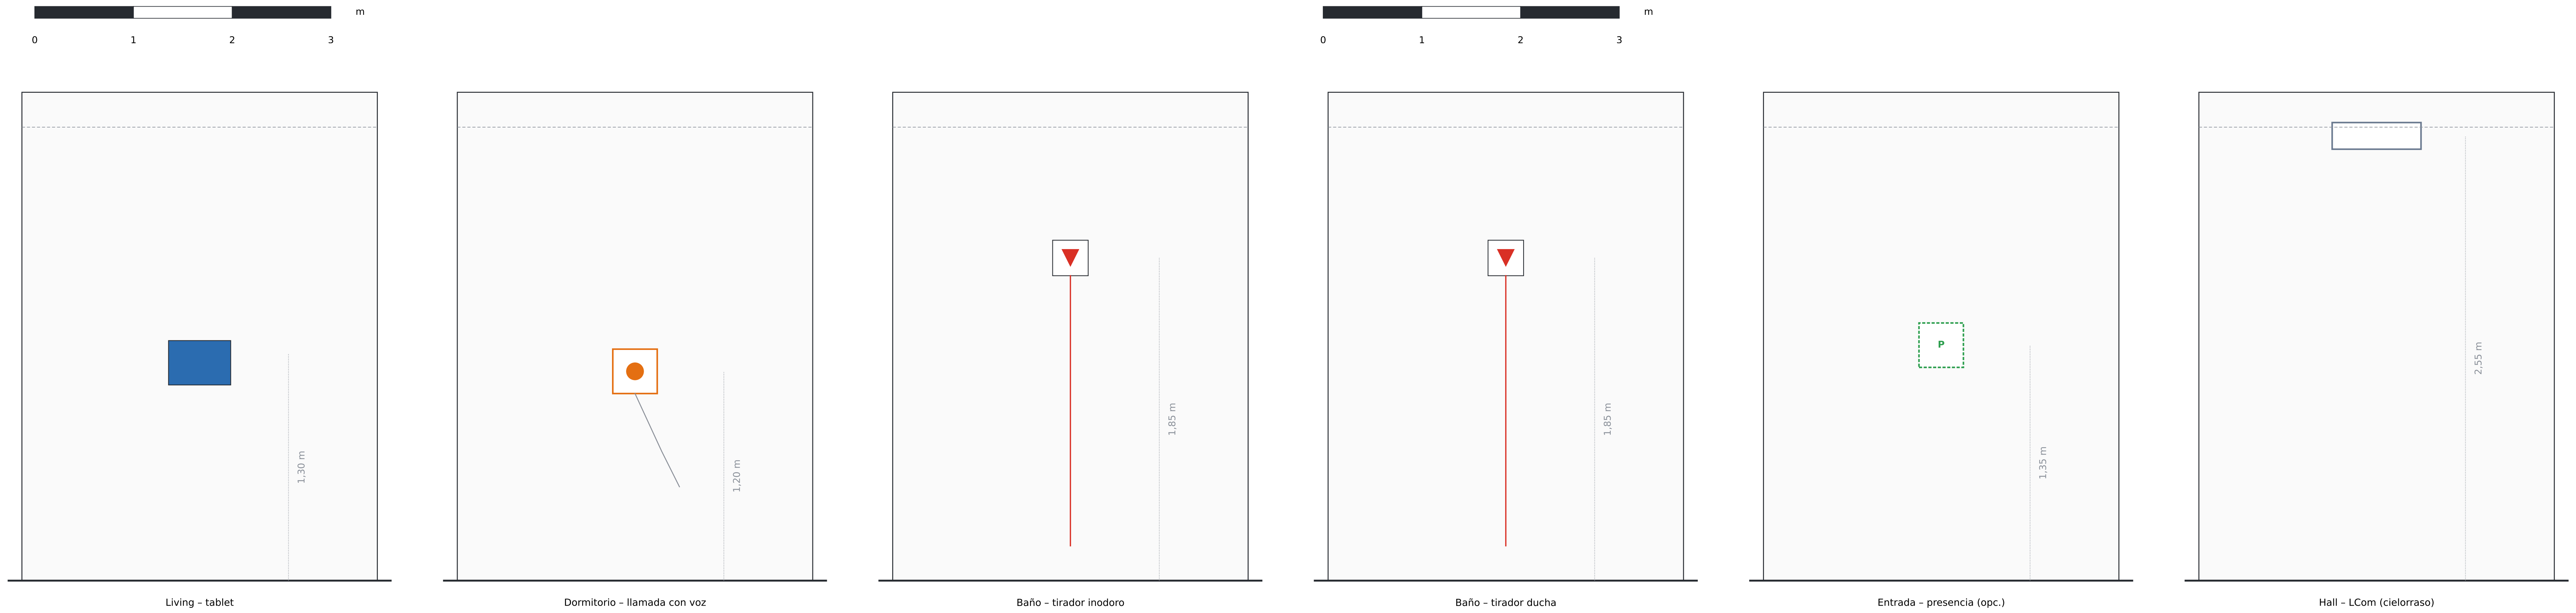

SÍMBOLOS Y CABLEADO · SYMBOLS & WIRING

🟦	TAB · Tablet Android en el living – llamada y voz Android tablet in the living room – call and voice · טלבאט דיאורדנא וןלסב – קראיה רובידו
T	TI / TD · Tirador inodoro / ducha ACE40320303W (baño principal, h 1,85 m) Toilet / shower pull-cord ACE40320303W (main bath, h 1.85 m) · תכישמ לבח הלסא / מקלחת ACE40320303W
▮▮	LCom ACE71610003 · concentrador del departamento (cielorraso del hall) LCom ACE71610003 · apartment hub (hall ceiling) · LCom ACE71610003 · רכזמ דירה (תרקת האובמה)
━	Cat6 / Cat7 en cadena: LCom → LCom → LCom → Buscomm (3 por Buscomm) Cat6 / Cat7 chain: LCom → LCom → LCom → Buscomm · Cat6 / Cat7 תרשרש: LCom ← LCom ← Buscomm
●	VOZ · Llamada de enfermería con voz ACE82182451 (dormitorio principal) Voice nurse call ACE82182451 (main bedroom) · קראית אחות קולית ACE82182451 (ישאר הניש רדח)
P	PR · Presencia / cancelación junto a la puerta – OPCIONAL Presence / cancel next to the door – OPTIONAL · נוכחות / ביטול ליד הדלת – ילנויצפוא
━	Cat6 radial: cada elemento del departamento → su LCom Cat6 radial: each device → its LCom · Cat6 ילאידר: כל התקן ← LCom
╌	Cat6 al pulsador opcional de presencia / cancelación Cat6 to optional presence / cancel button · Cat6 ללחצן נוכחות ילנויצפוא

MIGDALEI YAM A TIJON · DEPARTAMENTOS TUTELADOS

Sistema de llamada de enfermería – PB + 6 pisos · 36 departamentos

Sistema: ACE BG · Advantecnia   Elaboró: Telab International

DEPARTAMENTO TIPO B – DETALLE

Apartment type B – detail

ESCALA · SCALE	FECHA · DATE	REV	LÁMINA
1:50	**12/10/2026**	**A**	**04**

Cotas en metros · Dimensions in m · מידות במטרים

Formato A1 · Rev. A – Anteproyecto

A · ESQUEMA VERTICAL DEL EDIFICIO (PB + 6 PISOS)

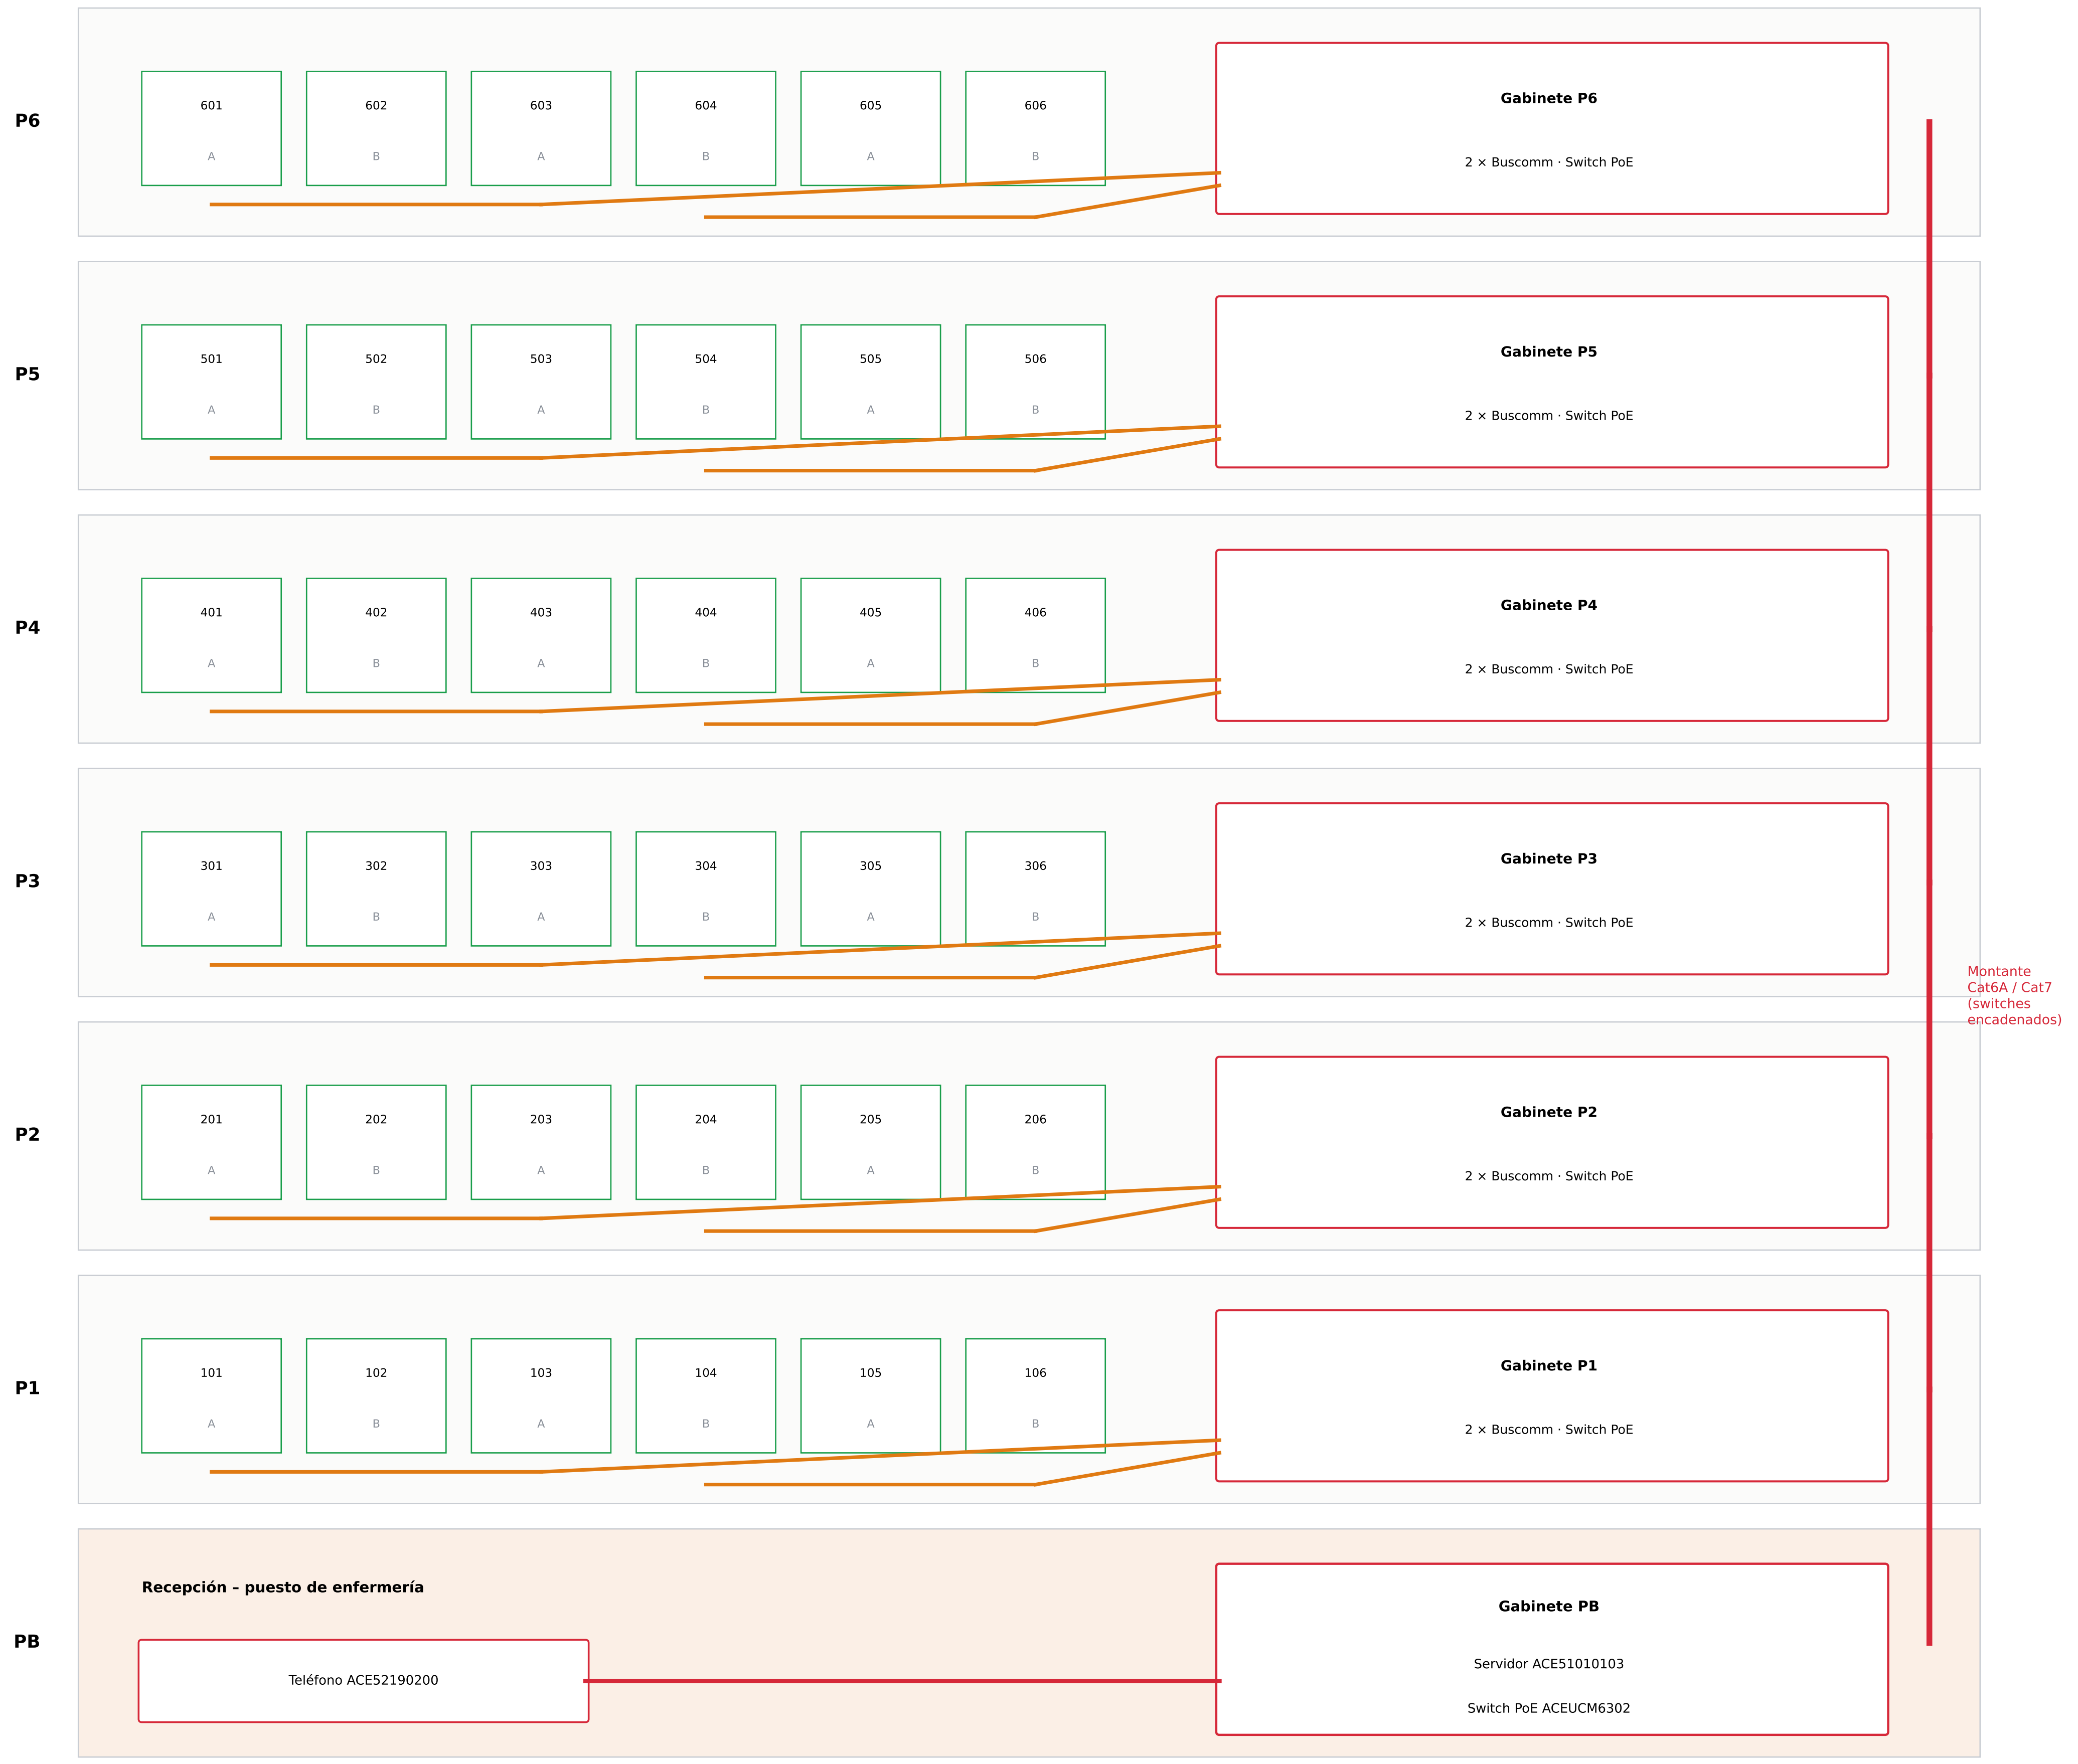

B · TOPOLOGÍA POR DEPARTAMENTO Y POR PISO

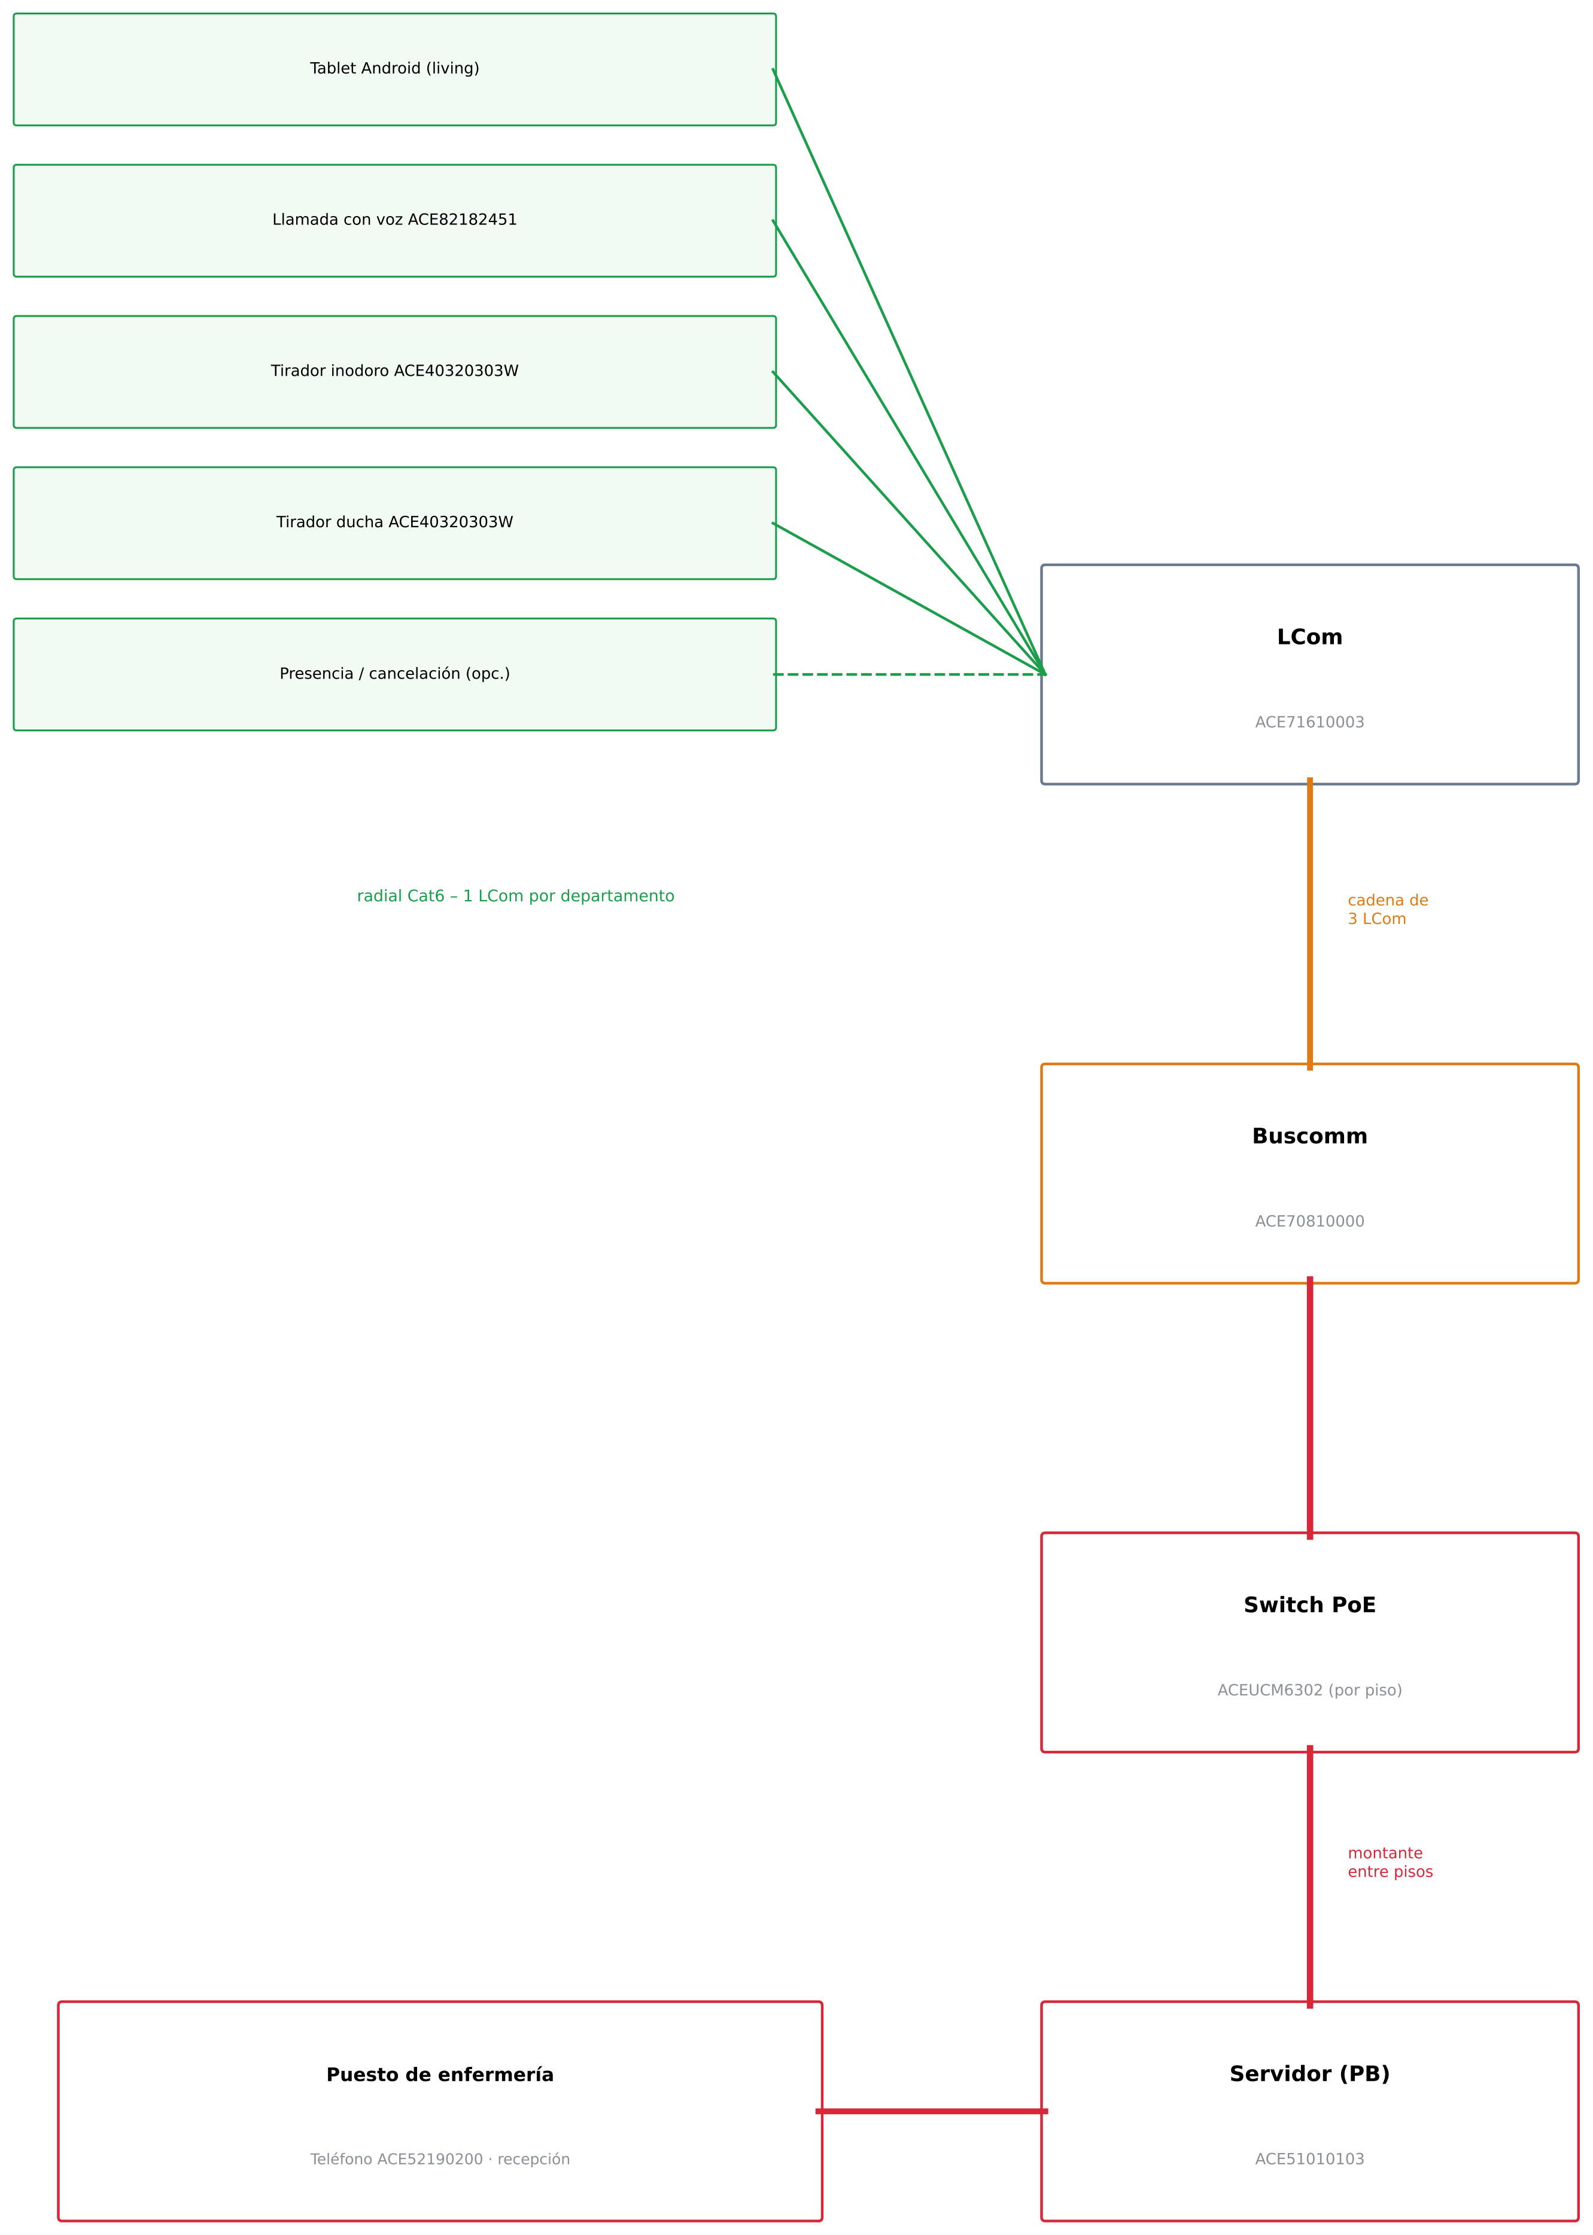
Tablet Android (living)
Llamada con voz ACE82182451
Tirador inodoro ACE40320303W
Tirador ducha ACE40320303W
Presencia / cancelación (opc.)
LCom
ACE71610003
radial Cat6 – 1 LCom por departamento
cadena de 3 LCom
Buscomm
ACE70810000
Switch PoE
ACEUCM6302 (por piso)
montante entre pisos
Puesto de enfermería
Teléfono ACE52190200 · recepción
Servidor (PB)
ACE51010103

NOTAS · NOTES

1. Planta baja: recepción con el puesto de enfermería (teléfono ACE52190200) y el gabinete principal con el servidor.
2. Pisos 1 a 6: 6 departamentos por piso (3 tipo A y 3 tipo B intercalados).
3. En cada piso: 2 Buscomm (3 LCom cada una) y un switch PoE en el gabinete.
4. Los switches se encadenan piso a piso por el montante Cat6A / Cat7 hasta el servidor de PB.
5. Todo el sistema es PoE.
6. Las llamadas llegan por voz o como alarma al puesto de enfermería.
7. Cantidades de anteproyecto: validar con Advantecnia y en obra.

C · LISTA DE MATERIALES – EDIFICIO COMPLETO (36 departamentos)

Código	Descripción	Cant.	Observación
EN CADA DEPARTAMENTO (× 36)			
TAB	Tablet Android de pared (living) – llamada y voz	36	1 por departamento
VOZ	Llamada de enfermería con voz – ACE82182451	36	dormitorio principal
TI / TD	Tirador baño / ducha – ACE40320303W	72	2 por departamento
PR	Presencia / cancelación junto a la puerta – OPCIONAL	(36)	opcional
LCom	Concentrador de departamento – ACE71610003	36	1 por departamento
POR PISO (× 6) Y PLANTA BAJA			
BC	Buscomm – ACE70810000	12	2 por piso (3 LCom c/u)
SW	Switch PoE – ACEUCM6302	7	1 por piso + PB
GAB	Gabinete de comunicaciones con patch panel y UPS	7	1 por piso + PB
SV	Servidor + software Advantecnia – ACE51010103	1	PB
TEL	Teléfono de escritorio enfermería – ACE52190200	1	recepción PB
CABLES (piso tipo × 6, + 15 % de reserva)			
—	Cat6 radial dentro de los departamentos (verde)	1640 m	237 m por piso
—	Cat6 / Cat7 cadena LCom → Buscomm (naranja)	620 m	89 m por piso
—	Cat6A / Cat7 gabinete + montante 7 niveles (rojo)	70 m	incluye montante

MIGDALEI YAM A TIJON · DEPARTAMENTOS TUTELADOS

Sistema de llamada de enfermería – PB + 6 pisos · 36 departamentos

Sistema: ACE BG · Advantecnia   Elaboró: Telab International

ESQUEMA VERTICAL, TOPOLOGÍA Y MATERIALES

Riser diagram, topology & bill of materials

ESCALA · SCALE	FECHA · DATE	REV	LÁMINA
S/E	**12/10/2026**	**A**	**05**

Cotas en metros · Dimensions in m · מידות במטרים

Formato A1 · Rev. A – Anteproyecto

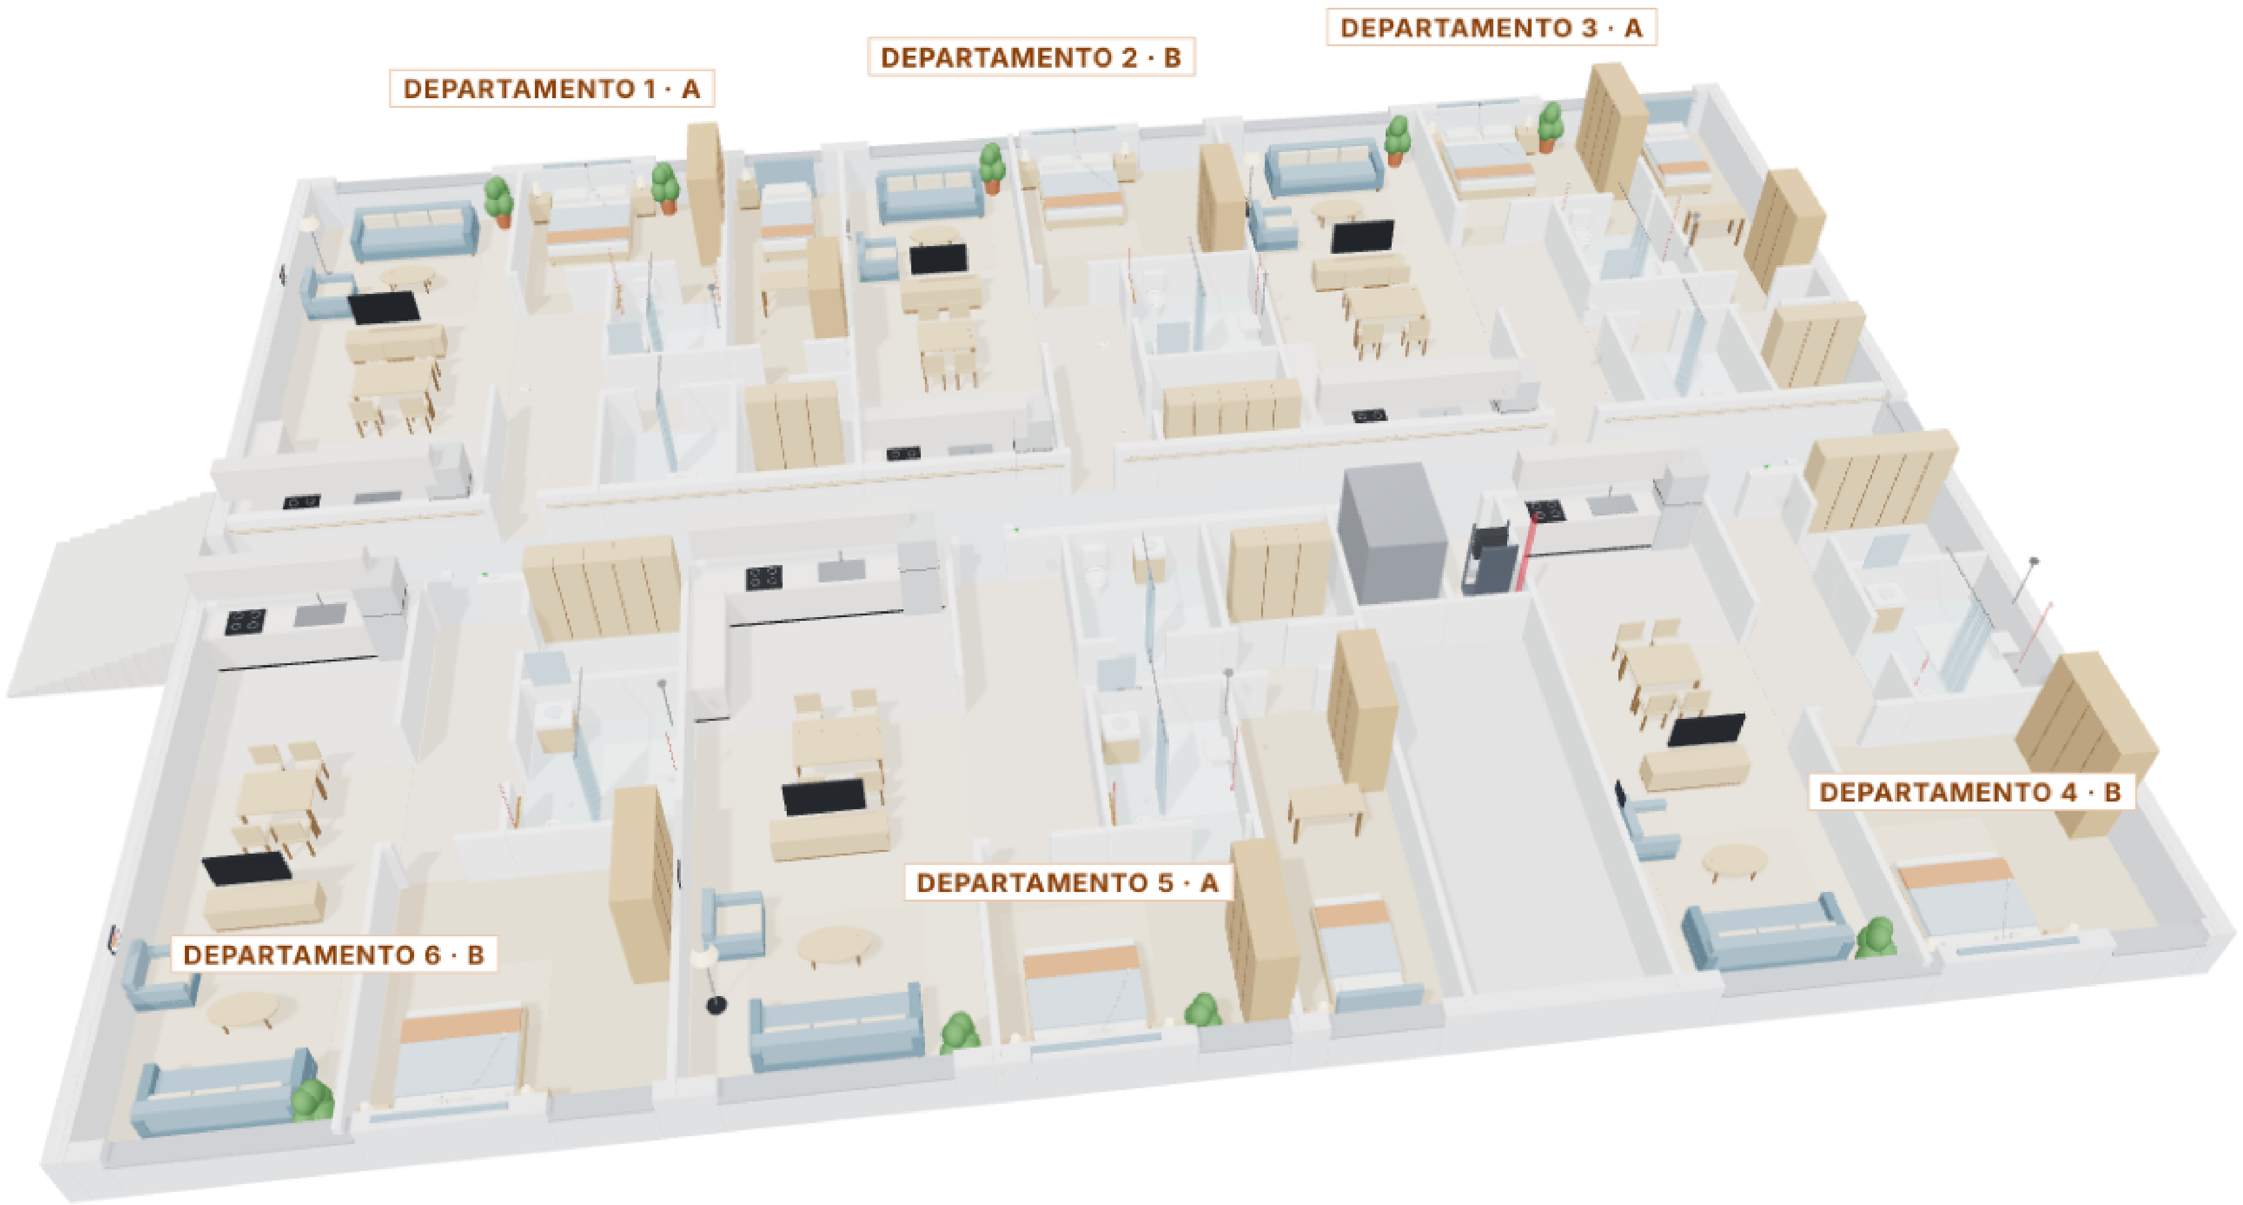

A · Piso tipo – departamentos 1 (tipo A) y 2 (tipo B) destacados

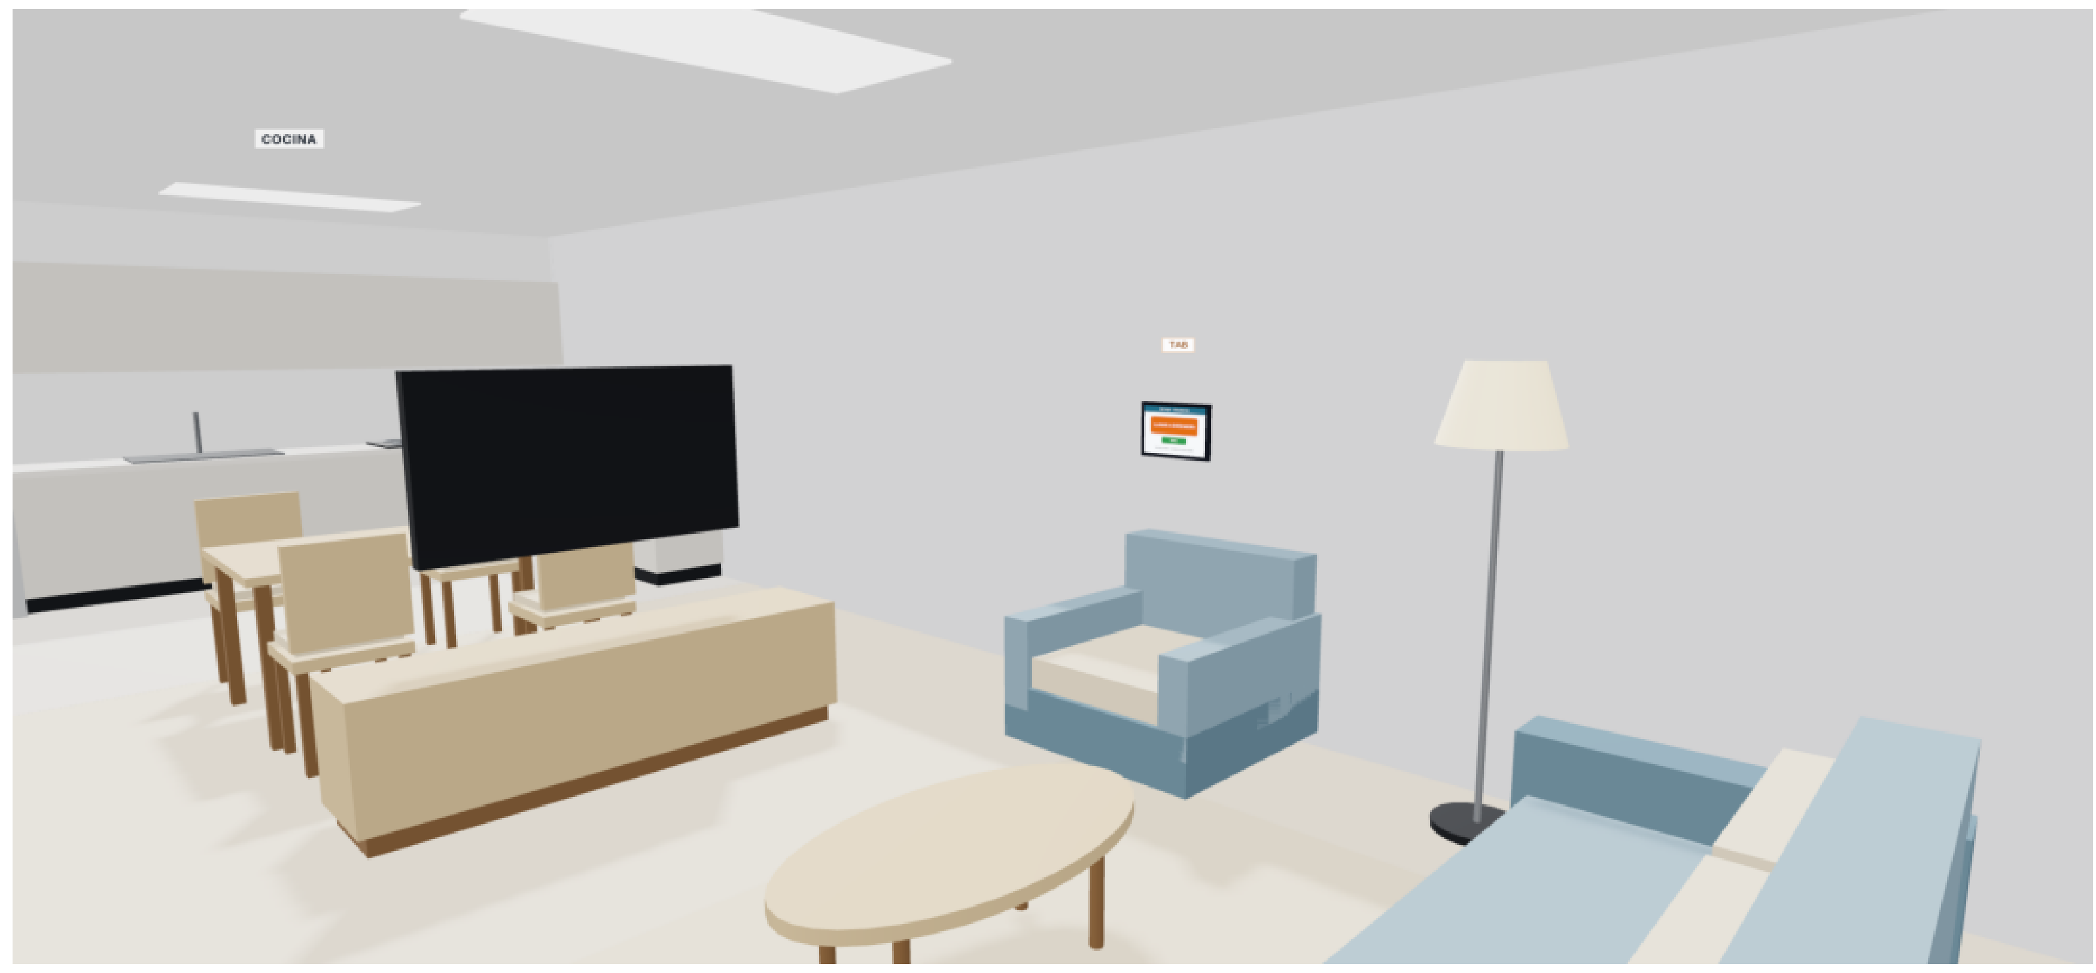

B · Living con tablet Android

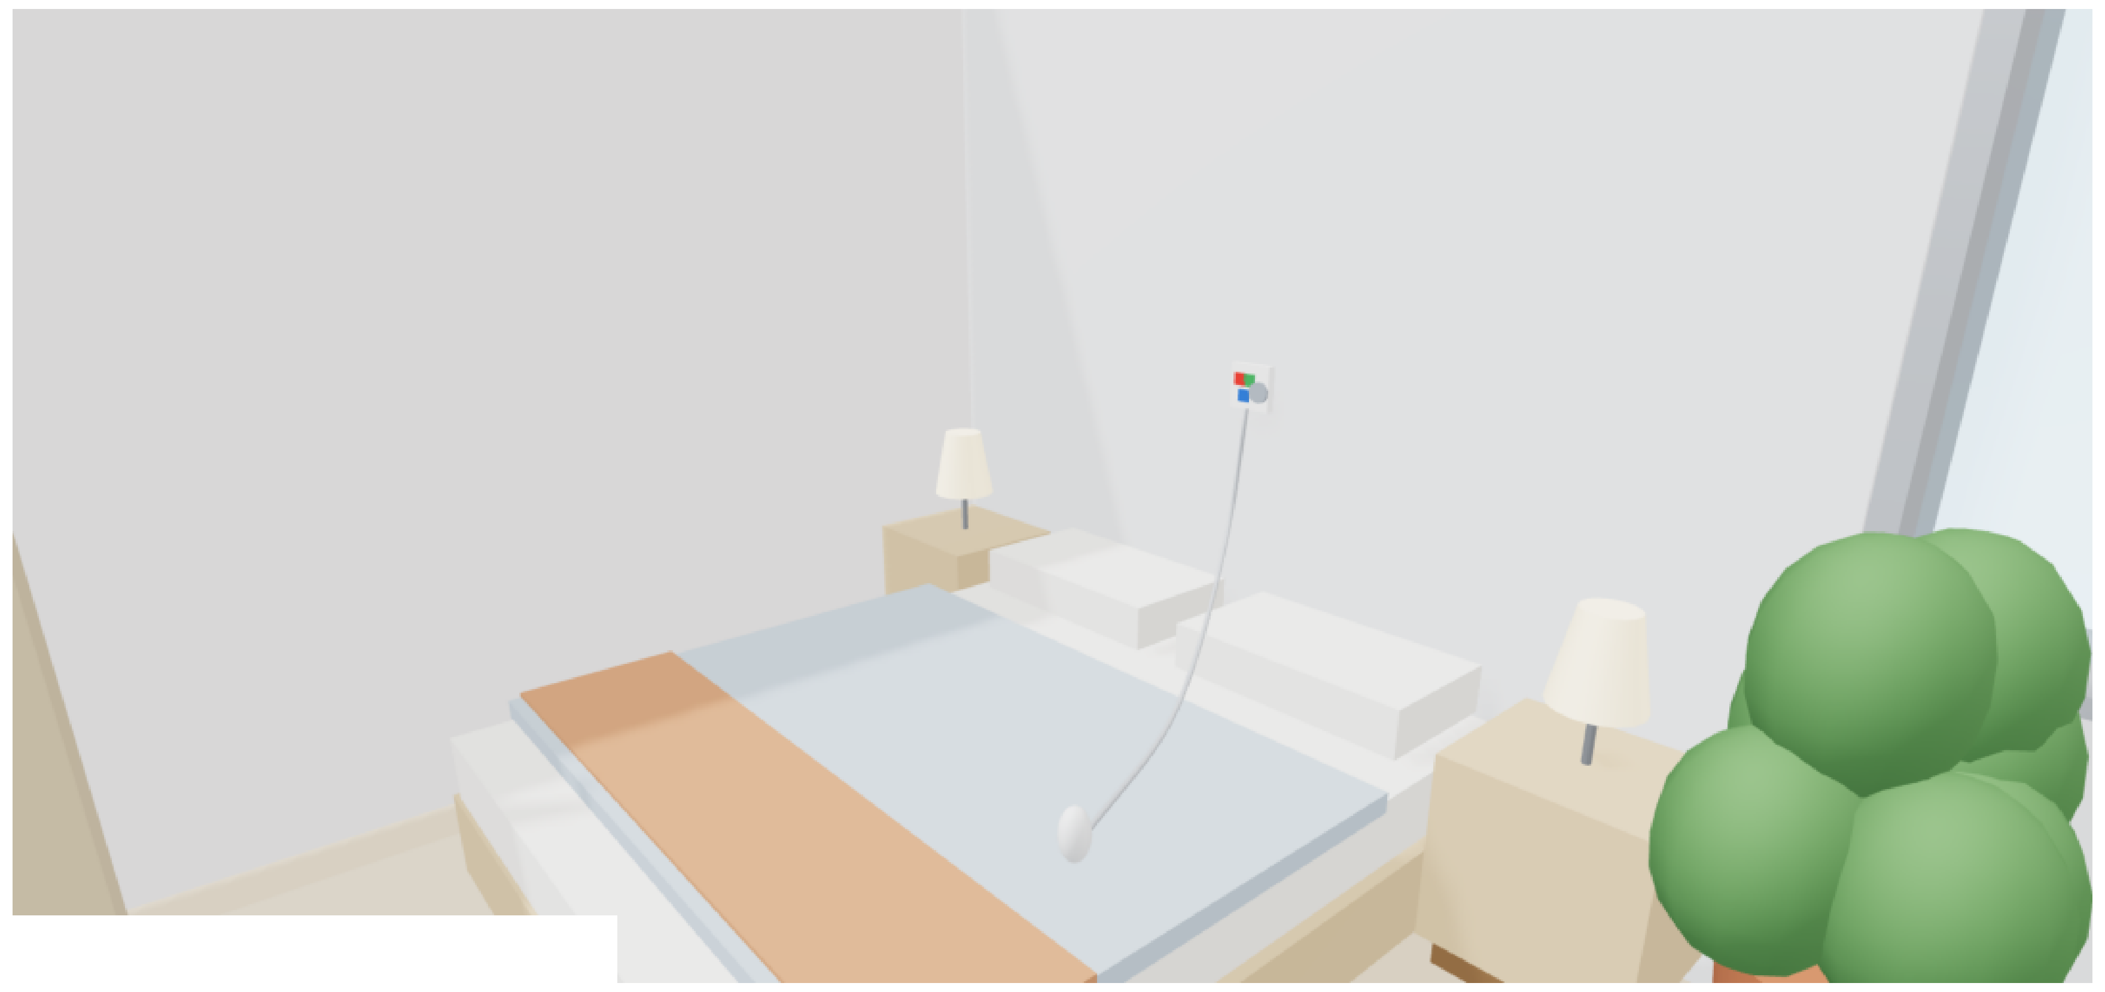

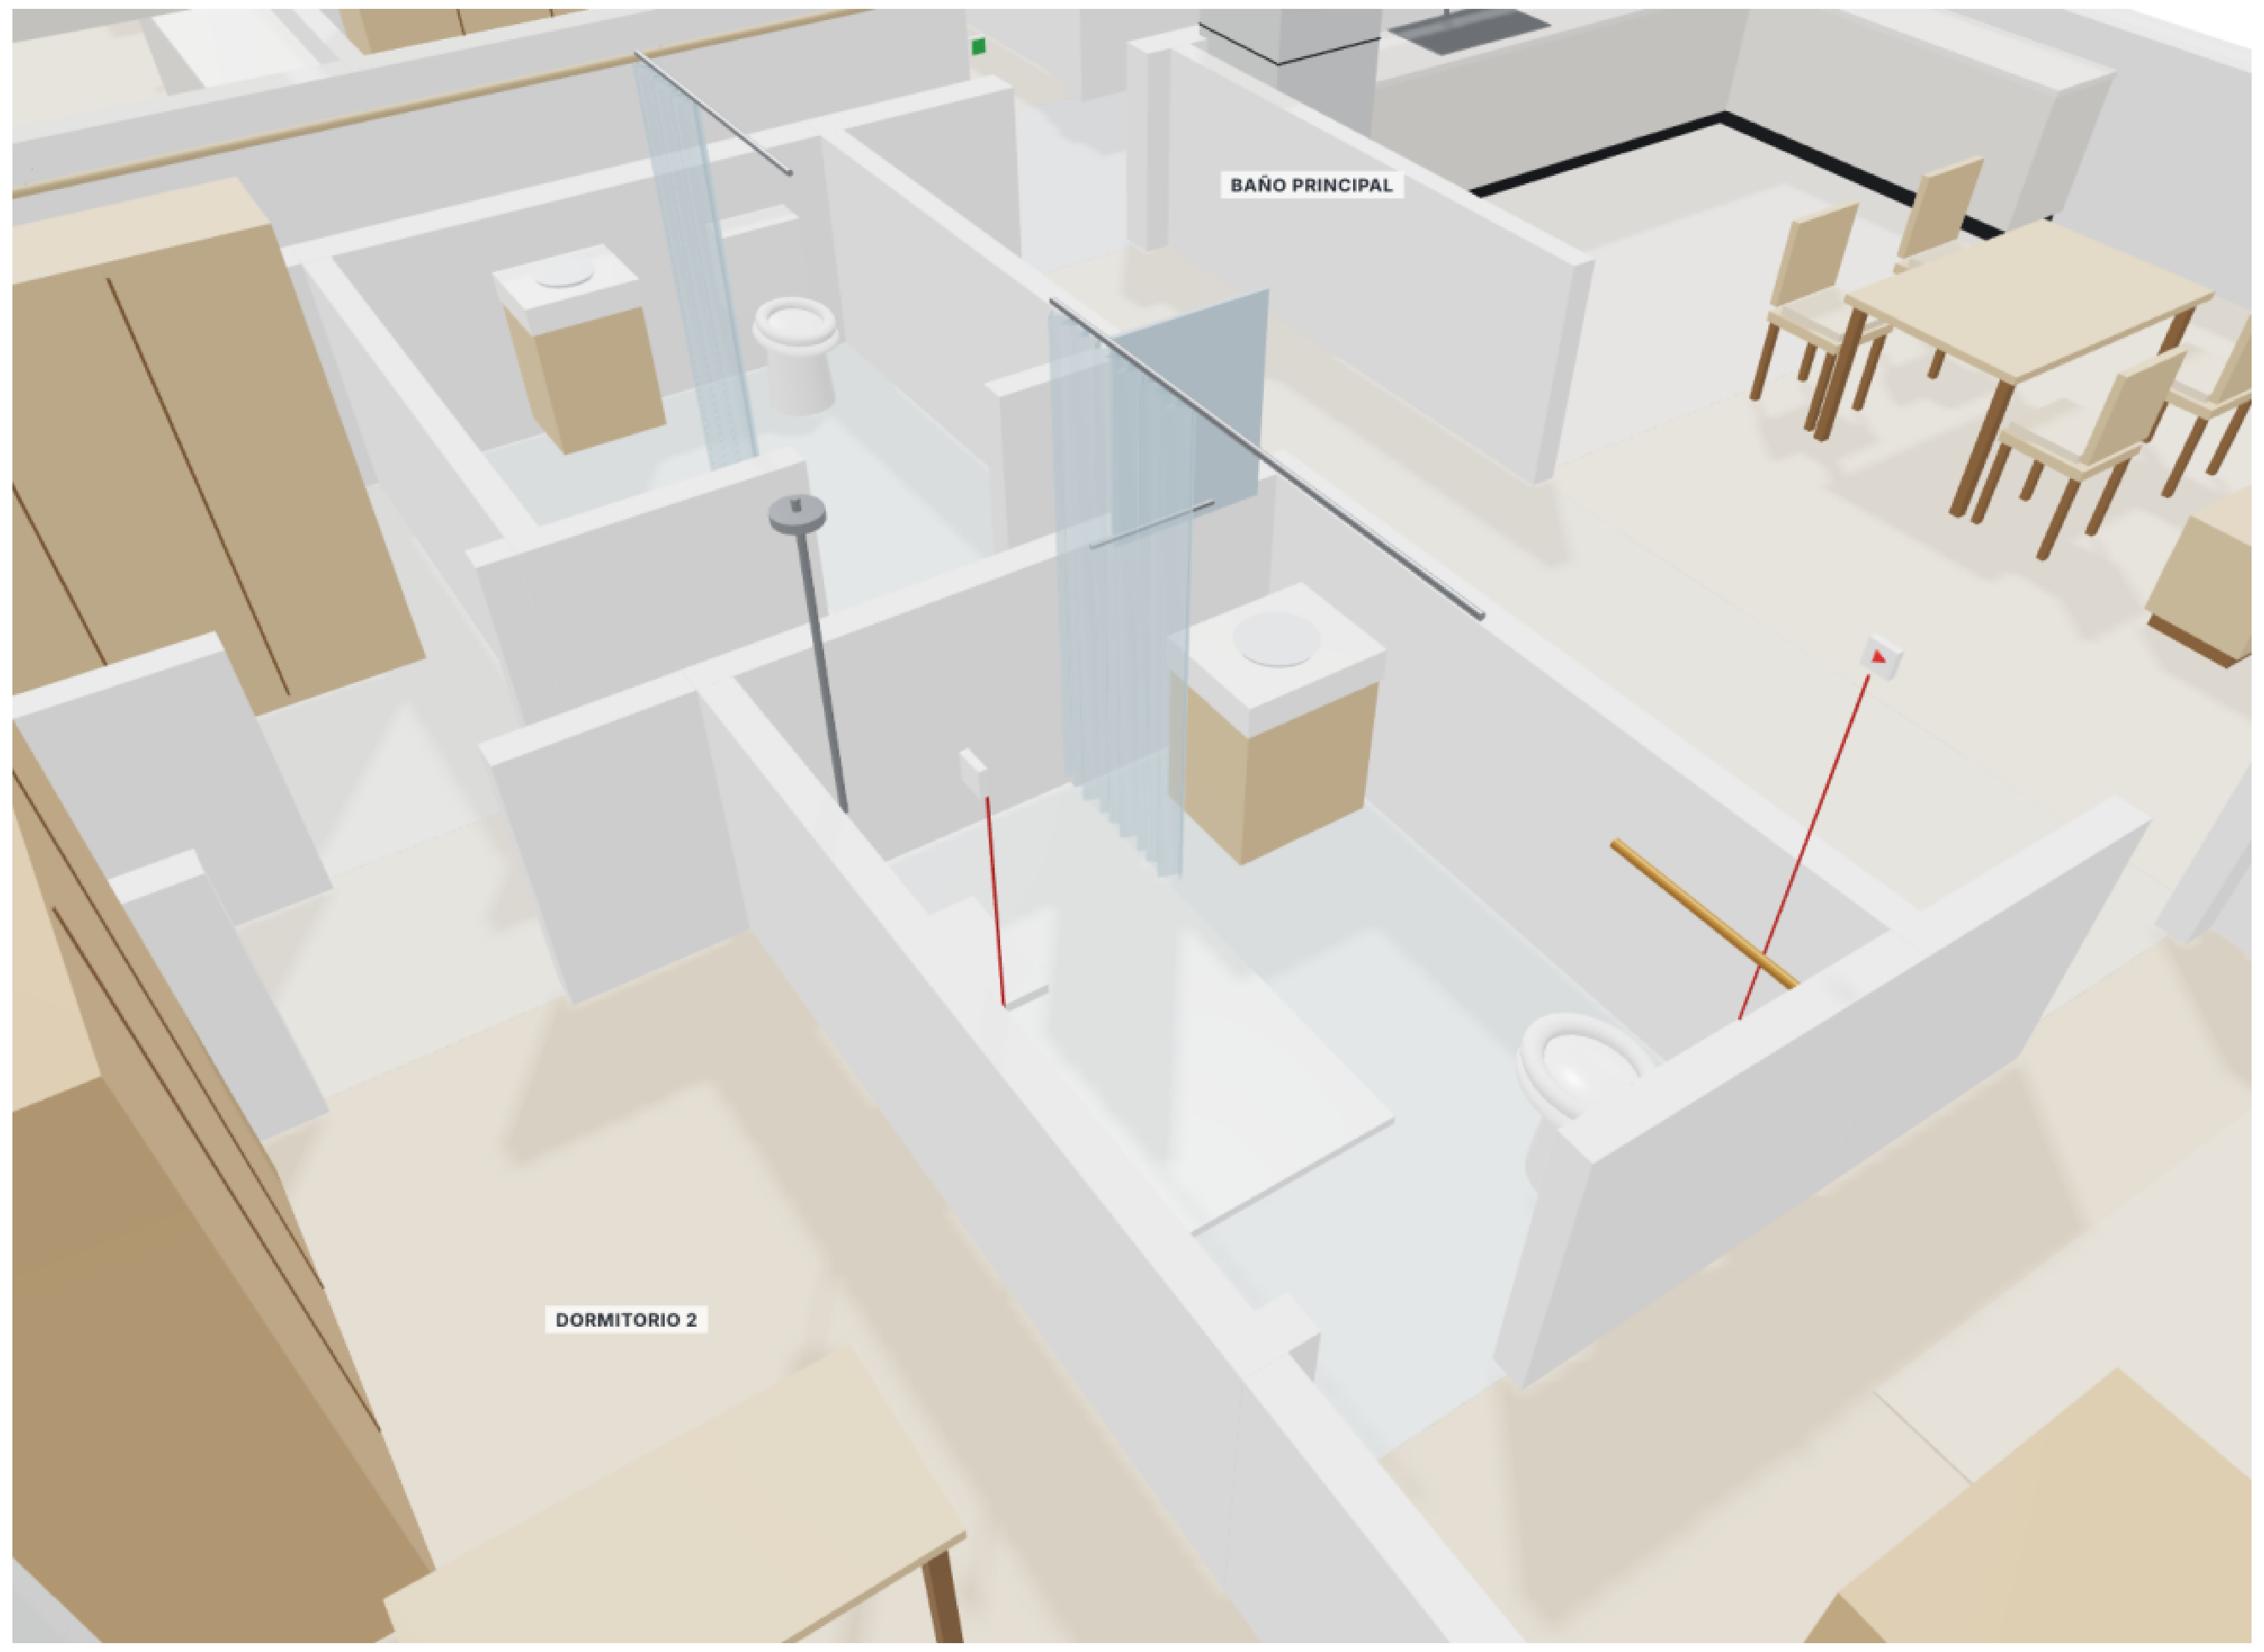

D · Baño principal – tiradores inodoro y ducha

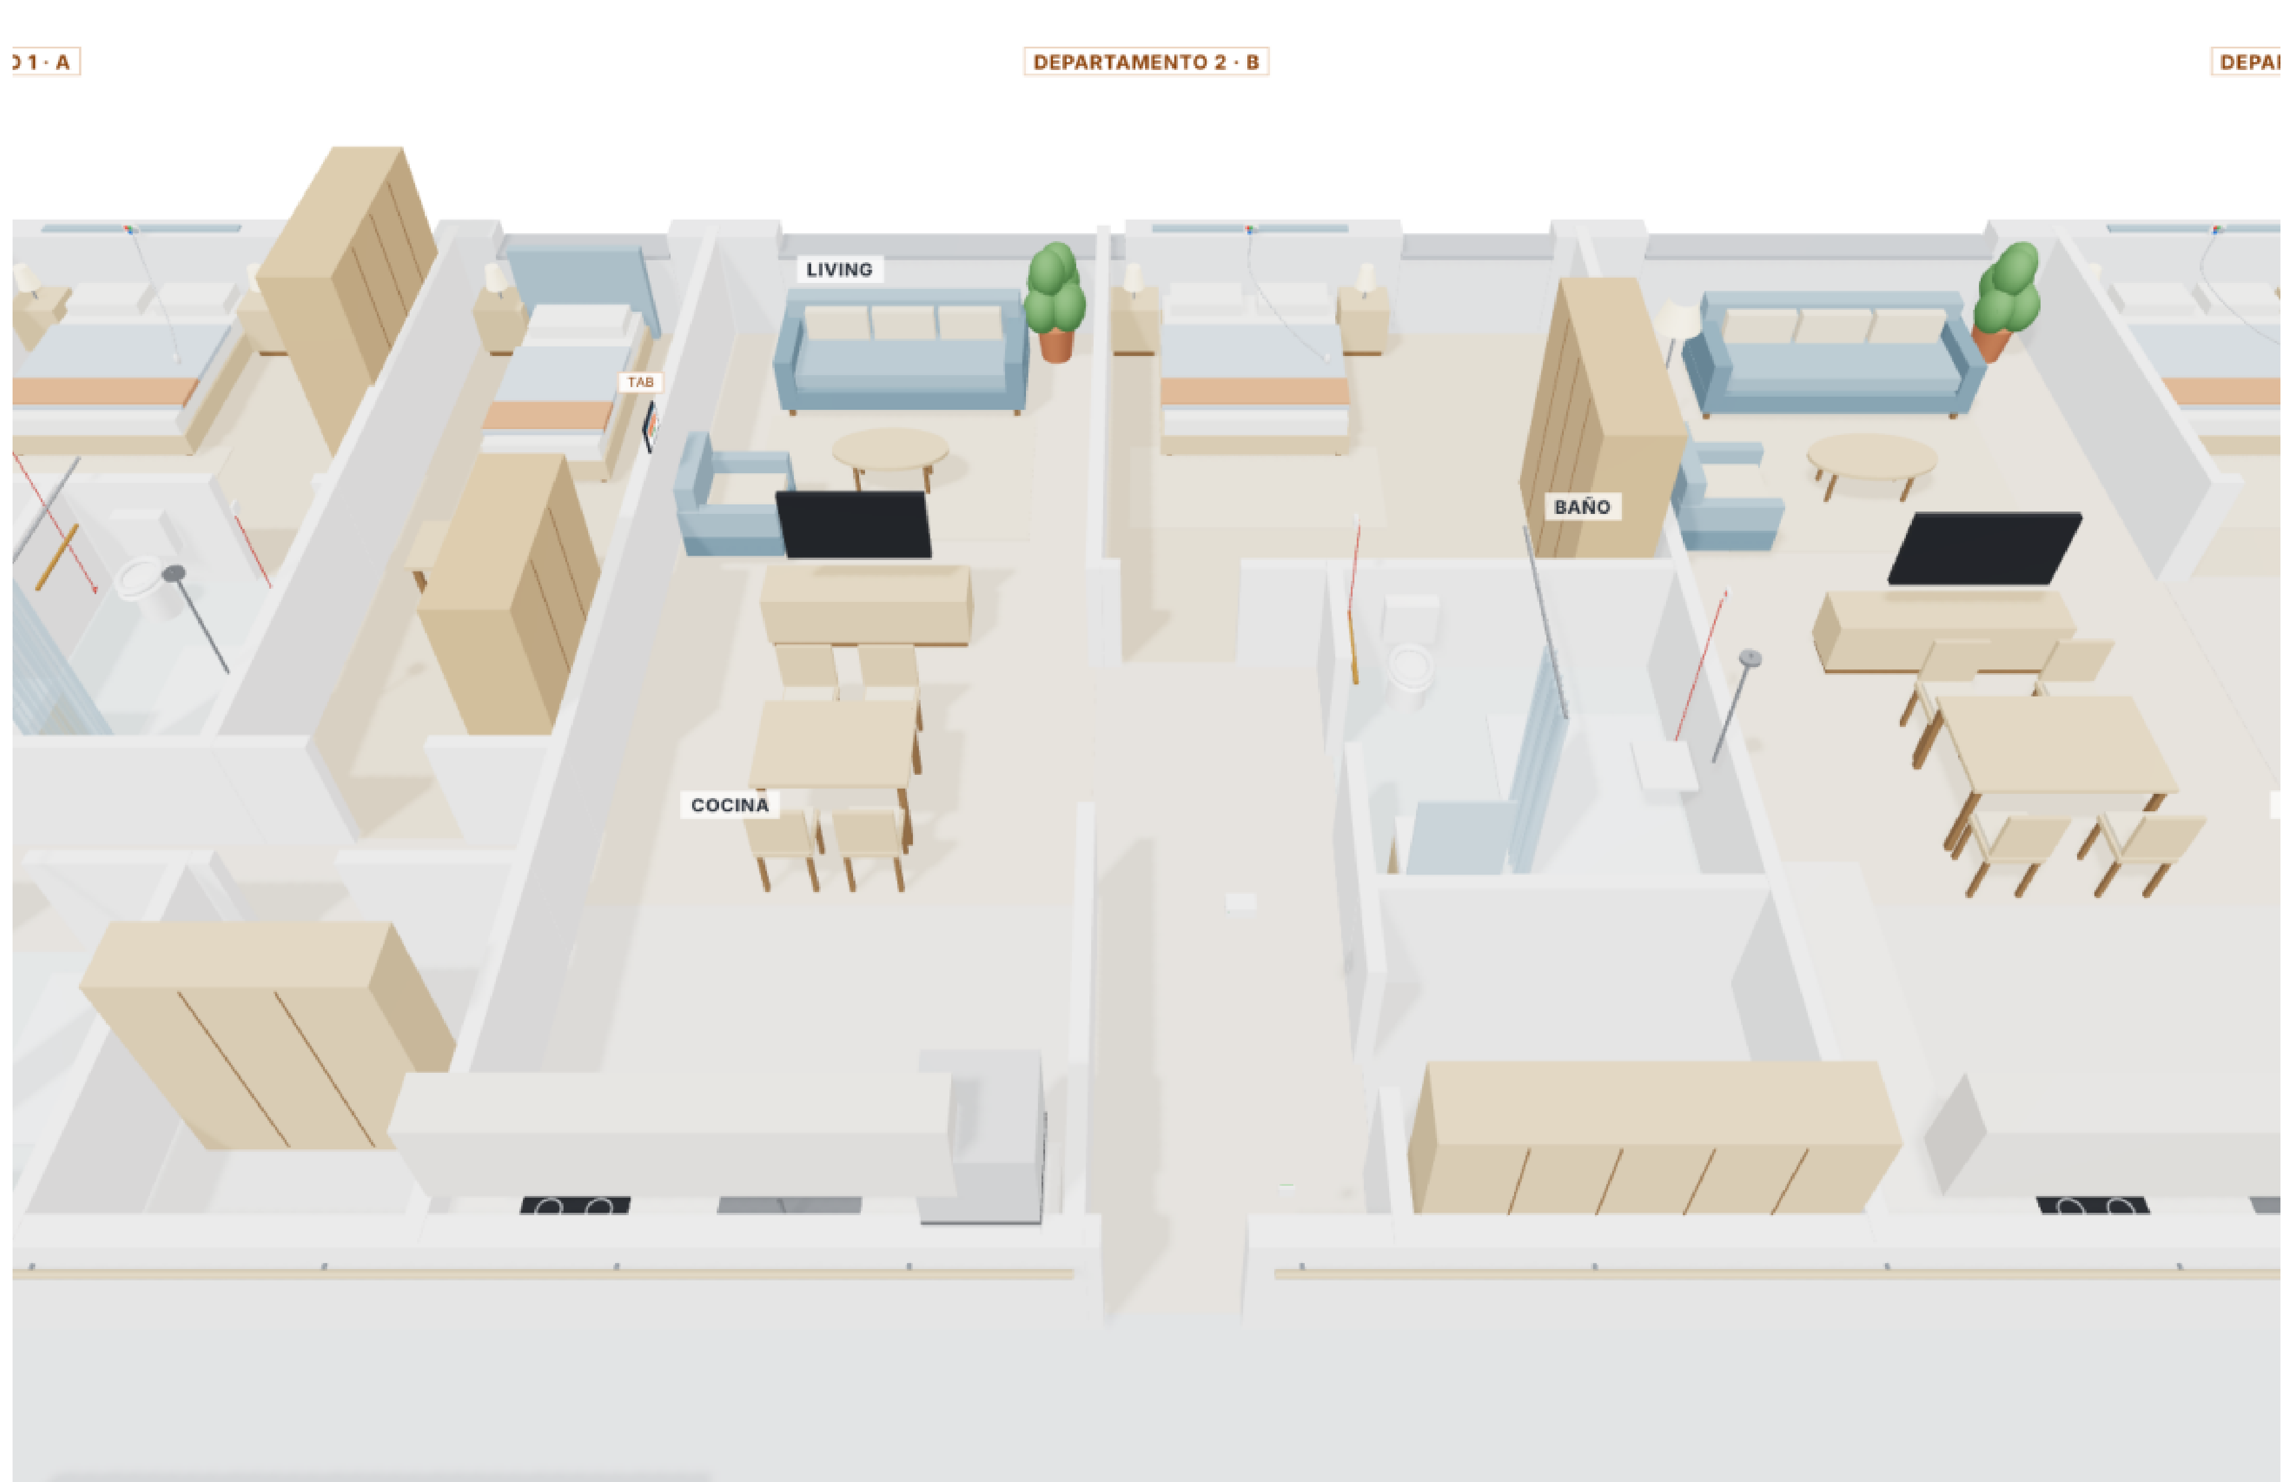

E · Departamento tipo B

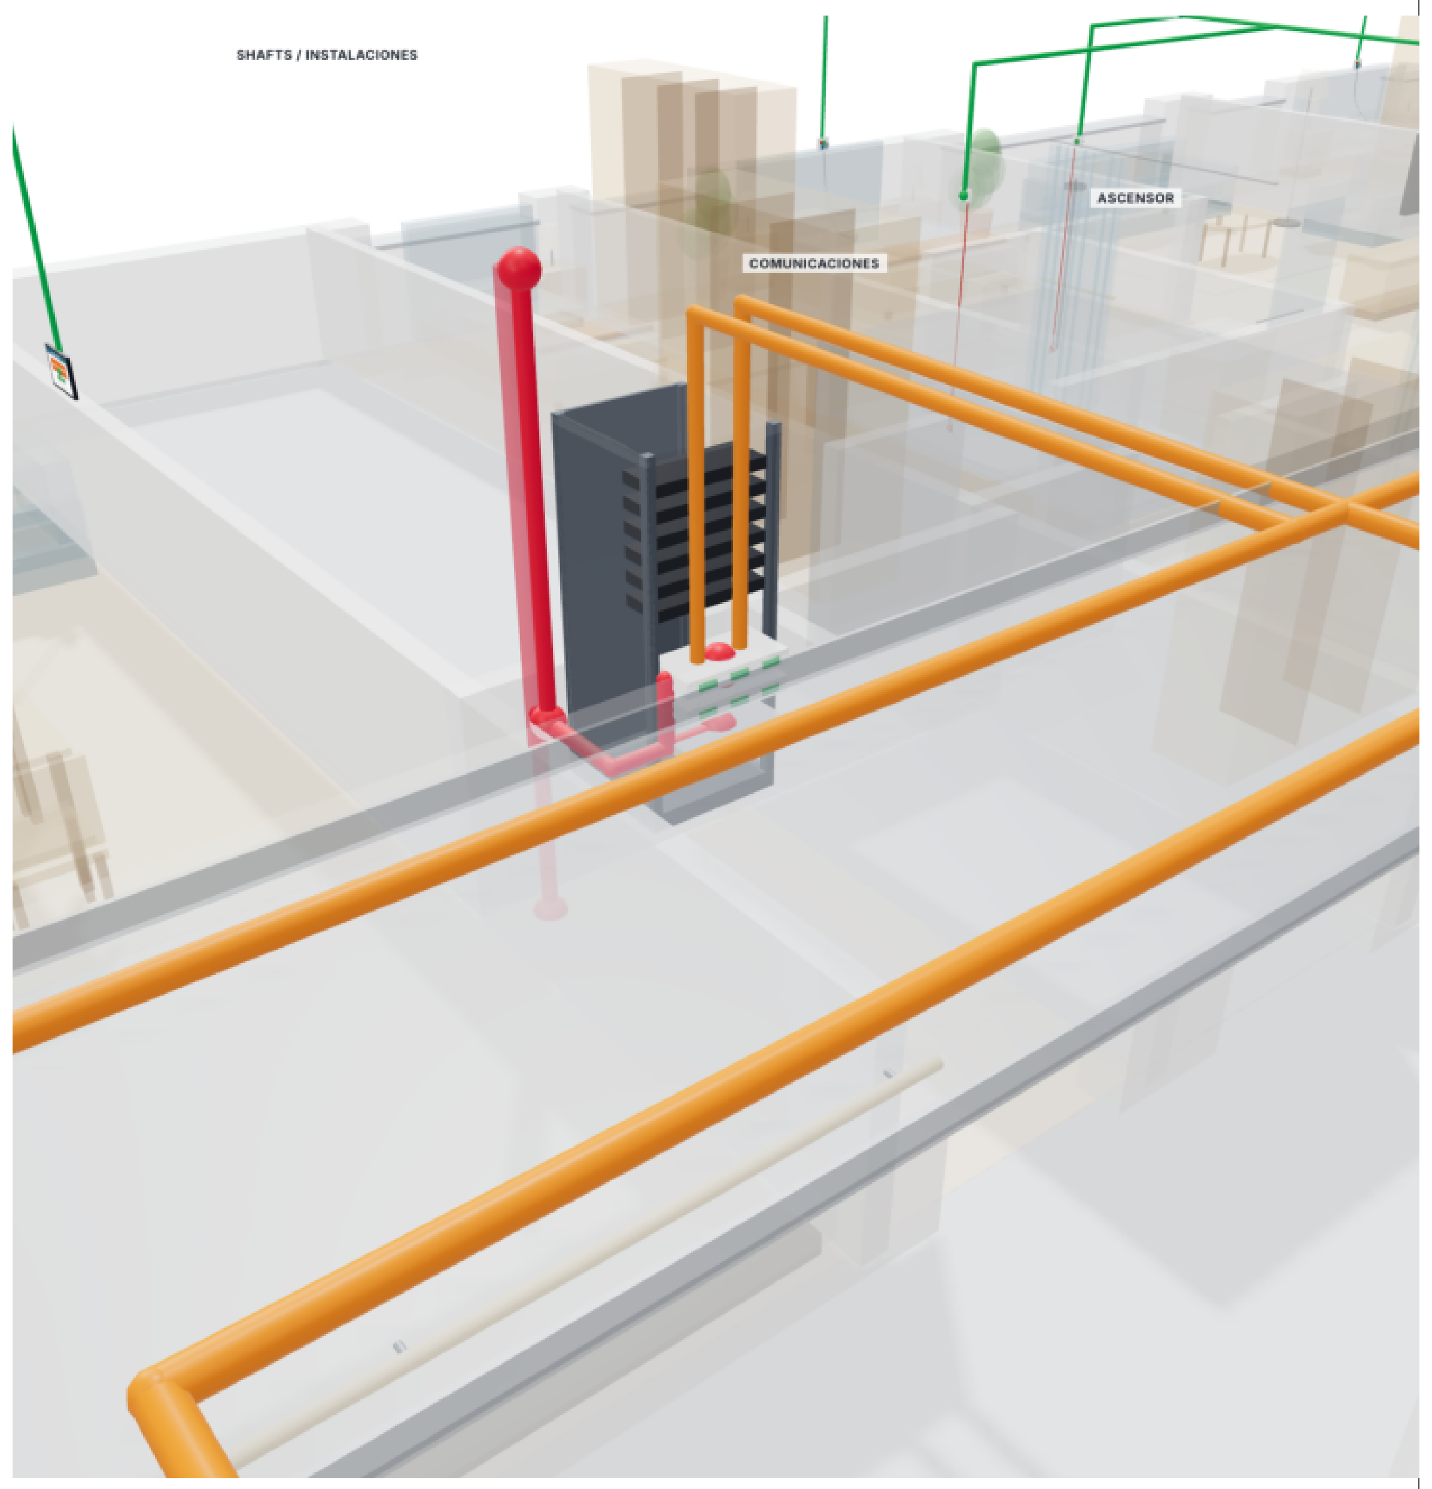

F · Sala de comunicaciones del piso

MIGDALEI YAM A TIJON · DEPARTAMENTOS TUTELADOS

Sistema de llamada de enfermería – PB + 6 pisos · 36 departamentos

Sistema: ACE BG · Advantecnia   Elaboró: Telab International

VISTAS 3D – EQUIPAMIENTO

3D views – equipment

ESCALA · SCALE	FECHA · DATE	REV	LÁMINA
S/E	**12/10/2026**	**A**	**06**

Cotas en metros · Dimensions in m · מידות במטרים

Formato A1 · Rev. A – Anteproyecto

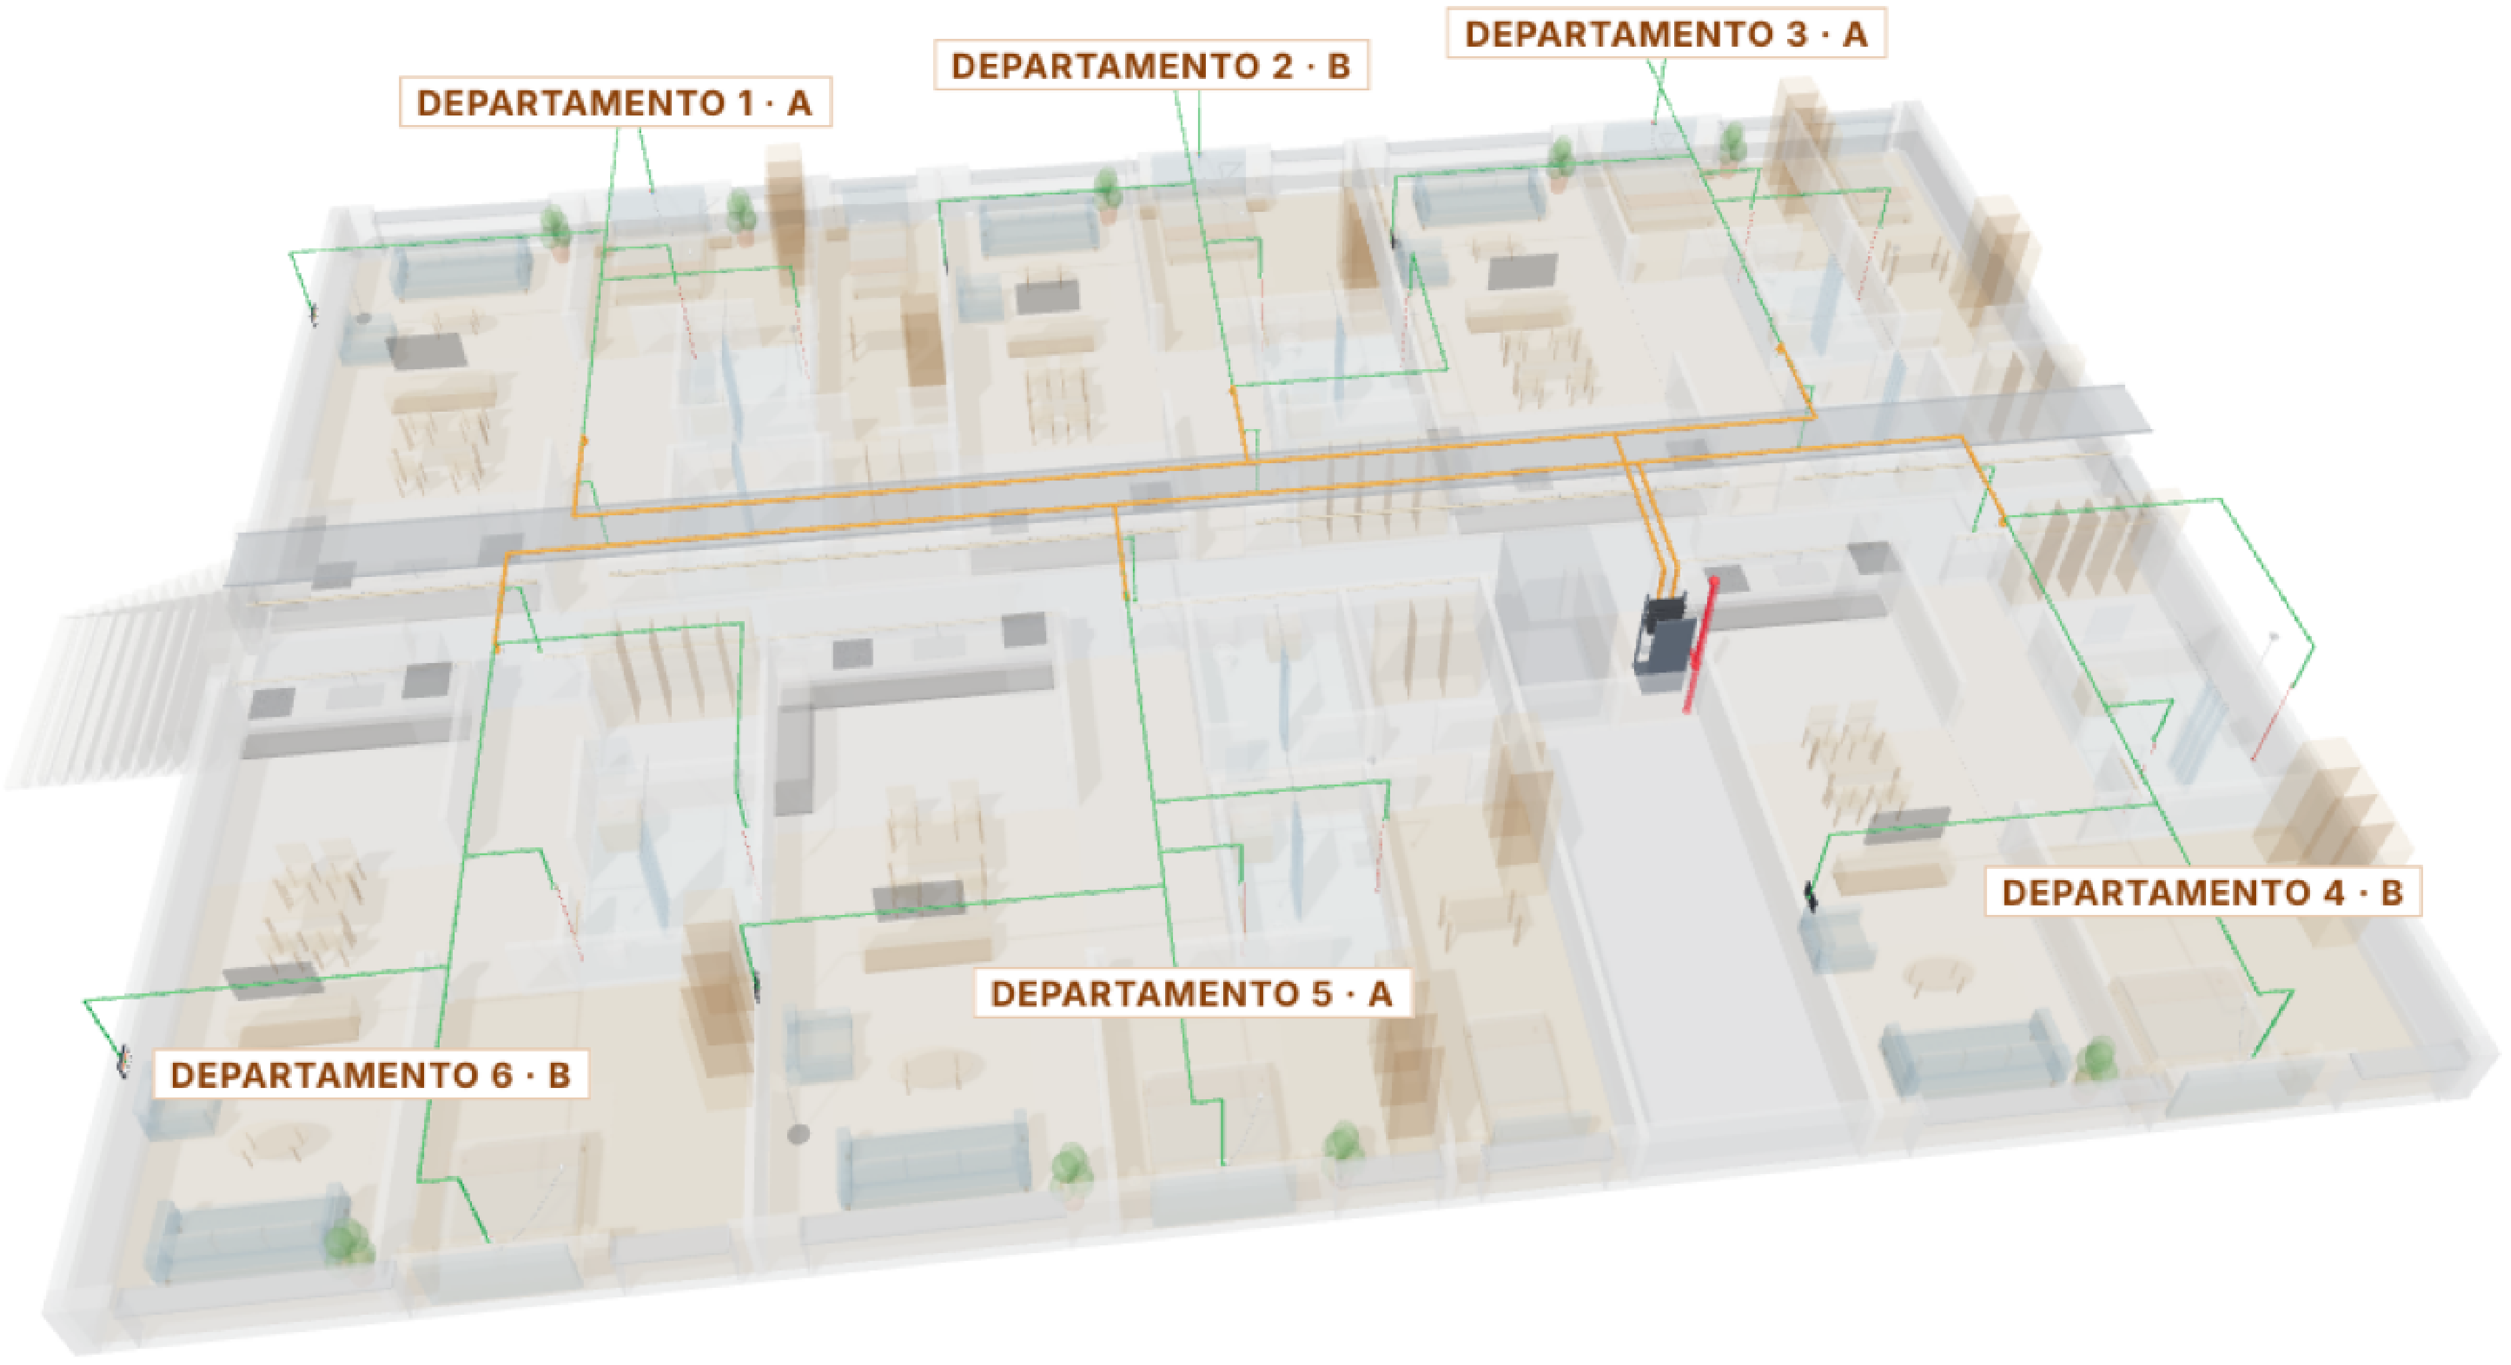

A · Piso tipo – cableado (verde radial · naranja cadena LCom · rojo red)

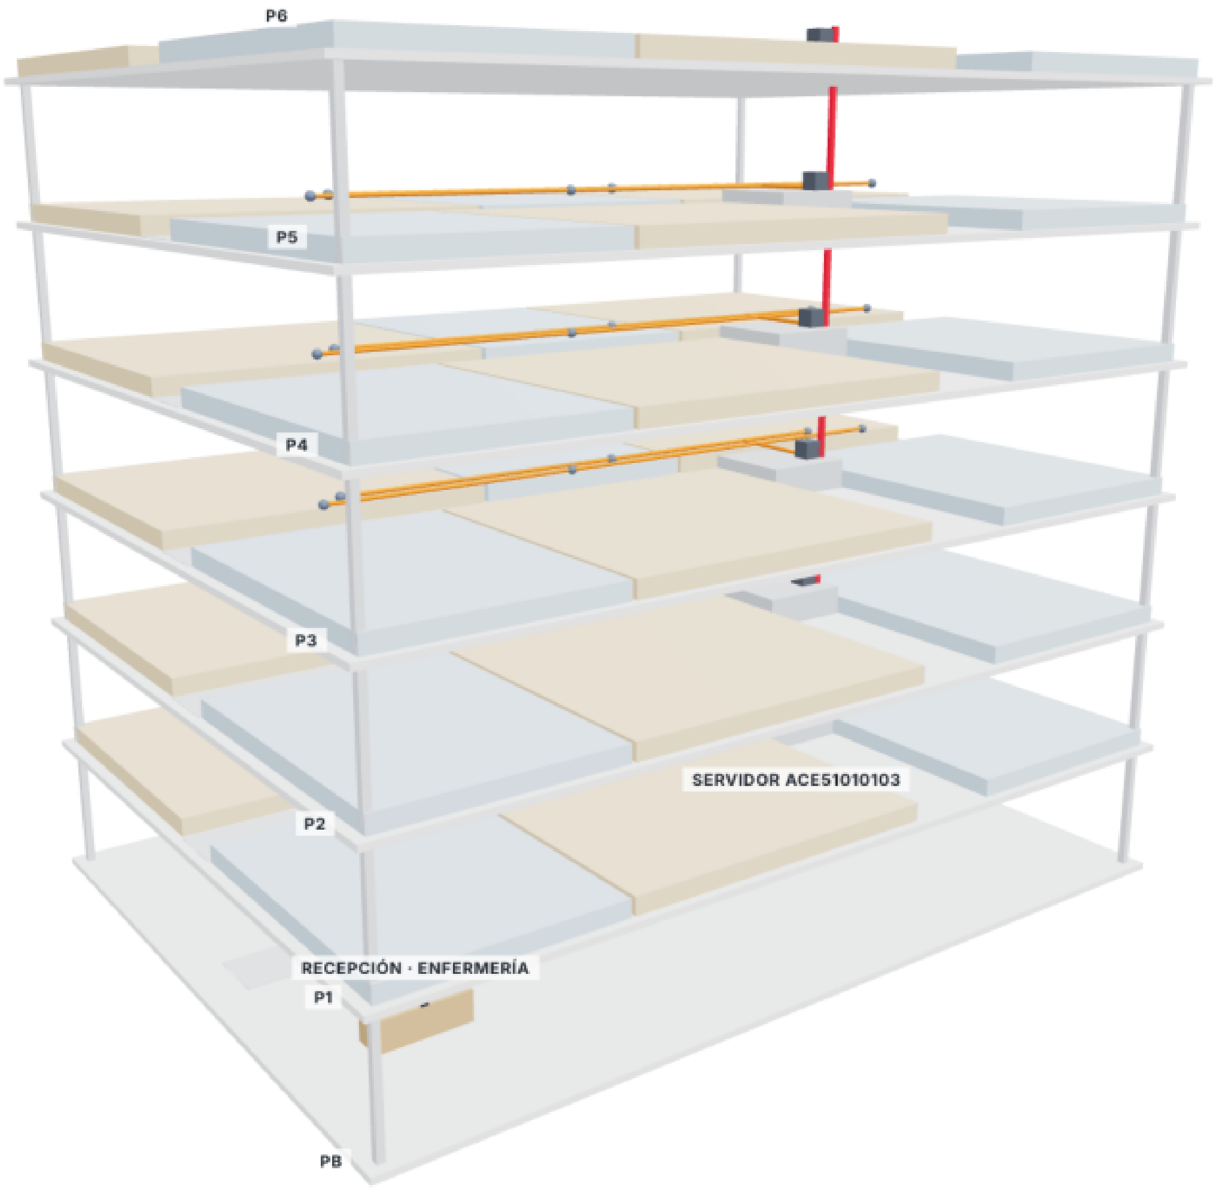

B · Edificio PB + 6 pisos – montante

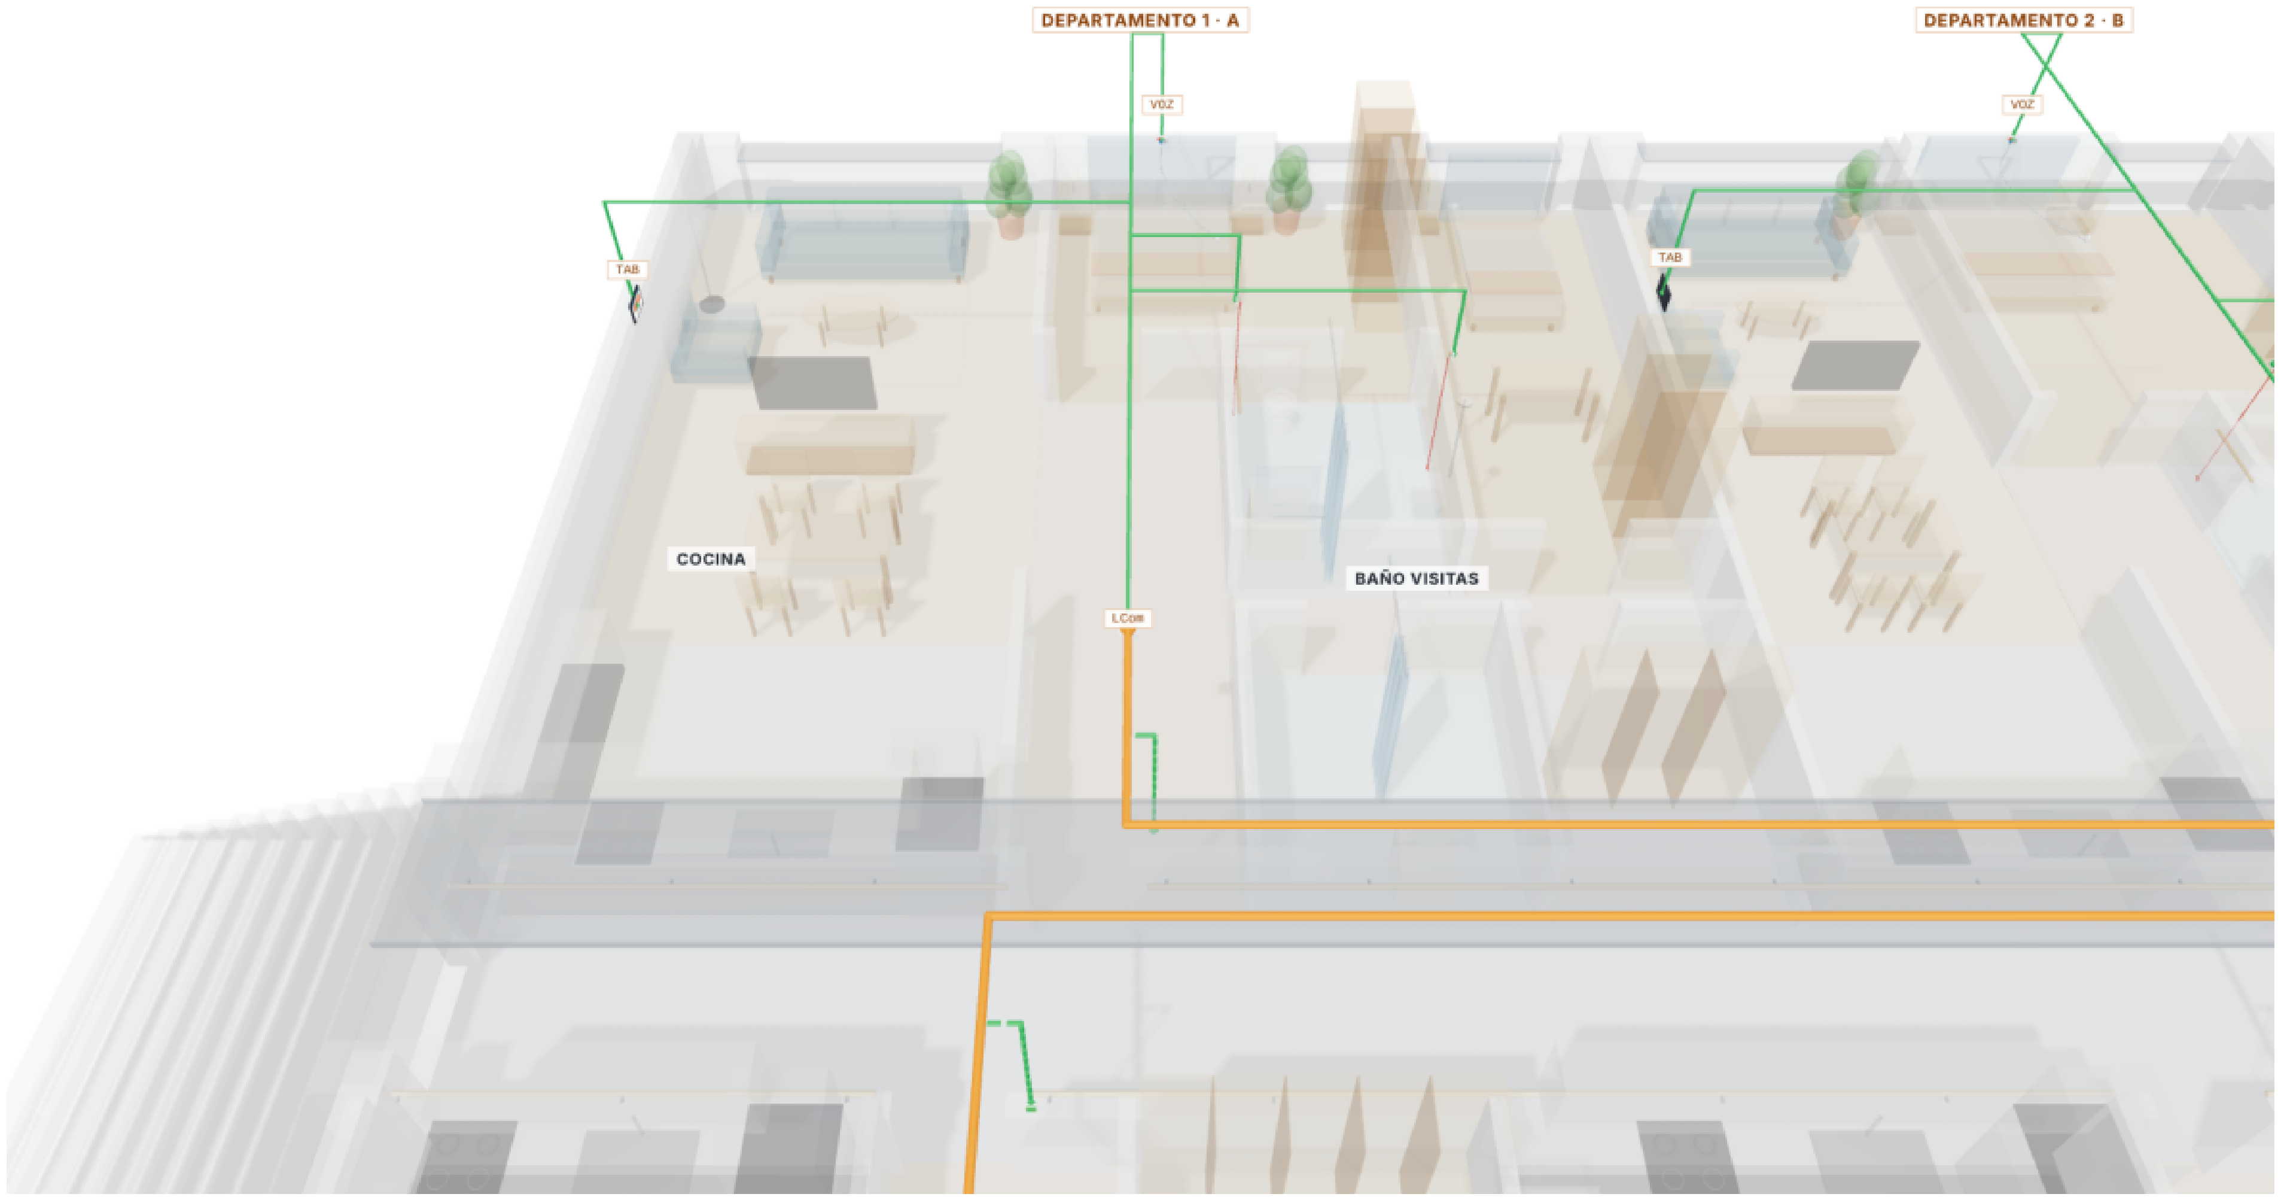

C · Departamento tipo A – radial al LCom

COLORES · COLOURS · םיעבצ

🟩	Cat6 radial: cada elemento del departamento → su LCom Cat6 radial: each device → its LCom · Cat6 ילאידר: לכ ןקתה ← LCom
🟧	Cat6 / Cat7 en cadena: LCom → LCom → LCom → Buscomm (3 por Buscomm) Cat6 / Cat7 chain: LCom → LCom → LCom → Buscomm · Cat6 / Cat7 תרשרש: LCom ← LCom ← Buscomm
🟥	Cat6A / Cat7 red: Buscomm → switch del piso → montante → servidor (PB) Cat6A / Cat7 network: Buscomm → floor switch → riser → server · Cat6A / Cat7 תשר: Buscomm ← גתמ ← דומע ← תרש
- - -	Cat6 al pulsador opcional de presencia / cancelación Cat6 to optional presence / cancel button · Cat6 ללחצן תוחכונ ילנויצפוא

MIGDALEI YAM A TIJON · DEPARTAMENTOS TUTELADOS

Sistema de llamada de enfermería – PB + 6 pisos · 36 departamentos

Sistema: ACE BG · Advantecnia Elaboró: Telab International

VISTAS 3D – CABLEADO Y EDIFICIO

3D views – wiring and building

ESCALA · SCALE	FECHA · DATE	REV	LÁMINA
S/E	12/10/2026	A	07

Cotas en metros · Dimensions in m · םירטמב תודימ

Formato A1 · Rev. A – Anteproyecto