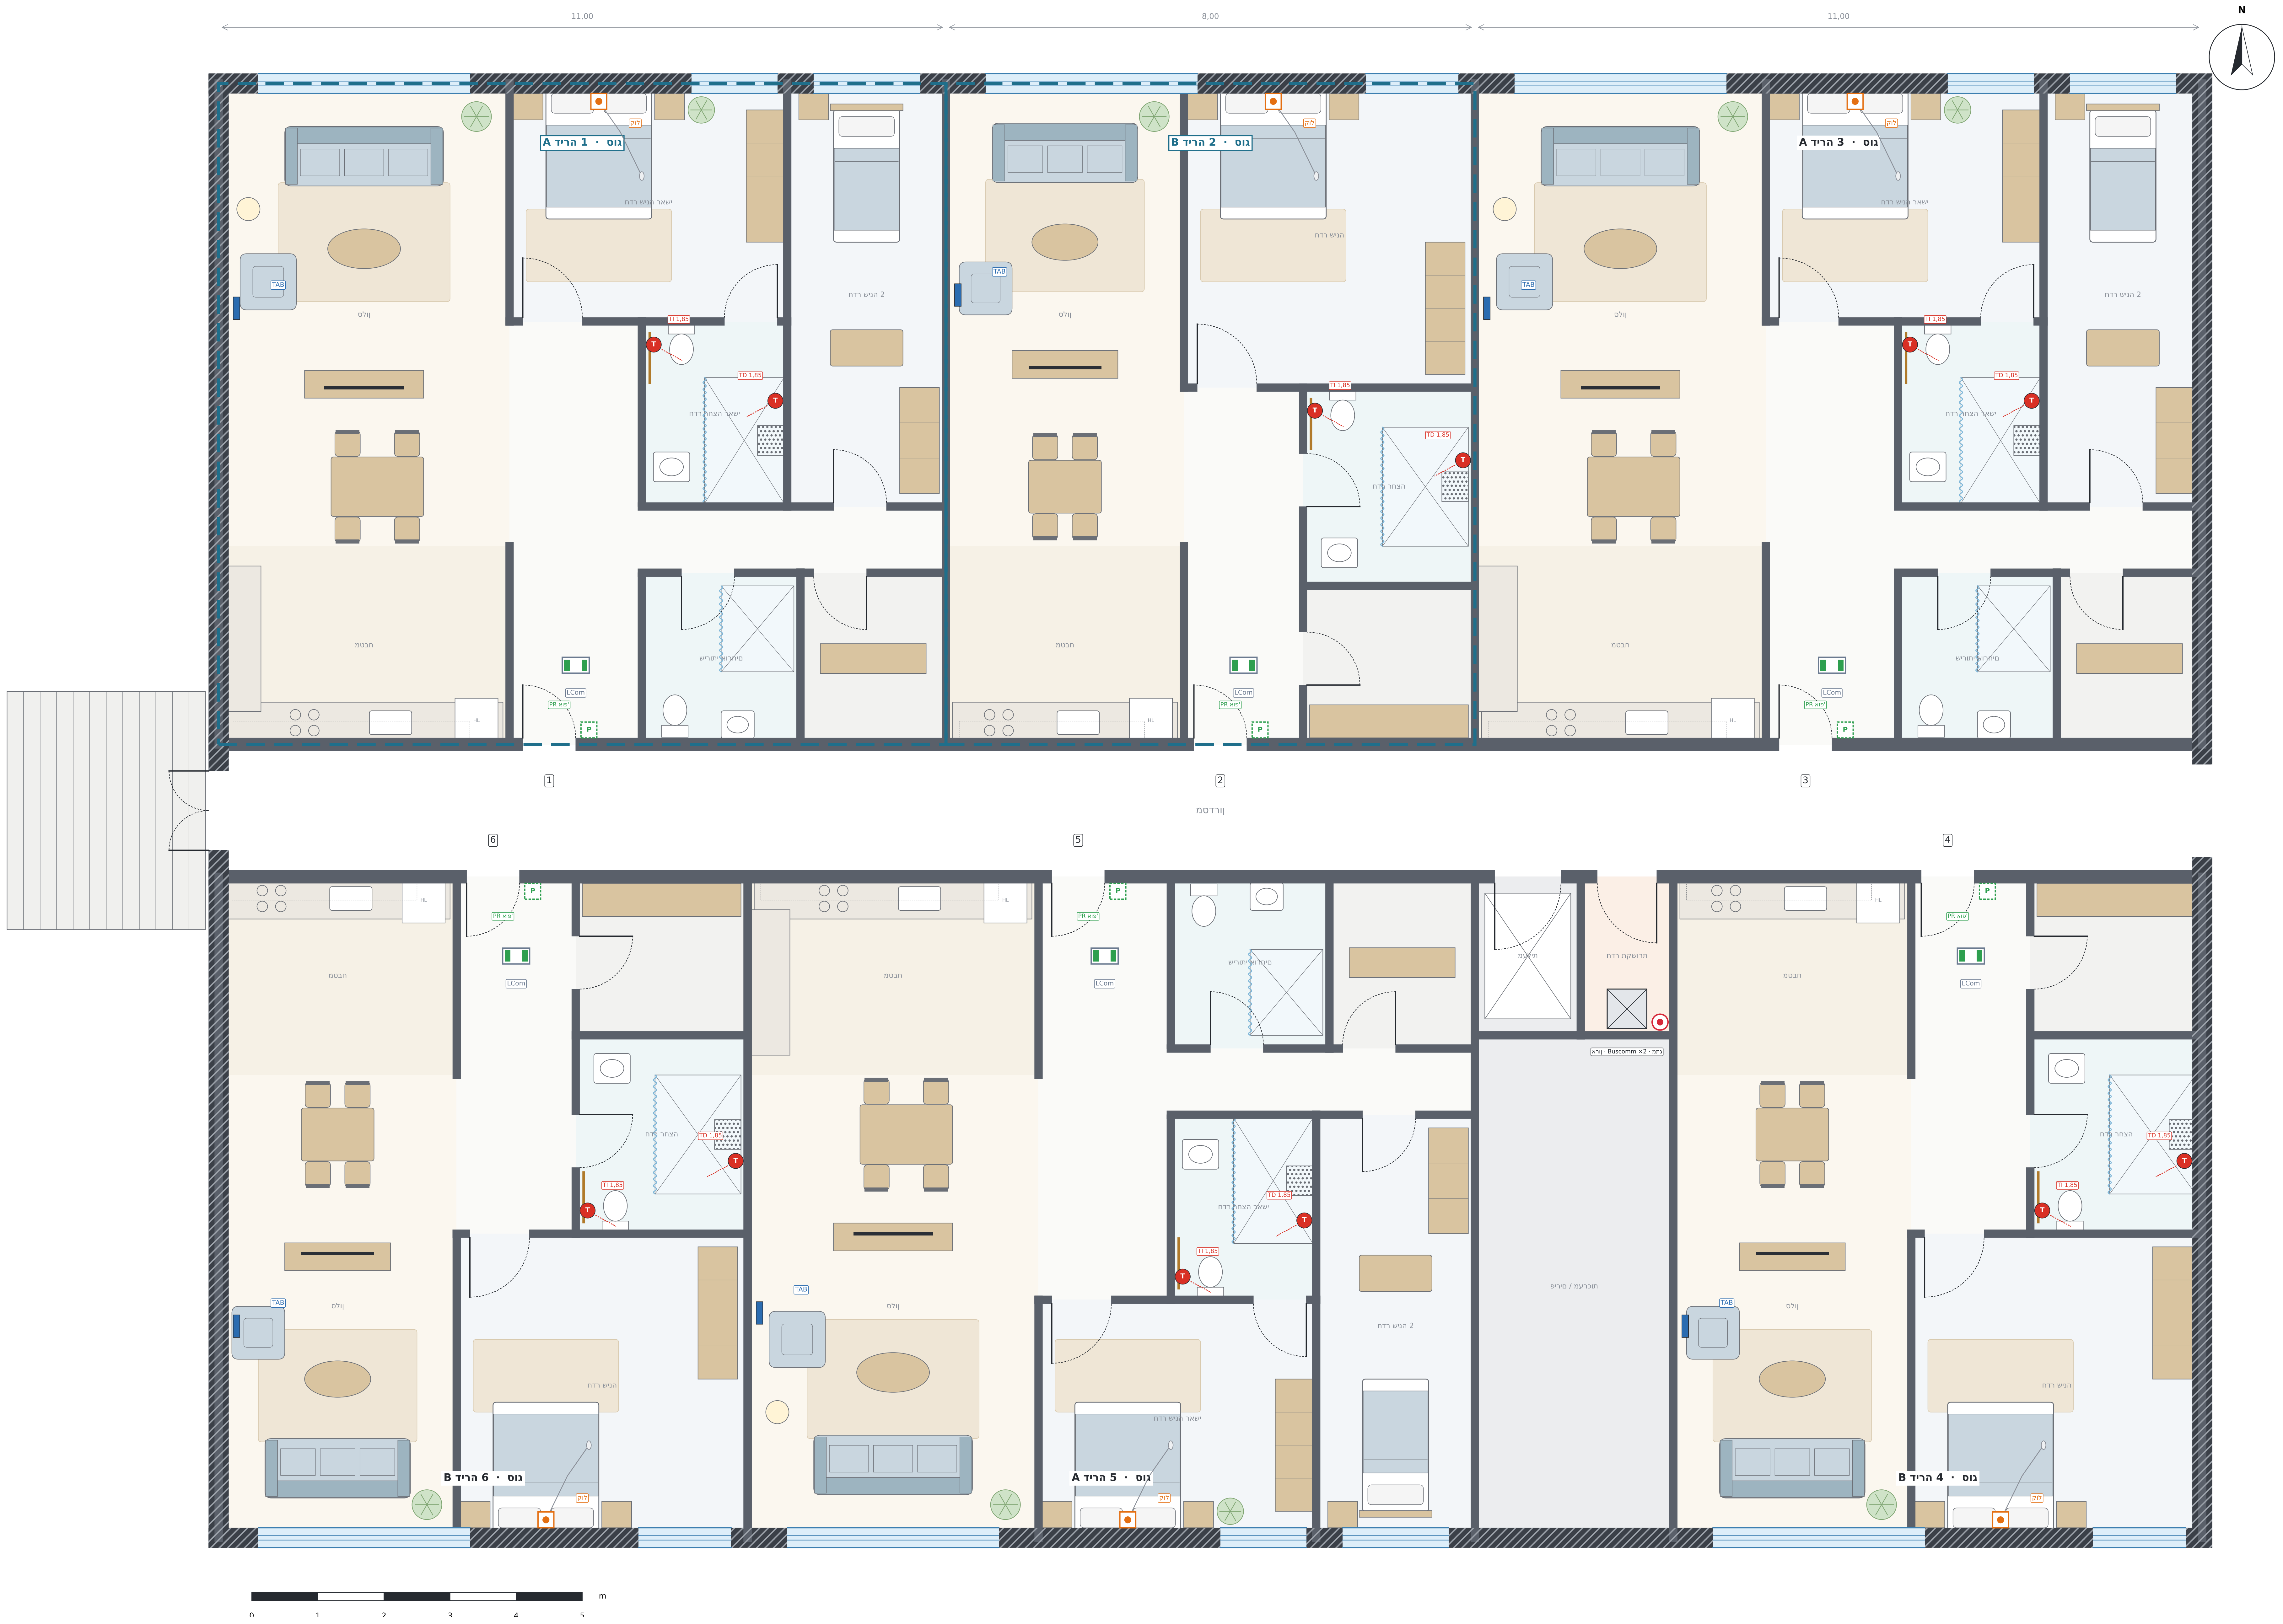

תורעה

tipo: 6 departamentos intercalados 1. הפצר
(A-B-A al norte, B-A-B al sur). Se destacan
el 1 (tipo A) y el 2 (tipo B).

2. גוס A: ןולס + חבטמ חותפ, רדח הניש
ישאר םע רדח הצחר דומצ (תחלקמ +
הלסא), רדח הניש 2, יתוריש םיחרוא
םע תחלקמ, האובמ ןסחמו.

3. גוס B: ןולס + חבטמ חותפ, רדח
הניש דחא ורדח הצחר םע תחלקמ.

4. לכב הריד: טלבאט דיאורדנא ןולסב,
ישארה הנישה רדחב תילוק האירק
ו-2 תוכישמ לבח (הלסא ותחלקמ)
ישארה הצחרה רדחב.

5. ןצחל תוחכונ / לוטיב דיל
תלד הסינכה: ילנויצפוא.

6. רדח תרושקת המוקה דיל תילעמה;
םדרגות הצקב יברעמה.

7. ריהוט יתיב (אל תיב-םילוח).

םילמס

▮	TAB · טלבאט דיאורדנא ןולסב – האירק רובידו Android tablet in the living room – call and voice · טלבאט דיאורדנא ןולסב – האירק רובידו
●	TI / TD · תוכישמ לבח הלסא / תחלקמ ACE40320303W (רדח הצחר ישאר, הבוג 1.85 מ') Toilet / shower pull-cord ACE40320303W (main bath, h 1.85 m) · תוכישמ לבח הלסא / תחלקמ ACE40320303W
▮▮	LCom ACE71610003 · זכרמ הרידה (תרקת האובמה) LCom ACE71610003 · apartment hub (hall ceiling) · LCom ACE71610003 · זכרמ הריד (תרקת האובמה)
●	לוק · האירק תוחא תילוק ACE82182451 (רדח הניש ישאר) Voice nurse call ACE82182451 (main bedroom) · האירק תוחא תילוק ACE82182451 (רדח הניש ישאר)
P	PR · תוחכונ / לוטיב junto a la puerta – OPCIONAL Presence / cancel next to the door – OPTIONAL · תוחכונ / לוטיב דיל תלדה – ילנויצפוא
ןורא	del piso: 2 Buscomm ACE70810000 + switch PoE ACEUCM6302 ןורא Floor rack: 2 Buscomm ACE70810000 + PoE switch ACEUCM6302 · 2 :ןורא המוק Buscomm + גתמ PoE

ןגומ רויד · ןוכיתה םי ילדגמ

תוריד 36 · תומוק 6 + עקרק – תוחא תאירק תכרעמ

Telab International :ןכוה ע"י ACE BG · Advantecnia :תכרעמ

דויצ – תיסופיט המוק

Typical floor – equipment

הדימ הנק	ךיראת	REV	ןוילג
1:60	12/10/2026	A	01

םירטמב תודימ

טמרופ A1 · הרודהמ A – תנכות םדקומ

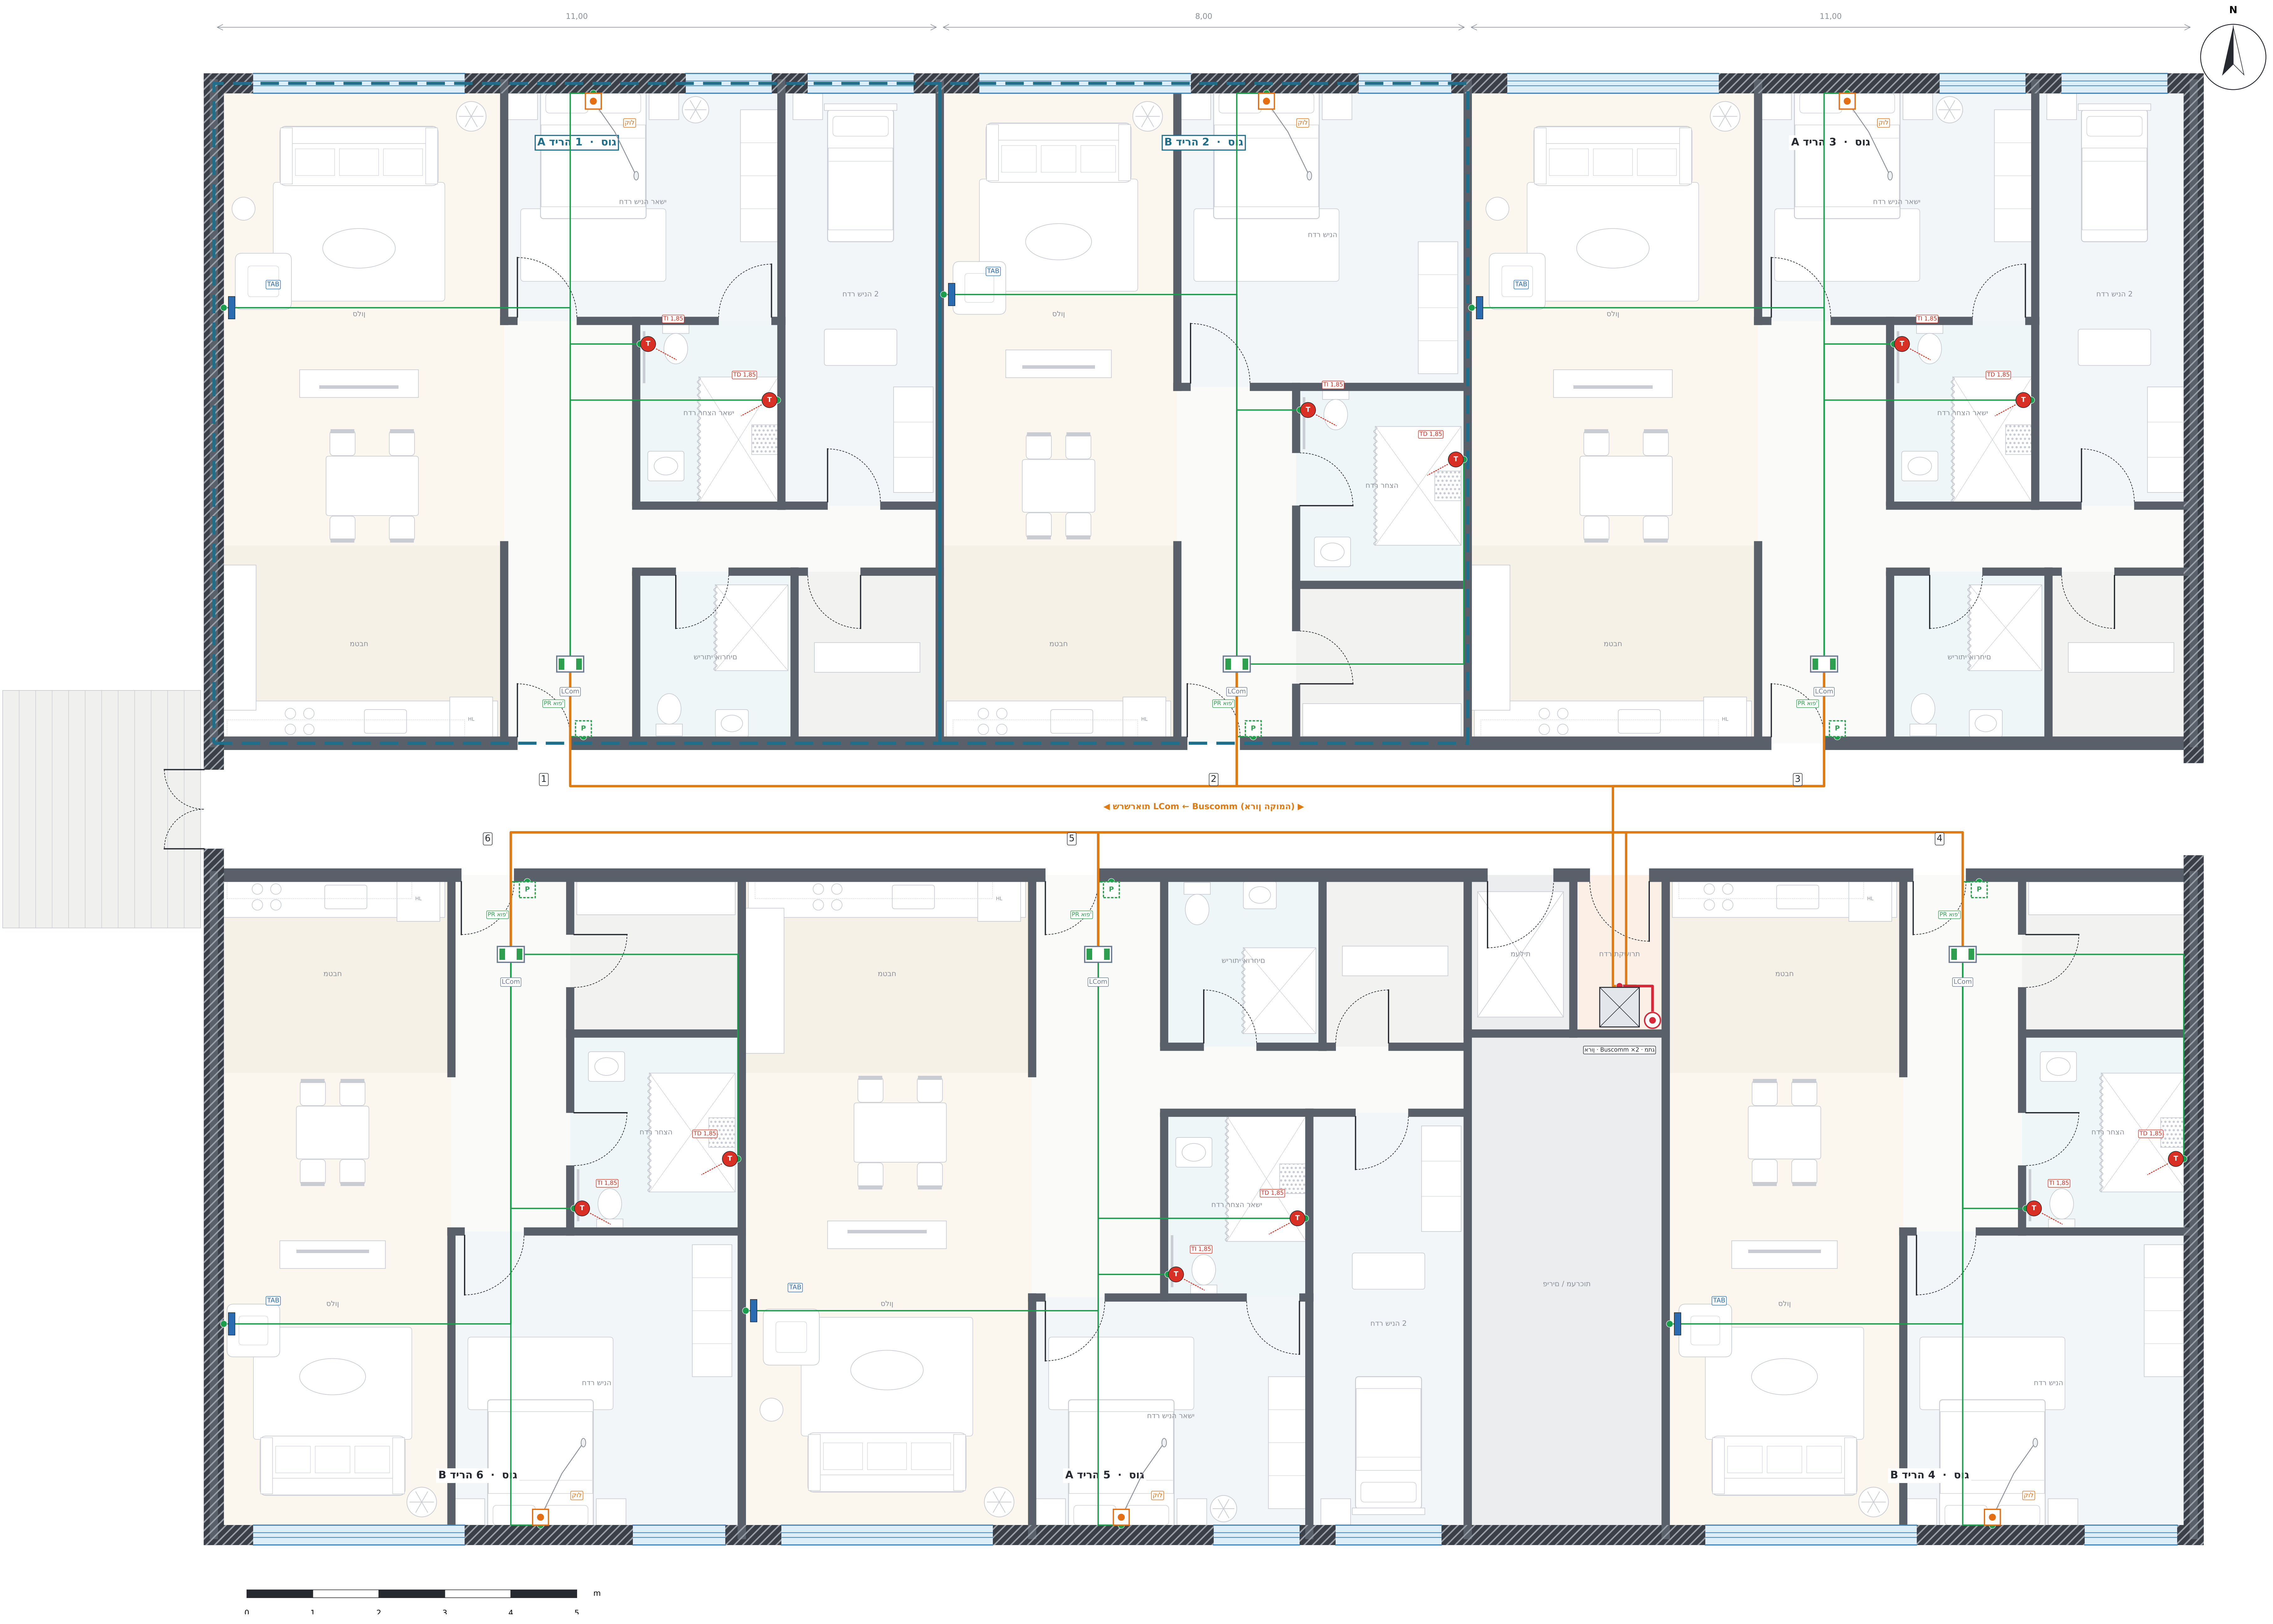

תורעה

tipo: 6 departamentos intercalados 1. הפצר
(3 tipo A + 3 tipo B). Se destacan el 1 (A)
y el 2 (B), detallados en las láminas 03 y 04.

2. בכל הריד LCom בתקרת האובמה:
לכ ההתקנים מגיעים אליו
.Cat6 ילאידר טוויחב

:Buscomm-משורשרים בשלשות ל LCom-3. ה
,Buscomm 1 ← 1-2-3 ןופצ
.Buscomm 2 ← 4-5-6 םורד

4. 2 ה-Buscomm ומתג ה-PoE םיאצמנ
בארון התקשורת של הקומה,
ליד המעלית.

5. םירשרושמ תומוקה 6 לש םיגתמה
בעמוד עד השרת במוקמת הקרקע.
תרשים אנכי בגיליון 05.

6. לכ המערכת PoE: ןיא ךרוצ
במעגלי חשמל בדירות.

7. ללא מנורת מסדרון. הקריאה מגיעה
בקול / התראה למעמדת האחות
בקבלה (קרקע).

טווח – הכול Cat6 / Cat7 ו-PoE (ללא משחל למערכת)

━ Cat6 ילאידר: כל התקן בדירה ← ה-LCom שלה
Cat6 radial: each device → its LCom · Cat6 ילאידר: לכ התקן ← LCom

━ Cat6A / Cat7 רשת: Buscomm ← מתג הקומה ← עמוד ← שרת (קרקע)
Cat6A / Cat7 network: Buscomm → floor switch → riser → server · Cat6A / Cat7 רשת: Buscomm ← מתג ← עמוד ← שרת

━ Cat6 / Cat7 בשרשרת: LCom ← LCom ← LCom ← Buscomm (3 לכל Buscomm)
Cat6 / Cat7 chain: LCom → LCom → LCom → Buscomm · Cat6 / Cat7 שרשרת: LCom ← LCom ← Buscomm

╍ Cat6 ללחצן נוכחות / ביטול אופציונלי
Cat6 to optional presence / cancel button · Cat6 ללחצן נוכחות אופציונלי

םילמס

▮ TAB · טאבלט אנדרואיד בסלון – קריאה ודיבור
Android tablet in the living room – call and voice · טאבלט אנדרואיד בסלון – קריאה ודיבור

T TI / TD · משיכה לבית השימוש / מקלחת ACE40320303W (חדר רחצה ראשי, גובה 1.85 מ')
Toilet / shower pull-cord ACE40320303W (main bath, h 1.85 m) · משיכה לבית השימוש / מקלחת ACE40320303W

▮▮ LCom ACE71610003 · רכזת הדירה (תקרת המבואה)
LCom ACE71610003 · apartment hub (hall ceiling) · LCom ACE71610003 · רכזת הדירה (תקרת המבואה)

◉ קול · קריאת אחות קולית ACE82182451 (חדר שינה ראשי)
Voice nurse call ACE82182451 (main bedroom) · קריאת אחות קולית ACE82182451 (חדר שינה ראשי)

P PR · נוכחות / ביטול junto a la puerta – OPCIONAL
Presence / cancel next to the door – OPTIONAL · נוכחות / ביטול ליד הדלת – אופציונלי

ארון del piso: 2 Buscomm ACE70810000 + switch PoE ACEUCM6302 ארון
Floor rack: 2 Buscomm ACE70810000 + PoE switch ACEUCM6302 · 2 :ארון הקומה Buscomm + מתג PoE

מגדלי םי התיכון · דיור מוגן
מערכת קריאת אחות – קרקע + 6 קומות · 36 דירות
Telab International :הוכן ע"י ACE BG · Advantecnia :מערכת

טווח – תיסופיט המוק
Typical floor – wiring

קנה מידה	תאריך	REV	גיליון
1:60	12/10/2026	A	02

מידות במטרים
פורמט A1 · מהדורה A – לתכנון מוקדם

A · 1:50 · דויצ

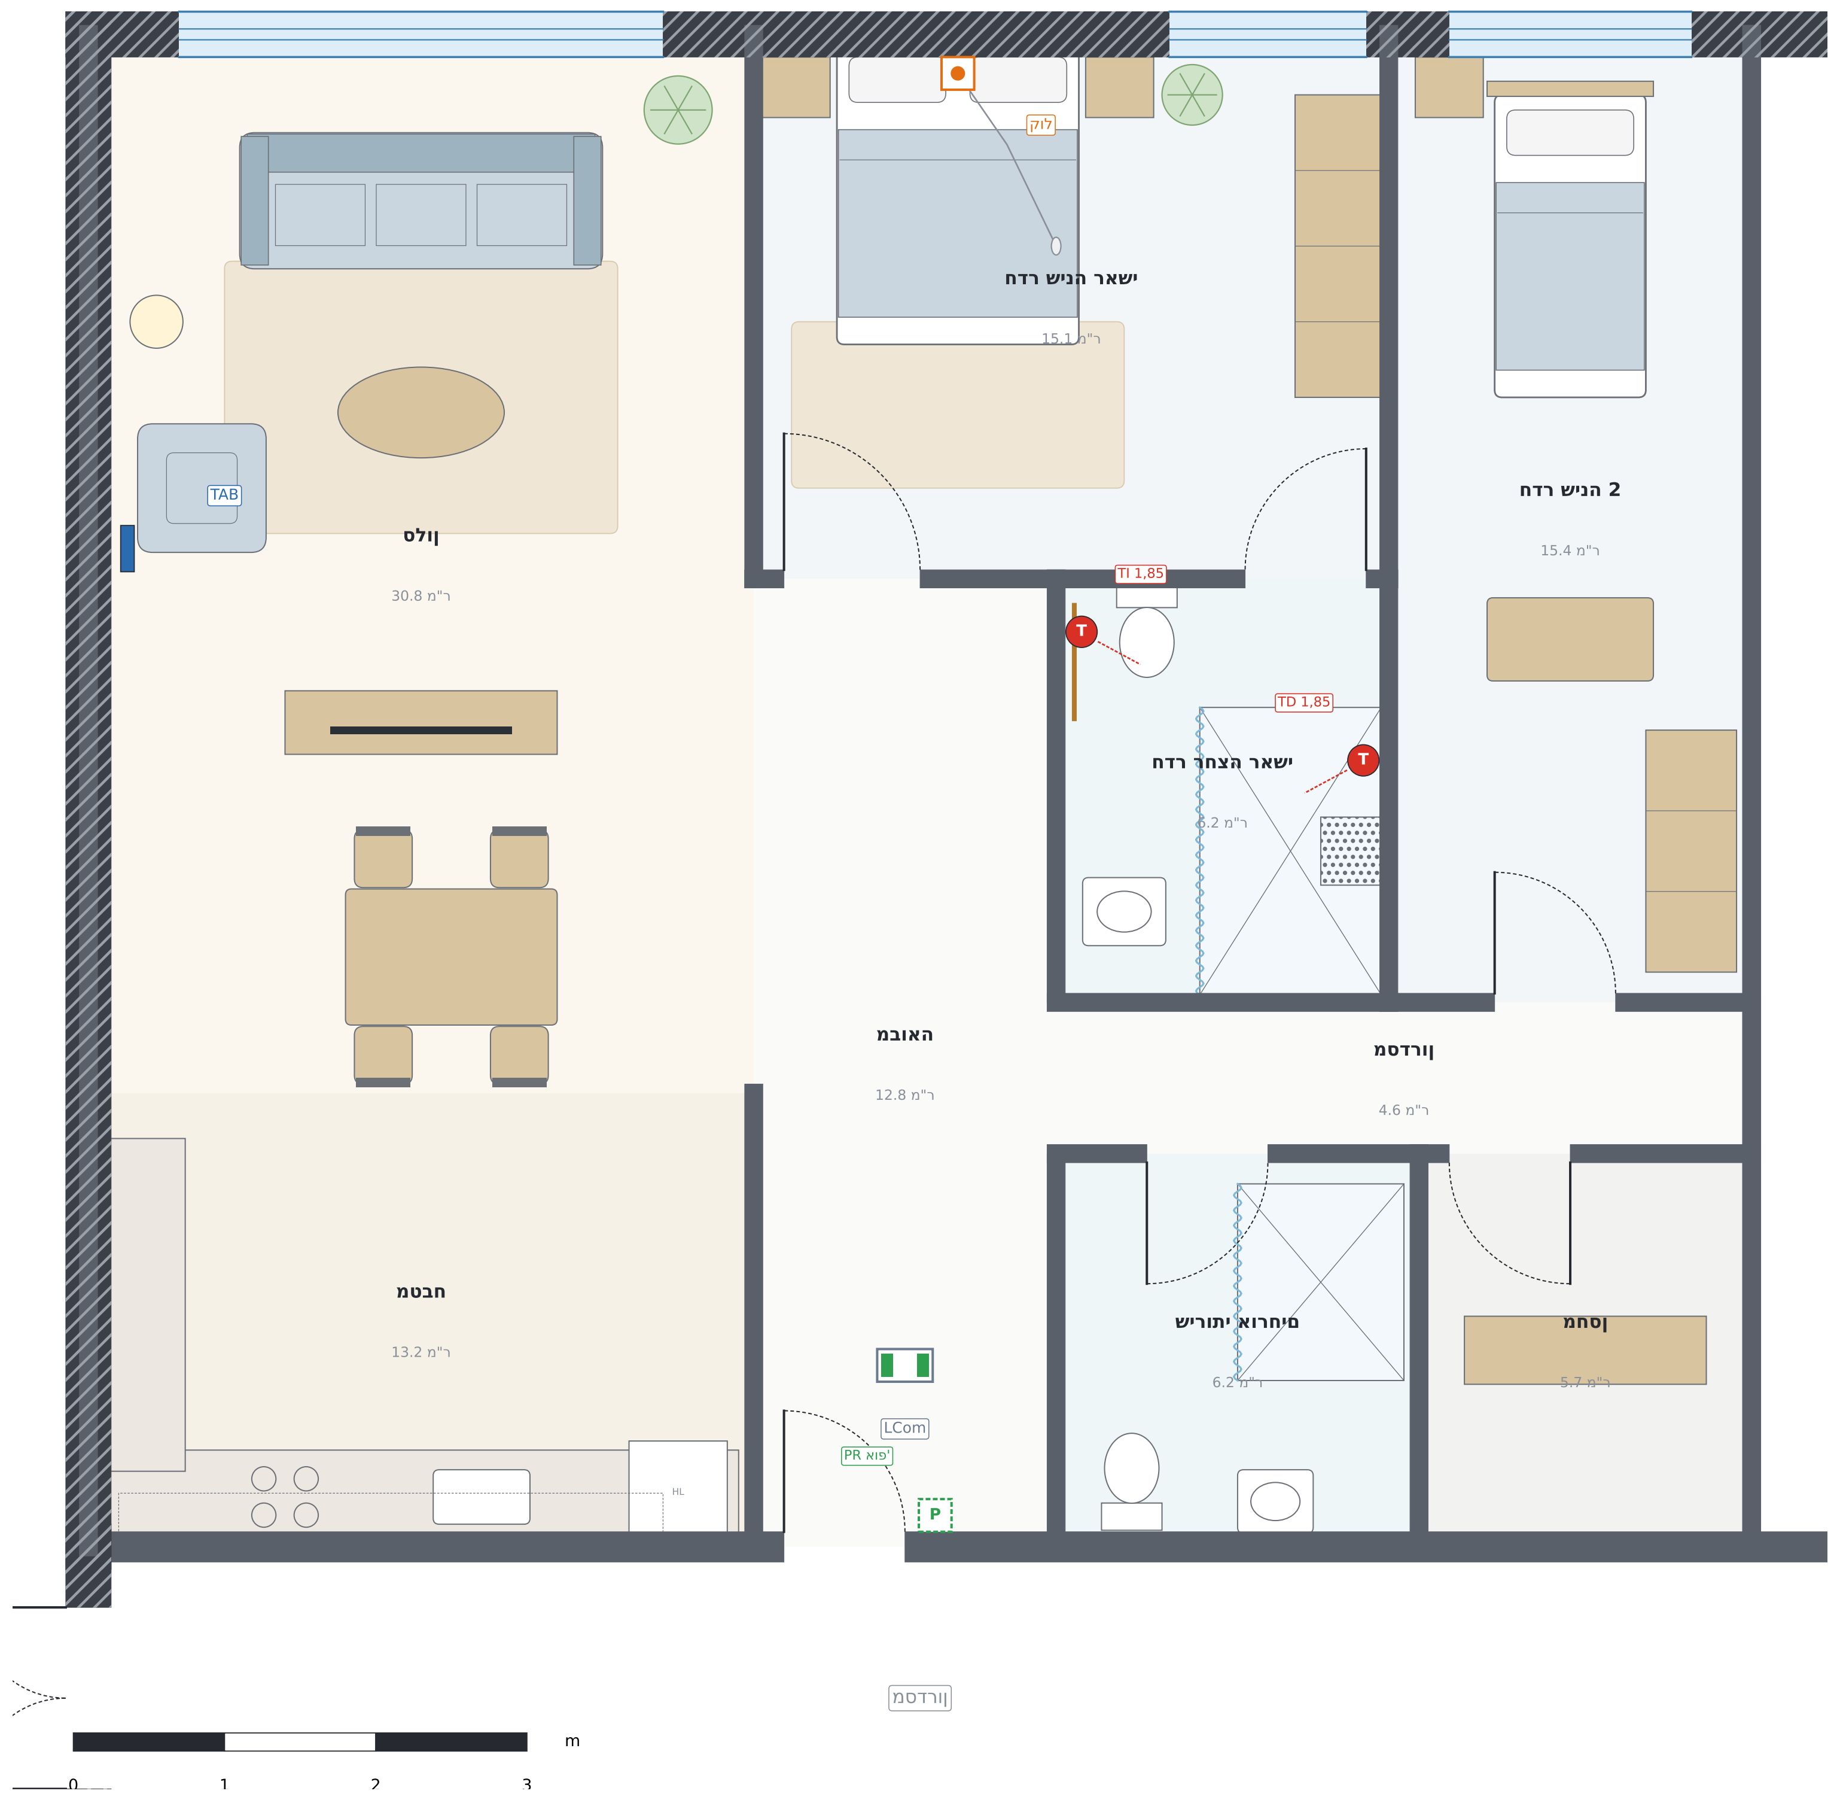

B · 1:50 · טוויח

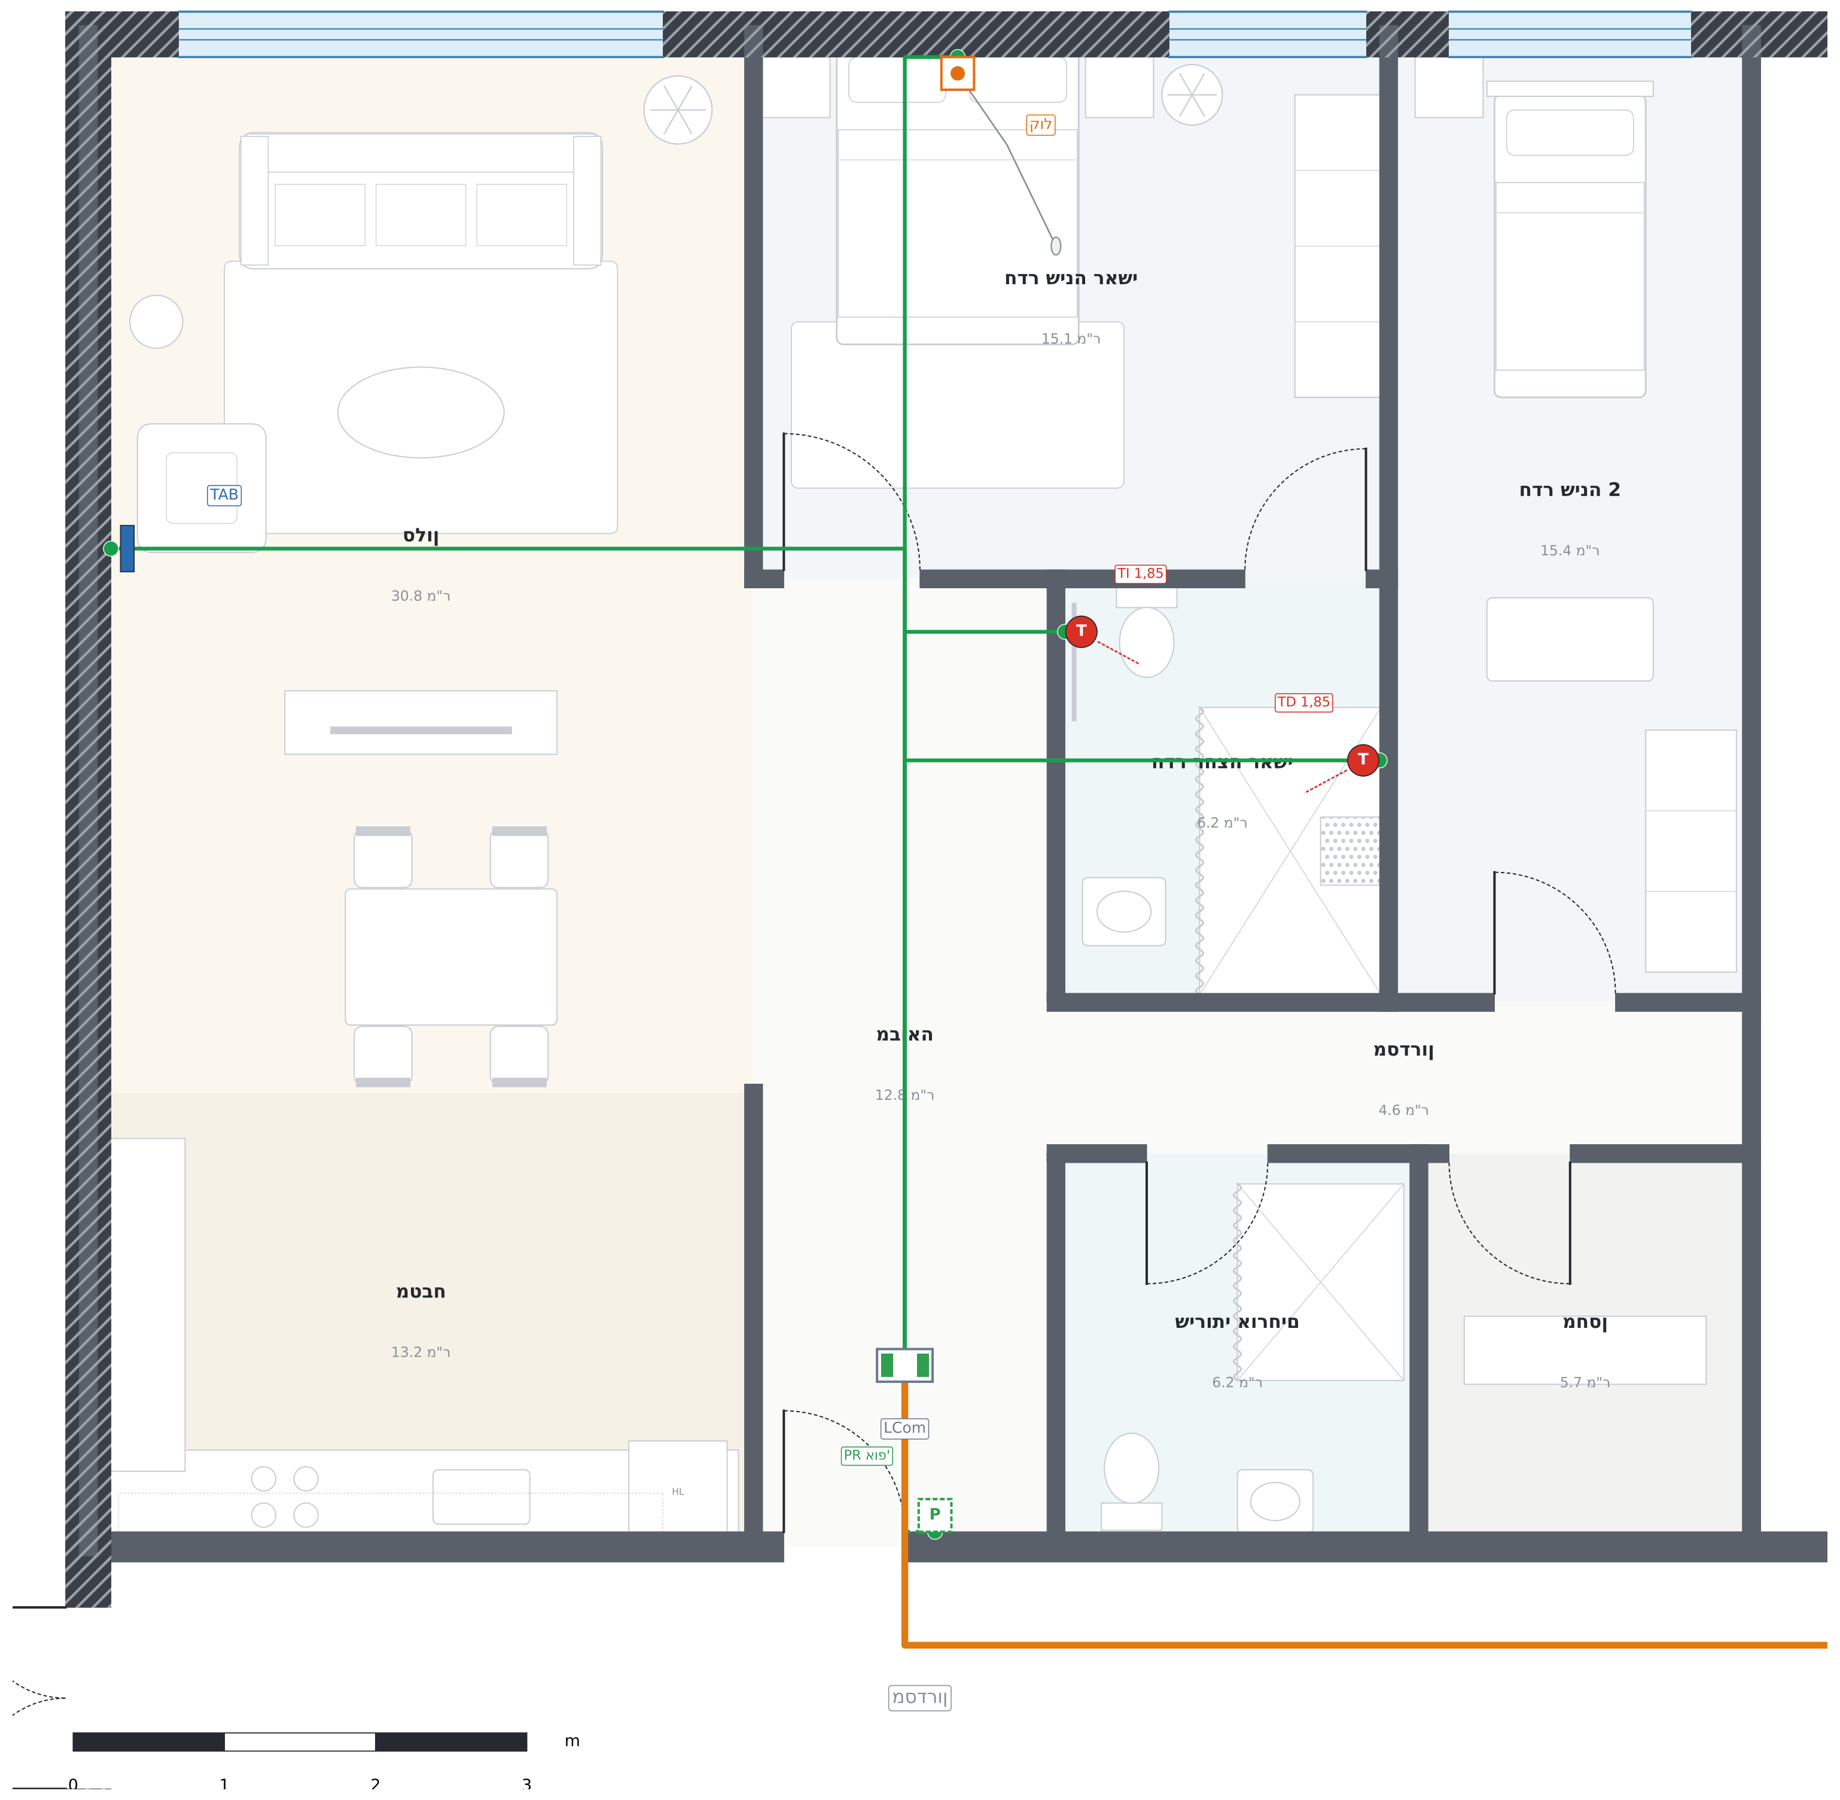

תורעה

1. הריד 1 – גוס A, כ-110 ר"מ.
2. ןולס םע חבטמ חותפ; יתוריש םיחרוא םע תחלקמ דיל ןולסה.
3. ישאר הניש רדח םע רדח הצחר דומצ (תחלקמ + הלסא) ורדחו הניש 2.
4. האירק: טלבאט דיאורדנא ןולסב, האירק תילוק רדחב הנישה ישארה, תוכישמ לבח הלסאב ובו תחלקמב לש רדח הצחרה ישארה.
5. ןצחל תוחכונ / לוטיב דיל תלדה: ילנויצפוא (וקווקמ).
6. לוכה Cat6 ילאידר ל-LCom האובמב; ה-LCom ךישממ תרשרשב לא ה-Buscomm. לוכה לש המוקה PoE.

C · גובהי הנקתה (תיזח תיטמכס)

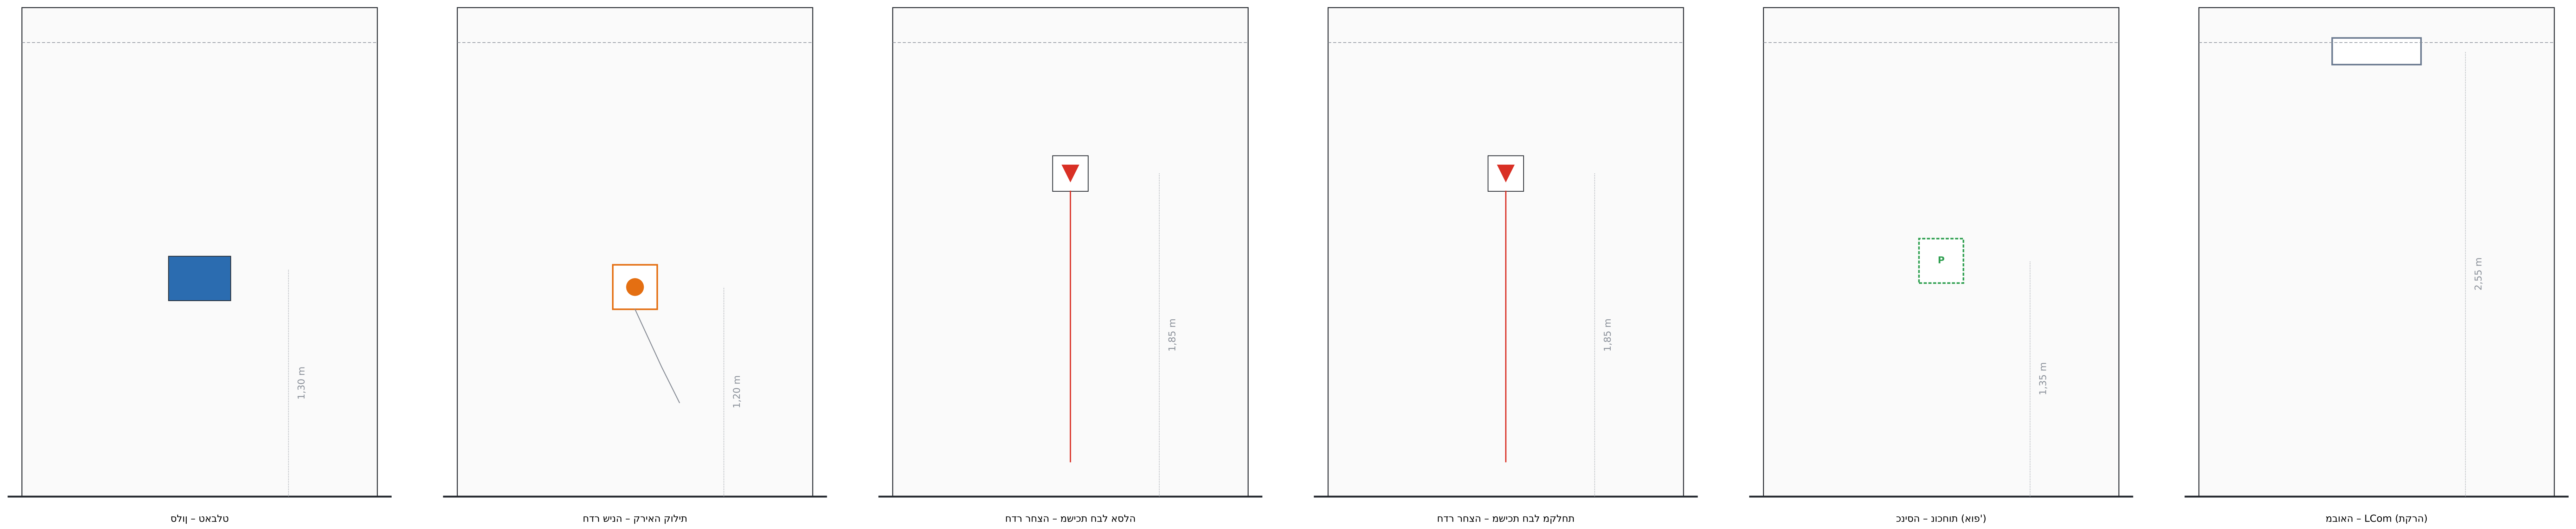

ןולס – טלבאט

הניש רדח – האירק תילוק

הצחר רדח – הלסא לבח תכישמ

הצחר רדח – תחלקמ לבח תכישמ

הסינכ – תוחכונ ('פוא)

האובמ – LCom (הרקת)

SÍMBOLOS Y CABLEADO · SYMBOLS & WIRING

🟦 TAB · טלבאט דיאורדנא ןולסב – האירק רובידו
Android tablet in the living room – call and voice · טלבאט דיאורדנא ןולסב – האירק רובידו

● TI / TD · תכישמ לבח הלסא / תחלקמ ACE40320303W (רדח הצחר ישאר, הבוג 1.85 'מ)
Toilet / shower pull-cord ACE40320303W (main bath, h 1.85 m) · תכישמ לבח הלסא / תחלקמ ACE40320303W

🟩 LCom ACE71610003 · זכרמ הרידה (תרקת האובמה)
LCom ACE71610003 · apartment hub (hall ceiling) · LCom ACE71610003 · זכרמ הריד (תרקת האובמה)

━ Cat6 / Cat7 תרשרשב: LCom ← LCom ← LCom ← Buscomm (3 לכל Buscomm)
Cat6 / Cat7 chain: LCom → LCom → LCom → Buscomm · Cat6 / Cat7 תרשרש: LCom ← LCom ← Buscomm

▣ לוק · תאירק תוחא תילוק ACE82182451 (רדח הניש ישאר)
Voice nurse call ACE82182451 (main bedroom) · תאירק תוחא תילוק ACE82182451 (רדח הניש ישאר)

P PR · תוחכונ / לוטיב junto a la puerta – OPCIONAL
Presence / cancel next to the door – OPTIONAL · תוחכונ / לוטיב דיל תלדה – ילנויצפוא

━ Cat6 ילאידר: לכ ןקתה הרידב ← ה-LCom הלש
Cat6 radial: each device → its LCom · Cat6 ילאידר: לכ ןקתה ← LCom

╍ Cat6 ןצחלל תוחכונ / לוטיב ילנויצפוא
Cat6 to optional presence / cancel button · Cat6 ןצחלל תוחכונ ילנויצפוא

ןגומ רויד · ןוכיתה םי ילדגמ
תכרעמ תאירק תוחא – עקרק + 6 תומוק · 36 תוריד
Telab International :ןכוה ע"י ACE BG · Advantecnia :תכרעמ

גוס הריד A – טרפ

Apartment type A – detail

הדימ הנק	ךיראת	REV	ןוילג
1:50	12/10/2026	A	**03**

םירטמב תודימ
טמרופ A1 · הרודהמ A – תנכנון םדקומ

A · 1:45 · דויצ

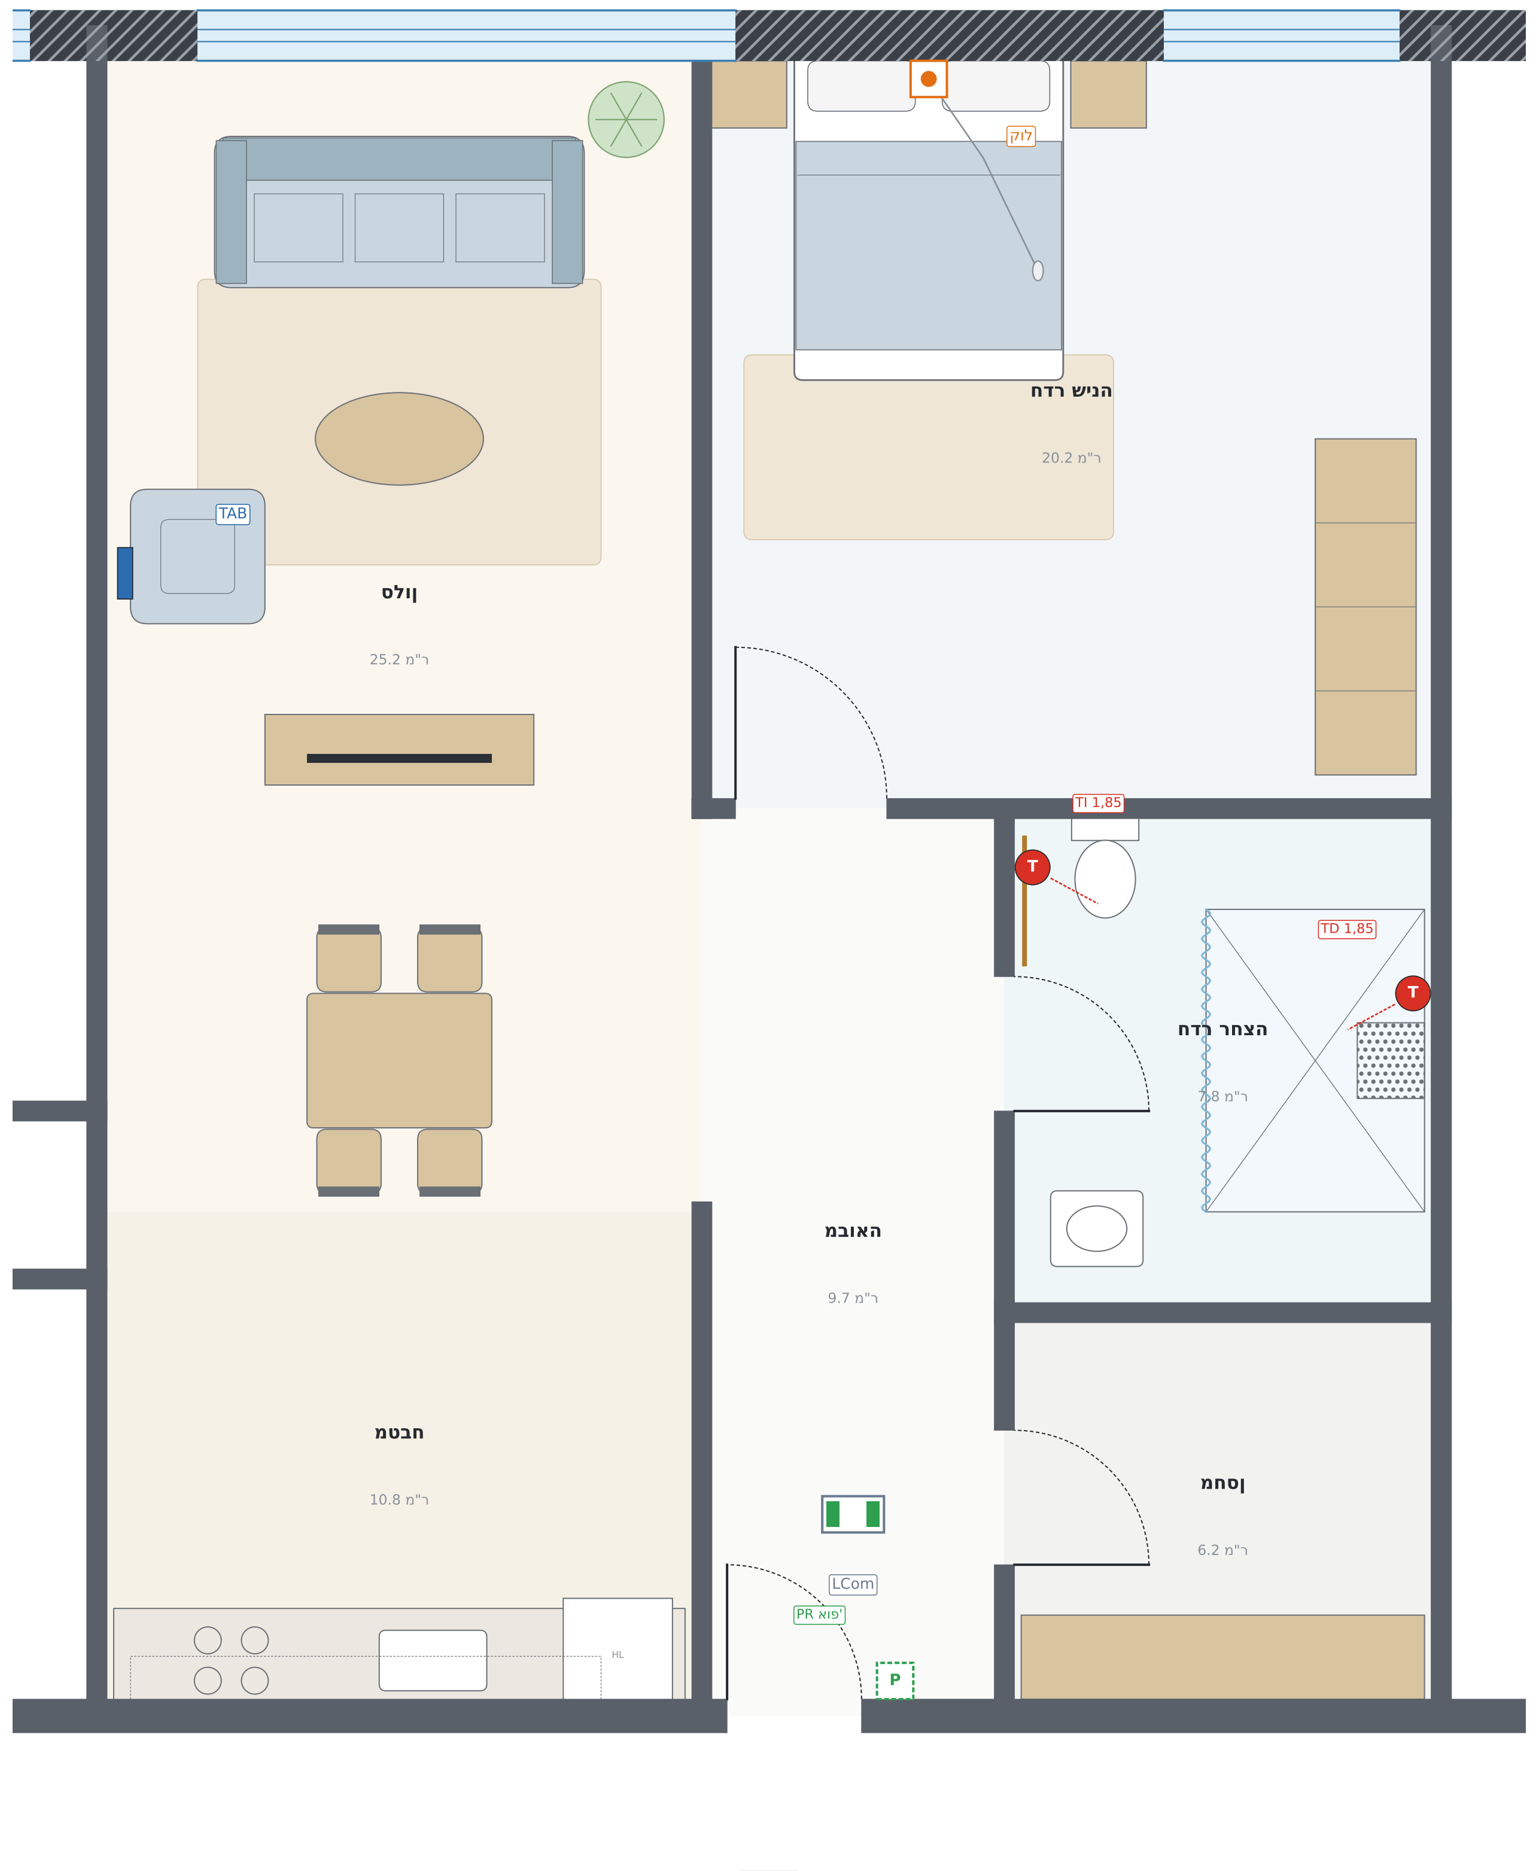

B · 1:45 · טוויח

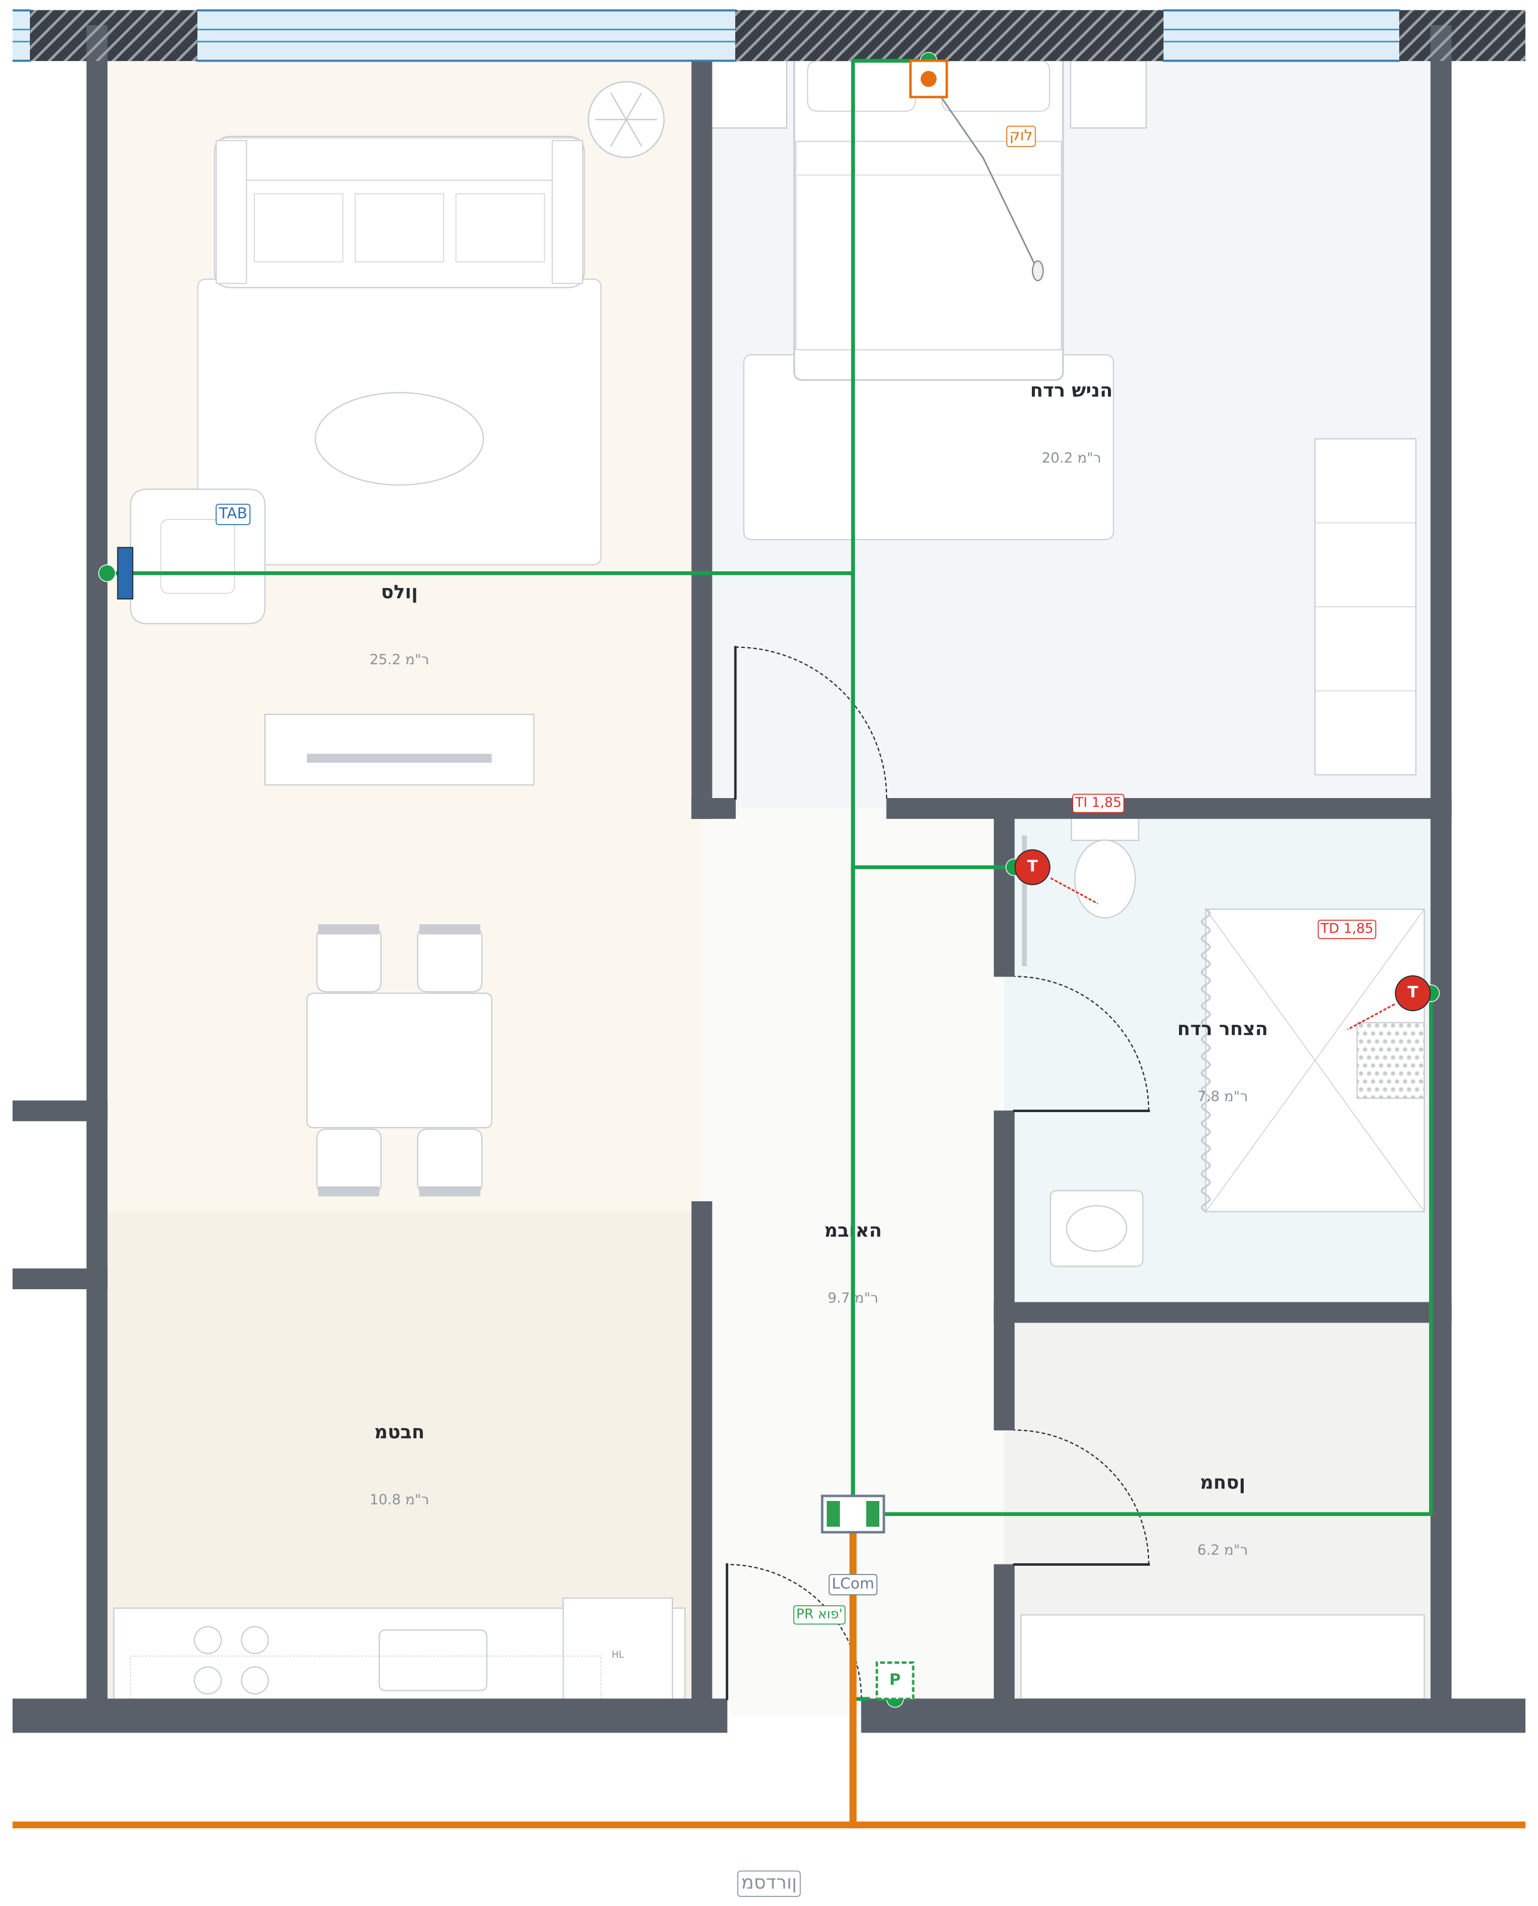

הערות

1. הריד 2 – גוס B, כ-80 ר"מ.
2. ןולס םע חבטמ חותפ, הניש רדח דחא ורדח הצחר םע תחלקמ.
3. האירק: טלבאט דיאורדנא ןולסב, האירק תילוק רדחב הנישה, תוכישמ לבח הלסאב תחלקמבו.
4. ןצחל תוחכונ / לוטיב דיל תלדה: ילנויצפוא (וקווקמ).
5. לוכה Cat6 ילאידר ל-LCom האובמב; ה-LCom ךישממ תרשרשב לא ה-Buscomm לוכה. המוקה לש PoE.

C · גובהי הנקתה (תיטמכס תיזח)

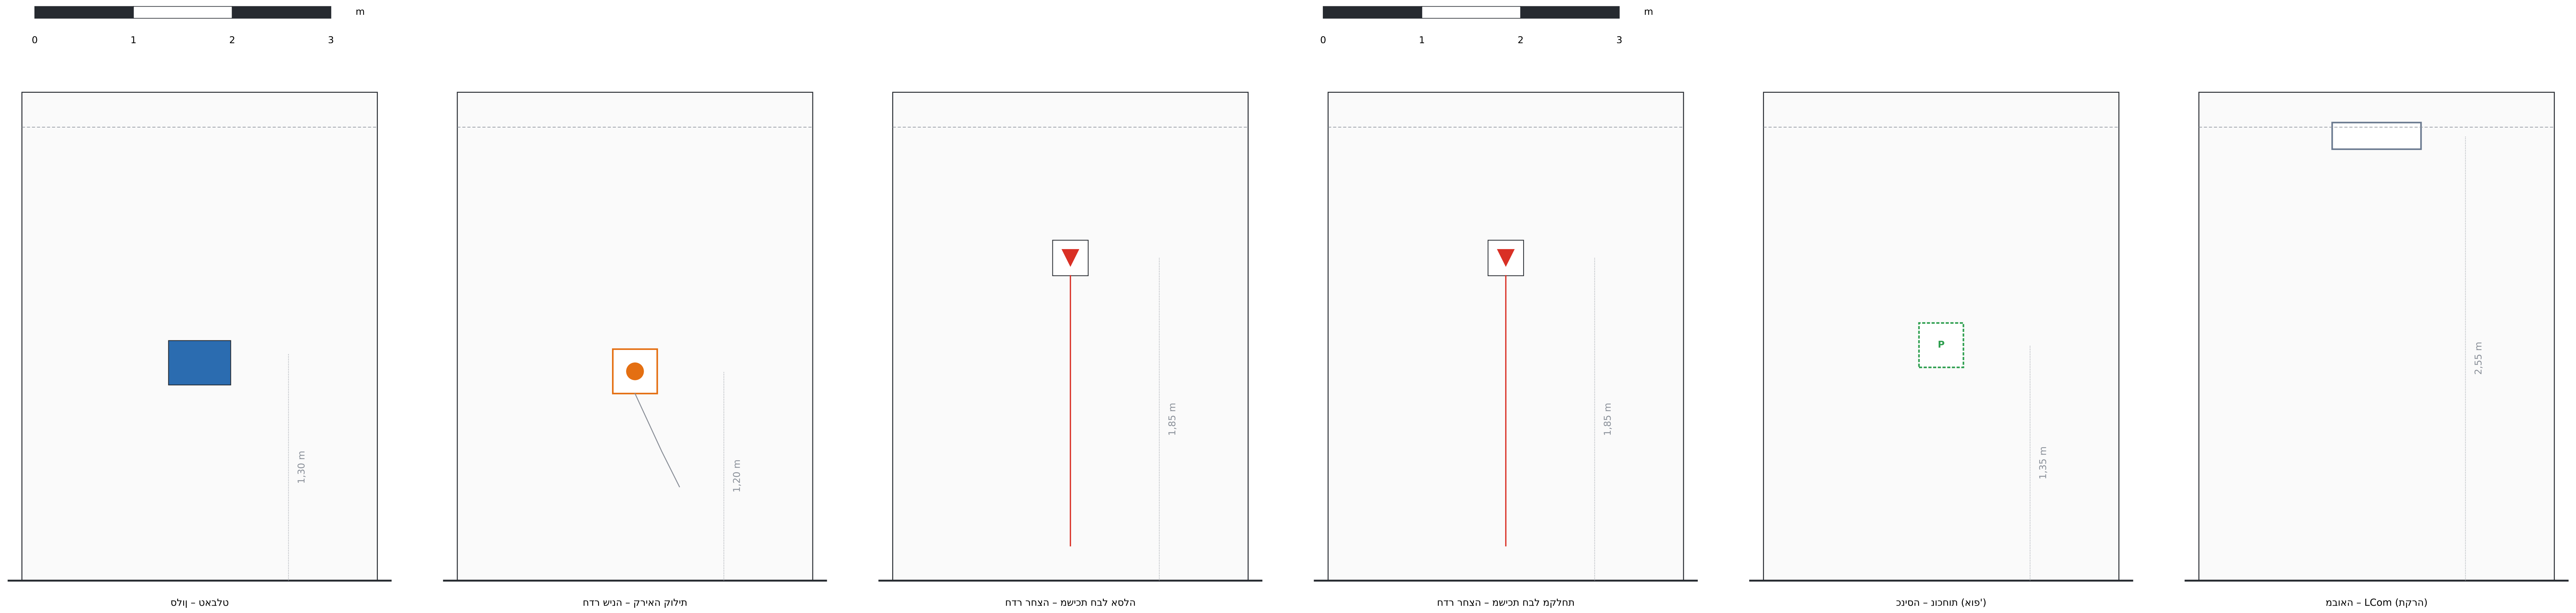

טלבאט – ןולס · תילוק האירק – הניש רדח · הלסא לבח תכישמ – הצחר רדח · תחלקמ לבח תכישמ – הצחר רדח · הסינכ – תוחכונ ('פוא) · האובמ – LCom (הרקת)

SÍMBOLOS Y CABLEADO · SYMBOLS & WIRING

🟦	TAB · טלבאט דיאורדנא ןולסב – האירק ודיבור Android tablet in the living room – call and voice · טלבאט דיאורדנא ןולסב – האירק ודיבור
● T	TI / TD · תכישמ לבח הלסא / תחלקמ ACE40320303W (רדח הצחר ישאר, הבוג 1.85 מ') Toilet / shower pull-cord ACE40320303W (main bath, h 1.85 m) · תכישמ לבח הלסא / תחלקמ ACE40320303W
🟩🟩	LCom ACE71610003 · זכרמ הרידה (תרקת האובמה) LCom ACE71610003 · apartment hub (hall ceiling) · LCom ACE71610003 · זכרמ הריד (תרקת האובמה)
━	Cat6 / Cat7 תרשרשב: LCom ← LCom ← LCom ← Buscomm (3 לכל Buscomm) Cat6 / Cat7 chain: LCom → LCom → LCom → Buscomm · Cat6 / Cat7 תרשרש: LCom ← LCom ← Buscomm
●	לוק · תאירק תוחא תילוק ACE82182451 (רדח הניש ישאר) Voice nurse call ACE82182451 (main bedroom) · תאירק תוחא תילוק ACE82182451 (רדח הניש ישאר)
P	PR · תוחכונ / לוטיב junto a la puerta – OPCIONAL Presence / cancel next to the door – OPTIONAL · תוחכונ / לוטיב דיל תלדה – ילנויצפוא
━	Cat6 ילאידר: לכ ןקתה הרידב ← ה-LCom הלש Cat6 radial: each device → its LCom · Cat6 ילאידר: לכ ןקתה ← LCom
╍	Cat6 ללחצן תוחכונ / לוטיב ילנויצפוא Cat6 to optional presence / cancel button · Cat6 ללחצן תוחכונ ילנויצפוא

ןגומ רויד · ןוכיתה םי ילדגמ

תוריד 36 · תומוק 6 + עקרק – תוחא תאירק תכרעמ

Telab International :ץעוי ACE BG · Advantecnia :תכרעמ

גוס הריד B – טרפ

Apartment type B – detail

הדימ הנק	ךיראת	REV	ןויליג
1:50	12/10/2026	A	04

םירטמב תודימ

טמרופ A1 · הרודהמ A – תוכנו םדקומ

A · תרשים אנכי של הבניין (קרקע + 6 קומות)

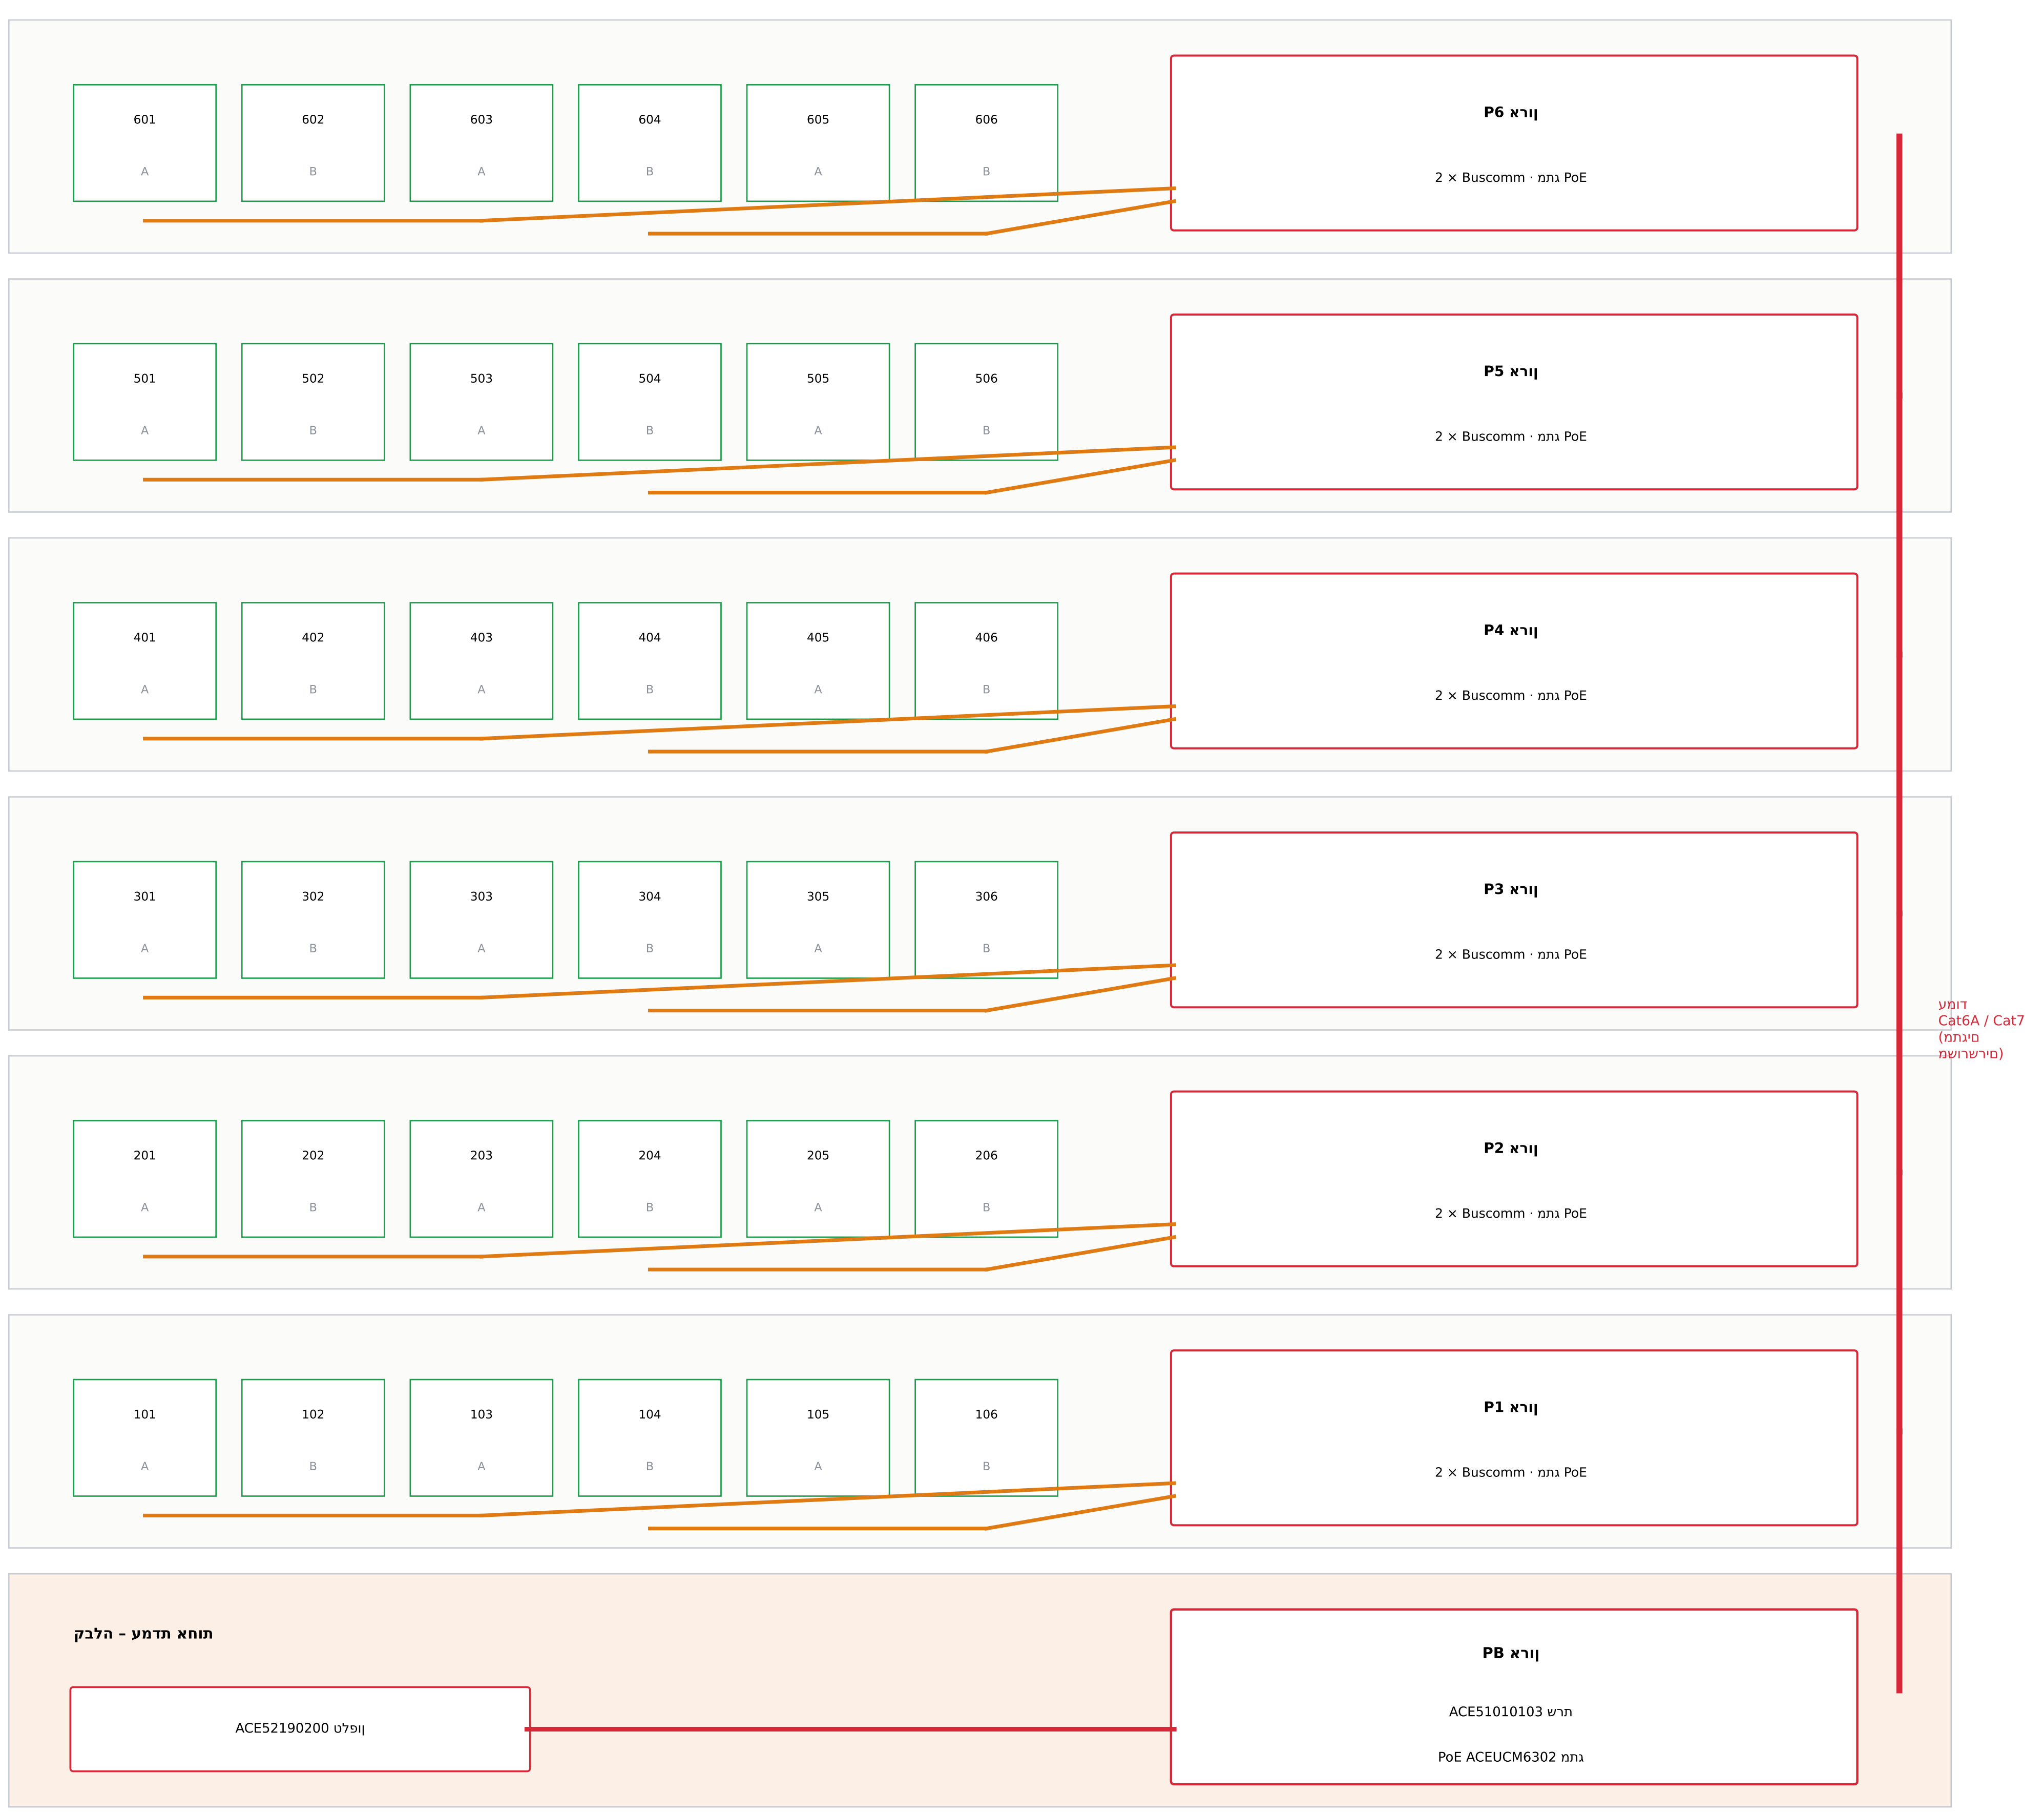

B · טופולוגיה לפי דירה ולפי קומה

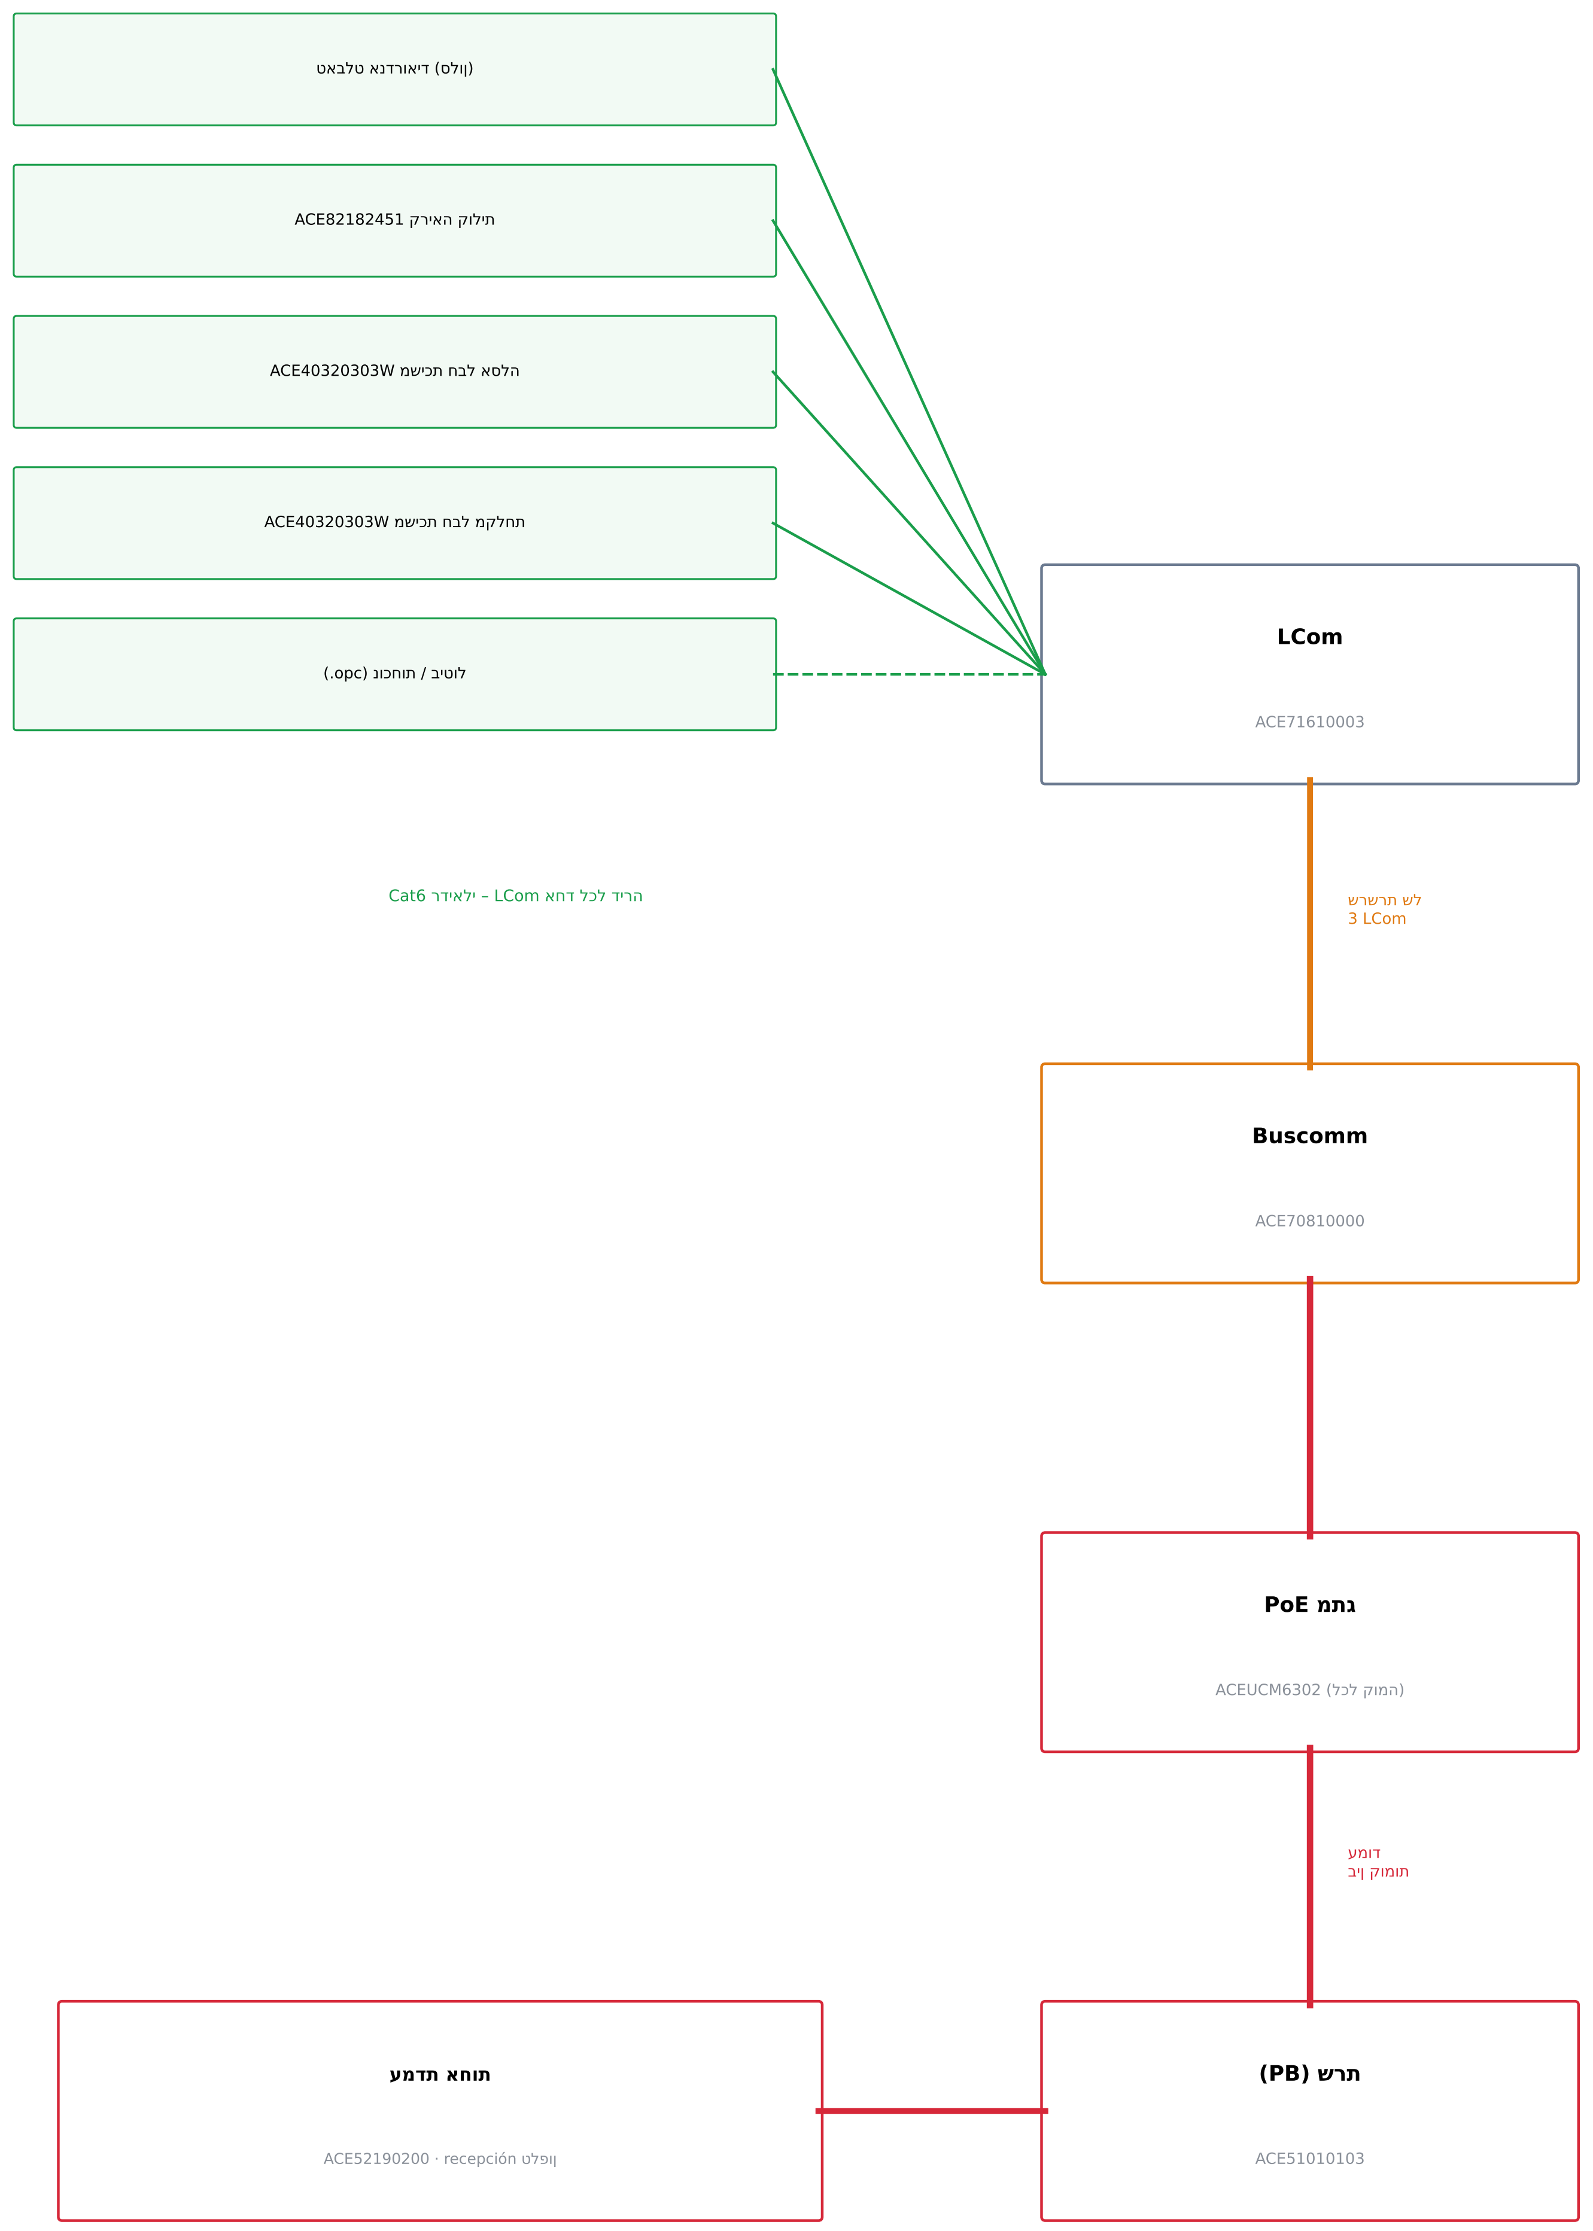

הערות

1. קומת קרקע: קבלה עם עמדת האחות (טלפון ACE52190200) והארון הראשי עם השרת.

s 1 a 6: 6 departamentos por piso2. רצפה (3 tipo A y 3 tipo B intercalados).

Buscomm (3 LCom 2 :3. בכל קומה לכל אחד) ומתג PoE בארון.

4. המתגים משורשרים מקומה לקומה בעמוד Cat6A / Cat7 עד השרת בקומת הקרקע.

.PoE 5. כל המערכת

6. הקריאות מגיעות לעמדת האחות בקול או כהתראה.

7. כמויות ראשוניות: לאמת מול Advantecnia ובאתר.

C · רשימת חומרים – כל הבניין (36 דירות)

קוד	תיאור	כמות	הערה
בכל דירה (× 36)			
TAB	טאבלט אנדרואיד על הקיר (סלון) – קריאה ודיבור	36	1 לכל דירה
קול	ACE82182451 – קריאת אחות קולית	36	חדר שינה ראשי
TI / TD	ACE40320303W – משיכת חבל אסלה / מקלחת	72	2 לכל דירה
PR	junto a la puerta – OPCIONAL נוכחות / ביטול	(36)	אופציונלי
LCom	ACE71610003 – מרכז דירה	36	1 לכל דירה
לכל קומה (× 6) וקומת קרקע			
BC	Buscomm – ACE70810000	12	2 לכל קומה (LCom 3 לכל אחד)
SW	PoE – ACEUCM6302 מתג	7	1 לכל קומה + קרקע
ארון	de comunicaciones con patch panel y UPS ארון	7	1 לכל קומה + קרקע
SV	Advantecnia – ACE51010103 שרת + תוכנת	1	קרקע
TEL	ACE52190200 – טלפון שולחני לאחיות	1	קבלה בקרקע
כבלים (קומה טיפוסית × 6, + 15% רזרבה)			
—	Cat6 רדיאלי בתוך הדירות (ירוק)	1640 m	237 מ' לקומה
—	Cat6 / Cat7 שרשרת LCom ← Buscomm (כתום)	620 m	89 מ' לקומה
—	Cat6A / Cat7 ארון + עמוד 7 מפלסים (אדום)	70 m	כולל עמוד

מגדלי ים התיכון · דיור מוגן
מערכת קריאת אחות – קרקע + 6 קומות · 36 דירות
הוכן ע"י: Telab International   מערכת: ACE BG · Advantecnia

תרשים אנכי, טופולוגיה וחומרים
Riser diagram, topology & bill of materials

קנה מידה	תאריך	REV	גיליון
ללא קנ"מ	12/10/2026	A	05

מידות במטרים
פורמט A1 · מהדורה A – תכנון מוקדם

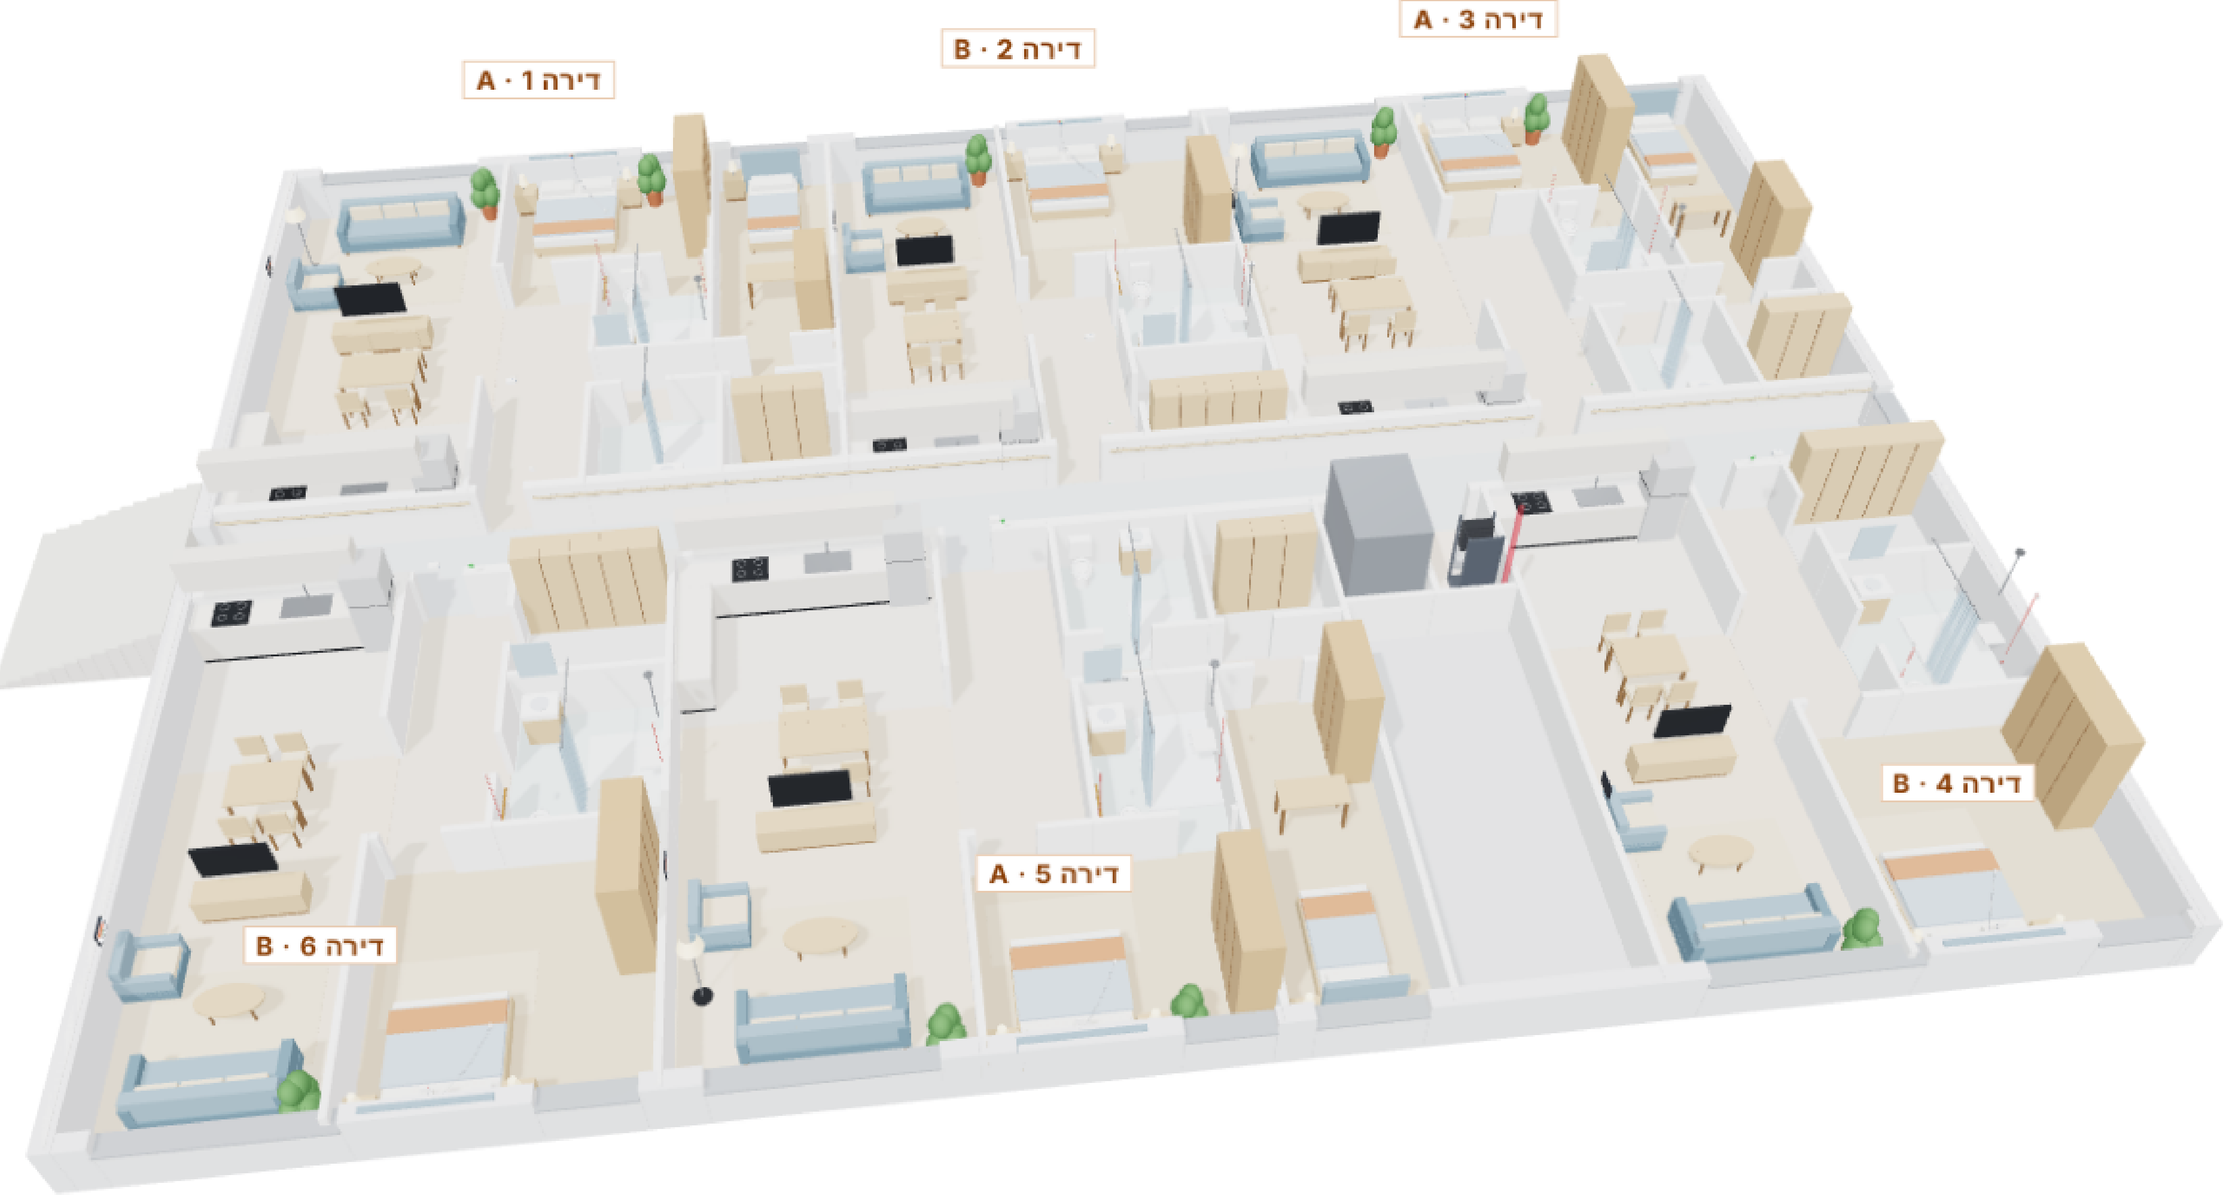

A · הפצר tipo – departamentos 1 (tipo A) y 2 (tipo B) destacados

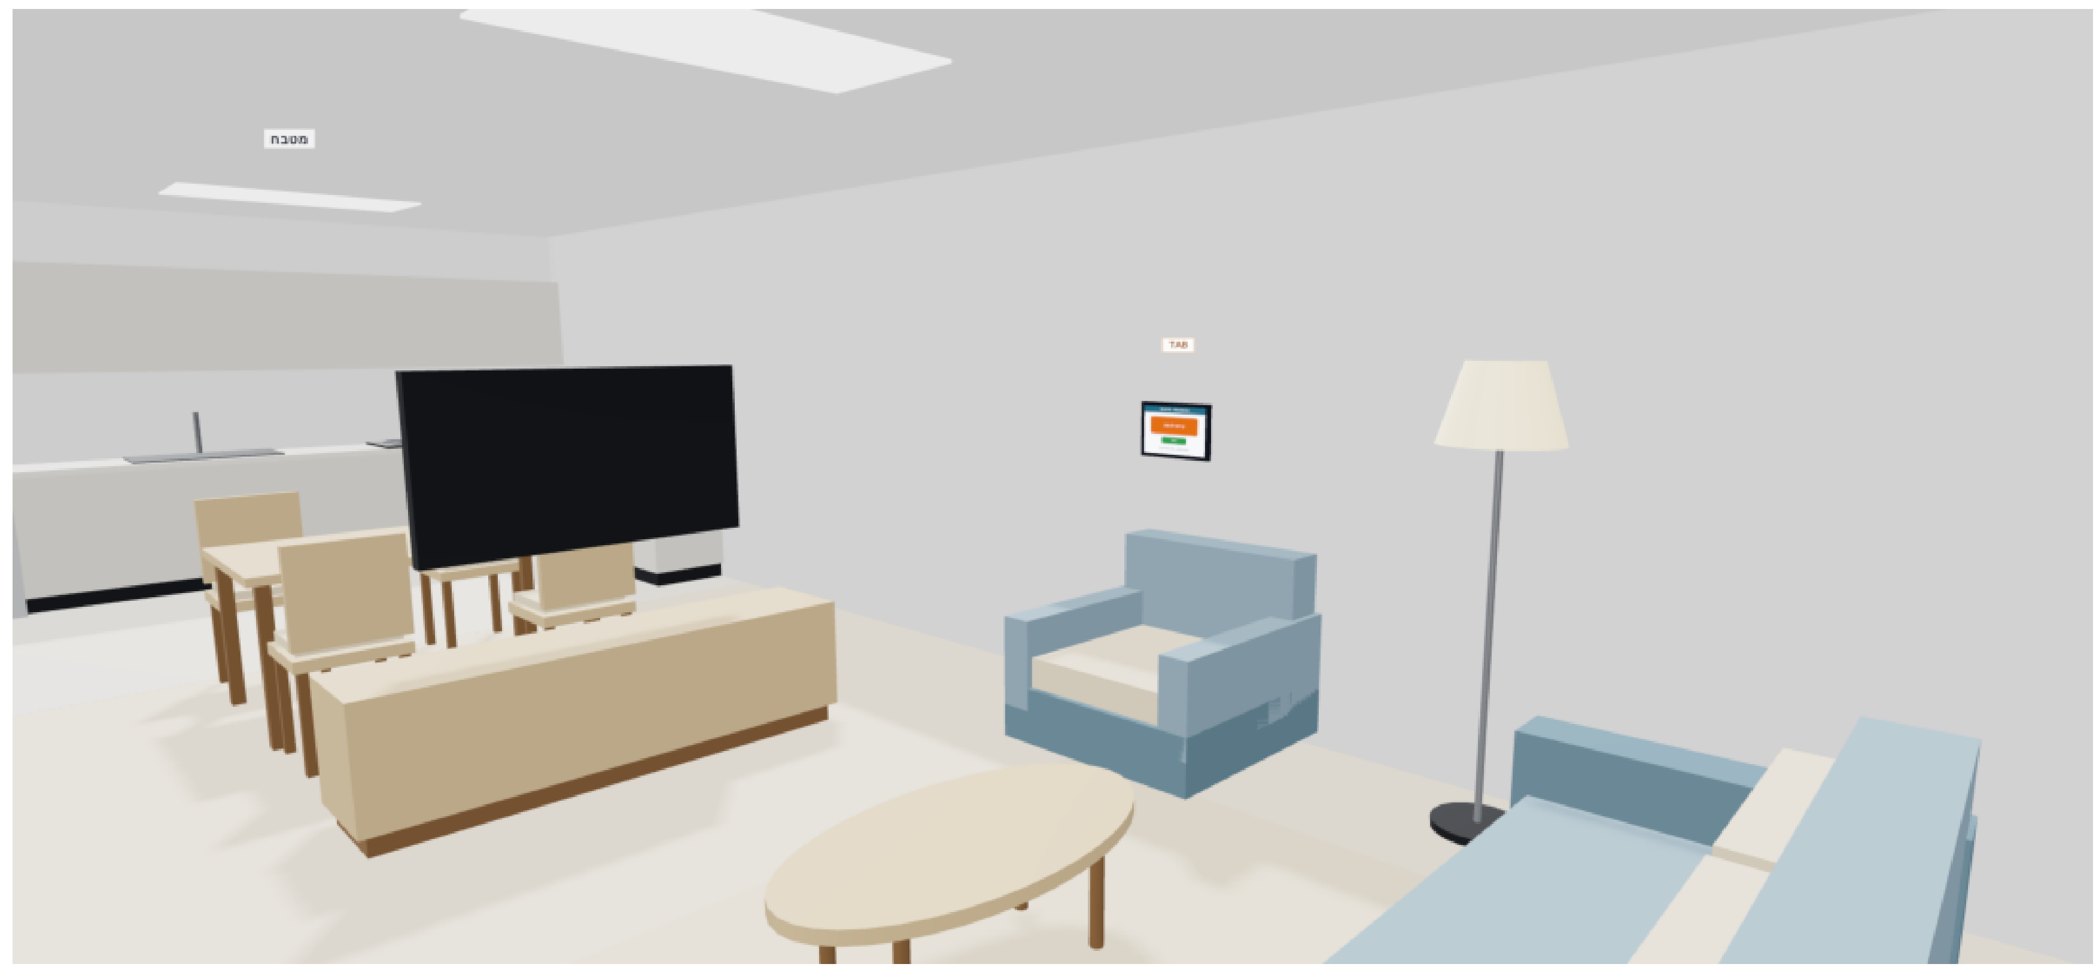

דיאורדנא טלבאט םע ןולס · B

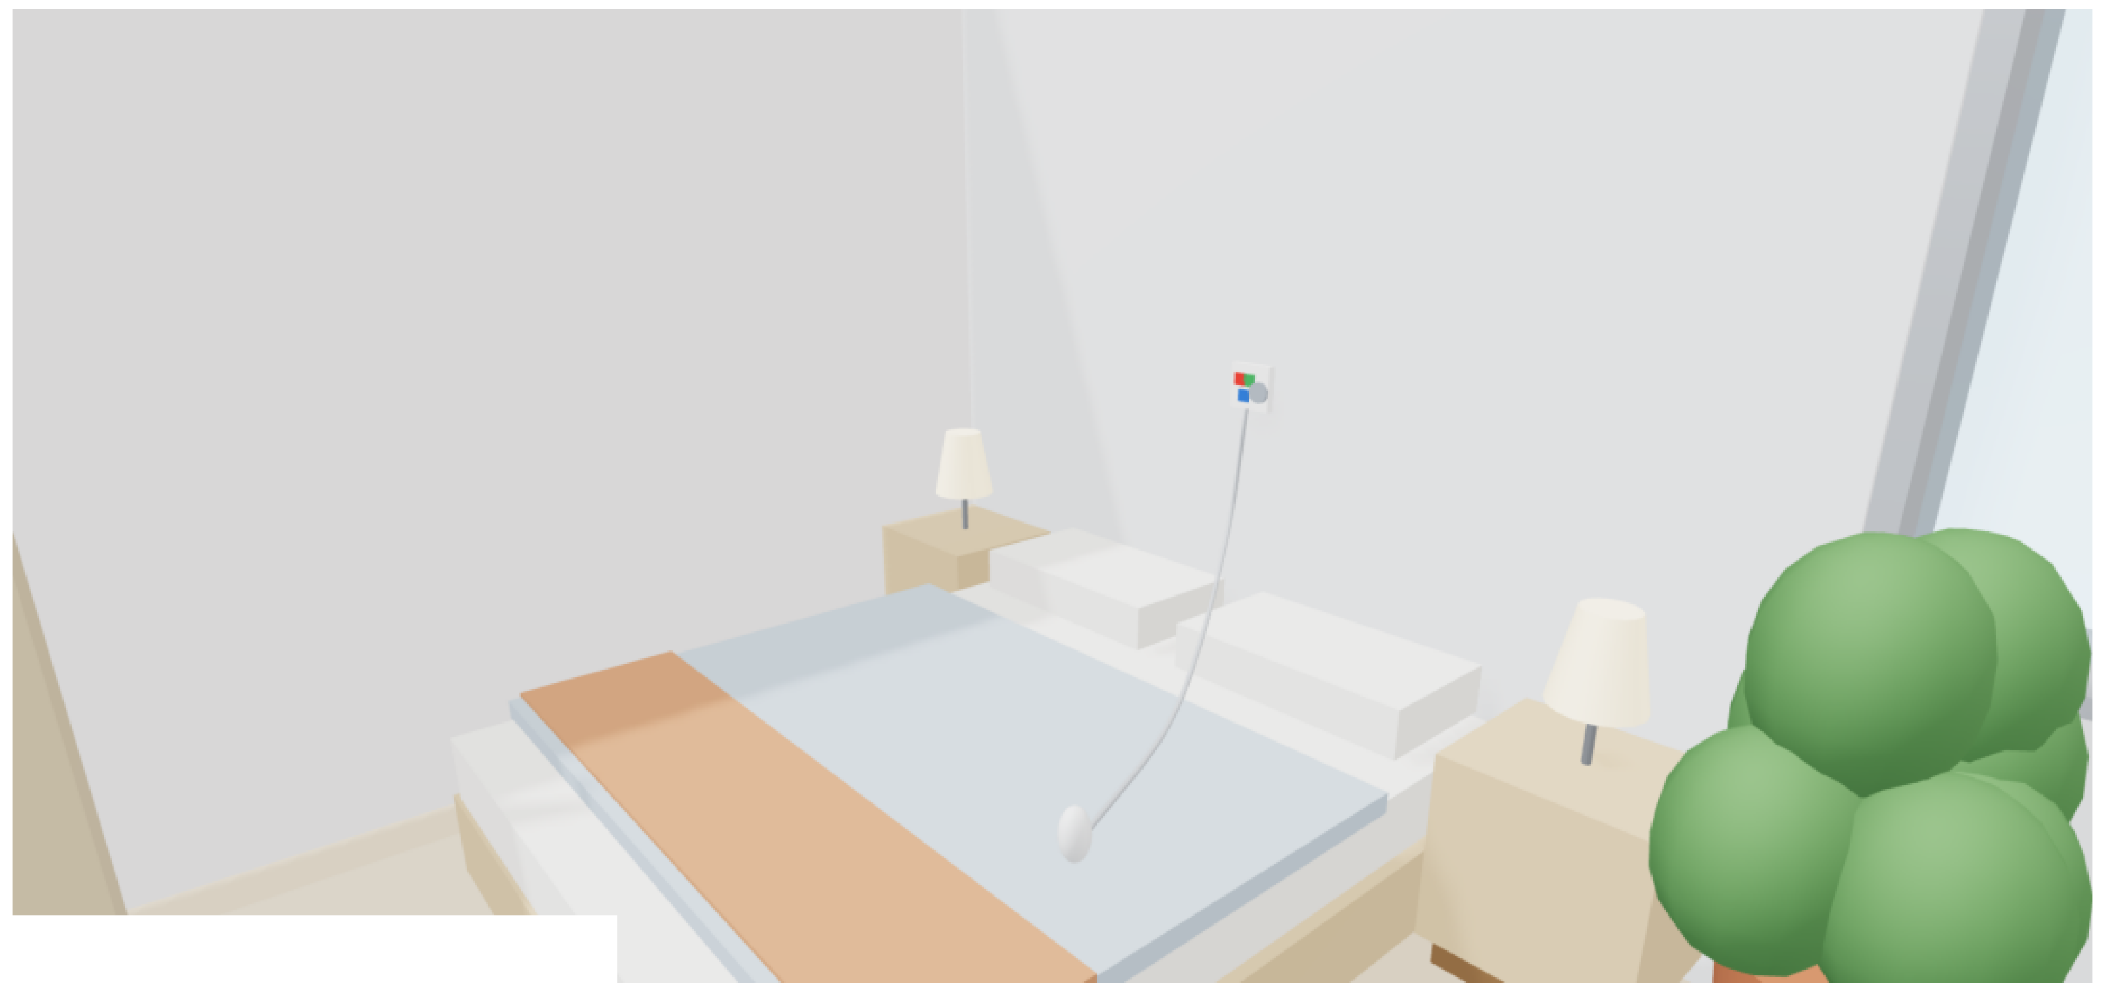

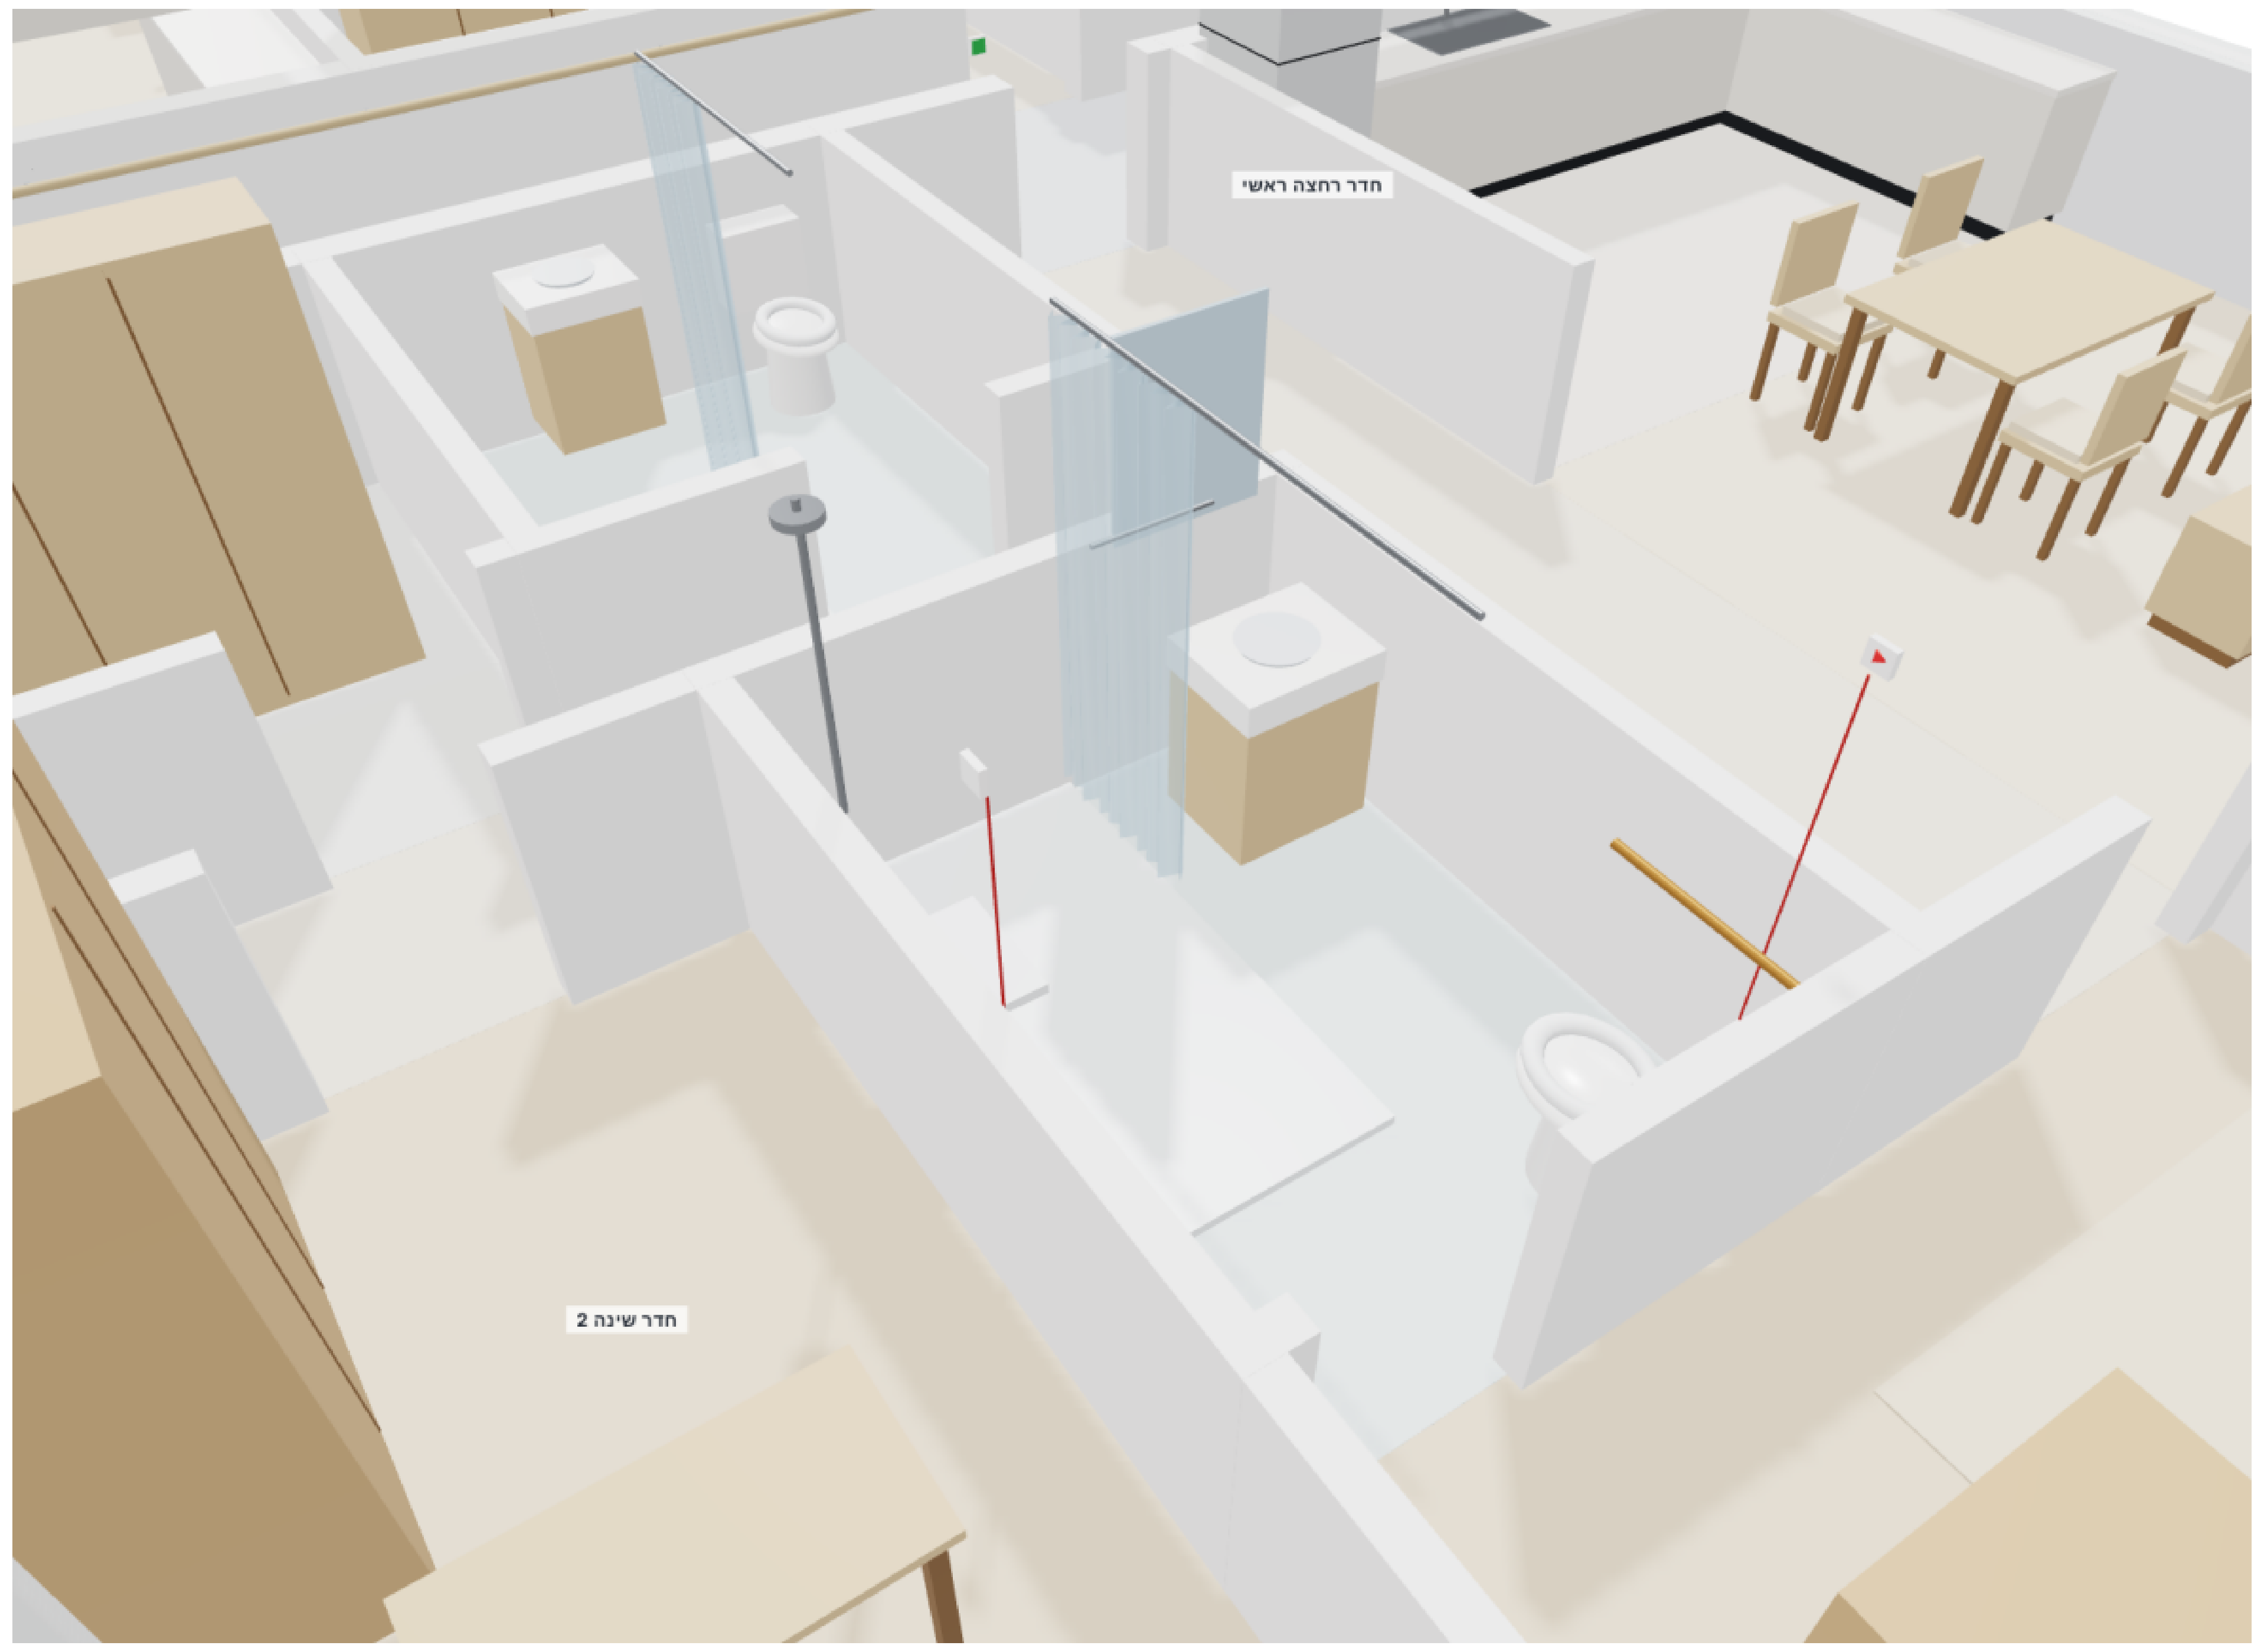

תחלקמבו הלסאב לבח תוכישמ – ישאר הצחר רדח · D

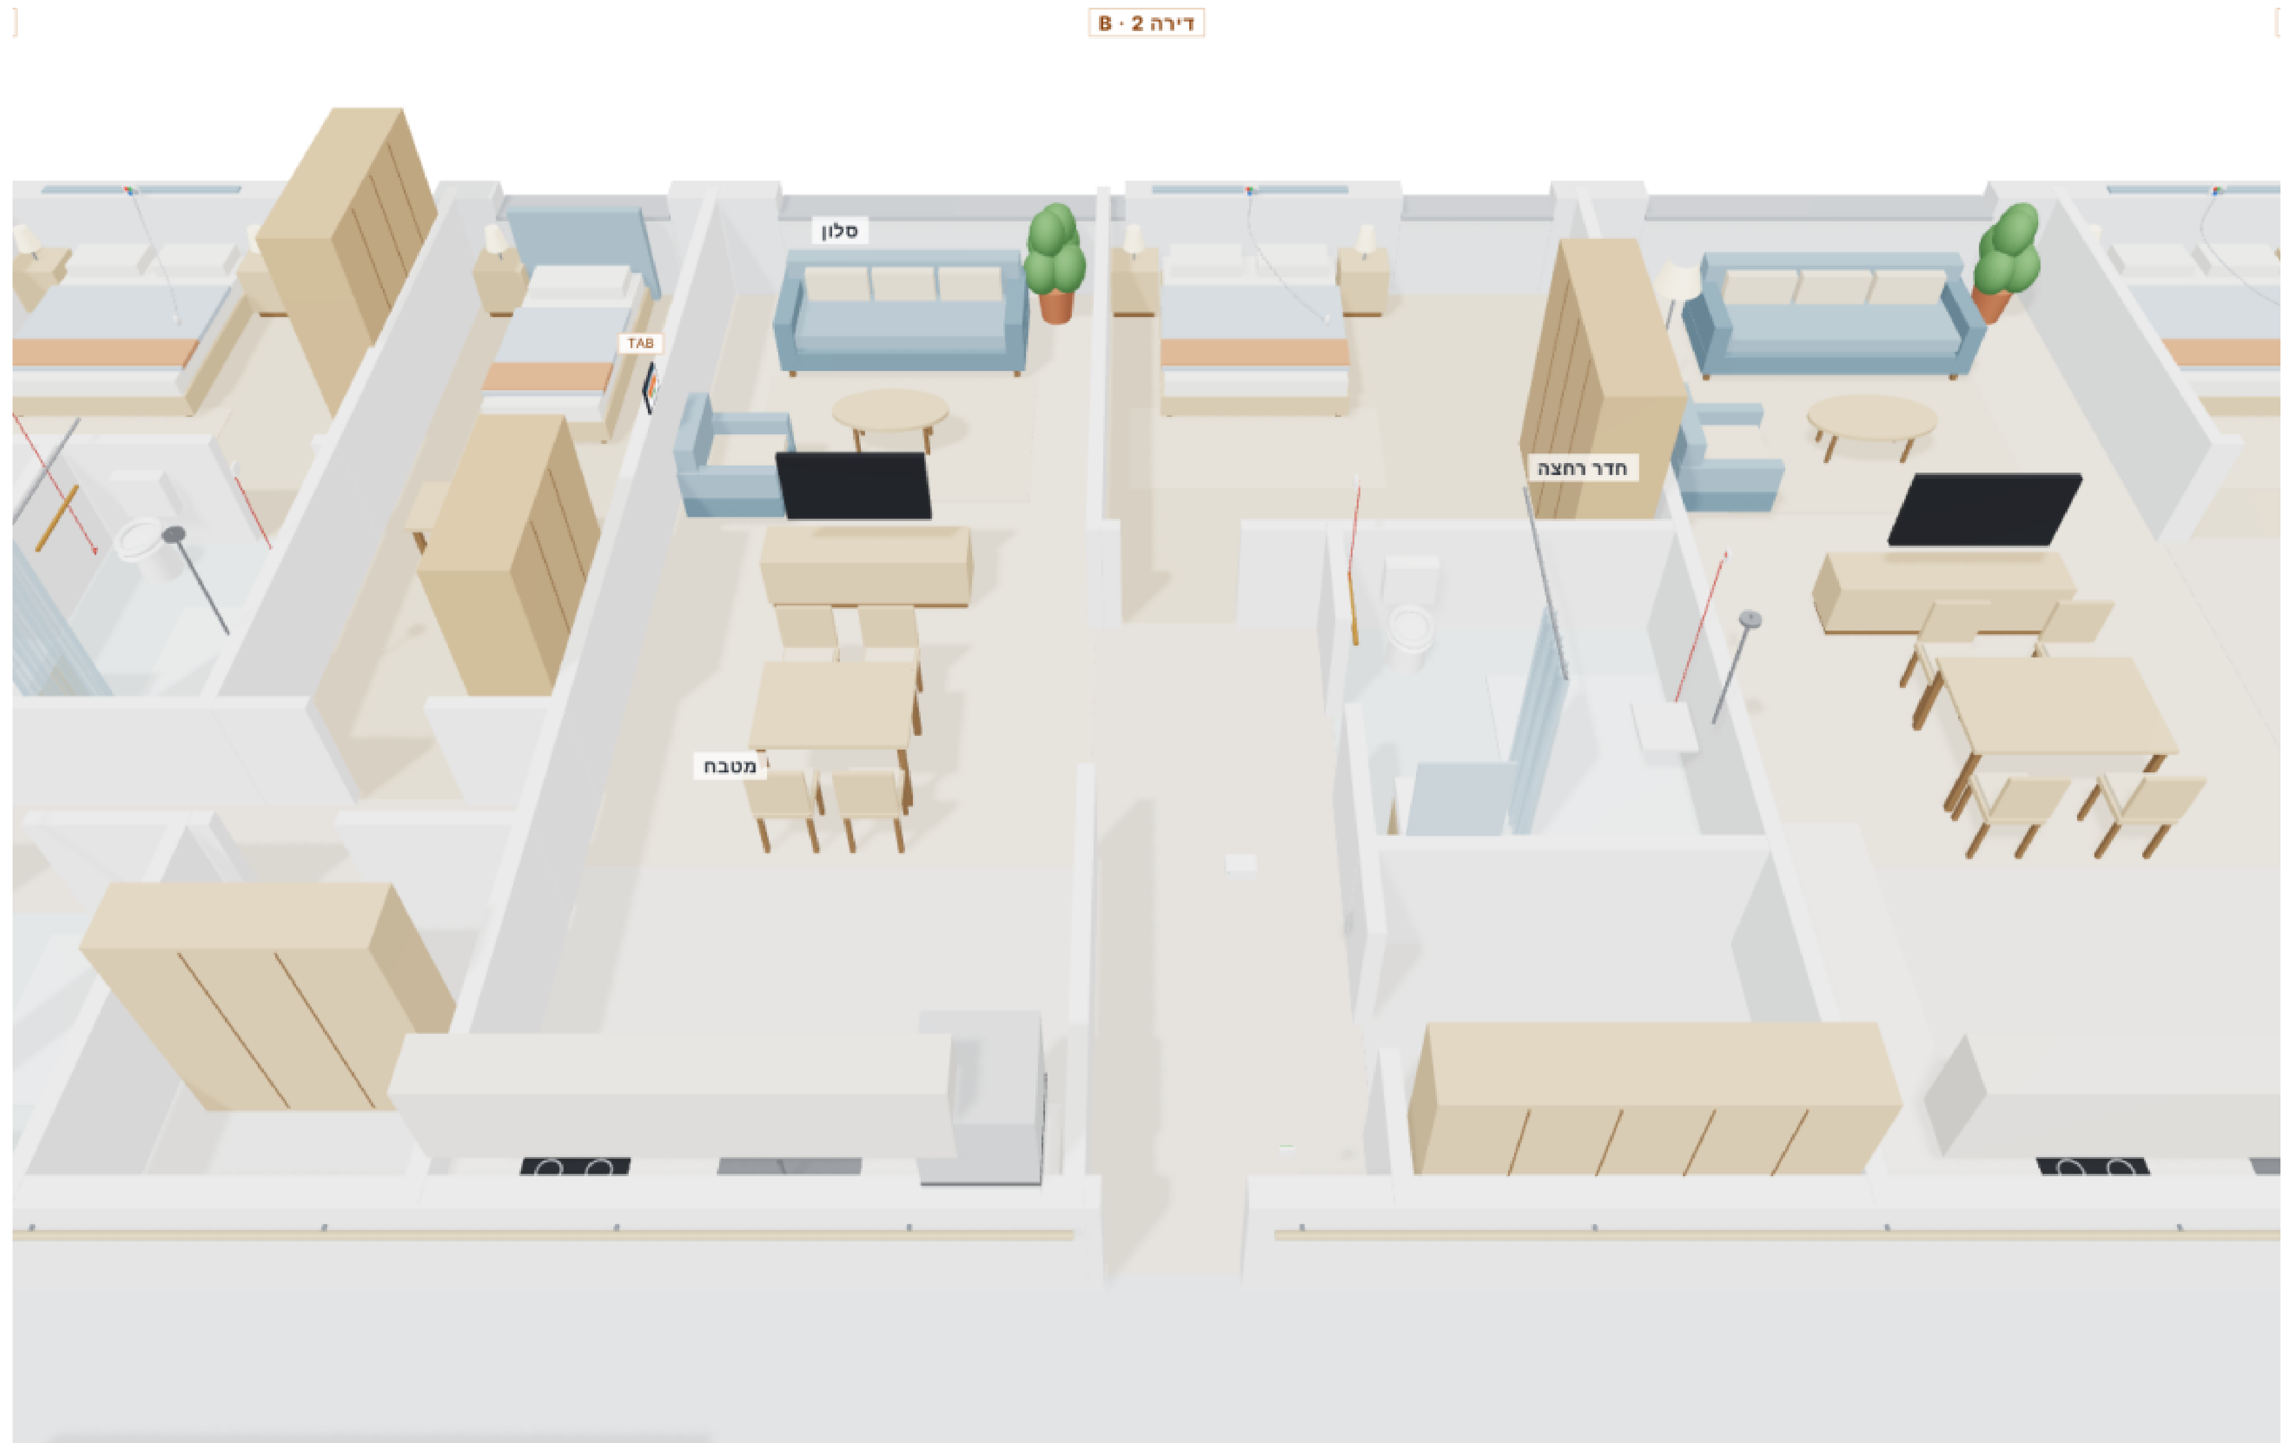

E · הריד גוס B

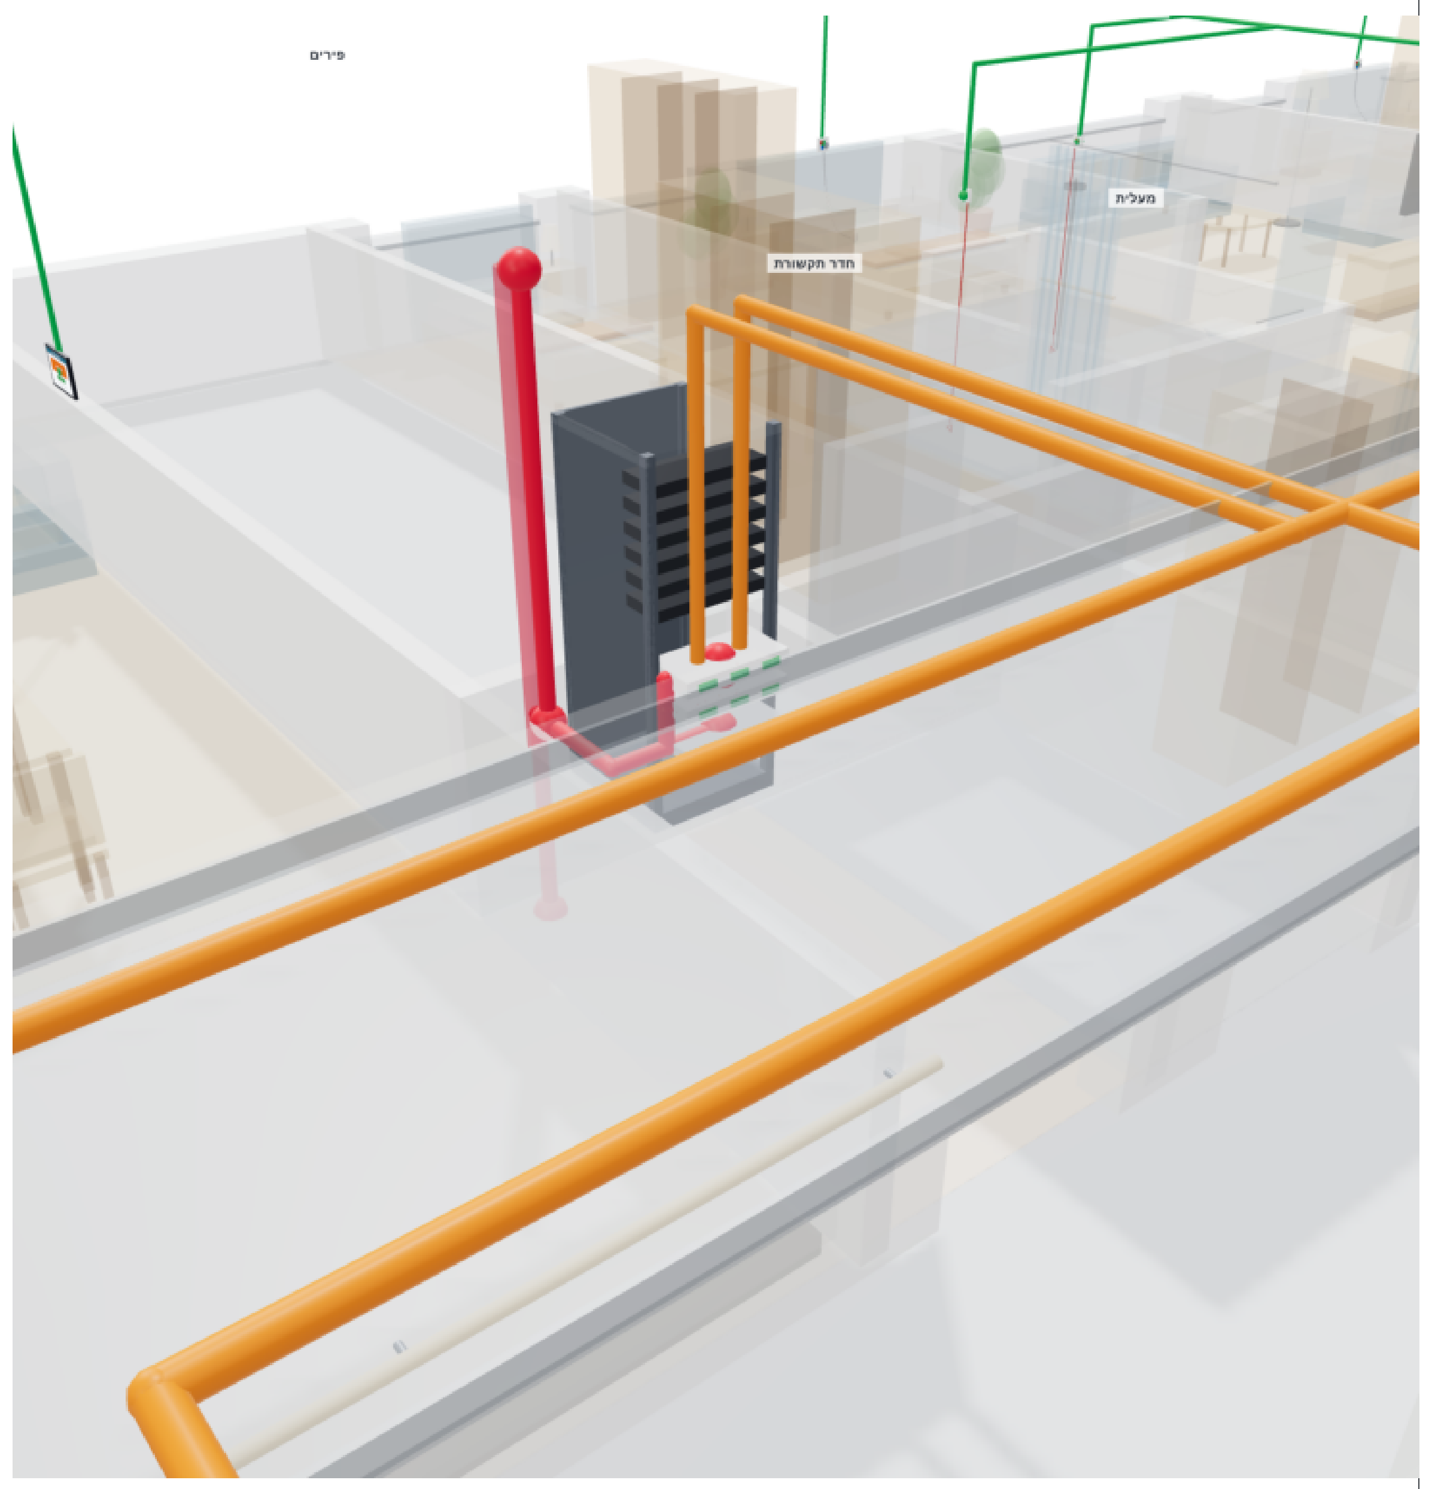

F · המוקה תרושקת רדח

ןגומ רויד · ןוכיתה םי ילדגמ

תוריד 36 · תומוק 6 + עקרק – תוחא תאירק תכרעמ

Telab International :ןכוה י"ע ACE BG · Advantecnia :תכרעמ

דויצ – םיידממ-תלת םיטבמ

3D views – equipment

הדימ הנק	ךיראת	REV	ןוילִיג
מ"נק אלל	**12/10/2026**	**A**	**06**

םירטמב תודימ

טמרופ A1 · הרודהמ A – ןונכת םדקומ

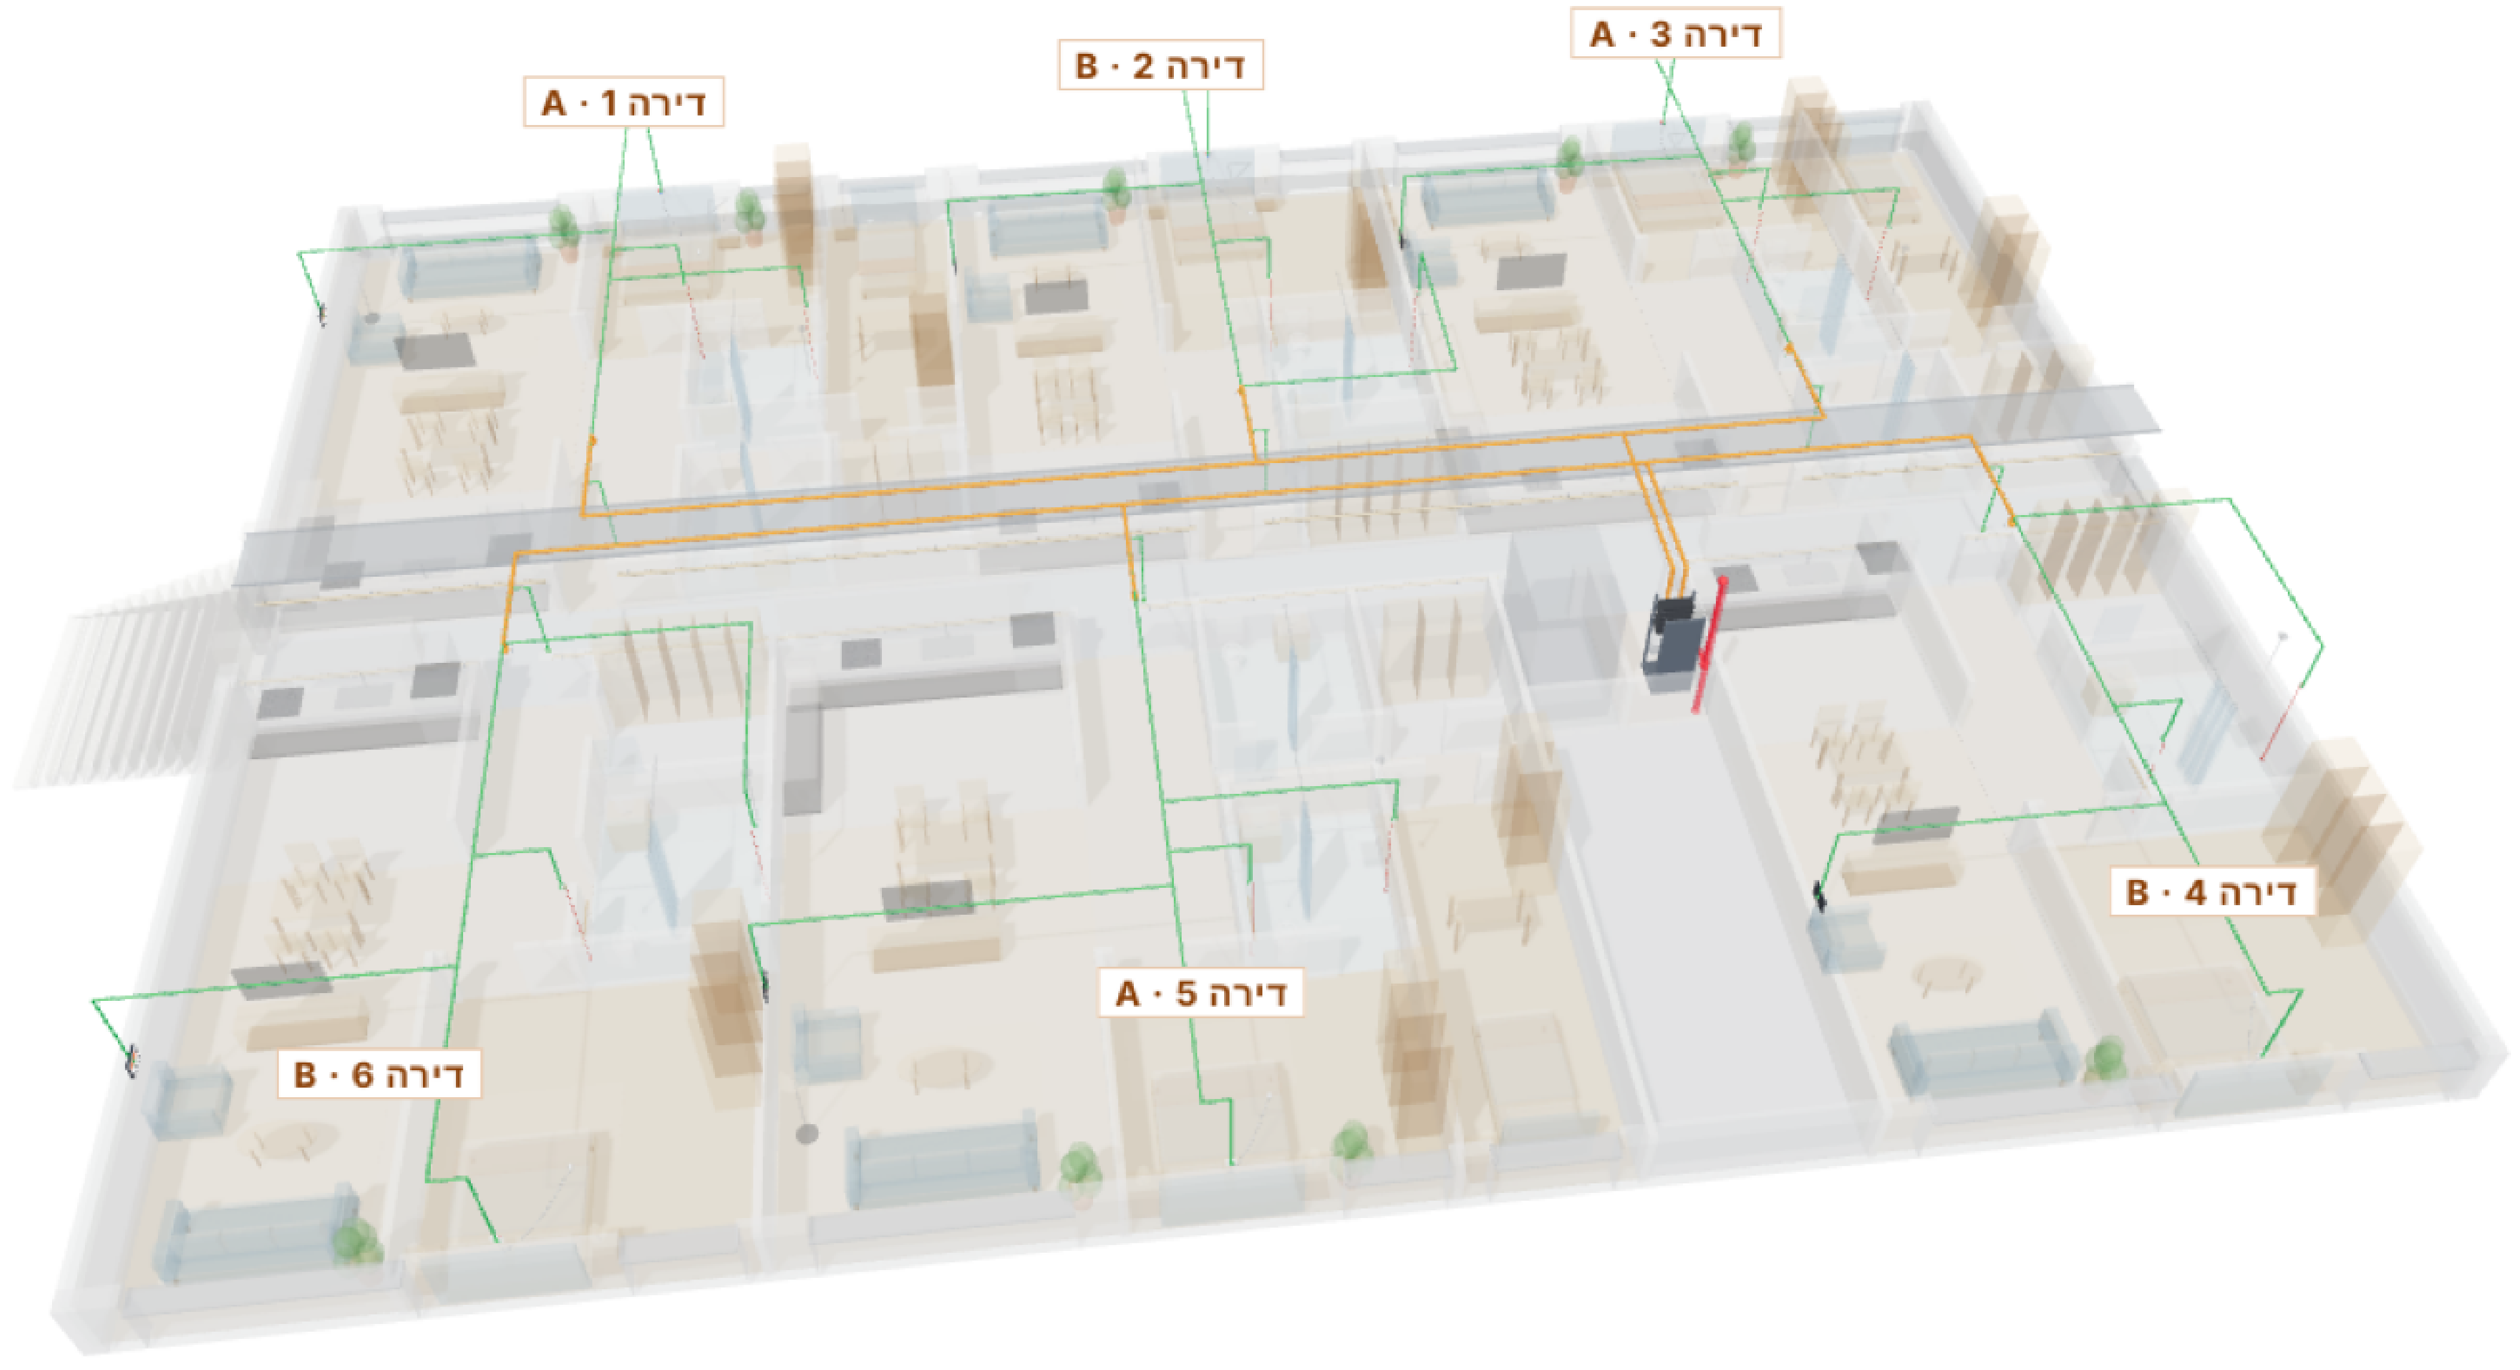

A · הפצר tipo – cableado (verde radial · naranja cadena LCom · rojo red)

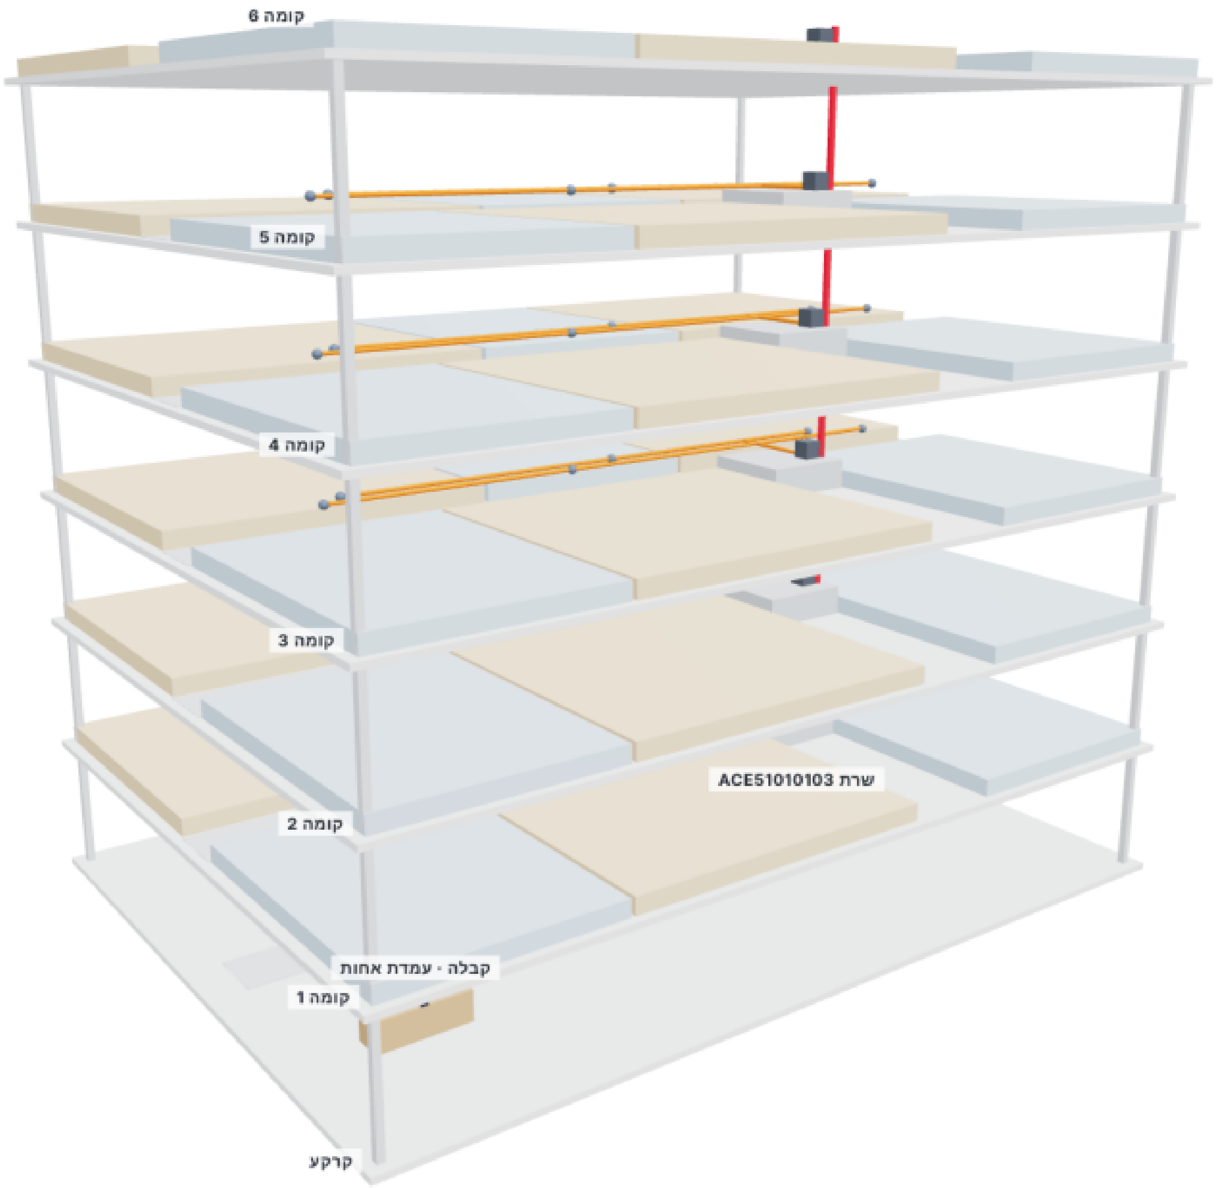

B · ןיינב עקרק + 6 תומוק – דומע

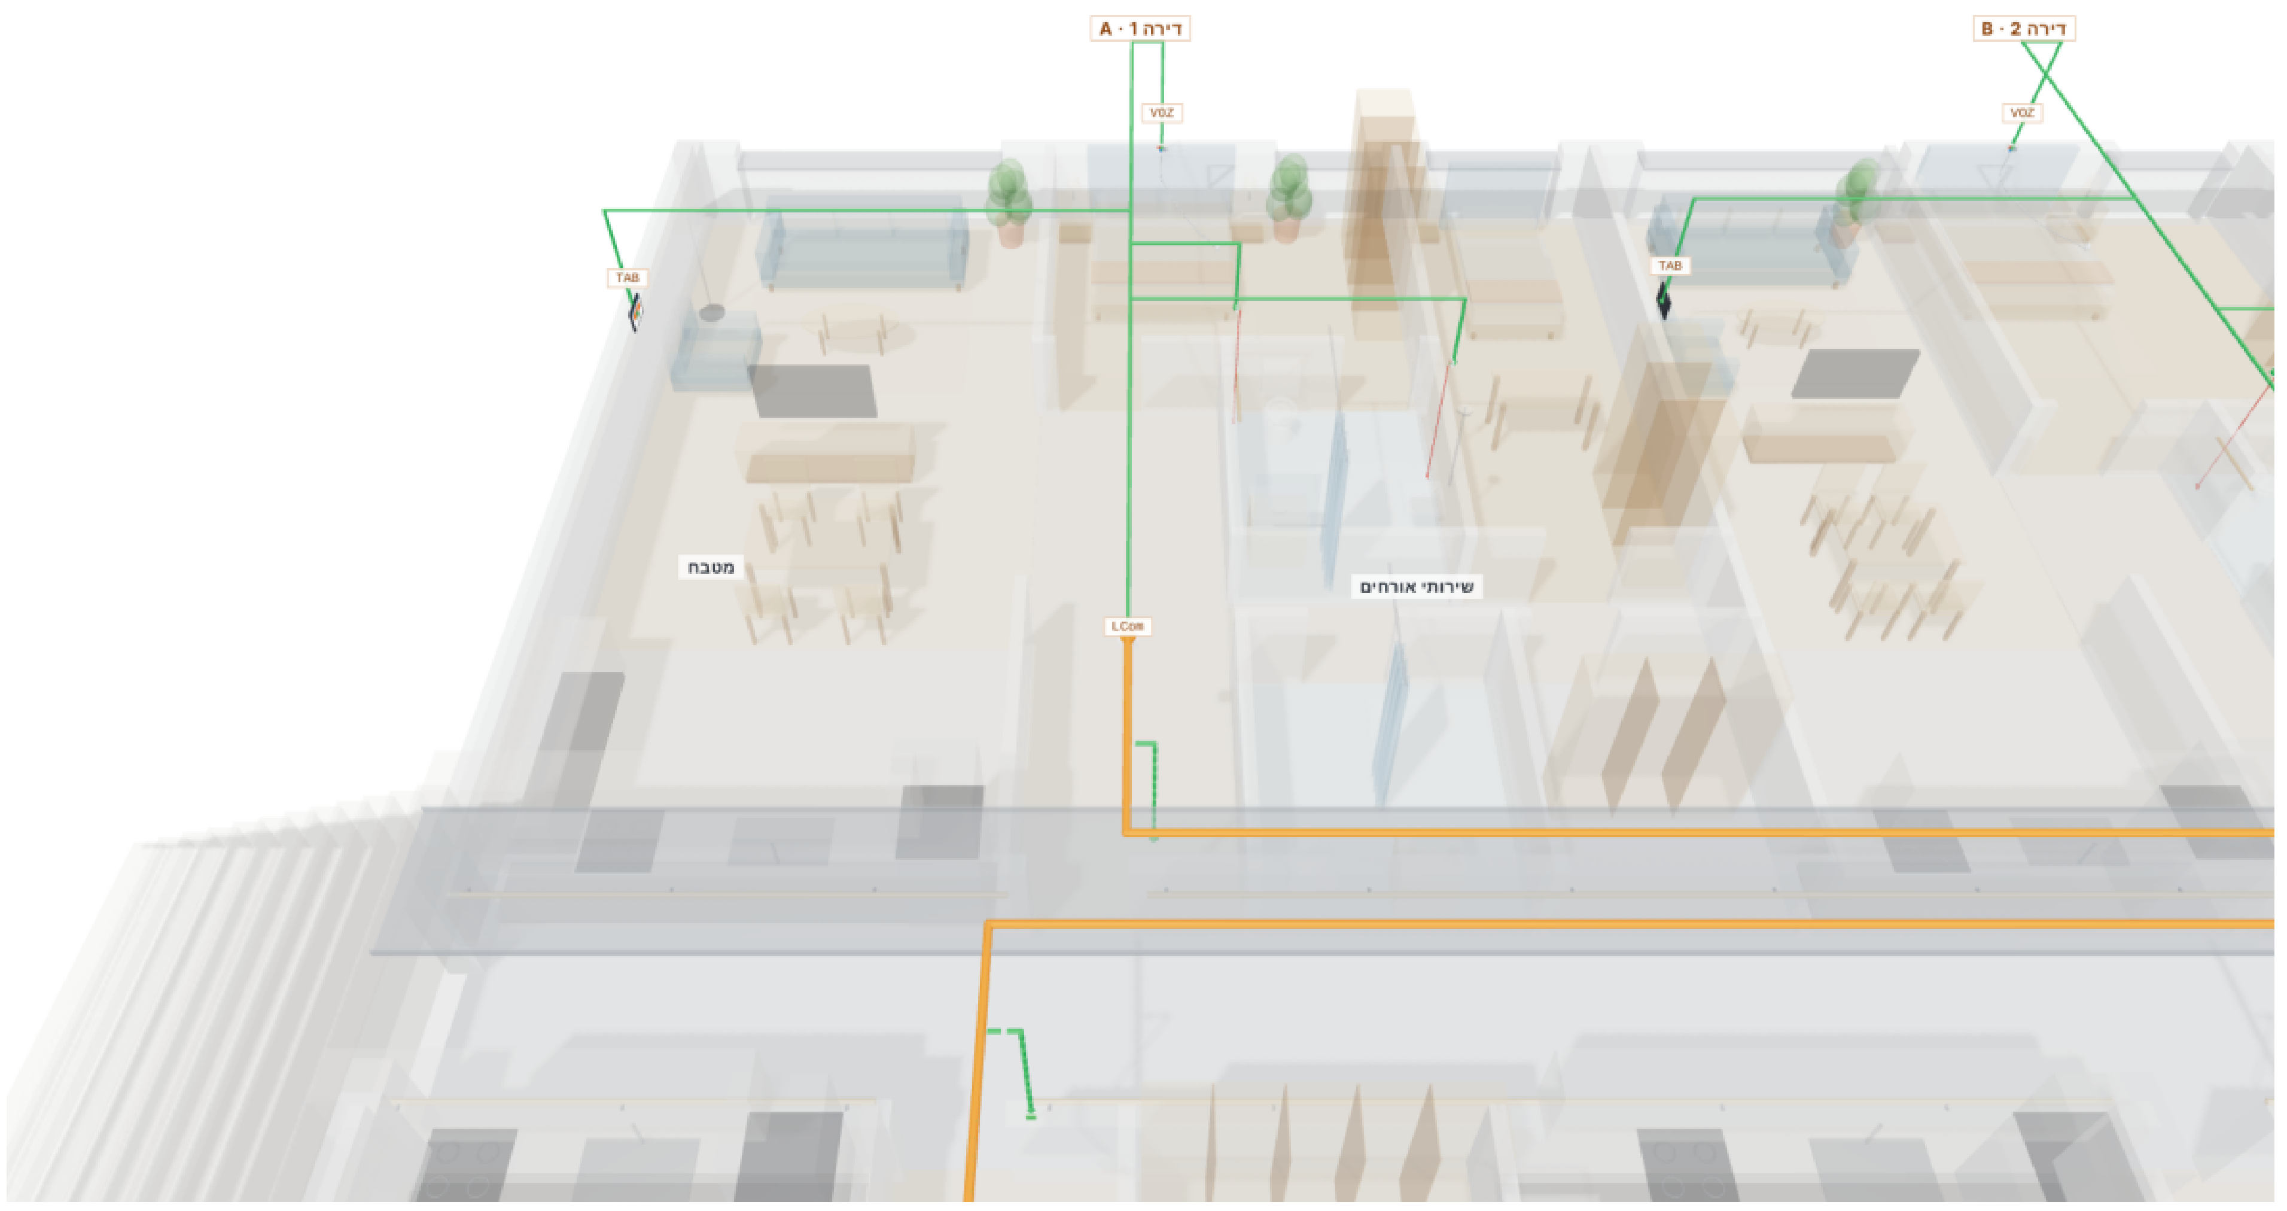

C · הריד גוס A – ילאידר ל-LCom

םיעבצ

- 🟩 Cat6 ילאידר: לכ ןקתה הרידב ← ה-LCom הלש
  Cat6 radial: each device → its LCom · Cat6 ילאידר: לכ ןקתה ← LCom
- 🟧 Cat6 / Cat7 תרשרשב: LCom ← LCom ← LCom ← Buscomm (3 לכל Buscomm)
  Cat6 / Cat7 chain: LCom → LCom → LCom → Buscomm · Cat6 / Cat7 תרשרש: LCom ← LCom ← Buscomm
- 🟥 Cat6A / Cat7 תשר: Buscomm ← המוק גתמ ← דומע ← תרש (עקרק)
  Cat6A / Cat7 network: Buscomm → floor switch → riser → server · Cat6A / Cat7 תשר: Buscomm ← גתמ ← דומע ← תרש
- ╌ Cat6 ילנויצפוא לוטיב / תוחכונ ןצחלל
  Cat6 to optional presence / cancel button · Cat6 ילנויצפוא תוחכונ ןצחלל

ןגומ רויד · ןוכיתה םי ילדגמ

תוריד 36 · תומוק 6 + עקרק – תוחא תאירק תכרעמ

Telab International :ןכוה ע"י ACE BG · Advantecnia :תכרעמ

ןיינבו טוויח – םיידממ-תלת םיטבמ

3D views – wiring and building

הדימ הנק	ךיראת	REV	ןויליג
ללא מ"נק	12/10/2026	A	07

םירטמב תודימ

טמרופ A1 · הרודהמ A – תכנון םדקומ