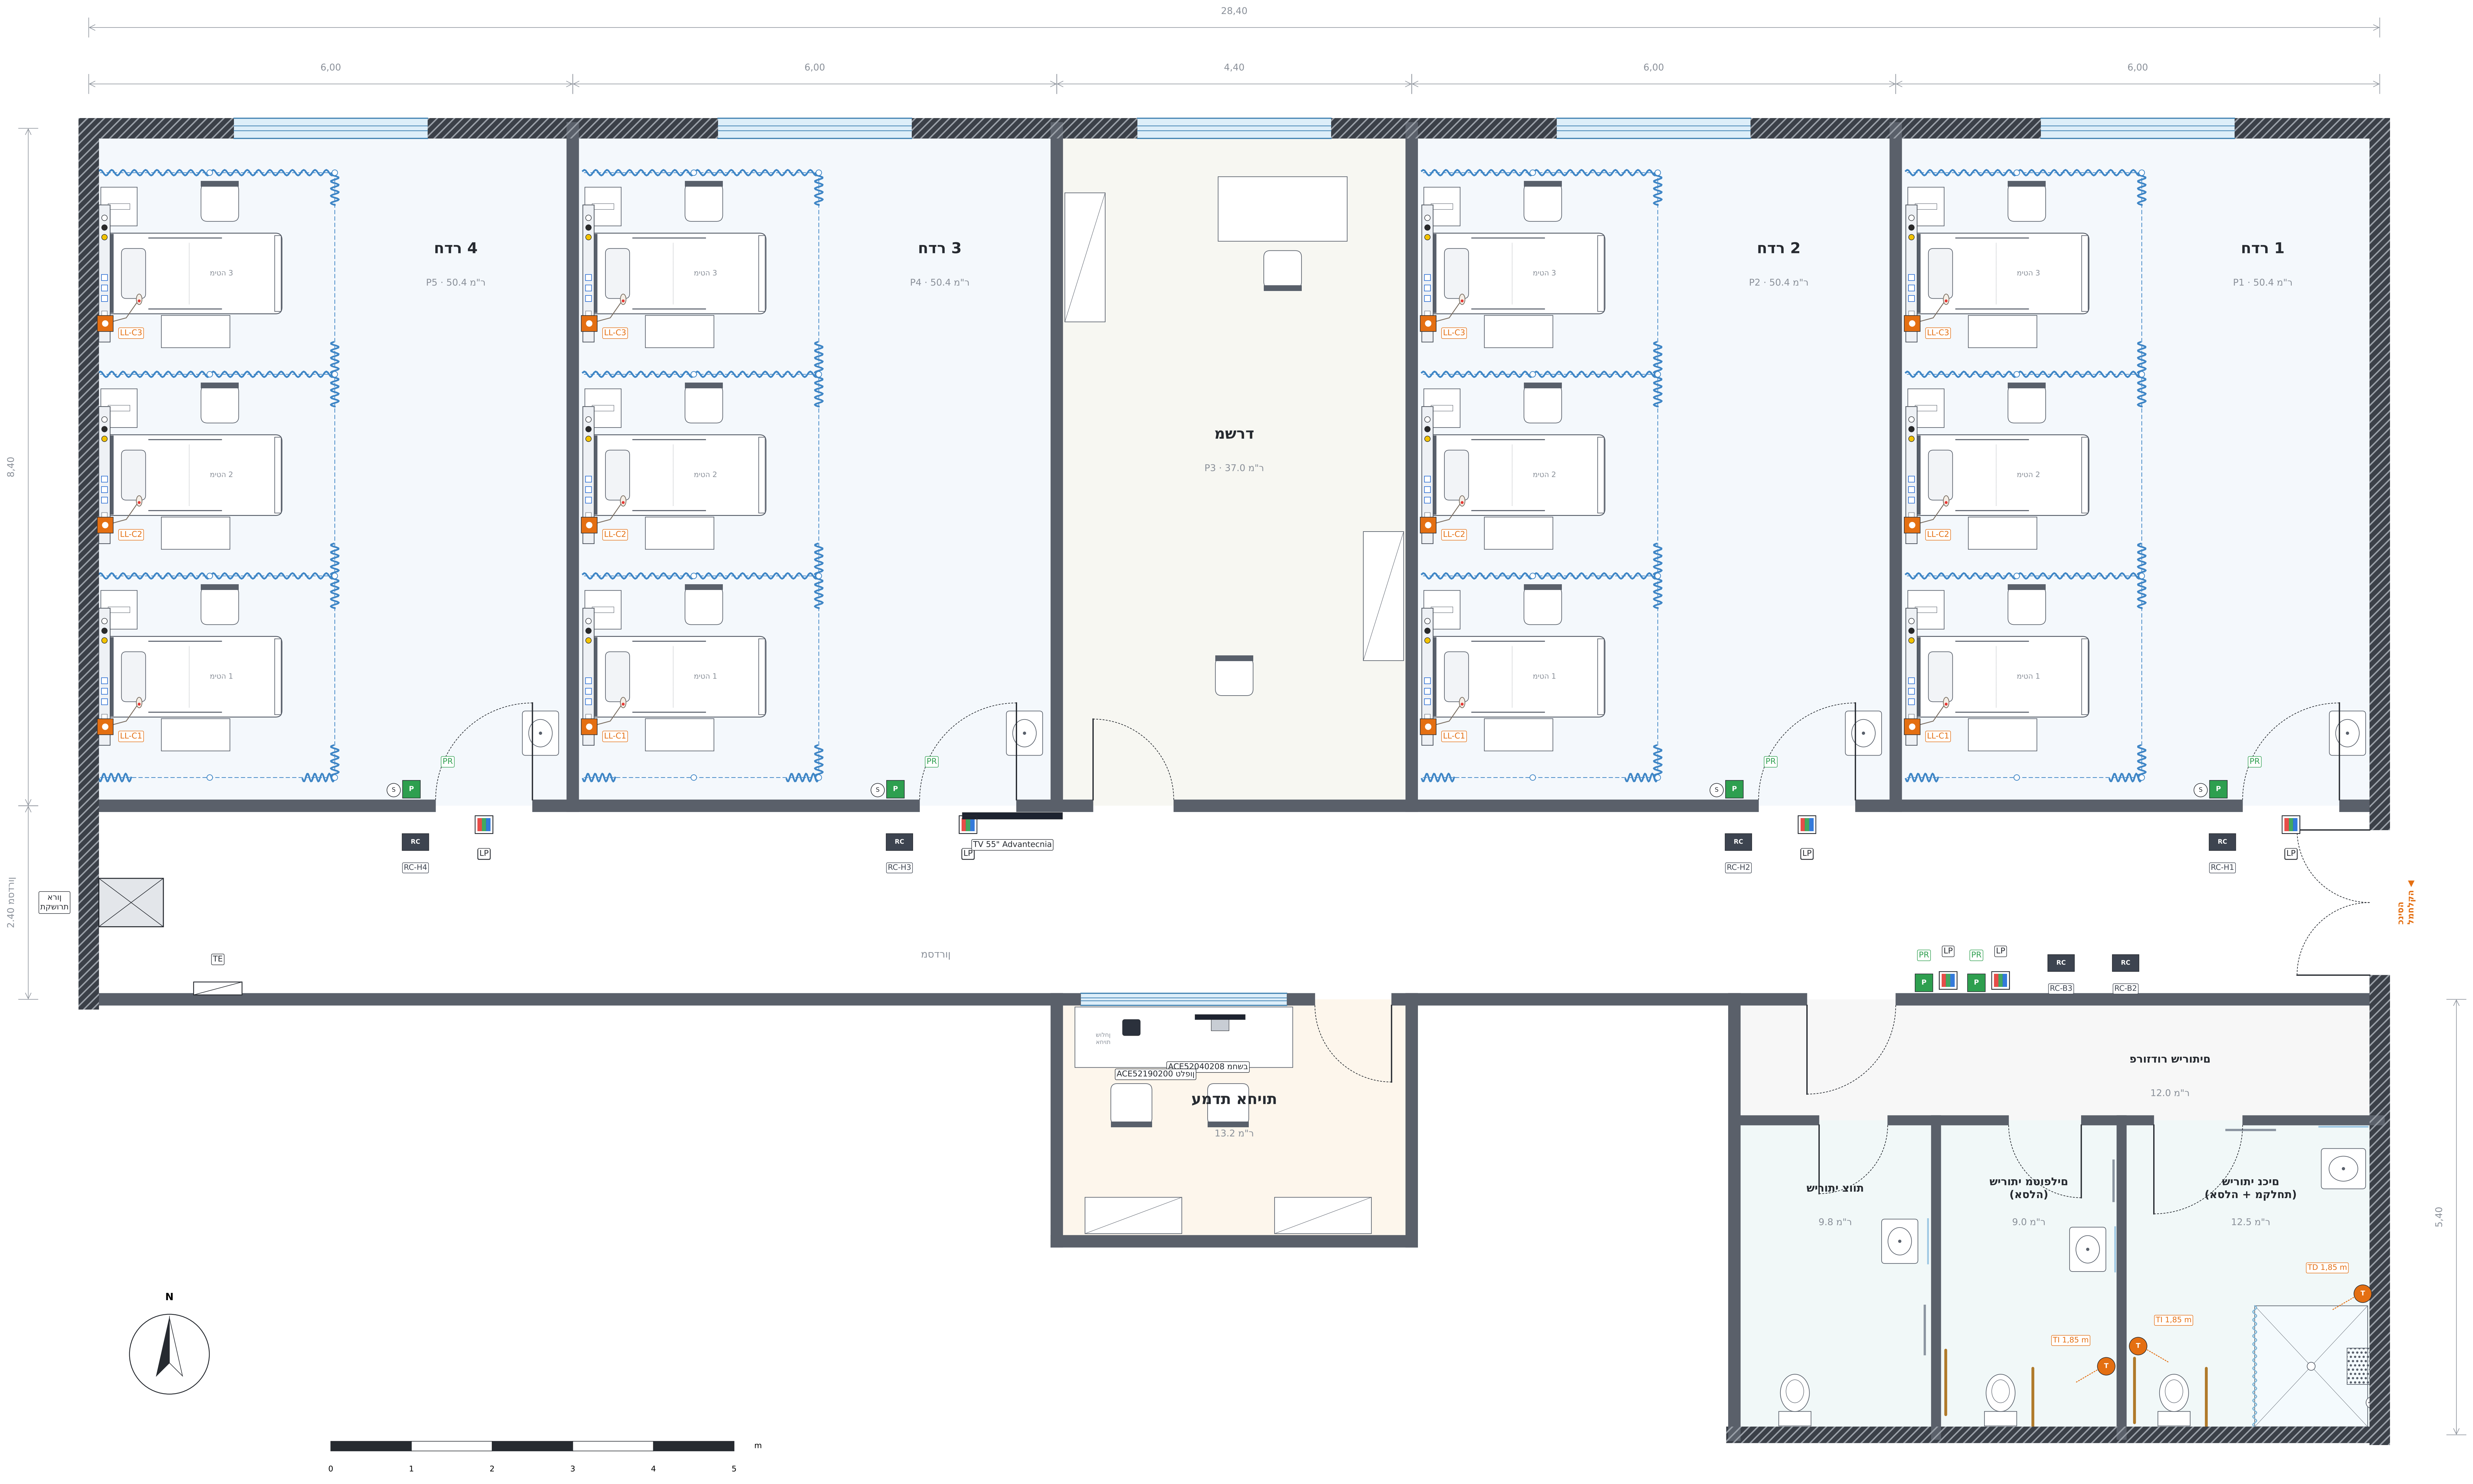
28,40
6,00
6,00
4,40
6,00
6,00
8,40
2.40 ןורדסמ
5,40
4 רדח
P5 · 50.4 ר"מ
3 רדח
P4 · 50.4 ר"מ
דרשמ
P3 · 37.0 ר"מ
2 רדח
P2 · 50.4 ר"מ
1 רדח
P1 · 50.4 ר"מ
3 הטימ
2 הטימ
1 הטימ
LL-C3
LL-C2
LL-C1
PR
P
S
RC
LP
RC-H4
RC-H3
RC-H2
RC-H1
TV 55" Advantecnia
ןורא תרושקת
TE
ןורדסמ
ACE52040208 בשחמ
ACE52190200 ןופלט
ןחלוש תויחא
תויחא תדמע
13.2 ר"מ
RC-B3
RC-B2
הסינכ הקלחמל
םיתוריש רודזורפ
12.0 ר"מ
תווצ יתוריש
9.8 ר"מ
םילפוטמ יתוריש (הלסא)
9.0 ר"מ
םיכנ יתוריש (תחלקמ + הלסא)
12.5 ר"מ
TD 1,85 m
TI 1,85 m
T
N
0
1
2
3
4
5
m

םילמס

🟧 LL · ןצחל האירק הטימל ACE41220316 + סגא (1 הטימל)
Bed call panel + pear push · ןצחל האירק הטימל + סגא

🟥 LP · ןורדסמ תרונמ ACE41020309 (אדום האירק · ירוק הנוכות · לוחכ קוד לוחכ)
Corridor indicator light, 3 colours · ןורדסמ תרונמ תלת-עבעית

RC · רכזיס םימר / רקב רדח ECV169 (תקרת ןורדסמ)
Room controller ECV169 (corridor ceiling) · רקב רדח ECV169 (תקרת ןורדסמ)

S · יגתמ תרואת רדח
Room light switches · יגתמ הרואת

PC · TV-ו ACE52040208 בשחמ / ACE52190200 ןופלט :תויחא תדמע
Touch all-in-one PC & TV running Advantecnia · ךסמו עגמ בשחמ TV םע תנכות Advantecnia

P · PR · הנוכות / לוטיב ACE80081001
Presence / cancel button · ןצחל הנוכות / לוטיב

T · TI/TD · הכישמ לבח הלסא / תחלקמ ACE40320303 (≥ 1.80 מ')
Pull-cord (mounted ≥ 1.80 m) · הכישמ לבח םישרותיס (≥1.80 מ')

○●●□□□ CT · 230 תלוסנוק הטימ: םיזג ןצחמ · ריווא · ואקוס, שקעי, V, RJ45
Bed-head unit: medical gases, power, data · תלוסנוק הטימ: םיזג, למשח, תרושקת

GAB · ןורא: SmartHub, גתמ ACEUCM6302, תרש ACE51010103
Comms rack: SmartHub, switch, server · ןורא תרושקת: SmartHub, גתמ, תרש

TE · יתקלחמ למשח חול
Electrical sub-panel · למשח חול

תורעה

1. םירדח: 3 תוטימ םע הראה ריקל דצה,
U קונסולה לכל הטימ ןוליוו תרוצב
לכל הטימ (םסילת הרקת).

2. ךותב רדחה דיל תלדה: יגתמ הרואת +
ןוכוחת/לוטיב (הבוג 1.05 / 1.35 מ').

3. תרונמ ןוסימ תעבורמ ACE41020309 לעמ
ןורדסמה ןוויכל ,תלד לכ ףוקשמ
(הבוג 2.42 מ').

4. םיתוריש B2 ו-B3: םילבח הבוגב ≥ 1.80 מ'.
תורונמ ולחצני תוכוחנ לש B2/B3 ןורדסמב,
דיל הסינכה שוגל םיתורישה.

5. תדמע תויחא לומ P3 םע תלד המשלה;
תואחא (ןולח): ןצח דומצ ריקל ןורדסמה שולחן
.P4-ל P3 ןיבש TV-הנופמ ןורדסמל ךסמלו ה

תוחא תאירק תכרעמ · זופשא תקלחמ
Nurse Call System · Inpatient Ward
Telab International :ןכוה ע"י ACE BG · Advantecnia :תכרעמ

דויצ – תיללכ תינכות

General floor plan – Equipment & devices

םינקתהו דויצ – תיללכ תינכות

הדימ הנק	ךיראת	REV	ןוילג
1:50	12/10/2026	A	01

םירטמב תודימ

טמרופ A1 · הרודהמ A – תכנון םדקומ

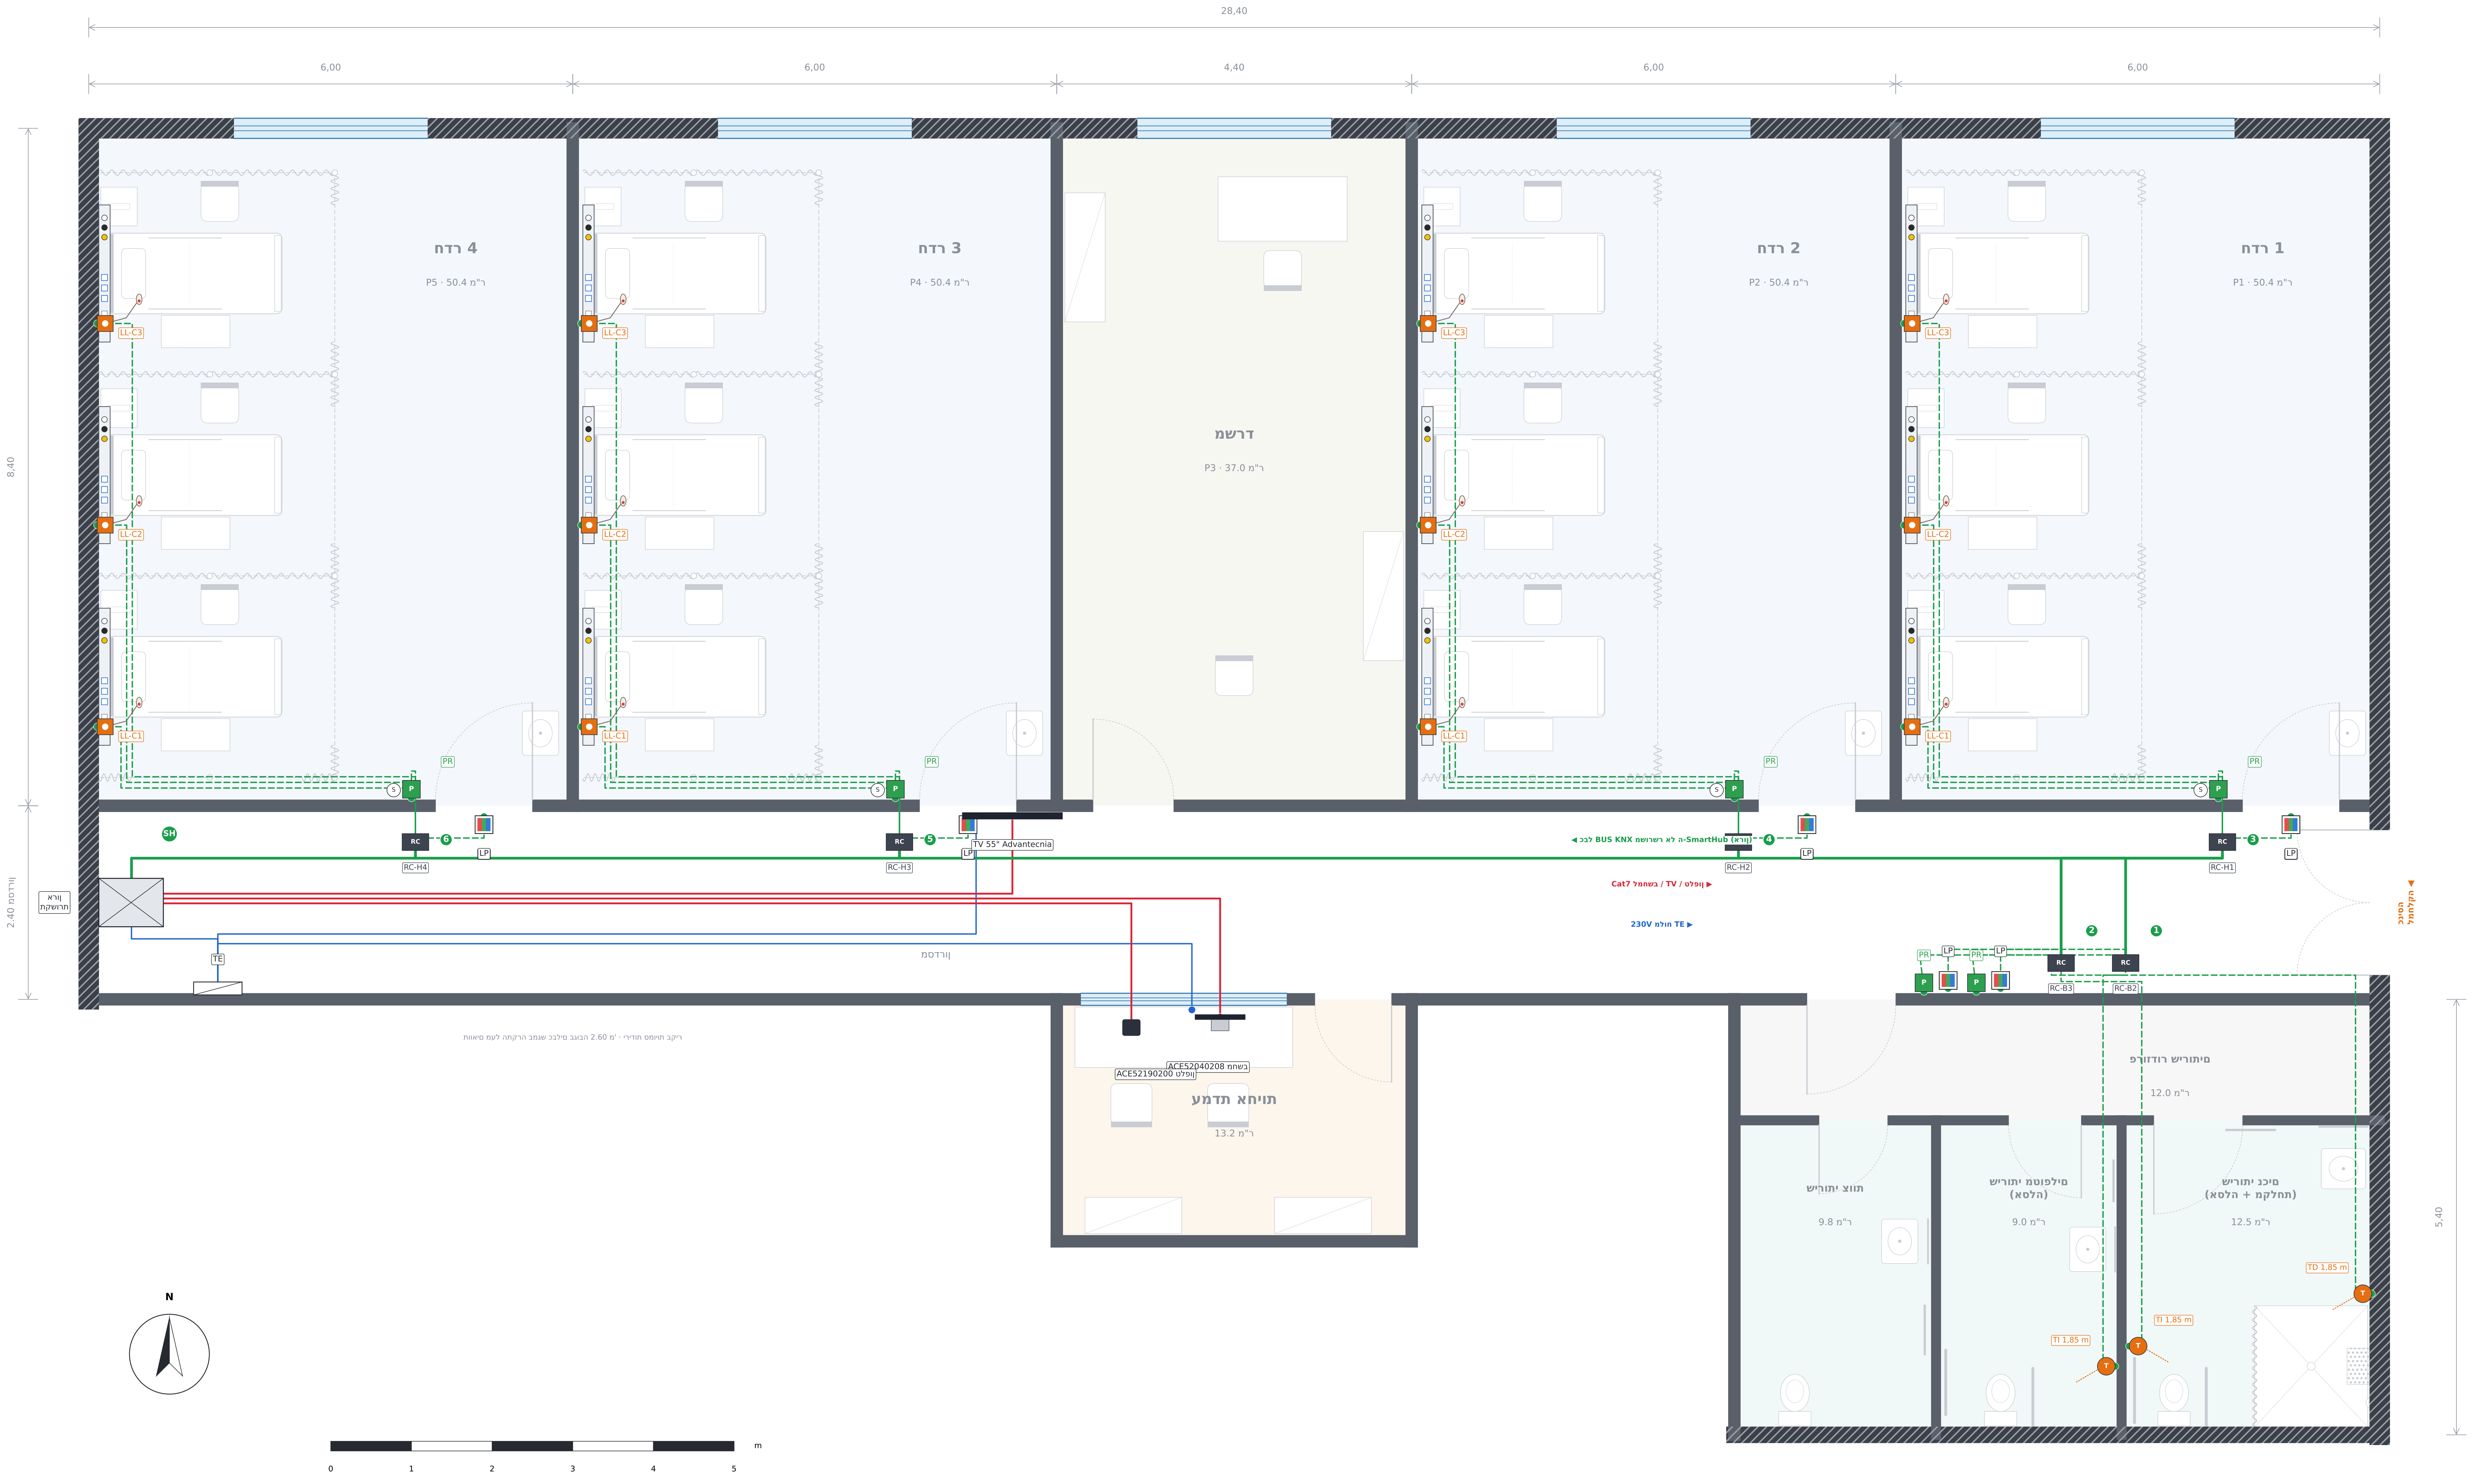
28,40
6,00
6,00
4,40
6,00
6,00
8,40
2.40 ןורדסמ
5,40
רדח 4
P5 · 50.4 ר"מ
רדח 3
P4 · 50.4 ר"מ
דרשמ
P3 · 37.0 ר"מ
רדח 2
P2 · 50.4 ר"מ
רדח 1
P1 · 50.4 ר"מ
LL-C1
LL-C2
LL-C3
PR
P
S
RC
LP
RC-H4
RC-H3
RC-H2
RC-H1
RC-B3
RC-B2
SH
TV 55" Advantecnia
◀ לבכ BUS KNX תמשרשו לא ה-SmartHub (ןורא)
Cat7 לחמשב / TV / ןופלט ▶
230V תולוח TE ▶
הסינכ הקלחמל ▶
ןורא תרושקת
TE
ןורדסמ
ריקב תויומס תודירי · 'מ 2.60 הבוגב םילבכ שגמב הרקתה לעמ םיאוות
ACE52040208 בשחמ
ACE52190200 ןופלט
עמדת אתיות
13.2 ר"מ
םיתוריש רודזורפ
12.0 ר"מ
תווצ יתוריש
9.8 ר"מ
םילפוטמ יתוריש
(הלסא)
9.0 ר"מ
םיכנ יתוריש
(הלסא + תחלקמ)
12.5 ר"מ
TI 1,85 m
TD 1,85 m
T
N
0
1
2
3
4
5
m

םילבכ יעבצ דוק

🟩 SmartHub ← (תרשרש) םיניפ 24 סיטרכ ← סיטרכ – BUS KNX 2x2x0.8 לבכ
KNX bus – board-to-board chain · BUS – םיסיטרכ רושרש

🟥 Cat6 / Cat7 דבלב: SmartHub ← גתמ ← תרש · בשחמ / ןופלט · TV
Cat6/Cat7 only: SmartHub, switch, server, PC/phone, TV · Cat6/Cat7 דבלב: SmartHub, גתמ, תרש, בשחמ, TV

- - - ילאידר לבכ רדח – לכ ןקתה לכרטיס 24 הפינים ולש
Radial in each room – device to its 24-pin board · ילאידר לבכ רדח – ןקתה לכרטיס

🟦 (PoE ראשה) דבלב TV-230 – ןוראל, בשחמל/ןופלט ולV למשח
230 V only to rack, PC/phone, TV – rest is PoE · 230V ןוראל, בשחמ/ןופלט ו-TV דבלב – ראשה PoE

םילמס

🟧 LL · לחצן קריאה למיטה ACE41220316 + סגא (1 למיטה)
Bed call panel + pear push · סגא + הטימל האירק ןצחל

LP · ןורדסמ תרונמ ACE41020309 (לוחכ קוד לוחכ · תוחכונ · ירוק · האירק · סודא)
Corridor indicator light, 3 colours · תיעבצ-תלת ןורדסמ תרונמ

RC · סיטרכ םימיר / בקר רדח ECV169 (ןורדסמ תרקת)
Room controller ECV169 (corridor ceiling) · בקר רדח ECV169 (ןורדסמ תרקת)

S · רדח תרואת יגתמ
Room light switches · הרואת יגתמ

PC · TV-ו ACE52040208 בשחמ / ACE52190200 עמדת תויחא: ןופלט
Touch all-in-one PC & TV running Advantecnia · Advantecnia תנכות םע TV ךסמו עגמ בשחמ

P · PR · תוחכונ / לוטיב ACE80081001
Presence / cancel button · לוטיב / תוחכונ ןצחל

T · TI/TD · למשח לבח תכישמ הלסא / תחלקמ ACE40320303 (≥ 1.80 'מ)
Pull-cord (mounted ≥ 1.80 m) · למשח לבח תכישמ םיתורישב (≥1.80 'מ)

○●●□□□ CT · 230 קנוסולות הטימ: ןצמח · ריווא · םוקאו, שקעיV, RJ45
Bed-head unit: medical gases, power, data · קנוסולת הטימ: םיזג, למשח, תרושקת

GAB · ACE51010103 תרש ,ACEUCM6302 גתמ ,SmartHub :ןורא
Comms rack: SmartHub, switch, server · ןורא תרושקת: SmartHub, גתמ, תרש

TE · יתקלחמ למשח חול
Electrical sub-panel · למשח חול

תורעה

1. לכ רדח מחווט רדילאית: לכל התקן (LL, PR, LP, TI) לבכ משלו לכרטיס רדחה של הפינים 24 (ECV169).

2. רדחל ץוחמ םינקתומ הפינים 24 יסיטרכ, מעל תרקת המסדרון, ומשורשרים כרטיס לכרטיס בכבל BUS KNX 2x2x0.8.

3. הבקר האחרון (H4) סוגר את השרשרת ב-SmartHub (Raspberry) שבארון; משם Cat6A למתג ומהמתג לשרת.

4. Cat6/Cat7 רק עבור: SmartHub ← מתג ← השרת, הטלפון או המחשב, TV-ה והאחיות, אין חיבור Cat6/Cat7 בחדרים.

PoE: 230V-5. לכ מערכת הקריאה מוזנת ב PoE. 230V רק בארון, בחמבש/ןופלט ובו TV-רק.

תוחא תאירק תכרעמ · זופשא תקלחמ
Nurse Call System · Inpatient Ward
Telab International :הכון ע"י   ACE BG · Advantecnia :תכרעמ

טוויח – תיללכ תינכות

General floor plan – Wiring & cable routes
טוויח – תיללכ תינכות

הדימ הנק	ךיראת	REV	ןוילג
1:50	12/10/2026	A	02

םירטמב תודימ
טמרופ A1 · הרודהמ A – ןונכת םדקומ

A · 1:30 · חדר טיפוסי – ציוד

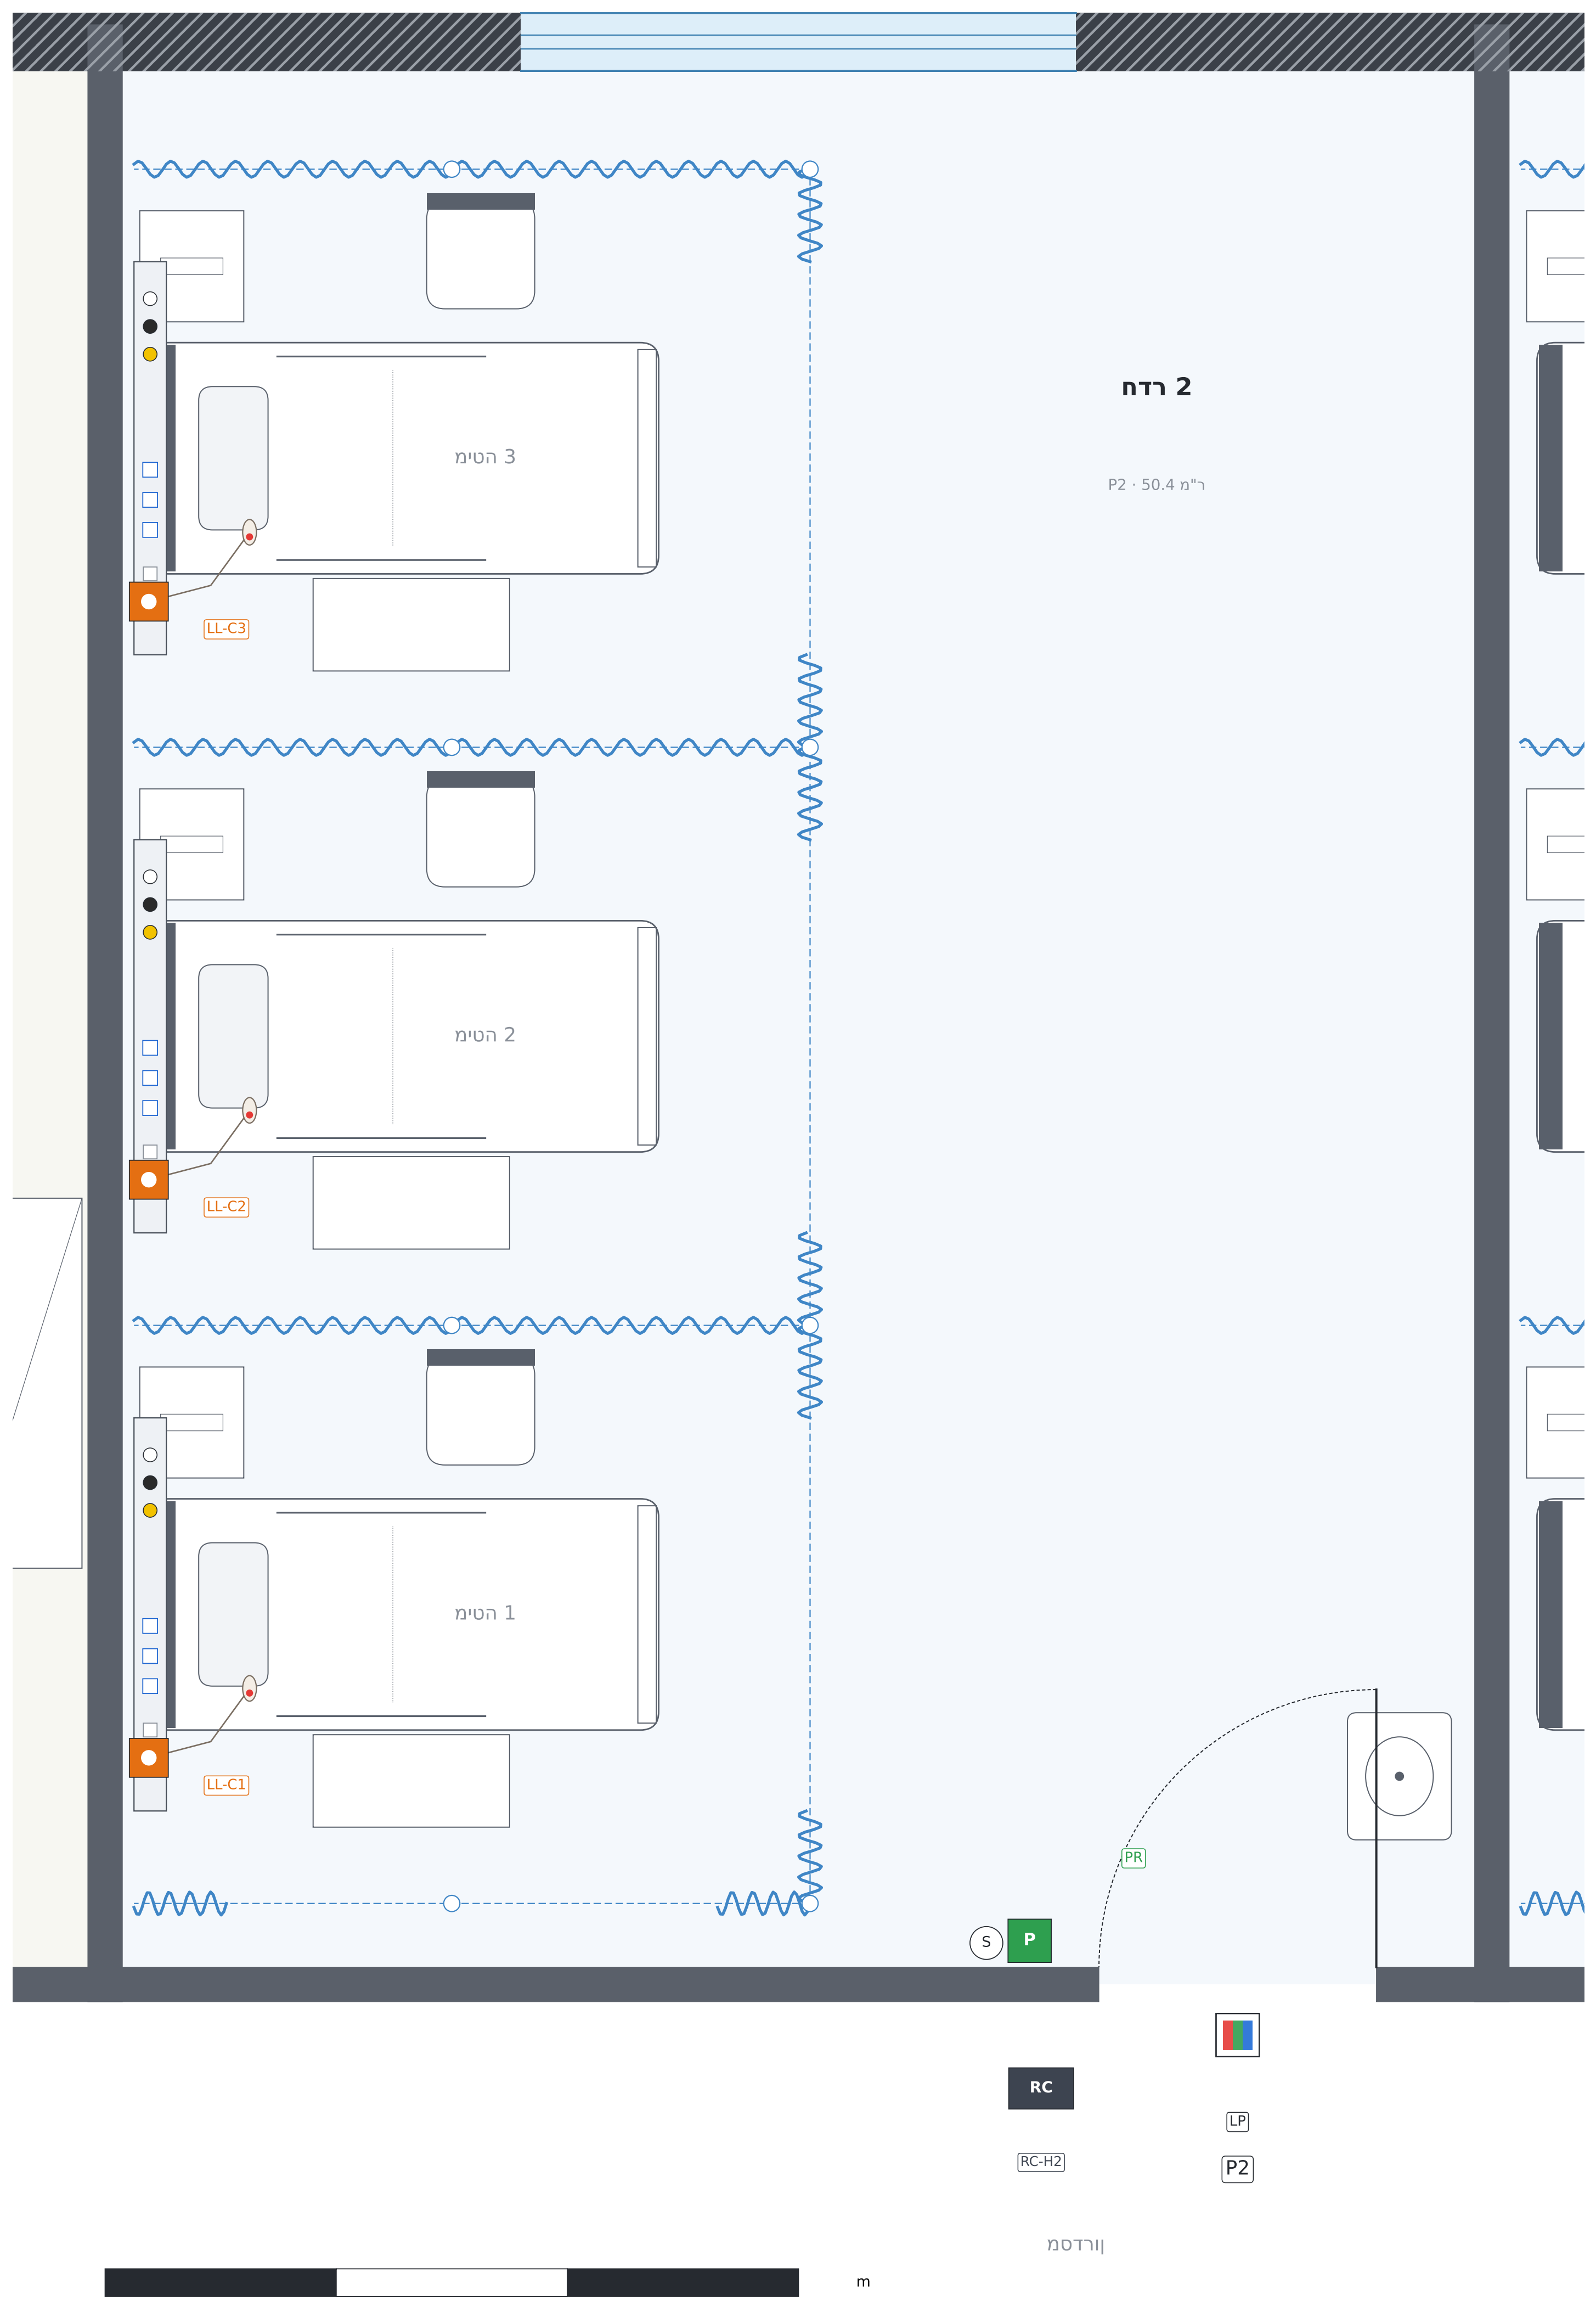
חדר 2
P2 · 50.4 מ"ר
מיטה 3
מיטה 2
מיטה 1
LL-C3
LL-C2
LL-C1
PR
S
P
RC
RC-H2
LP
P2
מסדרון
m

B · 1:30 · חדר טיפוסי – חיווט

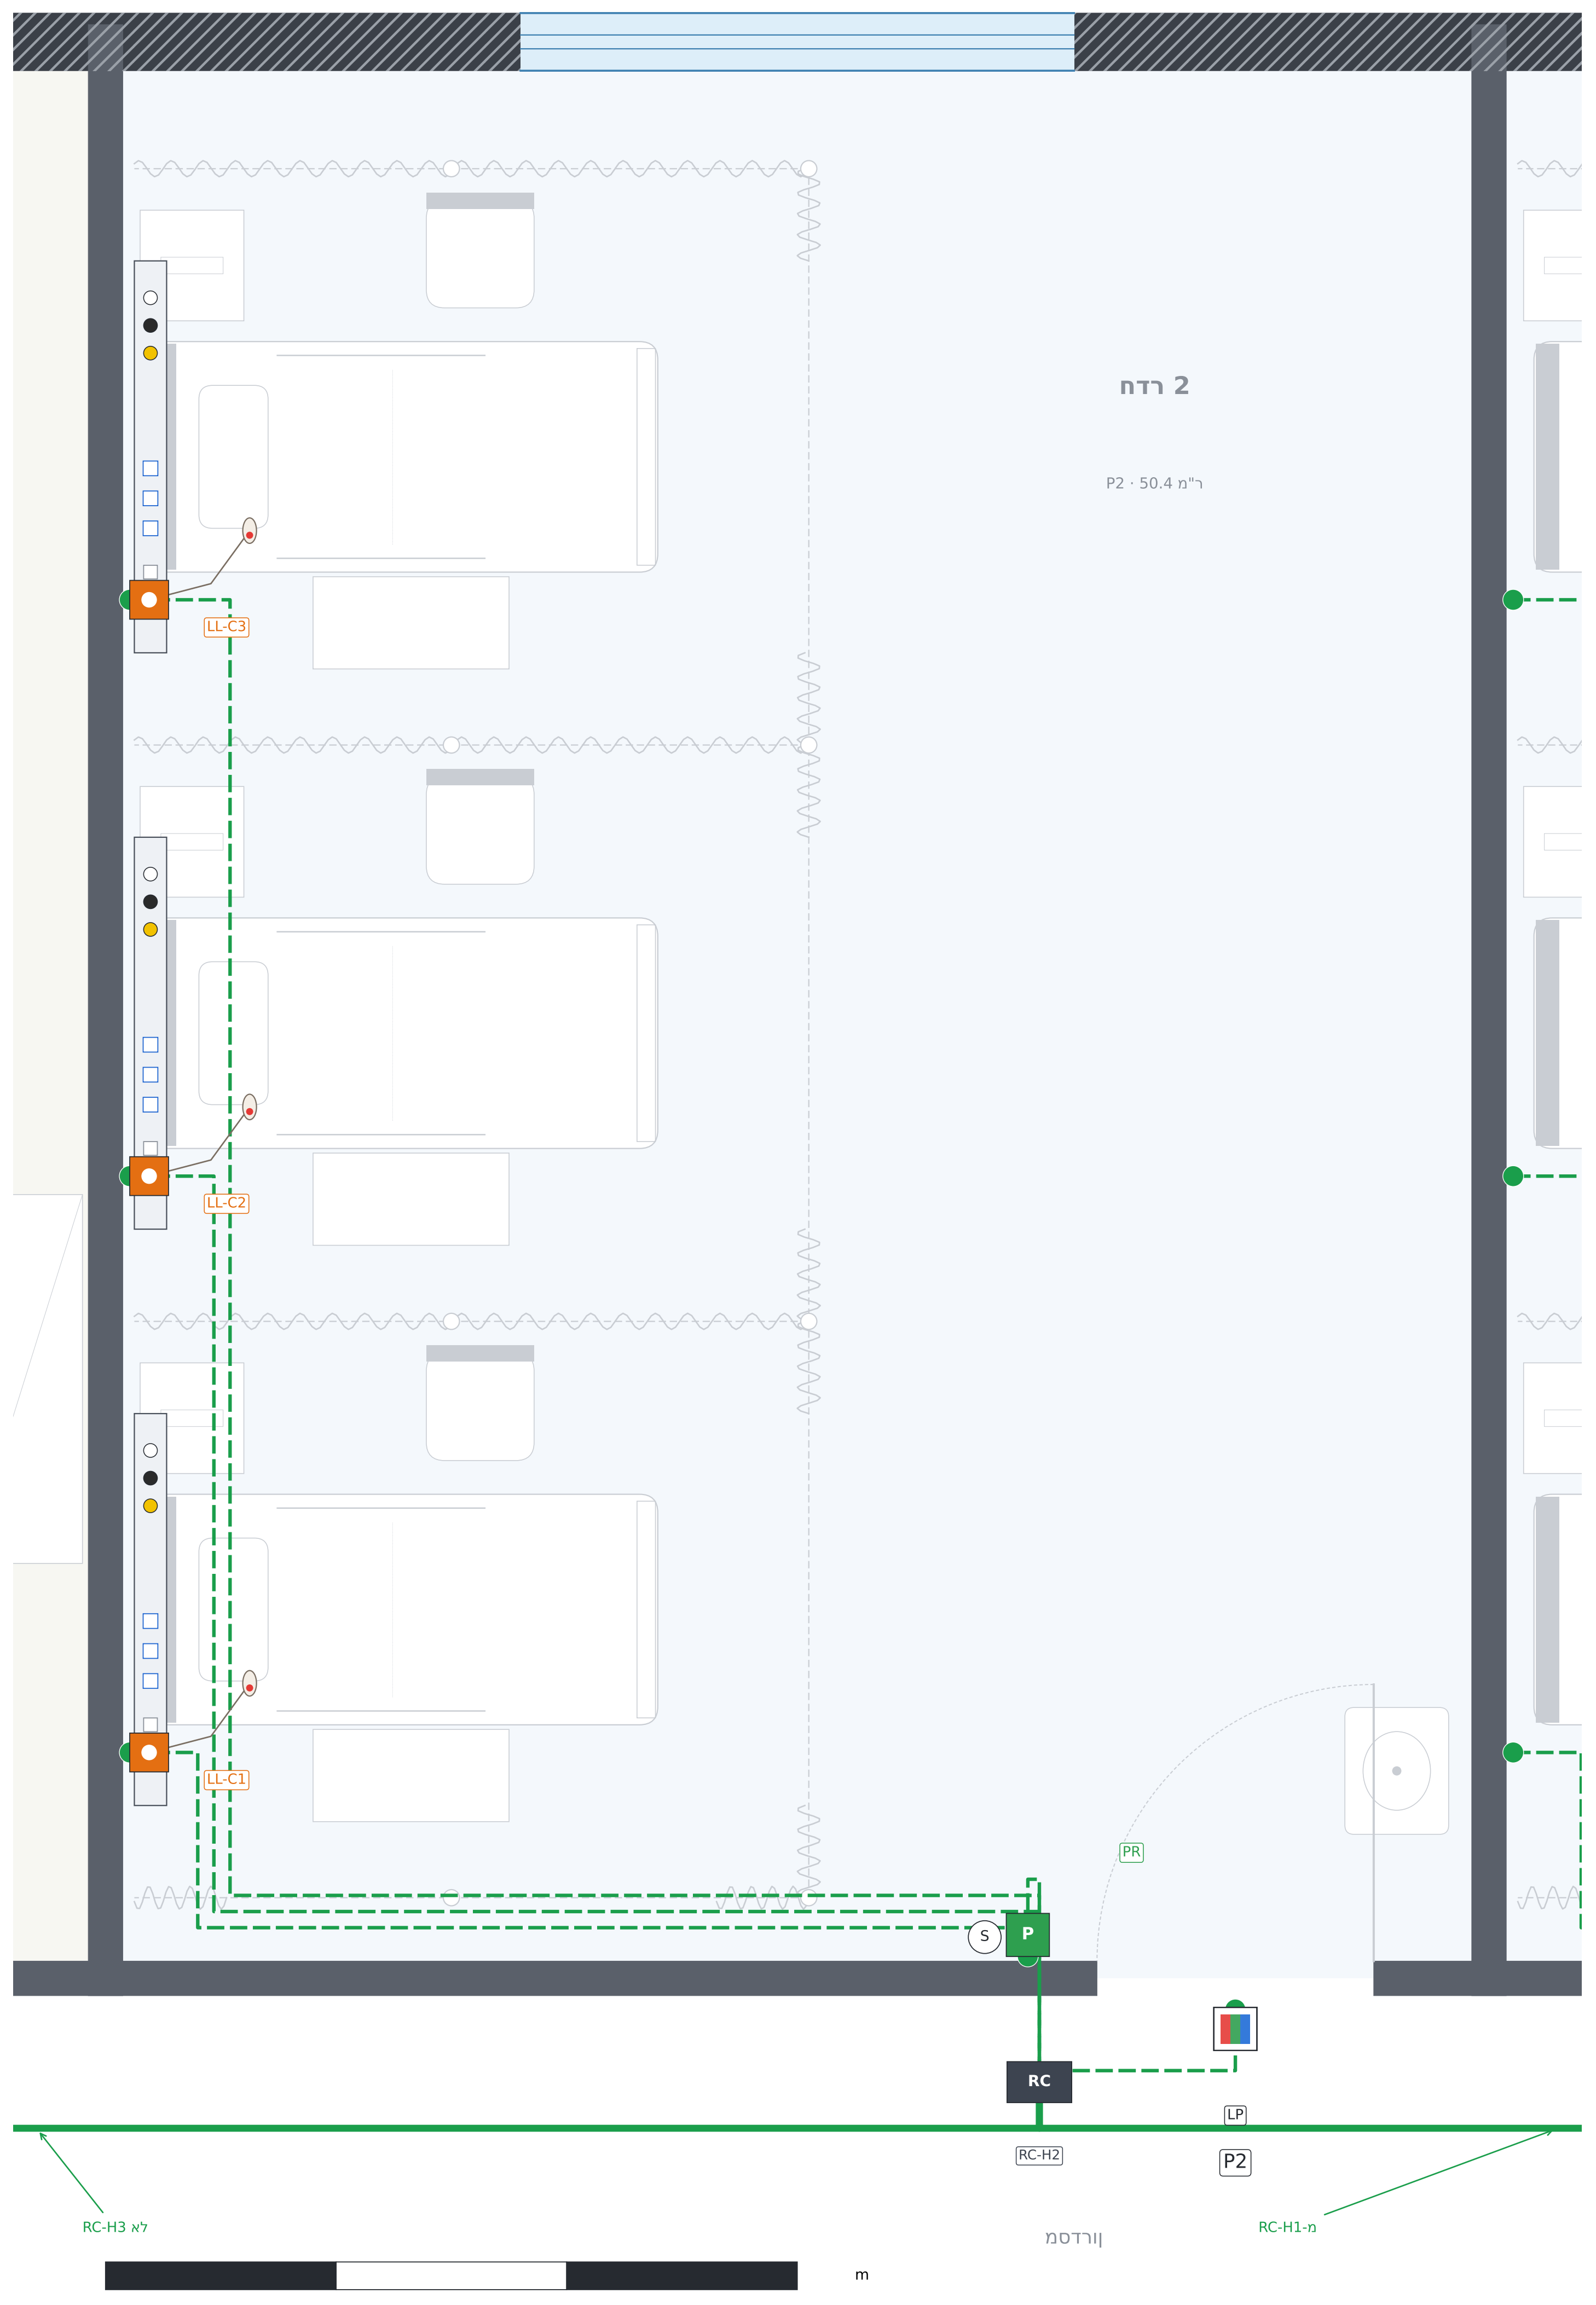
חדר 2
P2 · 50.4 מ"ר
LL-C3
LL-C2
LL-C1
PR
S
P
RC
RC-H2
LP
P2
מסדרון
אל RC-H3
מ-RC-H1
m

C · 1:30 · חזית קיר הקונסולות (מתוך החדר)

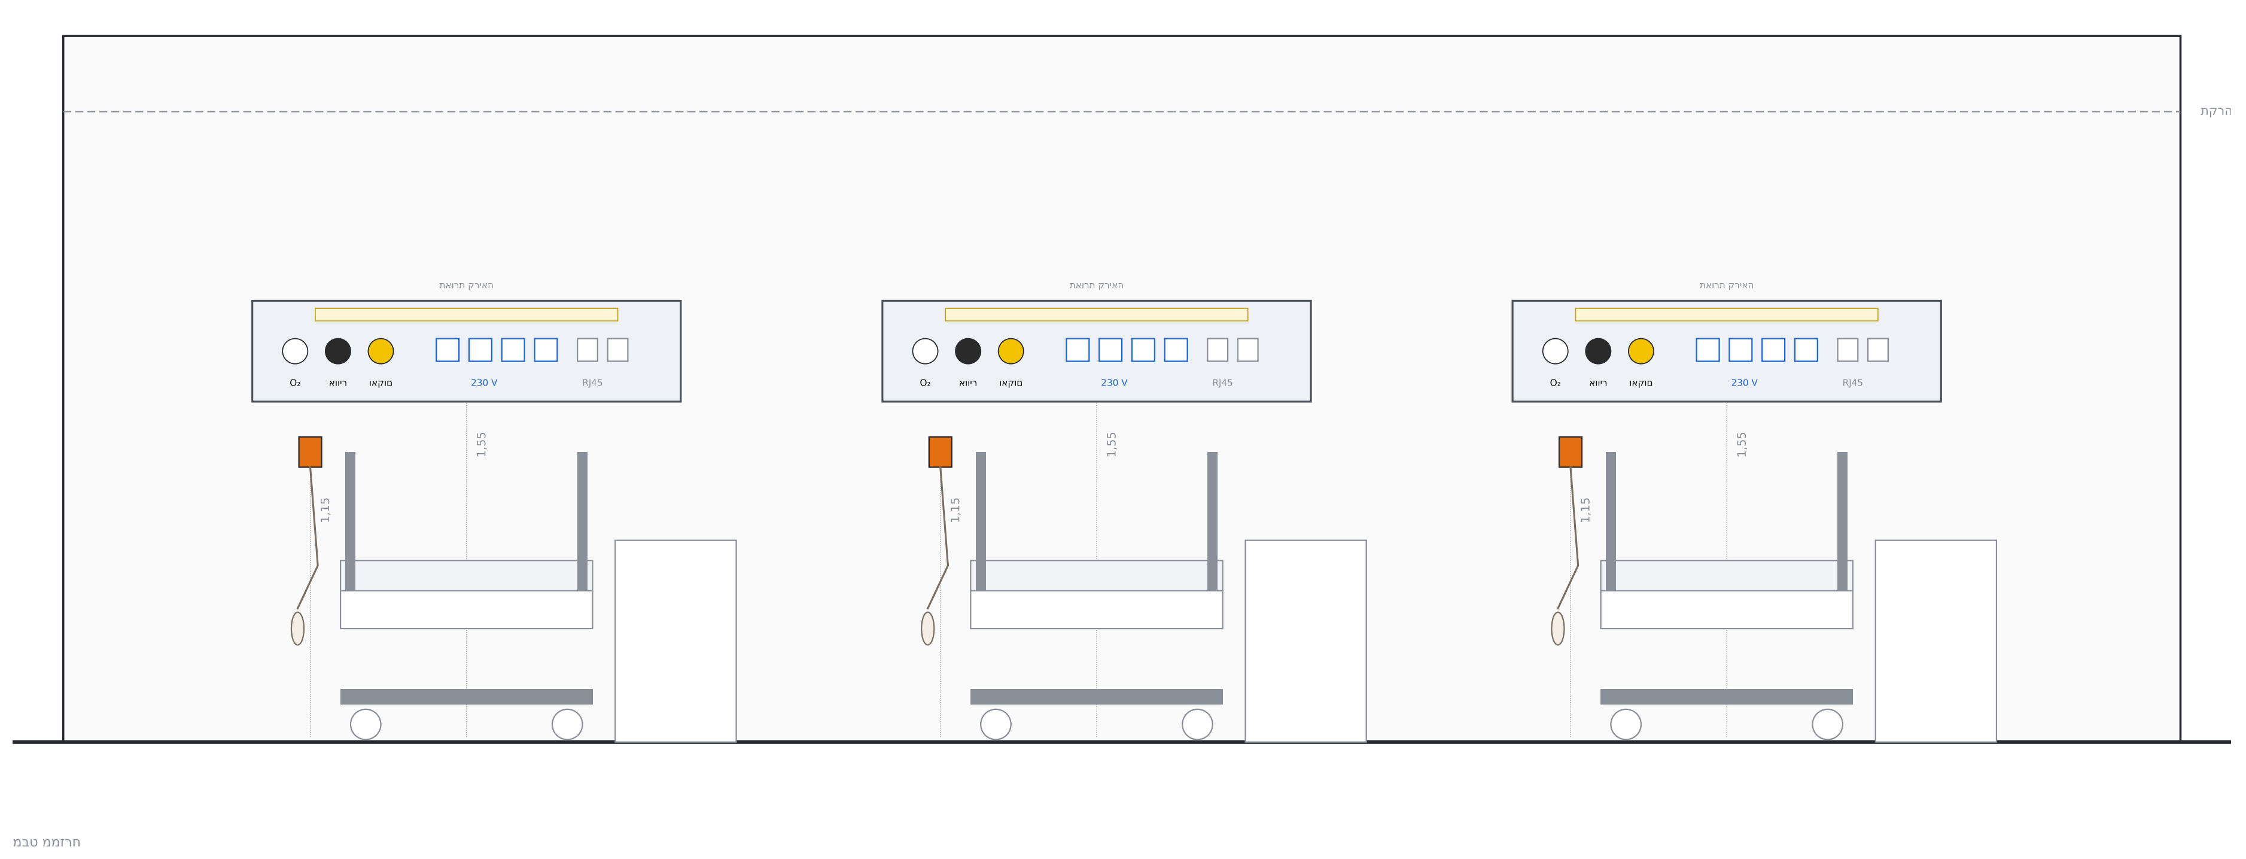
תאורת קריאה
O_2
אוויר
ואקום
230 V
RJ45
1,55
1,15
מבט ממזרח

D · חזית מסדרון – P2 · 1:30

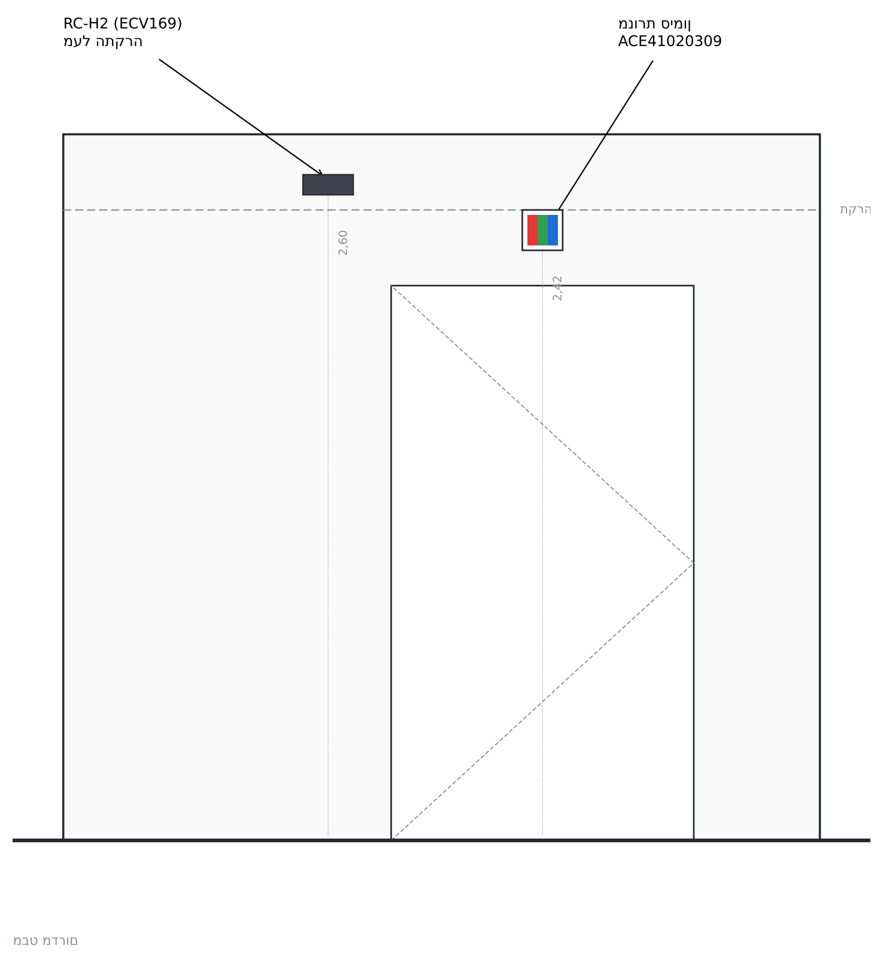
RC-H2 (ECV169)
מעל התקרה
מנורת סימון
ACE41020309
תקרה
2,60
2,42

הערות

1. מיטות עם הראש לקיר צדדי; קונסולה לכל מיטה: חמצן, אוויר, ואקום, 4 שקעי 230V, 2 RJ45, תאורת קריאה.

2. לחצן קריאה Advantecnia ליד הקונסולה (גובה 1.15 מ') עם אגס נתיק שמגיע למיטה.

3. ליד הדלת (בפנים): מתגי תאורה בגובה 1.05 מ' וביטול/נוכחות בגובה 1.35 מ'.

4. מנורת סימון ACE41020309 מעל המשקוף, לכיוון המסדרון, גובה 2.42 מ': אדום = קריאה · ירוק = נוכחות · כחול = קוד כחול · כבוי = אין קריאה.

5. כרטיס 24 פינים ECV169 מחוץ לחדר, מעל תקרת המסדרון. כל LL, PR ו-LP מגיעים בכבל משלו (רדיאלי).

6. וילון U לכל מיטה: מסילת תקרה על מוטות, רשת עליונה לבנה ובד תכלת מעכב בעירה; החזית פתוחה.

7. חלון בקצה כל חדר, 2.40 × 1.30 מ', אדן בגובה 0.90 מ'.

סמלים

🟧	LL · לחצן קריאה למיטה ACE41220316 + אגס (1 למיטה) Bed call panel + pear push · לחצן קריאה למיטה + אגס
LP	LP · מנורת מסדרון ACE41020309 (אדום קריאה · ירוק נוכחות · כחול קוד כחול) Corridor indicator light, 3 colours · מנורת מסדרון תלת-צבעית
RC	RC · בקר חדר / ממיר כרטיס ECV169 (תקרת מסדרון) Room controller ECV169 (corridor ceiling) · בקר חדר ECV169 (תקרת מסדרון)
S	S · מתגי תאורת חדר Room light switches · מתגי תאורה
PC	טלפון: עמדת אחיות ACE52190200 / מחשב ACE52040208 ו-TV Touch all-in-one PC & TV running Advantecnia · מחשב מגע וצג TV עם תוכנת Advantecnia
P	PR · ביטול / נוכחות ACE80081001 Presence / cancel button · לחצן נוכחות / ביטול
T	TI/TD · משיכת חבל לאסלה / מקלחת ACE40320303 (≥ 1.80 מ') Pull-cord (mounted ≥ 1.80 m) · משיכת חבל בשירותים (≥1.80 מ')
○●●□□□	CT · קונסולת מיטה: חמצן · אוויר · ואקום, שקעי 230V, RJ45 Bed-head unit: medical gases, power, data · קונסולת מיטה: גזים, חשמל, תקשורת
GAB	ארון: SmartHub, מתג ACEUCM6302, שרת ACE51010103 Comms rack: SmartHub, switch, server · ארון תקשורת: SmartHub, מתג, שרת
TE	לוח חשמל מחלקתי Electrical sub-panel · לוח חשמל

גבהים במטרים מהריצוף. תקני Advantecnia: LL 1.15 · PR 1.35 · מתגי תאורה LP 2.42 · RC · 1.05 מעל התקרה.

מחלקת אשפוז · מערכת קריאת אחות
Nurse Call System · Inpatient Ward
הוכן ע"י: Telab International   מערכת: ACE BG · Advantecnia

חדר אשפוז טיפוסי (H2) – פרט

Typical patient room – plan, wiring & elevations
חדר אשפוז טיפוסי – פרטים

קנה מידה	תאריך	REV	גיליון
1:30	12/10/2026	A	03

מידות במטרים
פורמט A1 · מהדורה A – תכנון מוקדם

A · 1:30 · גוש שירותים – ציוד וחיווט

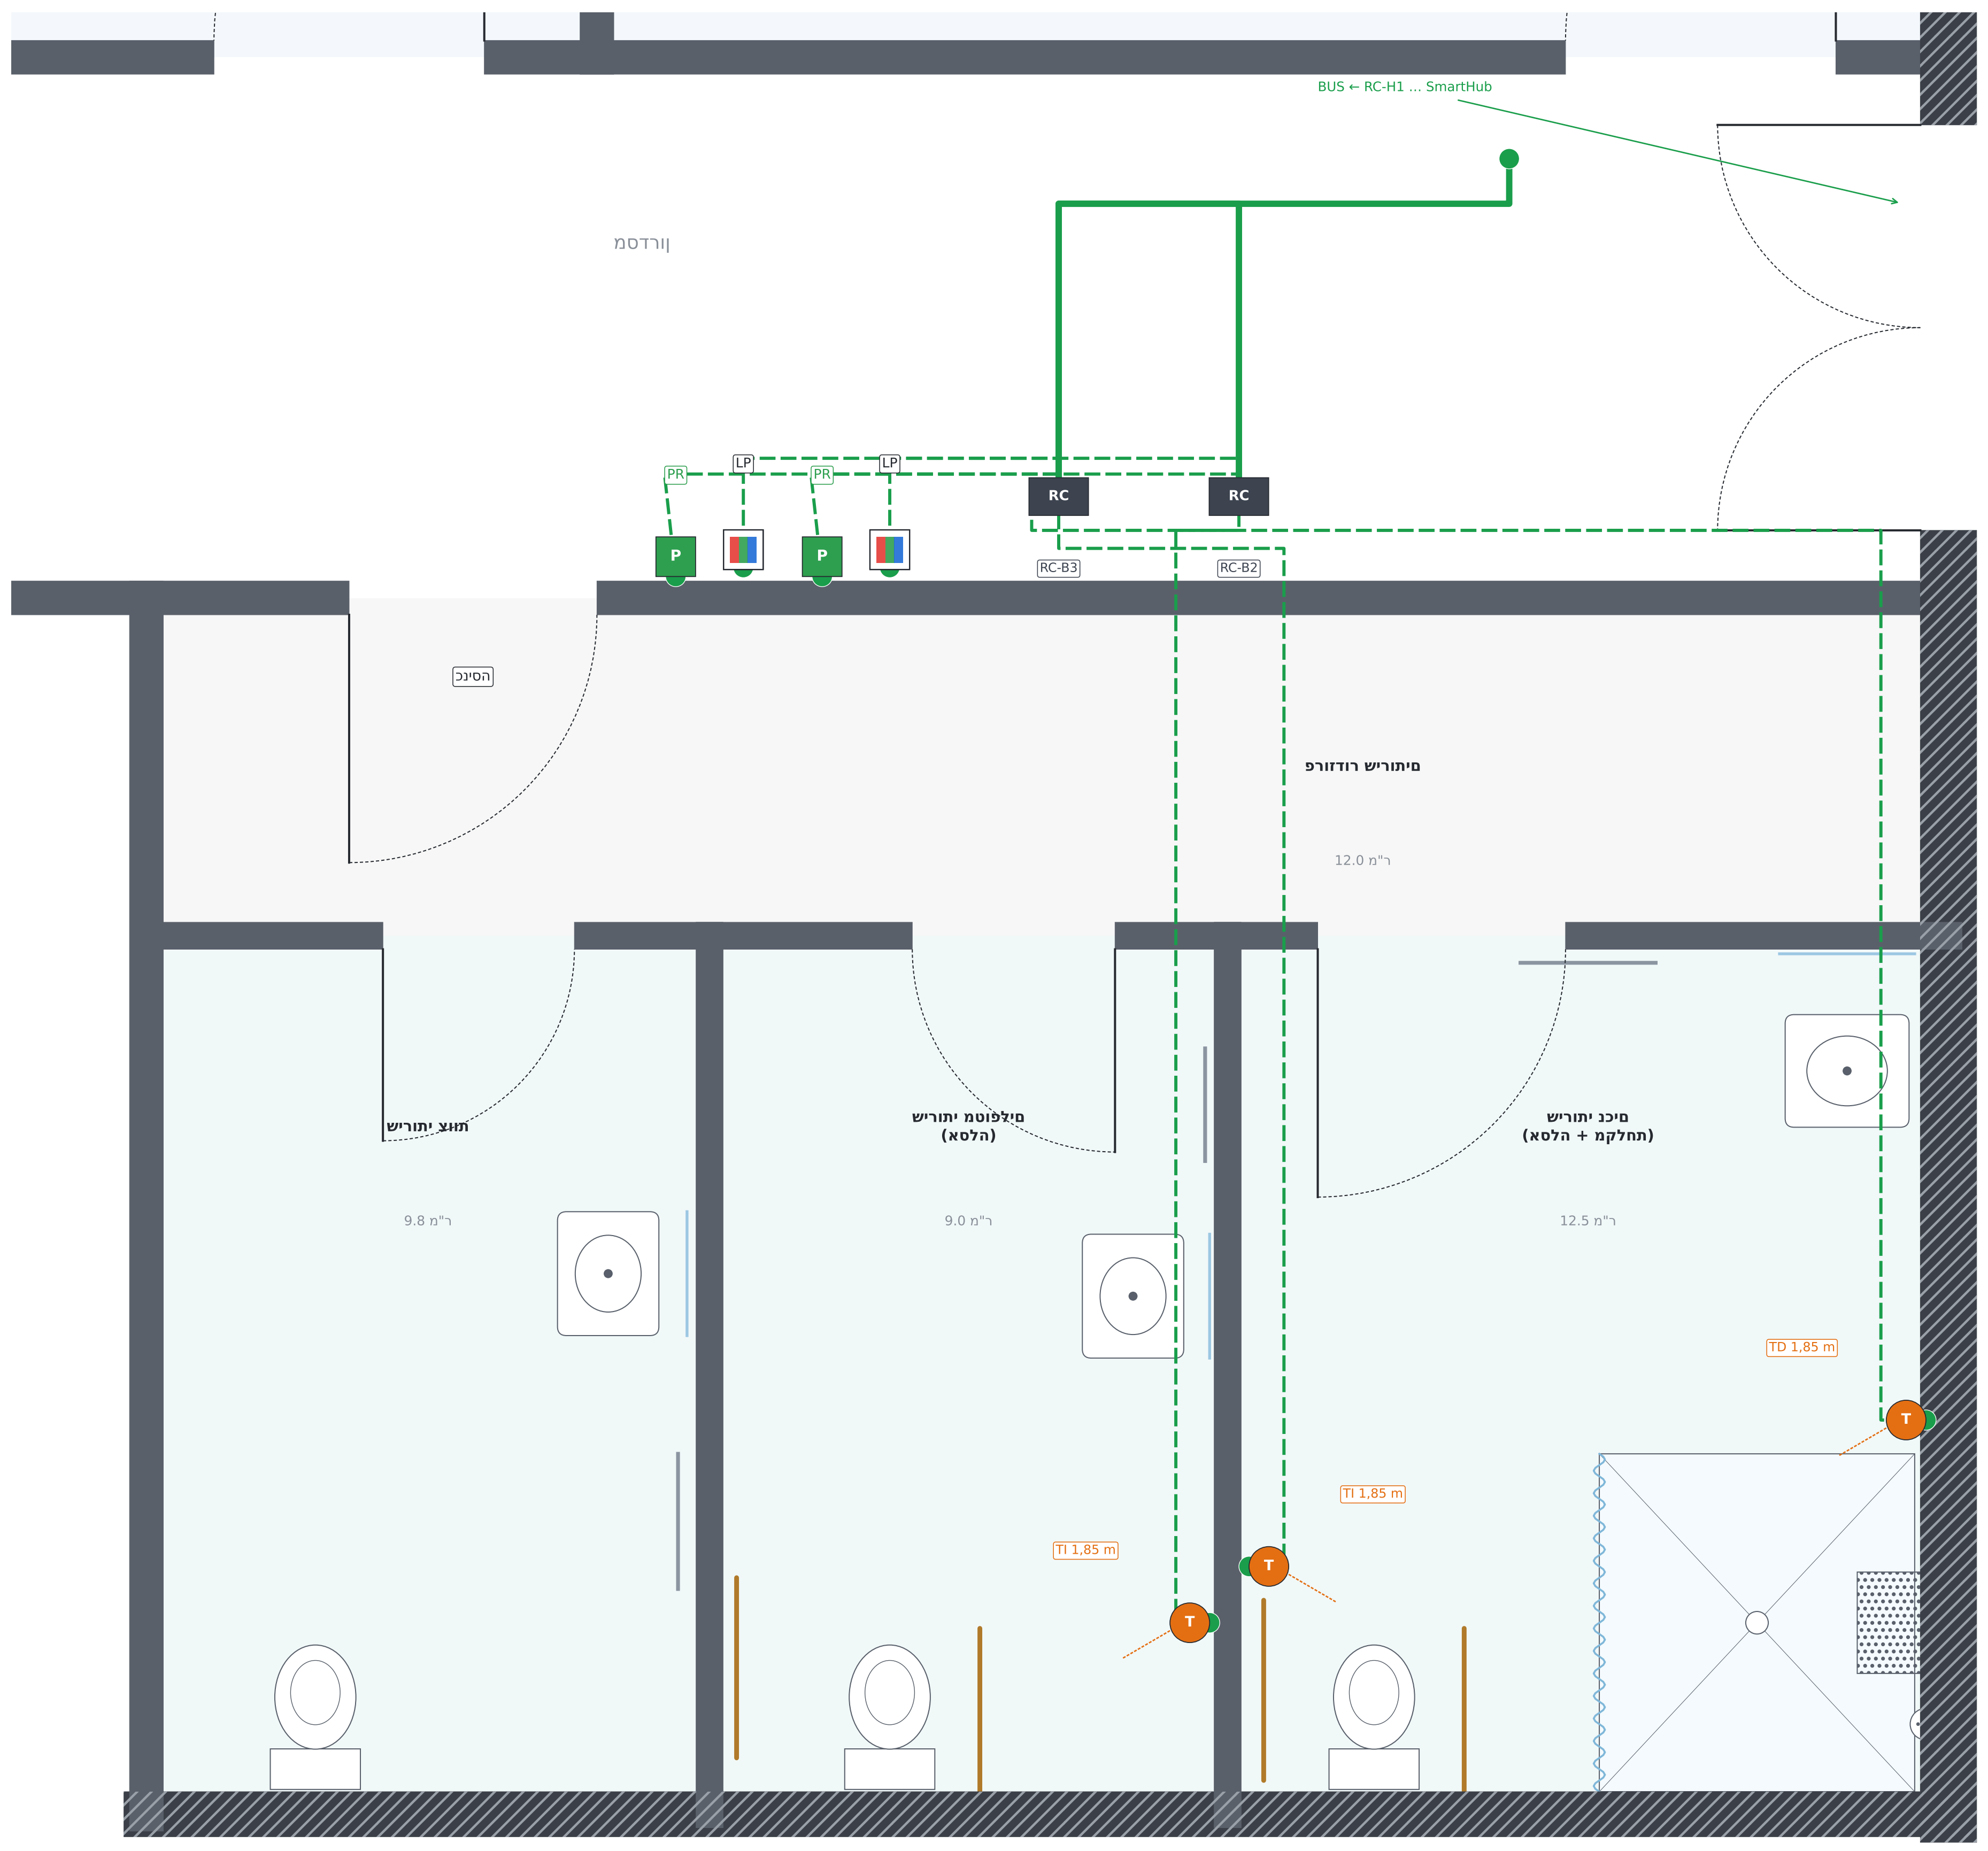
BUS ← RC-H1 … SmartHub
מסדרון
PR
LP
PR
LP
P
P
RC
RC
RC-B3
RC-B2
כניסה
פרוזדור שירותים
12.0 מ"ר
שירותי צוות
9.8 מ"ר
שירותי מטופלים
(אסלה)
9.0 מ"ר
שירותי נכים
(אסלה + מקלחת)
12.5 מ"ר
TD 1,85 m
TI 1,85 m
TI 1,85 m
T
T
T

F · עמדת אחיות + TV · 1:30

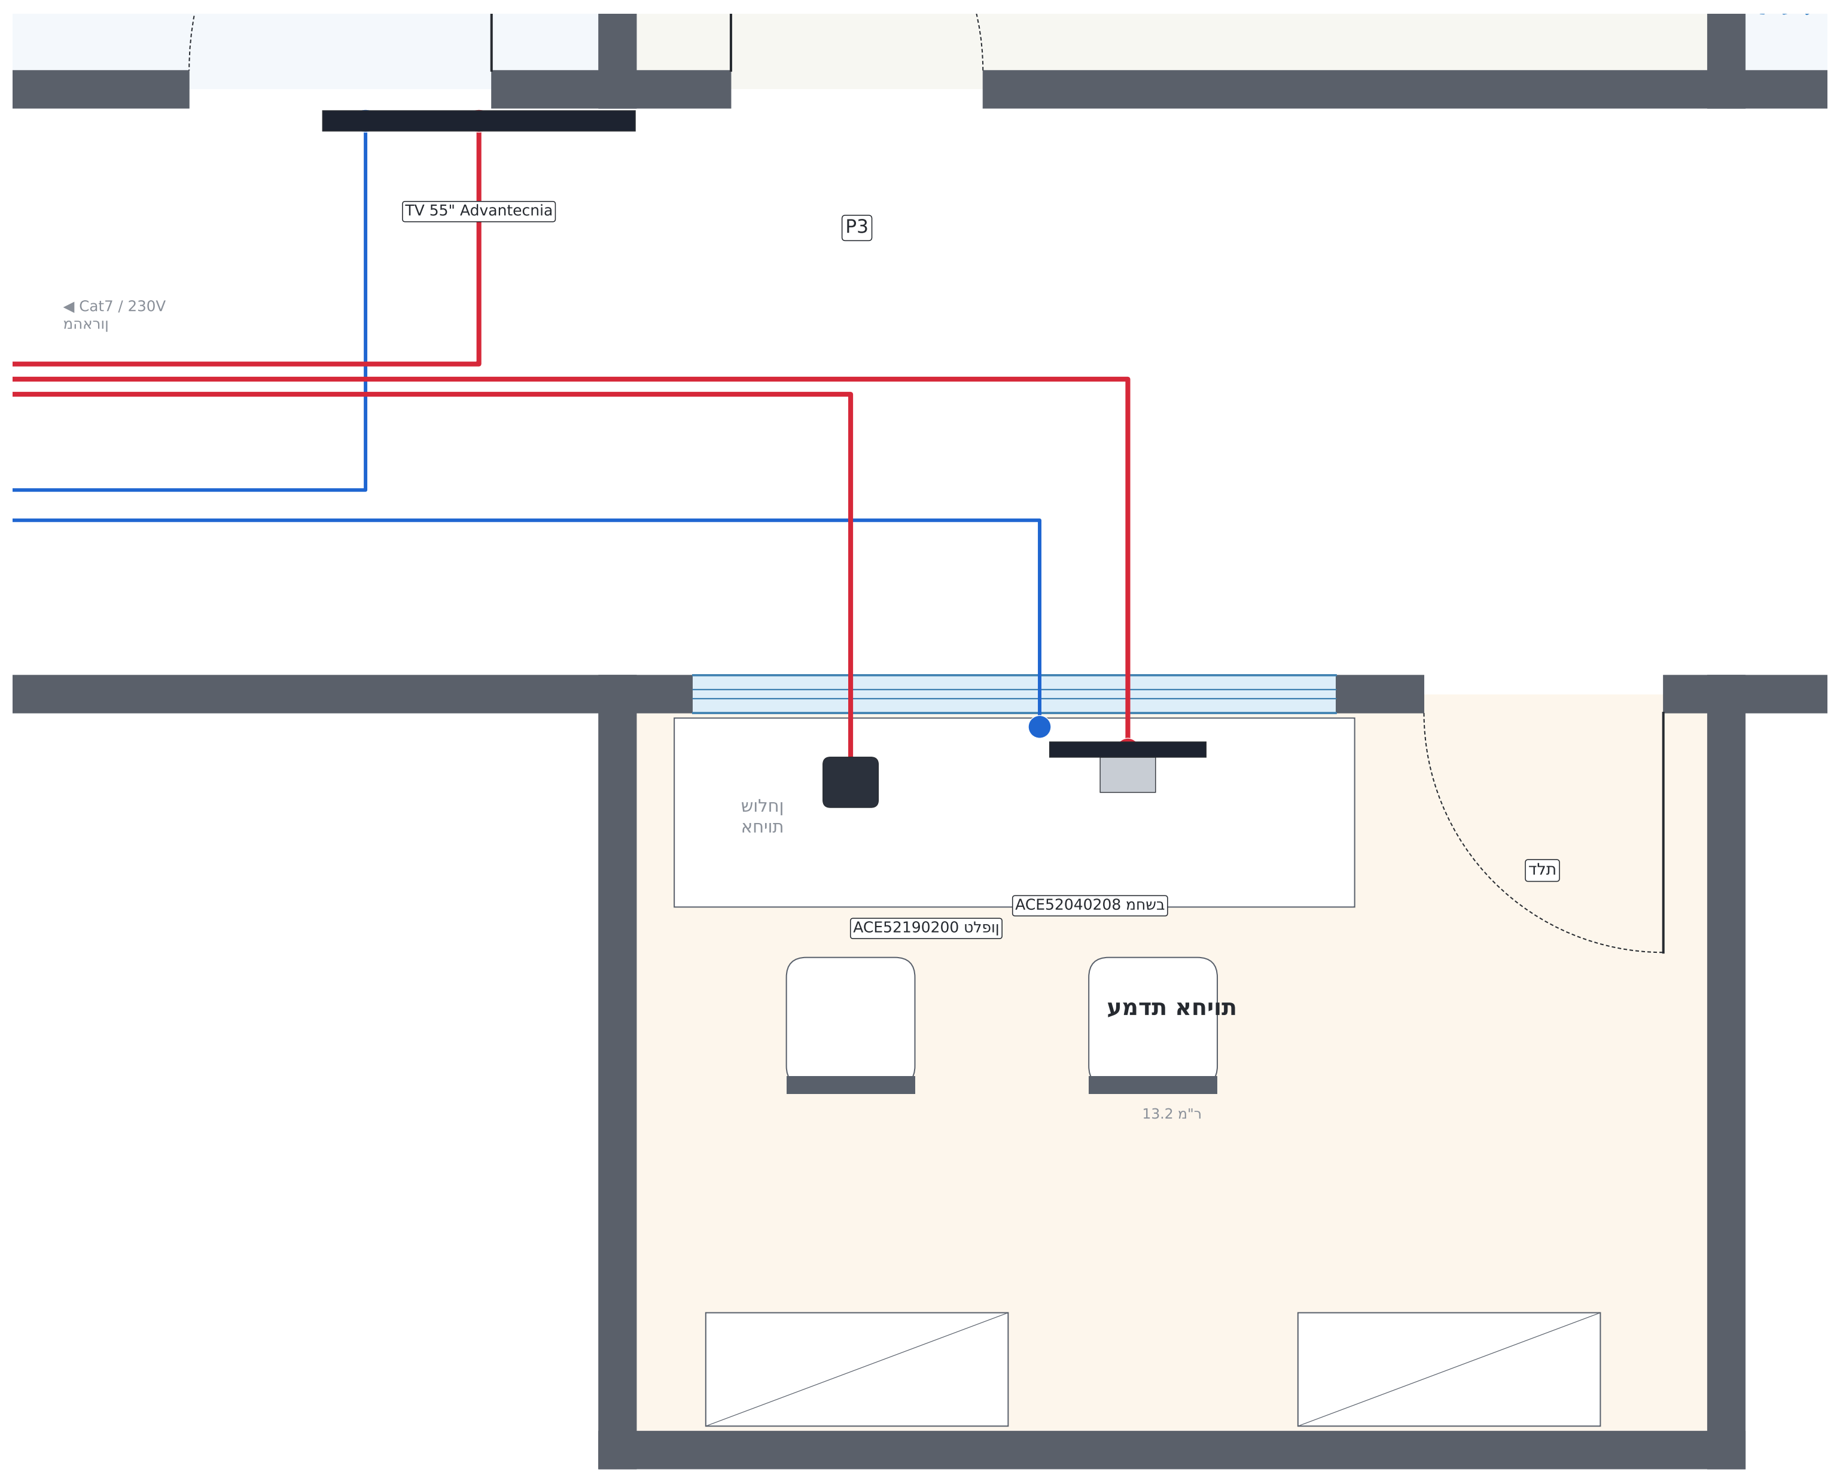
TV 55" Advantecnia
P3
◀ Cat7 / 230V
מהארון
שולחן
אחיות
מחשב ACE52040208
טלפון ACE52190200
דלת
עמדת אחיות
13.2 מ"ר

G · חזית TV (קיר P3–P4)

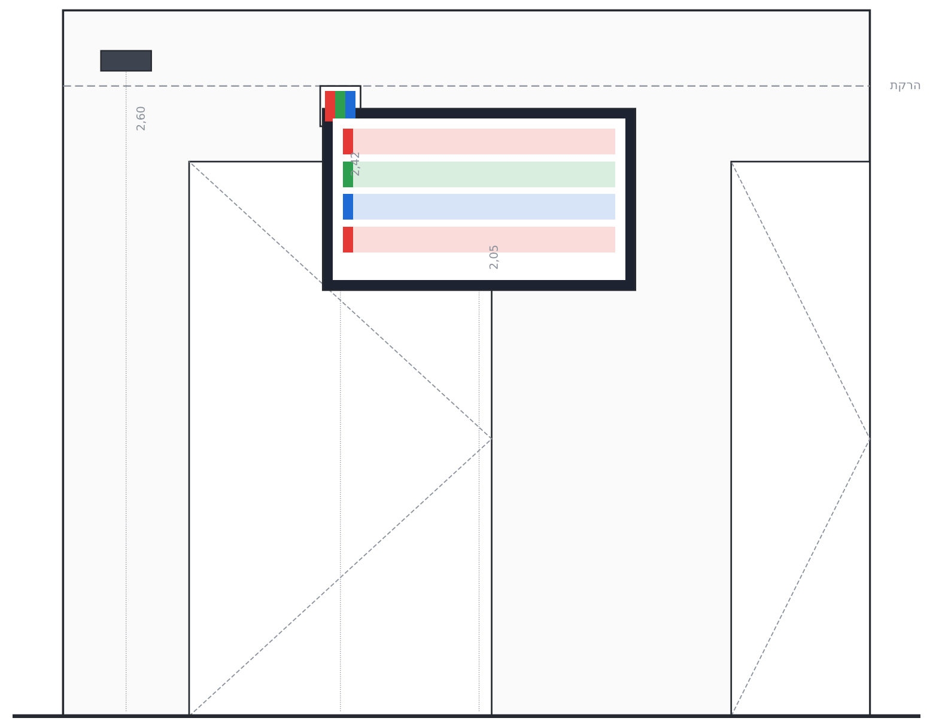
תקרה
2,60
2,42
2,05

מבט מדרום

הערות

1. B1 שירותי צוות (ללא קריאה).

2. B2: אסלה עם מאחז קבוע ומתקפל;
חבל TI בגובה 1.85 מ'.

3. B3 נגיש: אסלה + מקלחת עם מושב מתקפל
ומאחזים; חבלים TI (אסלה)
ו-TD (מקלחת) בגובה 1.85 מ'.

4. במסדרון, ליד הכניסה: LP-B2 / LP-B3
בגובה 2.42 מ' ו-PR-B2 / PR-B3 בגובה 1.35 מ'.

5. RC-B2 ו-RC-B3 בתקרת המסדרון;
מצטרפים לשרשרת ה-BUS (1 ו-2).

6. עמדה עם דלת משלה; שולחן צמוד
לקיר המסדרון (חלון): האחות פונה
למסדרון ול-TV.
טלפון ACE52190200 / מחשב ACE52040208.

B · חזית B2 – משיכת חבל אסלה

מבט ממזרח

חבלי TI/TD בגובה 1.85 מ' (≥ 1.80 מ') עם חבל עד 0.20 מ' מהרצפה · LP בגובה 2.42 מ' · PR בגובה 1.35 מ' · גבהים מהריצוף.

C · חזית B3 – משיכת חבל אסלה

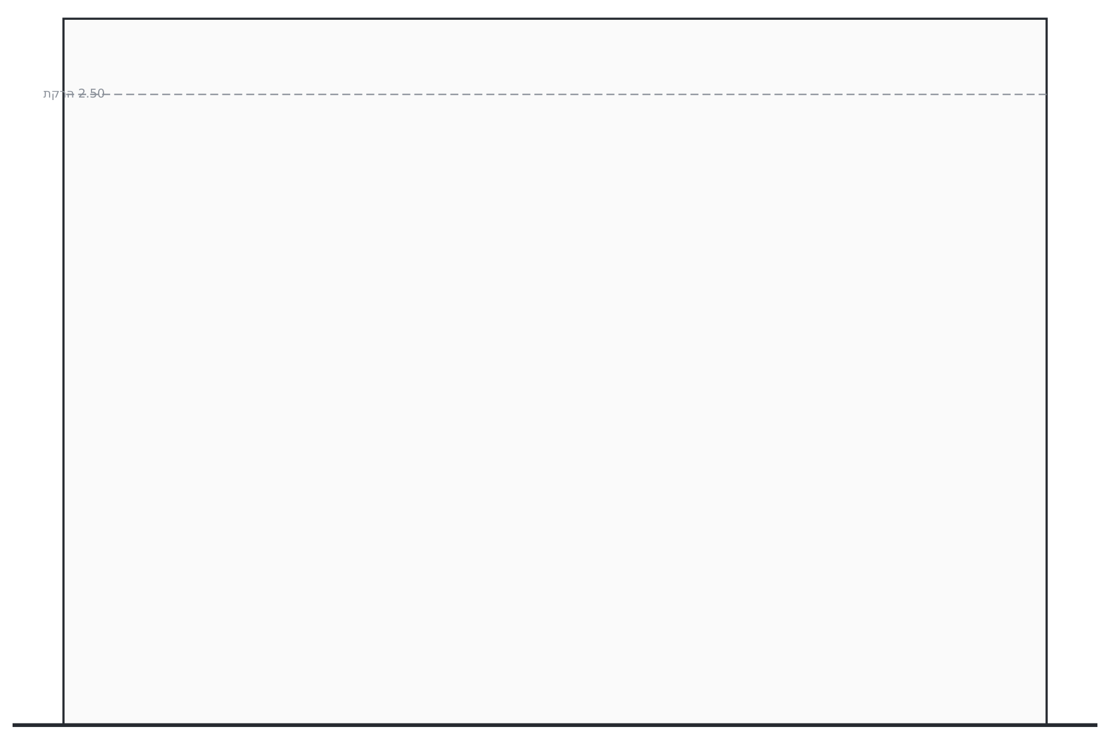

מבט ממערב

D · חזית B3 – משיכת חבל מקלחת

מבט ממזרח

E · חזית מסדרון – כניסה לשירותים

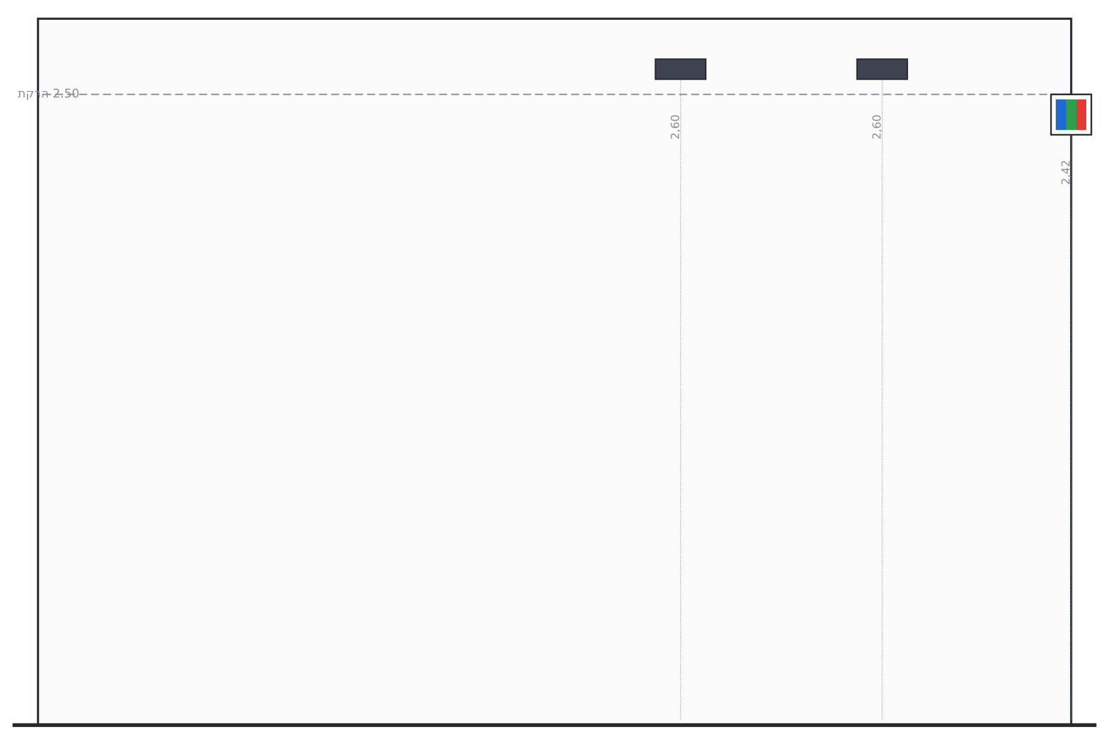
תקרה 2.50
2,60
2,60
2,42

מבט מצפון

מחלקת אשפוז · מערכת קריאת אחות
Nurse Call System · Inpatient Ward
מערכת: ACE BG · Advantecnia   יועץ: Telab International

שירותים ועמדת אחות
Toilets & nurse station – plans and elevations
שירותים ועמדת אחות

קנה מידה	תאריך	REV	גיליון
1:30	12/10/2026	A	04

מידות במטרים
פורמט A1 · מהדורה A – תכנון מוקדם

A · טופולוגיית מערכת קריאת אחות

שירותים B2
שירותים B3
חדר 1
חדר 2
חדר 3
חדר 4
אסלה TI
PR-B2 (מסדרון)
LP-B2 (מסדרון)
מקלחת TD
PR-B3 · LP-B3
מיטה 1·2·3 LL
נוכחות PR
מסדרון LP
רדיאלי
מהדקים / RJ12
RC-B2
RC-B3
RC-H1
RC-H2
RC-H3
RC-H4
ECV169 · 24 פינים 12-48V
כבל BUS KNX 2x2x0.8 – כרטיס ← כרטיס 24 פינים (שרשרת) ← SmartHub
ארון תקשורת (סוף המסדרון)
SmartHub
שער · Raspberry Pi
Cat6A
מחשב All-in-One
עמדת אחיות · מגע
TV 55"
תצוגת קריאות
טלפון שולחני
שולחן
מתג PoE
מזין 24 פורטים
Cat7 – כל התקן ישירות לפורט במתג
לוח חשמל TE
230V לארון, מחשב/טלפון, TV בלבד
UPS + הזנת PoE
כרטיסים והתקנים ב-PoE
שרת
תוכנת Advantecnia

מצבי מנורת המסדרון:

- 🟥 אדום – קריאה (מיטה / שירותים)
- 🟩 ירוק – נוכחות אחות
- 🟦 כחול – קוד כחול
- ⬜ כבוי – אין קריאה

מהלך קריאה:

1. המטופל לוחץ על האגס (או מושך בחבל בשירותים).
2. הלחצן מדווח לבקר החדר (UTP Cat6).
3. הבקר מדליק את מנורת המסדרון באדום ושולח את האירוע ב-BUS.
4. ה-SmartHub מעביר אותו ב-IP לשרת Advantecnia.
5. הקריאה מופיעה במחשב העמדה, בטלפון וב-TV.
6. האחות נכנסת, לוחצת נוכחות (ירוק) ואחר כך ביטול.

B · רשימת חומרים

קוד	תיאור	כמות	הערה
ADVANTECNIA / ACE BG			
LL	ACE41220316 – לחצן קריאה למיטה עם שקע אגס	12	1 למיטה
—	אגס קריאה (כבל + לחצן)	12	1 למיטה
PR	ACE80081001 – נוכחות / ביטול	6	4 חדרים + 2 שירותים
LP	ACE41020309 – מנורת מסדרון תלת-צבעית	6	4 חדרים + 2 שירותים
TI/TD	ACE40320303 – קריאת שירותים / מקלחת במשיכת חבל	3	B2 ×1 · B3 ×2
RC	בקר חדר / ממיר כרטיס PCB 24 פינים ECV169 12-48V	6	H1 H2 H3 H4 B2 B3
SH	SmartHub (Raspberry Pi) – שער BUS/IP	1	ארון
SV	Advantecnia – ACE51010103 שרת + תוכנה	1	ארון
רשת ומחשוב			
PC	ACE52040208 – מחשב / מסך מגע	1	עמדת אחיות
TEL	ACE52190200 – טלפון שולחני לאחיות	1	חלופה למחשב
TV	TV 55" + זרוע קיר	1	קיר P3–P4
SW	ACEUCM6302 – מתג	1	ארון
GAB	ארון 42U + פאץ' פנל + UPS + PDU + ספק PoE	1	סוף המסדרון
כבלים (אורך מחושב + 15% רזרבה)			
—	כבל BUS KNX 2x2x0.8 (ירוק)	45 m	מחושב 35.8 m
—	כבל קריאה רדיאלי התקן ← כרטיס (ירוק)	190 m	מחושב 161.0 m
—	Cat6 / Cat7 – SmartHub, מתג, מחשב/טלפון, TV (אדום)	65 m	מחושב 52.6 m
—	חשמל 3x2.5 ממ"ר LSZH (כחול)	45 m	מחושב 35.3 m
תשתית בית חולים (מקצועות אחרים)			
CT	קונסולת מיטה (חמצן/אוויר/ואקום, 230V, 2×RJ45×4, תאורה)	12	1 למיטה
—	מיטות בית חולים + שידה + שולחן אוכל	12	
—	מסילת וילון U + וילונות מעכבי בעירה	4 סטים	1 לחדר
—	מאחזים קבועים / מתקפלים, מושב מקלחת	1 מנה	B2 · B3

הערות

1. אורכים נמדדו על תוואי המודל (כולל ירידות אנכיות) + 15%.
2. כרטיסי 24 הפינים והתקני הקריאה מוזנים ב-PoE מהארון: אין מעגלי חשמל בחדרים.
3. יש לאשר מול Advantecnia את מספר הבקרים המרבי לקו BUS ואת האורך הכולל.
4. כמויות לתכנון מוקדם: לאמת באתר.

מחלקת אשפוז · מערכת קריאת אחות
Nurse Call System · Inpatient Ward
יועץ: Telab International   מערכת: ACE BG · Advantecnia

טופולוגיית מערכת ורשימת חומרים

System topology & bill of materials
טופולוגיית מערכת ורשימת חומרים

קנה מידה	תאריך	REV	גיליון
S/E	12/10/2026	A	05

מידות במטרים
פורמט A1 · מהדורה A – תכנון מוקדם

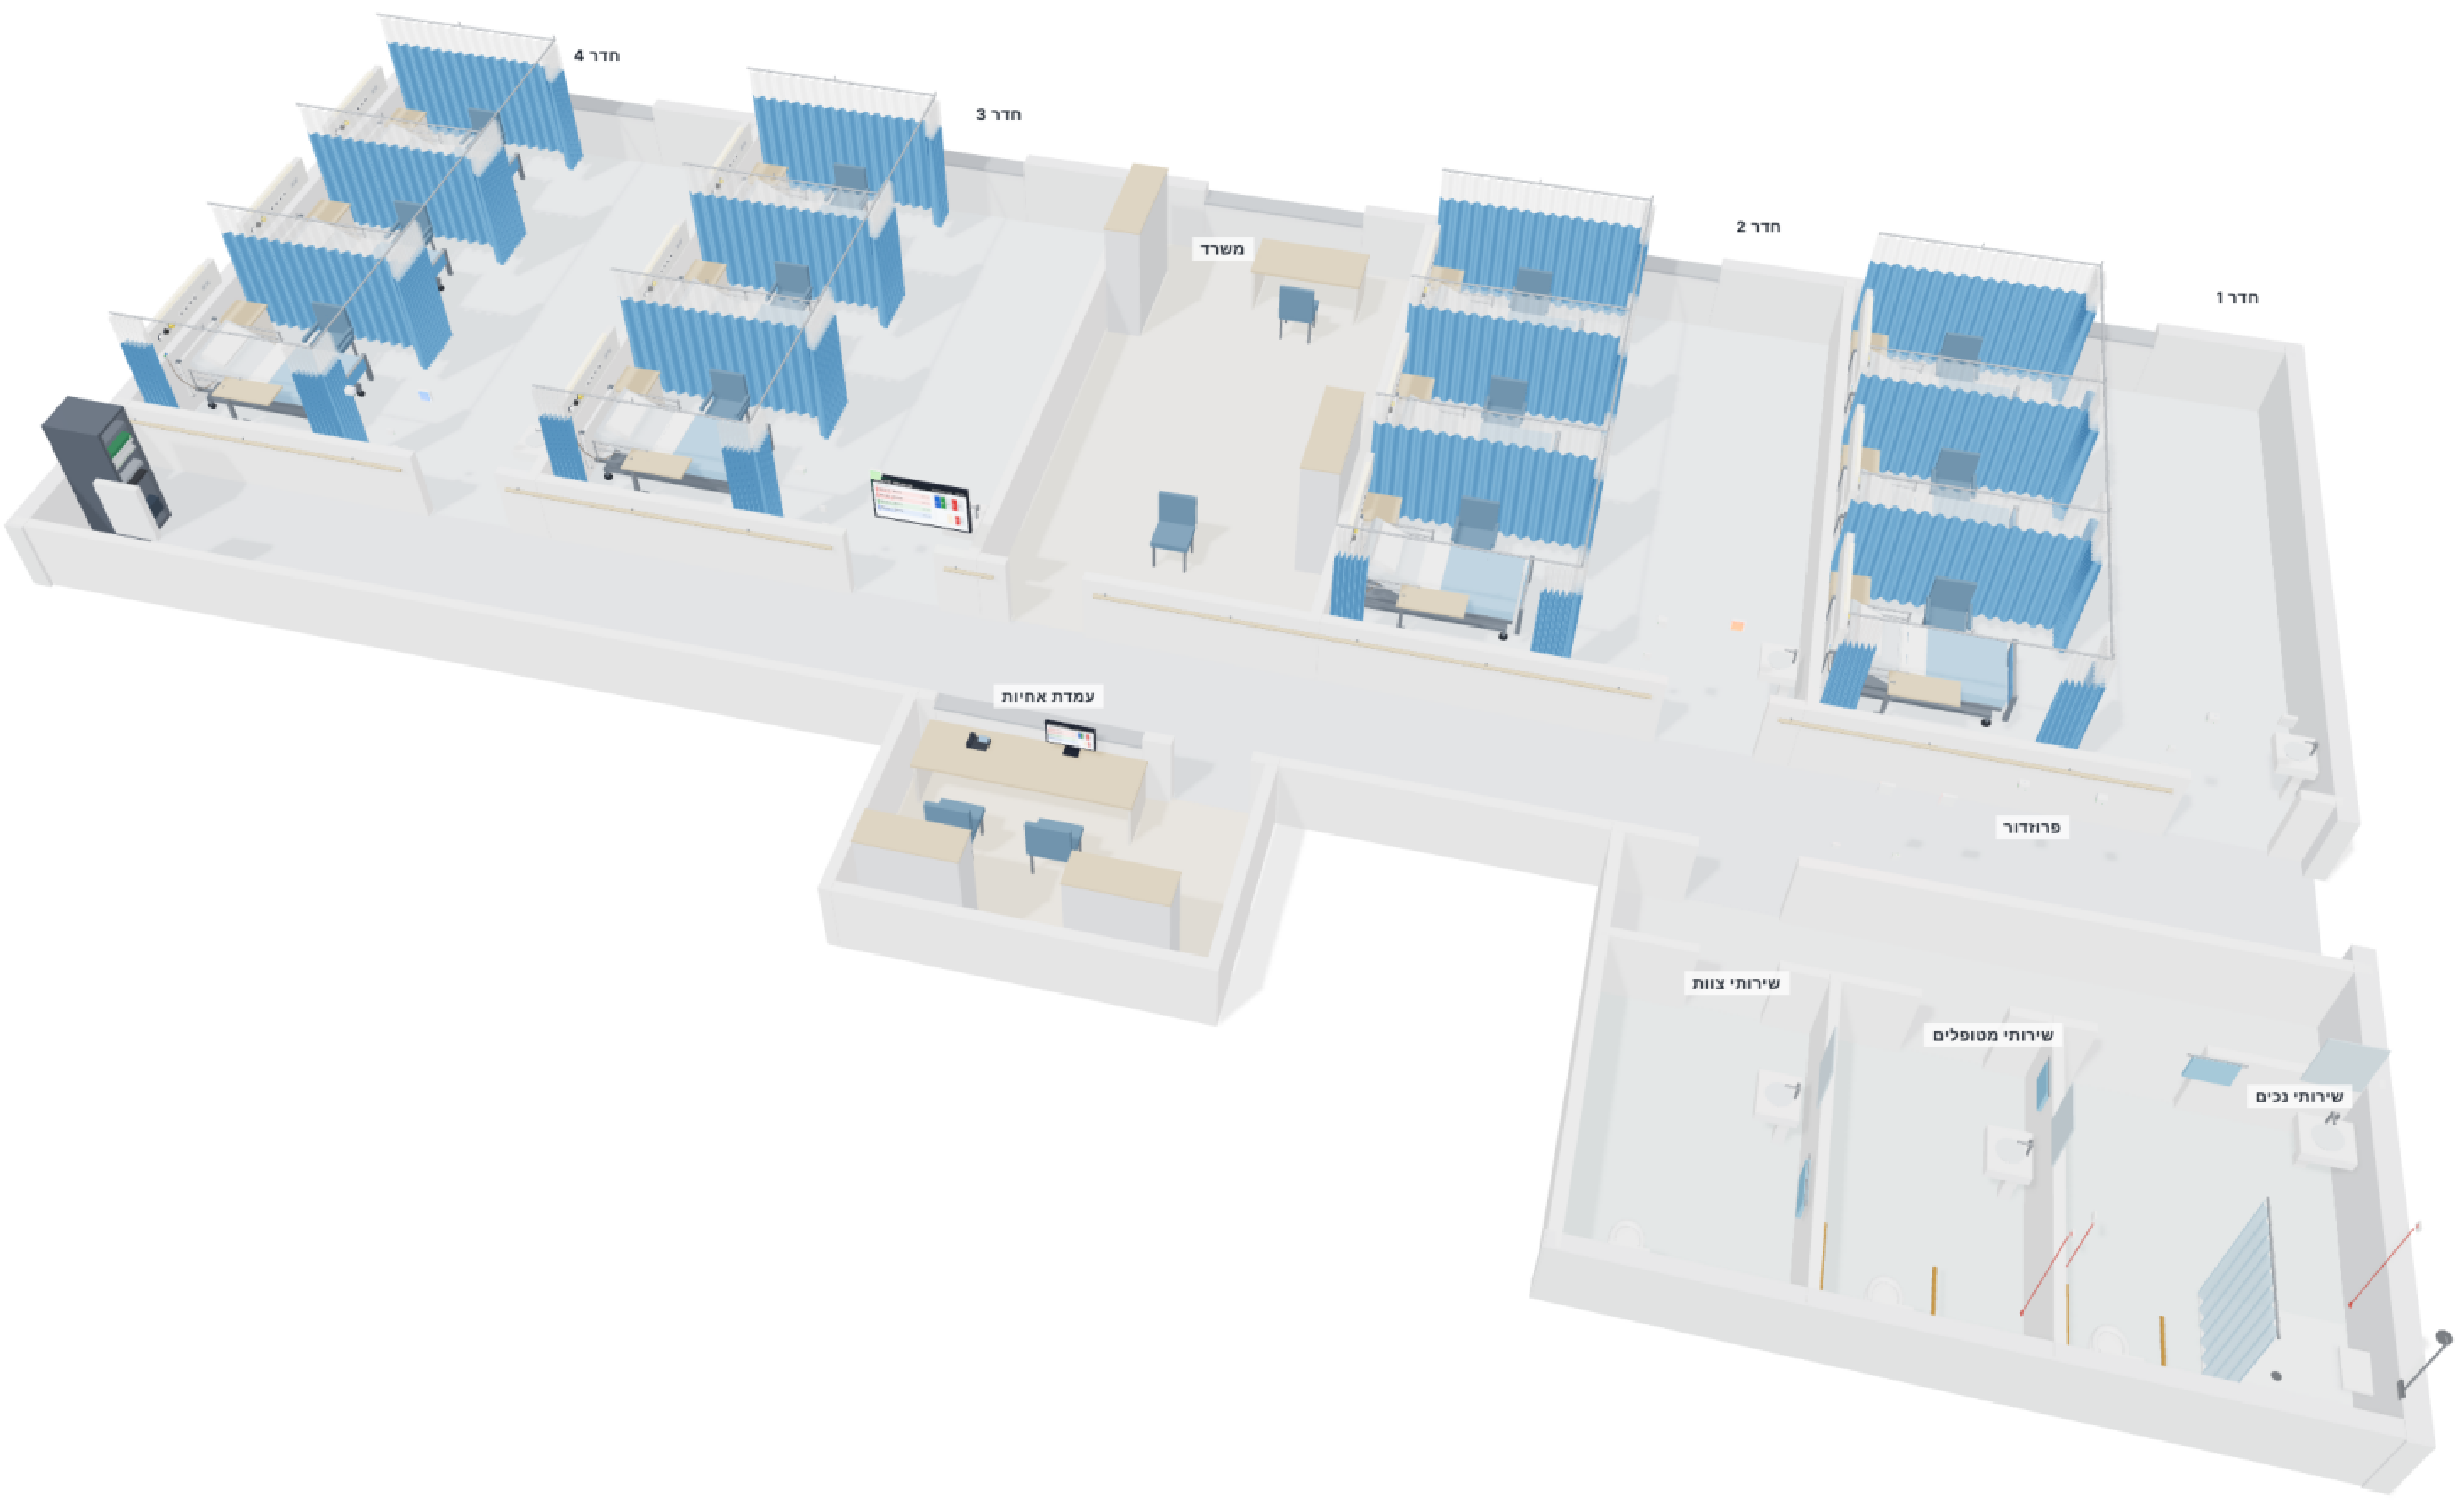

חדר 4
חדר 3
משרד
חדר 2
חדר 1
עמדת אחיות
פרוזדור
שירותי צוות
שירותי מטופלים
שירותי נכים

A · איזומטרי כללי – ציוד

B · חדר: מיטות, וילונות, קונסולות ולחצנים

C · מסדרון: מנורות ולחצני נוכחות של השירותים

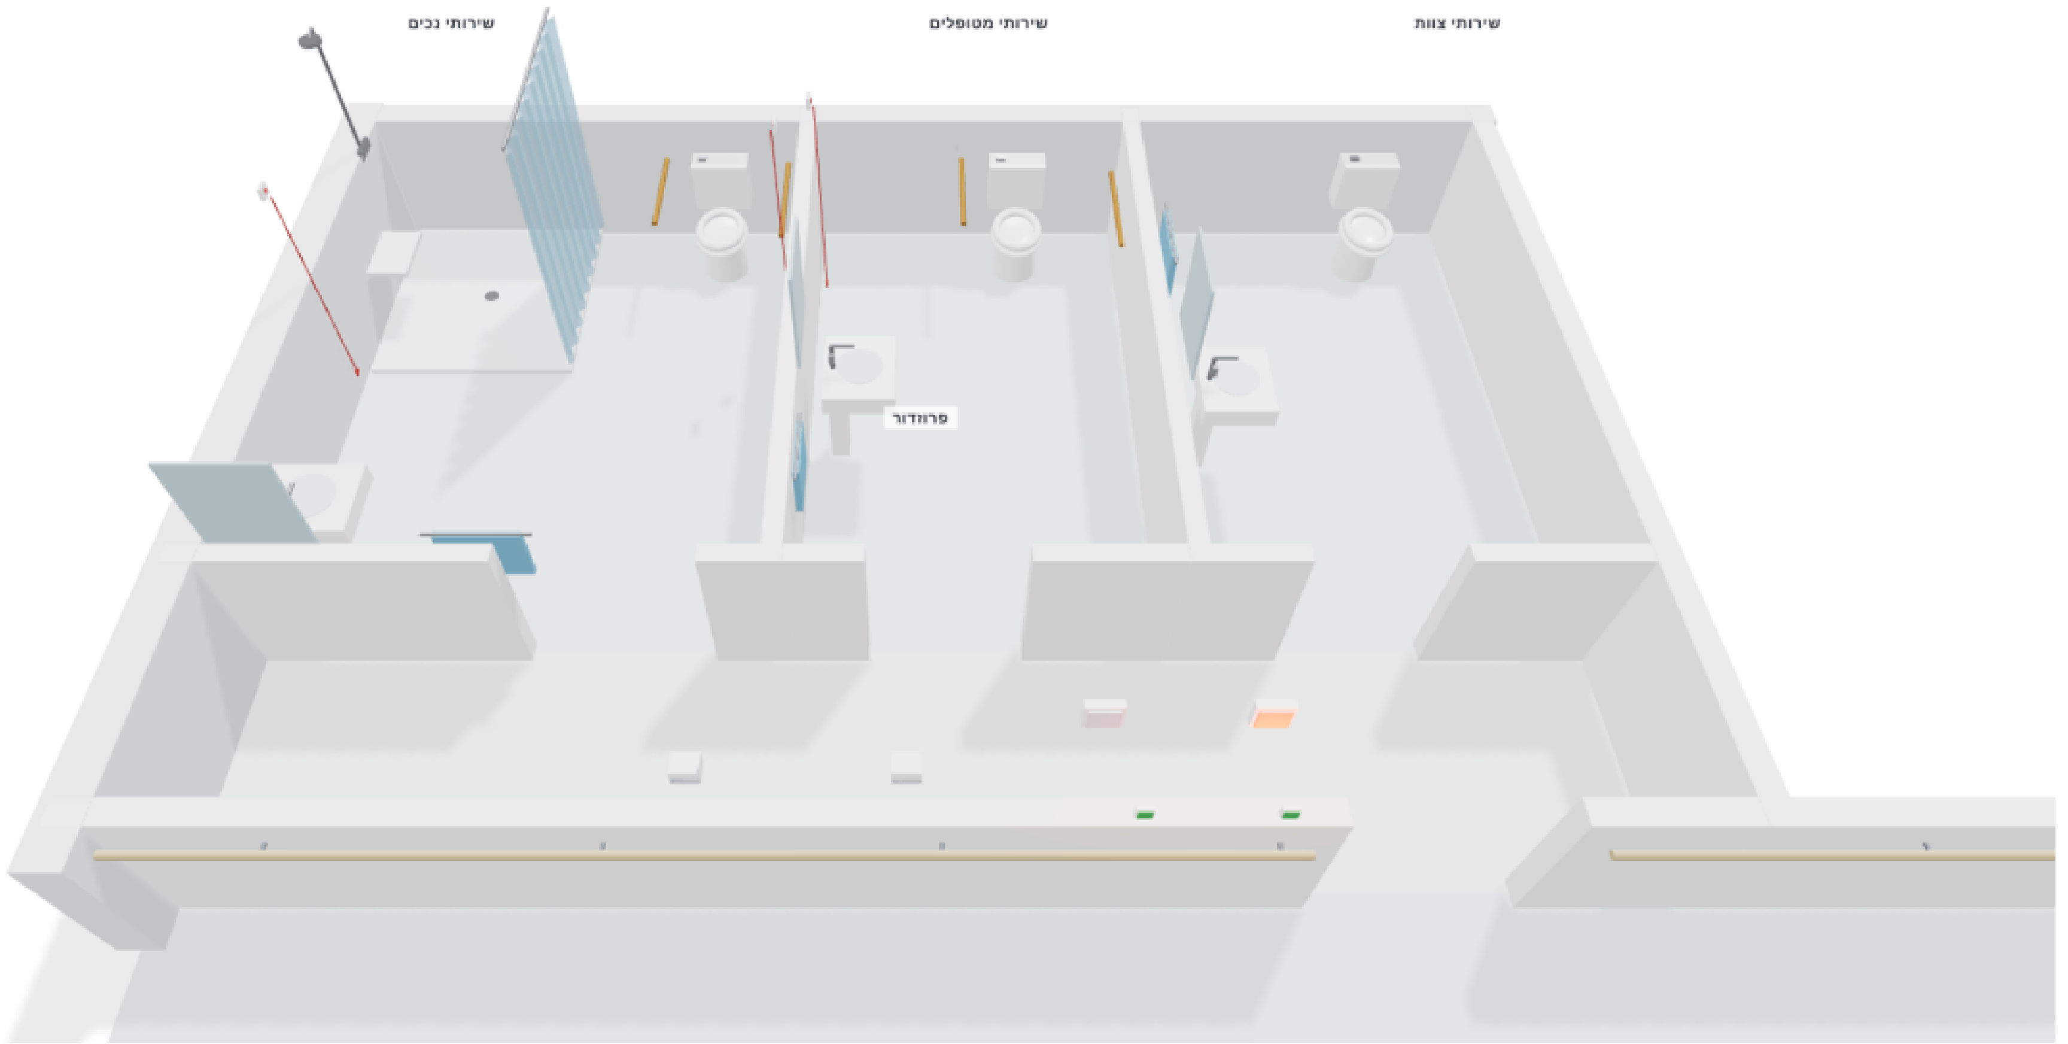

שירותי נכים
שירותי מטופלים
שירותי צוות
פרוזדור

D · גוש שירותים

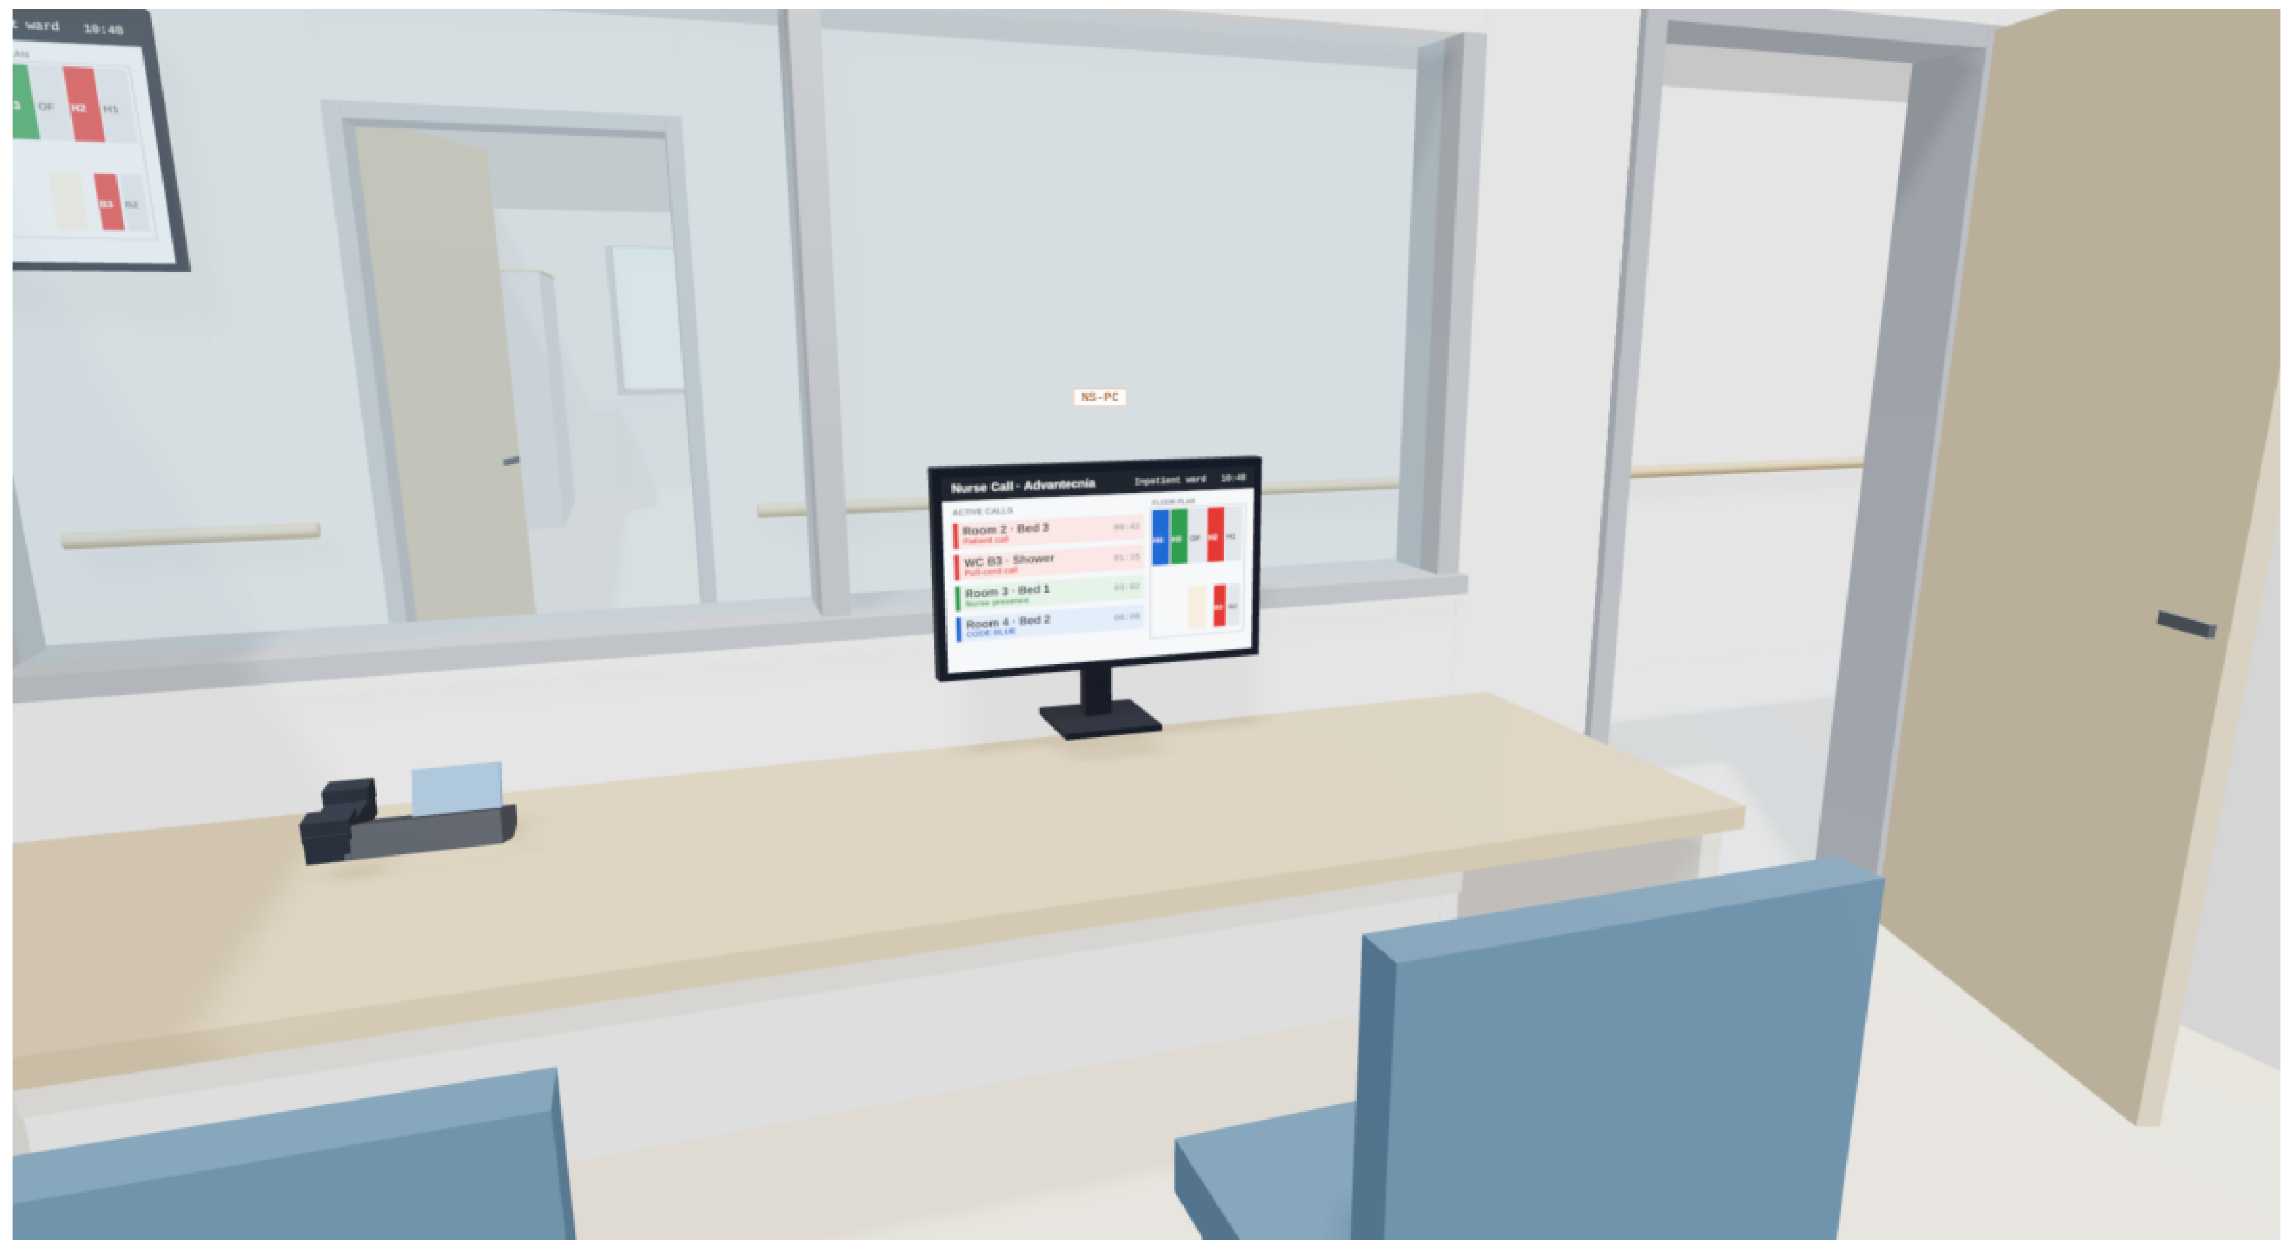

NS-PC
Nurse Call · Advantecnia
Inpatient ward
ACTIVE CALLS
Room 2 · Bed 3
Patient call
WC B3 · Shower
Pull-cord call
Room 3 · Bed 1
Nurse presence
Room 4 · Bed 2
CODE BLUE
FLOOR PLAN

E · עמדת אחיות – מחשב מגע Advantecnia

F · ארון תקשורת

מחלקת אשפוז · מערכת קריאת אחות

Nurse Call System · Inpatient Ward

מערכת: ACE BG · Advantecnia   הוכן ע"י: Telab International

מבטים תלת-ממדיים – ציוד

3D views – Equipment

מבטים תלת-ממדיים – ציוד

קנה מידה	תאריך	REV	גליון
S/E	**12/10/2026**	**A**	**06**

מידות במטרים

תכנון מוקדם – מהדורה A · פורמט A1

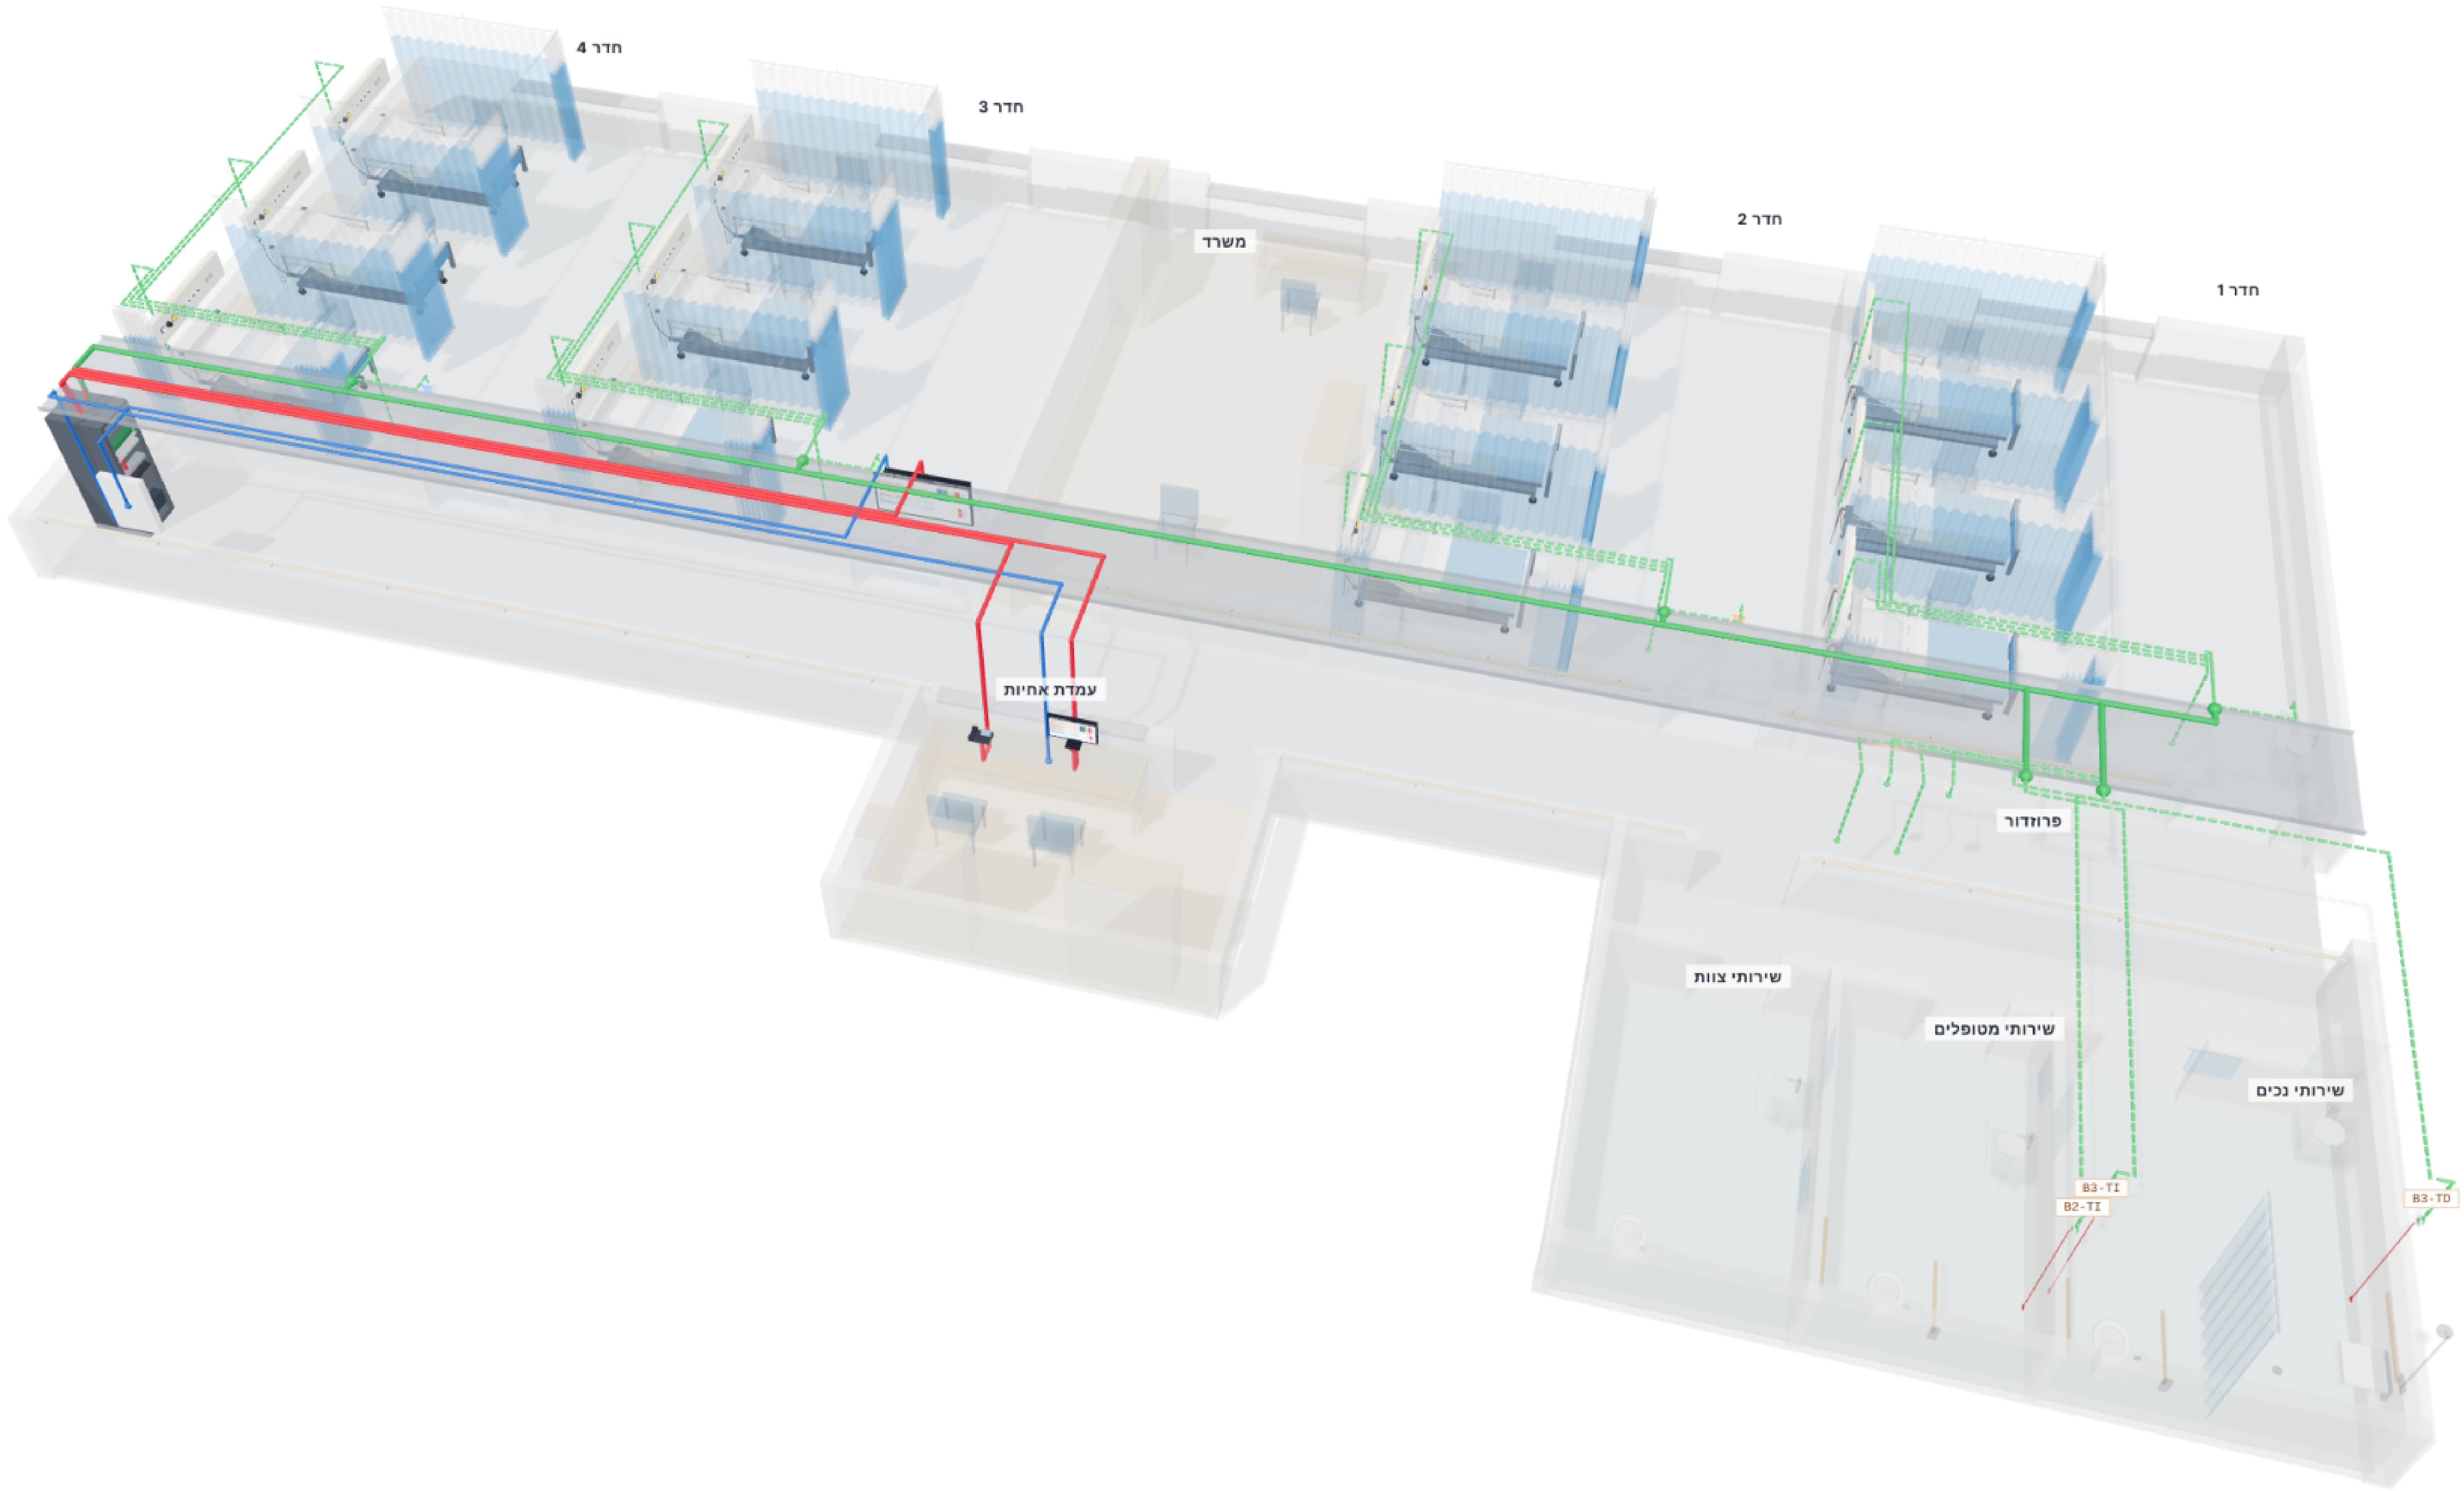
חדר 4
חדר 3
משרד
חדר 2
חדר 1
עמדת אחיות
פרוזדור
שירותי צוות
שירותי מטופלים
שירותי נכים
B3-TI
B2-TI
B3-TD

A · איזומטרי כללי – חיווט (קורי: BUS / UTP · אדום: רשת IP · כחול: 230V)

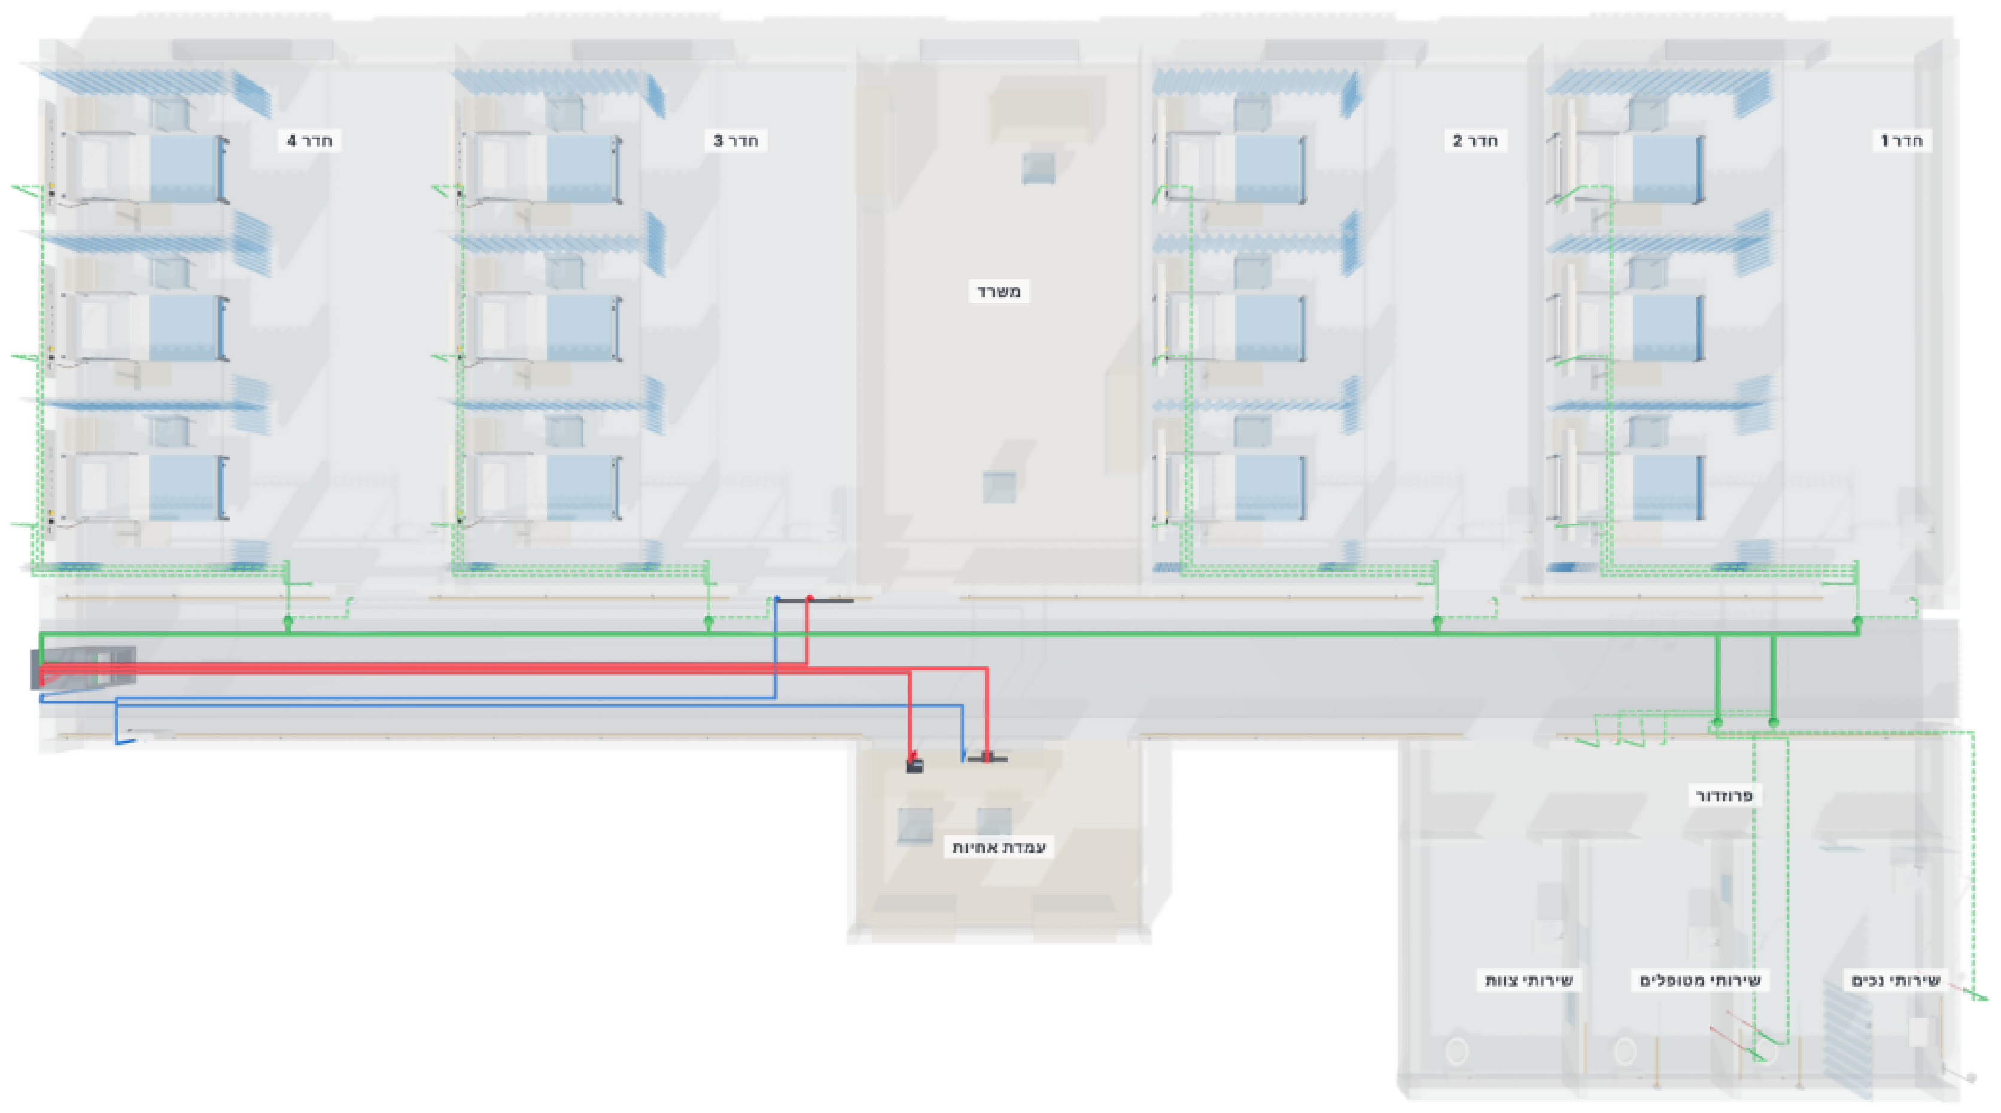
חדר 4
חדר 3
משרד
חדר 2
חדר 1
פרוזדור
עמדת אחיות
שירותי צוות
שירותי מטופלים
שירותי נכים

B · תינכות – טוויח

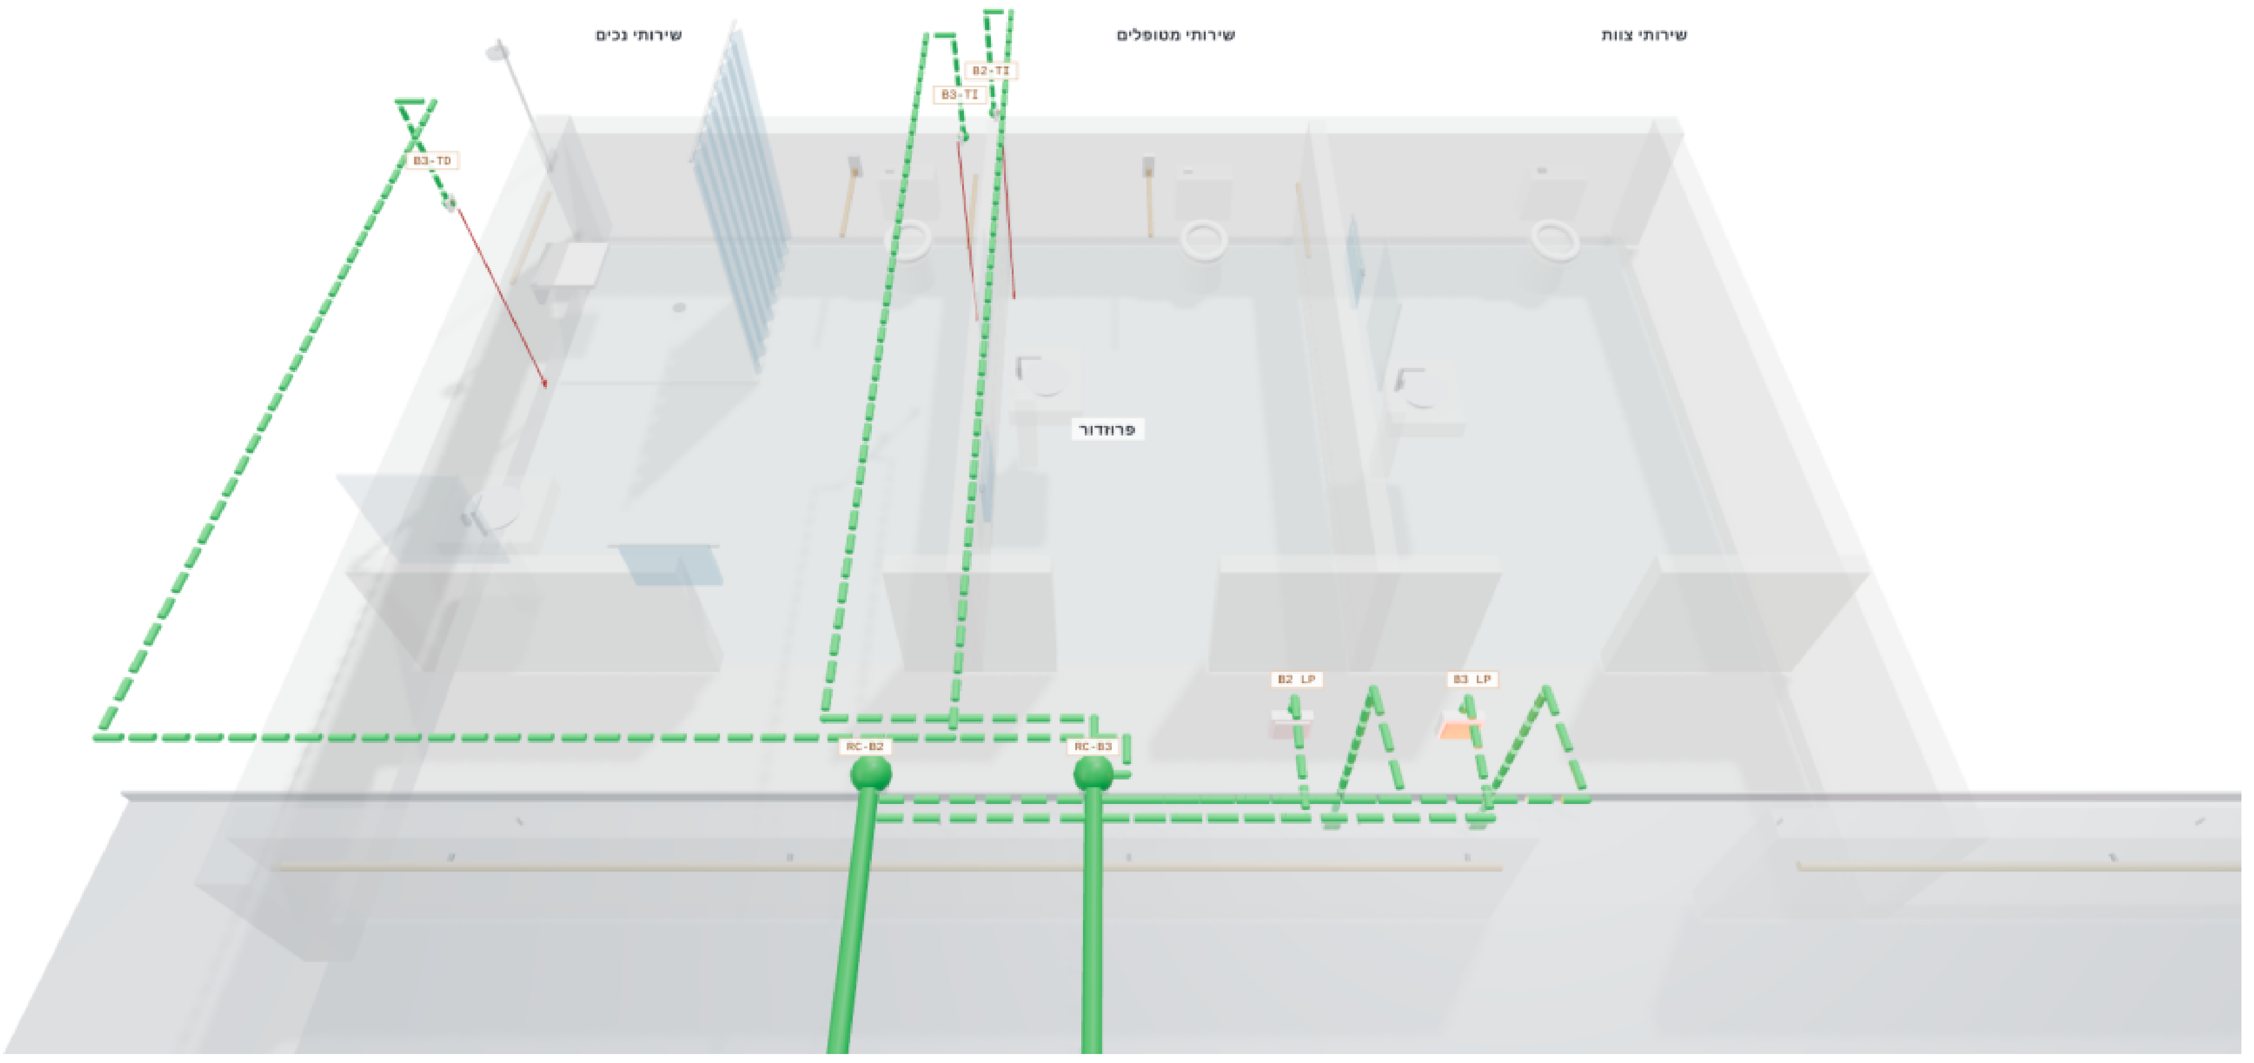
שירותי נכים
שירותי מטופלים
שירותי צוות
B2-TI
B3-TI
B3-TD
פרוזדור
B2 LP
B3 LP
RC-B2
RC-B3

C · םיתורש – םילבח, תורונמ תוחכונו רקבל

םיעבצ

🟩 לבכ 2x2x0.8 BUS KNX – סיטרכ ← םיניפ 24 סיטרכ (תרשרש) ← SmartHub
KNX bus – board-to-board chain · BUS – םיסיטרכ רושרש

▬ ▬ ולש םיניפה 24 סיטרכל ןקתה לכ – רדח לכב ילאידר
Radial in each room – device to its 24-pin board · סיטרכל ןקתה – רדח לכב ילאידר

🟥 Cat6 / Cat7 דבלב: SmartHub ← גתמ ← תרש · בשחמ / ןופלט · TV
Cat6/Cat7 only: SmartHub, switch, server, PC/phone, TV · Cat6/Cat7 דבלב: SmartHub, גתמ, תרש, בשחמ, TV

🟦 למשח V230 ולו ןופלט/בשחמל ,ןוראל – TV-230 דבלב (PoE ראשה)
230 V only to rack, PC/phone, TV – rest is PoE · 230V ןוראל, בשחמ/ןופלט ו-TV דבלב – ראשה PoE

תוחא תאירק תכרעמ · זופשא תקלחמ

Nurse Call System · Inpatient Ward

Telab International :ןכוה ע"י   ACE BG · Advantecnia :תכרעמ

םיטבמ תלת-םיידממ – טוויח

3D views – Wiring

םיטבמ תלת-םיידממ – טוויח

הדימ הנק
S/E

ךיראת
12/10/2026

REV
A

ןויליג
07

םירטמב תודימ

טמרופ A1 · הרודהמ A – תכנון םדקומ