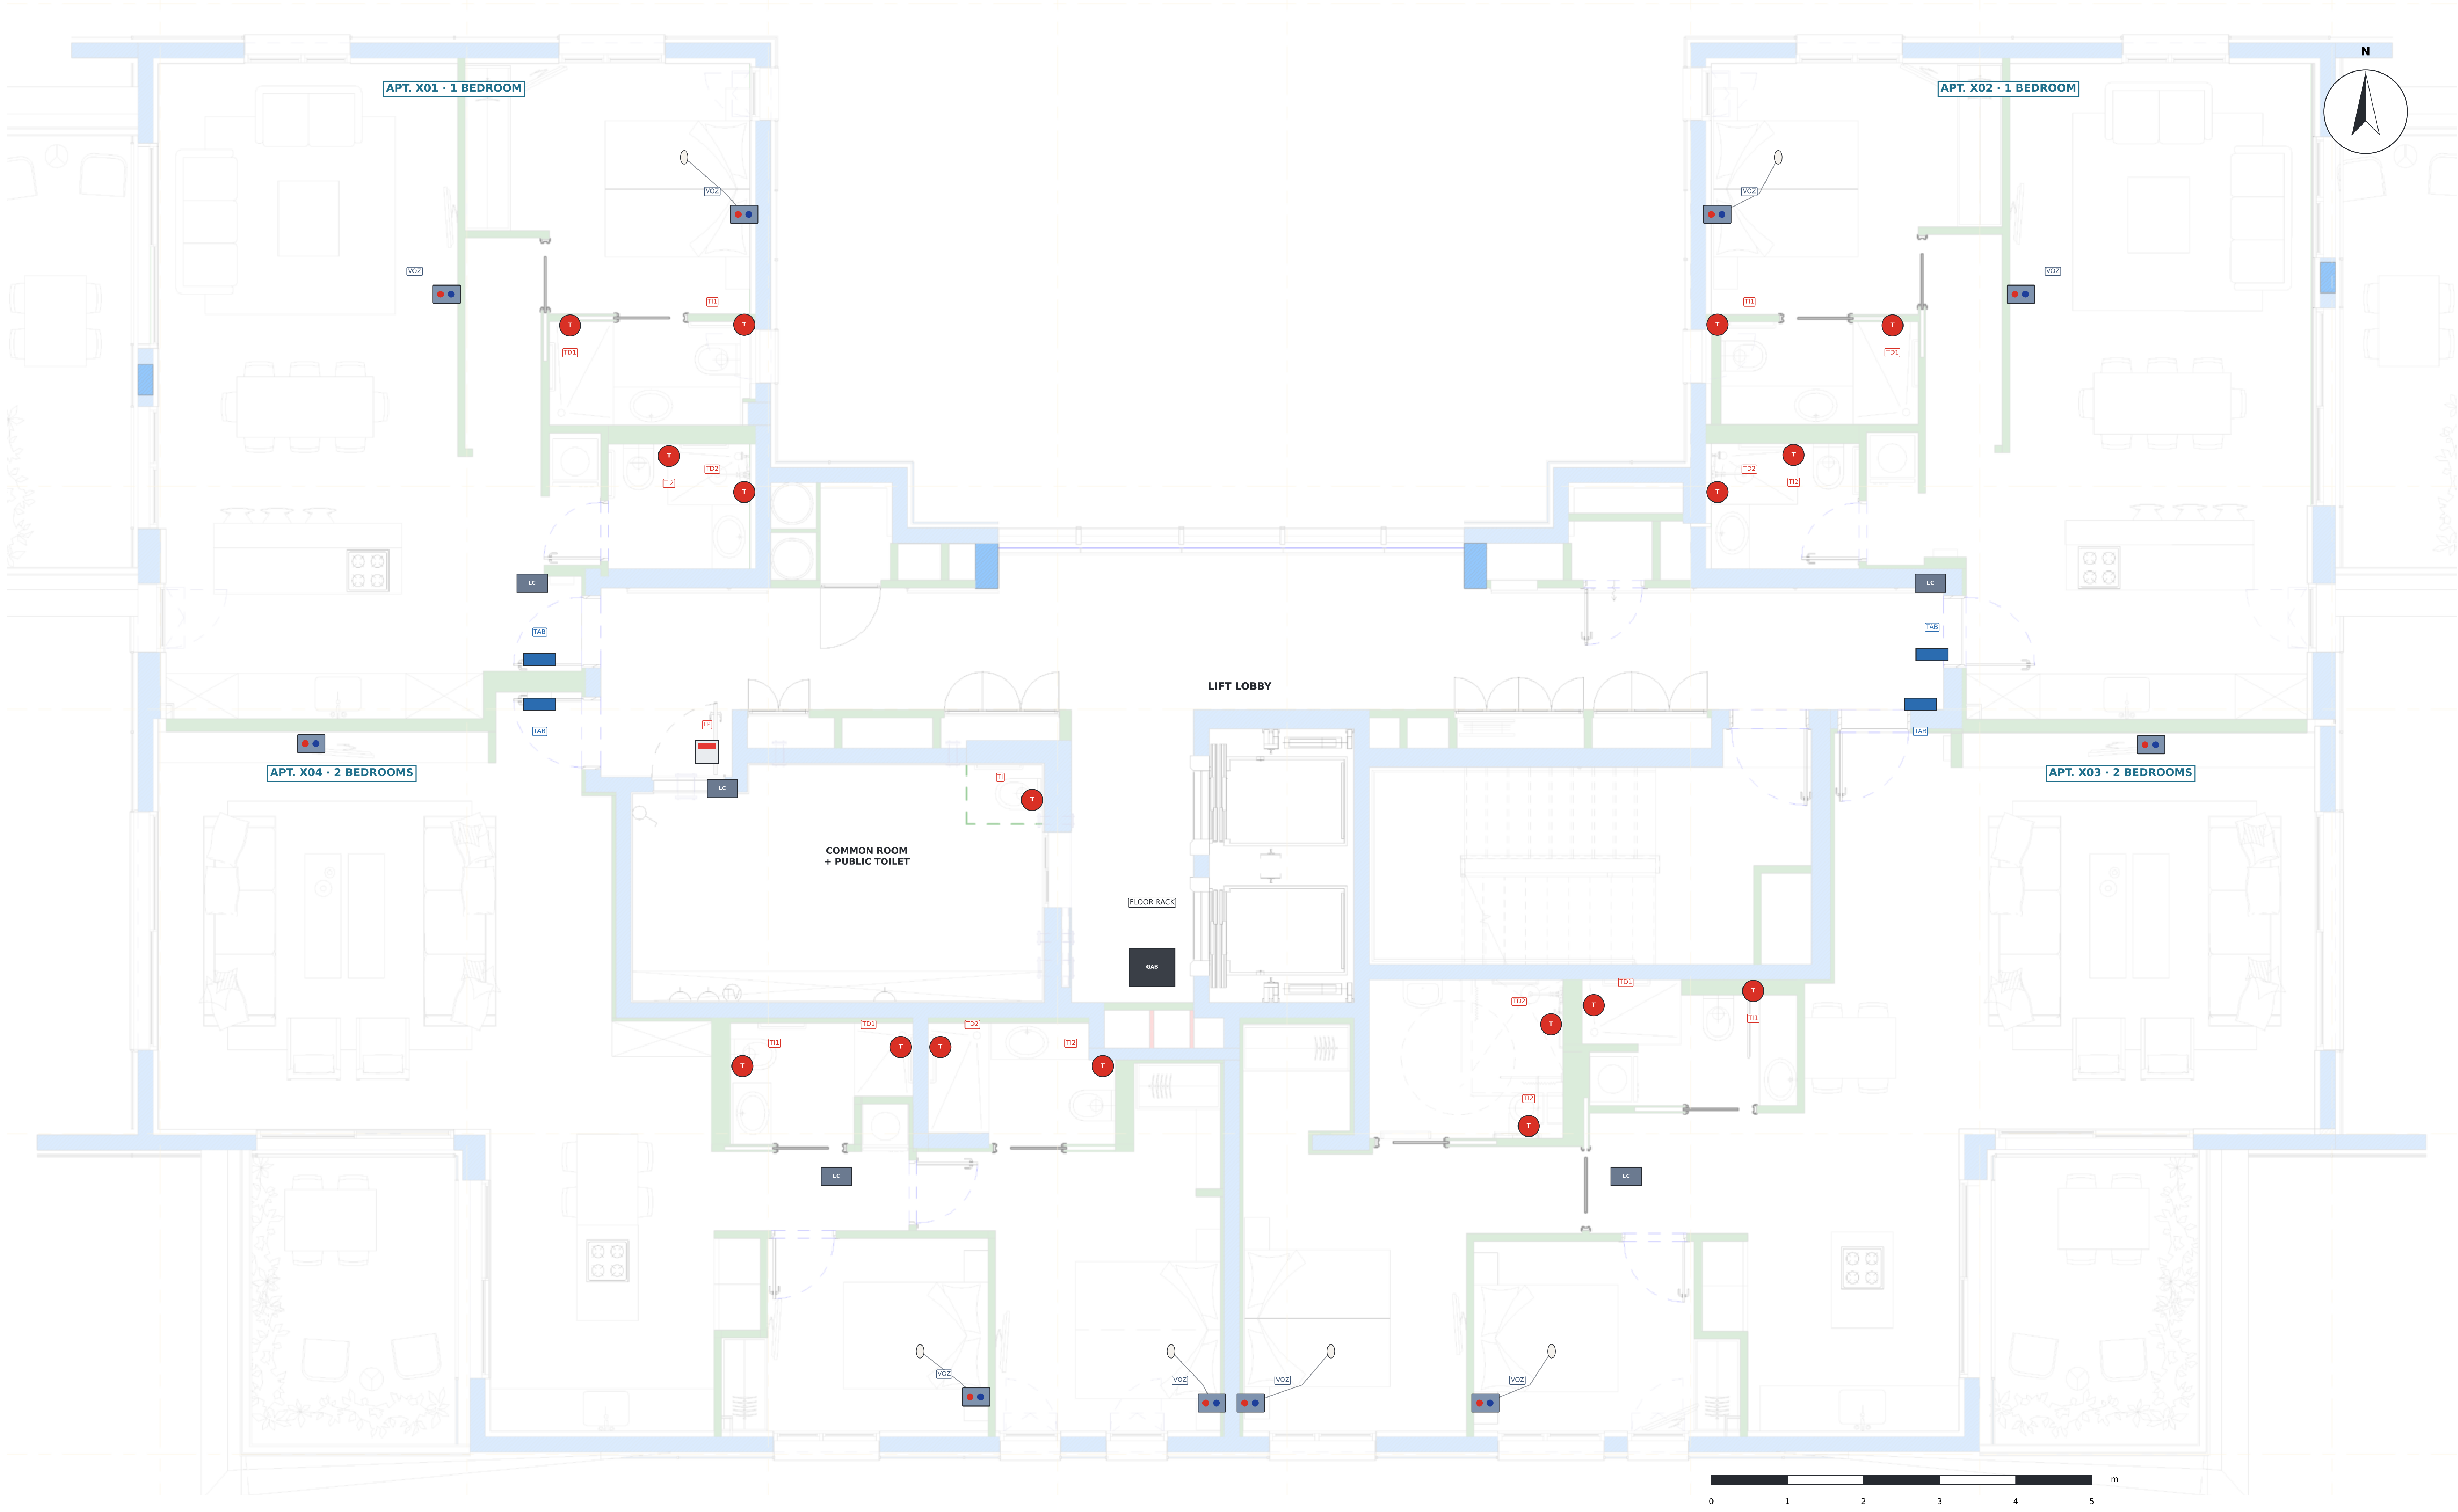

## DEVICES · EQUIPOS · ציוד

| | |
|---|---|
| ▬ | TAB · Door tablet (iPad / Android) – call and voice, h 1.40 m<br>Door tablet – call and voice · טאבלט בכניסה – קריאה ודיבור |
| ● ● | VOZ · Voice panel with buttons ACE82182451 – living room and bedrooms, h 1.20–1.30 m<br>Voice panel with buttons – living room and bedrooms · פנל קולי עם לחצנים – סלון וחדרי שינה |
| ○ | Call pear next to the bed (bedrooms)<br>Call pear next to the bed (bedrooms) · אגס קריאה ליד המיטה |
| T | TI / TD · Pull-cord ACE40320303W – toilet and shower, h 1.85 m<br>Pull-cord – toilet and shower, h 1.85 m · משיכת חבל – אסלה ומקלחת, גובה 1.85 מ' |
| 🟥 | LP · Corridor light ACE41020309 – above each public toilet door<br>Corridor light – above each public toilet door · מנורת מסדרון – מעל דלת כל שירותים ציבוריים |
| LC | LC · LCom ACE71610003 – apartment hub (ceiling)<br>LCom – apartment hub (ceiling) · LCom – מרכז הדירה (תקרה) |
| GAB | 12U floor rack: 2 Buscomm ACE70810000 + PoE switch ACEUCM6302<br>Floor rack: 2 Buscomm + PoE switch · ארון קומה: 2 Buscomm + מתג PoE |

## QUANTITIES PER FLOOR × 8 FLOORS

| Code | Device | Per floor | 8 floors |
|---|---|---|---|
| TAB | Door tablet | 4 | 32 |
| VOZ | Voice panel with buttons | 10 | 80 |
| TI/TD | Pull-cord (toilet + shower) | 17 | 136 |
| LP | Corridor light (public toilet) | 1 | 8 |
| LC | LCom | 5 | 40 |
| BC | Buscomm | 2 | 16 |
| SW | PoE switch | 1 | 8 |

## NOTES · NOTAS

1. Base: architectural plan L5 (typical floor) – all 8 floors are identical: 4 apartments per floor, 32 in total.
2. Apartments x01 and x02: 1 bedroom, living room with kitchen and 2 bathrooms. Apartments x03 and x04: 2 bedrooms and 2 bathrooms.
3. Tablet at the door of each apartment (iPad / Android) to call and talk to the nurse.
4. Voice panel with buttons (ACE82182451) in the living room and in each bedroom; in bedrooms, with a pear next to the bed.
5. Pull-cords (ACE40320303W) at the toilet and shower of every bathroom, at 1.85 m.
6. One public toilet per floor in the common room: pull-cord + corridor light above the door. With the 2 on GF, 10 public toilets in total.
7. Floor rack in the service corridor next to the lifts (Tripp Lite 12U, as in the IT plan).
8. Preliminary locations: confirm on site with the installer and Advantecnia.

## MOUNTING HEIGHTS

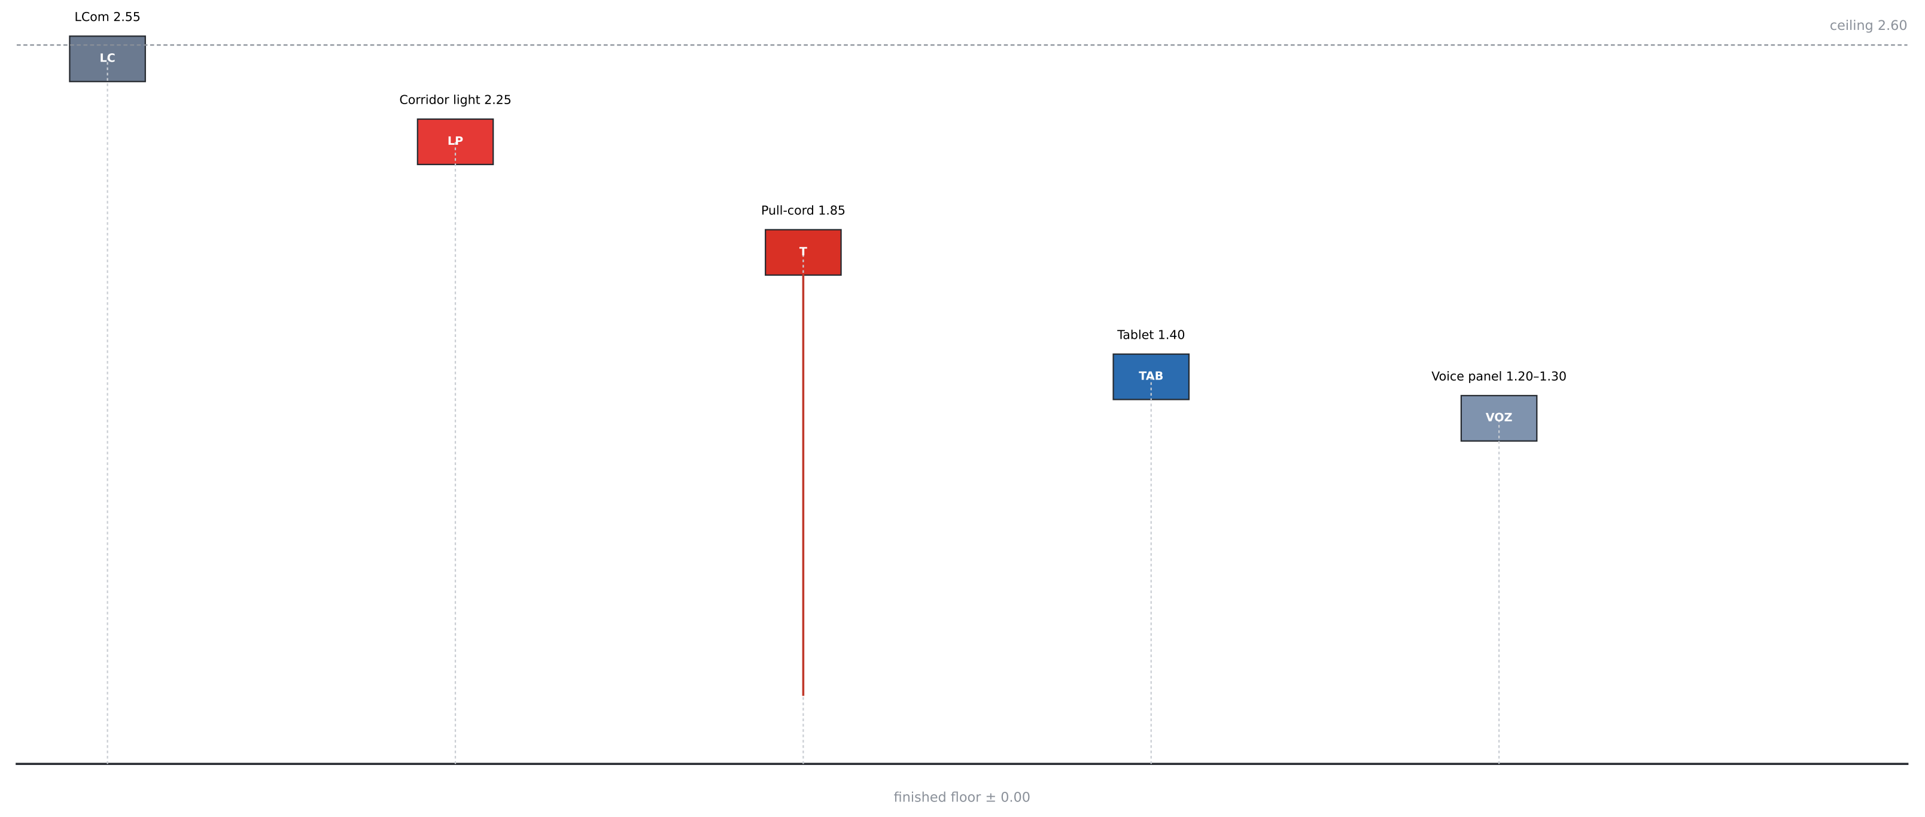

**MIGDALEI YAM A TIJON · ASSISTED LIVING**

Nurse call – GF + 8 floors · 32 apartments

System: ACE BG · Advantecnia  Prepared by: Telab International

# TYPICAL FLOOR F1–F8 · NURSE CALL

| SCALE · ESCALA | DATE · FECHA | REV | SHEET |
|---|---|---|---|
| 1:60 | 15/10/2026 | B | 01 |

Base: architect's plan L5 (Massad Oz / Triplet) · dimensions in m

A1 format · Rev. B – on the real plan

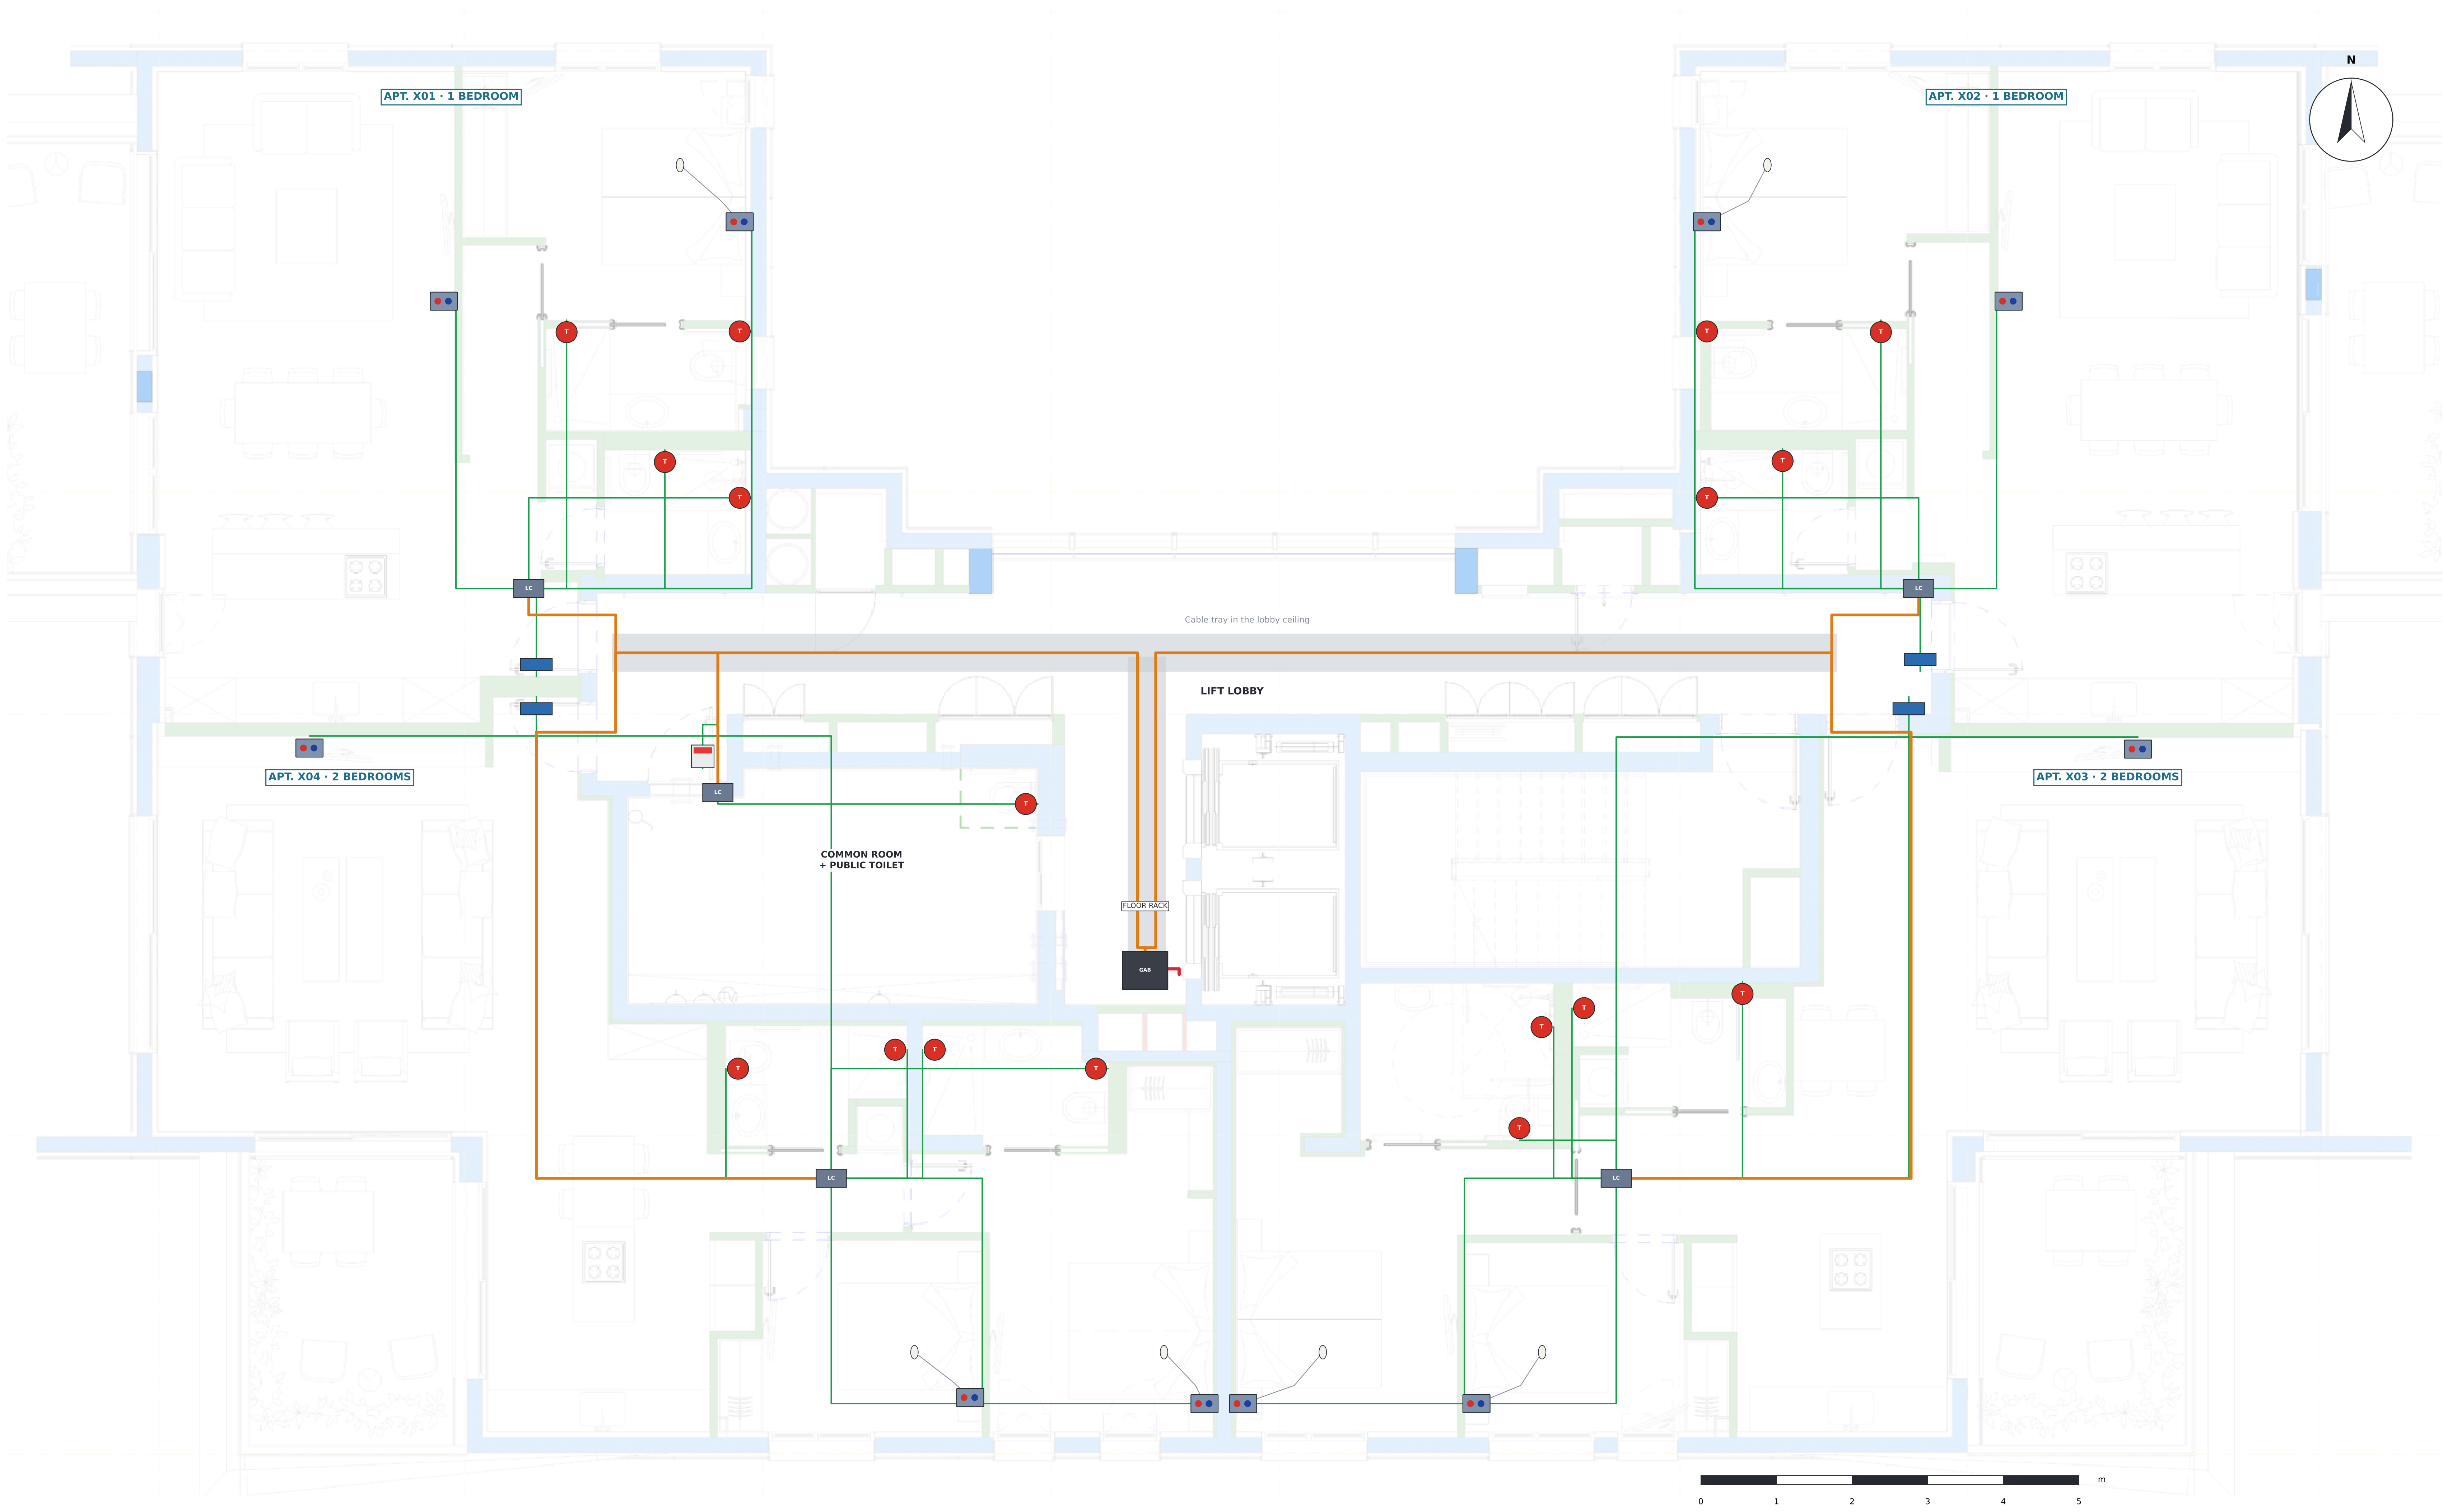

## NOTES · NOTAS

1. Base: architectural plan L5 (typical floor) – all 8 floors are identical: 4 apartments per floor, 32 in total.
2. Apartments x01 and x02: 1 bedroom, living room with kitchen and 2 bathrooms. Apartments x03 and x04: 2 bedrooms and 2 bathrooms.
3. Tablet at the door of each apartment (iPad / Android) to call and talk to the nurse.
4. Voice panel with buttons (ACE82182451) in the living room and in each bedroom; in bedrooms, with a pear next to the bed.
5. Pull-cords (ACE40320303W) at the toilet and shower of every bathroom, at 1.85 m.
6. One public toilet per floor in the common room: pull-cord + corridor light above the door. With the 2 on GF, 10 public toilets in total.
7. Floor rack in the service corridor next to the lifts (Tripp Lite 12U, as in the IT plan).
8. Preliminary locations: confirm on site with the installer and Advantecnia.

## WIRING · CABLEADO · חיווט

🟩 Cat6 radial: each device → its apartment LCom
Cat6 radial: each device → apartment LCom · Cat6 רדיאלי: כל התקן ← LCom של הדירה

🟧 Cat6 / Cat7 chain: LCom → LCom → rack Buscomm
Cat6 / Cat7 chain: LCom → LCom → Buscomm · Cat6 / Cat7 שרשרת: LCom ← LCom ← Buscomm

🟥 Cat6A / Cat7 network: Buscomm → switch → riser → GF server
Cat6A / Cat7 network: Buscomm → switch → riser → GF server · Cat6A / Cat7 רשת: Buscomm ← מתג ← עמוד ← שרת

## TYPICAL FLOOR LENGTHS (no spare)

| | | |
|---|---|---|
| 🟩 | Cat6 radial inside the apartments | **202 m** |
| 🟧 | Cat6 / Cat7 chain LCom → Buscomm | **82 m** |
| 🟥 | Cat6A / Cat7 rack and riser | **4 m** |

## NOTES · NOTAS

1. Each device runs radially (Cat6) to its apartment LCom, in the hall ceiling.

2. The LComs are chained along the lobby tray to the floor rack:
x01 → x04 → common room → Buscomm 1 · x02 → x03 → Buscomm 2.

3. The floor PoE switch runs up the Cat6A / Cat7 riser to
the GF server.

4. Everything is PoE: no 230 V needed for the apartment devices.

**MIGDALEI YAM A TIJON · ASSISTED LIVING**

Nurse call – GF + 8 floors · 32 apartments

System: ACE BG · Advantecnia Prepared by: Telab International

# TYPICAL FLOOR F1–F8 · WIRING

| SCALE · ESCALA | DATE · FECHA | REV | SHEET |
|---|---|---|---|
| **1:60** | **15/10/2026** | **B** | **02** |

Base: architect's plan L5 (Massad Oz / Triplet) · dimensions in m

A1 format · Rev. B – on the real plan

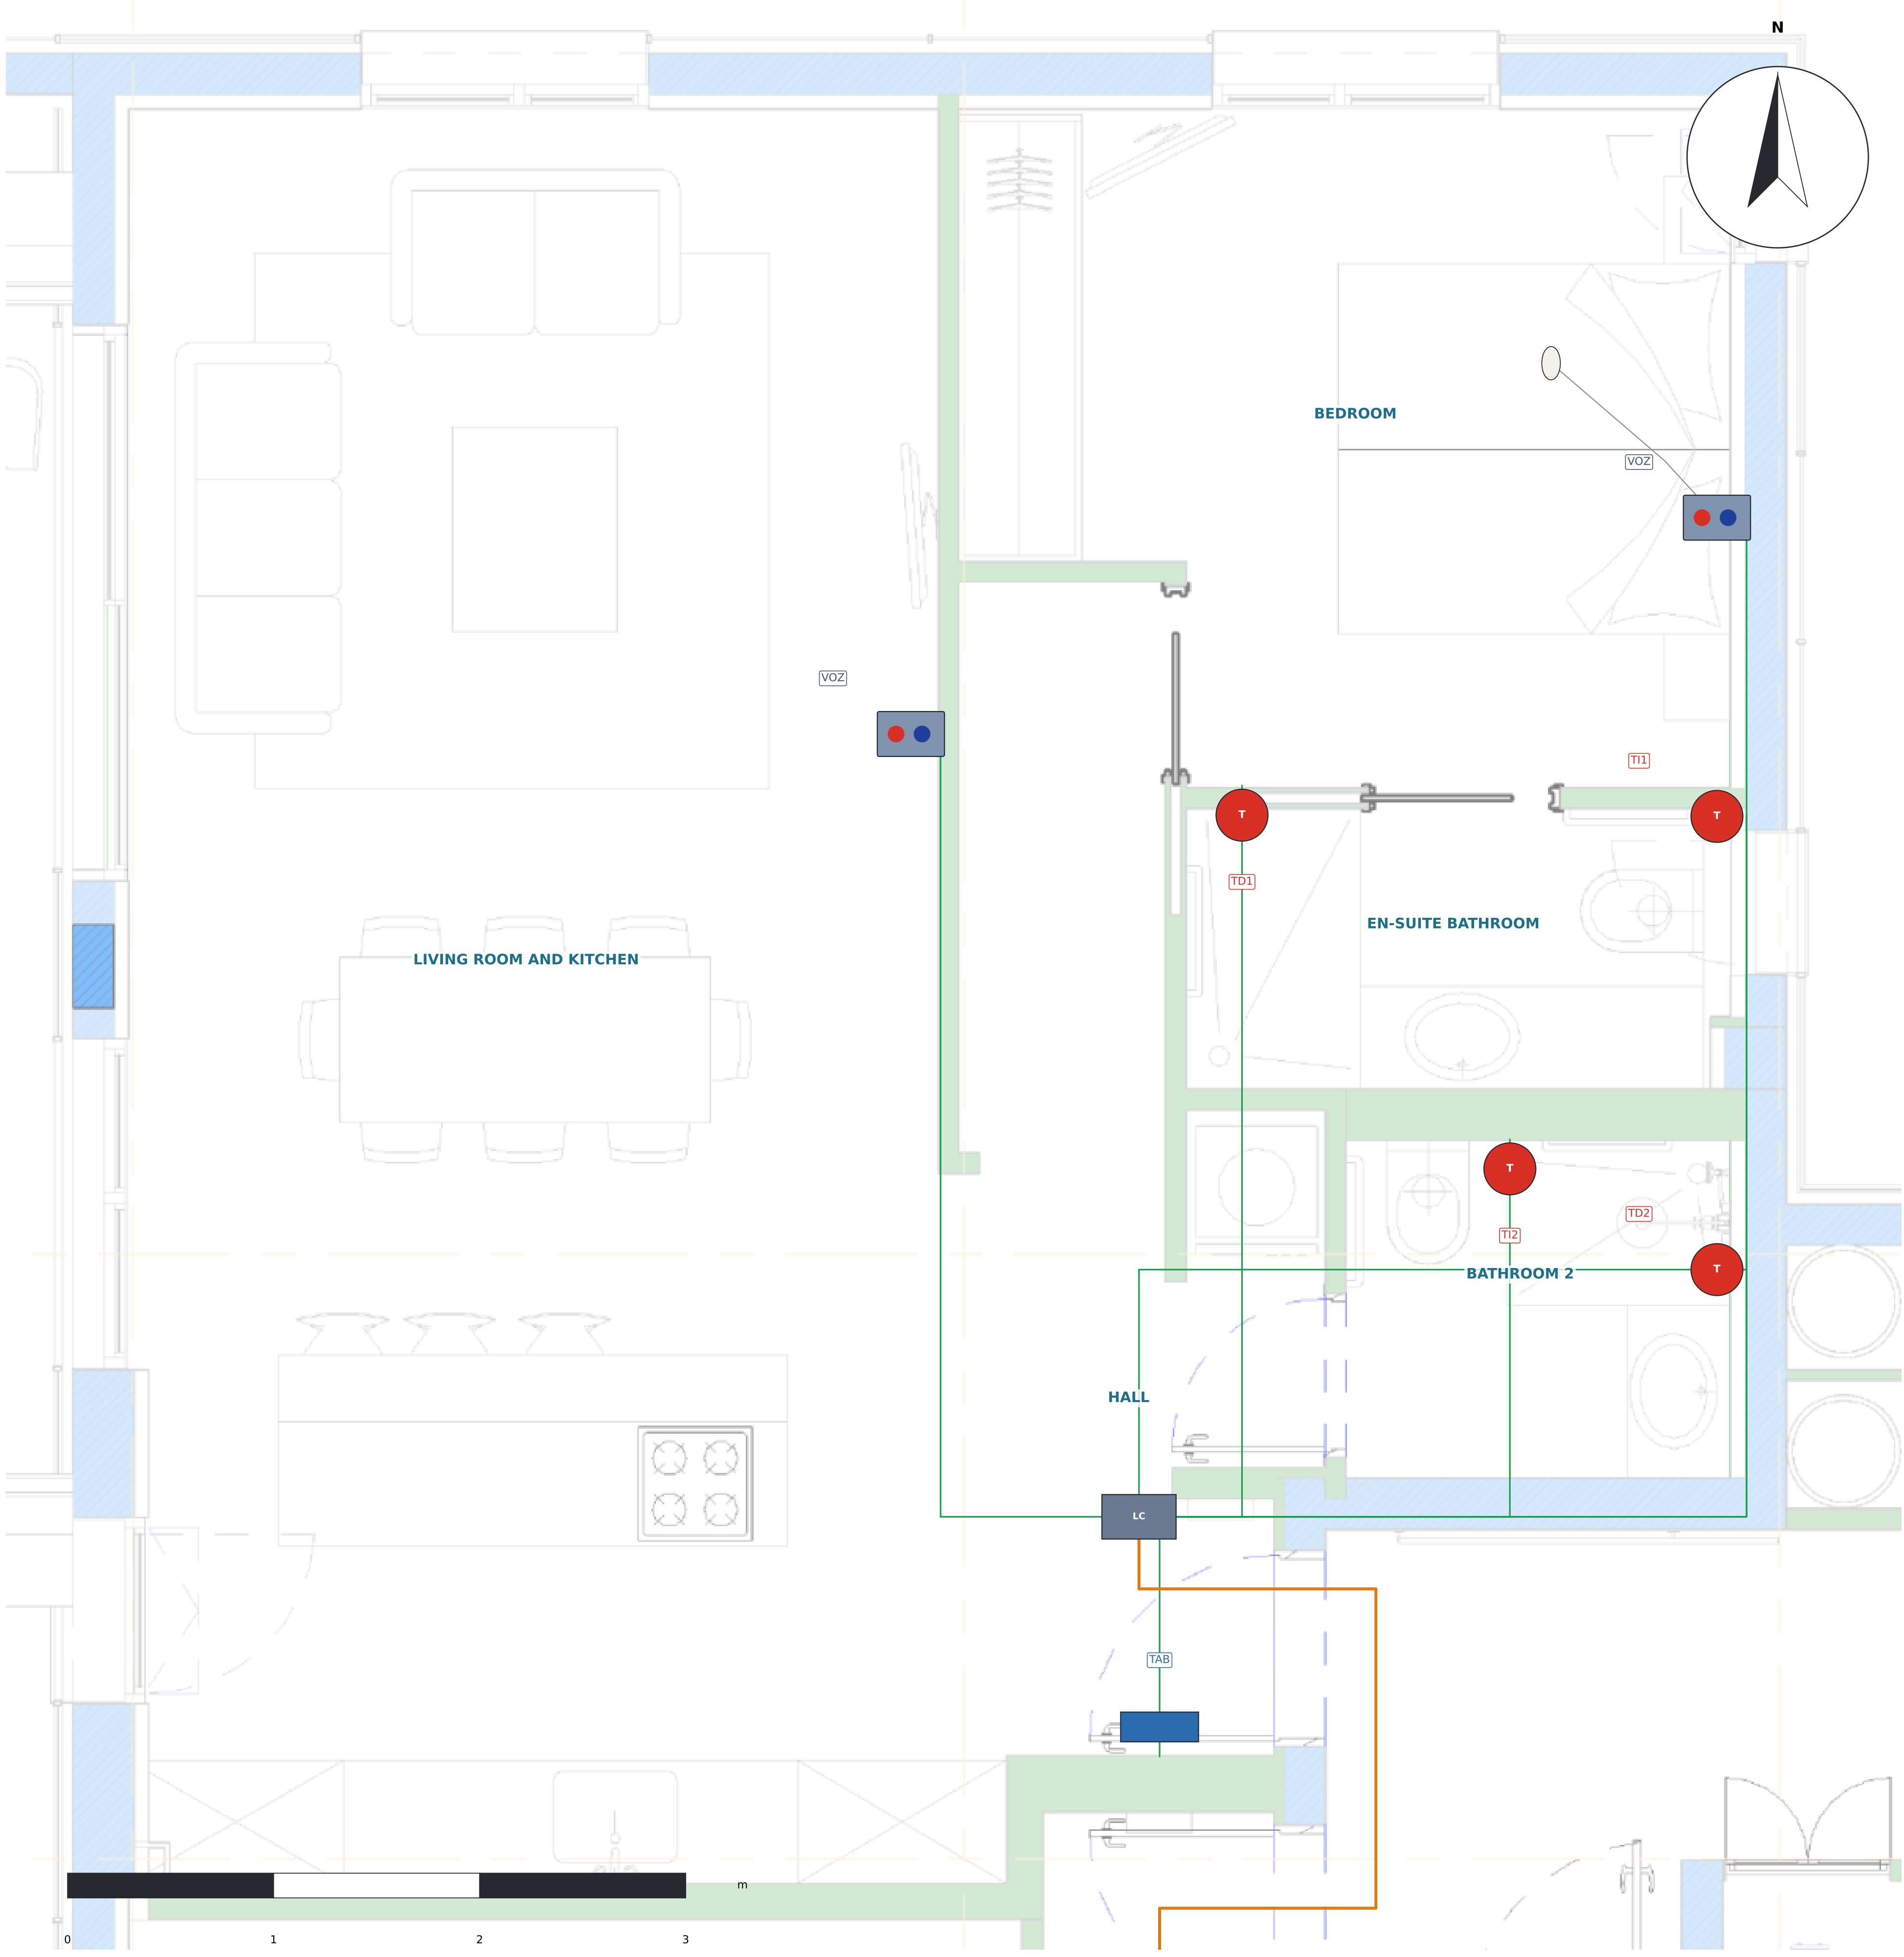

## APARTMENT DEVICES

| ID | Device | Room | Height |
|---|---|---|---|
| TAB | Door tablet | Hall | 1,40 m |
| VOZ-S | Voice panel with buttons | Living room and kitchen | 1,30 m |
| VOZ-D | Voice panel with buttons + pear | Bedroom | 1,20 m |
| TI1 | Pull-cord | En-suite bathroom | 1,85 m |
| TD1 | Pull-cord | En-suite bathroom | 1,85 m |
| TI2 | Pull-cord | Bathroom 2 | 1,85 m |
| TD2 | Pull-cord | Bathroom 2 | 1,85 m |
| LCOM | LCom ACE71610003 | Hall | 2,55 m |

## SYMBOLS · SÍMBOLOS · סמלים

| | |
|---|---|
| 🟦 | TAB · Door tablet (iPad / Android) – call and voice, h 1.40 m<br>Door tablet – call and voice · טאבלט בכניסה – קריאה ודיבור |
| ●● | VOZ · Voice panel with buttons ACE82182451 – living room and bedrooms, h 1.20–1.30 m<br>Voice panel with buttons – living room and bedrooms · פנל קולי עם לחצנים – סלון וחדרי שינה |
| ⬭ | Call pear next to the bed (bedrooms)<br>Call pear next to the bed (bedrooms) · אגס קריאה ליד המיטה |
| T | TI / TD · Pull-cord ACE40320303W – toilet and shower, h 1.85 m<br>Pull-cord – toilet and shower, h 1.85 m · משיכת חבל – אסלה ומקלחת, גובה 1.85 מ' |
| 🟥 | LP · Corridor light ACE41020309 – above each public toilet door<br>Corridor light – above each public toilet door · מנורת מסדרון – מעל כל דלת שירותים ציבוריים |
| LC | LC · LCom ACE71610003 – apartment hub (ceiling)<br>LCom – apartment hub (ceiling) · LCom – מרכז הדירה (תקרה) |

## NOTES · NOTAS

1. Apartment x02 mirrors x01 (same devices).
2. Tablet in the hall next to the front door.
3. Voice panel in the living room and in the bedroom (with pear next to the bed).
4. 2 bathrooms: pull-cord at the toilet and at the shower of each (4 pull-cords).
5. Everything runs radially in Cat6 to the hall LCom.

**MIGDALEI YAM A TIJON · ASSISTED LIVING**
Nurse call – GF + 8 floors · 32 apartments
System: ACE BG · Advantecnia Prepared by: Telab International

# 1-BEDROOM APT. (x01 / x02)

| SCALE · ESCALA | DATE · FECHA | REV | SHEET |
|---|---|---|---|
| **1:30** | **15/10/2026** | **B** | **03** |

Base: architect's plan L5 (Massad Oz / Triplet) · dimensions in m
A1 format · Rev. B – on the real plan

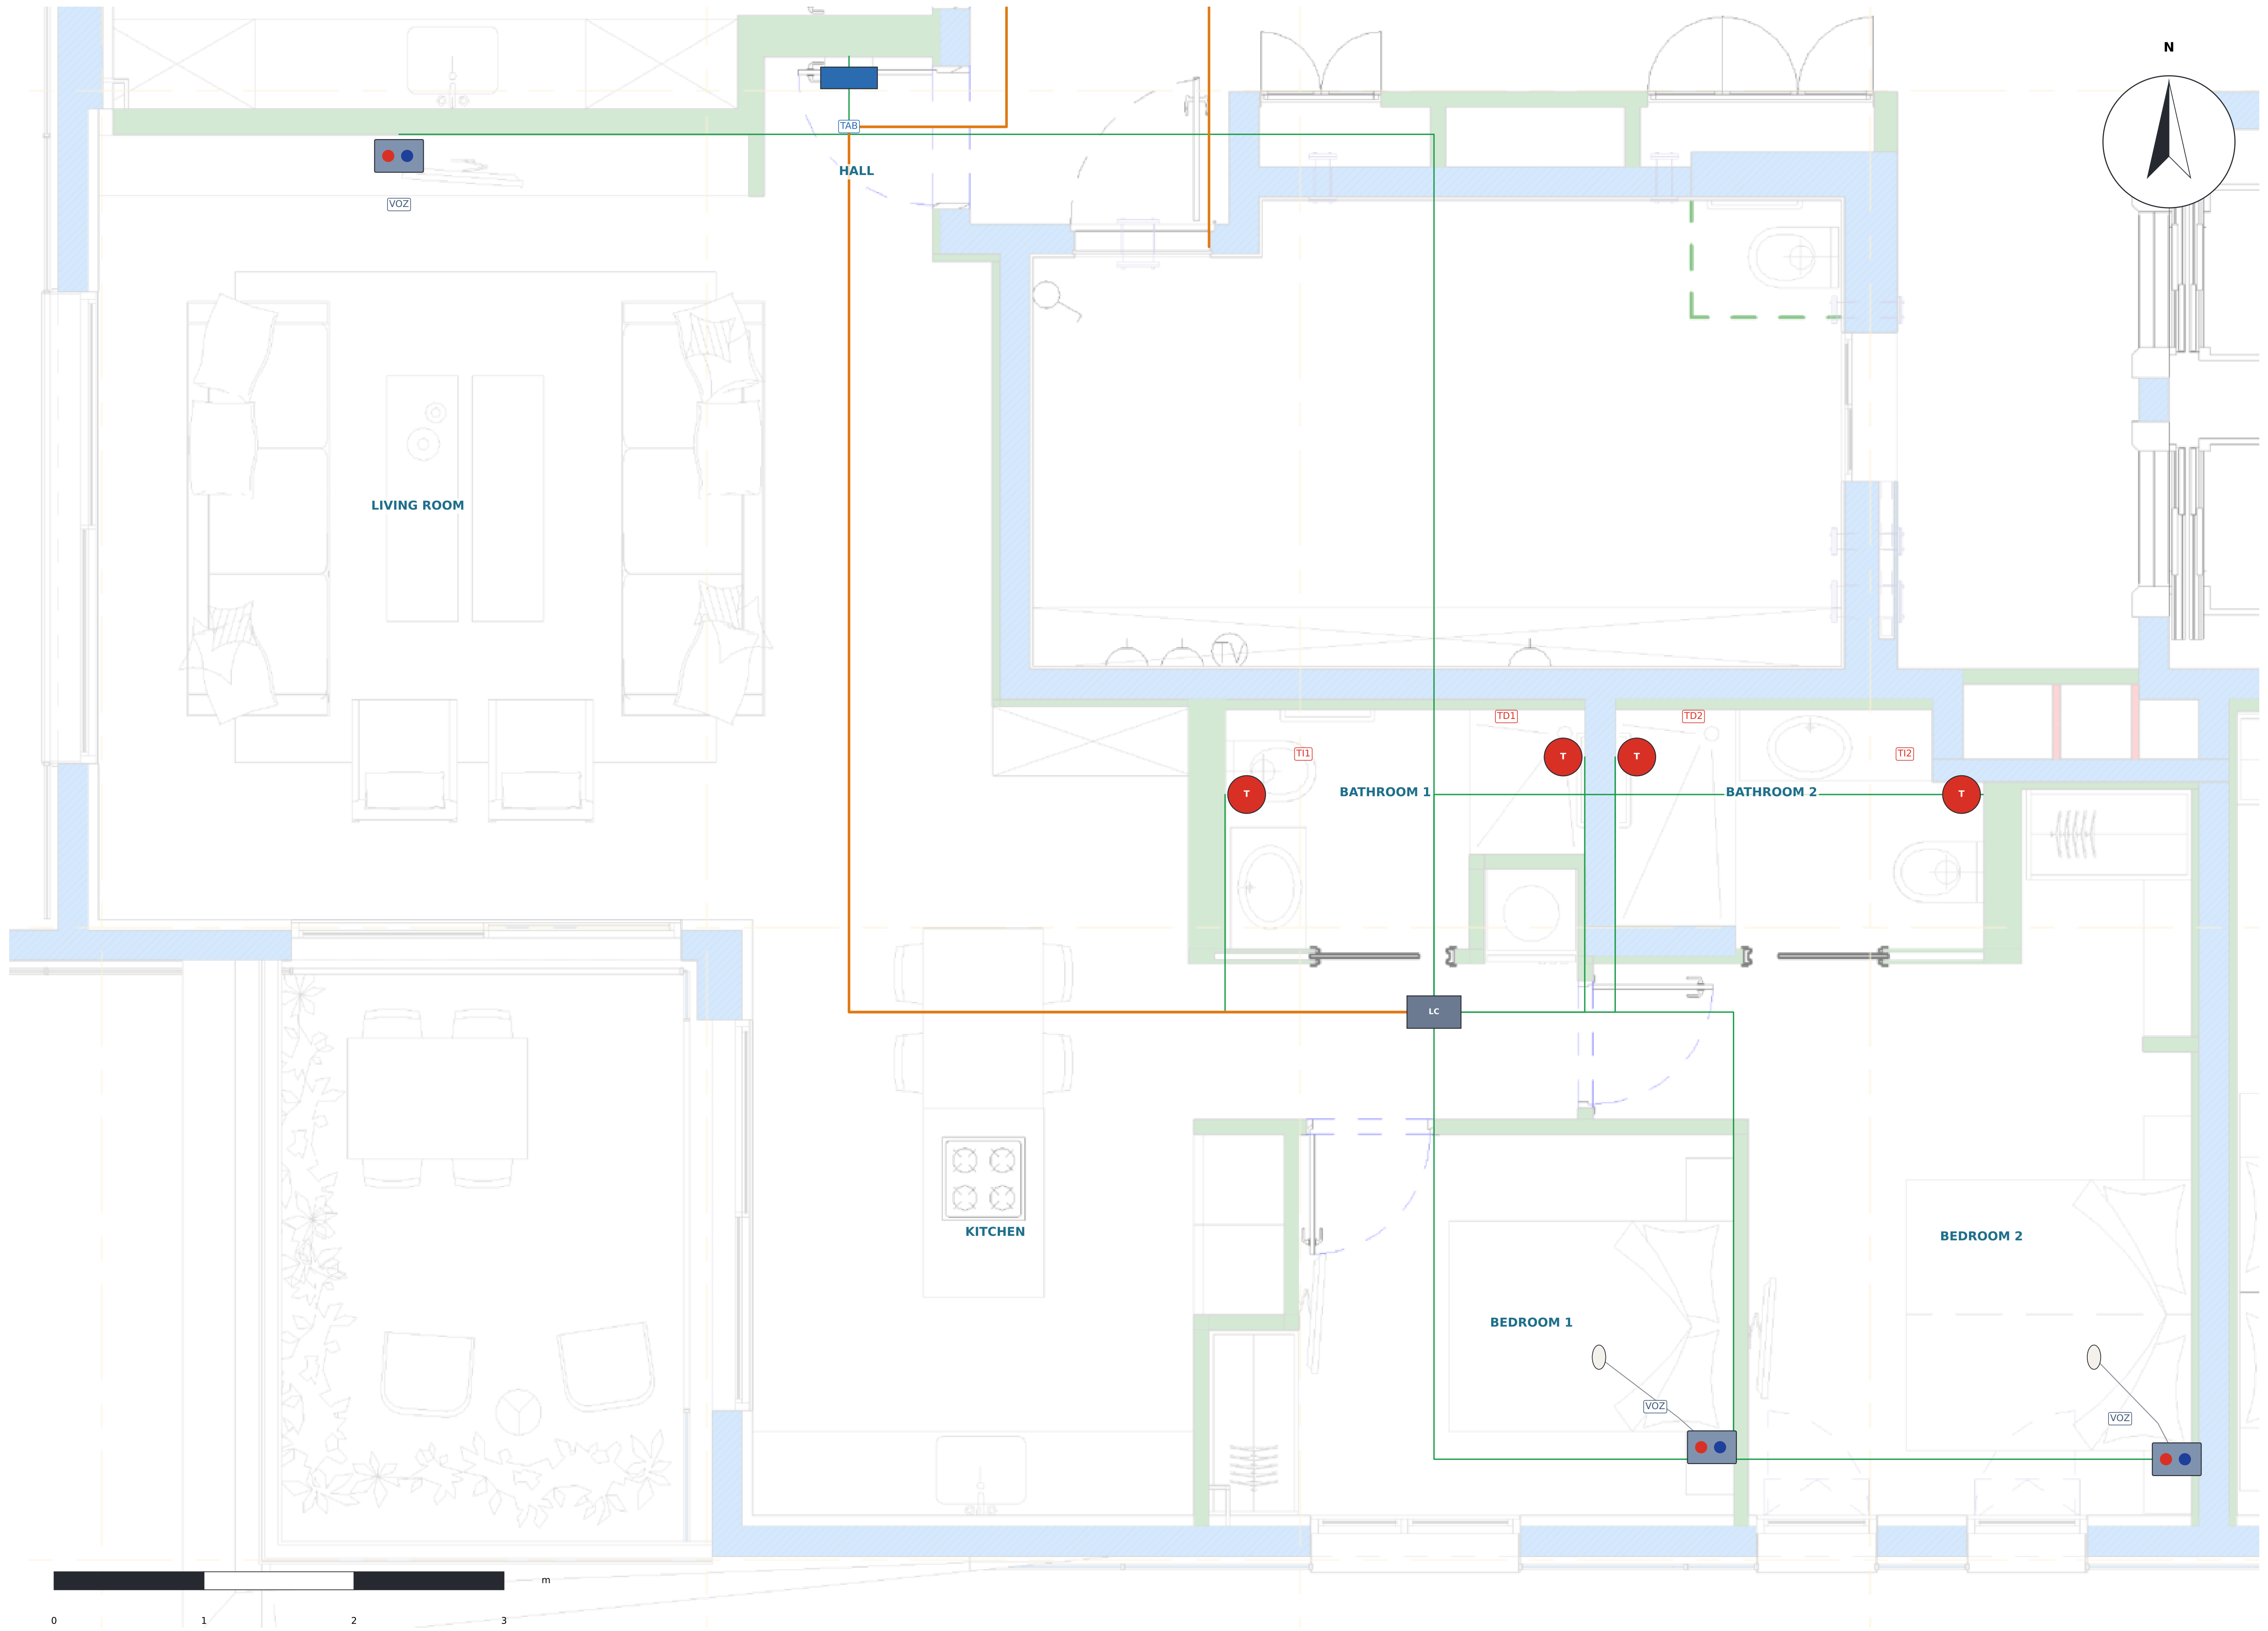

## APARTMENT DEVICES

| ID | Device | Room | Height |
|---|---|---|---|
| TAB | Door tablet | Hall | 1,40 m |
| VOZ-S | Voice panel with buttons | Living room | 1,30 m |
| LCOM | LCom ACE71610003 | Bedroom 1 | 2,55 m |
| VOZ-D1 | Voice panel with buttons + pear | Bedroom 1 | 1,20 m |
| VOZ-D2 | Voice panel with buttons + pear | Bedroom 2 | 1,20 m |
| TI1 | Pull-cord | Bathroom 1 | 1,85 m |
| TD1 | Pull-cord | Bathroom 1 | 1,85 m |
| TI2 | Pull-cord | Bathroom 2 | 1,85 m |
| TD2 | Pull-cord | Bathroom 2 | 1,85 m |

## SYMBOLS · SÍMBOLOS · סמלים

| | |
|---|---|
| ▬ | TAB · Door tablet (iPad / Android) – call and voice, h 1.40 m<br>Door tablet – call and voice · טאבלט בכניסה – קריאה ודיבור |
| ●● | VOZ · Voice panel with buttons ACE82182451 – living room and bedrooms, h 1.20–1.30 m<br>Voice panel with buttons – living room and bedrooms · פנל קולי עם לחצנים – סלון וחדרי שינה |
| ⬯ | Call pear next to the bed (bedrooms)<br>Call pear next to the bed (bedrooms) · אגס קריאה ליד המיטה |
| T | TI / TD · Pull-cord ACE40320303W – toilet and shower, h 1.85 m<br>Pull-cord – toilet and shower, h 1.85 m · משיכת חבל – אסלה ומקלחת, גובה 1.85 מ' |
| 🟥 | LP · Corridor light ACE41020309 – above each public toilet door<br>Corridor light – above each public toilet door · מנורת מסדרון – מעל דלת כל שירותים ציבוריים |
| LC | LC · LCom ACE71610003 – apartment hub (ceiling)<br>LCom – apartment hub (ceiling) · LCom – מרכז הדירה (תקרה) |

## NOTES · NOTAS

1. Apartment x03 has the same devices (bathrooms laid out differently).
2. Tablet in the hall next to the front door.
3. Voice panel in the living room and in both bedrooms (with pear next to the bed).
4. 2 bathrooms: pull-cord at the toilet and at the shower of each (4 pull-cords).
5. Everything runs radially in Cat6 to the LCom in the bedroom corridor.

**MIGDALEI YAM A TIJON · ASSISTED LIVING**
Nurse call – GF + 8 floors · 32 apartments
System: ACE BG · Advantecnia Prepared by: Telab International

**2-BEDROOM APT. (x04 / x03)**

| SCALE · ESCALA | DATE · FECHA | REV | SHEET |
|---|---|---|---|
| 1:35 | 15/10/2026 | B | 04 |

Base: architect's plan L5 (Massad Oz / Triplet) · dimensions in m
A1 format · Rev. B – on the real plan

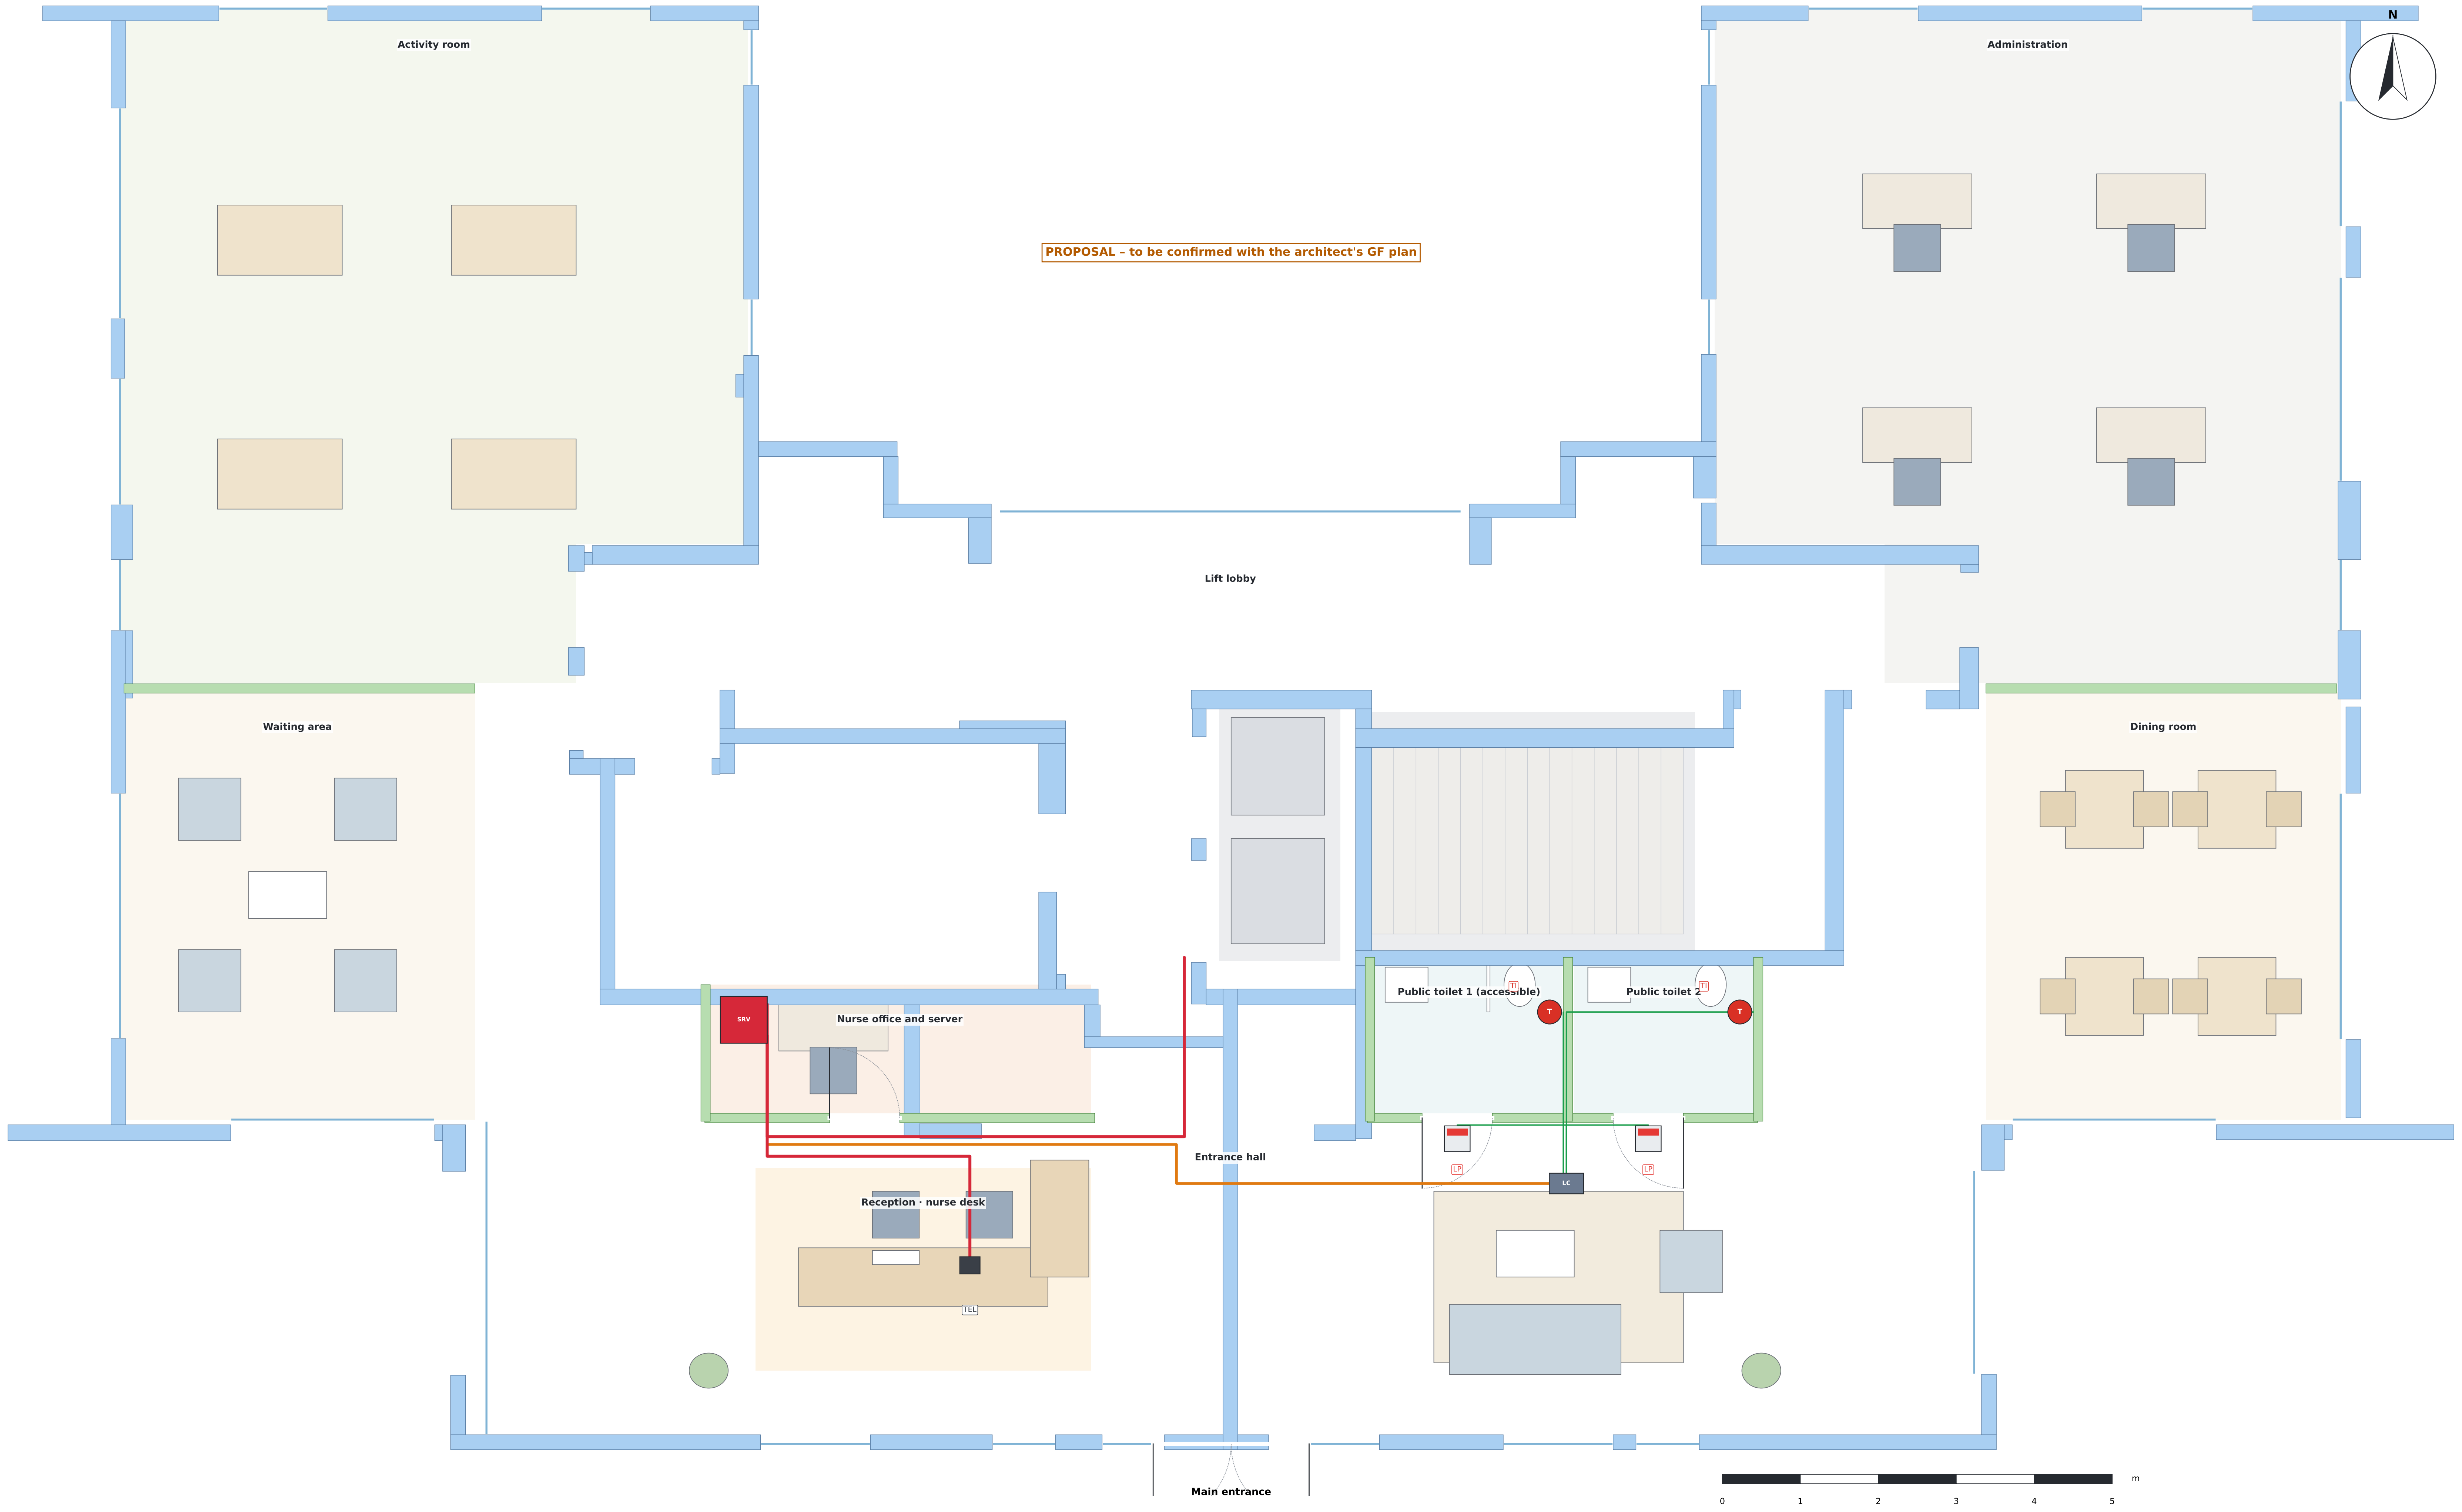
N
Activity room
Administration
PROPOSAL – to be confirmed with the architect's GF plan
Lift lobby
Waiting area
Dining room
Nurse office and server
SRV
Public toilet 1 (accessible)
Public toilet 2
TI
T
LP
LC
Entrance hall
Reception · nurse desk
TEL
Main entrance
0
1
2
3
4
5
m

## DETAIL · RECEPTION AND NURSE DESK (1:40)

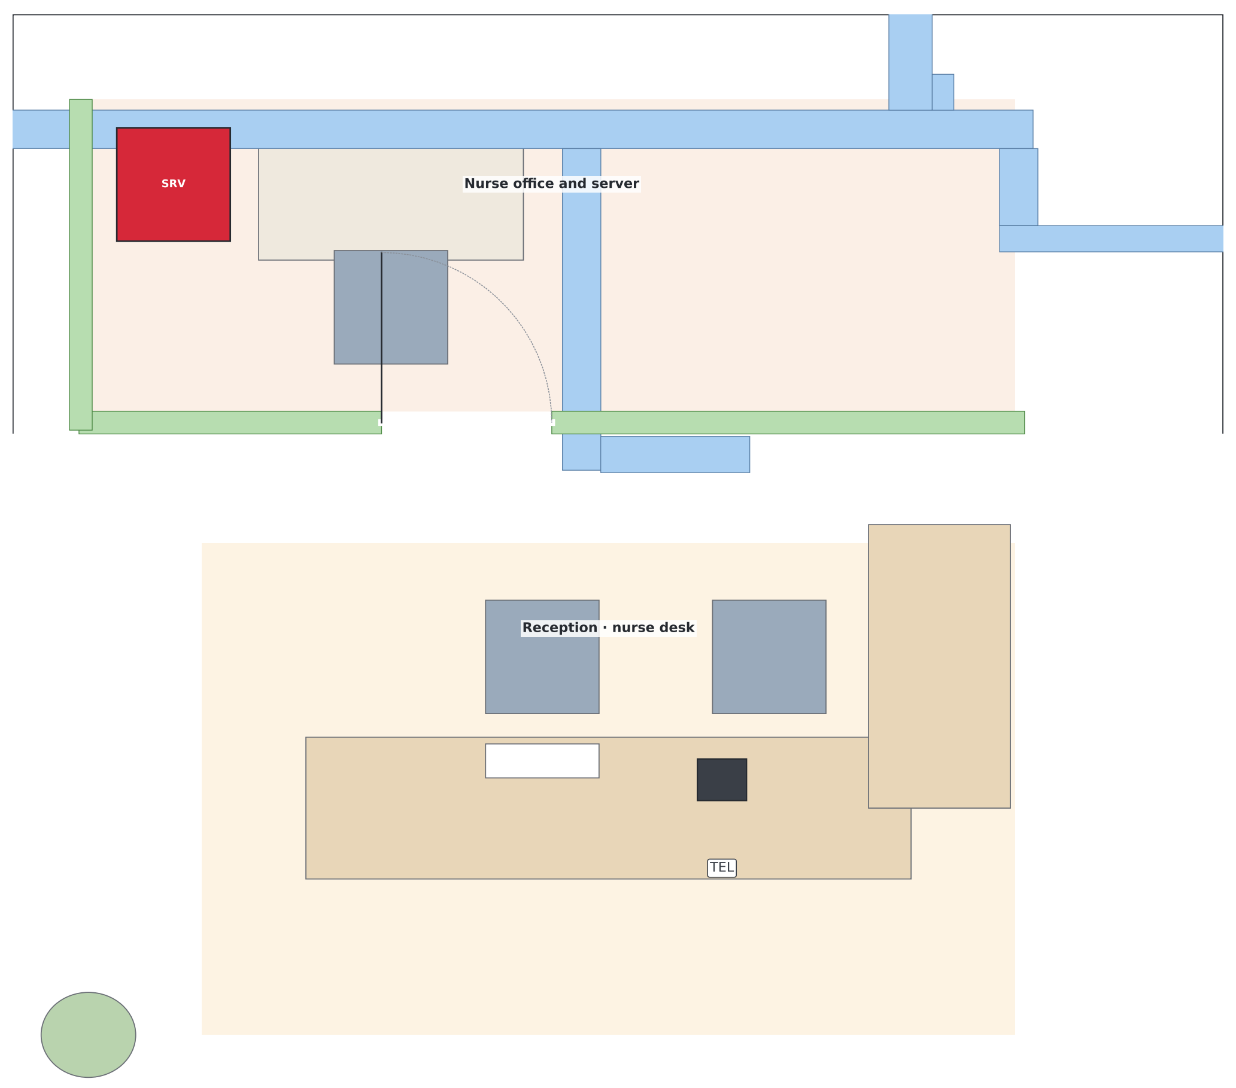
SRV
Nurse office and server
Reception · nurse desk
TEL

## NOTES · NOTAS

1. Nurse desk at reception, facing the entrance and the lifts.
2. On the desk: Android desk phone ACE52190200 (receives calls and voice).
3. Behind the desk: nurse office with the main rack: server ACE51010103, PoE switch ACEUCM6302 and GF Buscomm.
4. 2 public toilets on GF: pull-cord next to the toilet and corridor light above each door.
5. The riser from the 8 floors runs down the core to the main rack.
6. Proposed GF layout: to be adjusted when the architect's plan arrives.

## SYMBOLS · SÍMBOLOS · סמלים

| | |
|---|---|
| T | TI / TD · Pull-cord ACE40320303W – toilet and shower, h 1.85 m<br>Pull-cord – toilet and shower, h 1.85 m · משיכת חבל – אסלה ומקלחת, גובה 1.85 מ' |
| LC | LC · LCom ACE71610003 – apartment hub (ceiling)<br>LCom – apartment hub (ceiling) · LCom – מרכז דירה (תקרה) |
| SRV | SRV · GF rack: server ACE51010103 + switch + Buscomm<br>GF rack: server + switch + Buscomm · ארון קרקע: שרת + מתג + Buscomm |
| 🟥 | LP · Corridor light ACE41020309 – above each public toilet door<br>Corridor light – above each public toilet door · מנורת מסדרון – מעל דלת כל שירותים ציבוריים |
| TEL | TEL · Android desk phone ACE52190200<br>Android desk phone · טלפון שולחני אנדרואיד |

**MIGDALEI YAM A TIJON · ASSISTED LIVING**
Nurse call – GF + 8 floors · 32 apartments
System: ACE BG · Advantecnia      Prepared by: Telab International

**GROUND FLOOR · LOBBY AND NURSE DESK**

| SCALE · ESCALA | DATE · FECHA | REV | SHEET |
|---|---|---|---|
| 1:60 | 15/10/2026 | B | 05 |

Base: architect's plan L5 (Massad Oz / Triplet) · dimensions in m
A1 format · Rev. B – on the real plan

## A · BUILDING GF + 8 FLOORS

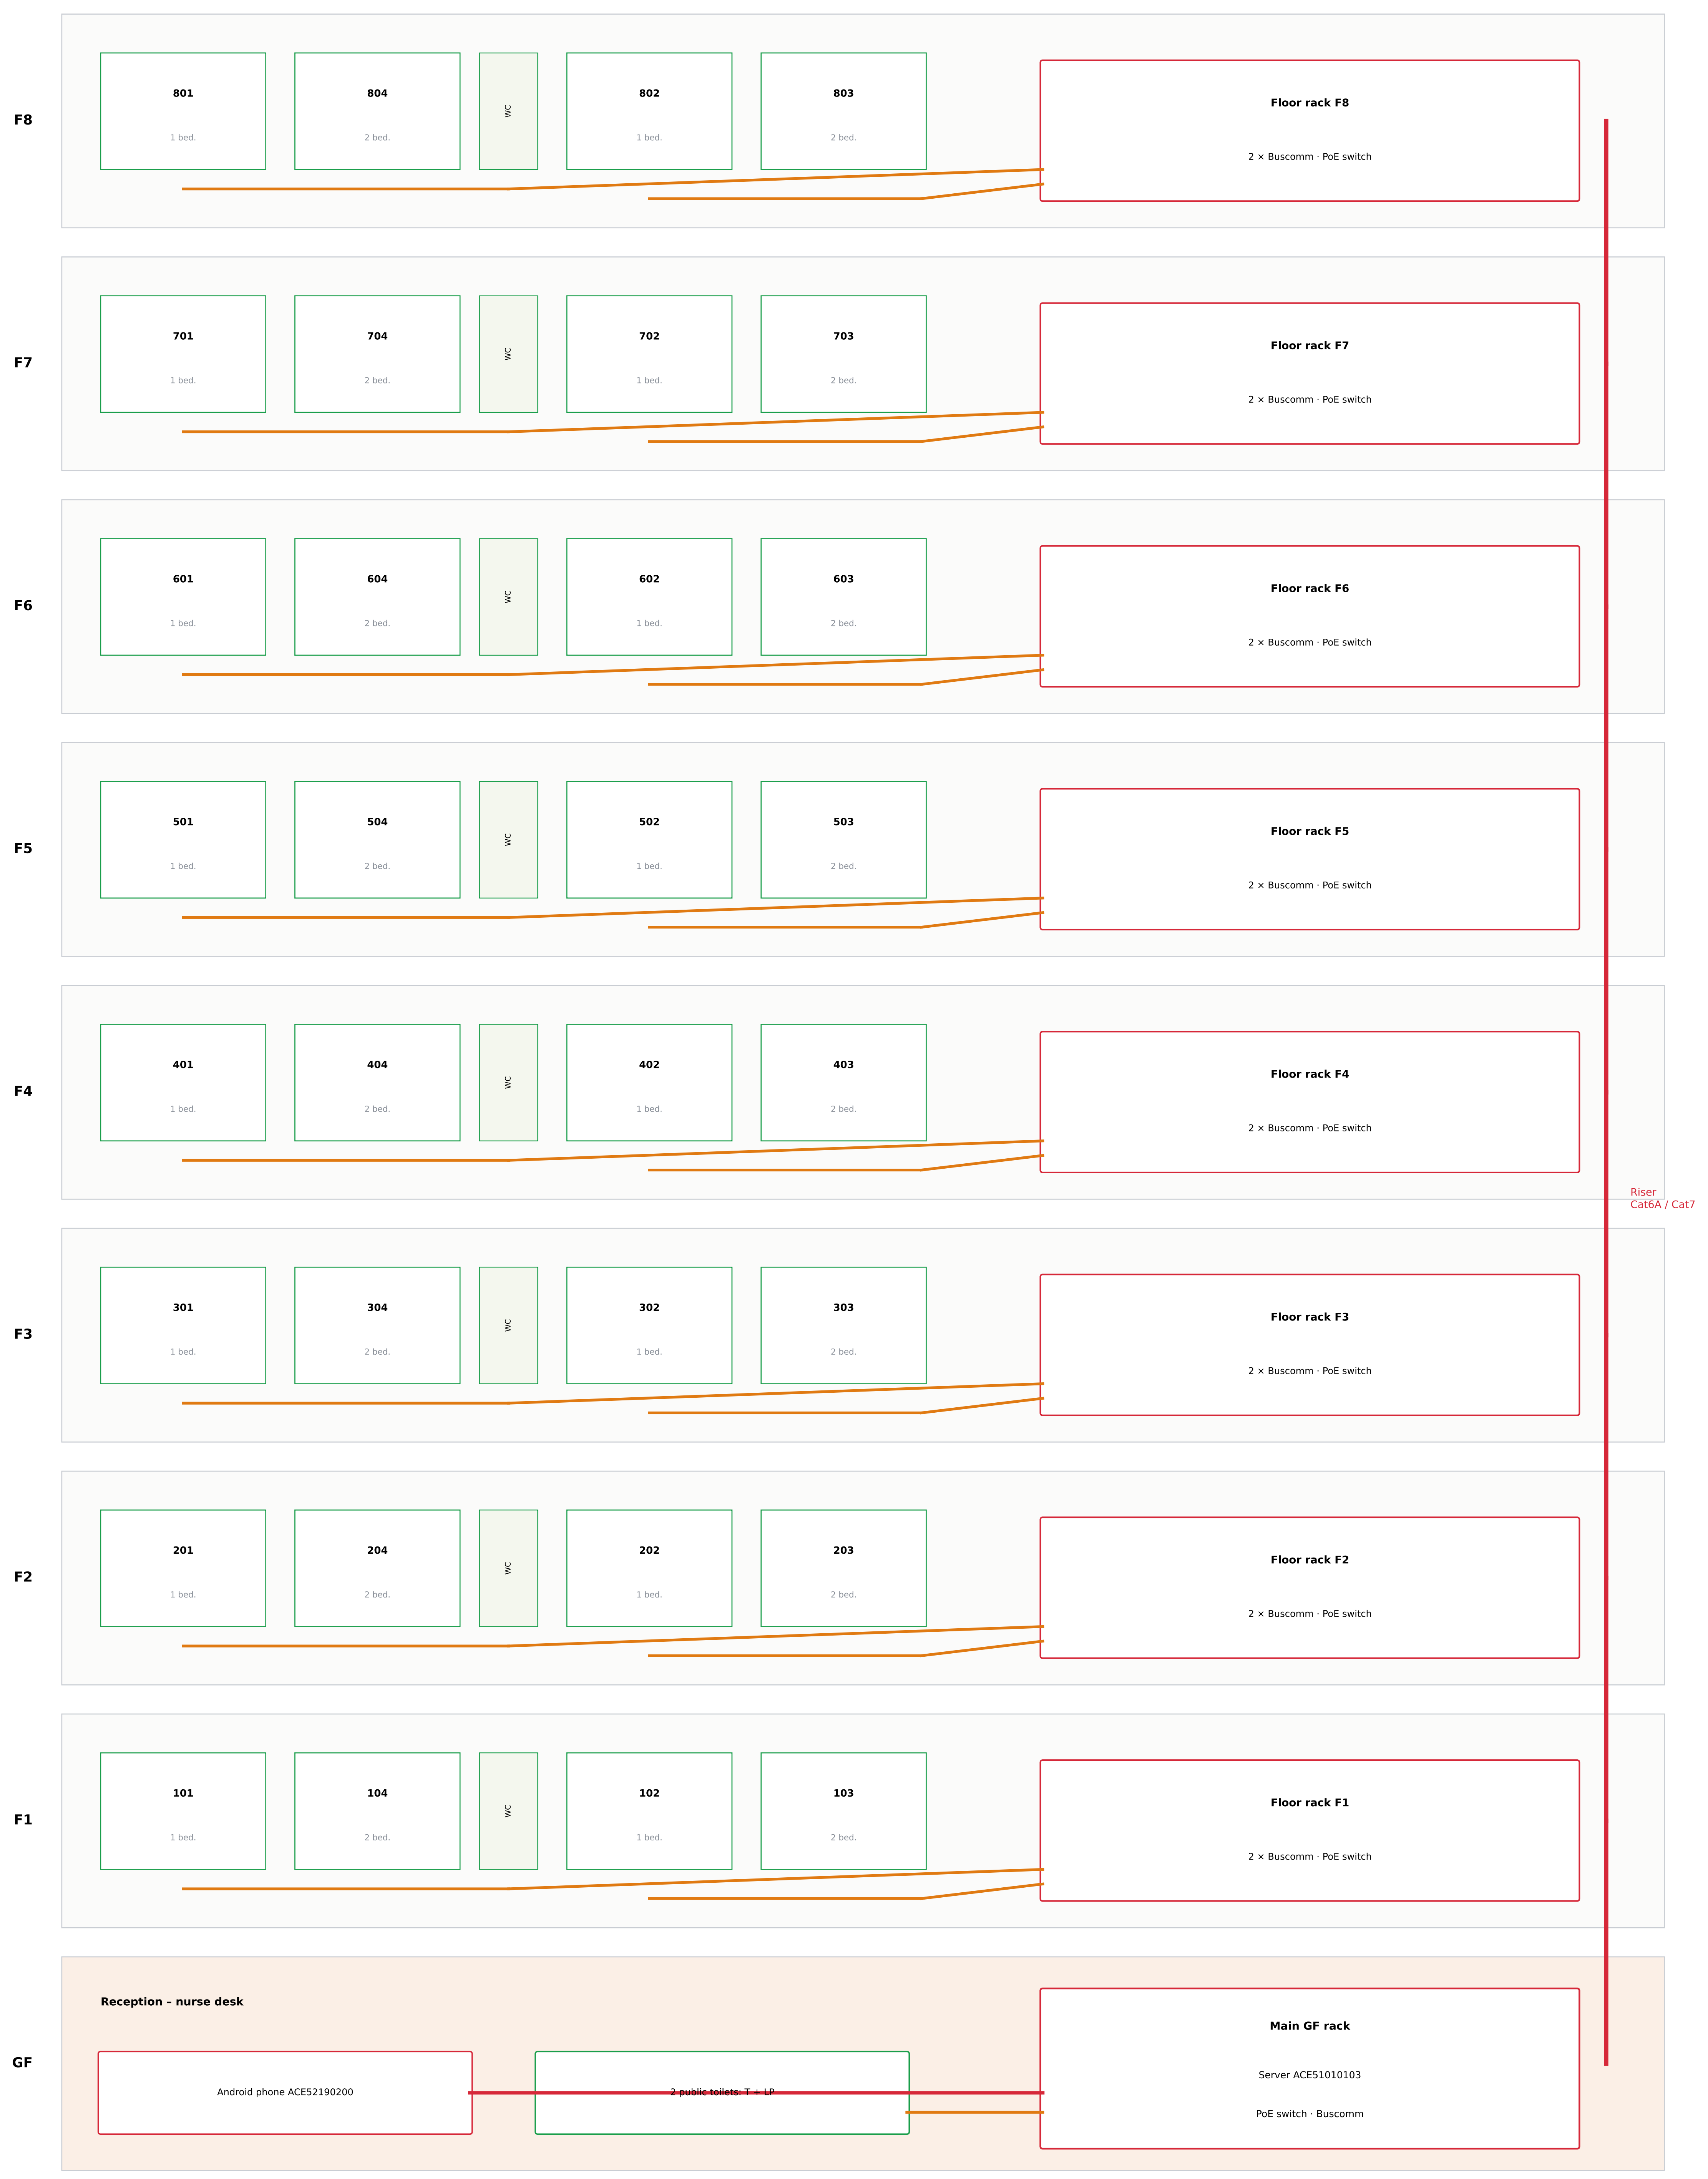
F8
801
1 bed.
804
2 bed.
WC
802
1 bed.
803
2 bed.
Floor rack F8
2 × Buscomm · PoE switch
F7
701
1 bed.
704
2 bed.
WC
702
1 bed.
703
2 bed.
Floor rack F7
2 × Buscomm · PoE switch
F6
601
1 bed.
604
2 bed.
WC
602
1 bed.
603
2 bed.
Floor rack F6
2 × Buscomm · PoE switch
F5
501
1 bed.
504
2 bed.
WC
502
1 bed.
503
2 bed.
Floor rack F5
2 × Buscomm · PoE switch
F4
401
1 bed.
404
2 bed.
WC
402
1 bed.
403
2 bed.
Floor rack F4
2 × Buscomm · PoE switch
Riser
Cat6A / Cat7
F3
301
1 bed.
304
2 bed.
WC
302
1 bed.
303
2 bed.
Floor rack F3
2 × Buscomm · PoE switch
F2
201
1 bed.
204
2 bed.
WC
202
1 bed.
203
2 bed.
Floor rack F2
2 × Buscomm · PoE switch
F1
101
1 bed.
104
2 bed.
WC
102
1 bed.
103
2 bed.
Floor rack F1
2 × Buscomm · PoE switch
GF
Reception – nurse desk
Android phone ACE52190200
2 public toilets: T + LP
Main GF rack
Server ACE51010103
PoE switch · Buscomm

## B · TOPOLOGY OF ONE APARTMENT

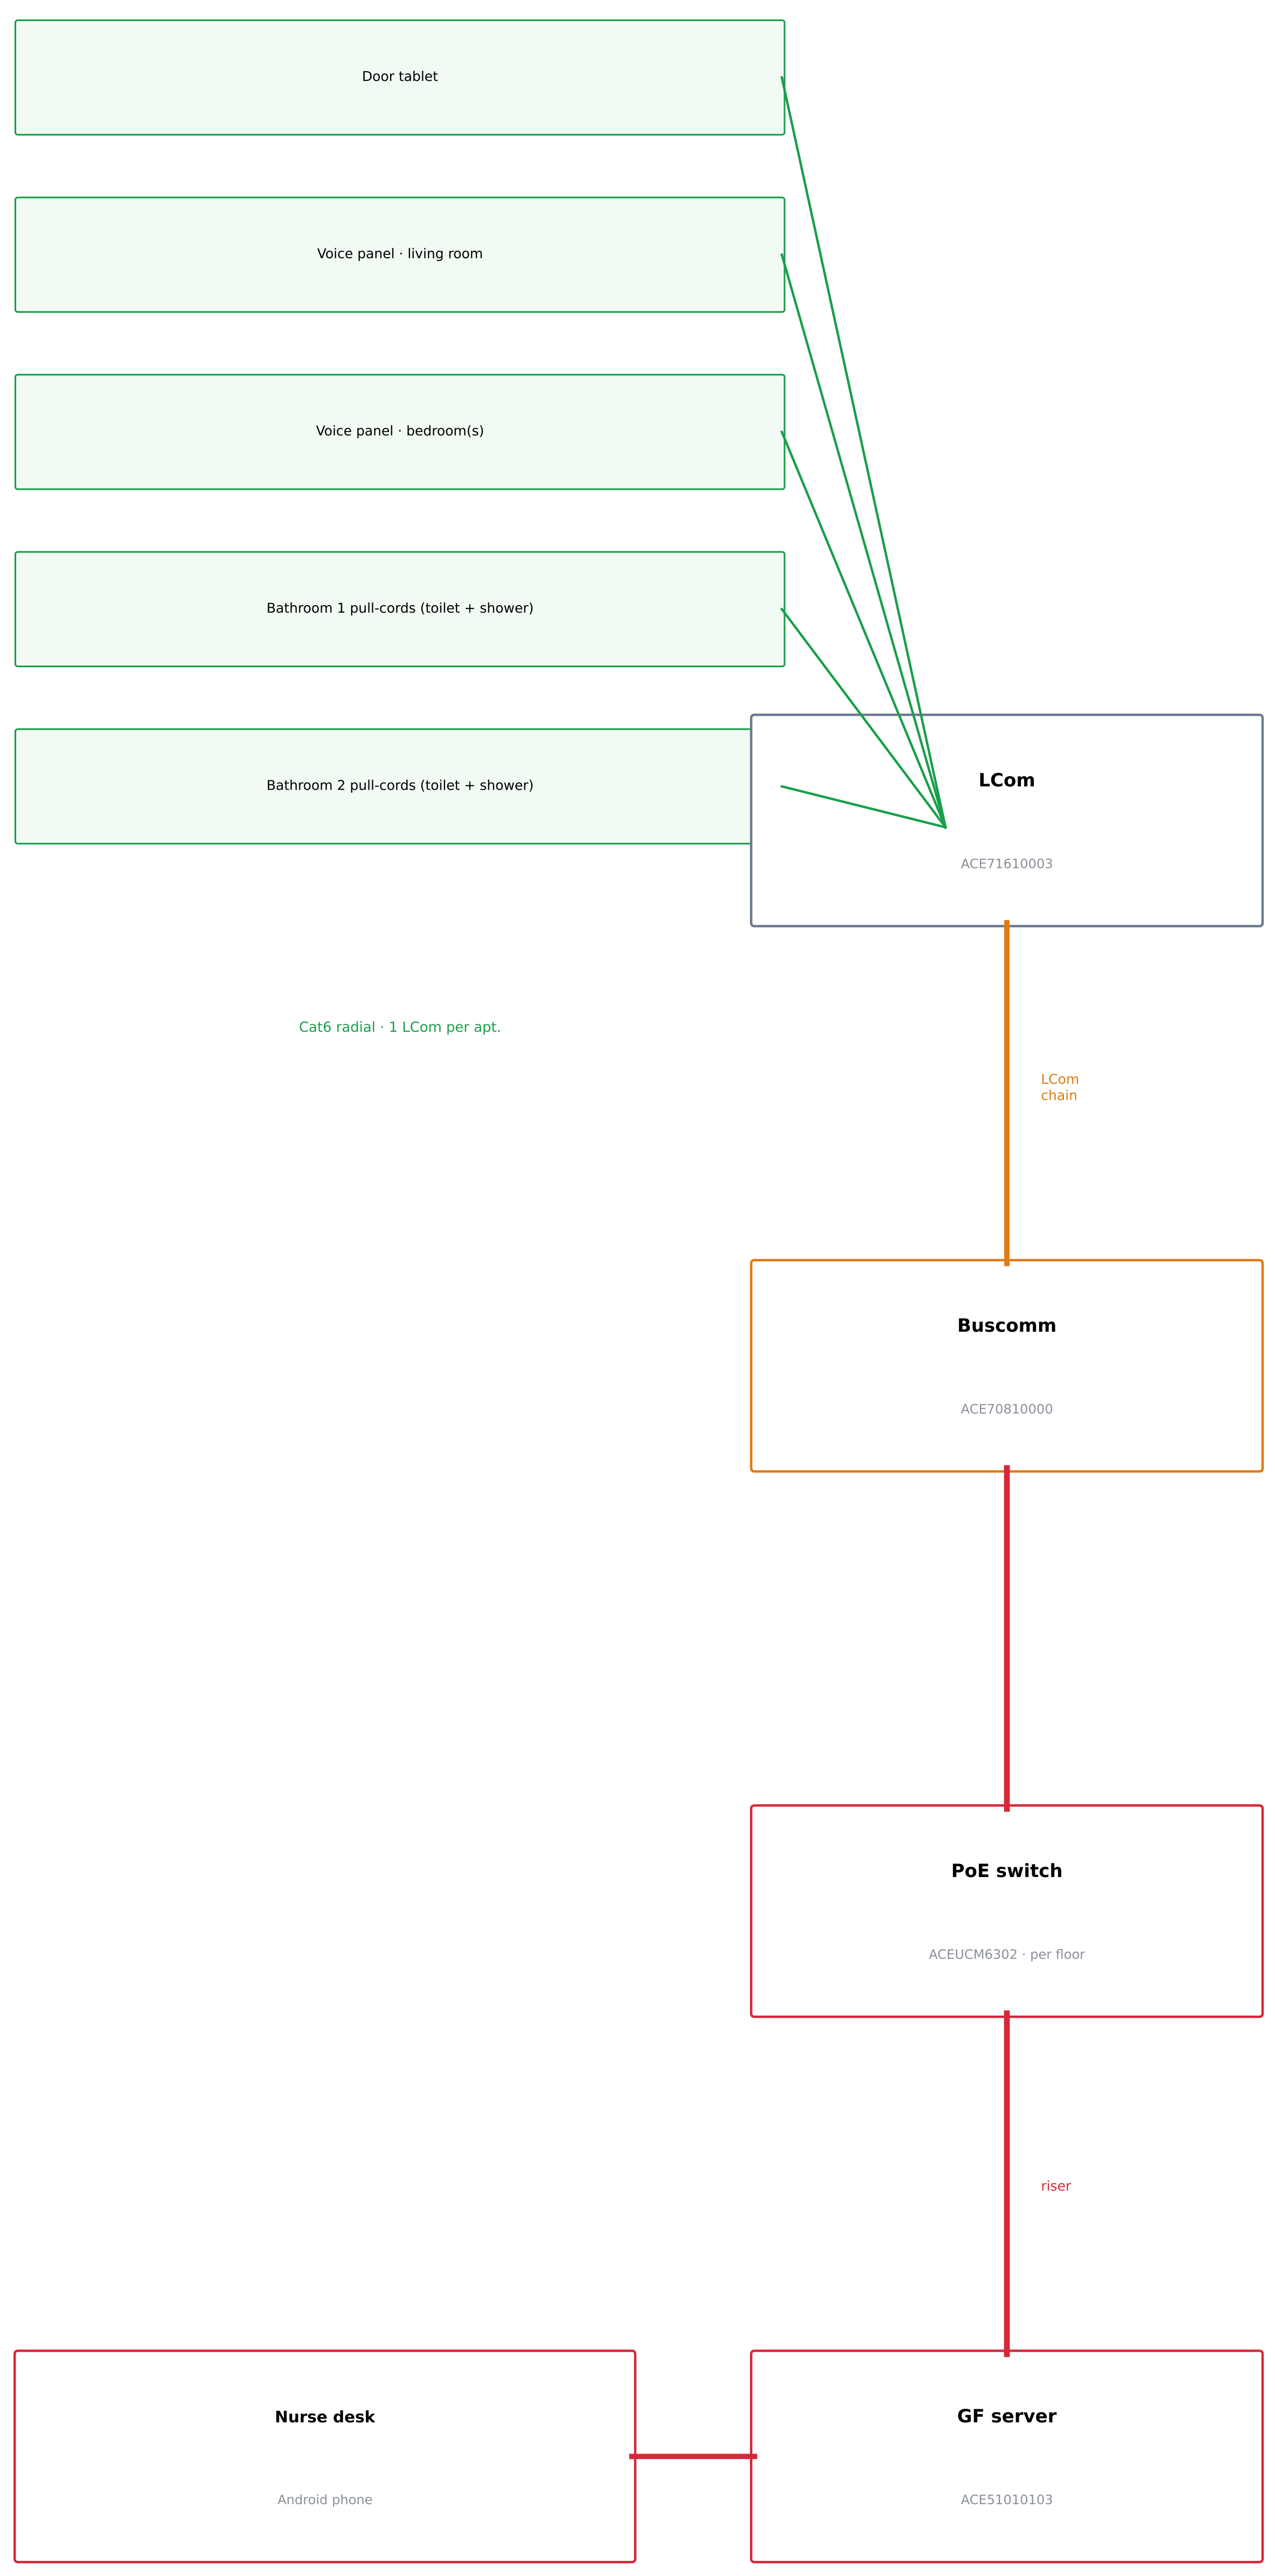
Door tablet
Voice panel · living room
Voice panel · bedroom(s)
Bathroom 1 pull-cords (toilet + shower)
Bathroom 2 pull-cords (toilet + shower)
LCom
ACE71610003
Cat6 radial · 1 LCom per apt.
LCom
chain
Buscomm
ACE70810000
PoE switch
ACEUCM6302 · per floor
riser
Nurse desk
Android phone
GF server
ACE51010103

### NOTES · NOTAS

1. 8 identical floors with 4 apartments (2 one-bedroom and 2 two-bedroom).
2. On each floor: rack with 2 Buscomm and a PoE switch.
3. Chain 1: x01 → x04 → public toilet. Chain 2: x02 → x03.
4. The switches run up the riser to the main GF rack.
5. Calls arrive by voice on the Android phone at the nurse desk.
6. The whole system is PoE.
7. Preliminary quantities: validate with Advantecnia and on site.

**MIGDALEI YAM A TIJON · ASSISTED LIVING**
Nurse call – GF + 8 floors · 32 apartments
System: ACE BG · Advantecnia Prepared by: Telab International

**RISER DIAGRAM AND TOPOLOGY**

| SCALE · ESCALA | DATE · FECHA | REV | SHEET |
|---|---|---|---|
| S/E | 15/10/2026 | B | 06 |

Base: architect's plan L5 (Massad Oz / Triplet) · dimensions in m
A1 format · Rev. B – on the real plan

## BILL OF MATERIALS – WHOLE BUILDING (GF + 8 floors · 32 apartments · 10 public toilets)

| Code | Description | Qty. | Remark |
|---|---|---|---|
| **IN THE APARTMENTS (32)** | | | |
| TAB | Door tablet (iPad / Android) – call and voice | **32** | 1 per apartment |
| VOZ | Voice call panel with buttons – ACE82182451 | **80** | living room + each bedroom |
| TI/TD | Pull-cord – ACE40320303W (toilet and shower) | **128** | 4 per apartment |
| LC | LCom – ACE71610003 | **32** | 1 per apartment |
| **PUBLIC TOILETS (10)** | | | |
| T | Pull-cord – ACE40320303W | **10** | 8 floors + 2 on GF |
| LP | Corridor light – ACE41020309 | **10** | above each door |
| LC | LCom – ACE71610003 | **9** | 1 per floor + 1 on GF |
| **RACKS AND HEAD-END** | | | |
| BC | Buscomm – ACE70810000 | **17** | 2 per floor + 1 on GF |
| SW | PoE switch – ACEUCM6302 | **9** | 1 per floor + GF |
| GAB | 12U wall rack (Tripp Lite SRW12US) with patch panel | **8** | 1 per floor |
| GAB-PB | Main floor-standing rack with UPS | **1** | GF |
| SRV | Server + Advantecnia software – ACE51010103 | **1** | GF |
| TEL | Android desk phone – ACE52190200 | **1** | nurse desk |
| **CABLES (+ 15 % spare)** | | | |
| — | Cat6 radial inside the apartments (green) | **1880 m** | 202 m por piso |
| — | Cat6 / Cat7 chain LCom → Buscomm (orange) | **780 m** | 82 m per floor |
| — | Cat6A / Cat7 racks and riser (red) | **100 m** | includes riser |

### NOTES · NOTAS

1. Quantities calculated from the model (typical floor × 8 + GF).
2. Cable lengths measured on the drawn route, + 15 %.
3. Prices: per current Advantecnia price list.
4. Validate on site before purchasing.

**MIGDALEI YAM A TIJON · ASSISTED LIVING**
Nurse call – GF + 8 floors · 32 apartments
System: ACE BG · Advantecnia Prepared by: Telab International

## BILL OF MATERIALS

| SCALE · ESCALA | DATE · FECHA | REV | SHEET |
|---|---|---|---|
| S/E | 15/10/2026 | B | 07 |

Base: architect's plan L5 (Massad Oz / Triplet) · dimensions in m
A1 format · Rev. B – on the real plan

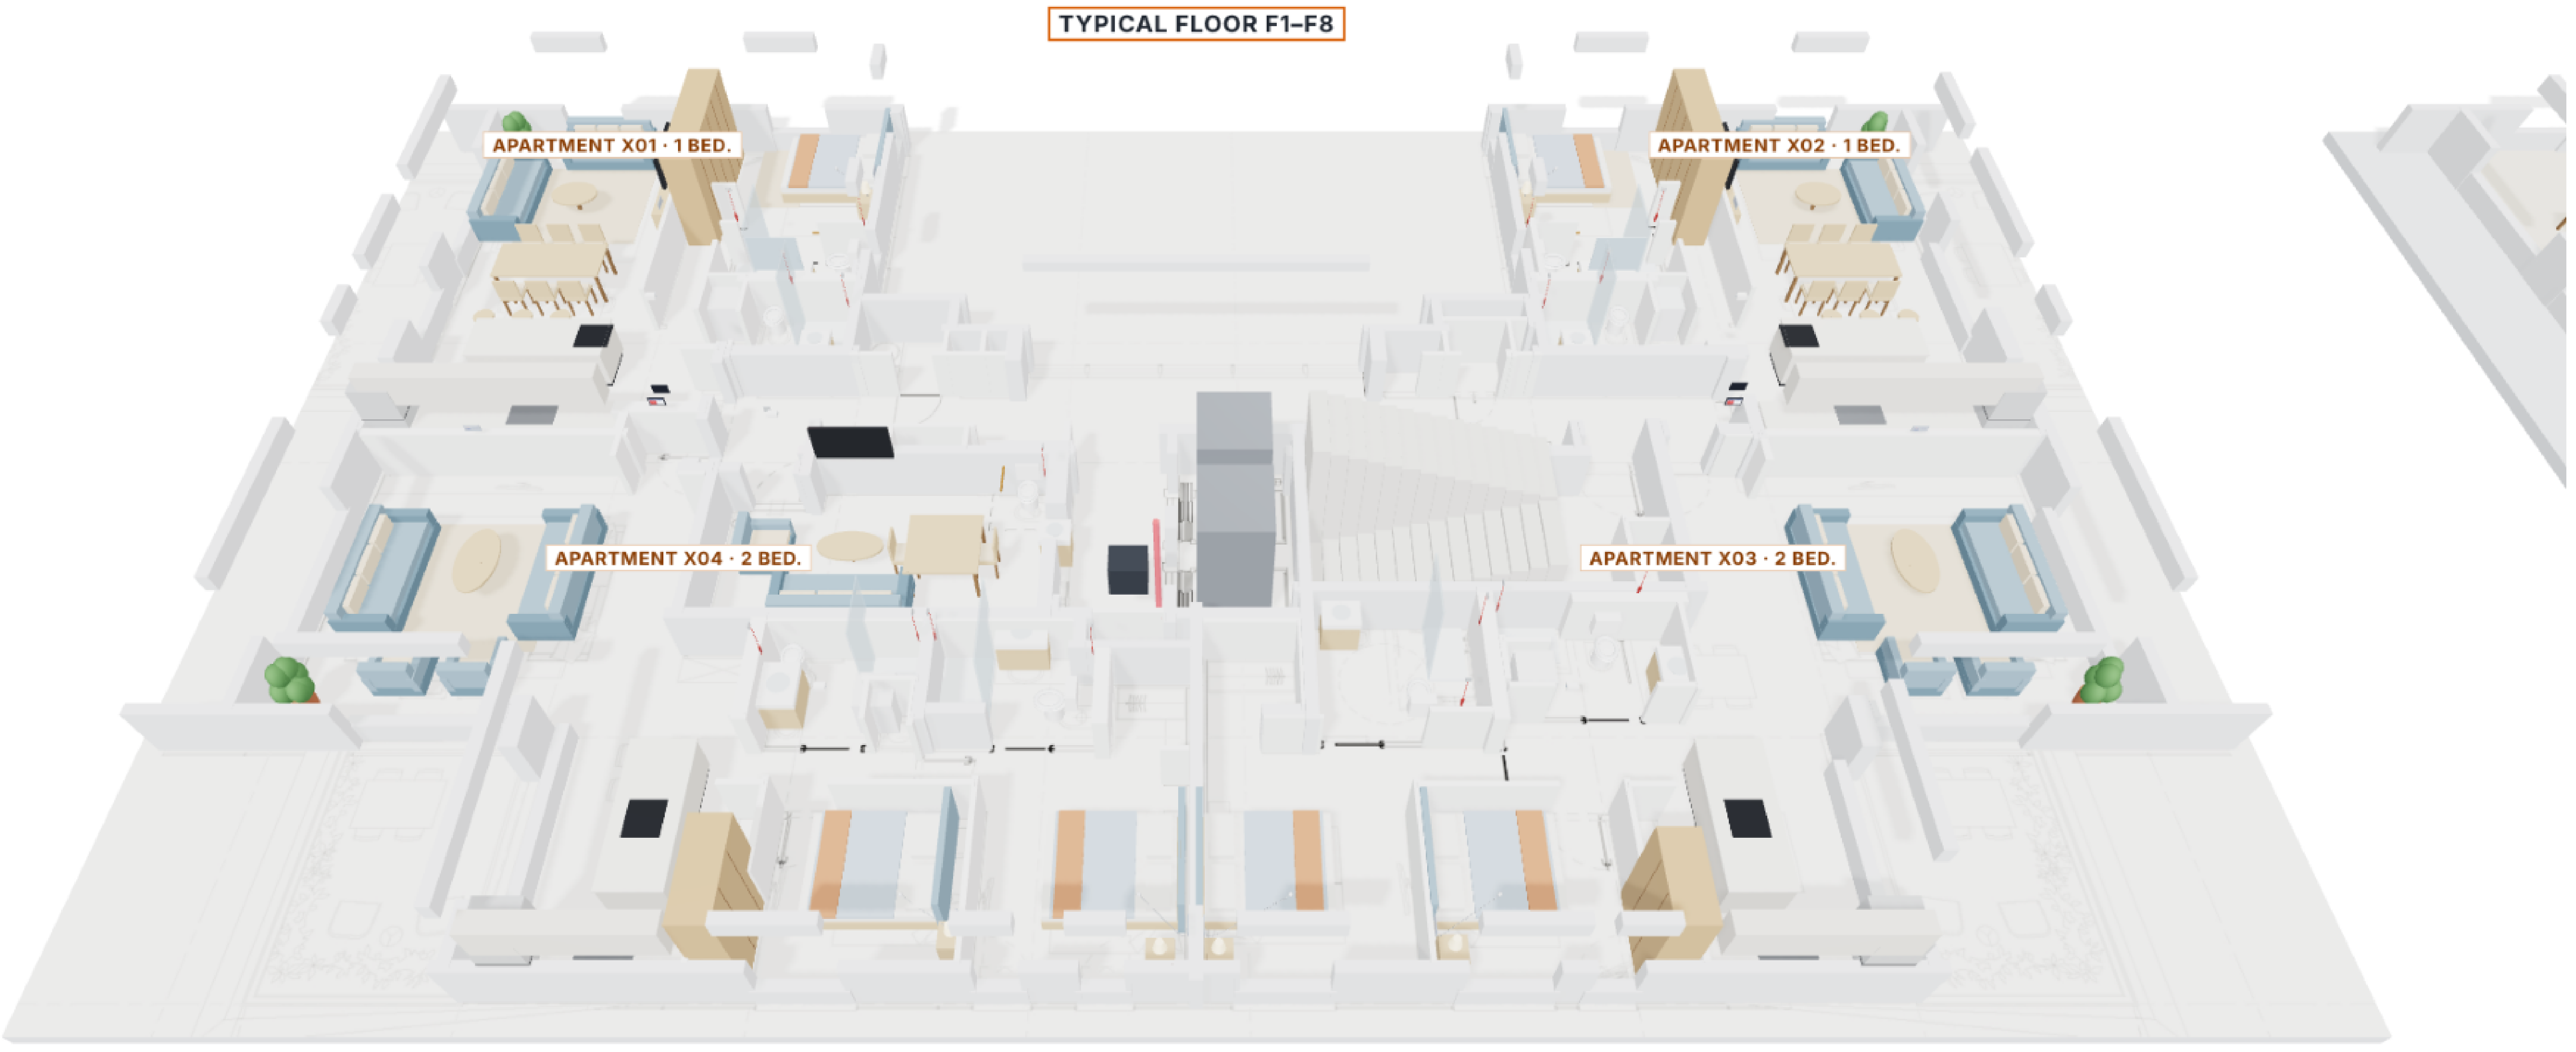
TYPICAL FLOOR F1–F8
APARTMENT X01 · 1 BED.
APARTMENT X02 · 1 BED.
APARTMENT X04 · 2 BED.
APARTMENT X03 · 2 BED.

A · Floor tipo – 4 departamentos

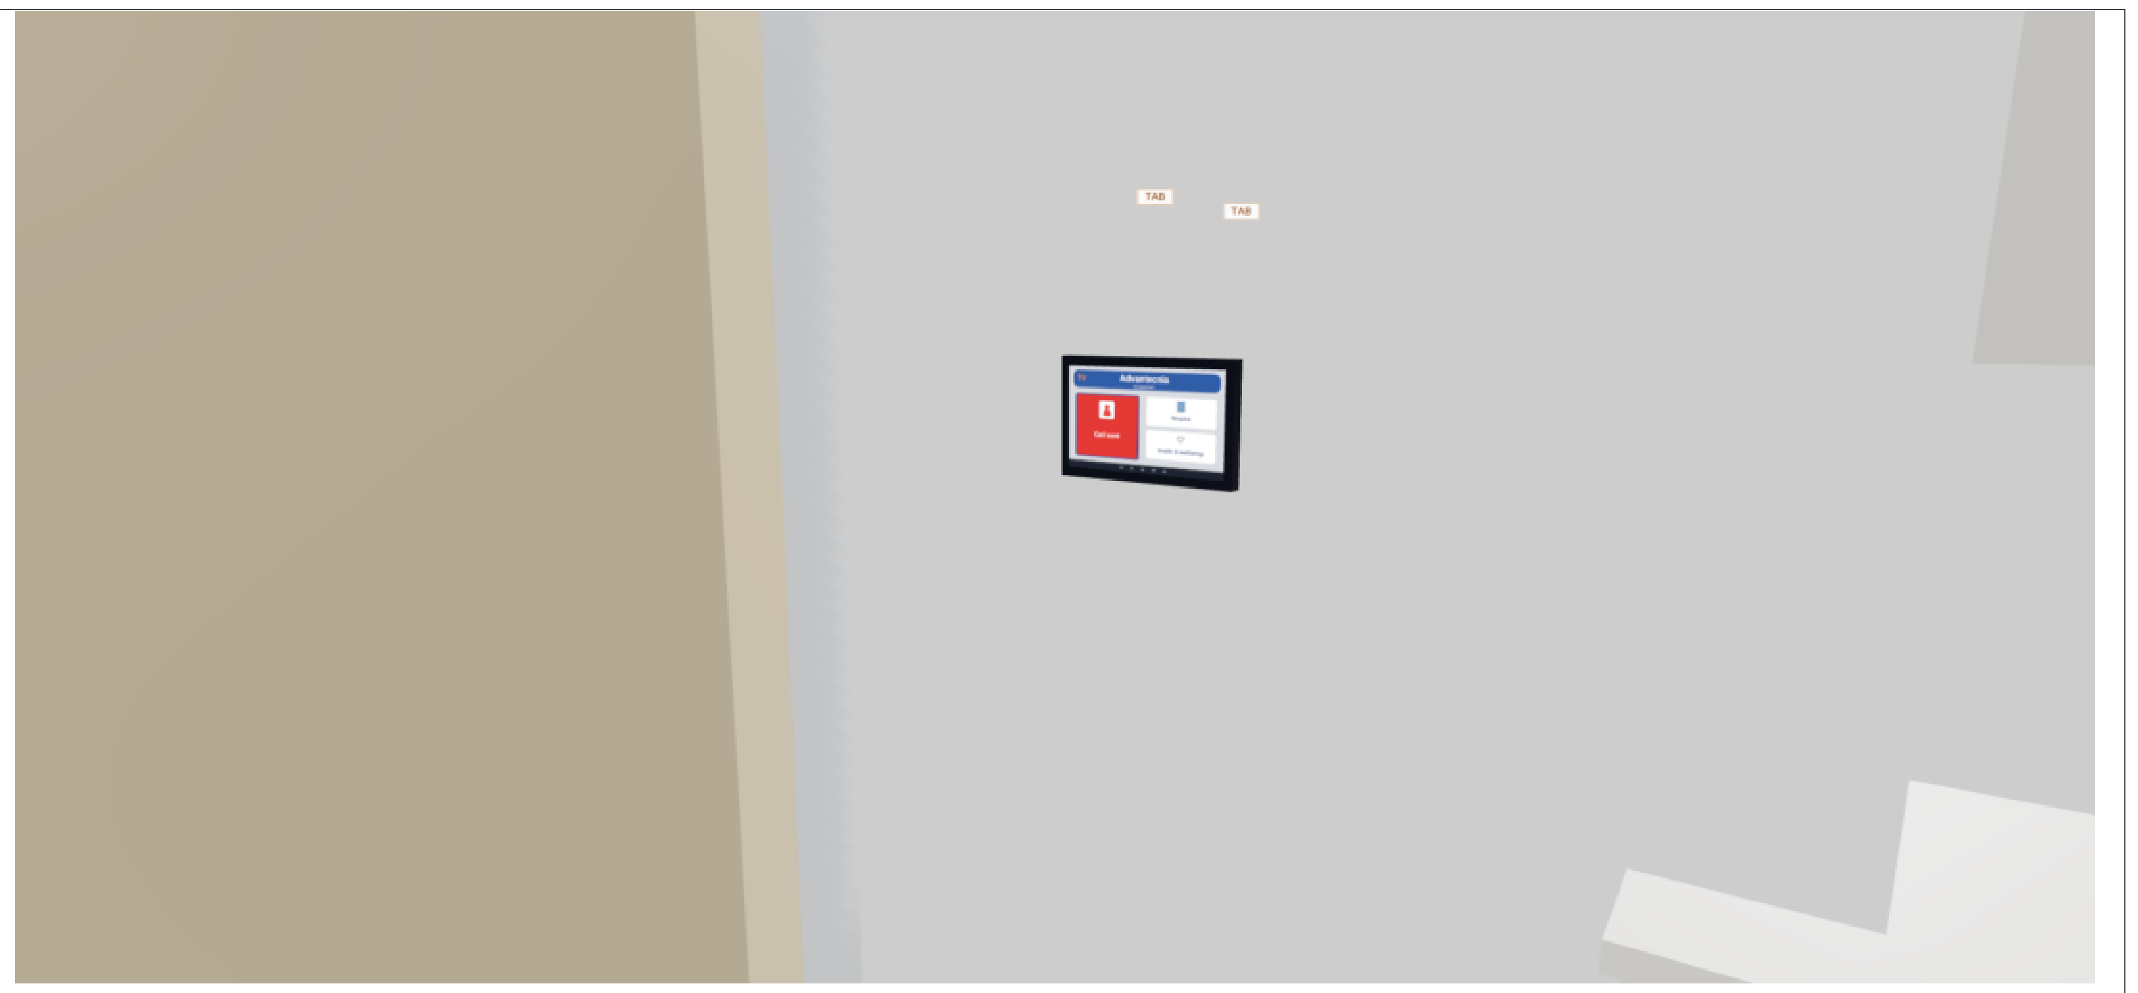

B · Tablet de la puerta

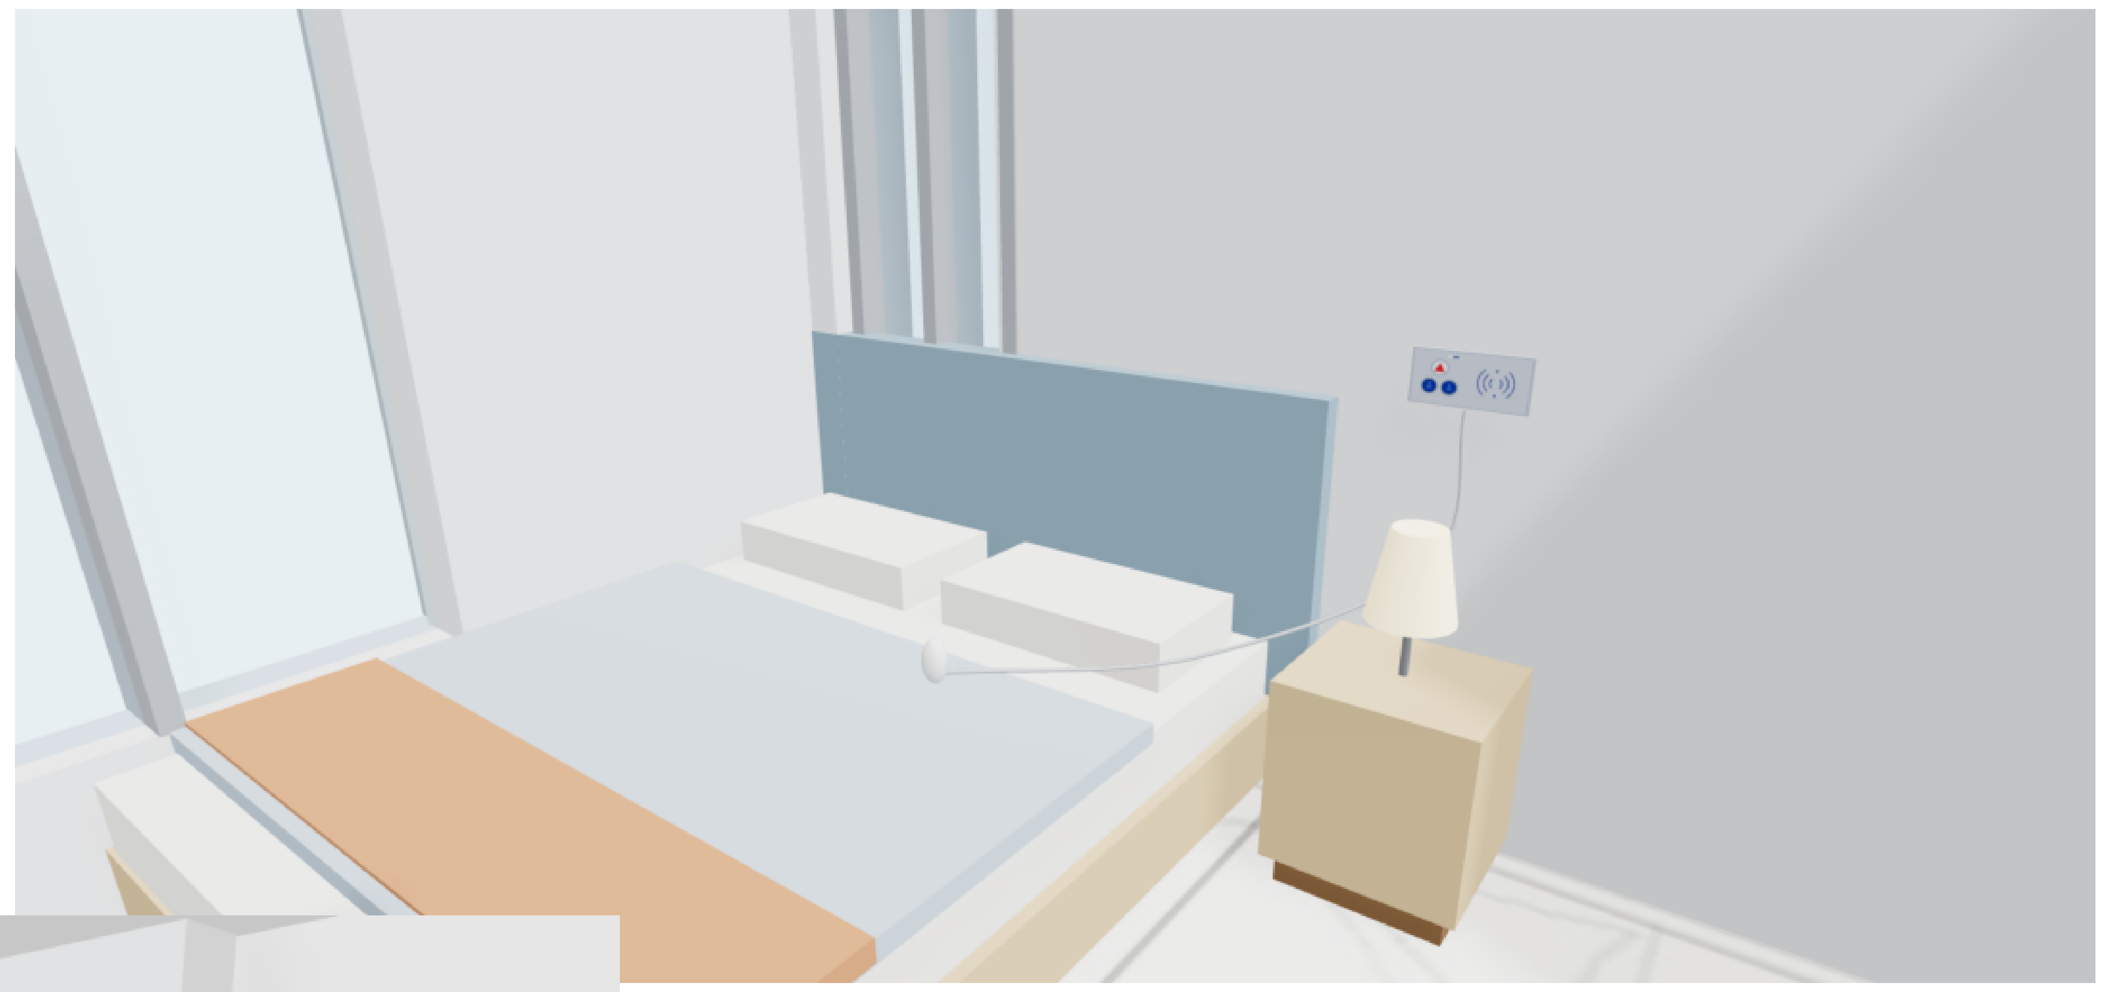

D · Baño – tiradores en inodoro y ducha

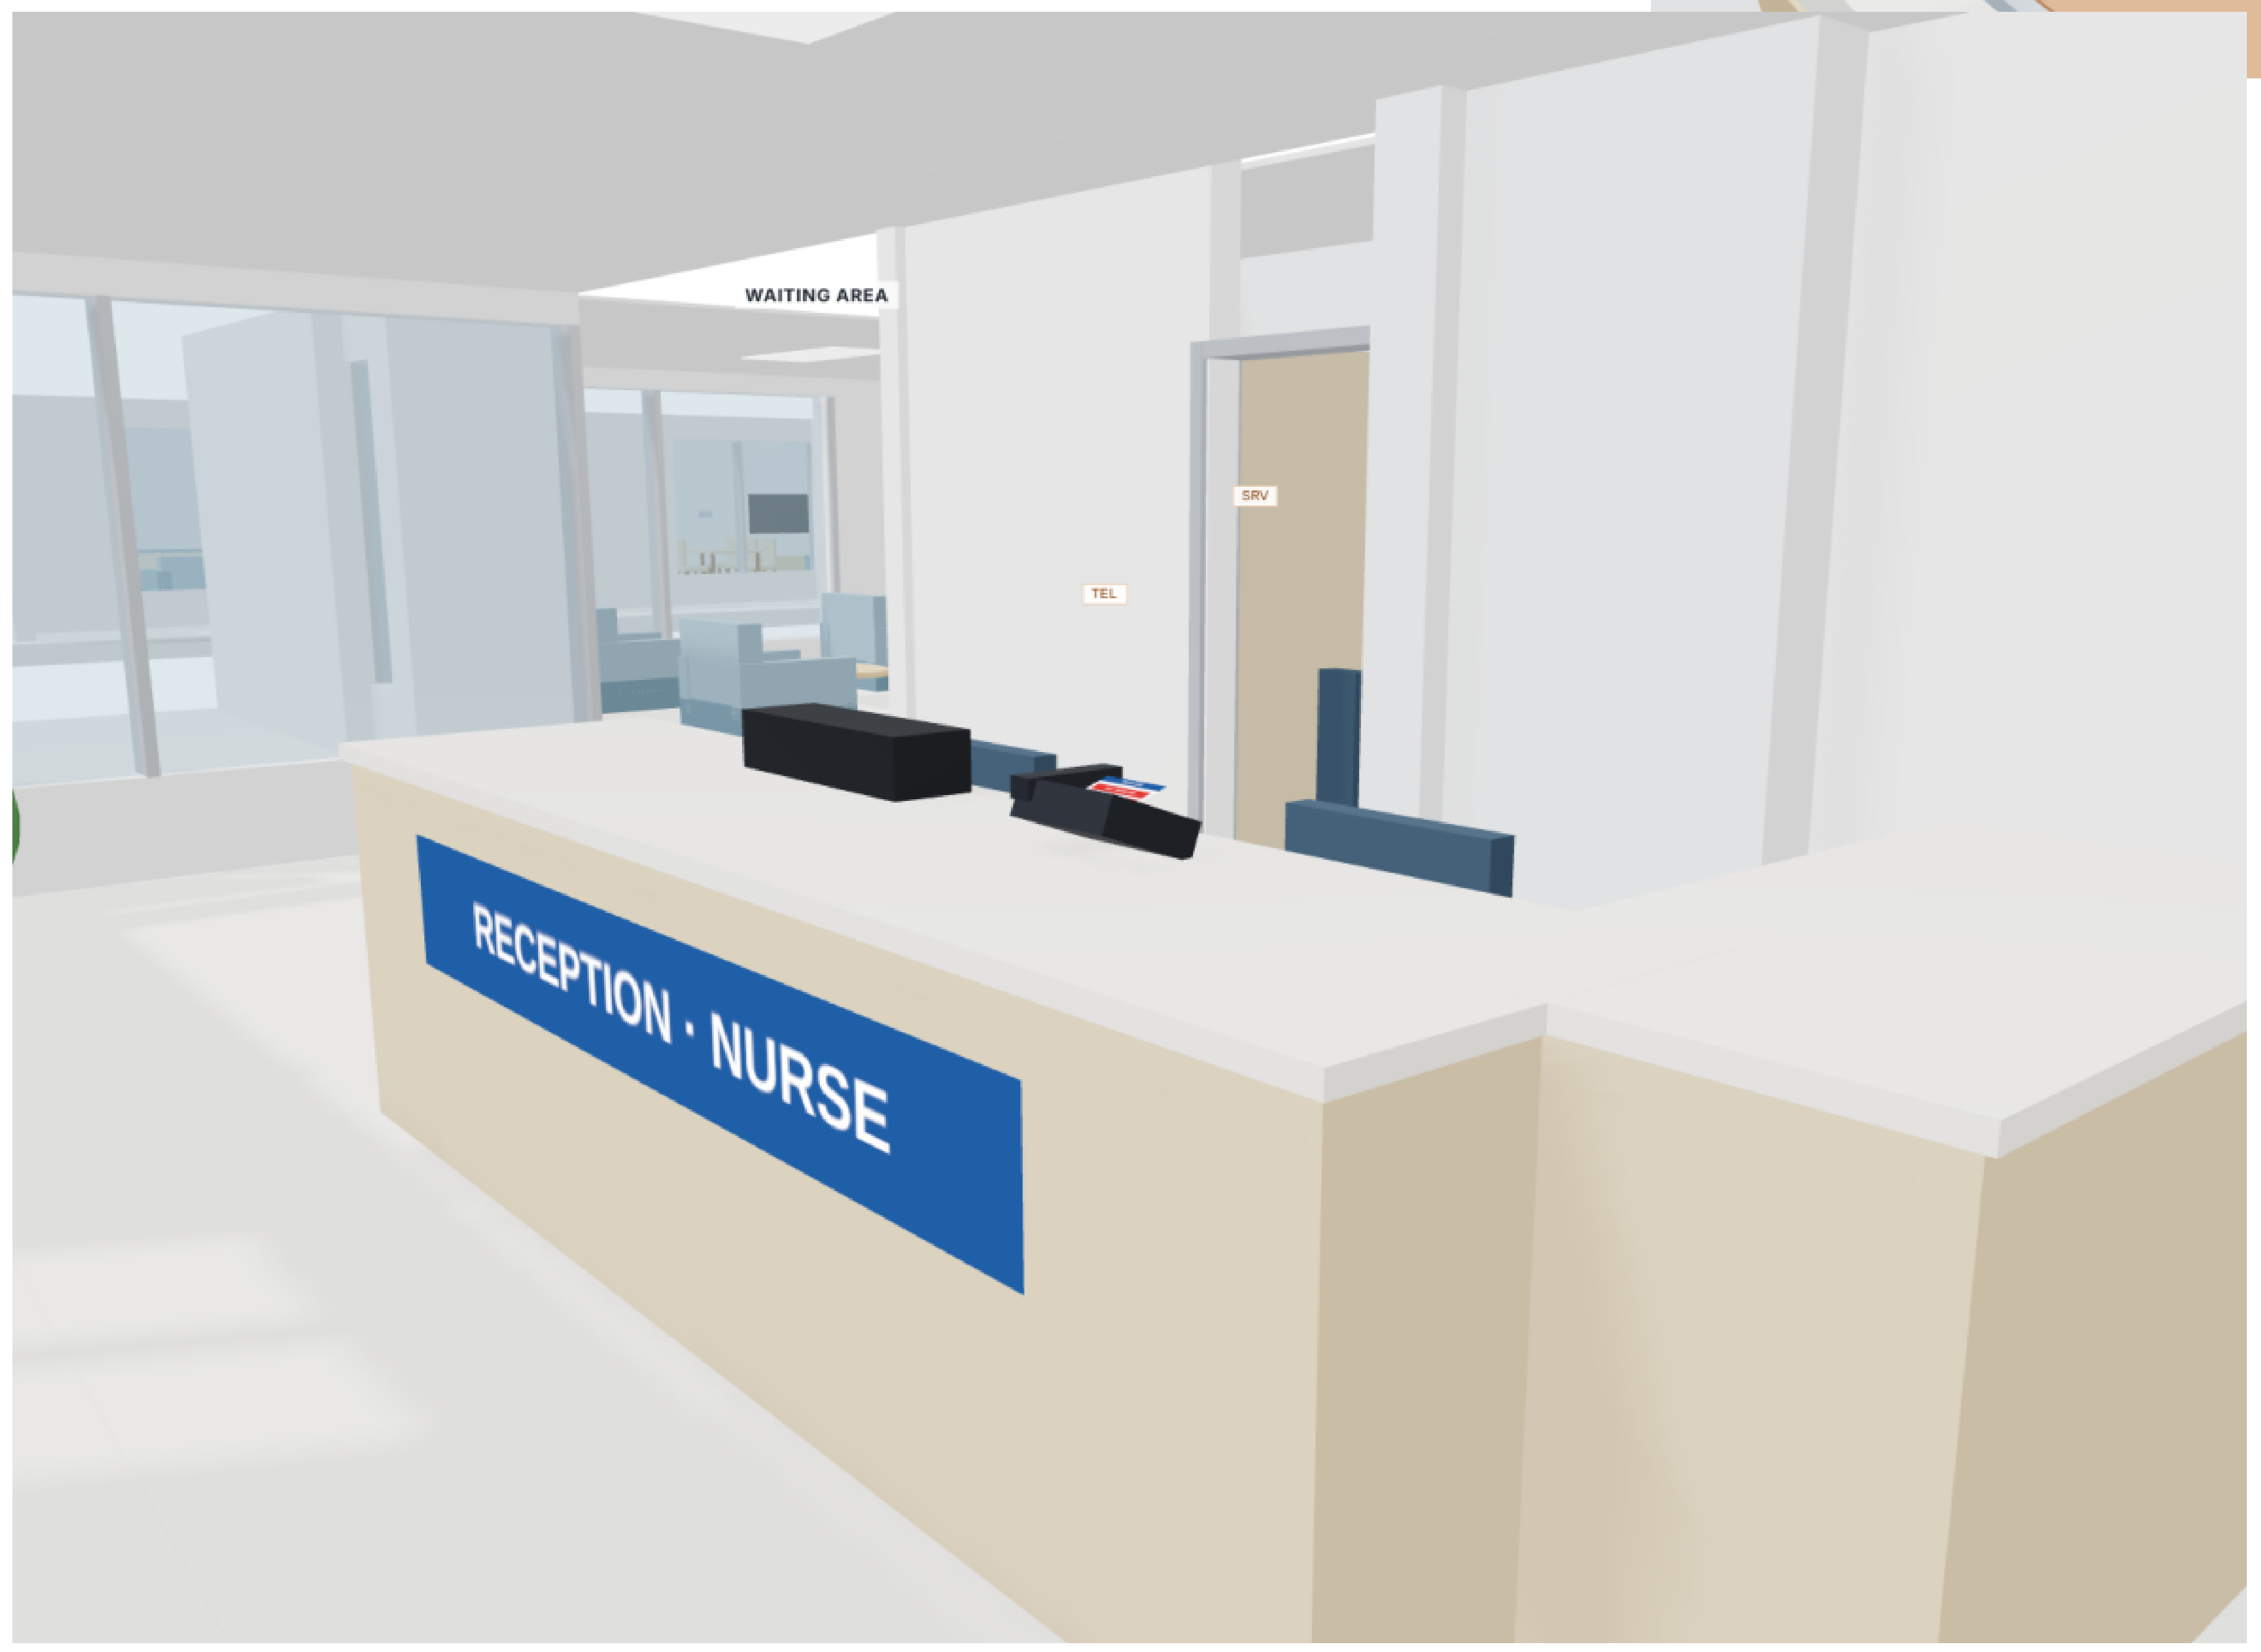
WAITING AREA
SRV
TEL
RECEPTION · NURSE

E · PB – desk de enfermería

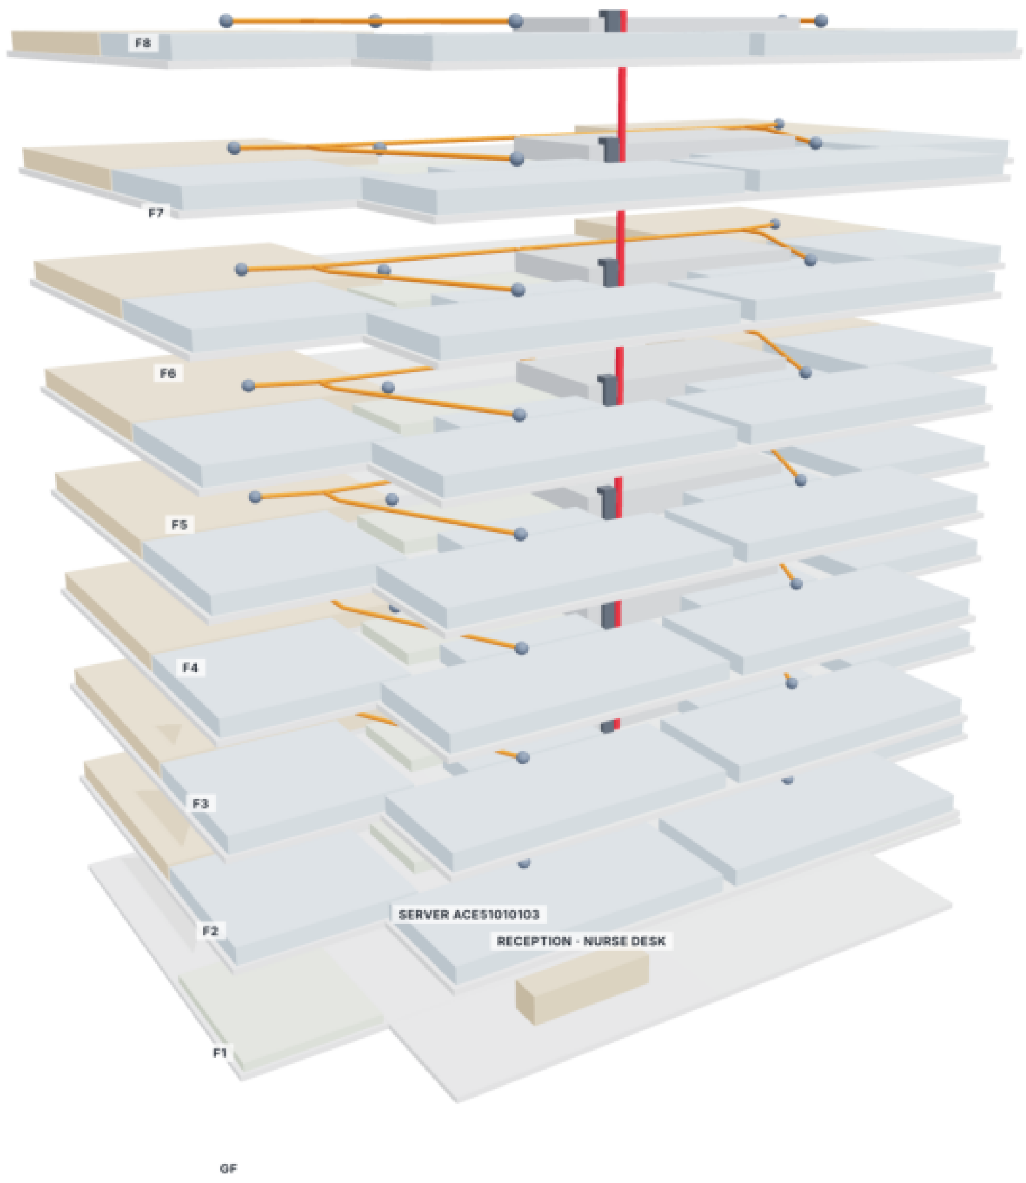
F8
F7
F6
F5
F4
F3
F2
F1
GF
SERVER ACES1010103
RECEPTION · NURSE DESK

F · Edificio PB + 8 pisos

**MIGDALEI YAM A TIJON · ASSISTED LIVING**

Nurse call – GF + 8 floors · 32 apartments

System: ACE BG · Advantecnia    Prepared by: Telab International

## 3D VIEWS

| SCALE · ESCALA | DATE · FECHA | REV | SHEET |
|---|---|---|---|
| **S/E** | **15/10/2026** | **B** | **08** |

Base: architect's plan L5 (Massad Oz / Triplet) · dimensions in m

A1 format · Rev. B – on the real plan

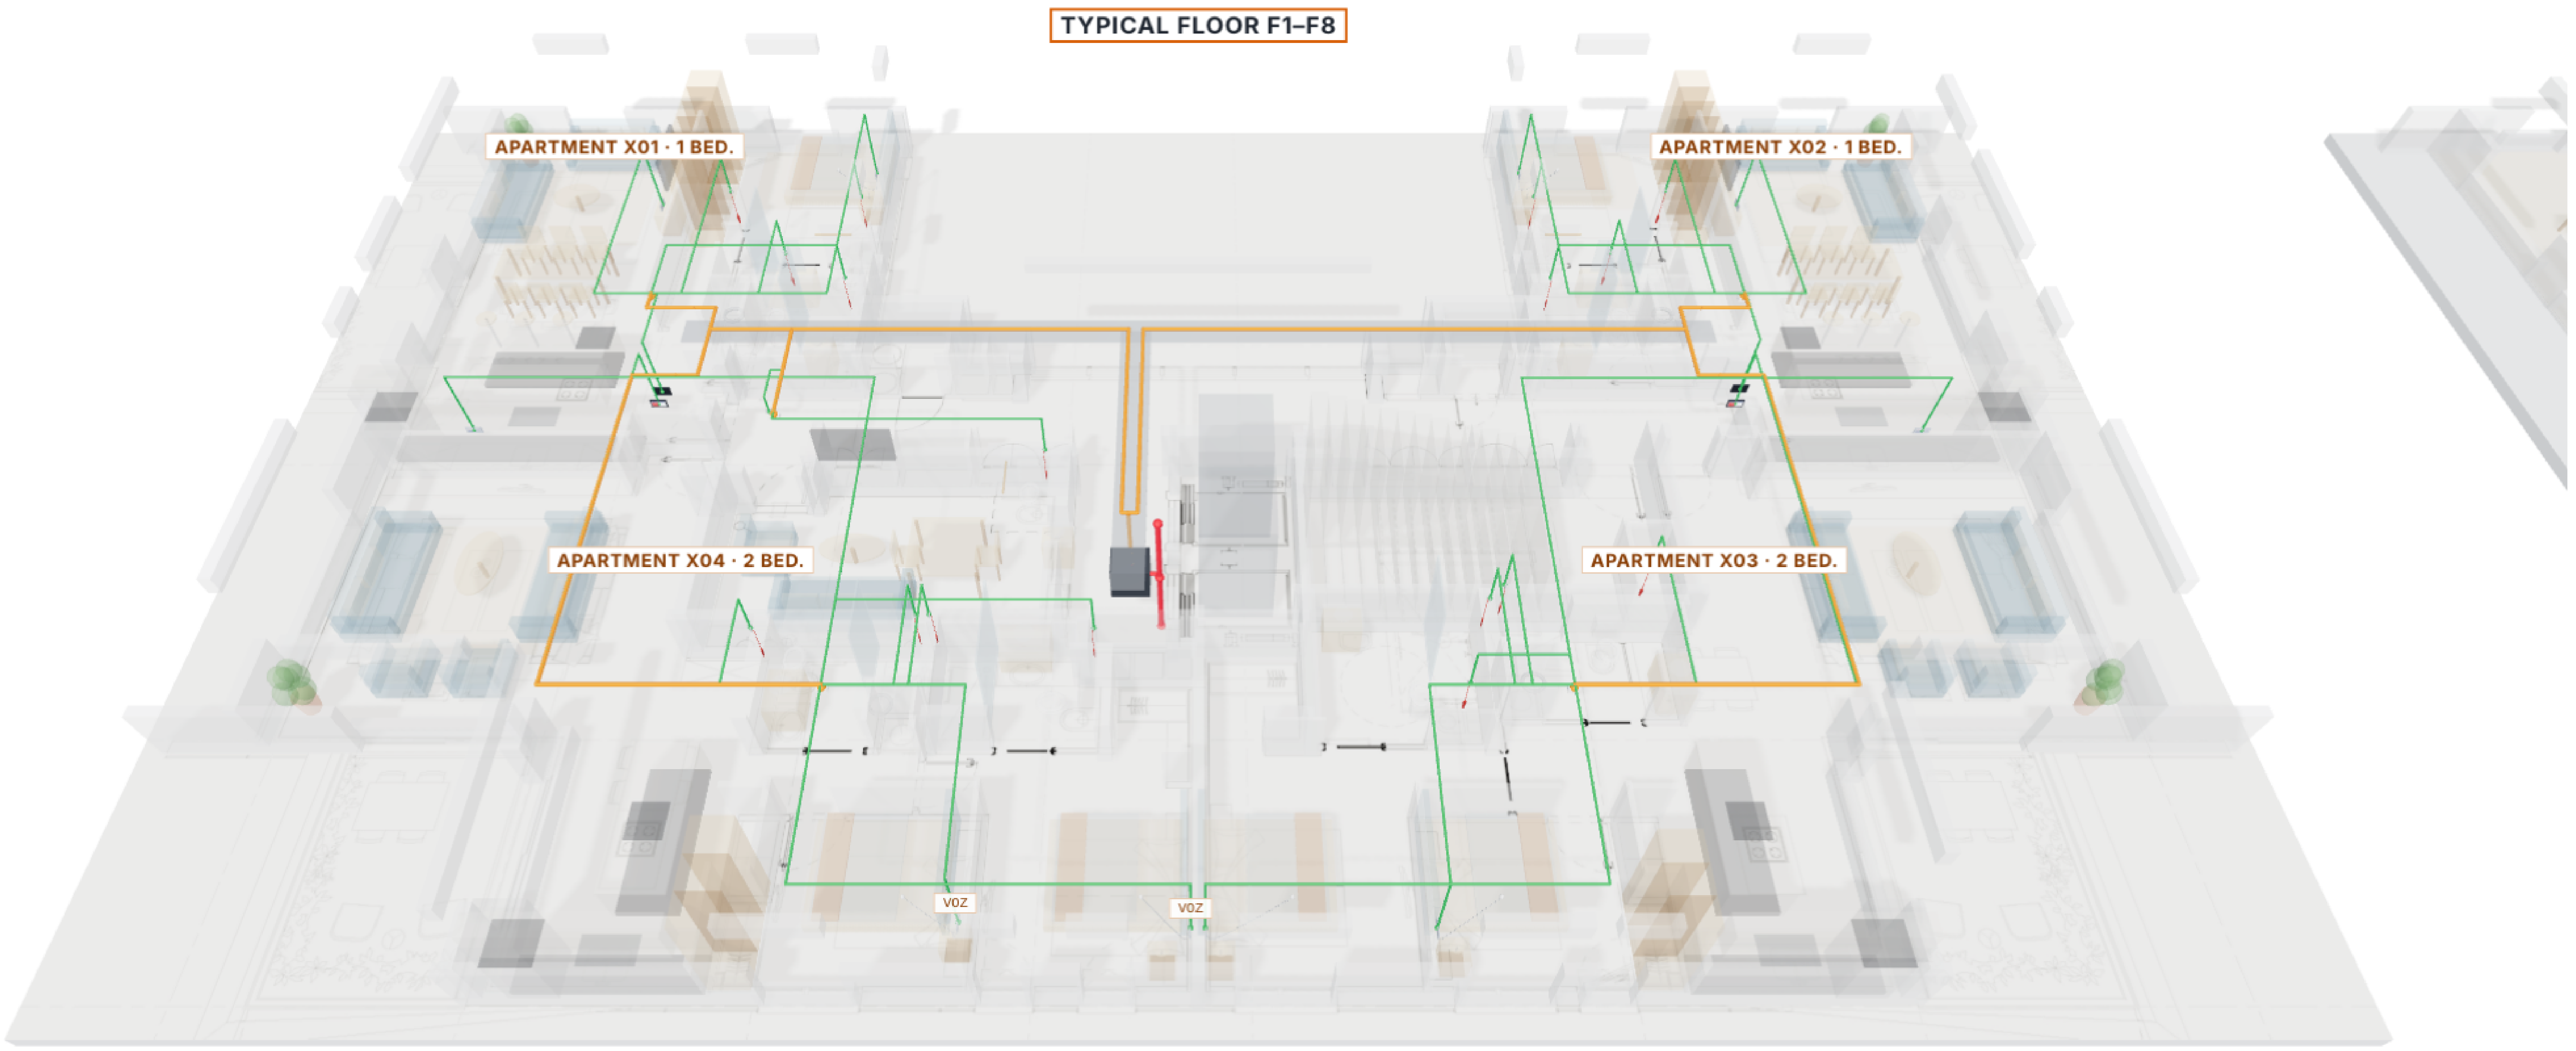
TYPICAL FLOOR F1–F8
APARTMENT X01 · 1 BED.
APARTMENT X02 · 1 BED.
APARTMENT X04 · 2 BED.
APARTMENT X03 · 2 BED.
VOZ
VOZ

A · Floor tipo – cableado (verde radial · naranja cadena LCom · rojo red)

GROUND FLOOR (GF)

B · Planta baja – lobby y recepción

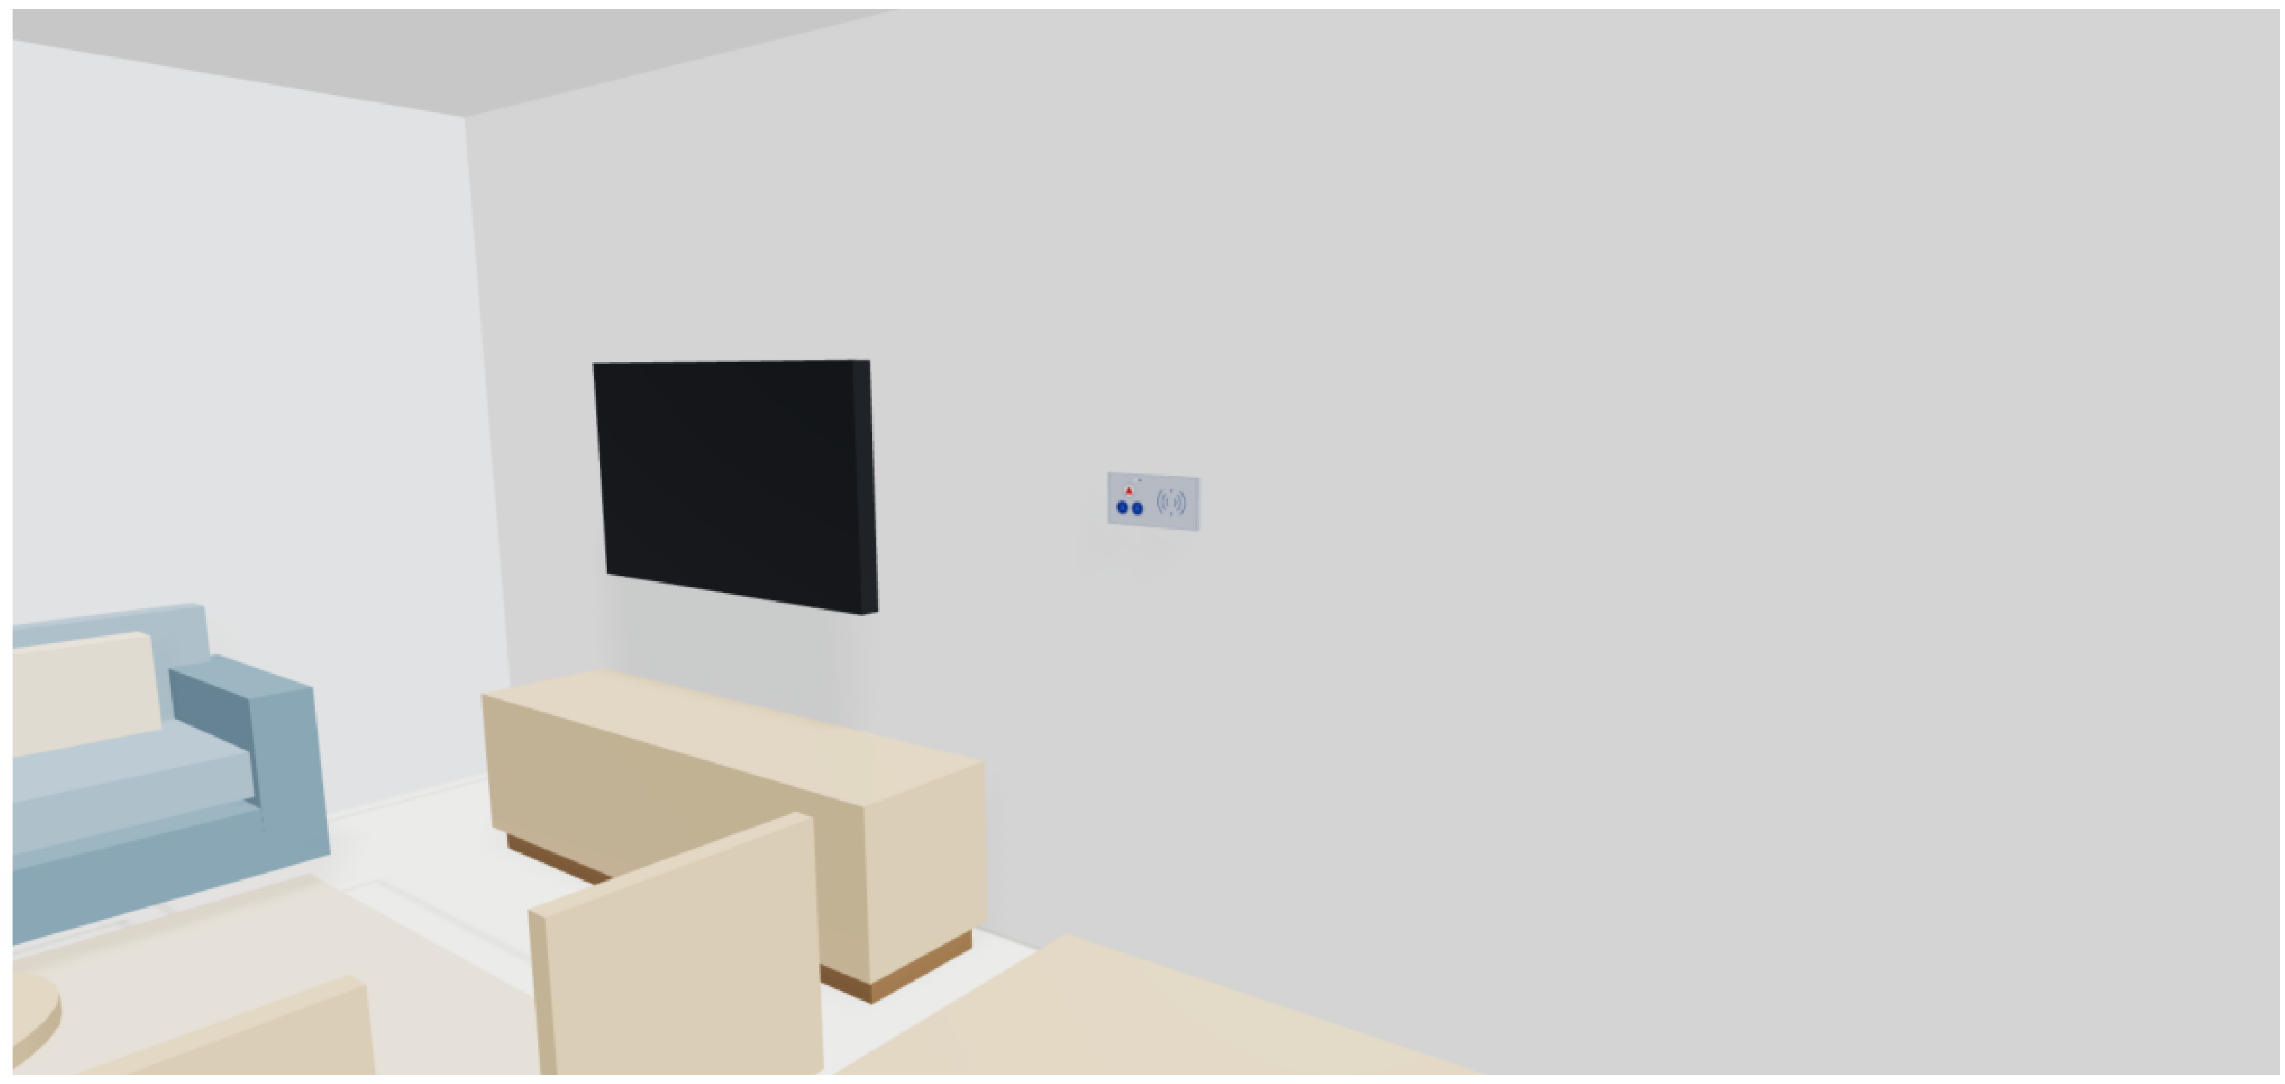

C · Salón – panel con voz y botones

**COLOURS · COLORES · צבעים**

| | |
|---|---|
| 🟩 | Cat6 radial: each device → its apartment LCom<br>Cat6 radial: each device → apartment LCom · Cat6 רדיאלי: כל התקן ← LCom של הדירה |
| 🟧 | Cat6 / Cat7 chain: LCom → LCom → rack Buscomm<br>Cat6 / Cat7 chain: LCom → LCom → Buscomm · Cat6 / Cat7 שרשרת: LCom ← LCom ← Buscomm |
| 🟥 | Cat6A / Cat7 network: Buscomm → switch → riser → GF server<br>Cat6A / Cat7 network: Buscomm → switch → riser → GF server · Cat6A / Cat7 רשת: Buscomm ← מתג ← עמוד ← שרת |

**MIGDALEI YAM A TIJON · ASSISTED LIVING**
Nurse call – GF + 8 floors · 32 apartments
System: ACE BG · Advantecnia Prepared by: Telab International

## 3D VIEWS – WIRING

| SCALE · ESCALA | DATE · FECHA | REV | SHEET |
|---|---|---|---|
| S/E | 15/10/2026 | B | 09 |

Base: architect's plan L5 (Massad Oz / Triplet) · dimensions in m
A1 format · Rev. B – on the real plan