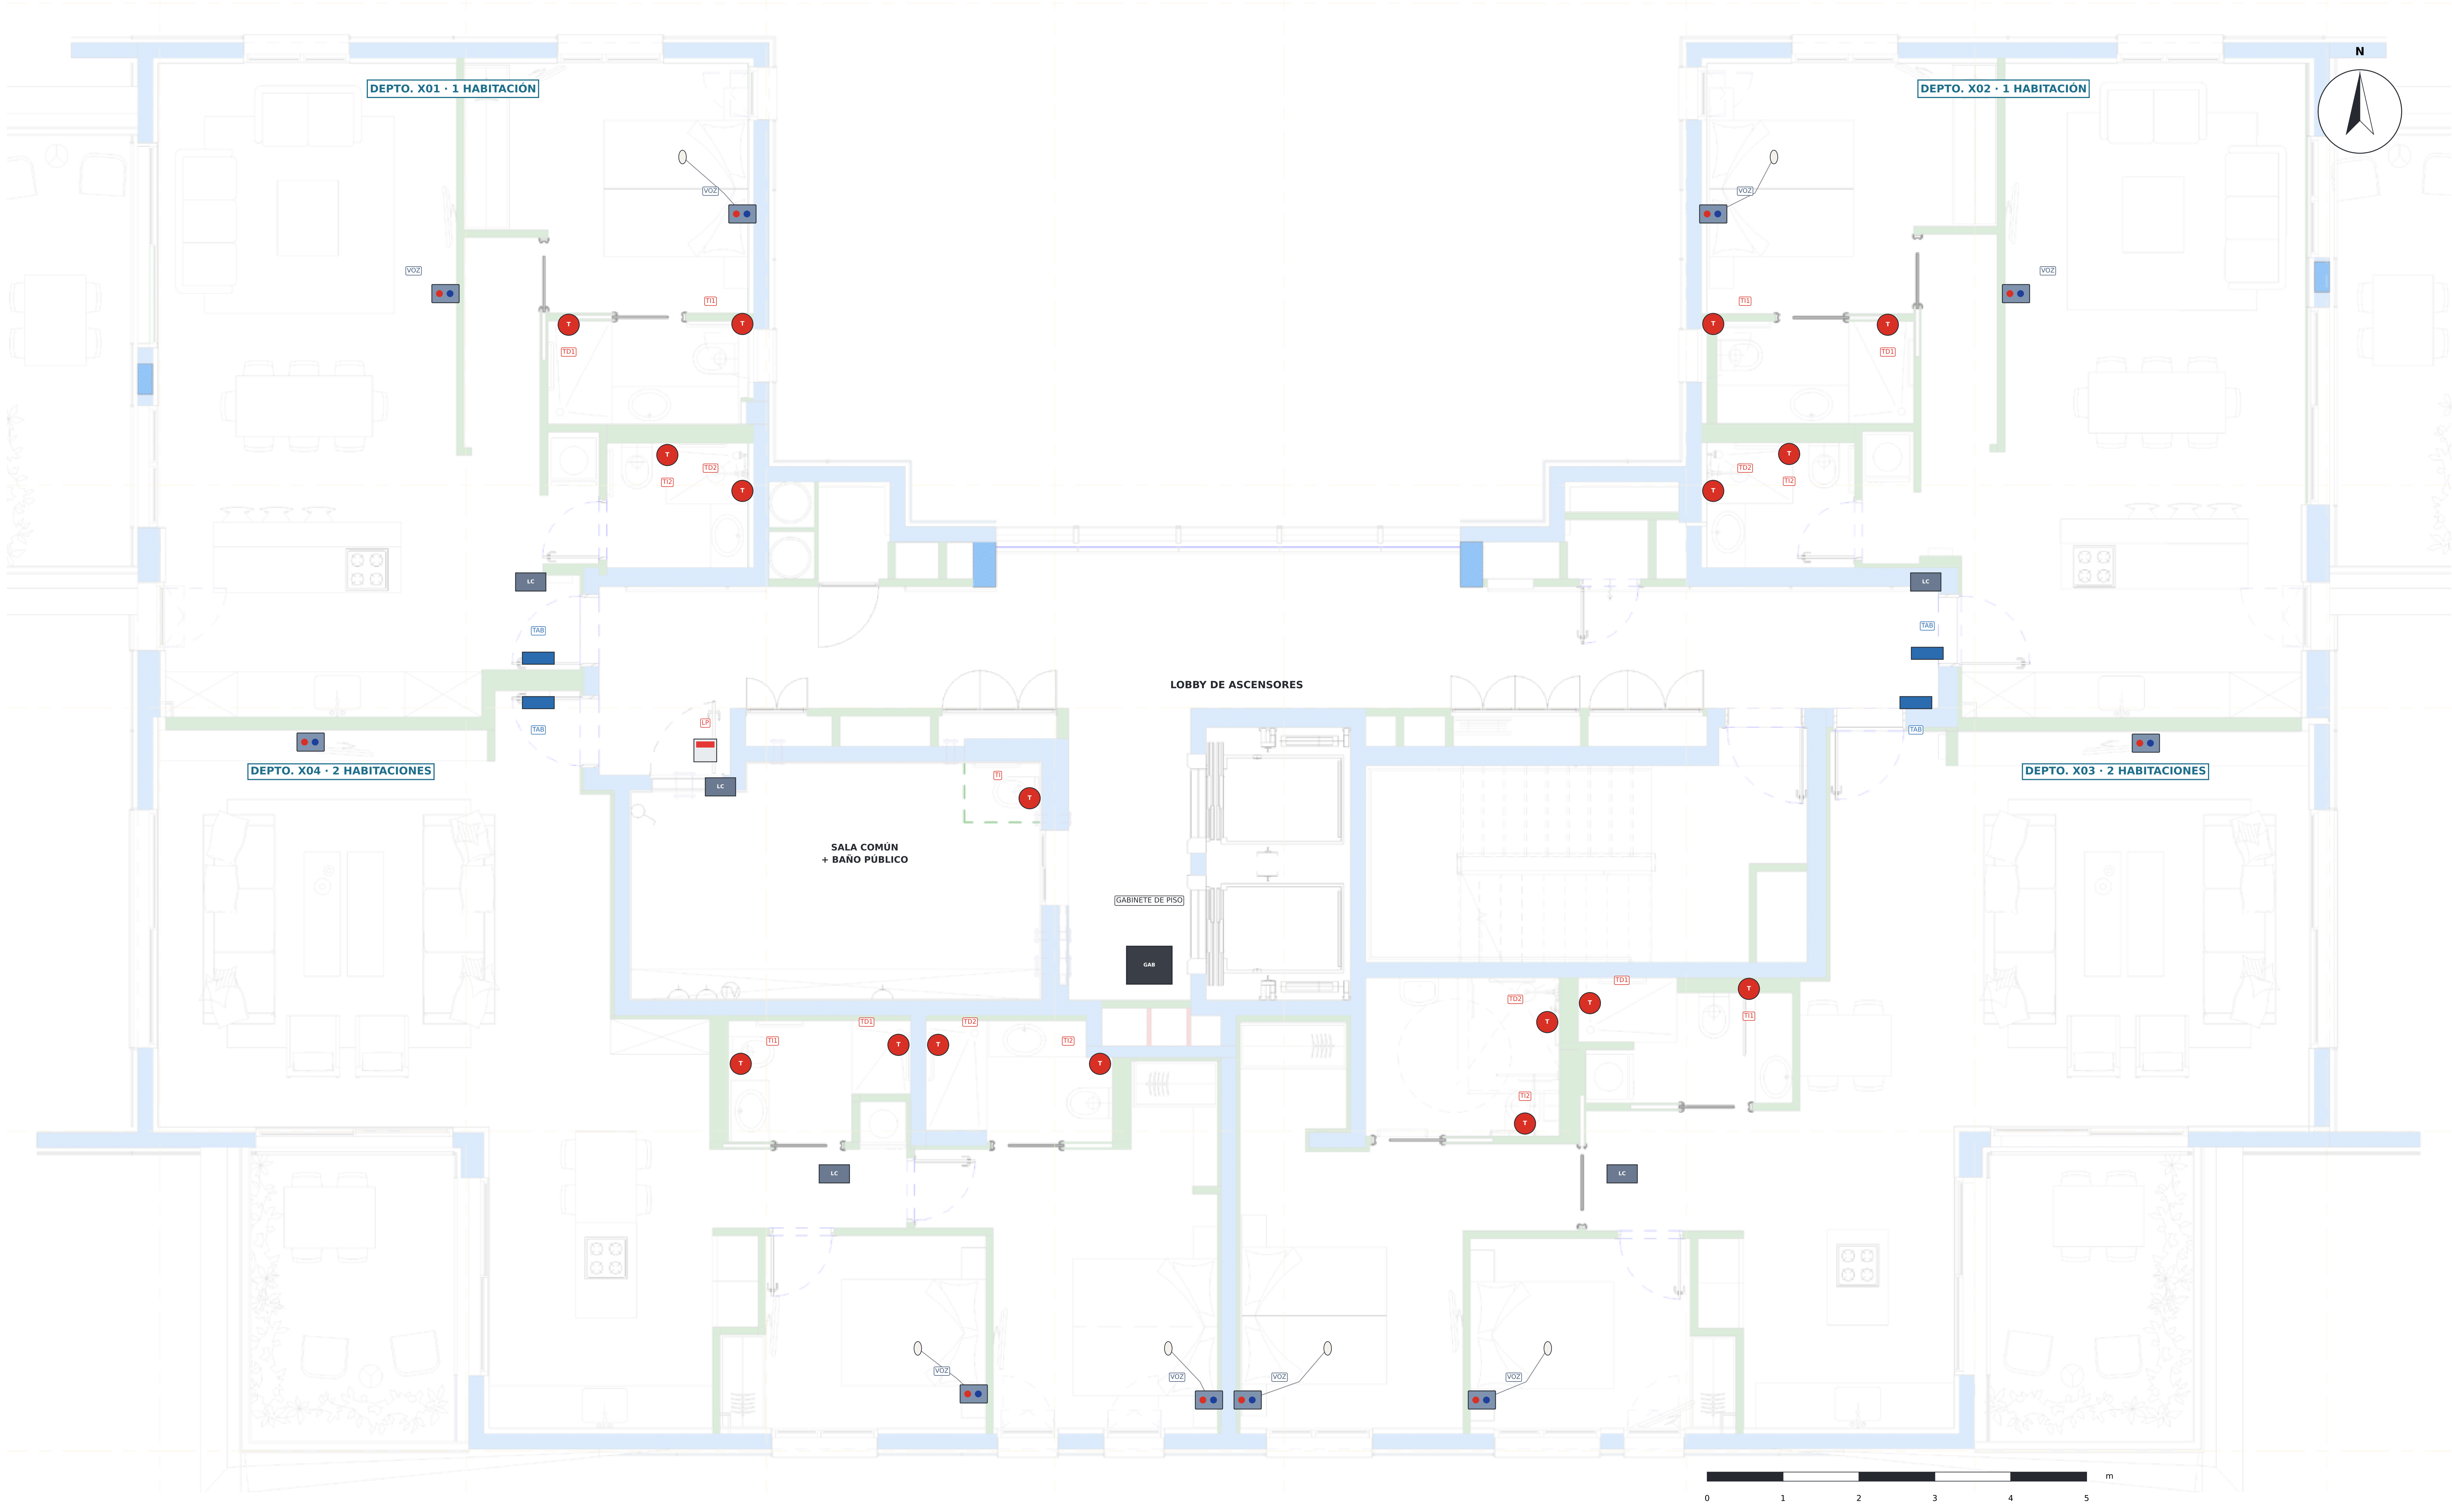
DEPTO. X01 · 1 HABITACIÓN
DEPTO. X02 · 1 HABITACIÓN
DEPTO. X04 · 2 HABITACIONES
DEPTO. X03 · 2 HABITACIONES
LOBBY DE ASCENSORES
SALA COMÚN
+ BAÑO PÚBLICO
GABINETE DE PISO
GAB
LC
TAB
VOZ
TI
TD
T
N
0
1
2
3
4
5
m

EQUIPOS · DEVICES · דויצ

🟦 TAB · Tablet de la puerta (iPad / Android) – llamada y voz, h 1,40 m
Door tablet – call and voice · טלבאט הסינככ – קראיה רובידו

VOZ · Panel con voz y botones ACE82182451 – salón y dormitorios, h 1,20–1,30 m
Voice panel with buttons – living room and bedrooms · פנל קולוי עם לחצנים – סלון וחדרי שינה

Pera de llamada junto a la cama (en los dormitorios)
Call pear next to the bed (bedrooms) · אגס קריאה ליד המיטה

T TI / TD · Tirador de baño ACE40320303W – inodoro y ducha, h 1,85 m
Pull-cord – toilet and shower, h 1.85 m · משיכת חבל – אסלה ומקלחת, גובה 1.85 מ'

LP · Luz de pasillo ACE41020309 – sobre la puerta de cada baño público
Corridor light – above each public toilet door · נורת מסדרון – מעל דלת כל שירותים ציבוריים

LC LC · LCom ACE71610003 – concentrador del departamento (cielorraso)
LCom – apartment hub (ceiling) · LCom – מרכז הדירה (תקרה)

GAB Gabinete de piso 12U: 2 Buscomm ACE70810000 + switch PoE ACEUCM6302
Floor rack: 2 Buscomm + PoE switch · ארון קומה: 2 Buscomm + מתג PoE

CANTIDADES POR PISO × 8 PISOS

Código	Equipo	Por piso	8 pisos
TAB	Tablet de la puerta	4	32
VOZ	Panel con voz y botones	10	80
TI/TD	Tirador de baño (inodoro + ducha)	17	136
LP	Luz de pasillo (baño público)	1	8
LC	LCom	5	40
BC	Buscomm	2	16
SW	Switch PoE	1	8

NOTAS · NOTES

1. Base: plano de arquitectura L5 (piso tipo) – los 8 pisos son iguales: 4 departamentos por piso, 32 en total.
2. Departamentos x01 y x02: 1 habitación, salón con cocina y 2 baños. Departamentos x03 y x04: 2 habitaciones y 2 baños.
3. Tablet en la puerta de cada departamento (iPad / Android) para llamar y hablar con enfermería.
4. Panel con voz y botones (ACE82182451) en el salón y en cada dormitorio; en el dormitorio, con pera junto a la cama.
5. Tiradores de baño (ACE40320303W) en el inodoro y en la ducha de todos los baños, a 1,85 m.
6. Baño público por piso en la sala común: tirador + luz de pasillo sobre la puerta. Con los 2 de PB suman 10 baños públicos.
7. Gabinete de piso en el pasillo de servicio junto a los ascensores (Tripp Lite 12U, como en el plano IT).
8. Ubicaciones de anteproyecto: confirmar en obra con el instalador y con Advantecnia.

ALTURAS DE MONTAJE

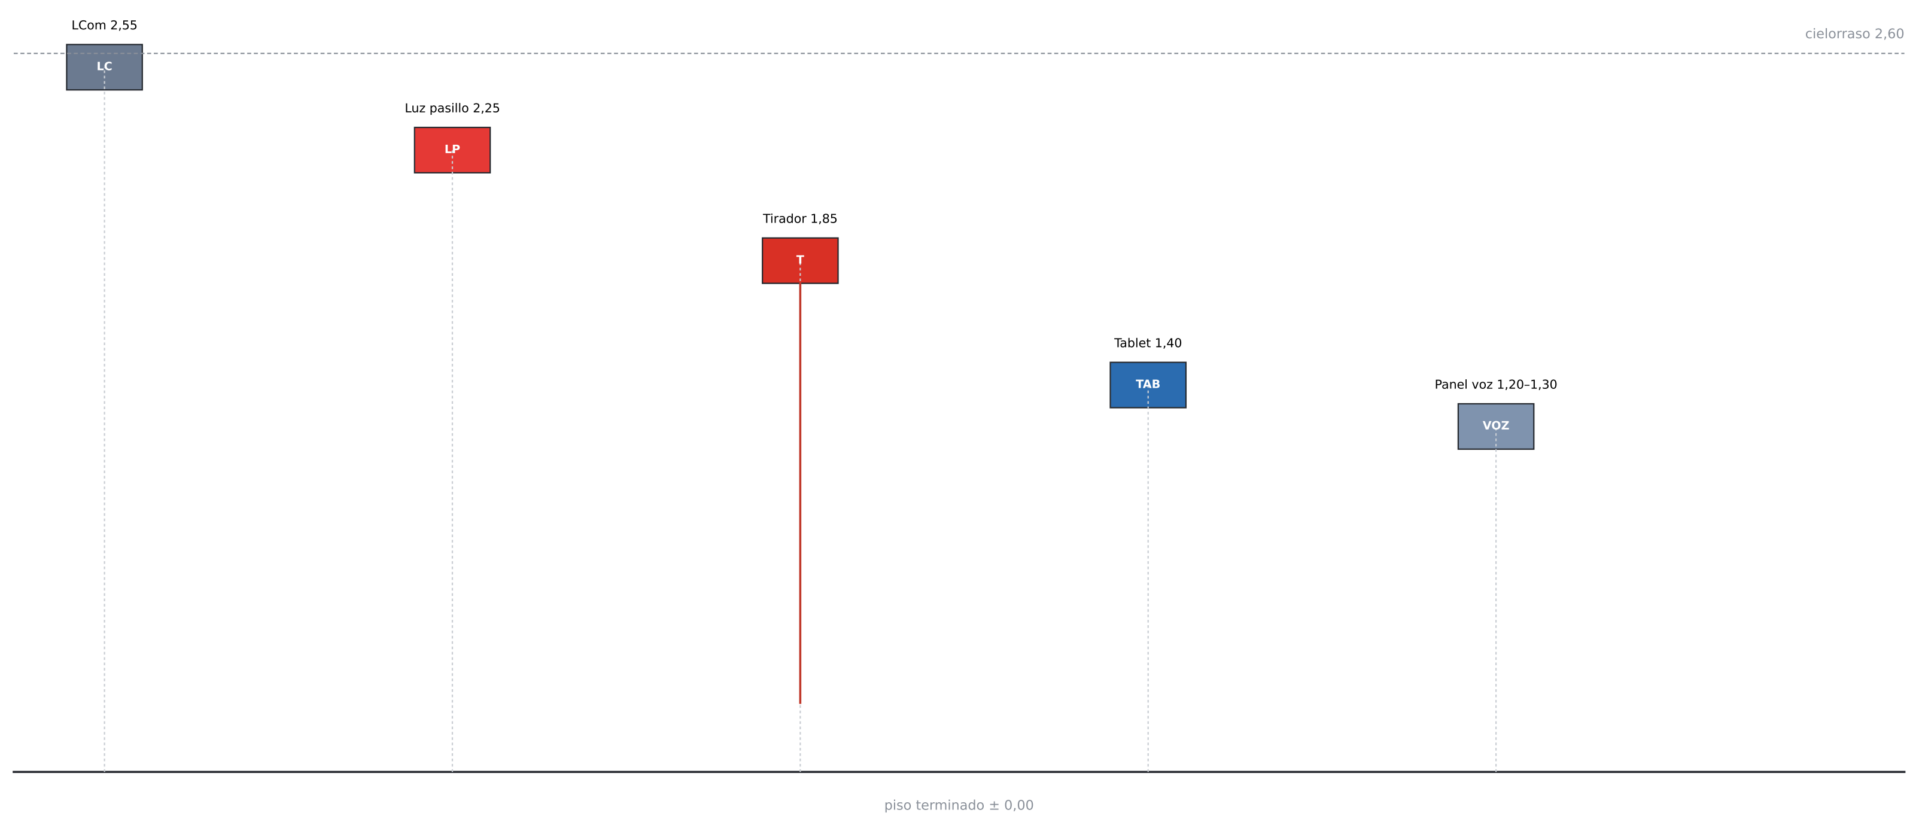

MIGDALEI YAM A TIJON · VIVIENDA TUTELADA

Llamada de enfermería – PB + 8 pisos · 32 departamentos

Sistema: ACE BG · Advantecnia   Elaboró: Telab International

PISO TIPO P1–P8 · LLAMADA DE ENFERMERÍA

Typical floor F1–F8 · nurse call

ESCALA · SCALE	FECHA · DATE	REV	LÁMINA
1:60	15/10/2026	B	01

Base: plano del arquitecto L5 (Massad Oz / Triplet) · cotas en metros

Formato A1 · Rev. B – sobre plano real

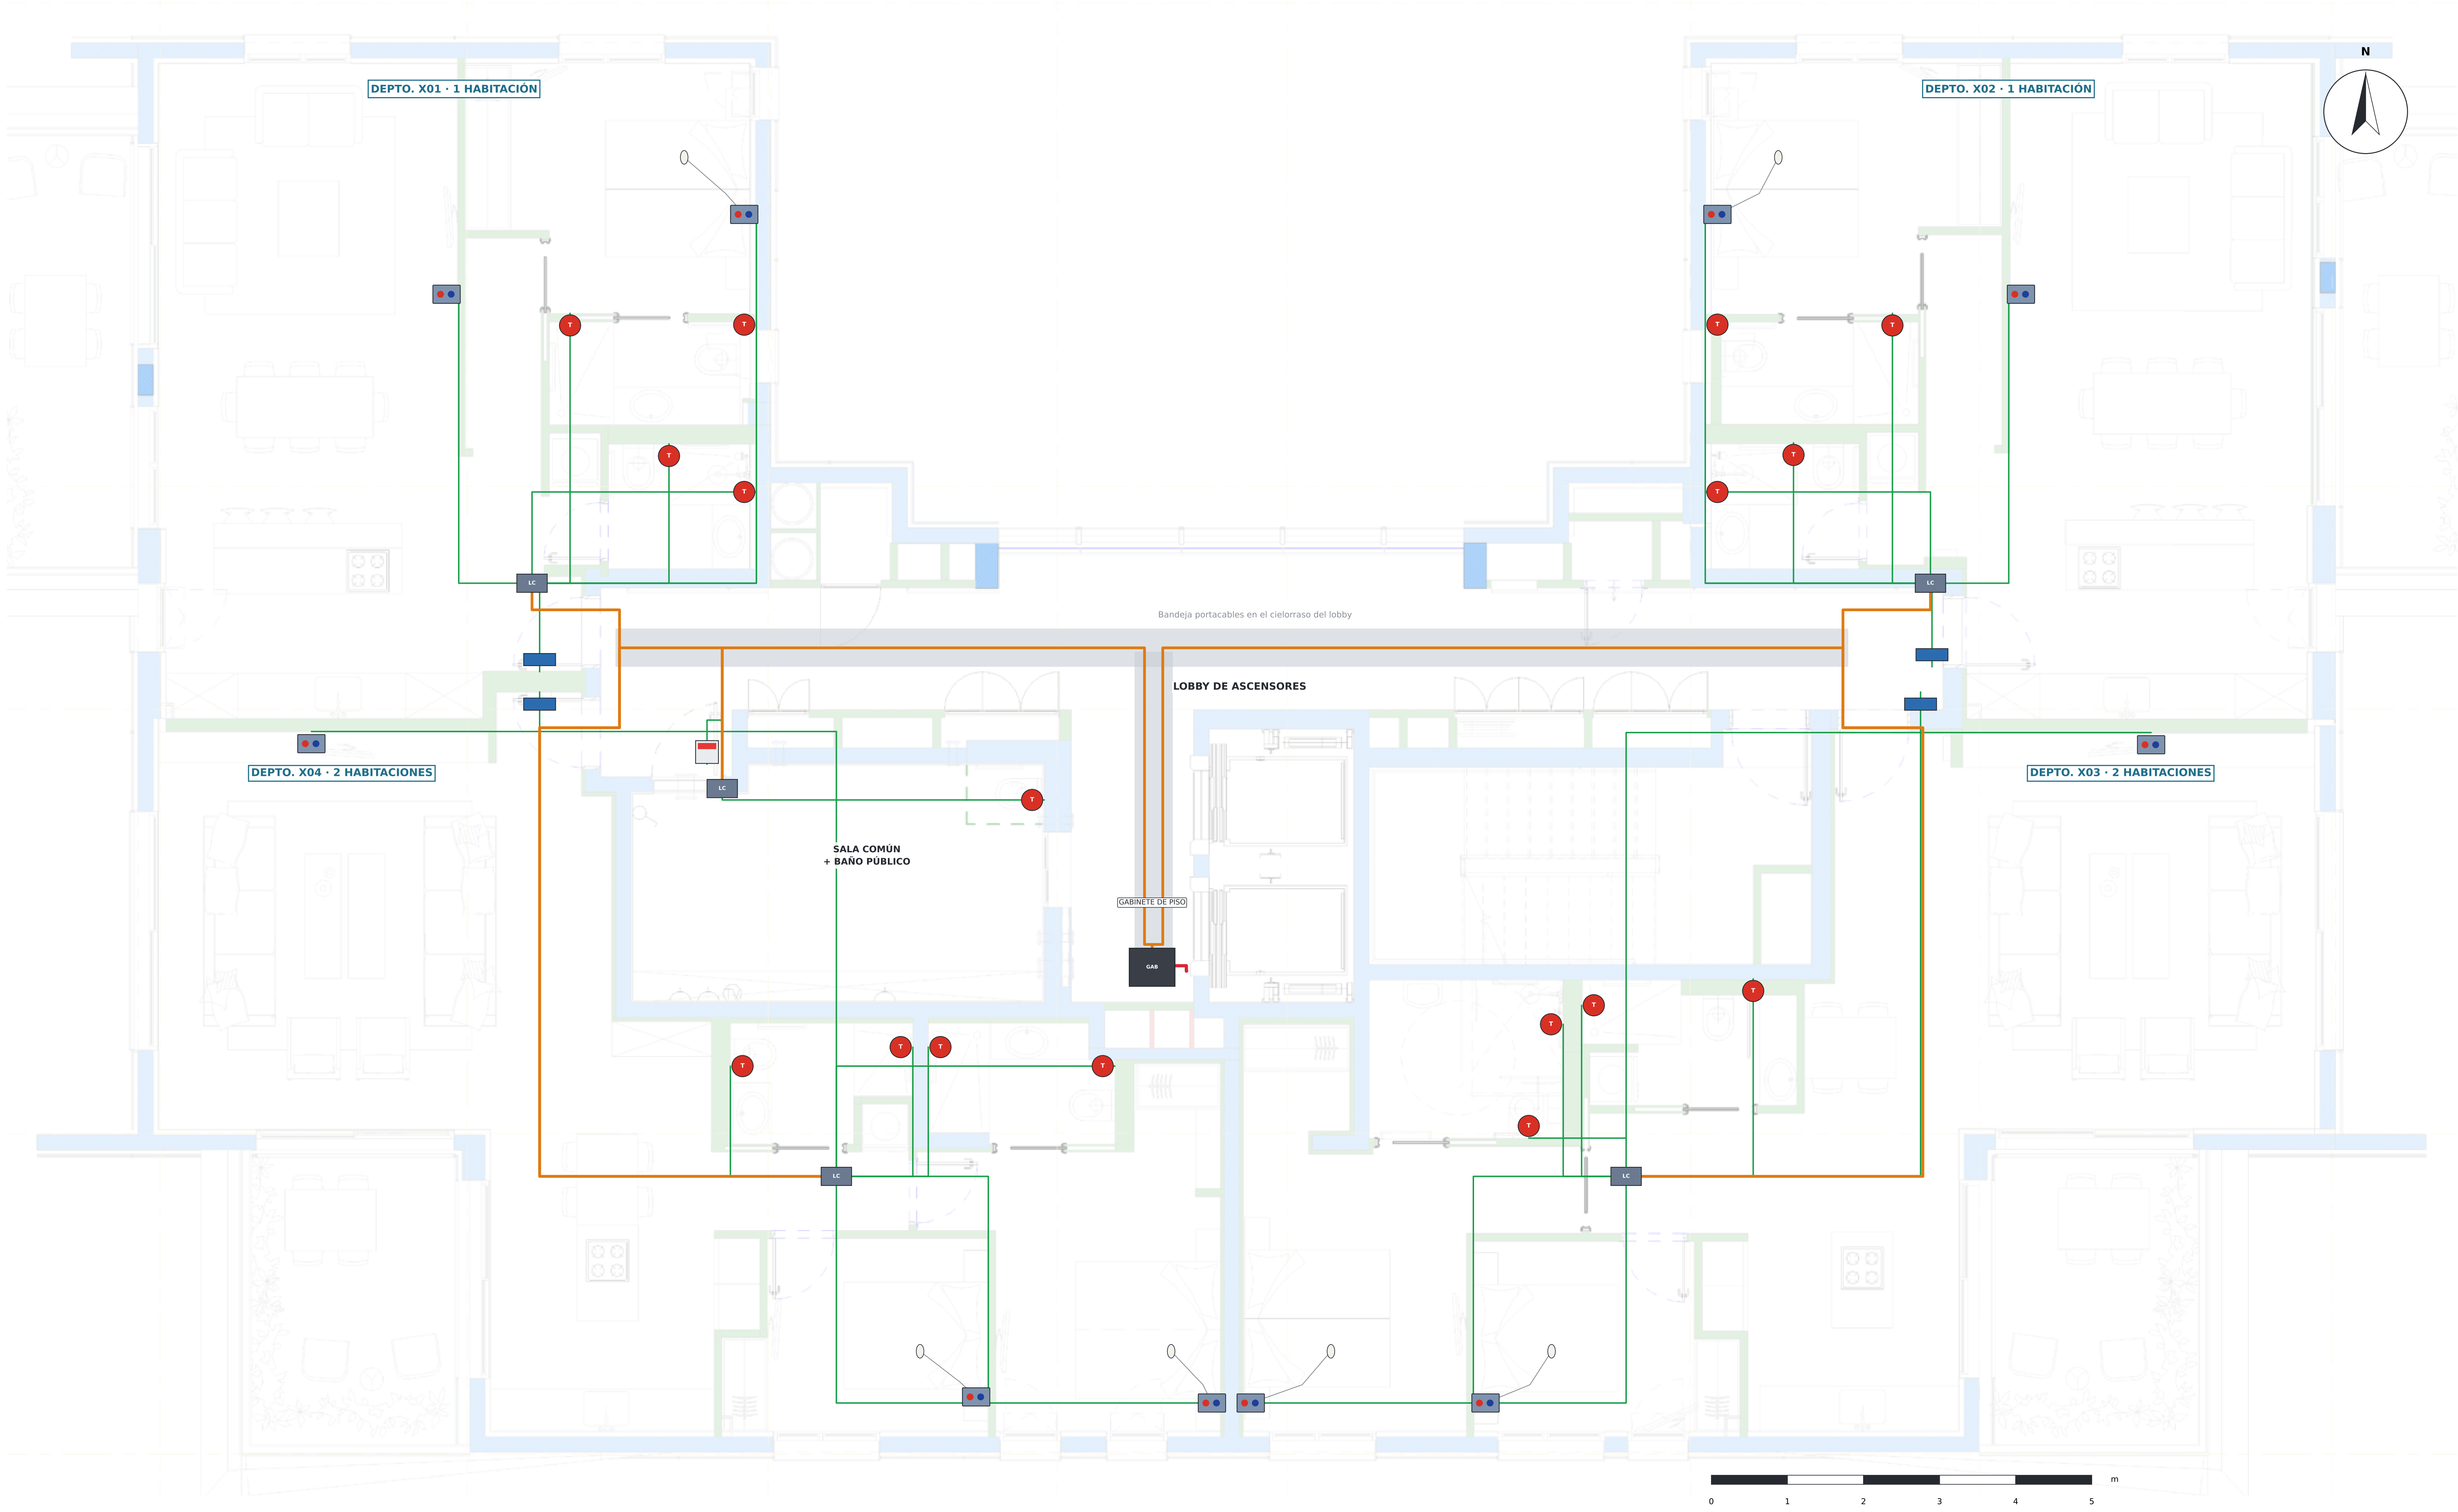
DEPTO. X01 · 1 HABITACIÓN
DEPTO. X02 · 1 HABITACIÓN
N
Bandeja portacables en el cielorraso del lobby
LC
LOBBY DE ASCENSORES
DEPTO. X04 · 2 HABITACIONES
DEPTO. X03 · 2 HABITACIONES
SALA COMÚN
+ BAÑO PÚBLICO
GABINETE DE PISO
GAB
T
0
1
2
3
4
5
m

CABLEADO · WIRING · חיווט

🟩 Cat6 radial: cada equipo → LCom de su departamento
Cat6 radial: each device → apartment LCom · Cat6 רדיאלי: כל התקן ← LCom של הדירה

🟧 Cat6 / Cat7 cadena: LCom → LCom → Buscomm del gabinete
Cat6 / Cat7 chain: LCom → LCom → Buscomm · Cat6 / Cat7 שרשרת: LCom ← LCom ← Buscomm

🟥 Cat6A / Cat7 red: Buscomm → switch → montante → servidor PB
Cat6A / Cat7 network: Buscomm → switch → riser → GF server · Cat6A / Cat7 רשת: Buscomm ← מתג ← עמוד ← שרת

LONGITUDES DEL PISO TIPO (sin reserva)

🟩	Cat6 radial dentro de los departamentos	**202 m**
🟧	Cat6 / Cat7 cadena LCom → Buscomm	**82 m**
🟥	Cat6A / Cat7 gabinete y montante	**4 m**

NOTAS · NOTES

1. Cada equipo va radial (Cat6) al LCom de su departamento, en el cielorraso del hall.
2. Los LCom se encadenan por la bandeja del lobby hasta el gabinete del piso: x01 → x04 → sala común → Buscomm 1 · x02 → x03 → Buscomm 2.
3. El switch PoE del piso sube por el montante Cat6A / Cat7 hasta el servidor de PB.
4. Todo es PoE: no hace falta 230 V en los equipos de los departamentos.

NOTAS · NOTES

1. Base: plano de arquitectura L5 (piso tipo) – los 8 pisos son iguales: 4 departamentos por piso, 32 en total.
2. Departamentos x01 y x02: 1 habitación, salón con cocina y 2 baños. Departamentos x03 y x04: 2 habitaciones y 2 baños.
3. Tablet en la puerta de cada departamento (iPad / Android) para llamar y hablar con enfermería.
4. Panel con voz y botones (ACE82182451) en el salón y en cada dormitorio; en el dormitorio, con pera junto a la cama.
5. Tiradores de baño (ACE40320303W) en el inodoro y en la ducha de todos los baños, a 1,85 m.
6. Baño público por piso en la sala común: tirador + luz de pasillo sobre la puerta. Con los 2 de PB suman 10 baños públicos.
7. Gabinete de piso en el pasillo de servicio junto a los ascensores (Tripp Lite 12U, como en el plano IT).
8. Ubicaciones de anteproyecto: confirmar en obra con el instalador y con Advantecnia.

MIGDALEI YAM A TIJON · VIVIENDA TUTELADA
Llamada de enfermería – PB + 8 pisos · 32 departamentos
Sistema: ACE BG · Advantecnia   Elaboró: Telab International

PISO TIPO P1–P8 · CABLEADO

Typical floor F1–F8 · wiring

ESCALA · SCALE	FECHA · DATE	REV	LÁMINA
1:60	**15/10/2026**	**B**	**02**

Base: plano del arquitecto L5 (Massad Oz / Triplet) · cotas en metros
Formato A1 · Rev. B – sobre plano real

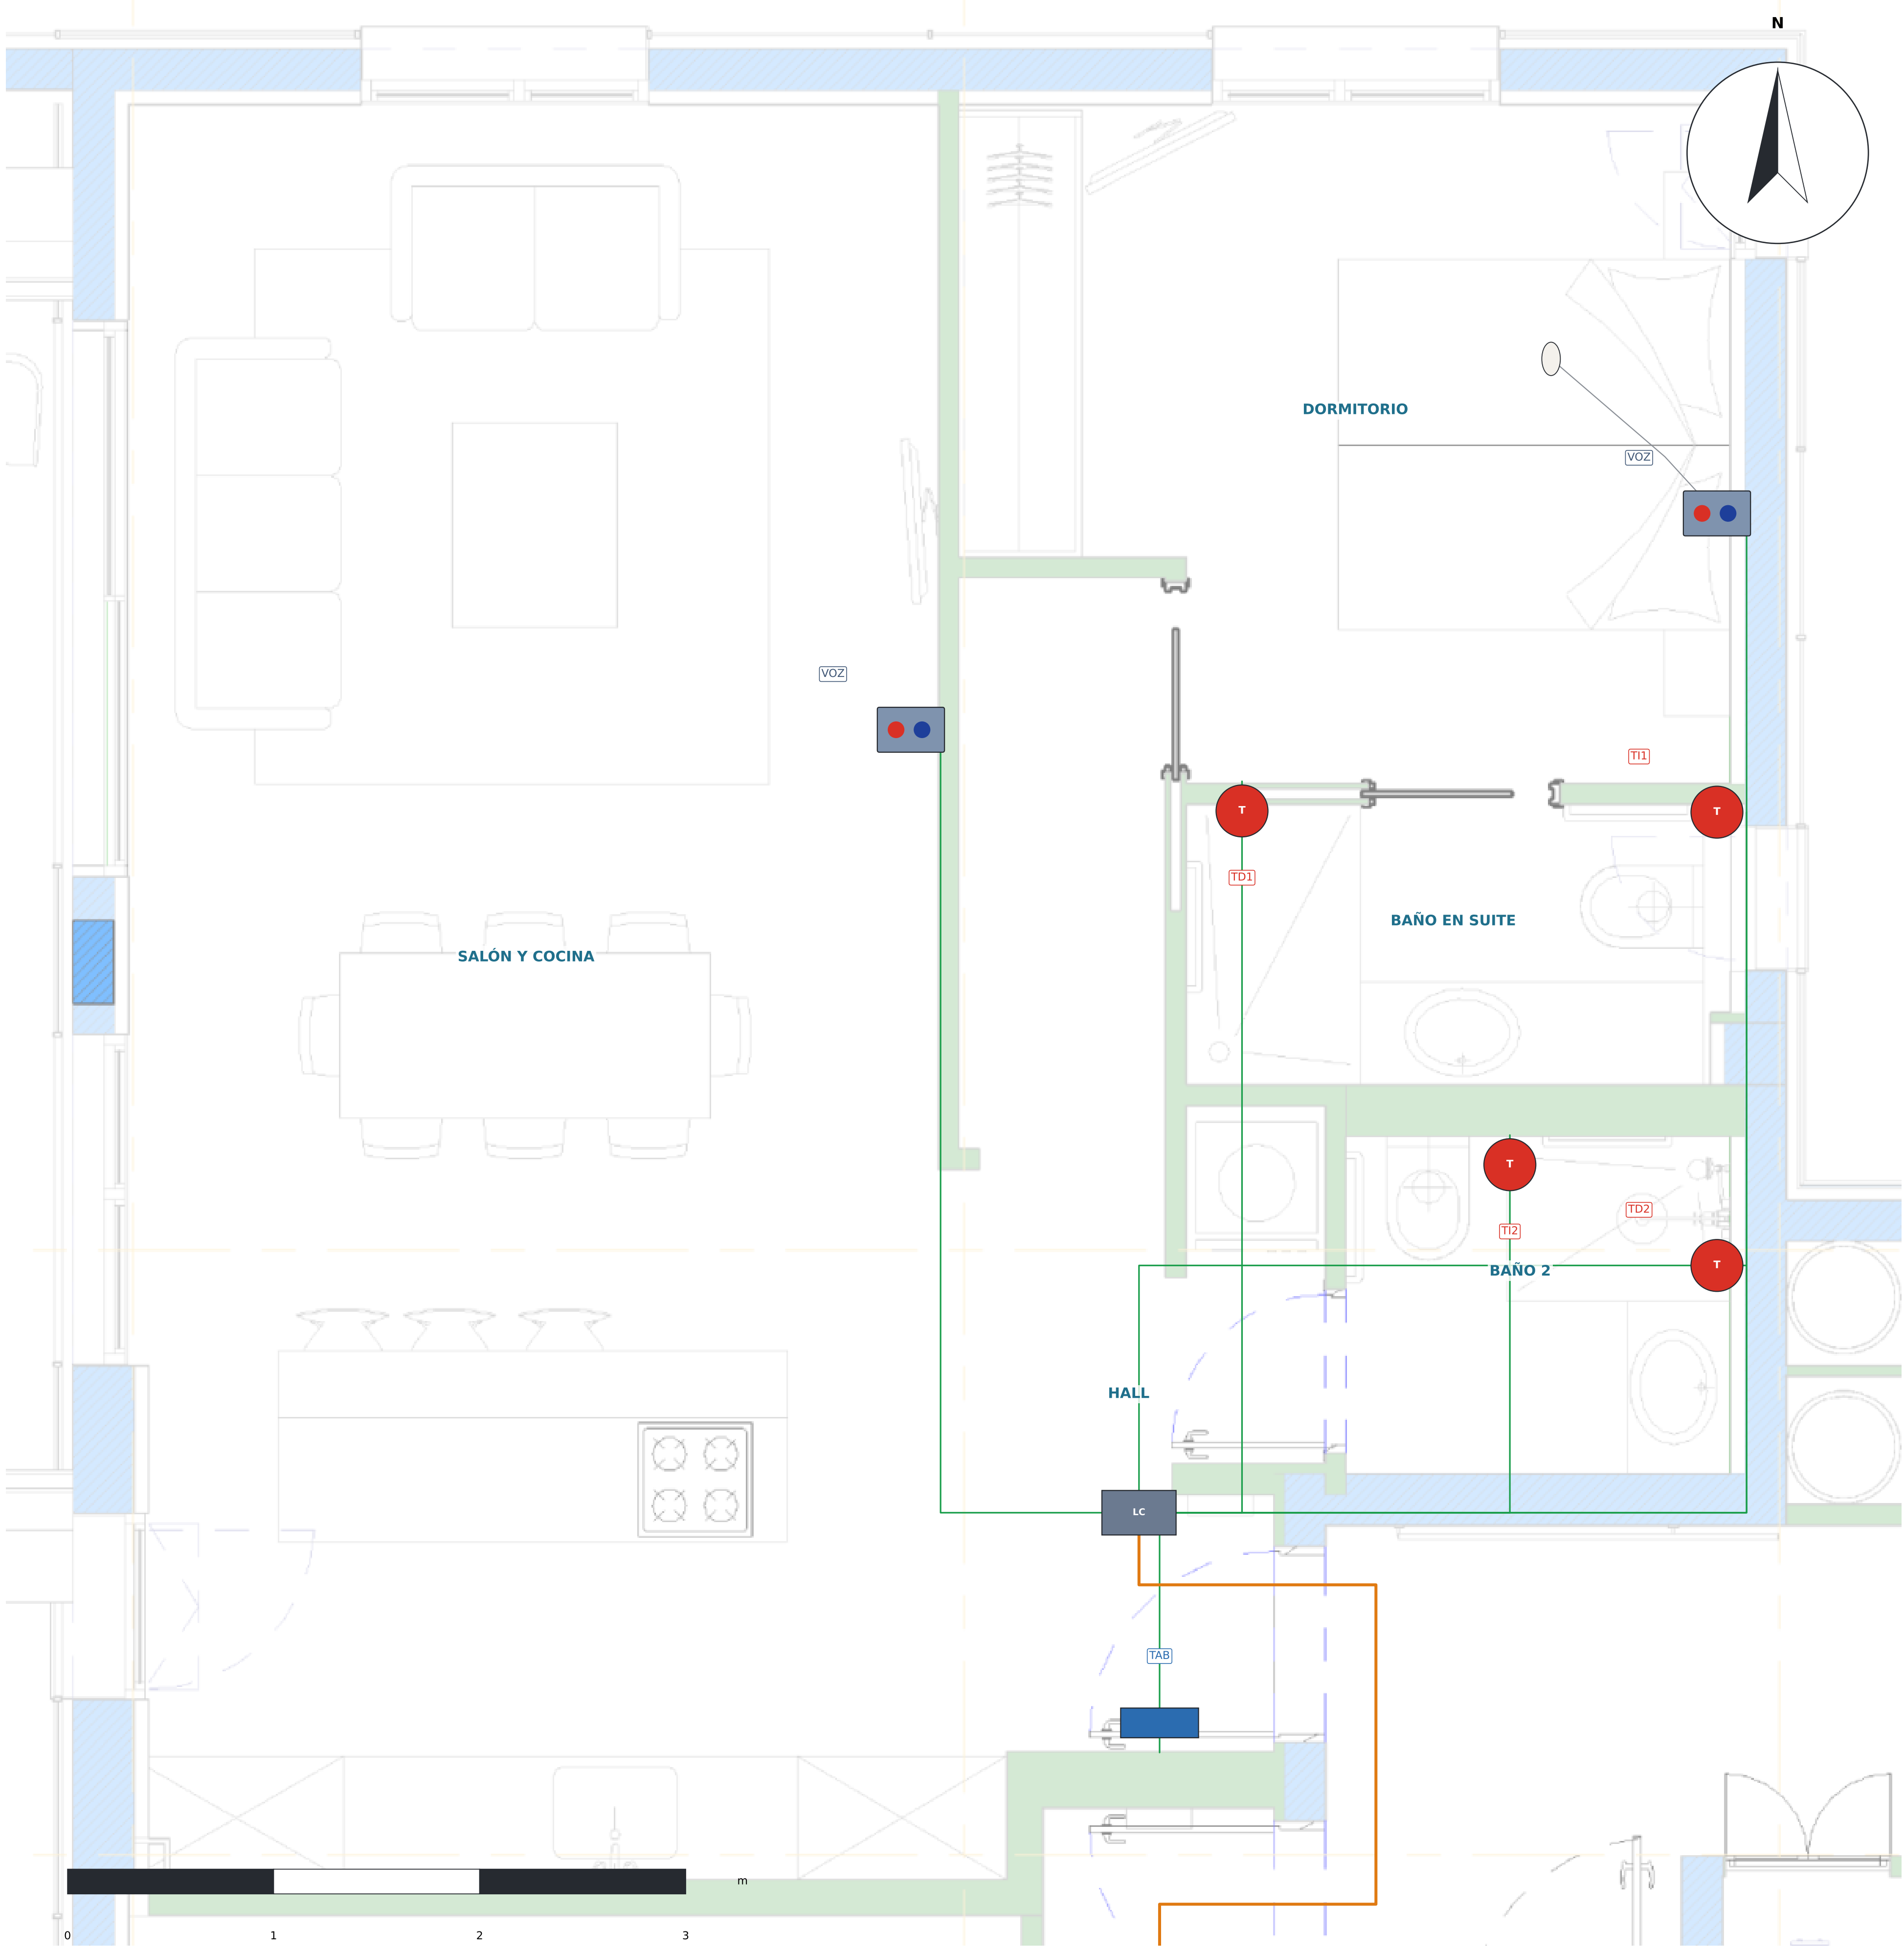

EQUIPOS DEL DEPARTAMENTO

ID	Equipo	Local	Altura
TAB	Tablet de la puerta	Hall	1,40 m
VOZ-S	Panel voz y botones	Salón y cocina	1,30 m
VOZ-D	Panel voz y botones + pera	Dormitorio	1,20 m
TI1	Tirador de baño	Baño en suite	1,85 m
TD1	Tirador de baño	Baño en suite	1,85 m
TI2	Tirador de baño	Baño 2	1,85 m
TD2	Tirador de baño	Baño 2	1,85 m
LCOM	LCom ACE71610003	Hall	2,55 m

SÍMBOLOS · SYMBOLS · םילמס

🟦	TAB · Tablet de la puerta (iPad / Android) – llamada y voz, h 1,40 m Door tablet – call and voice · רובידו האירק – הסינכב טלבאט
●●	VOZ · Panel con voz y botones ACE82182451 – salón y dormitorios, h 1,20–1,30 m Voice panel with buttons – living room and bedrooms · הניש ירדחו ןולס – םינצחל םע ילוק לנפ
○	Pera de llamada junto a la cama (en los dormitorios) Call pear next to the bed (bedrooms) · הטימה דיל האירק סגא
T	TI / TD · Tirador de baño ACE40320303W – inodoro y ducha, h 1,85 m Pull-cord – toilet and shower, h 1.85 m · 'מ 1.85 הבוג ,תחלקמו הלסא – לבח תכישמ
🟥	LP · Luz de pasillo ACE41020309 – sobre la puerta de cada baño público Corridor light – above each public toilet door · םיירוביצ םיתוריש לכ תלד לעמ – ןורדסמ תרונמ
LC	LC · LCom ACE71610003 – concentrador del departamento (cielorraso) LCom – apartment hub (ceiling) · LCom – הרידה זכרמ (הרקת)

NOTAS · NOTES

1. El departamento x02 es el espejo del x01 (misma dotación).
2. Tablet en el hall junto a la puerta de entrada.
3. Panel con voz en el salón y en el dormitorio (con pera junto a la cama).
4. 2 baños: tirador en el inodoro y en la ducha de cada uno (4 tiradores).
5. Todo va radial en Cat6 al LCom del hall.

MIGDALEI YAM A TIJON · VIVIENDA TUTELADA

Llamada de enfermería – PB + 8 pisos · 32 departamentos

Sistema: ACE BG · Advantecnia Elaboró: Telab International

DEPTO. 1 HABITACIÓN (x01 / x02)

1-bedroom apartment (x01 / x02)

ESCALA · SCALE	FECHA · DATE	REV	LÁMINA
1:30	**15/10/2026**	**B**	**03**

Base: plano del arquitecto L5 (Massad Oz / Triplet) · cotas en metros

Formato A1 · Rev. B – sobre plano real

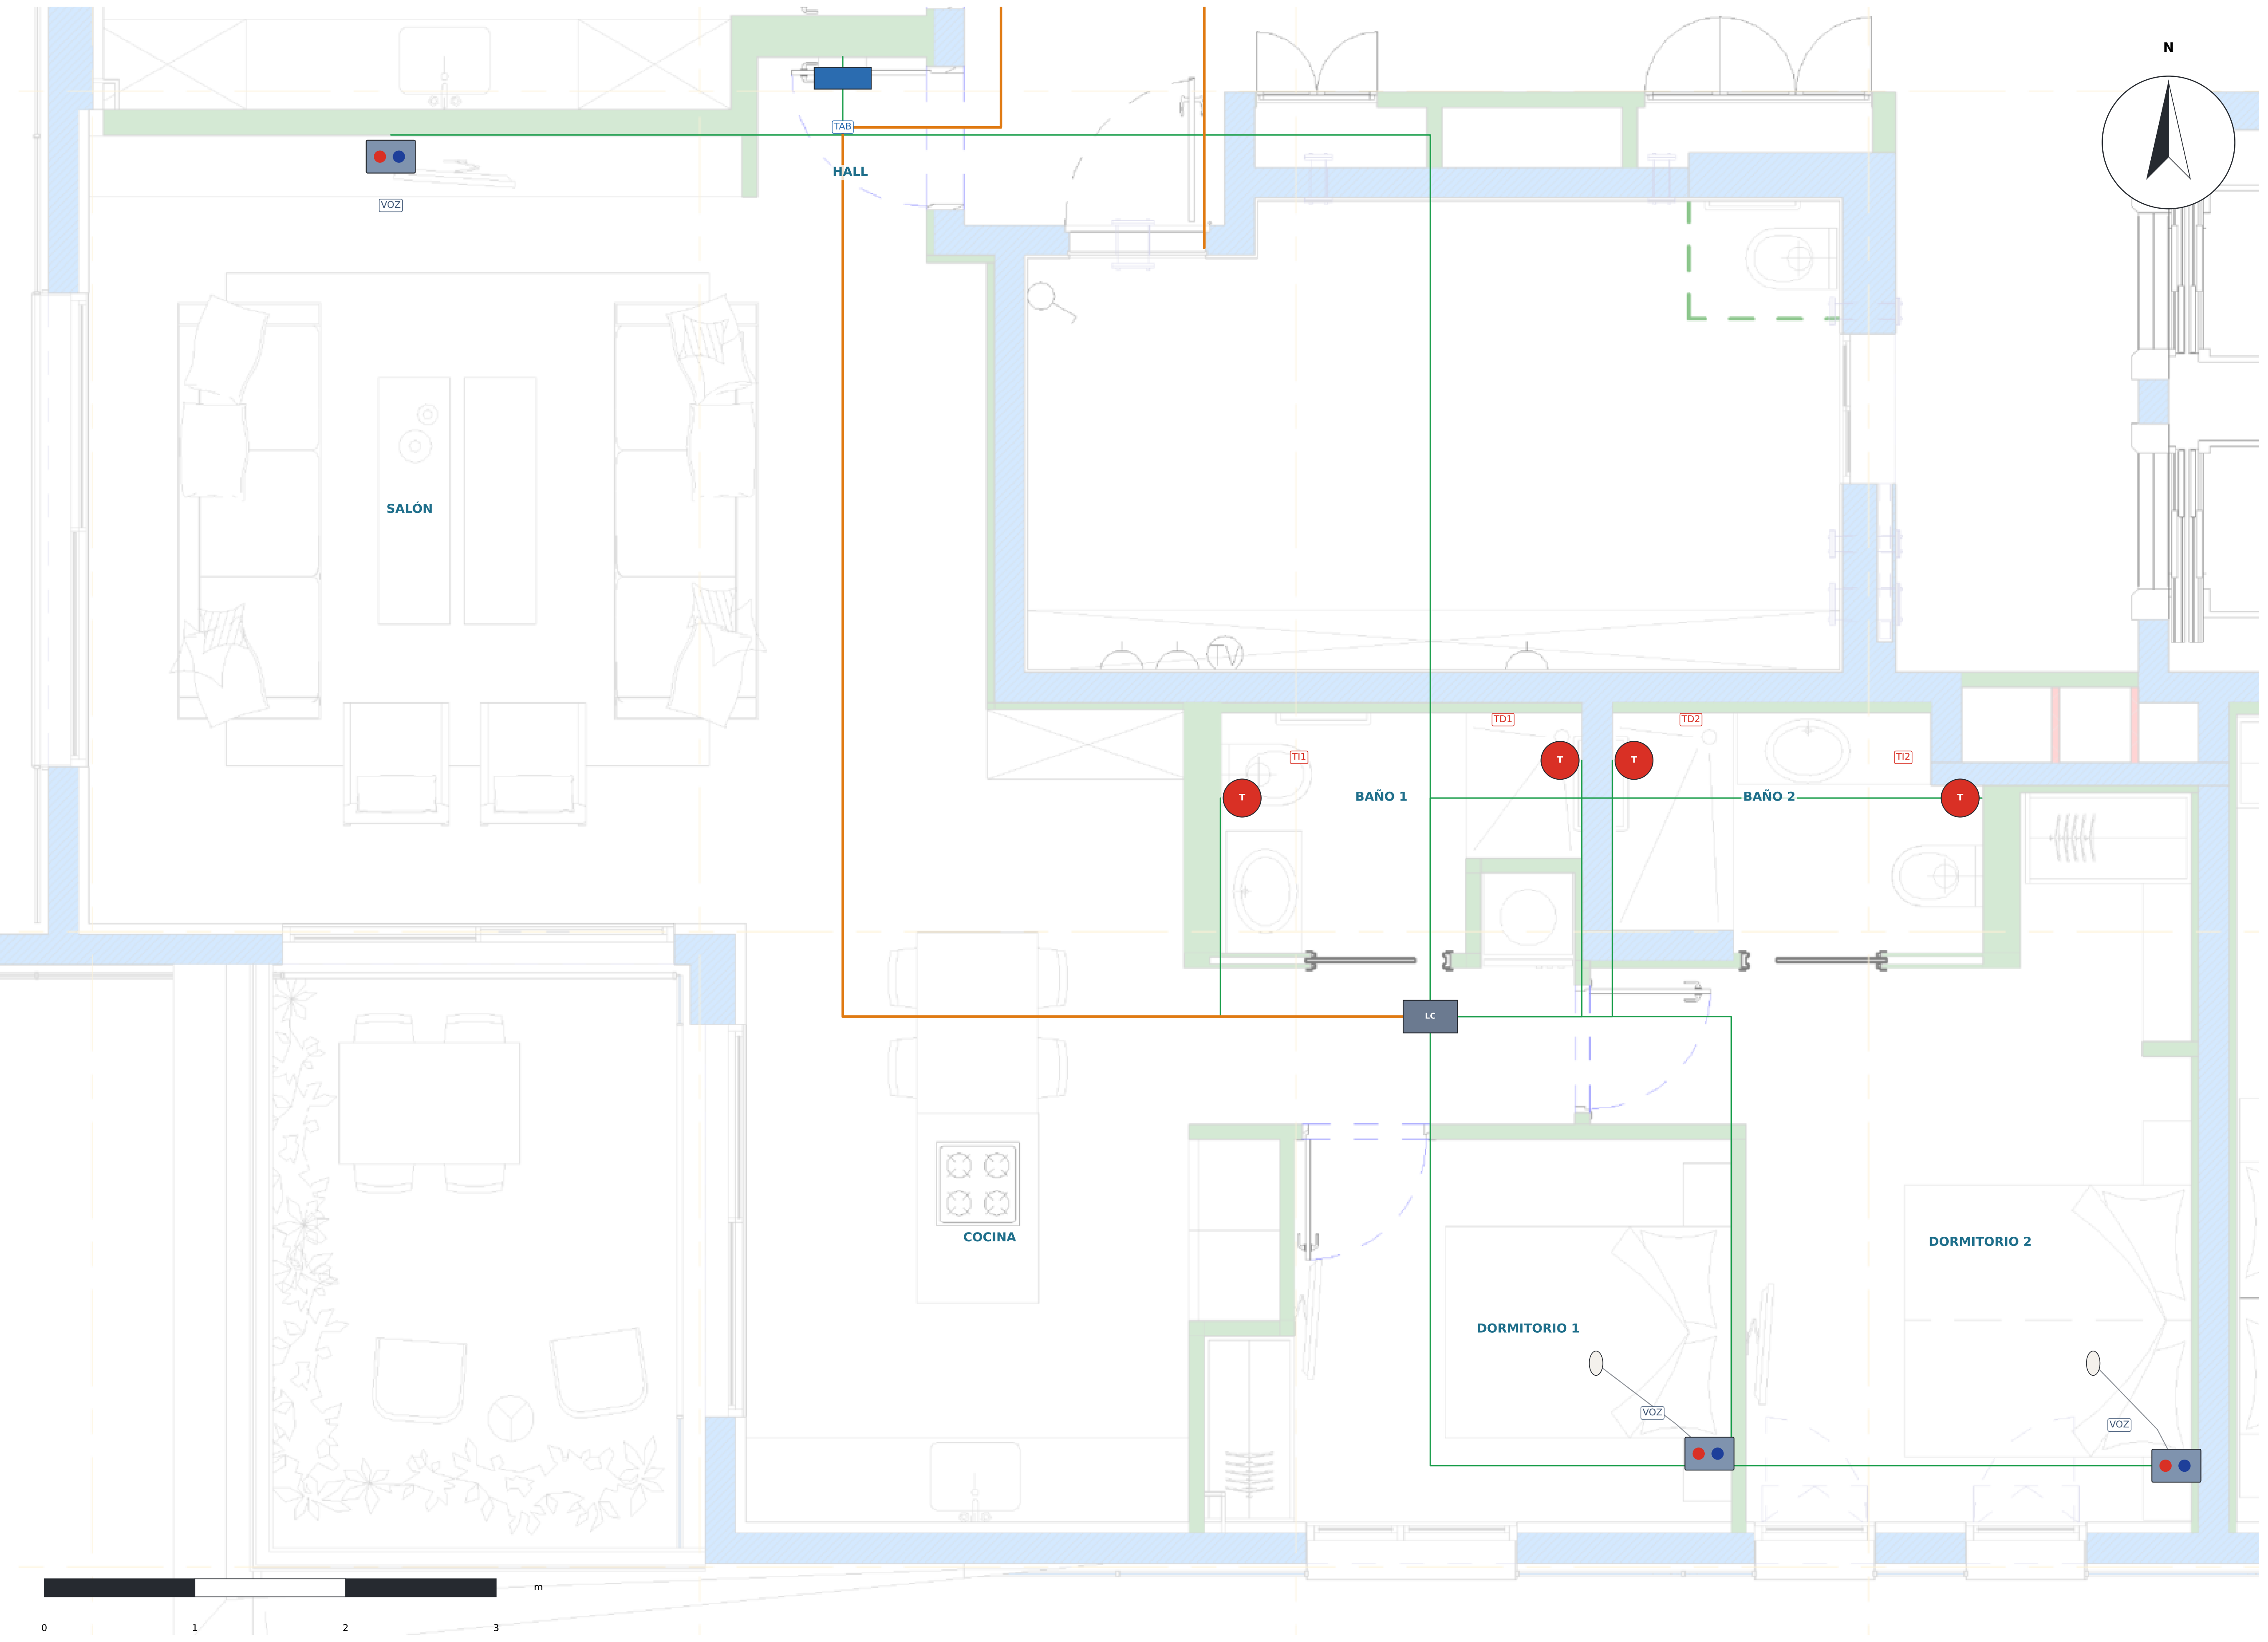

EQUIPOS DEL DEPARTAMENTO

ID	Equipo	Local	Altura
TAB	Tablet de la puerta	Hall	1,40 m
VOZ-S	Panel voz y botones	Salón	1,30 m
LCOM	LCom ACE71610003	Dormitorio 1	2,55 m
VOZ-D1	Panel voz y botones + pera	Dormitorio 1	1,20 m
VOZ-D2	Panel voz y botones + pera	Dormitorio 2	1,20 m
TI1	Tirador de baño	Baño 1	1,85 m
TD1	Tirador de baño	Baño 1	1,85 m
TI2	Tirador de baño	Baño 2	1,85 m
TD2	Tirador de baño	Baño 2	1,85 m

SÍMBOLOS · SYMBOLS · םילמס

🟦	TAB · Tablet de la puerta (iPad / Android) – llamada y voz, h 1,40 m Door tablet – call and voice · רובידו האירק – הסינכב טלבאט
● ●	VOZ · Panel con voz y botones ACE82182451 – salón y dormitorios, h 1,20–1,30 m Voice panel with buttons – living room and bedrooms · הניש ירדחו ןולס – םינצחל םע ילוק לנפ
⬯	Pera de llamada junto a la cama (en los dormitorios) Call pear next to the bed (bedrooms) · הטימה דיל האירק סגא
T	TI / TD · Tirador de baño ACE40320303W – inodoro y ducha, h 1,85 m Pull-cord – toilet and shower, h 1.85 m · לבח תכישמ – הלסא תחלקמו, הבוג 1.85 מ'
🟥	LP · Luz de pasillo ACE41020309 – sobre la puerta de cada baño público Corridor light – above each public toilet door · ןורדסמ תרונמ – לעמ דלת לכ םיתוריש םייבויצ
LC	LC · LCom ACE71610003 – concentrador del departamento (cielorraso) LCom – apartment hub (ceiling) · LCom – הרידה זכרמ (הרקת)

NOTAS · NOTES

1. El departamento x03 tiene la misma dotación (baños con otra distribución).
2. Tablet en el hall junto a la puerta de entrada.
3. Panel con voz en el salón y en los 2 dormitorios (con pera junto a la cama).
4. 2 baños: tirador en el inodoro y en la ducha de cada uno (4 tiradores).
5. Todo va radial en Cat6 al LCom del pasillo de los dormitorios.

MIGDALEI YAM A TIJON · VIVIENDA TUTELADA
Llamada de enfermería – PB + 8 pisos · 32 departamentos
Sistema: ACE BG · Advantecnia Elaboró: Telab International

DEPTO. 2 HABITACIONES (x04 / x03)

2-bedroom apartment (x04 / x03)

ESCALA · SCALE	FECHA · DATE	REV	LÁMINA
1:35	**15/10/2026**	**B**	**04**

Base: plano del arquitecto L5 (Massad Oz / Triplet) · cotas en metros
Formato A1 · Rev. B – sobre plano real

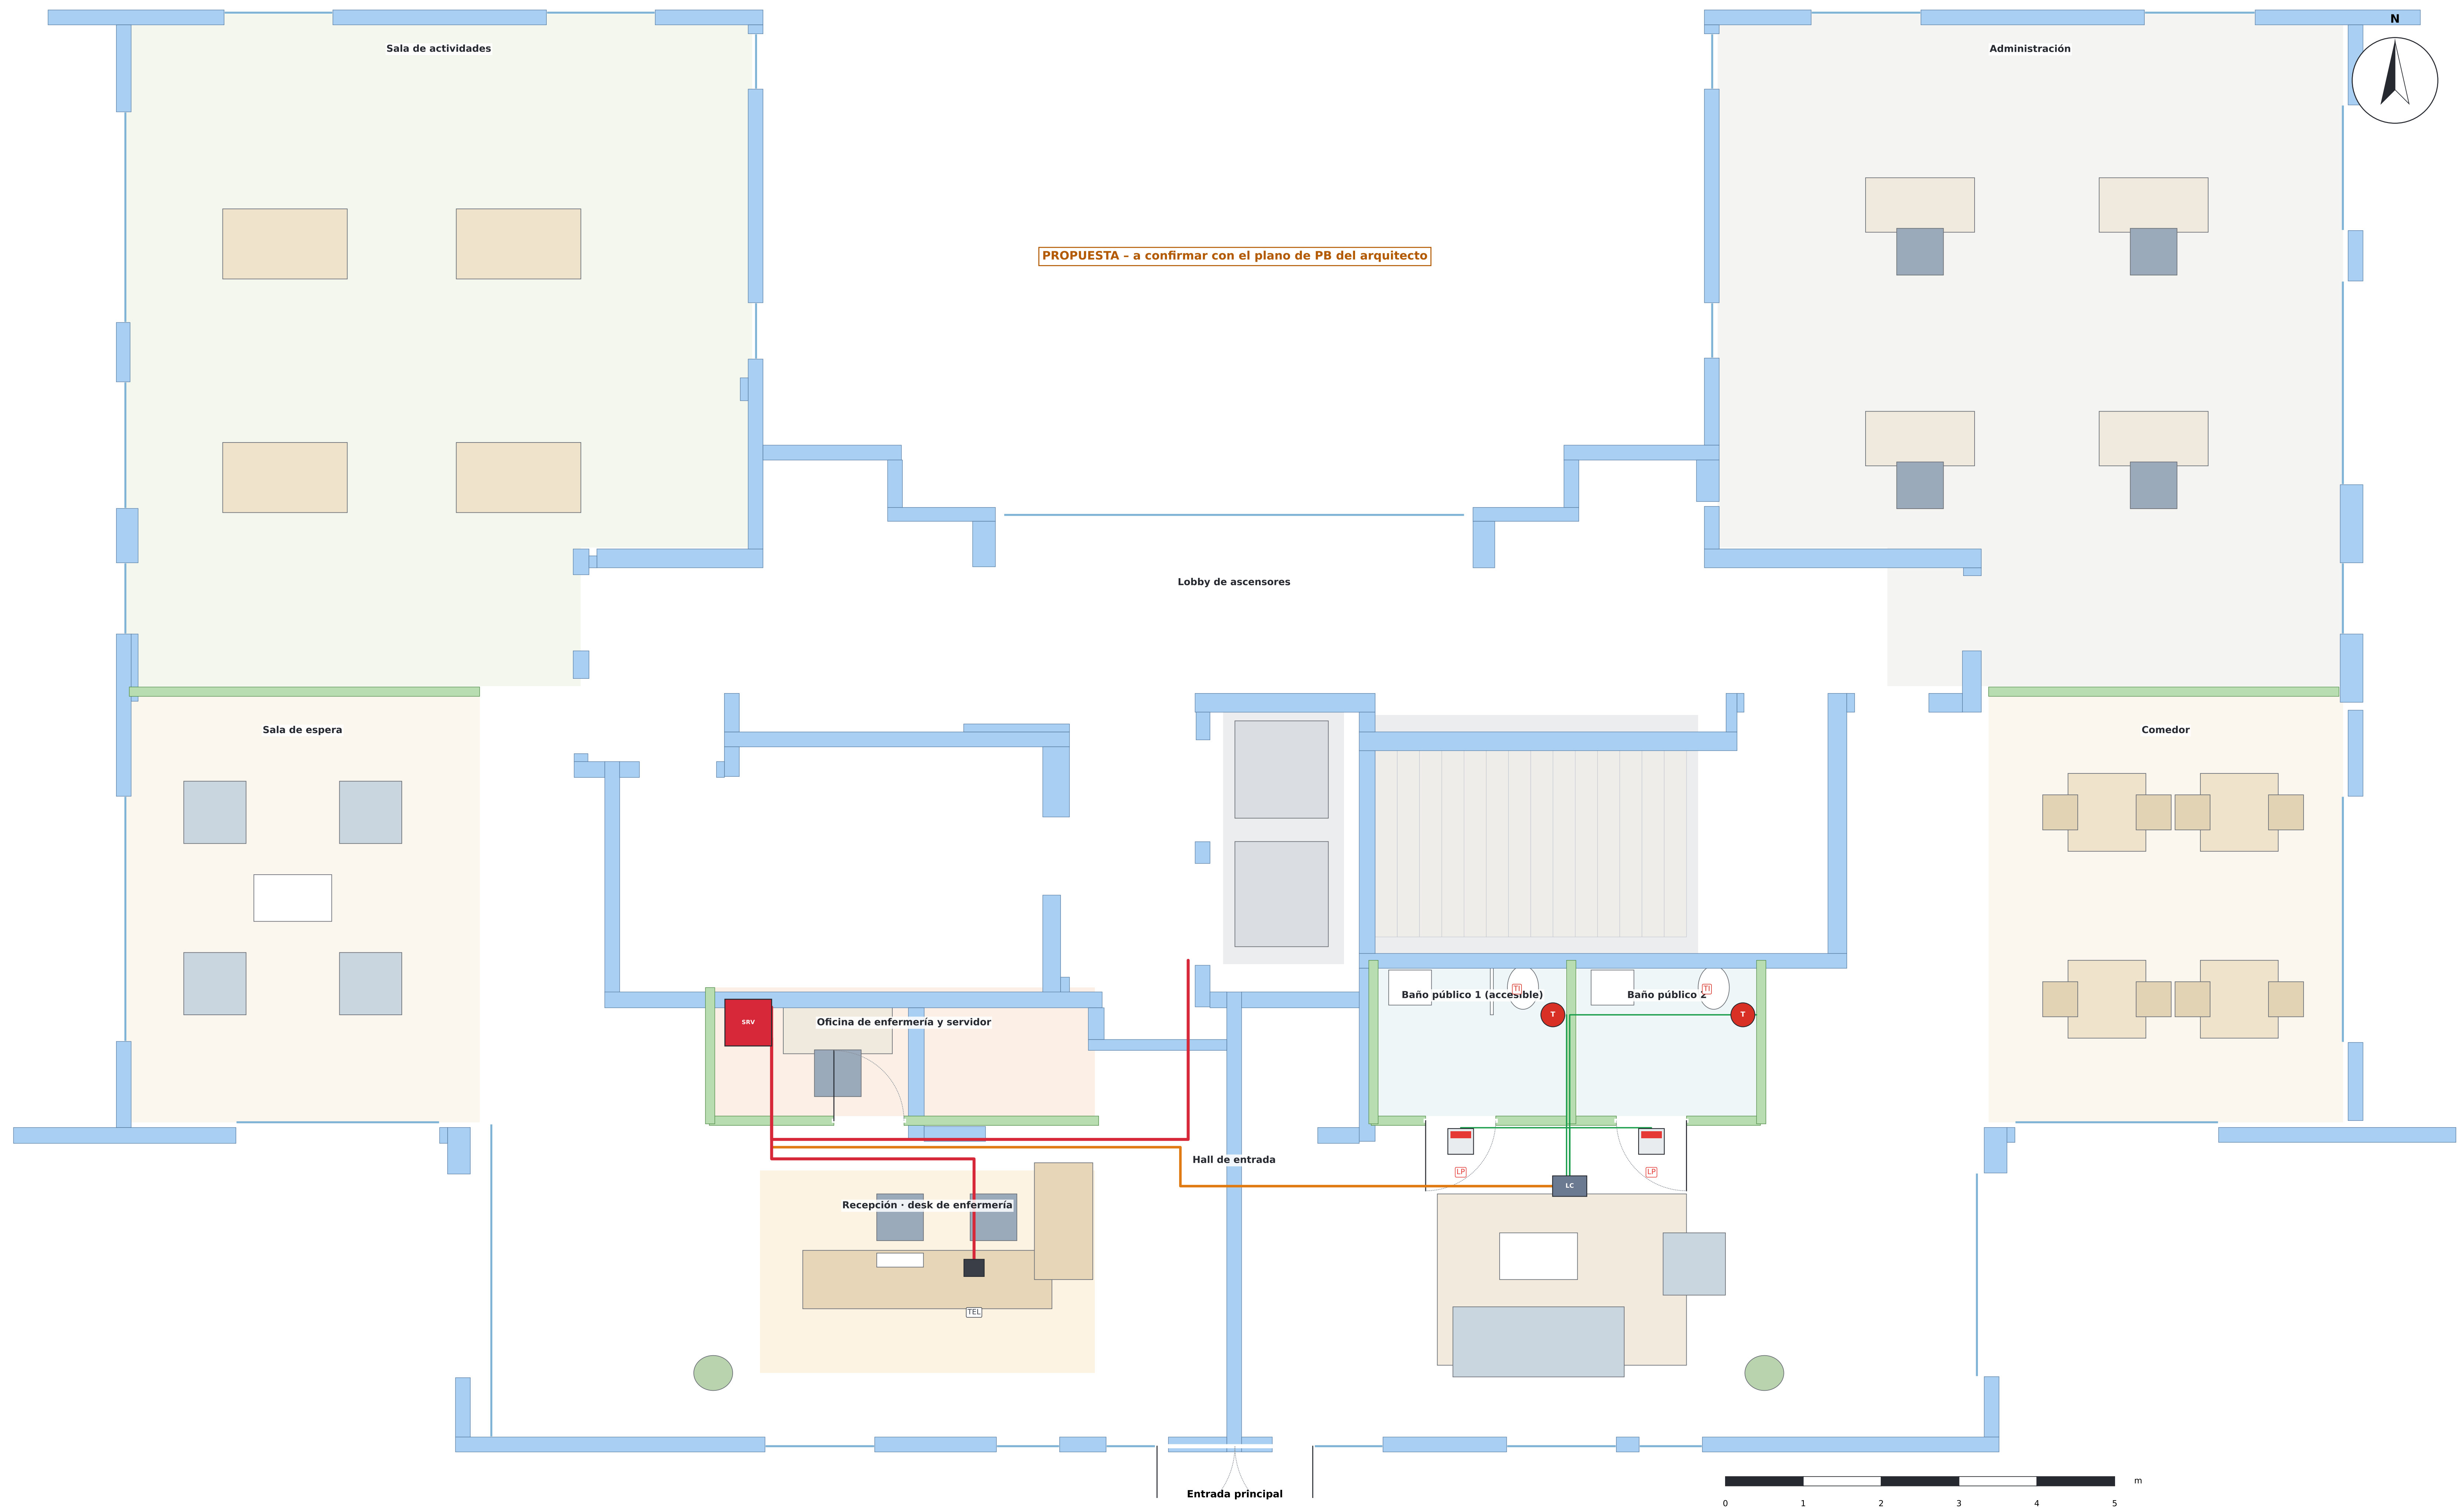
N
Sala de actividades
Administración
PROPUESTA – a confirmar con el plano de PB del arquitecto
Lobby de ascensores
Sala de espera
Comedor
SRV
Oficina de enfermería y servidor
Baño público 1 (accesible)
Baño público 2
T
LP
LC
Hall de entrada
Recepción · desk de enfermería
TEL
Entrada principal
0
1
2
3
4
5
m

DETALLE · RECEPCIÓN Y DESK DE ENFERMERÍA (1:40)

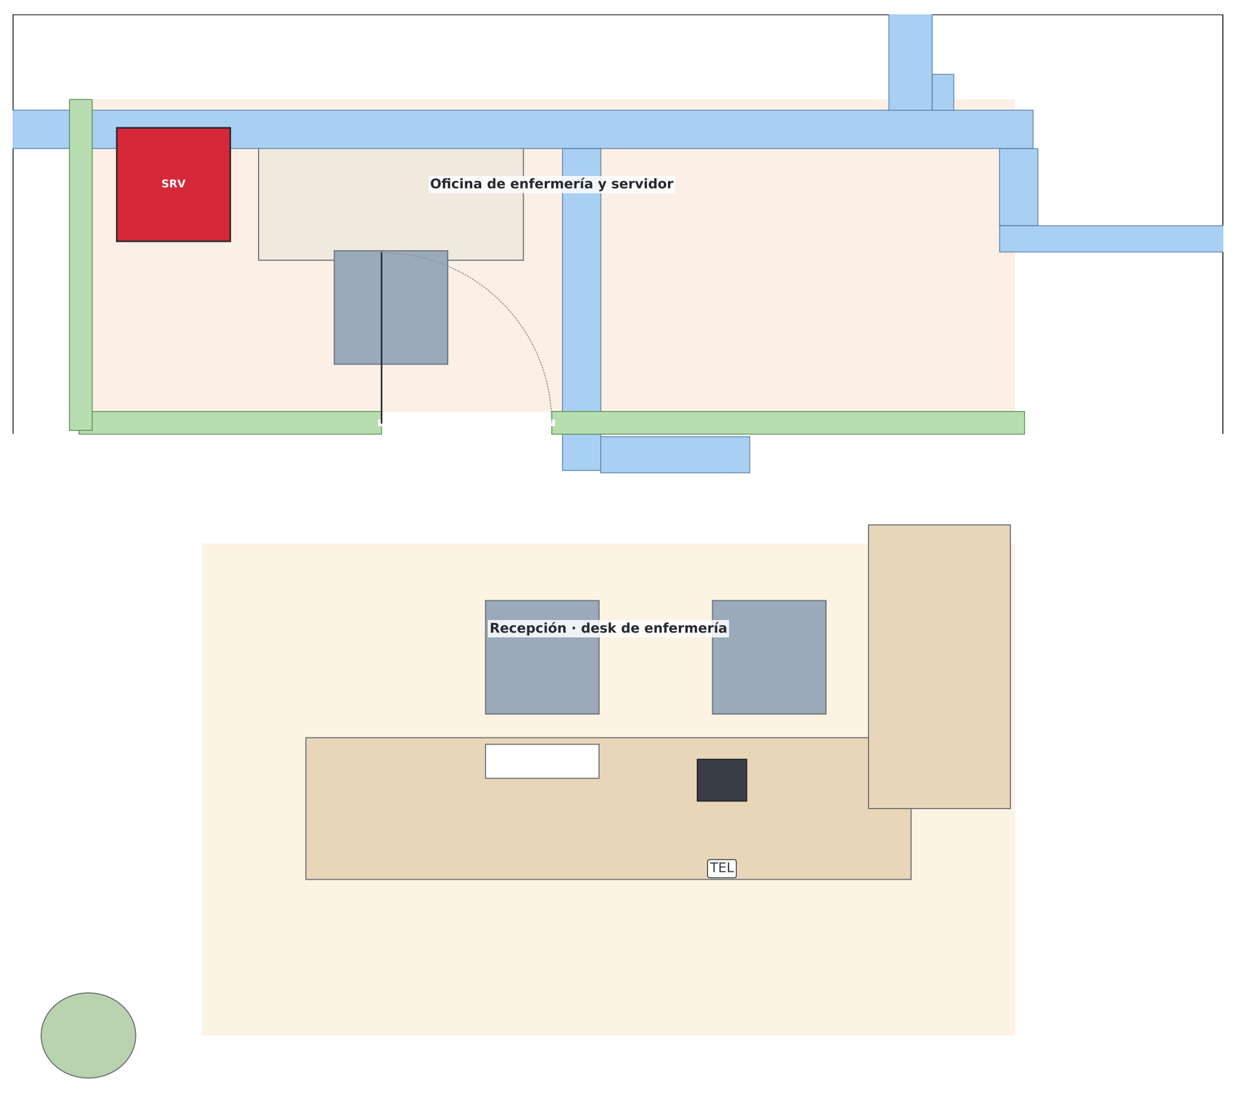
SRV
Oficina de enfermería y servidor
Recepción · desk de enfermería
TEL

NOTAS · NOTES

1. Desk de enfermería en la recepción, frente a la entrada y a los ascensores.
2. Sobre el desk: teléfono de escritorio Android ACE52190200 (recibe llamadas y voz).
3. Detrás del desk: oficina de enfermería con el gabinete principal: servidor ACE51010103, switch PoE ACEUCM6302 y Buscomm de PB.
4. 2 baños públicos en PB: tirador junto al inodoro y luz de pasillo sobre cada puerta.
5. El montante de los 8 pisos baja por el núcleo hasta el gabinete principal.
6. Distribución de PB propuesta: se ajusta cuando llegue el plano del arquitecto.

SÍMBOLOS · SYMBOLS · סמלים

T	TI / TD · Tirador de baño ACE40320303W – inodoro y ducha, h 1,85 m Pull-cord – toilet and shower, h 1.85 m · חבל משיכה – אסלה ומקלחת, גובה 1.85 מ'
LC	LC · LCom ACE71610003 – concentrador del departamento (cielorraso) LCom – apartment hub (ceiling) · LCom – מרכז דירה (תקרה)
SRV	SRV · Gabinete PB: servidor ACE51010103 + switch + Buscomm GF rack: server + switch + Buscomm · ארון קרקע: שרת + מתג + Buscomm
🟥	LP · Luz de pasillo ACE41020309 – sobre la puerta de cada baño público Corridor light – above each public toilet door · נורת מסדרון – מעל דלת כל שירותים ציבוריים
TEL	TEL · Teléfono de escritorio Android ACE52190200 Android desk phone · טלפון שולחני אנדרואיד

MIGDALEI YAM A TIJON · VIVIENDA TUTELADA
Llamada de enfermería – PB + 8 pisos · 32 departamentos
Sistema: ACE BG · Advantecnia   Elaboró: Telab International

PLANTA BAJA · LOBBY Y DESK DE ENFERMERÍA

Ground floor · lobby and nurse desk

ESCALA · SCALE	FECHA · DATE	REV	LÁMINA
1:60	15/10/2026	B	05

Base: plano del arquitecto L5 (Massad Oz / Triplet) · cotas en metros
Formato A1 · Rev. B – sobre plano real

A · EDIFICIO PB + 8 PISOS

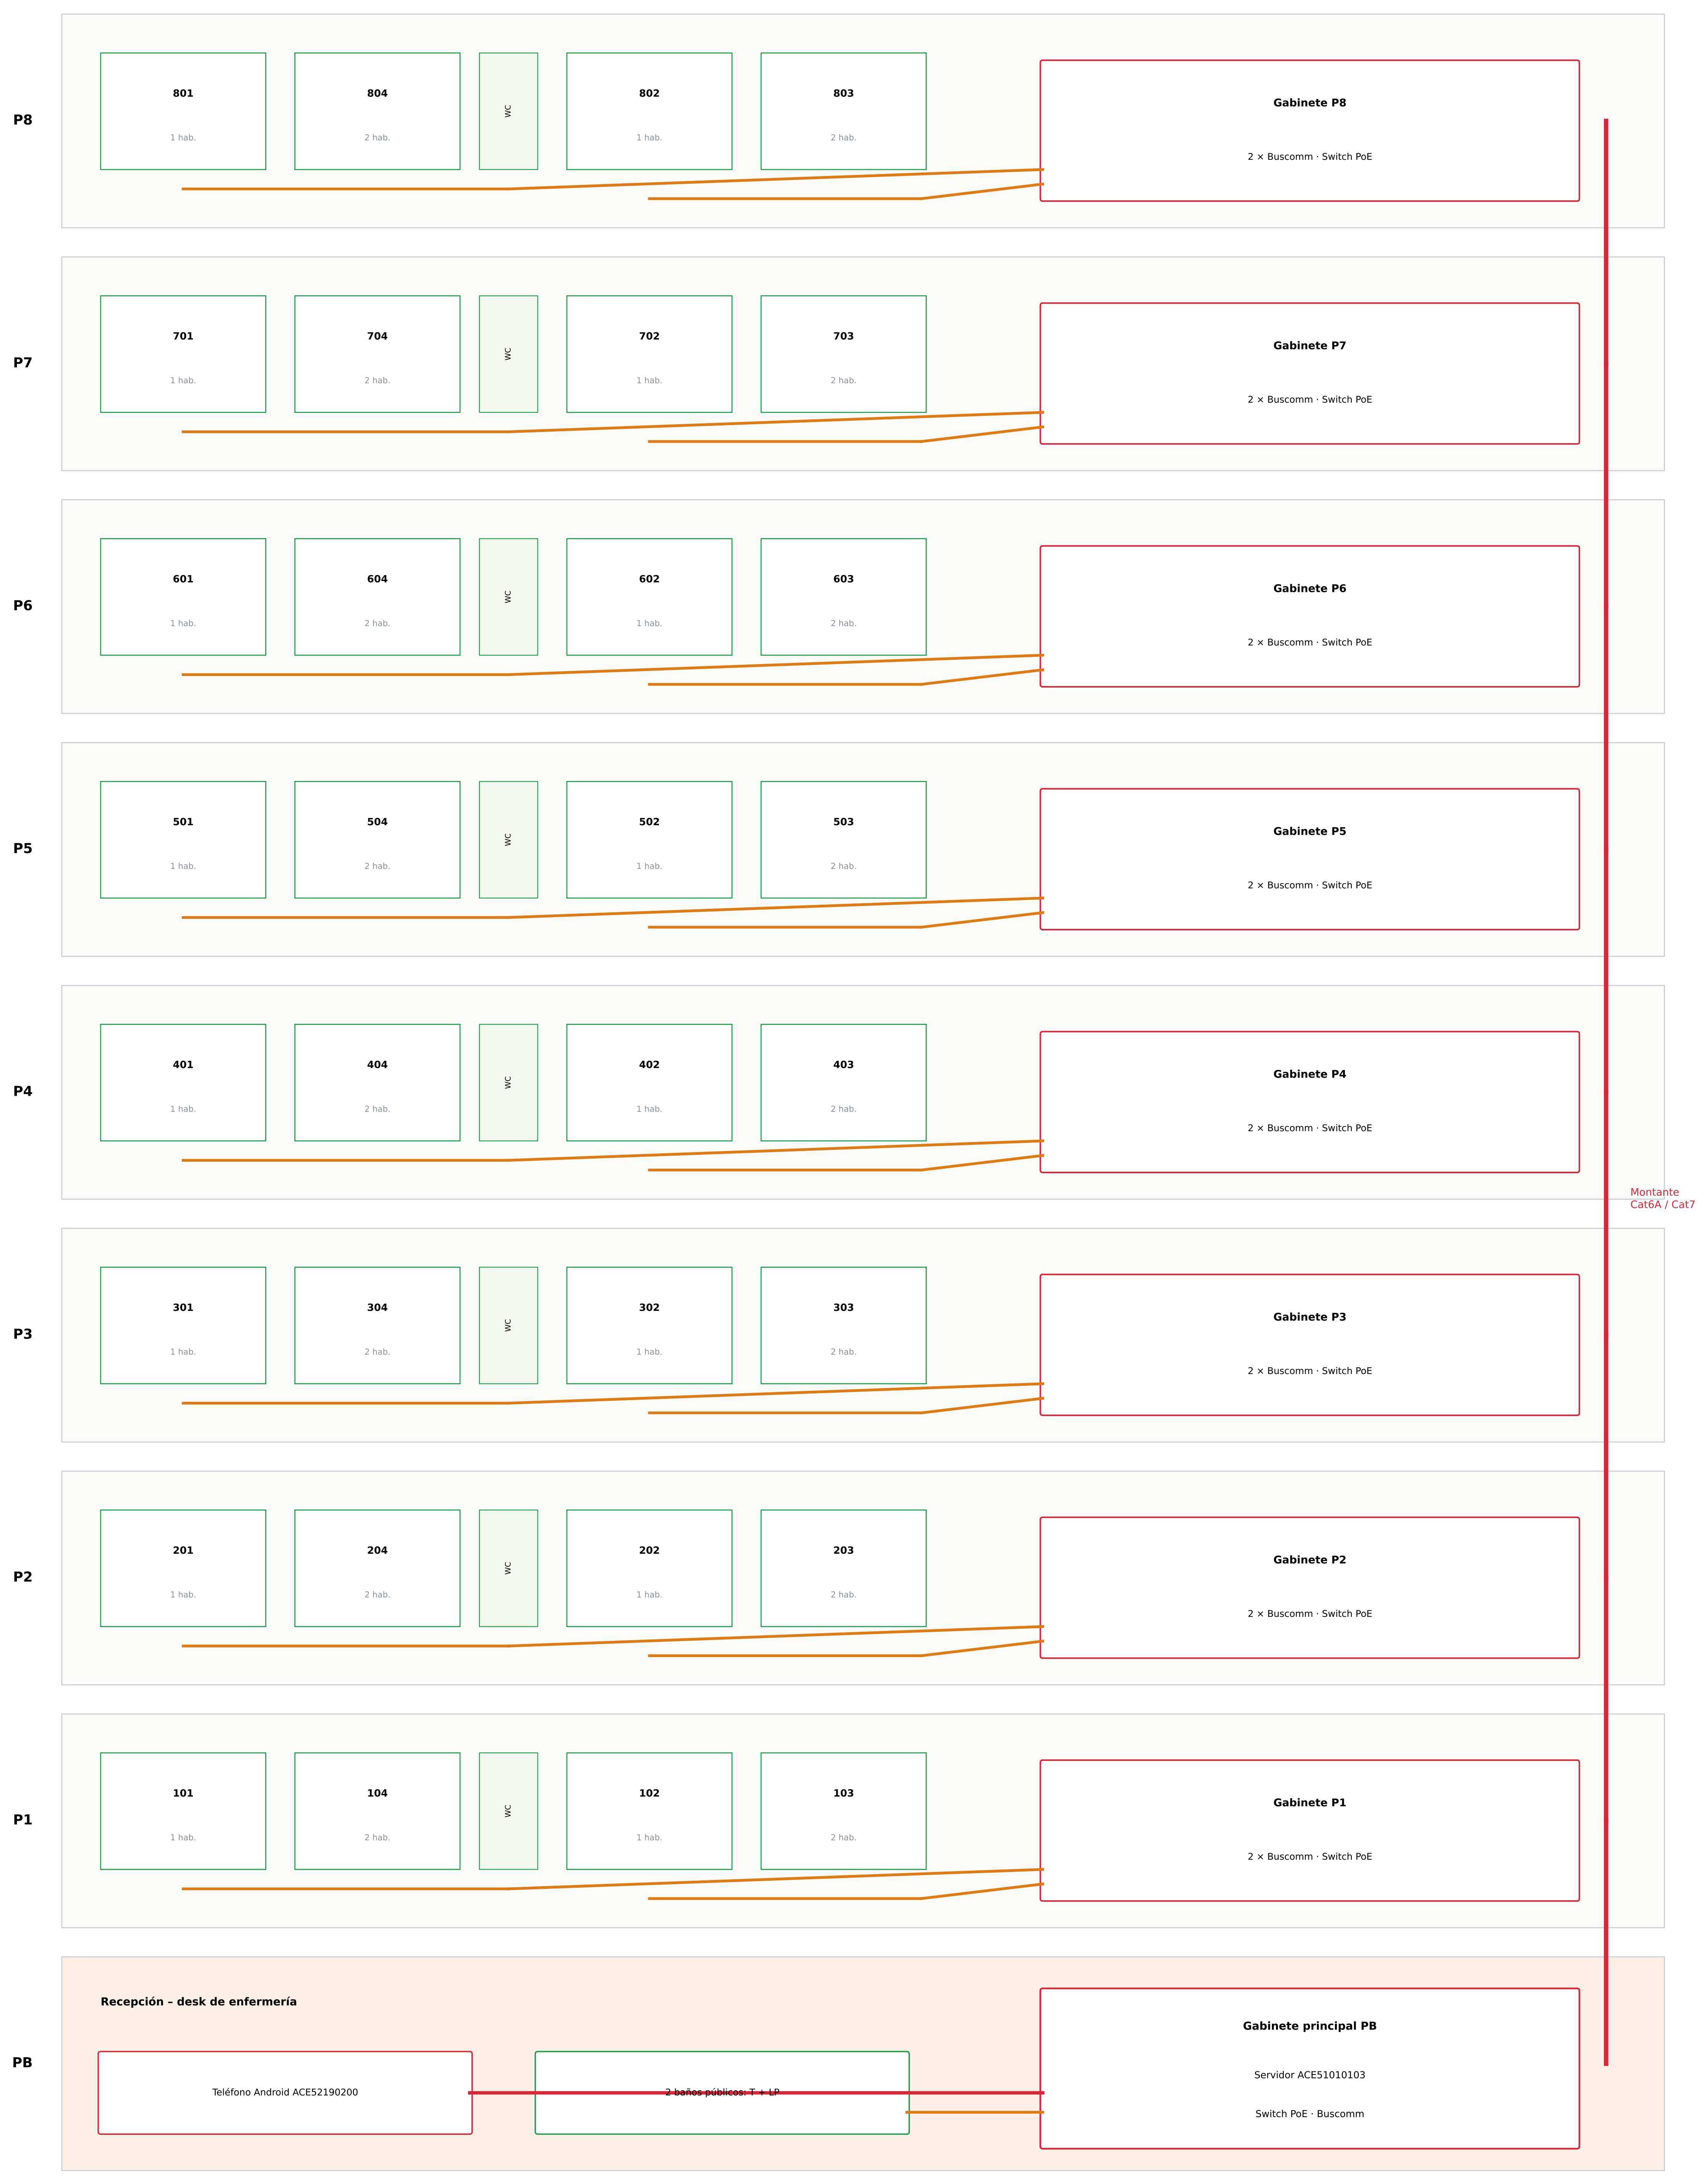

B · TOPOLOGÍA DE UN DEPARTAMENTO

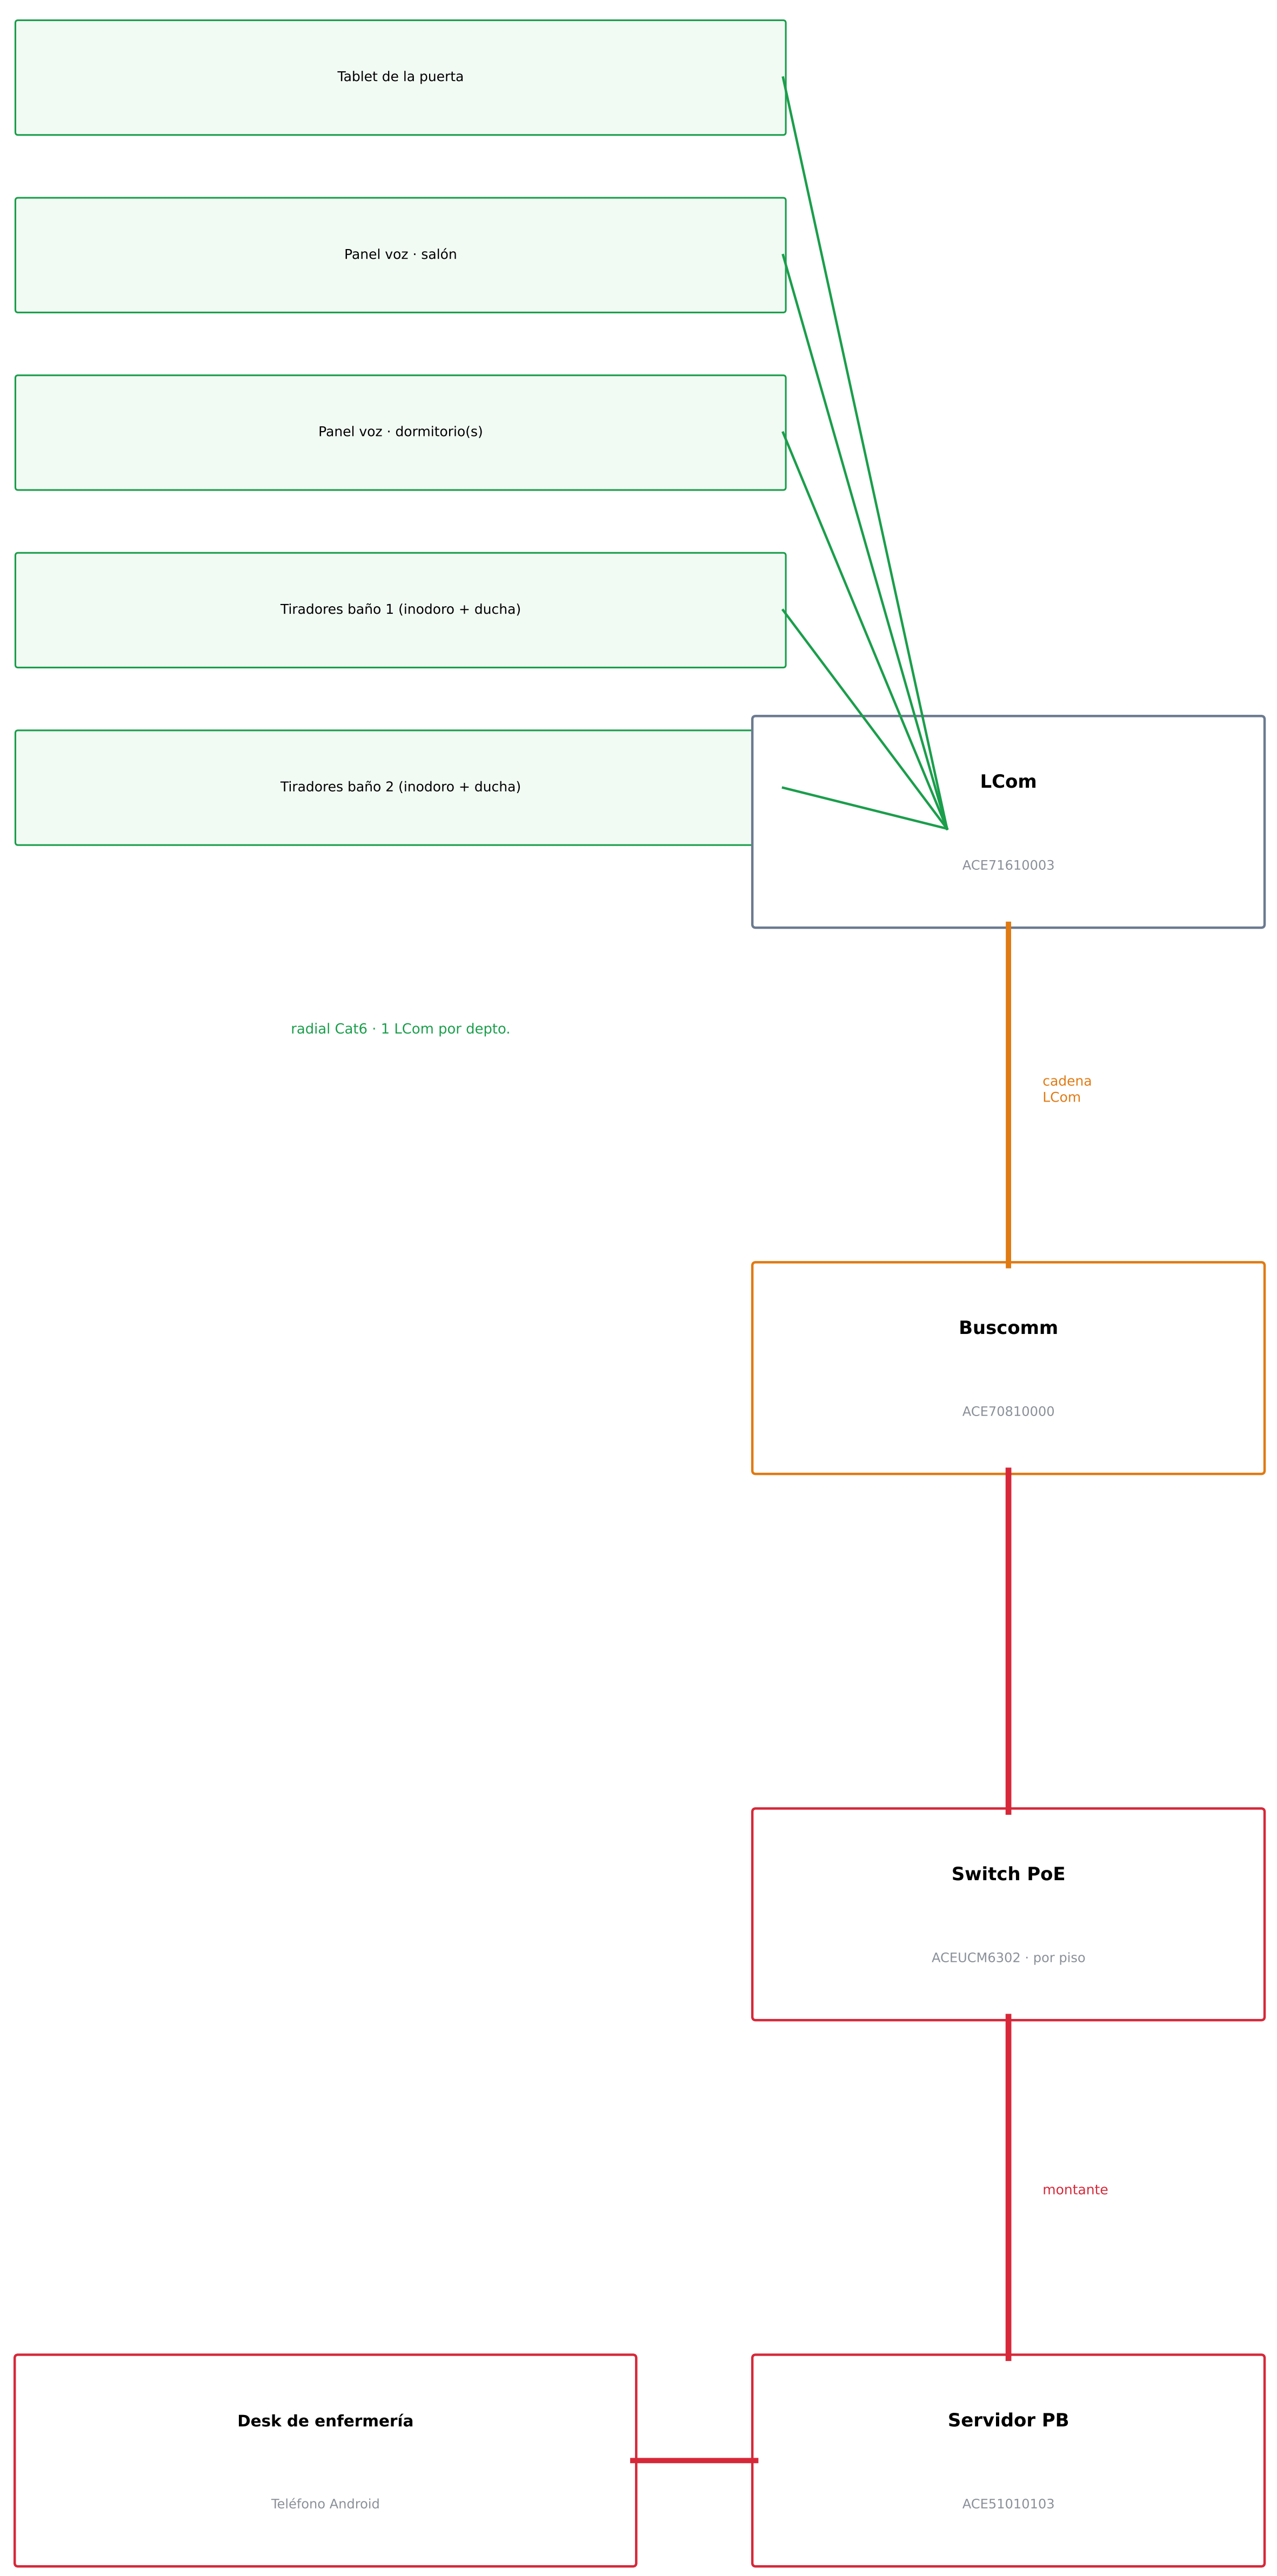

NOTAS · NOTES

1. 8 pisos iguales con 4 departamentos (2 de 1 habitación y 2 de 2).
2. En cada piso: gabinete con 2 Buscomm y un switch PoE.
3. Cadena 1: x01 → x04 → baño público. Cadena 2: x02 → x03.
4. Los switches suben por el montante hasta el gabinete principal de PB.
5. Las llamadas llegan por voz al teléfono Android del desk de enfermería.
6. Todo el sistema es PoE.
7. Cantidades de anteproyecto: validar con Advantecnia y en obra.

MIGDALEI YAM A TIJON · VIVIENDA TUTELADA

Llamada de enfermería – PB + 8 pisos · 32 departamentos

Sistema: ACE BG · Advantecnia   Elaboró: Telab International

ESQUEMA VERTICAL Y TOPOLOGÍA

Riser diagram and topology

ESCALA · SCALE	FECHA · DATE	REV	LÁMINA
S/E	**15/10/2026**	**B**	**06**

Base: plano del arquitecto L5 (Massad Oz / Triplet) · cotas en metros

Formato A1 · Rev. B – sobre plano real

LISTA DE MATERIALES – EDIFICIO COMPLETO (PB + 8 pisos · 32 departamentos · 10 baños públicos)

Código	Descripción	Cant.	Observación
EN LOS DEPARTAMENTOS (32)			
TAB	Tablet de la puerta (iPad / Android) – llamada y voz	**32**	1 por departamento
VOZ	Panel de llamada con voz y botones – ACE82182451	**80**	salón + cada dormitorio
TI/TD	Tirador de baño – ACE40320303W (inodoro y ducha)	**128**	4 por departamento
LC	LCom – ACE71610003	**32**	1 por departamento
BAÑOS PÚBLICOS (10)			
T	Tirador de baño – ACE40320303W	**10**	8 pisos + 2 en PB
LP	Luz de pasillo – ACE41020309	**10**	sobre cada puerta
LC	LCom – ACE71610003	**9**	1 por piso + 1 en PB
GABINETES Y CENTRAL			
BC	Buscomm – ACE70810000	**17**	2 por piso + 1 en PB
SW	Switch PoE – ACEUCM6302	**9**	1 por piso + PB
GAB	Gabinete mural 12U (Tripp Lite SRW12US) con patch panel	**8**	1 por piso
GAB-PB	Gabinete principal de piso con UPS	**1**	PB
SRV	Servidor + software Advantecnia – ACE51010103	**1**	PB
TEL	Teléfono de escritorio Android – ACE52190200	**1**	desk de enfermería
CABLES (+ 15 % de reserva)			
—	Cat6 radial dentro de los departamentos (verde)	**1880 m**	202 m por piso
—	Cat6 / Cat7 cadena LCom → Buscomm (naranja)	**780 m**	82 m por piso
—	Cat6A / Cat7 gabinetes y montante (rojo)	**100 m**	incluye montante

NOTAS · NOTES

1. Cantidades calculadas del modelo (piso tipo × 8 + PB).
2. Longitudes de cable medidas sobre el recorrido dibujado, + 15 %.
3. Precios: según lista vigente de Advantecnia.
4. Validar en obra antes de comprar.

MIGDALEI YAM A TIJON · VIVIENDA TUTELADA
Llamada de enfermería – PB + 8 pisos · 32 departamentos
Sistema: ACE BG · Advantecnia   Elaboró: Telab International

LISTA DE MATERIALES
Bill of materials

ESCALA · SCALE	FECHA · DATE	REV	LÁMINA
S/E	**15/10/2026**	**B**	**07**

Base: plano del arquitecto L5 (Massad Oz / Triplet) · cotas en metros
Formato A1 · Rev. B – sobre plano real

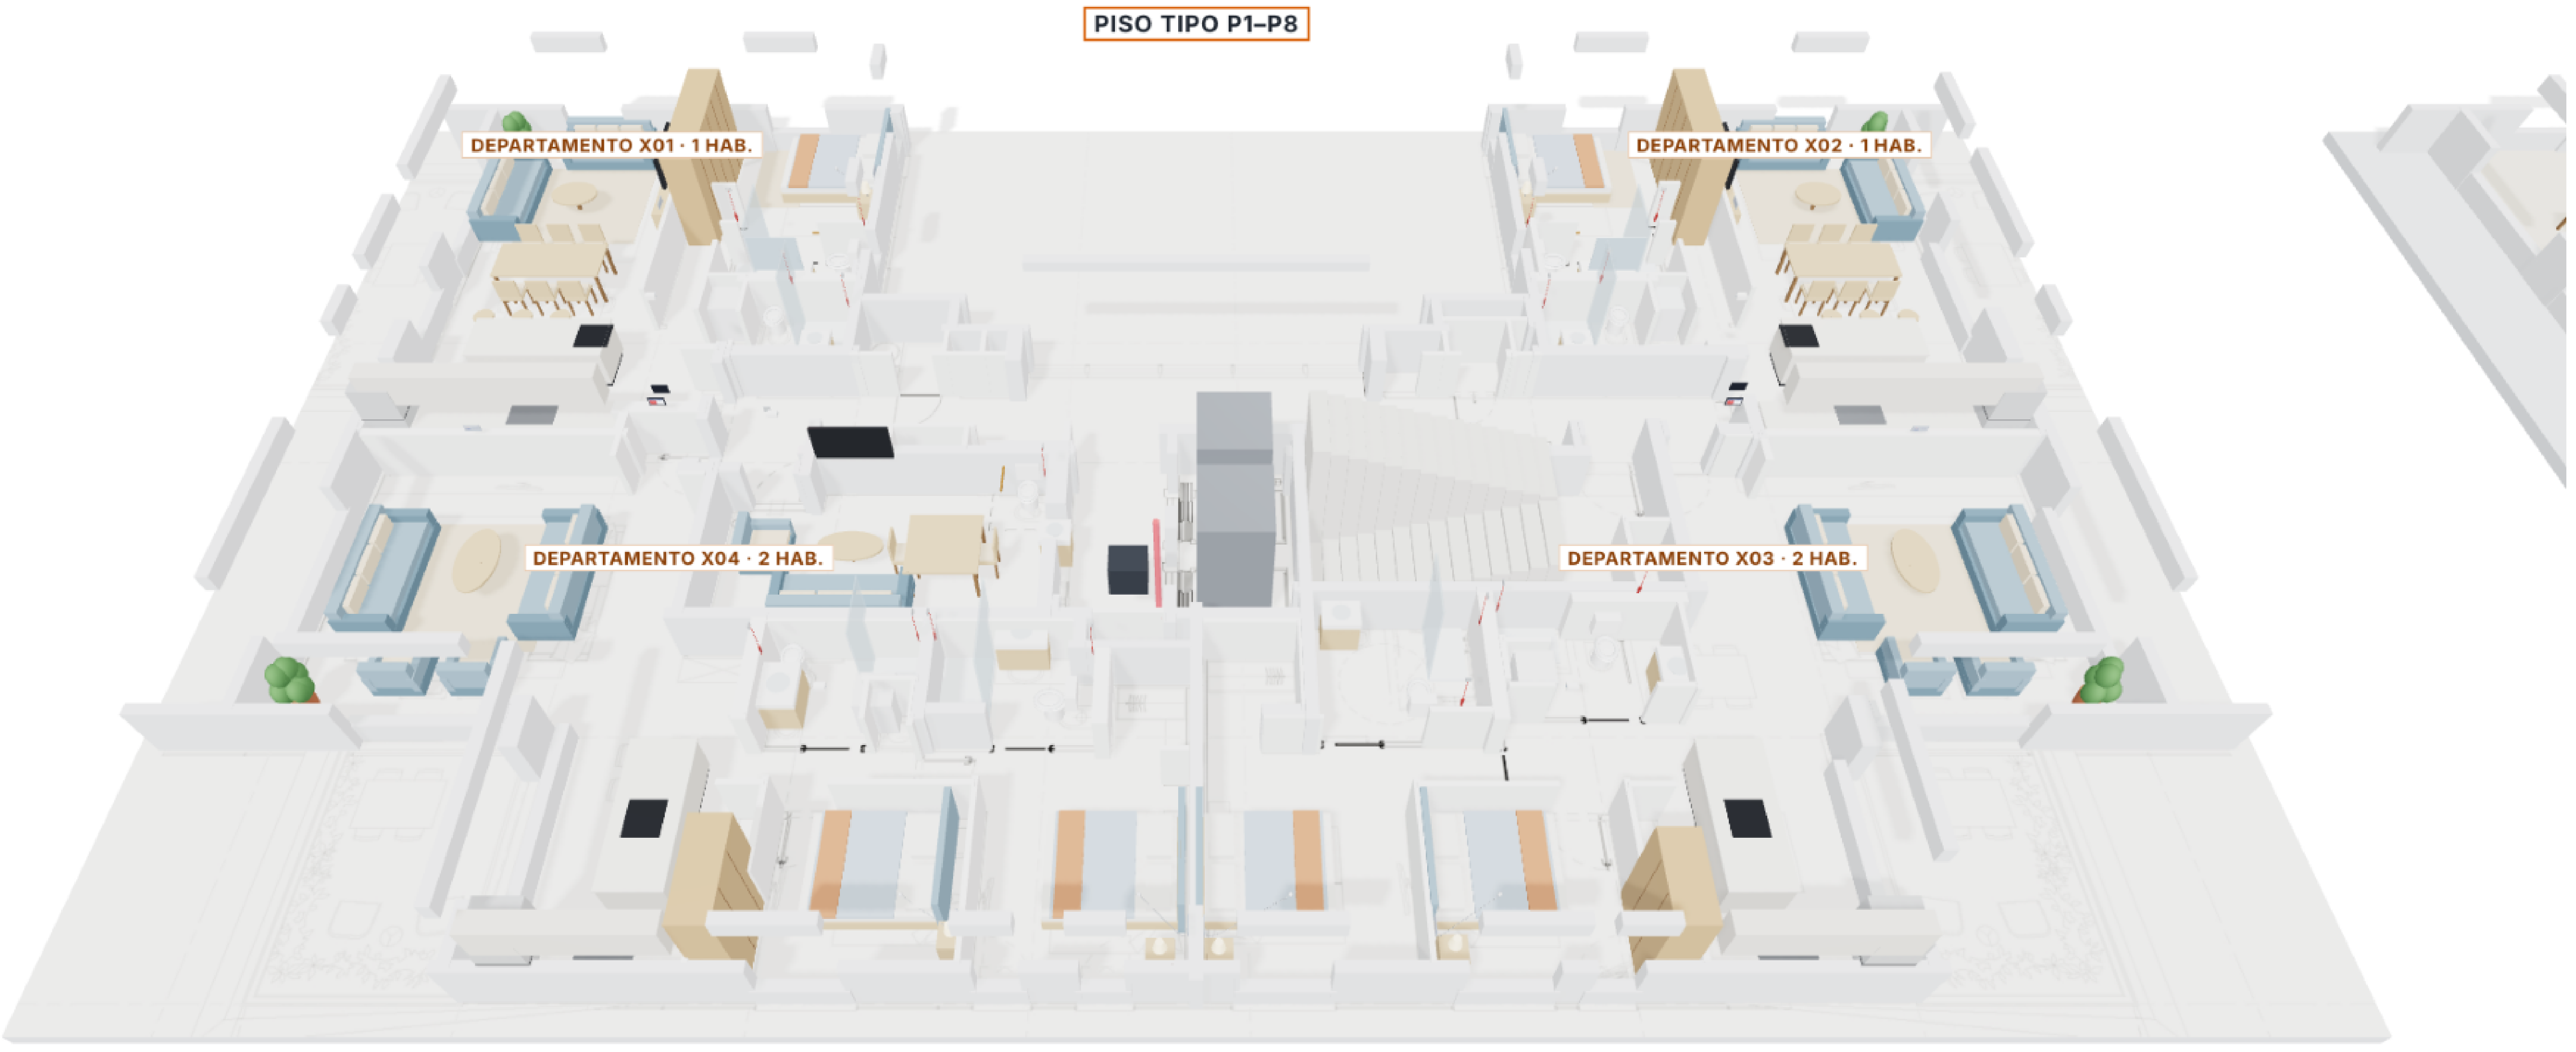
PISO TIPO P1–P8
DEPARTAMENTO X01 · 1 HAB.
DEPARTAMENTO X02 · 1 HAB.
DEPARTAMENTO X04 · 2 HAB.
DEPARTAMENTO X03 · 2 HAB.

A · Piso tipo – 4 departamentos

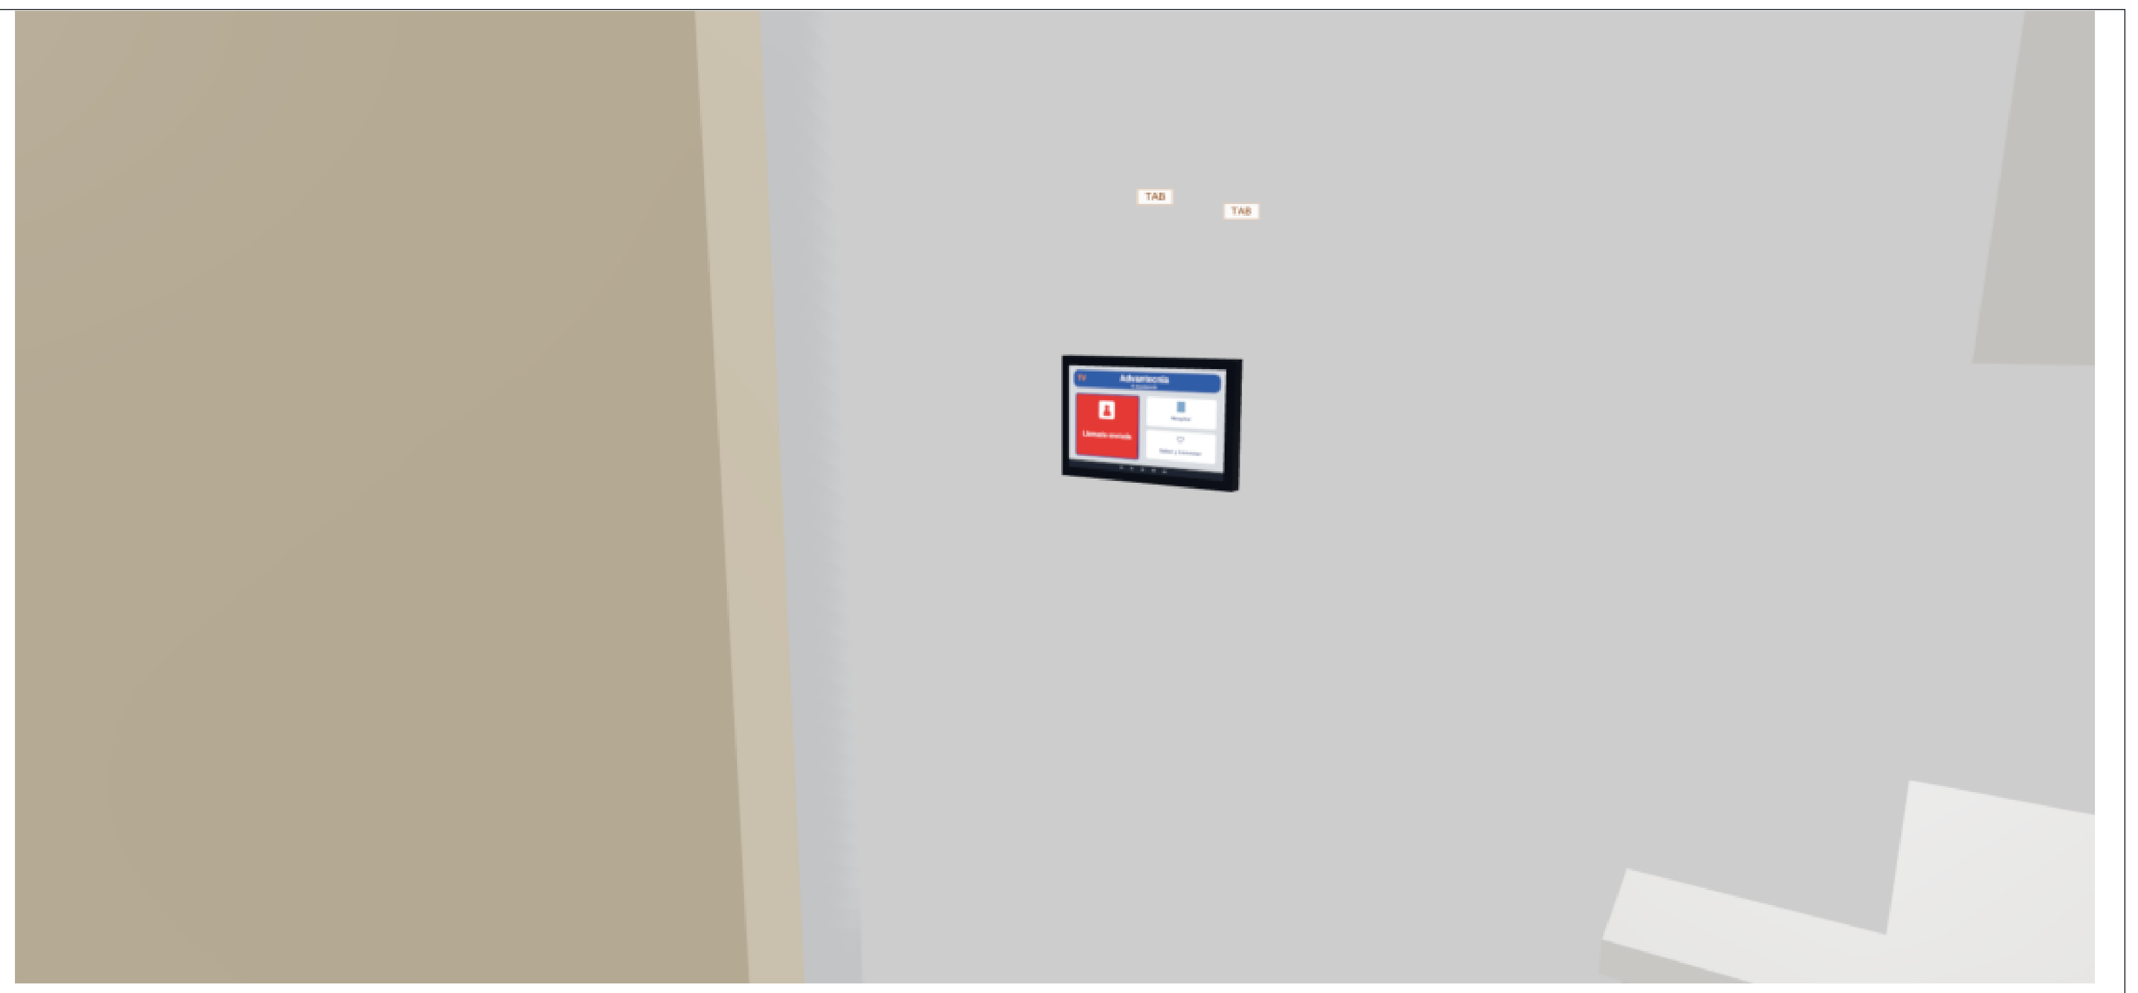

B · Tablet de la puerta

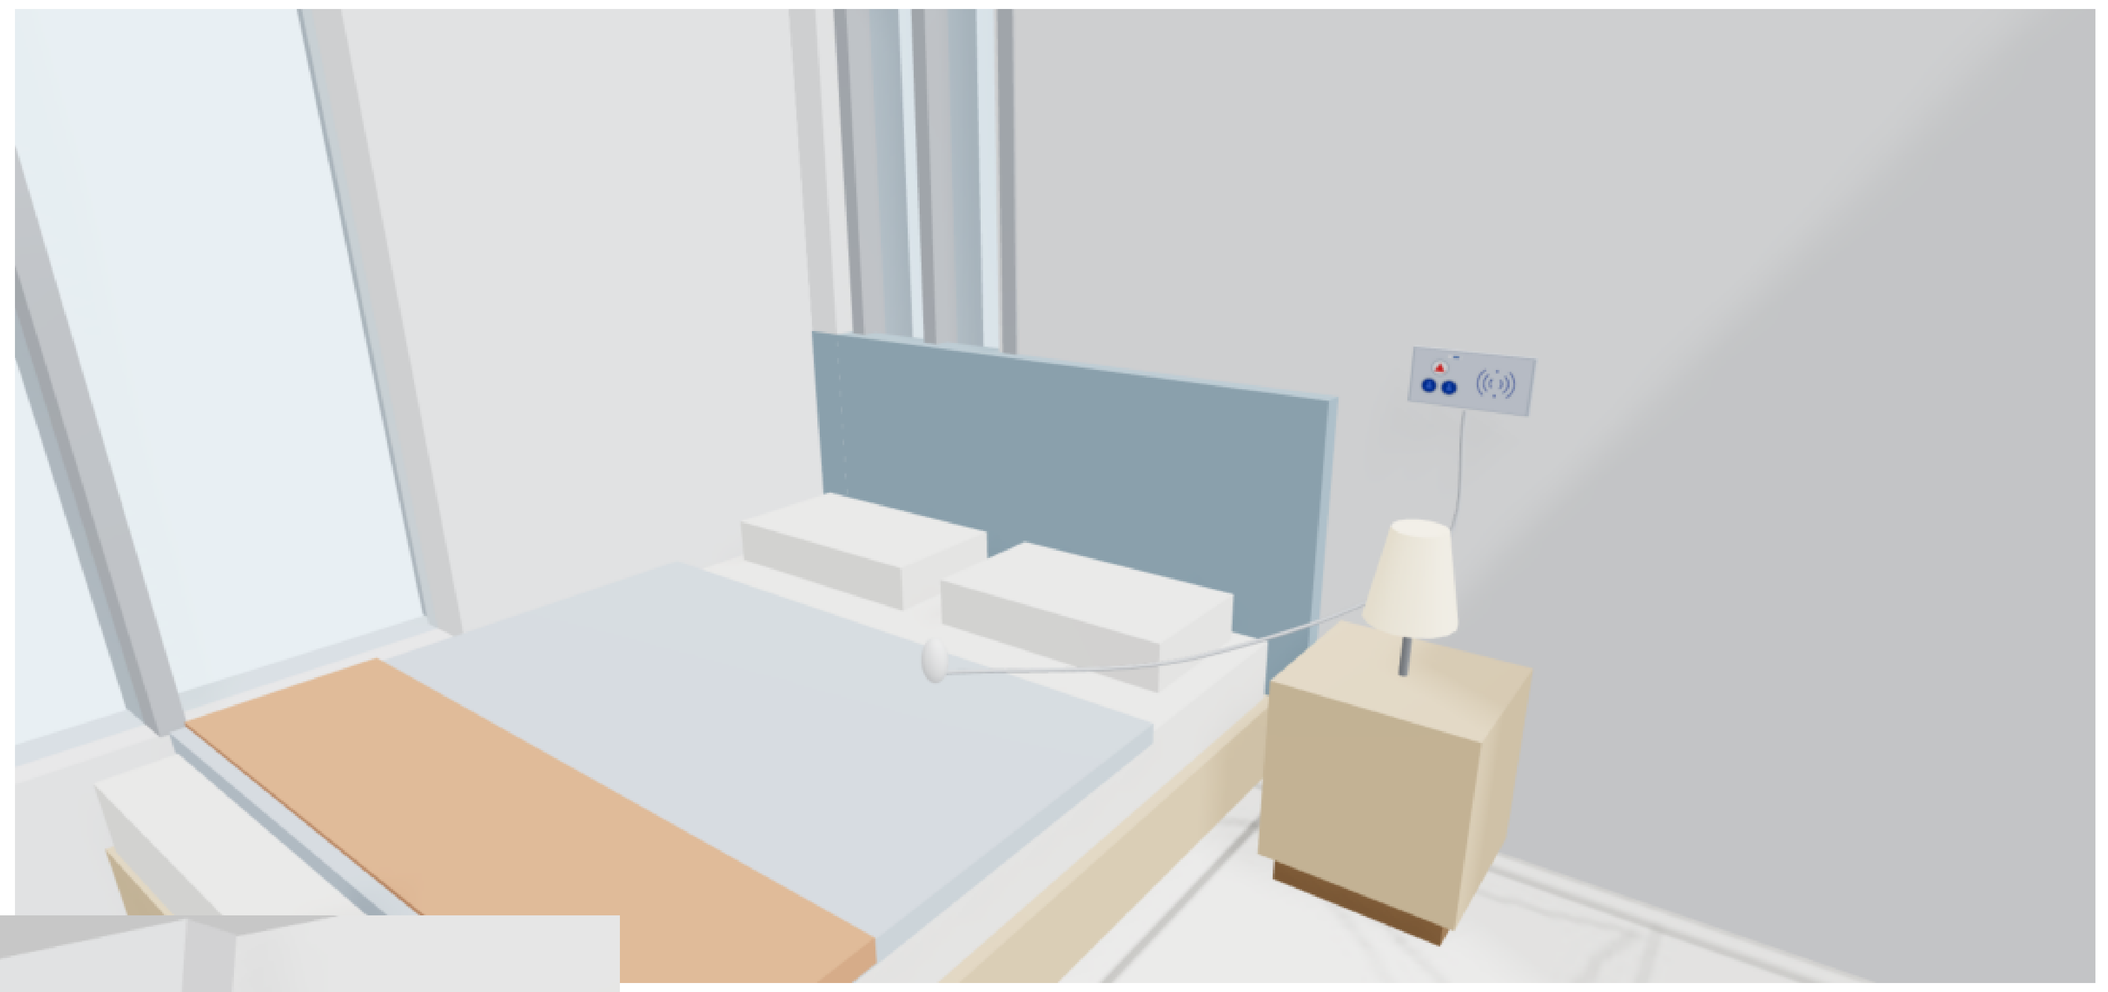

D · Baño – tiradores en inodoro y ducha

E · PB – desk de enfermería

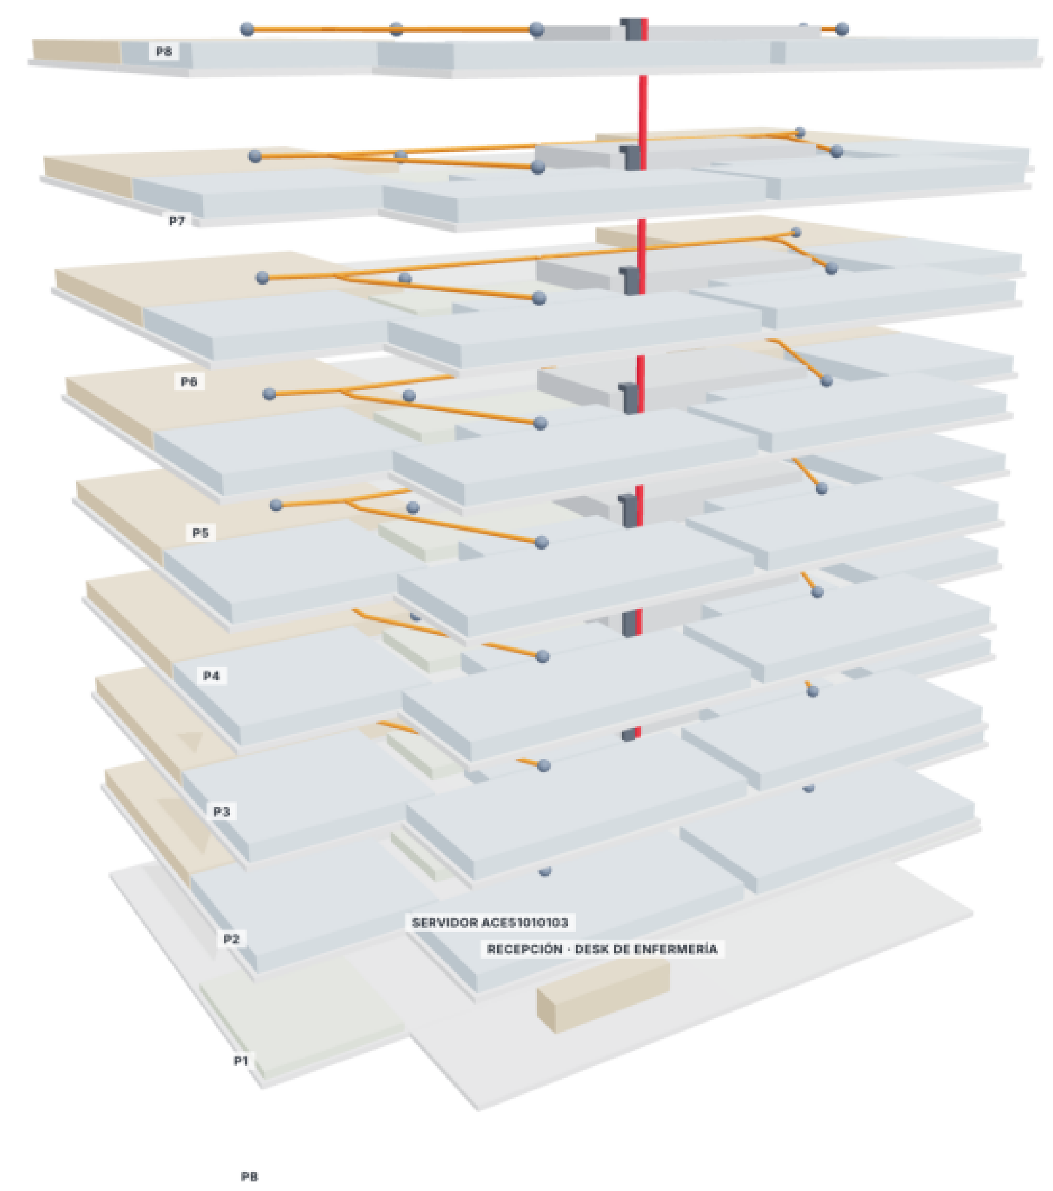

F · Edificio PB + 8 pisos

MIGDALEI YAM A TIJON · VIVIENDA TUTELADA

Llamada de enfermería – PB + 8 pisos · 32 departamentos

Sistema: ACE BG · Advantecnia   Elaboró: Telab International

VISTAS 3D

3D views

ESCALA · SCALE	FECHA · DATE	REV	LÁMINA
S/E	**15/10/2026**	**B**	**08**

Base: plano del arquitecto L5 (Massad Oz / Triplet) · cotas en metros

Formato A1 · Rev. B – sobre plano real

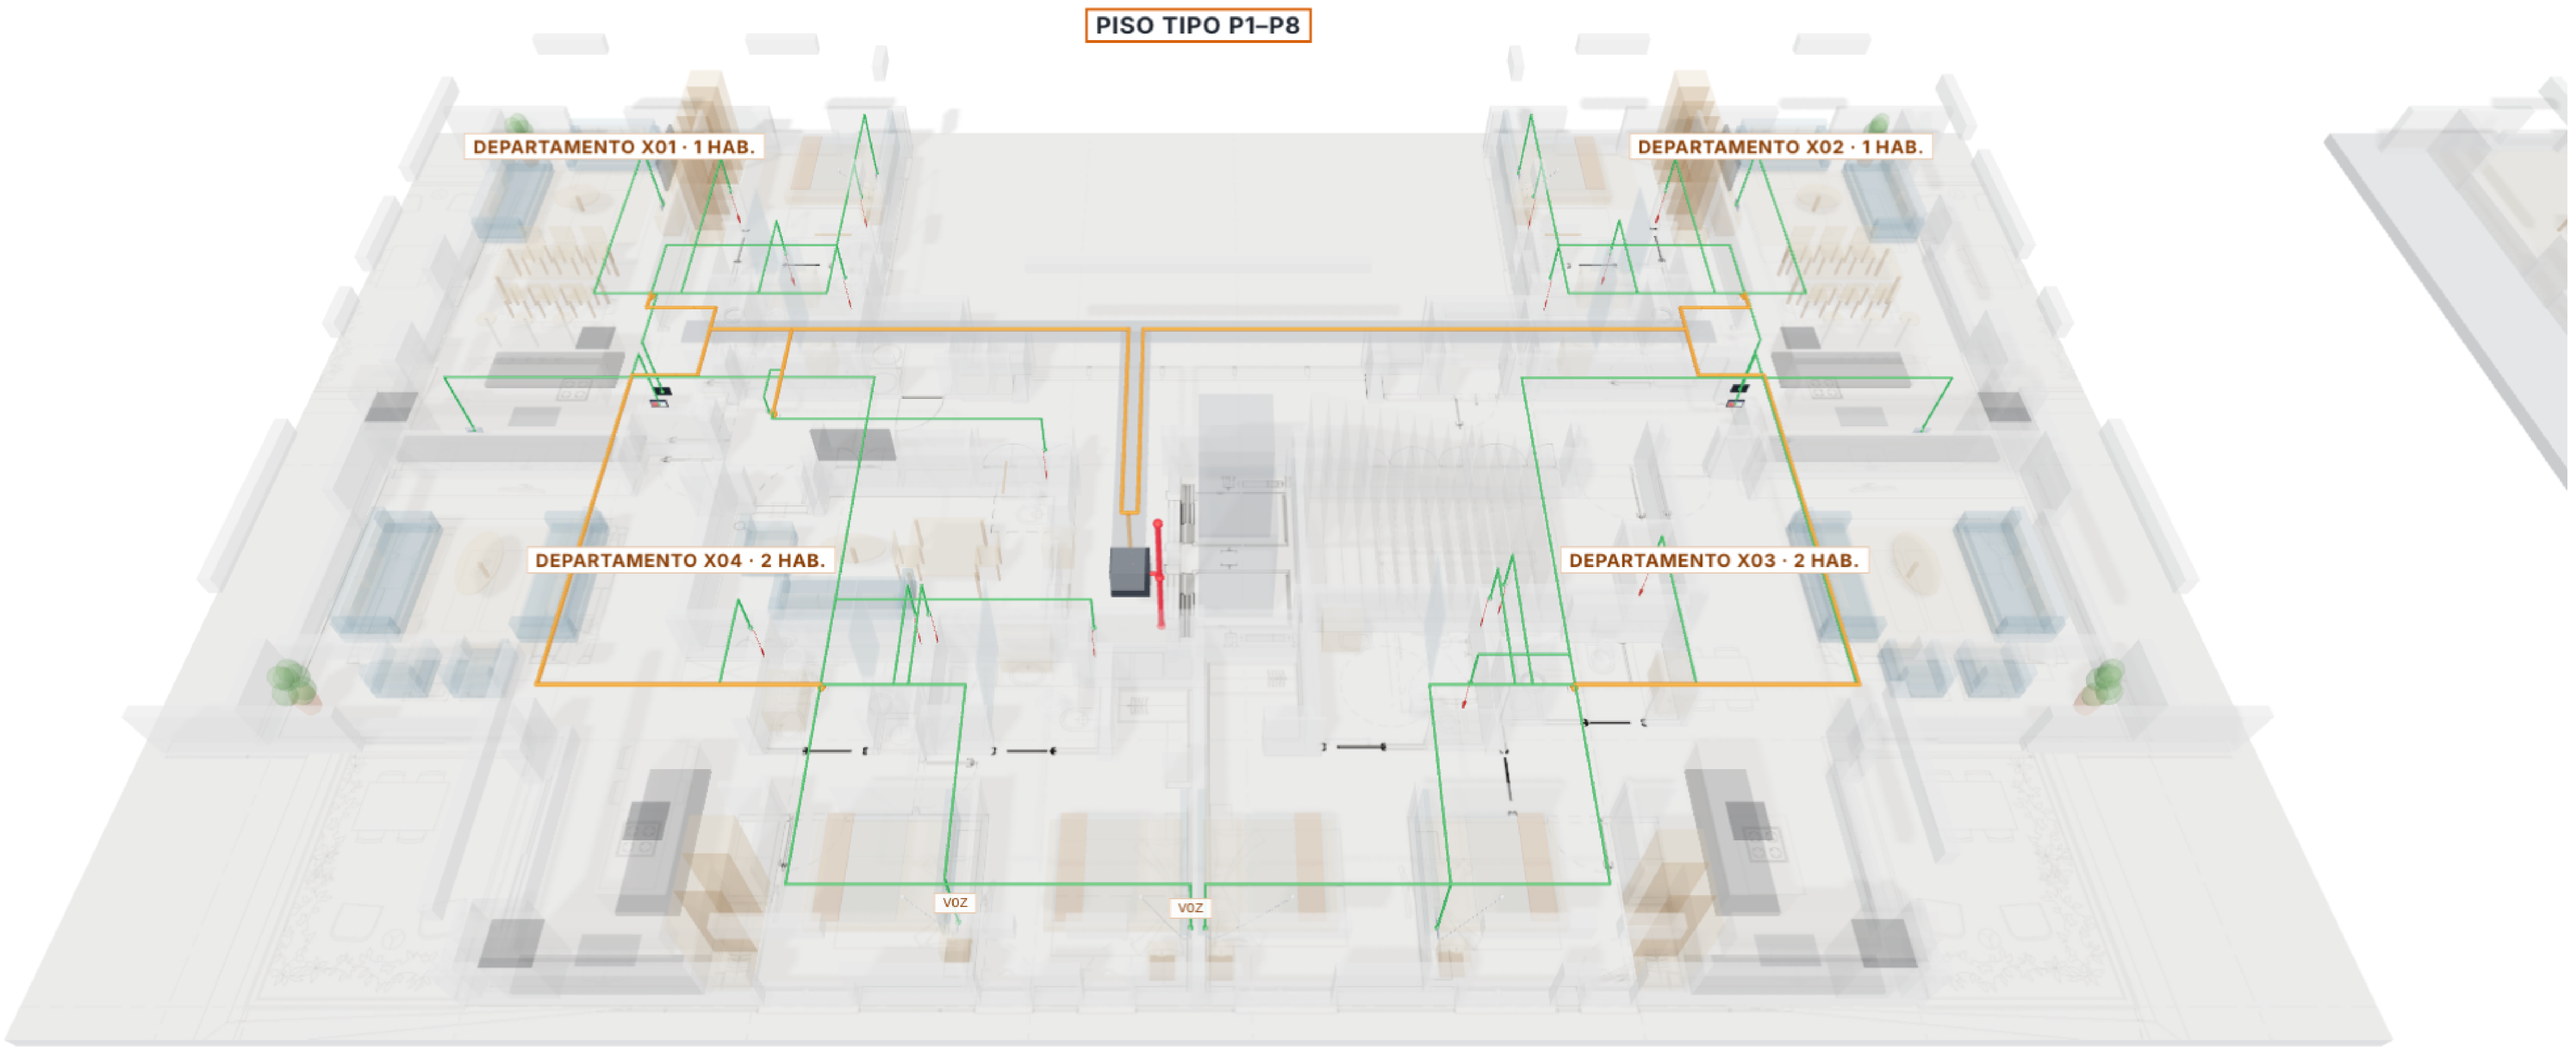
PISO TIPO P1–P8
DEPARTAMENTO X01 · 1 HAB.
DEPARTAMENTO X02 · 1 HAB.
DEPARTAMENTO X04 · 2 HAB.
DEPARTAMENTO X03 · 2 HAB.
VOZ
VOZ

A · Piso tipo – cableado (verde radial · naranja cadena LCom · rojo red)

COLORES · COLOURS · צבעים

🟩 Cat6 radial: cada equipo → LCom de su departamento
Cat6 radial: each device → apartment LCom · Cat6 רדיאלי: כל התקן ← LCom של הדירה

🟧 Cat6 / Cat7 cadena: LCom → LCom → Buscomm del gabinete
Cat6 / Cat7 chain: LCom → LCom → Buscomm · Cat6 / Cat7 שרשרת: LCom ← LCom ← Buscomm

🟥 Cat6A / Cat7 red: Buscomm → switch → montante → servidor PB
Cat6A / Cat7 network: Buscomm → switch → riser → GF server · Cat6A / Cat7 רשת: Buscomm ← מתג ← עמוד ← שרת

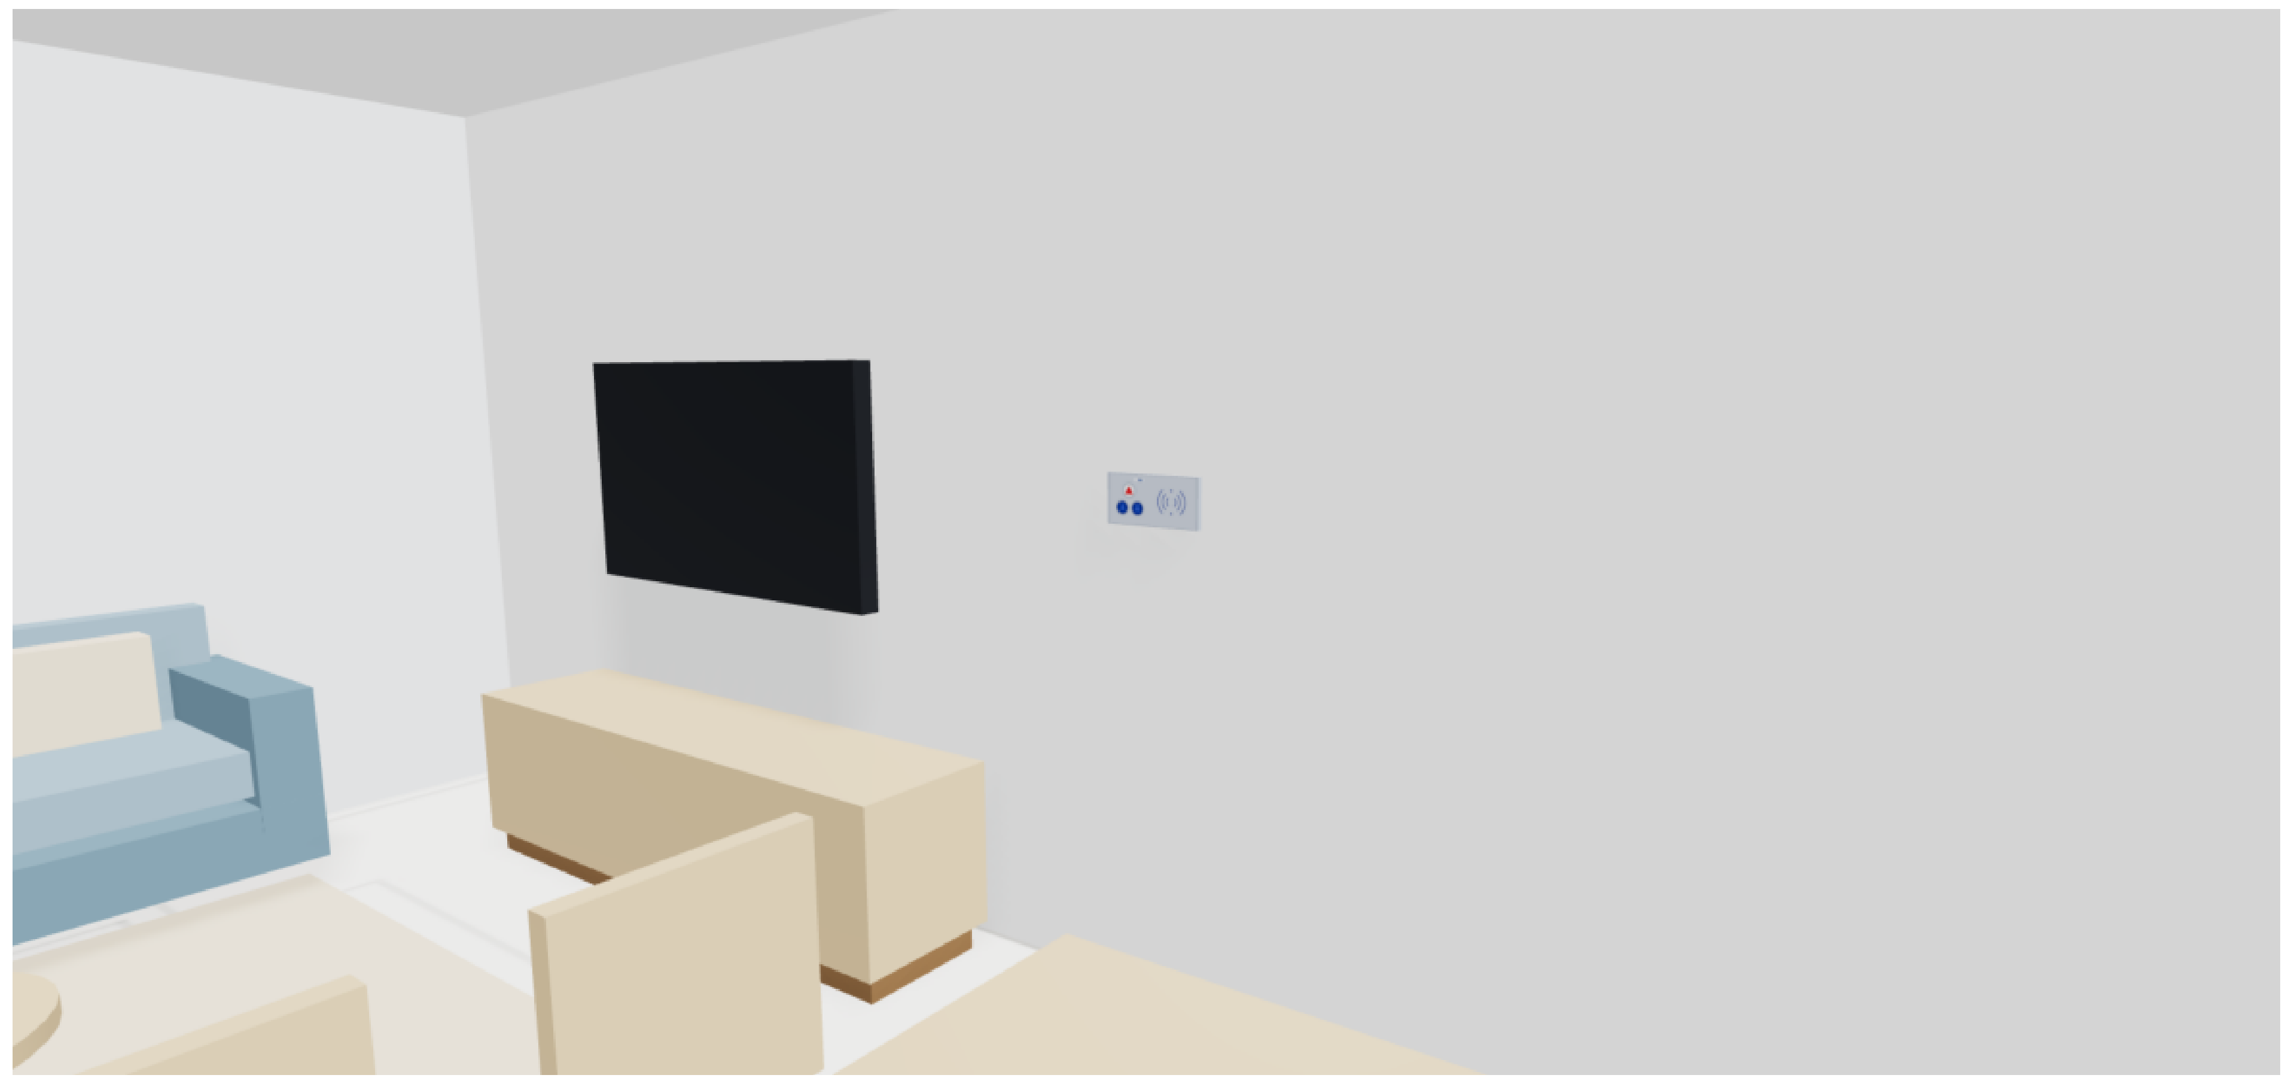

C · Salón – panel con voz y botones

B · Planta baja – lobby y recepción

MIGDALEI YAM A TIJON · VIVIENDA TUTELADA
Llamada de enfermería – PB + 8 pisos · 32 departamentos
Sistema: ACE BG · Advantecnia   Elaboró: Telab International

VISTAS 3D – CABLEADO

3D views – wiring

ESCALA · SCALE	FECHA · DATE	REV	LÁMINA
S/E	**15/10/2026**	**B**	**09**

Base: plano del arquitecto L5 (Massad Oz / Triplet) · cotas en metros
Formato A1 · Rev. B – sobre plano real